




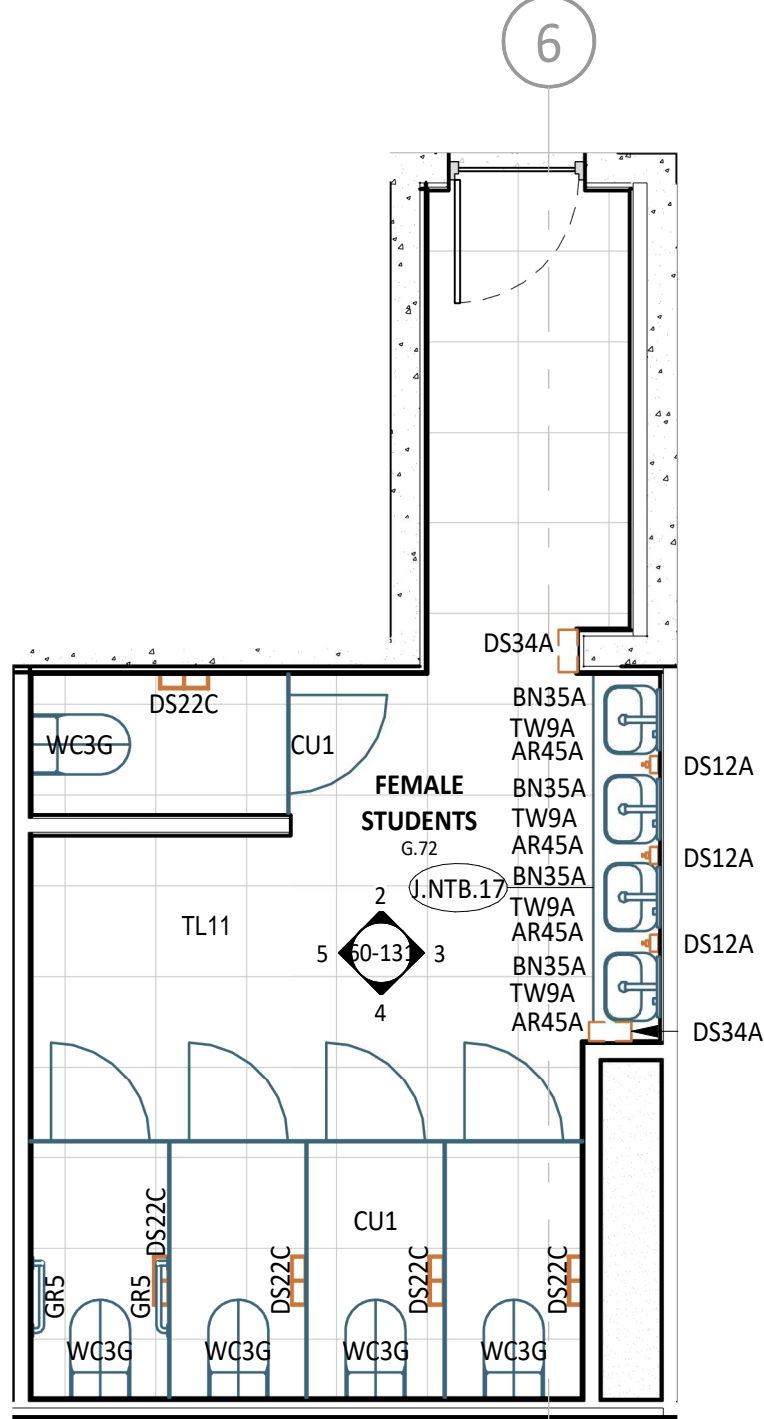


1 PLAN DETAIL
30-01 1 : 50

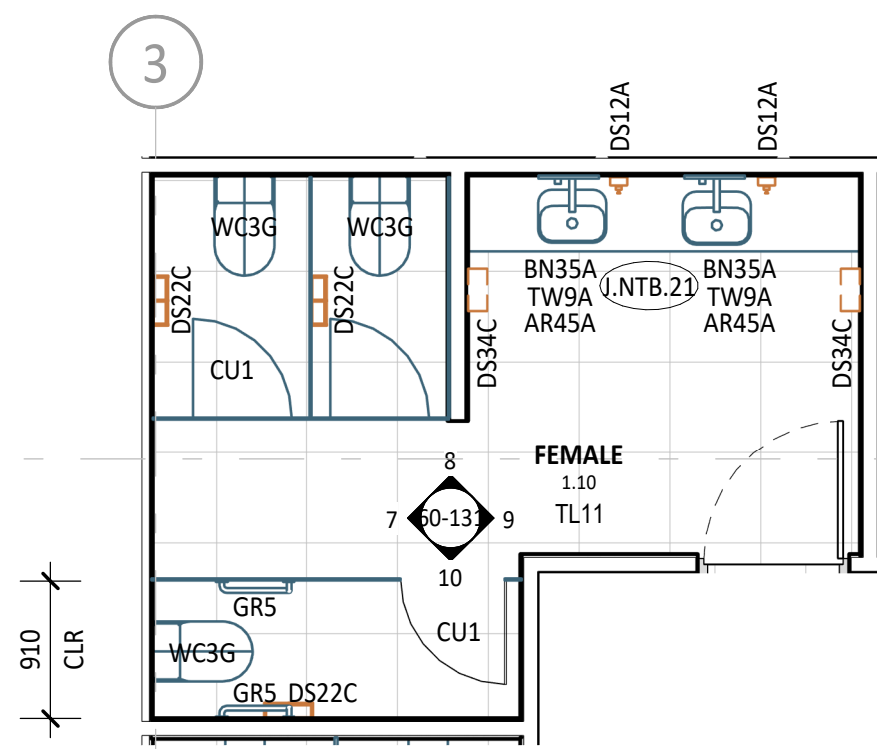


6 PLAN DETAIL
30-01 1 : 50

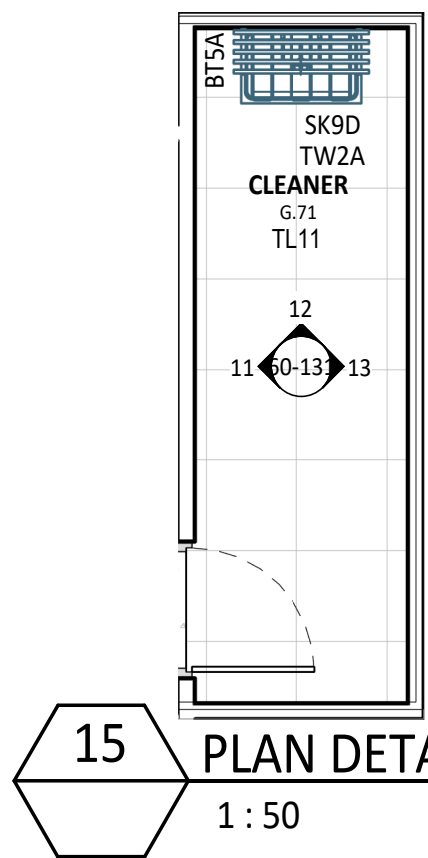


15 PLAN DETAIL
1 : 50

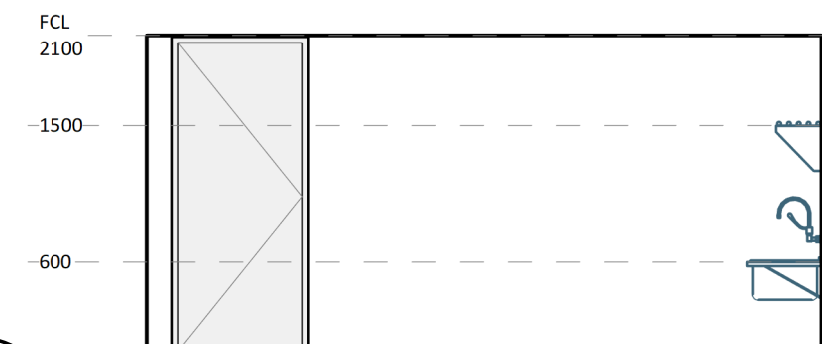


11 ELEVATION DETAIL
60-036 1 : 50

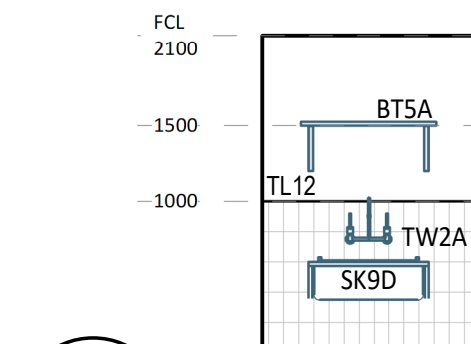


12 ELEVATION DETAIL
60-036 1 : 50

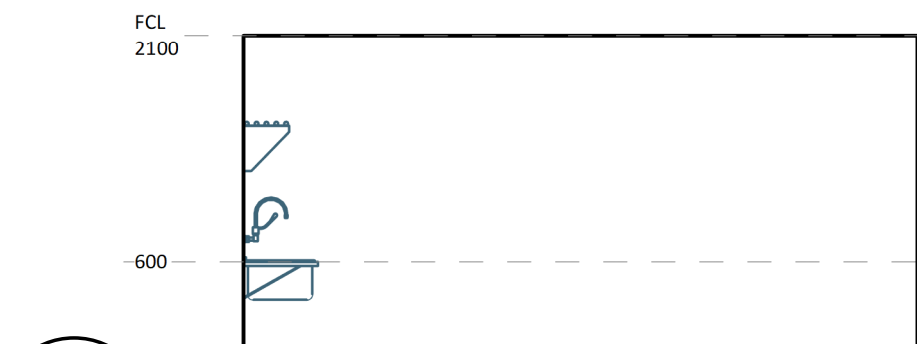


13 ELEVATION DETAIL
60-036 1 : 50

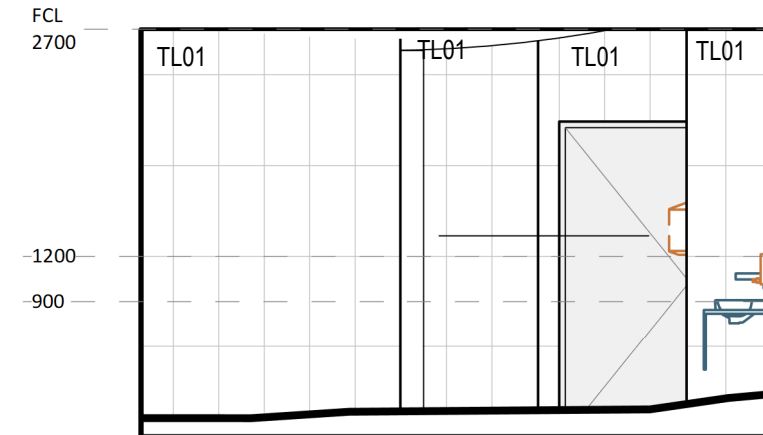


2 ELEVATION DETAIL
60-131 1 : 50

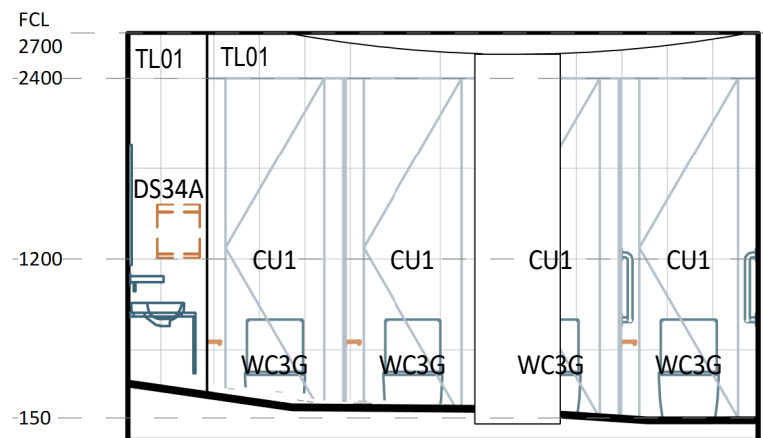


4 ELEVATION DETAIL
60-131 1 : 50

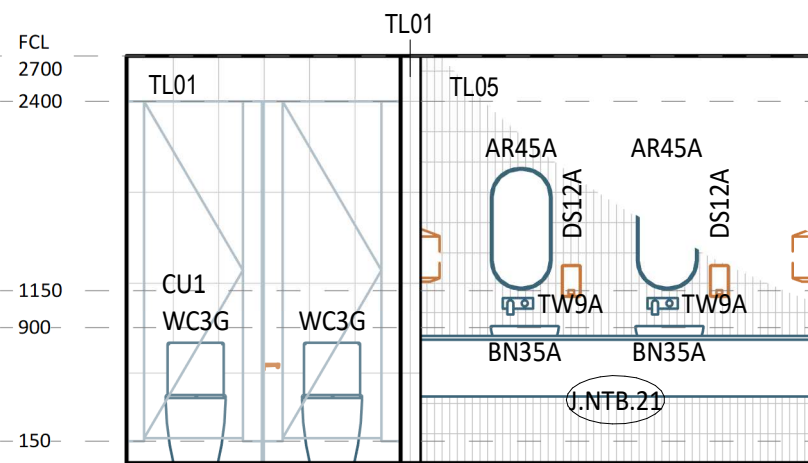


8 ELEVATION DETAIL
60-131 1 : 50

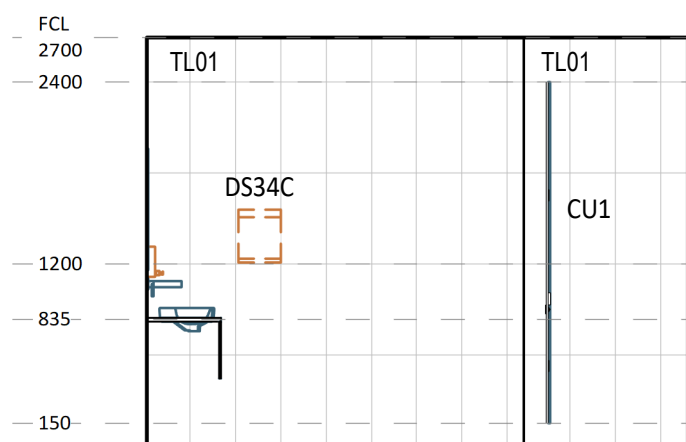


9 ELEVATION DETAIL
60-042 1 : 50

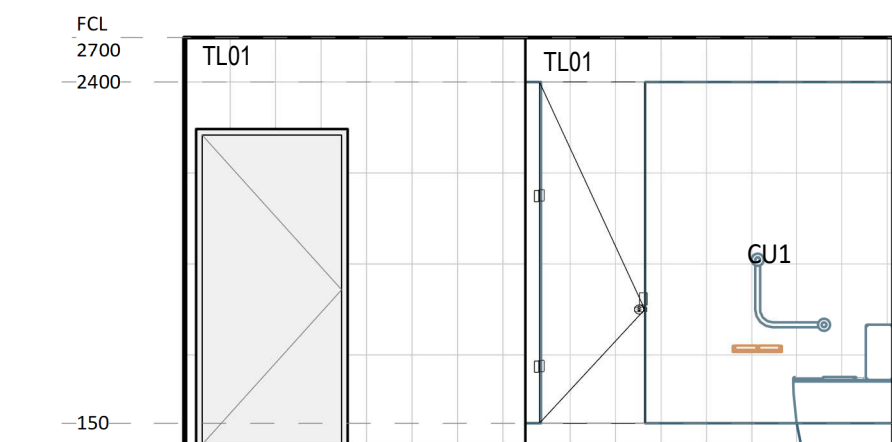

10 ELEVATION DETAIL
60-131 1 : 50

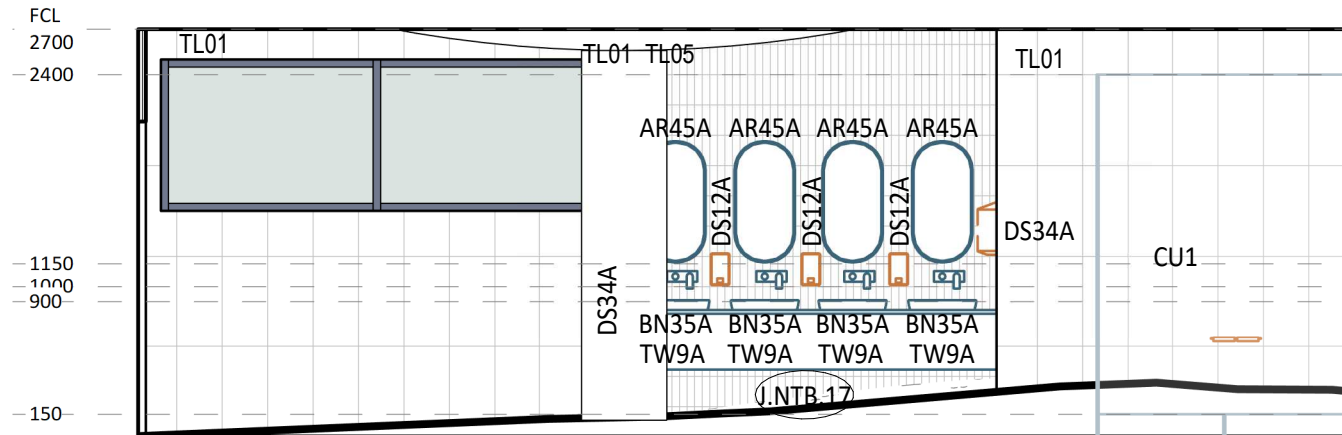

3 ELEVATION DETAIL
60-036 1 : 50

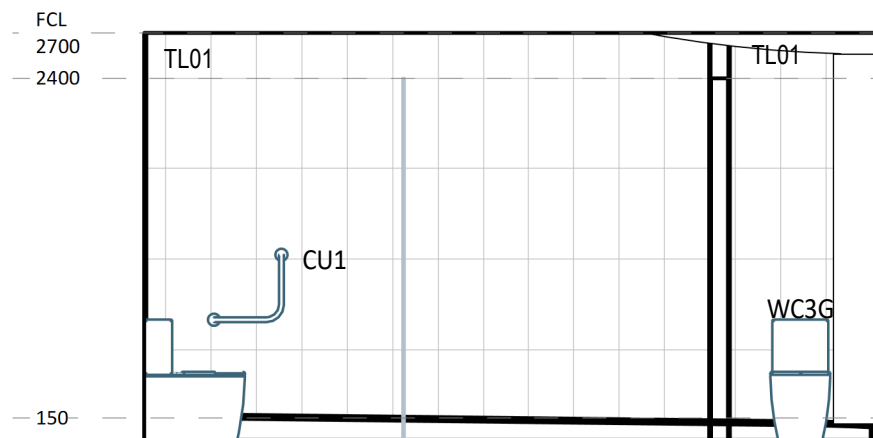

5 ELEVATION DETAIL
60-033 1 : 50

40-LEGEND FFE - FEMALE STUDENTS TOILETS 1.10			
Code	Description	Group	Count
AR45A	Mirror - Oval	1	2
BN35A	Caroma Luna Inset Basin	1	2
BT2	Benchtop	1	1
CU1	Cubicles - Toilet Partition	1	4
EP15B	Rectangular Gable	1	1
GR5	40D - Grab Rail 90 Degree	1	2
TW9A	Tapware - Wall Mounted Basin Mixer	1	2
WC3G	Toilets - Concealed Unit	1	3
DS12A	Dispenser - Soap	2	2
DS22C	Dispenser - Toilet Tissue 2 Roll	2	3
DS34C	Dispenser - Paper Hand Towel	2	2

40-LEGEND FFE - CLEANER G.71			
Code	Description	Group	Count
BT5A	Shelf - Wall Pipe SS	1	1
SK9D	Sink - Cleaner's with Lever Tapware - Wall Mounted	1	1

40-LEGEND FFE - FEMALE STUDENTS TOILETS 6.72			
Code	Description	Group	Count
AR45A	Mirror - Oval	1	4
BN35A	Caroma Luna Inset Basin	1	4
BT2	Benchtop	1	1
CU1	Cubicles - Toilet Partition	1	5
EP15B	Rectangular Gable	1	1
GR5	40D - Grab Rail 90 Degree	1	2
TW9A	Tapware - Wall Mounted Basin Mixer	1	4
WC3G	Toilets - Concealed Unit	1	5
DS12A	Dispenser - Soap	2	3
DS22C	Dispenser - Toilet Tissue 2 Roll	2	5
DS34A	Dispenser - Paper Hand Towel	2	2

NOTE: BUILDER TO ALLOW FOR HAND DRYERS, BUILDER TO CONSULT WITH CQU ON REQUIREMENT. ALLOW FOR POWER

- #### ROOM LAYOUT SHEET NOTES
- ALL ARCHITECTURAL DRAWINGS TO BE READ IN CONJUNCTION WITH OTHER DISCIPLINES.
 - REFER TO FF&E, SANITARYWARE SCHEDULES FOR ALL FURNITURE, FIXTURES, AND EQUIPMENT.
 - REFER TO ENGINEER'S DRAWINGS FOR DETAILS ON FIRE EXTINGUISHERS AND FIRE BLANKETS
 - REFER TO ELECTRICAL DOCUMENTATION FOR OUTLET DETAILS (ie. POWER, DATA, COMMS etc.)
 - REFER TO AUDIO VISUAL DOCUMENTATION (VideoPro) FOR AV REQUIREMENTS AND DETAILS.
 - AV SUPPLIER TO CONFIRM EXACT POSITIONS OF EQUIPMENT ON SITE
 - ALL FF&E ITEMS ARE TO BE READ IN CONJUNCTION WITH FF&E SCHEDULES AND CQU DESIGN MANUAL.
 - ALL FF&E AND TRANSFER ITEMS TO BE CONFIRMED BY THE CLIENT.
 - PROVIDE ALLOWANCE AND ADD SUPPORT TO WALLS, WHERE FITTINGS ARE WALL MOUNTED. THIS INCLUDES BUT NOT LIMITED TO HANDBASINS, HANDRAILS, SCREENS, PROJECTORS, etc.
 - SPECIALISED EQUIPMENT ARE SUPPLIED BY CLIENT AND INSTALLED BY THE BUILDER-CONTRACTOR.
 - FF&E COUNT IS FOR INFORMATION ONLY. THE TOTAL NUMBER OF FF&E ITEMS ARE TO BE CONFIRMED WITH CLIENT AND ARCHITECTS BEFORE PURCHASE OF ITEMS.
 - CONFIRM ALL DIMENSIONS ON SITE FOR JOINERY ITEMS.
 - REFER TO EQUIPMENT AUDIT SPREADSHEET FOR DETAILS OF TRANSFER EQUIPMENT
 - CONTRACTOR RESPONSIBLE FOR ALL TRANSFER INCLUDING DISCONNECTION, RECONNECTION, AND INSTALLATION OF TRANSFER EQUIPMENT
 - POWER AND DATA POINTS SHOWN ON THE ROOM LAYOUT SHEETS WERE SHOWN AND DISCUSSED DURING USER GROUP BRIEFING. THESE RELATE TO PARTICULAR EQUIPMENT THAT WAS DISCUSSED AS REQUIRING POWER AND DATA. THESE REFLECT STAKEHOLDER EXPECTATIONS FOR SPECIFIC POWER AND DATA POINTS AND HAVE REMAINED IN THE DOCUMENTATION AS A USEFUL REFERENCE FOR THE CONTRACTOR. THESE ARE NOT A COMPLETE QUANTITY AND SPECIFICATION OF POWER AND DATA. THE CONTRACTOR IS TO REFER TO ELECTRICAL ENGINEER'S DOCUMENTATION FOR ALLOWANCE. REFER TO ELECTRICAL DOCUMENTATION FOR AMPS AND 3 PHASE POWER REQUIREMENTS. REFER TO AUDIO VISUAL (VIDEOPRO) DOCUMENTATION FOR ADDITIONAL POWER AND DATA REQUIREMENTS
 - ALLOW FOR STRUCTURAL PLY BACKING BEHIND PLASTERBOARD FOR FULL EXTENT OF WALLS WITH MOUNTED AUDIO VISUAL EQUIPMENT. REFER TO AUDIO VISUAL (VIDEOPRO) DOCUMENTATION FOR LOCATIONS OF WALL MOUNTED EQUIPMENT.
 - REFER TO FLOOR PLANS FOR DETAILS ON DOORS
 - ALL THEORY ROOMS, CAD CLASS ROOMS, MEETING ROOMS, ONLINE TEACHING CLASS ROOMS WITH INTERNAL GLAZING ARE TO INCLUDE BLOCK OUT ROLLER BLINDS FOR SECURITY.
 - HEARING AUGMENTATION TO AUSTRALIAN STANDARDS – REFER VIDEOPRO AND ELECTRICAL SPECIFICATION

- #### FF&E LEGEND
- GROUP 1 ITEMS - PROVIDED & FITTED UNDER CONTRACT
 - GROUP 2 ITEMS - PROVIDED BY CLIENT & FITTED UNDER CONTRACT
 - GROUP 2T ITEMS - EXISTING EQUIPMENT - RELOCATED & FITTED UNDER CONTRACT
 - GROUP 3 ITEMS - PROVIDED & INSTALLED BY CLIENT
- PLANS TO BE PRINTED IN COLOUR