



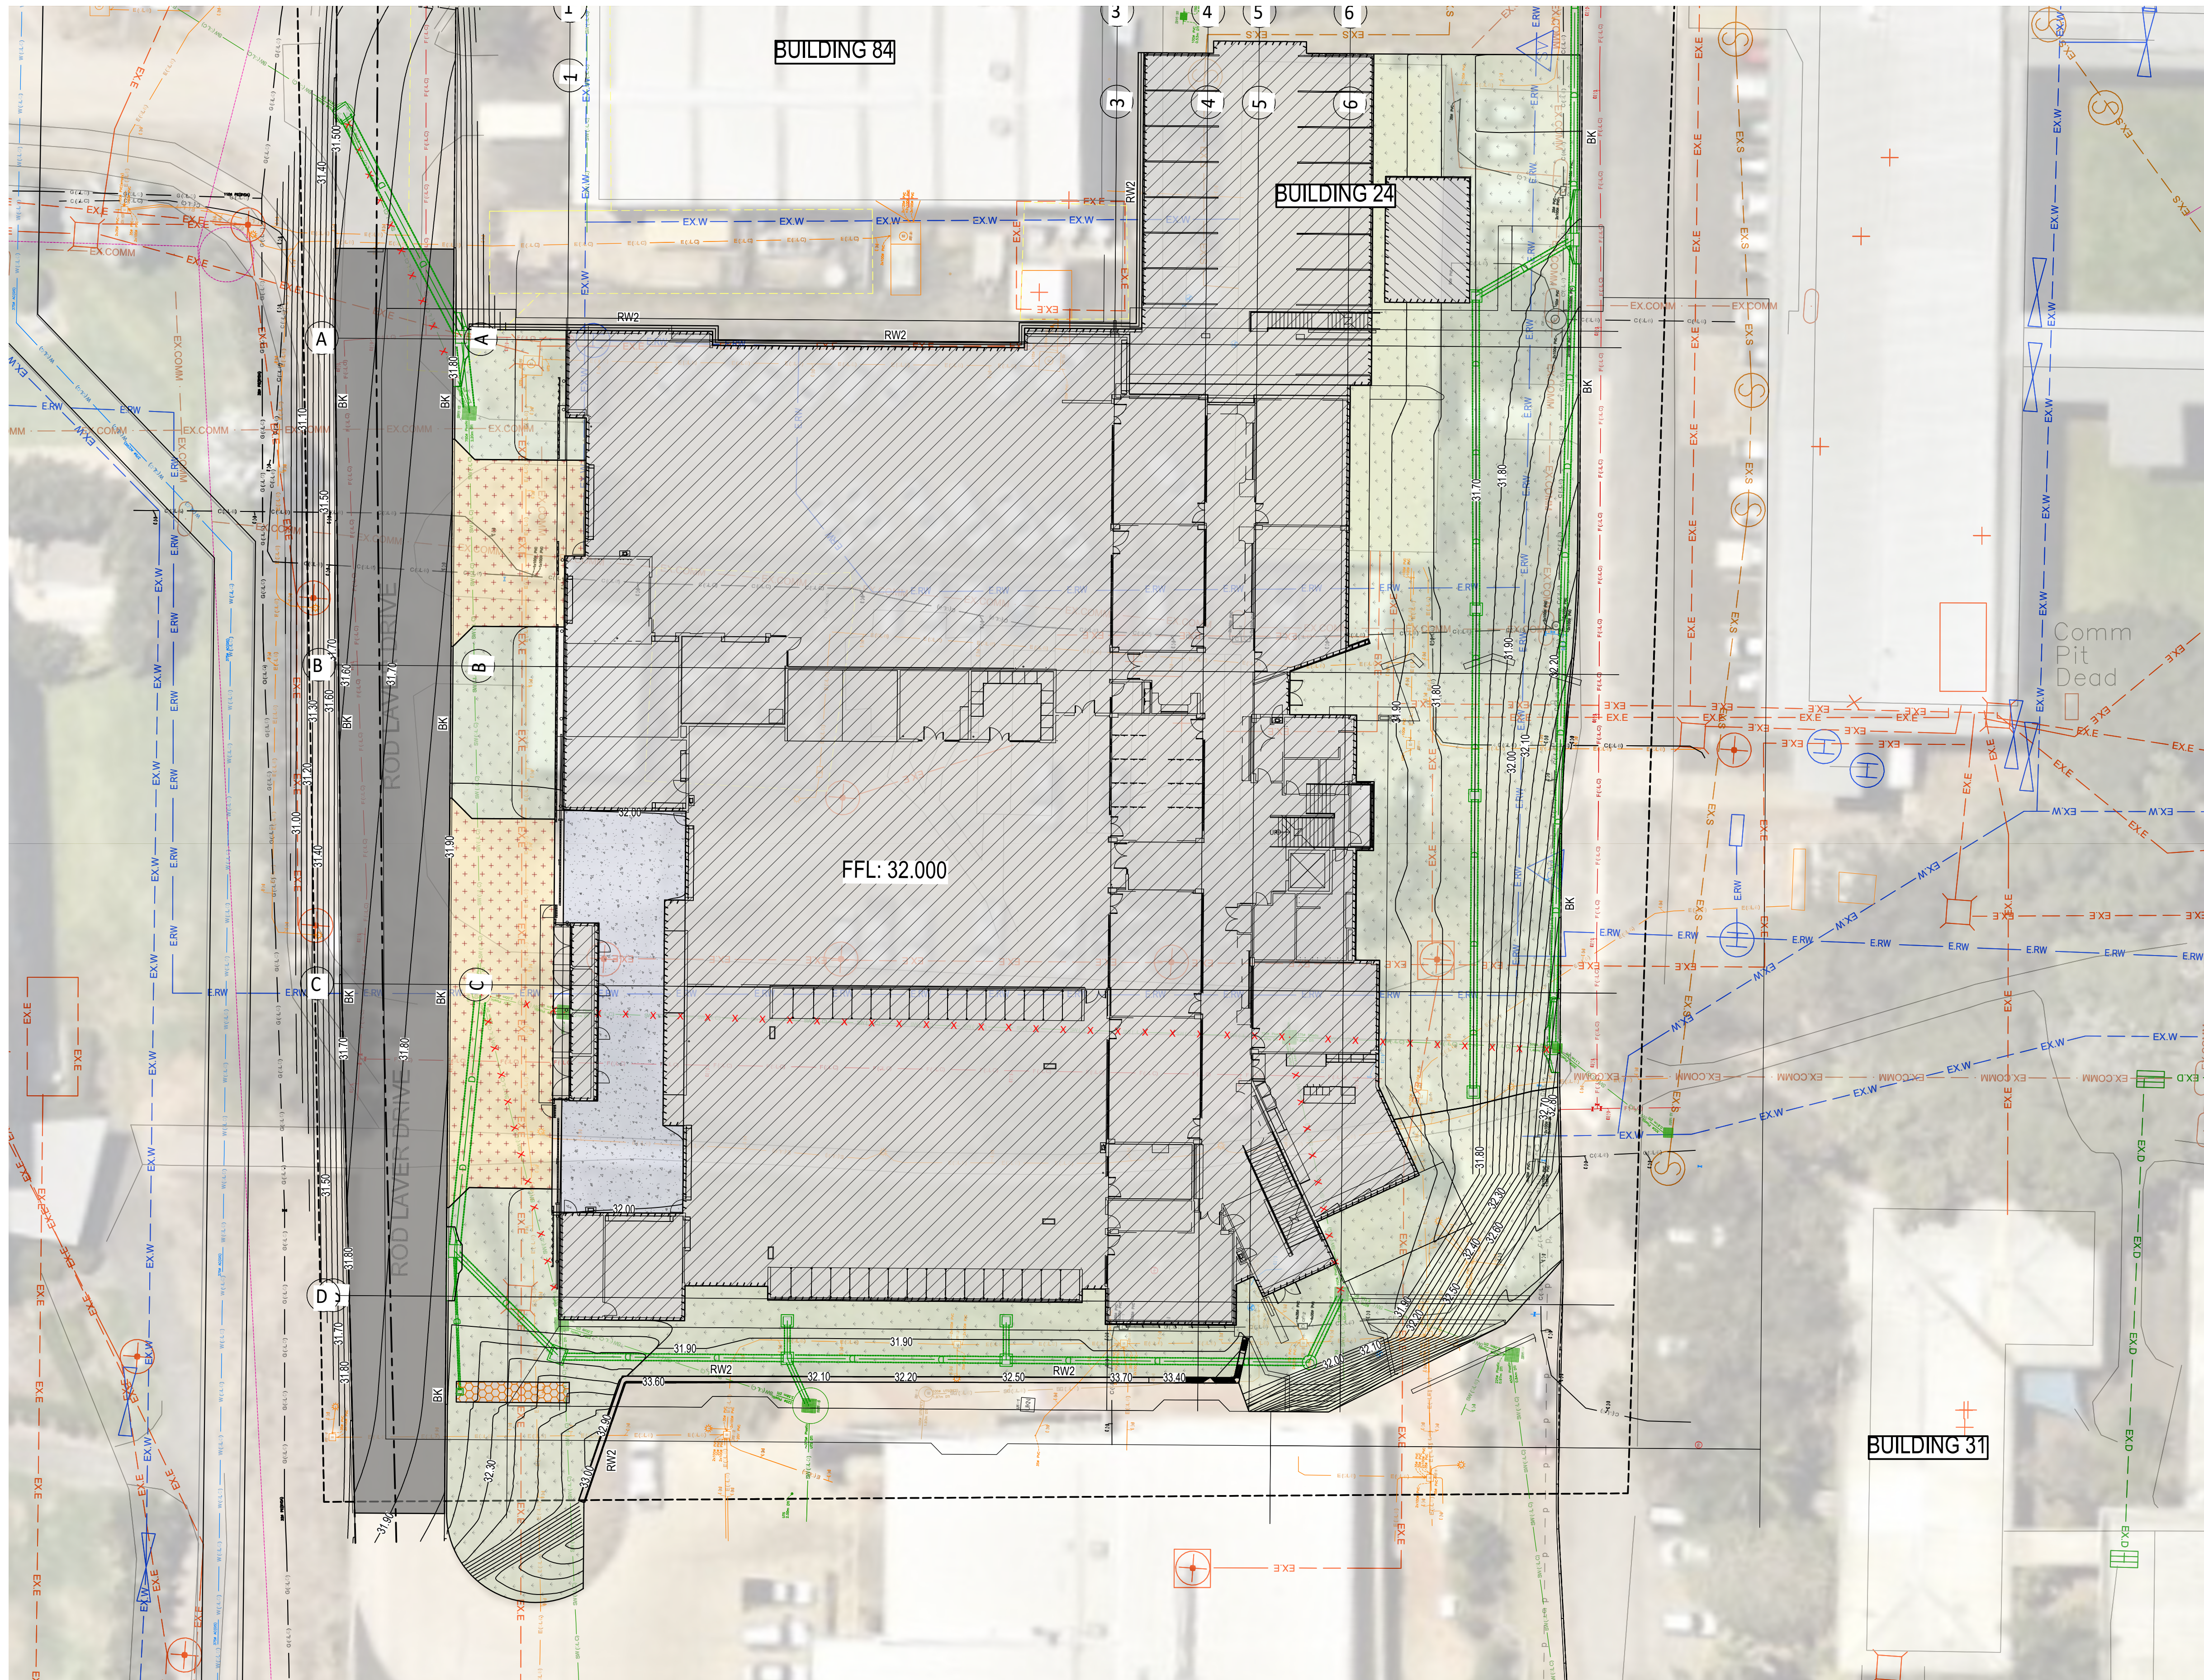

LEGEND EXISTING	
	EX.D EXISTING STORMWATER DRAINAGE
	EX.W EXISTING WATERMAIN
	EX.E EXISTING ELECTRICAL CONDUITS
	ER.W EXISTING FIREMAIN
	EX.COMM EXISTING COMMUNICATIONS
	EX.S EXISTING SEWER MAIN
	444.50 EXISTING CONTOURS

LEGEND	
	PROPOSED PAVEMENT TYPE 1 LIGHT DUTY ASPHALT - REFER DWG C140
	PROPOSED PAVEMENT TYPE 2 HEAVY DUTY ASPHALT - REFER DWG C140
	PROPOSED PAVEMENT TYPE 3 HEAVY DUTY CONCRETE - REFER DWG C140
	PROPOSED PAVEMENT TYPE 4 LIGHT DUTY CONCRETE - REFER DWG C140
	BULK EARTHWORKS TO BUILDING AREA. ALLOW TO CARRY OUT THE WORKS IN ACCORDANCE WITH EARTHWORKS NOTES ON GENERAL NOTES DRAWING INCLUDING STRIPPING, PROOF ROLLING AND FILLING WITH IMPORTED SELECT FILL MATERIAL TO ACHIEVE THE NOMINATED BULK EARTHWORKS LEVELS AS SPECIFIED IN THE PROJECT GEOTECHNICAL REPORT. ALLOW TO PROVIDE 100mm THICK TYPE 2.3 (CBR45%) MATERIAL.
	BULK EARTHWORKS TO LANDSCAPE AREA. ALLOW TO FINISH EARTHWORKS TO LANDSCAPE ARCHITECTS DETAILS, GENERALLY 300mm BELOW FINISHED SURFACE LEVEL (UNO).
	BE15.28 + PROPOSED BULK EARTHWORKS LEVEL FOLLOWING CARRYING OUT WORKS IN ACCORDANCE WITH EARTHWORKS NOTES ON GENERAL NOTES DRAWING INCLUDING STRIPPING, PROOF ROLLING AND FILLING.
	REFER NOTE 1 FOR DETAILS

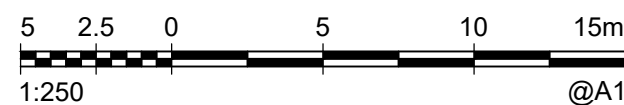

P1	30012026	RO	DRAFT 60% DESIGN DEVELOPMENT	JC	JC
REV	DATE	BY	DESCRIPTION	CHK	APP
DRAWING STATUS:			PRELIMINARY		



<http://www.wsp.com>

CLIENT:



ARCHITECT:



PROJECT:

CQU ROCKHAMPTON TAFE

TITLE:

TRADES BUILDING EARTHWORKS LAYOUT PLAN

SCALE @ A1:

1:250

CHECKED:

JC

APPROVED:

JC

PROJECT NUMBER:

PS229518

DRAWN:

RO

DATE:

1/30/2026

DRAWING No:

C100

REV:

P1

© WSP Australia Pty Ltd