

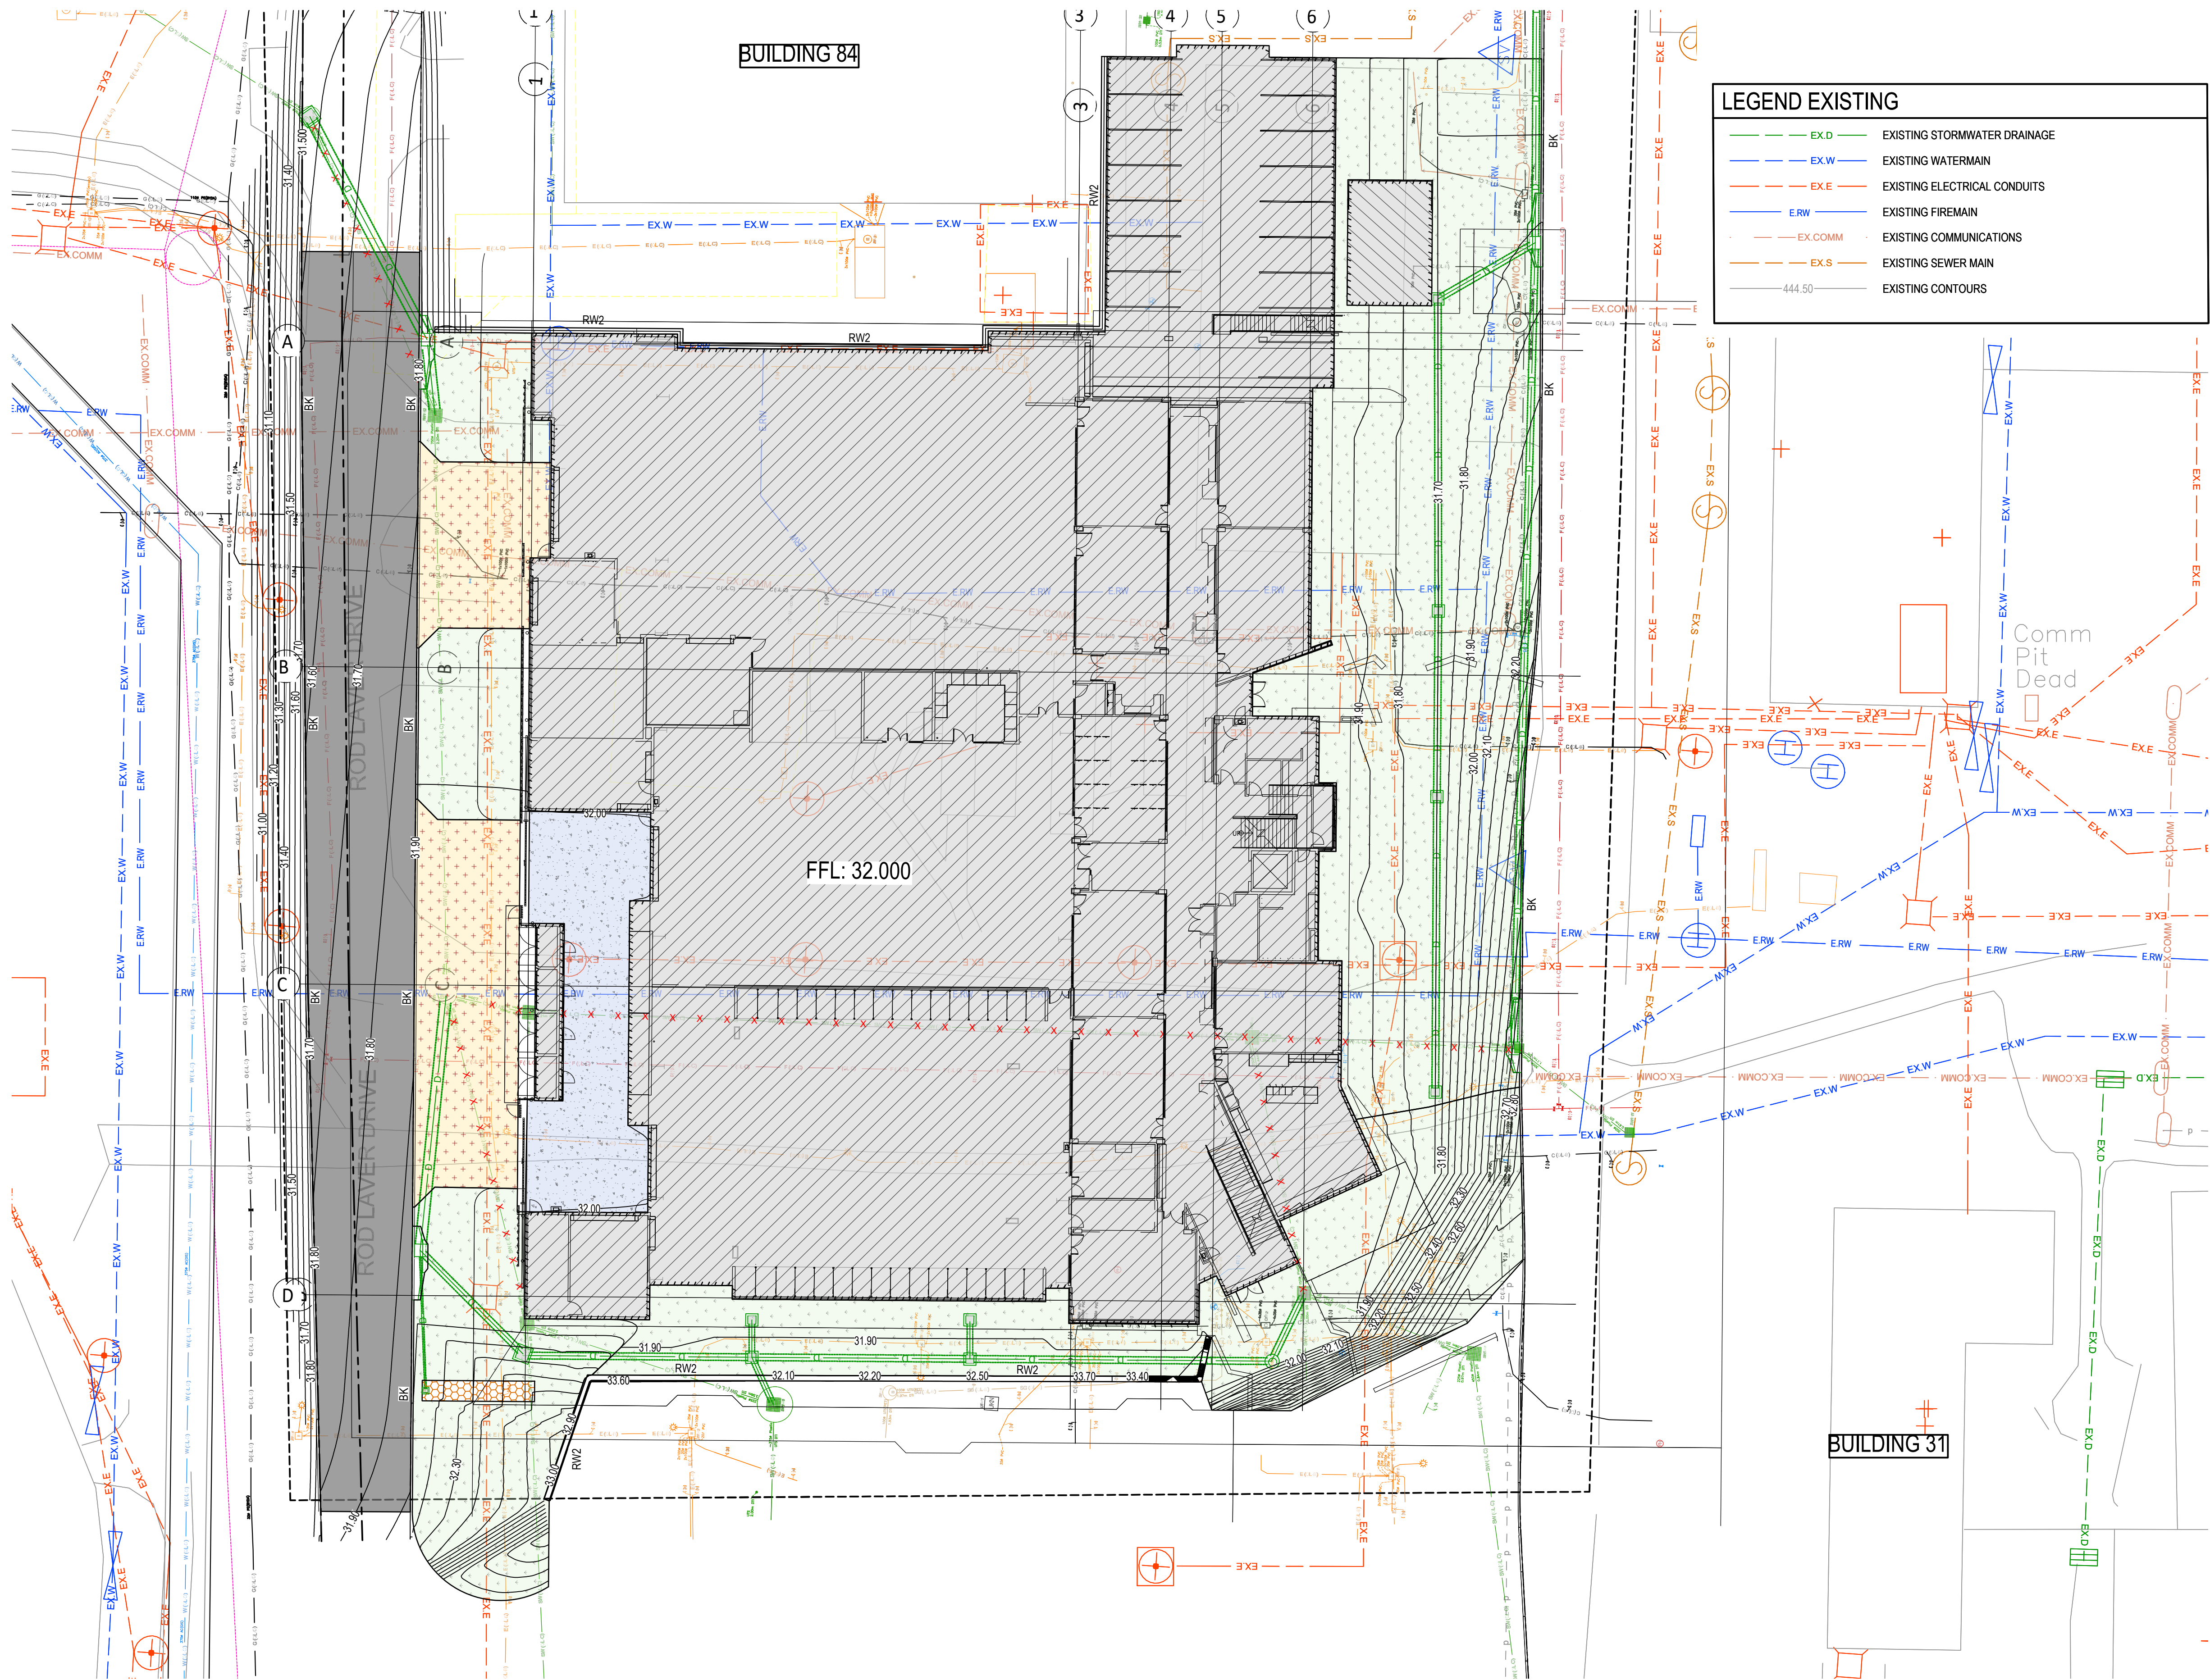


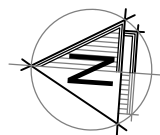

LEGEND EXISTING	
	EX.D EXISTING STORMWATER DRAINAGE
	EX.W EXISTING WATERMAIN
	EX.E EXISTING ELECTRICAL CONDUITS
	ER.W EXISTING FIREMAIN
	EX.COMM EXISTING COMMUNICATIONS
	EX.S EXISTING SEWER MAIN
	444.50 EXISTING CONTOURS

LEGEND	
	PROPOSED BUILDING AREA
	PROPOSED PAVEMENT TYPE 1 LIGHT DUTY ASPHALT - REFER DWG C140
	PROPOSED PAVEMENT TYPE 2 HEAVY DUTY ASPHALT - REFER DWG C140
	PROPOSED PAVEMENT TYPE 3 HEAVY DUTY CONCRETE - REFER DWG C140
	PROPOSED PAVEMENT TYPE 4 LIGHT DUTY CONCRETE - REFER DWG C140
	PROPOSED CHEVRON LINEMARKING TO AS1742.2
	PROPOSED LANDSCAPE AREA REFER LANDSCAPE PLANS FOR DETAILS
	STAGE BOUNDARY
	CONTOURS MAJOR
	PROPOSED TOP OF BATTER
	PROPOSED BOTTOM OF BATTER
	PROPOSED EDGE OF BITUMEN
	PROPOSED BARRIER KERB AND CHANNEL
	PROPOSED BARRIER KERB AND CHANNEL
	PROPOSED INVERT KERB
	PROPOSED BLOCK RETAINING WALL
	PROPOSED GALVANISED TUBULAR FENCE
	PROPOSED SIGN
	PROPOSED BOLLARD
	PROPOSED TACTILE GROUND SURFACE INDICATORS (TGSi)
	PROPOSED WHEEL STOP
	PROPOSED KERB RAMP
	ITEMS / SERVICES TO BE REMOVED
	PROPOSED PAVEMENT LEVEL
	PROPOSED SURFACE LEVEL
	PROPOSED BULK EARTHWORKS LEVEL
	PROPOSED TOP OF RETAINING WALL LEVEL
	PROPOSED BOTTOM OF RETAINING WALL LEVEL
	EXISTING SURFACE LEVEL
	PROPOSED SURFACE FALL
	PROPOSED TRENCH GRATE
	PROPOSED ROOFWATER DRAINAGE PIPE
	PROPOSED SUBSOIL DRAINAGE
	PROPOSED STORMWATER DRAINAGE PIPE AND MANHOLE
	PROPOSED HEADWALL AND ROCK OUTLET PROTECTION
	PROPOSED TABLEDRAIN
	PROPOSED WATER PIPE
	PROPOSED ELECTRICAL CONDUIT/CABLES
	REFER NOTE 1 FOR DETAILS

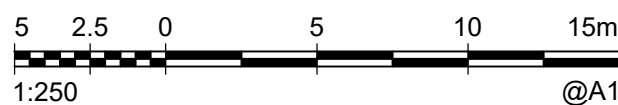

P1	30012026	RO	DRAFT 60% DESIGN DEVELOPMENT	JC	JC
REV	DATE	BY	DESCRIPTION	CHK	APP
DRAWING STATUS:			PRELIMINARY		



<http://www.wsp.com>

CLIENT:



ARCHITECT:



PROJECT:

CQU ROCKHAMPTON TAFE

TITLE:

TRADES BUILDING SITEWORKS LAYOUT PLAN

SCALE @ A1:

1:250

CHECKED:

JC

APPROVED:

JC

PROJECT NUMBER:

PS229518

DRAWN:

RO

DATE:

1/30/2026

DRAWING No:

C110

REV:

P1

© WSP Australia Pty Ltd