



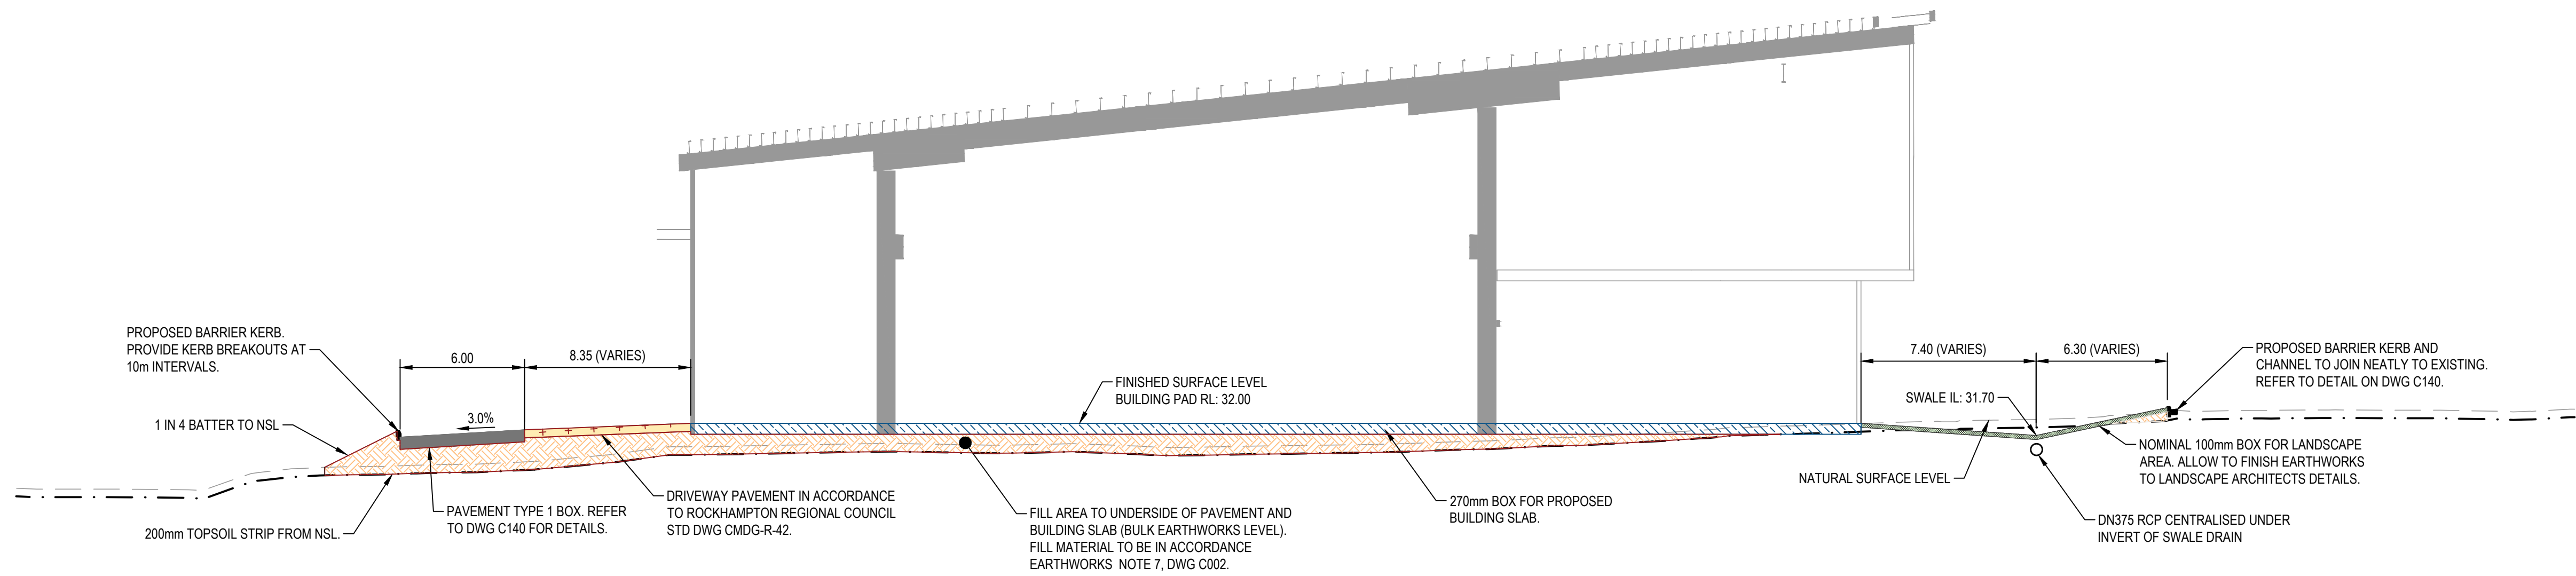

DATUM RL: 27.00

SECTION A
SCALE 1:200 H/C 100
1:100 V

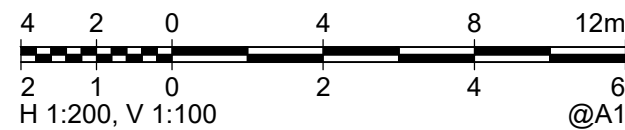

P1	12/02/2026	RO	60% DESIGN DEVELOPMENT	JC	JC
REV	DATE	BY	DESCRIPTION	CHK	APP
DRAWING STATUS:			PRELIMINARY		



<http://www.wsp.com>

CLIENT:


ARCHITECT:


PROJECT:
CQU ROCKHAMPTON TAFE

TITLE:
TRADES BUILDING CIVIL DETAILS
SHEET 2

SCALE @ A1: AS ABOVE	CHECKED: JC	APPROVED: JC
PROJECT NUMBER: PS229518	DRAWN: RO	DATE: 12/02/2026
DRAWING No: C141		REV: P1
© WSP Australia Pty Ltd		