


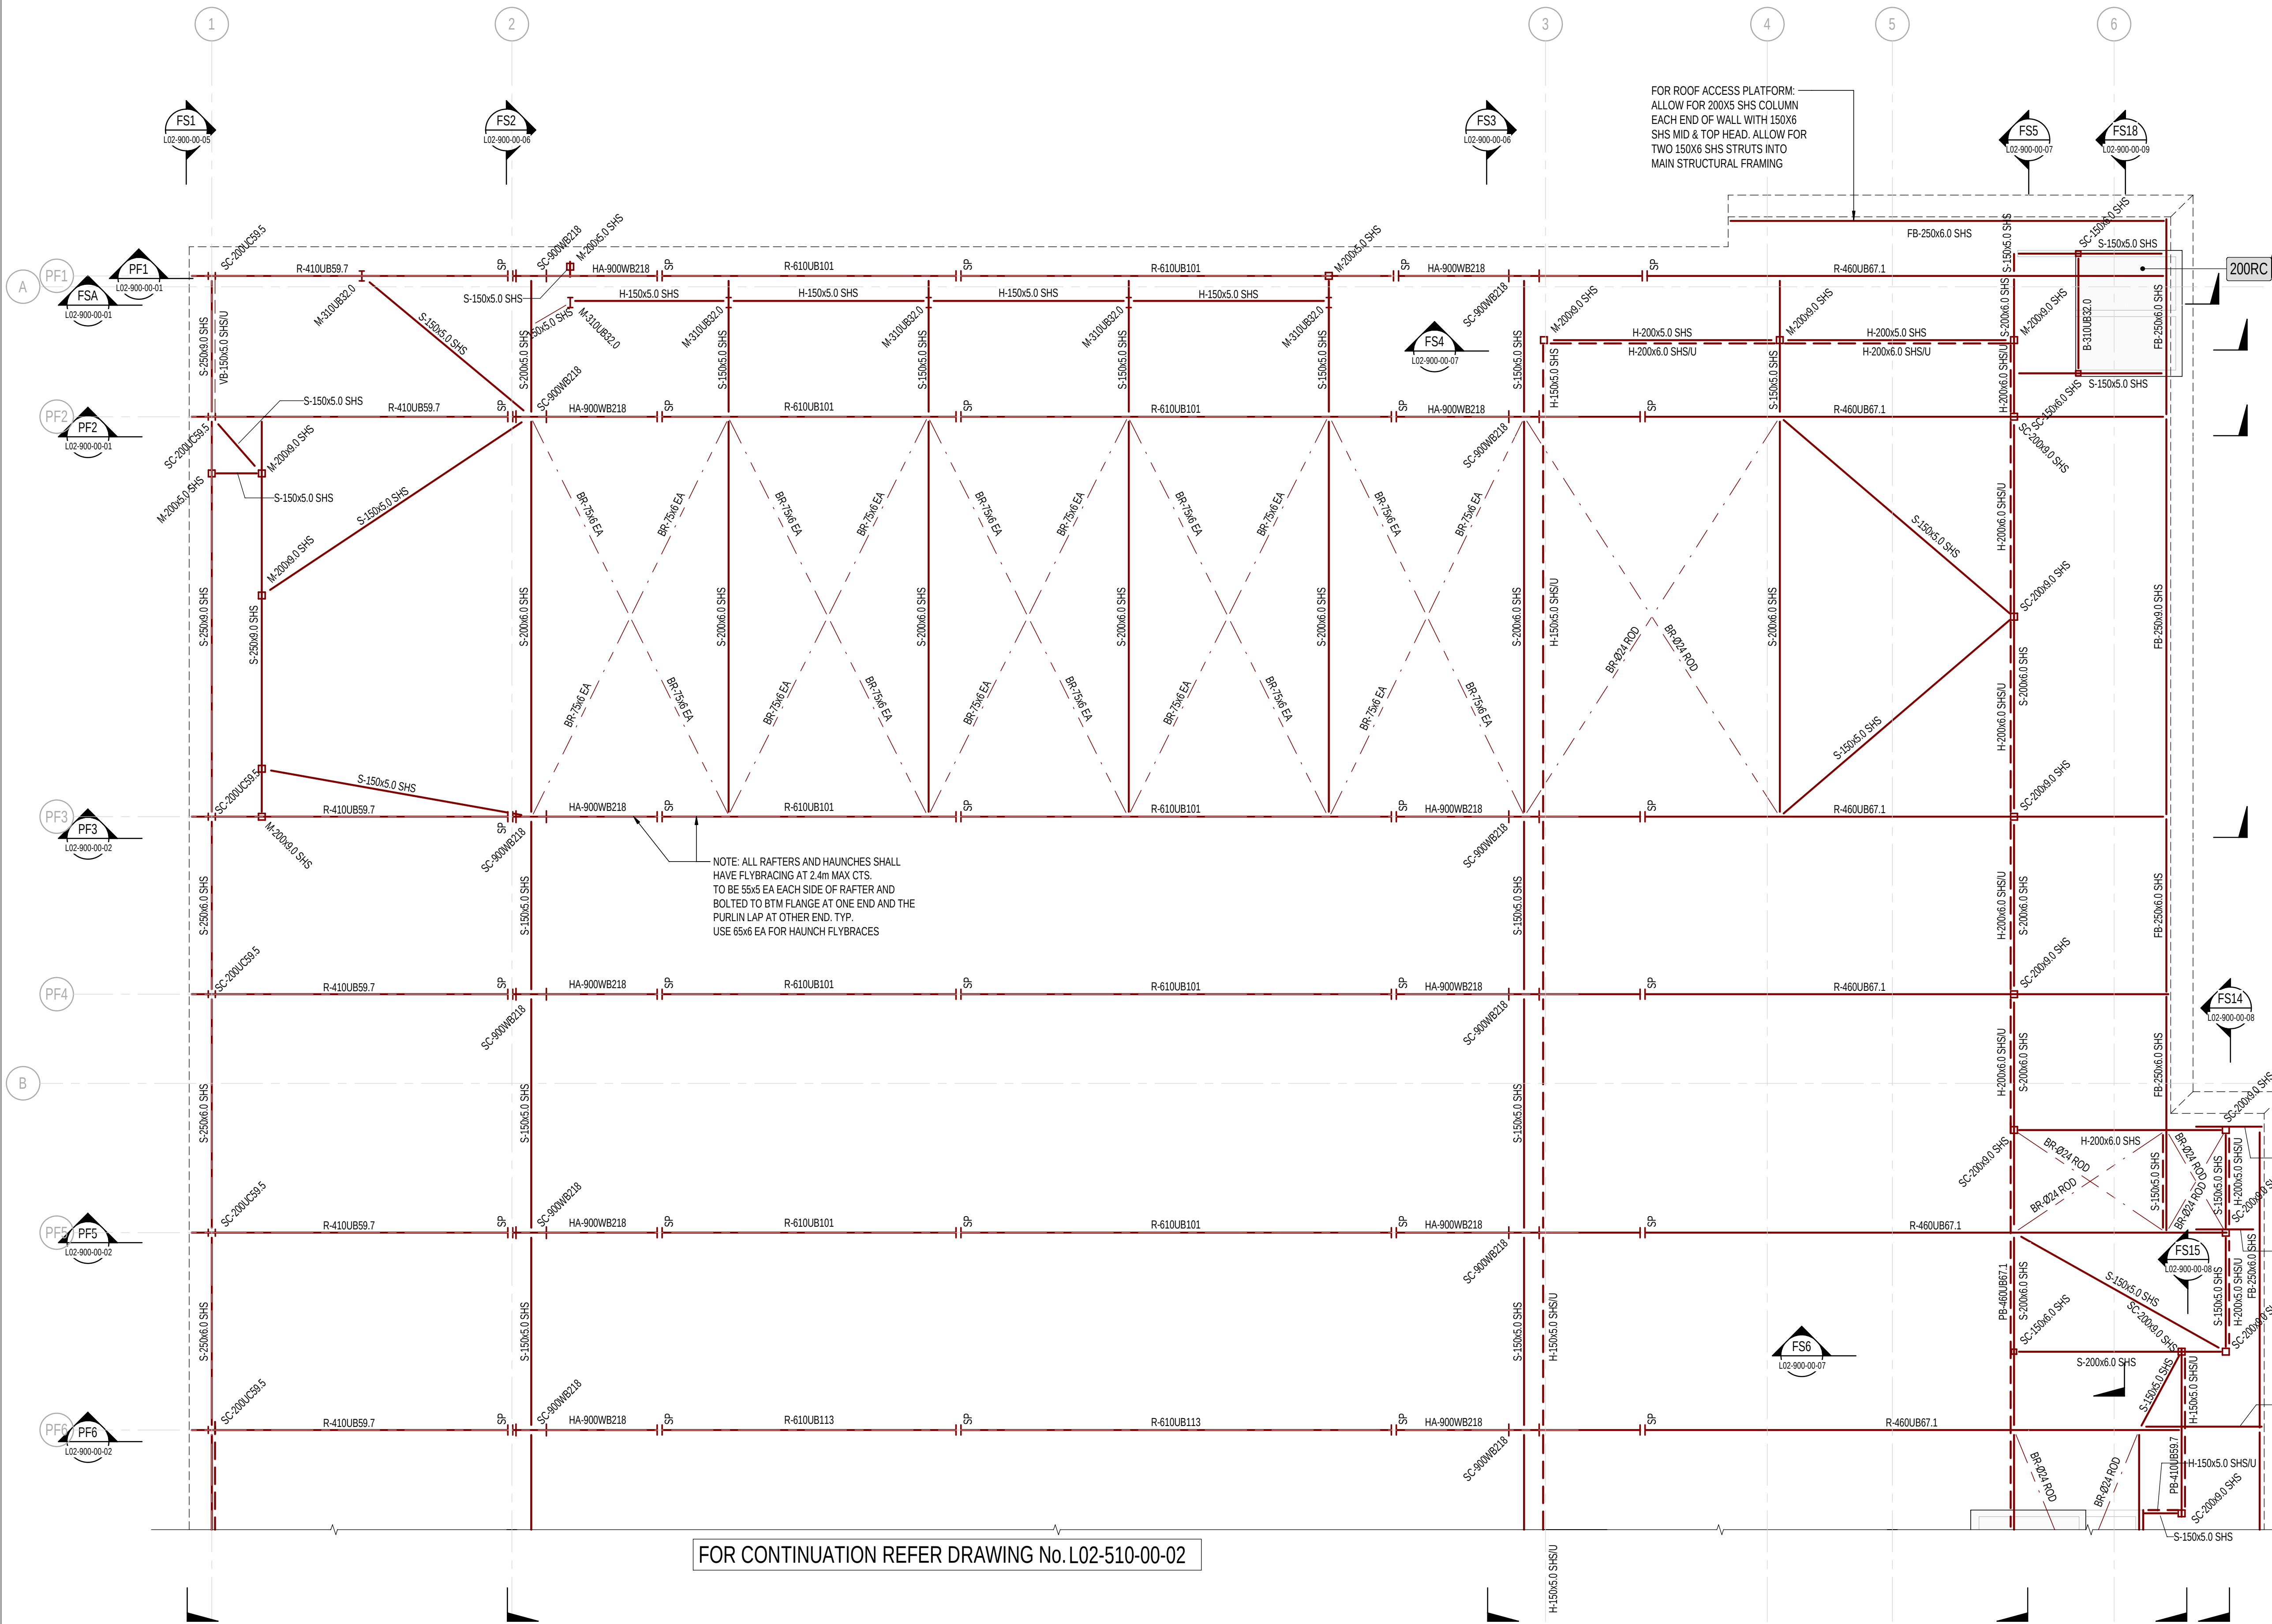

STEELWORK ROOF:

NOTES:

CONTRACTOR TO ALLOW FOR ADDITIONAL PURLIN SUPPORTS UNDER ALL GUTTERS.

CONTRACTOR TO ALLOW FOR ADDITIONAL TRIMMER PURLINS AROUND ALL VOIDS. REFER TO ARCHITECTURAL & SERVICES DRAWINGS FOR FULL EXTENT OF PENETRATIONS THROUGH ROOF.

REFER TO ARCHITECT FOR WATERPROOFING & SET-OUT DETAILS.

STEELWORK GENERAL:

NOTES:

READ IN CONJUNCTION WITH STEELWORK NOTES ON GENERAL NOTES DRAWING A00-0100-00-04.

STRUCTURAL PLANS SHOW PRIMARY STEELWORK & DOES NOT INCLUDE SECONDARY OR ARCHITECTURAL STEELWORK OUTSIDE THE STRUCTURAL SCOPE OF WORKS.

ALL PURLIN AND GIRT BRIDGING, NUMBER OF AND SETOUT, IN ACCORDANCE WITH MANUFACTURERS SPECIFICATIONS, UNLESS OTHERWISE NOTED.

ALL TENDERERS TO VISIT SITE & CONSIDER SITE ACCESS AND CONSTRAINTS IN THEIR SUBMISSIONS. ANY ADDITIONAL SPLICE LOCATIONS TO BE SUBMITTED TO THE STRUCTURAL ENGINEER, PRIOR TO FABRICATION, FOR REVIEW.

ALL EXPOSED STEELWORK TO BE HOT-DIP GALVANISED. ALL FIRE PROTECTION OF STEELWORK BY OTHERS.

CONTRACTOR TO ALLOW FOR CAST-IN PLATES AND CONNECTIONS AT ALL INTERFACES BETWEEN STEELWORK AND CONCRETE ELEMENTS.

STEEL BEAMS FOR OPERABLE WALLS AND ROOFS SHALL BE TAKEN AS SUGGESTIVE SUBJECT TO COORDINATION WITH SPECIALIST OPERABLE WALL MANUFACTURER. TOTAL WEIGHTS OF WALLS & DEFLECTION LIMITS OF SELECTED PRODUCTS SHALL BE CONFIRMED TO THE STRUCTURAL ENGINEER IN ORDER TO FINALISE DESIGN.

DESIGN ASSUMES TEMPORARY PROPPING OF STEELWORK. TEMPORARY PROPPING BY CONTRACTOR.

SERVICES ENGINEERS REQUIRED TO SUBMIT PROPOSED LOCATIONS OF ANY BEAM PENETRATIONS FOR STRUCTURAL ENGINEERS REVIEW. NO PENETRATIONS ARE PERMITTED THROUGH BEAMS UNTIL AGREED IN WRITING BY THE STRUCTURAL ENGINEER.

STEEL MEMBER MARKS:

PREFIX = MEMBER FUNCTION / DESCRIPTION.
REFER ABBREVIATIONS DRAWING A00-020-00-00 FOR SCHEDULE OF DESCRIPTIONS
MEMBER SIZE
SUFFIX = MEMBER POSITION (IF SHOWN)
REFER ABBREVIATIONS DRAWING A00-020-00-00 FOR SCHEDULE OF MEMBER POSITIONS

STEEL LEGEND:

SLAB THICKNESS AND REINFT. TYPE
RC = TRADITIONAL RC
DENOTES MOMENT SPLICE LOCATION & TYPE.
REFER DETAILS.

CRANE LOADING:

GANTRY CRANE OF 3.2T SWL IS SUPPORTED BY CRANE BEAMS DENOTED CB
WHEEL LOADS ASSUMED:
VERTICAL 40KN
LATERAL 7.2KN
BUFFER 40KN

FOR CONTINUATION REFER DRAWING No. L02-510-00-02

INFORMATION REFLECTED ON THIS DRAWING REPRESENTS STRUCTURAL DESIGN DEVELOPED FOR D&C TENDER ADVICE ONLY, AND SHOULD NOT BE REGARDED AS COMPLETE. THE D&C CONTRACTOR SHOULD REFER TO ALL ASSOCIATED ARCHITECTURAL AND OTHER DISCIPLINE DRAWINGS, PROJECT BRIEFS AND CLIENT REQUIREMENTS AND MAKE ADEQUATE ALLOWANCES FOR ALL NECESSARY STRUCTURAL WORKS TO MEET THESE REQUIREMENTS, EQUIPMENT SCHEDULES AND COMPLIANCE WITH THE NCC & APPROPRIATE AUSTRALIAN STANDARDS

A	12.02.2026	MSB	ISSUED FOR D&C TENDER	BM	DG
PI	30.01.2026	PJH	DRAFT 60% DD ISSUE FOR REVIEW	BM	DG
REV	DATE	BY	DESCRIPTION	CHK	APP
DRAWING STATUS:			DESIGN DEVELOPMENT		



http://www.wsp.com

CLIENT:
CQUniversity AUSTRALIA
ARCHITECT:
THOMSON ADSETT + PEDDLE THORP

PROJECT:
CQU ROCKHAMPTON TAFE CONSOLIDATION - STAGE 2
TITLE:
BuildingName
LEVEL 02 - ROOF FRAMING ARRANGEMENT PLAN - SHEET 01

SCALE @ A1: 1:100	CHECKED: BM	APPROVED: DG
PROJECT NUMBER: PS229518	DRAWN: PJH	DATE: 14.01.2026
DRAWING No: 92-ST-DR-L02-510-00-01		REV: A
© WSP Australia Pty Ltd		