


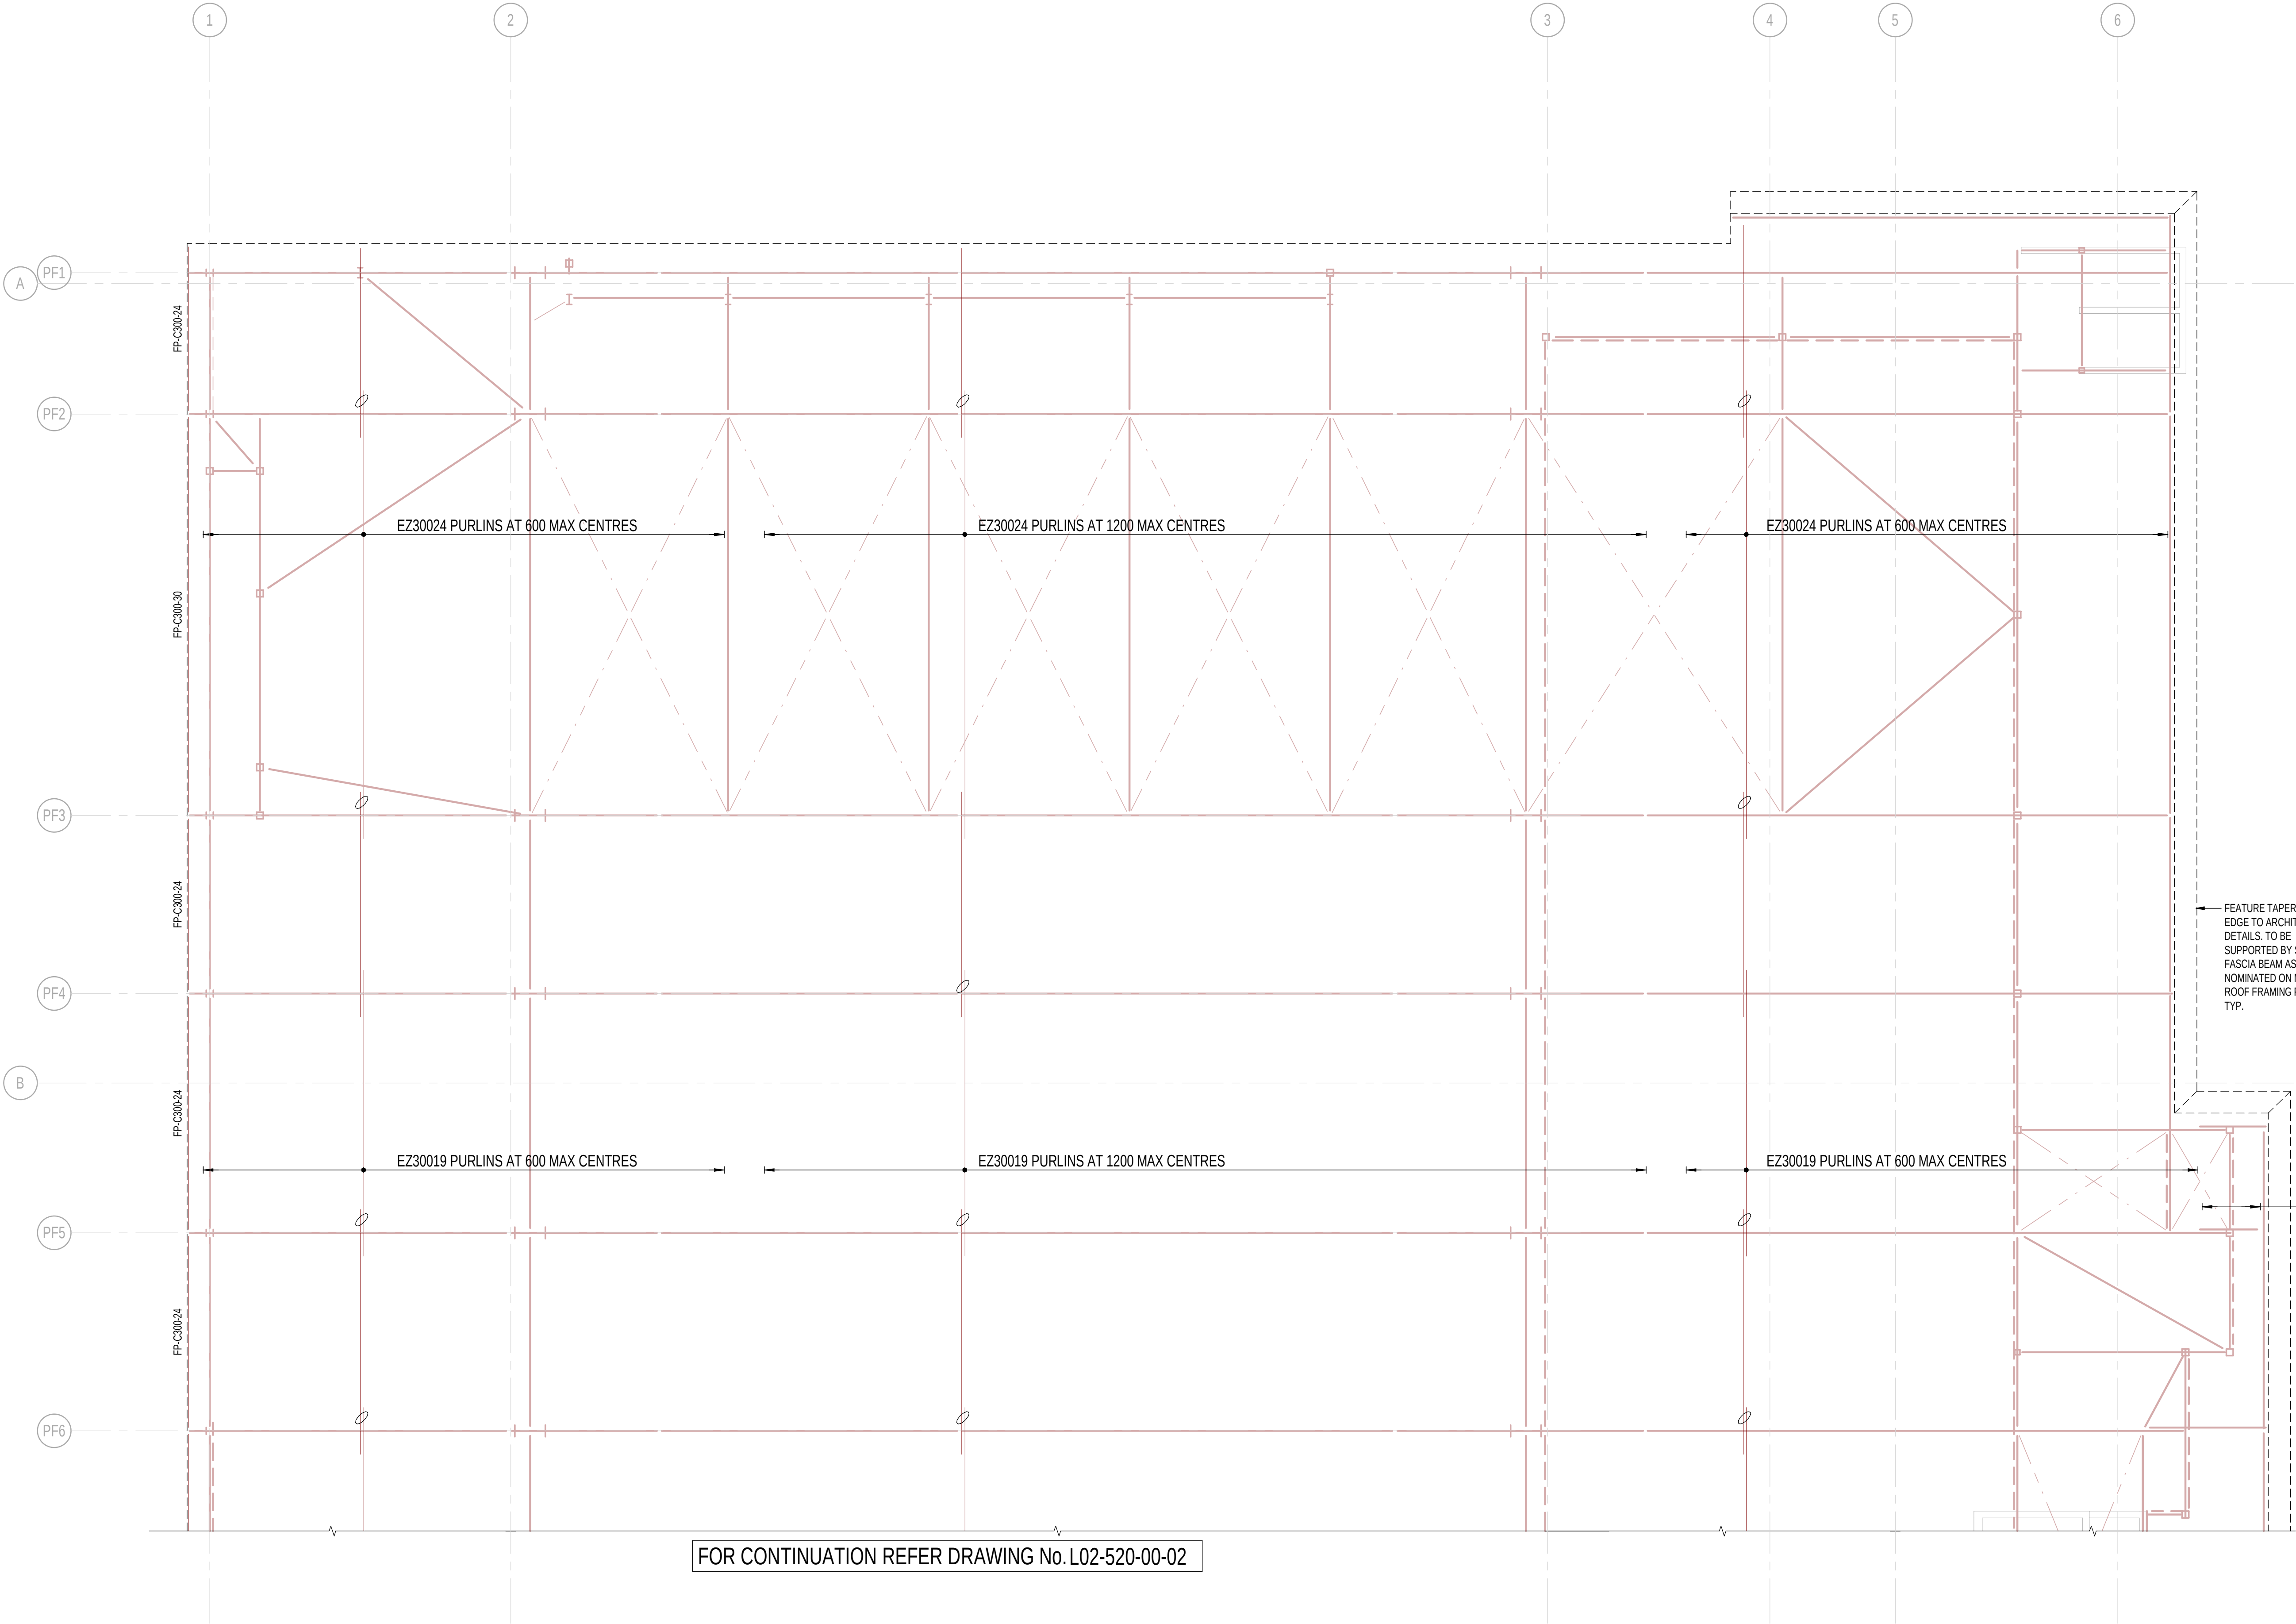

**STEELWORK ROOF:**

**NOTES:**  
CONTRACTOR TO ALLOW FOR ADDITIONAL PURLIN SUPPORTS UNDER ALL GUTTERS.  
CONTRACTOR TO ALLOW FOR ADDITIONAL TRIMMER PURLINS AROUND ALL VOIDS. REFER TO ARCHITECTURAL & SERVICES DRAWINGS FOR FULL EXTENT OF PENETRATIONS THROUGH ROOF.  
REFER TO ARCHITECT FOR WATERPROOFING & SET-OUT DETAILS.

**STEEL PURLINS:**

ALL Z PURLINS TO HAVE STRUCTURAL LAPS EQUAL TO NO LESS THAT 0.15% OF THE GREATEST SPAN  
INSTALL ALL PURLINS IN ACCORDANCE WITH MANUFACTURER DETAILS

**PURLIN BRIDGING:**

IF PURLIN SPAN <4M NO BRIDGING REQUIRED  
4M<SPAN<7M 1 ROW OF BRIDGING REQUIRED  
7M<SPAN<10M 2 ROWS BRIDGING  
SPAN>10M 3 ROWS BRIDGING

← FEATURE TAPERED ROOF  
EDGE TO ARCHITECT  
DETAILS. TO BE  
SUPPORTED BY SHS  
FASCIA BEAM AS  
NOMINATED ON MAIN  
ROOF FRAMING PLAN.  
TYP.

IN OVERHANG AREA  
WHERE PURLINS ARE  
SIMPLY SUPPORTED USE  
FOLLOWING:  
SPAN<=7000 EZ30019@  
600 CENTRES  
7000<SPAN<8000 EZ30024  
@600 CENTRES  
SPAN>8000 EZ30024@450  
CENTRES

FOR CONTINUATION REFER DRAWING No. L02-520-00-02

INFORMATION REFLECTED ON THIS DRAWING REPRESENTS STRUCTURAL DESIGN DEVELOPED FOR D&C TENDER ADVICE ONLY, AND SHOULD NOT BE REGARDED AS COMPLETE. THE D&C CONTRACTOR SHOULD REFER TO ALL ASSOCIATED ARCHITECTURAL AND OTHER DISCIPLINE DRAWINGS, PROJECT BRIEFS AND CLIENT REQUIREMENTS AND MAKE ADEQUATE ALLOWANCES FOR ALL NECESSARY STRUCTURAL WORKS TO MEET THESE REQUIREMENTS, EQUIPMENT SCHEDULES AND COMPLIANCE WITH THE NCC & APPROPRIATE AUSTRALIAN STANDARDS

|                                    |            |     |                               |  |  |         |
|------------------------------------|------------|-----|-------------------------------|--|--|---------|
|                                    |            |     |                               |  |  |         |
|                                    |            |     |                               |  |  |         |
|                                    |            |     |                               |  |  |         |
| A                                  | 12.02.2026 | MSB | ISSUED FOR D&C TENDER         |  |  | BM DG   |
| P1                                 | 30.01.2026 | PJH | DRAFT 60% DD ISSUE FOR REVIEW |  |  | BM DG   |
| REV                                | DATE       | BY  | DESCRIPTION                   |  |  | CHK APP |
| DRAWING STATUS: DESIGN DEVELOPMENT |            |     |                               |  |  |         |



<http://www.wsp.com>

CLIENT:



ARCHITECT:

THOMSON ADSETT + PEDDLE THORP

PROJECT:

CQU ROCKHAMPTON TAFE  
CONSOLIDATION - STAGE 2

TITLE:

BuildingName  
LEVEL 02 - ROOF PURLIN ARRANGEMENT PLAN -  
SHEET 01

SCALE @ A1:

1:100

CHECKED:

BM

APPROVED:

DG

PROJECT NUMBER:

PS229518

DRAWN:

PJH

DATE:

14.01.2026

DRAWING No:

92-ST-DR-L02-520-00-01

REV:

A

© WSP Australia Pty Ltd