DO NOT SCALE

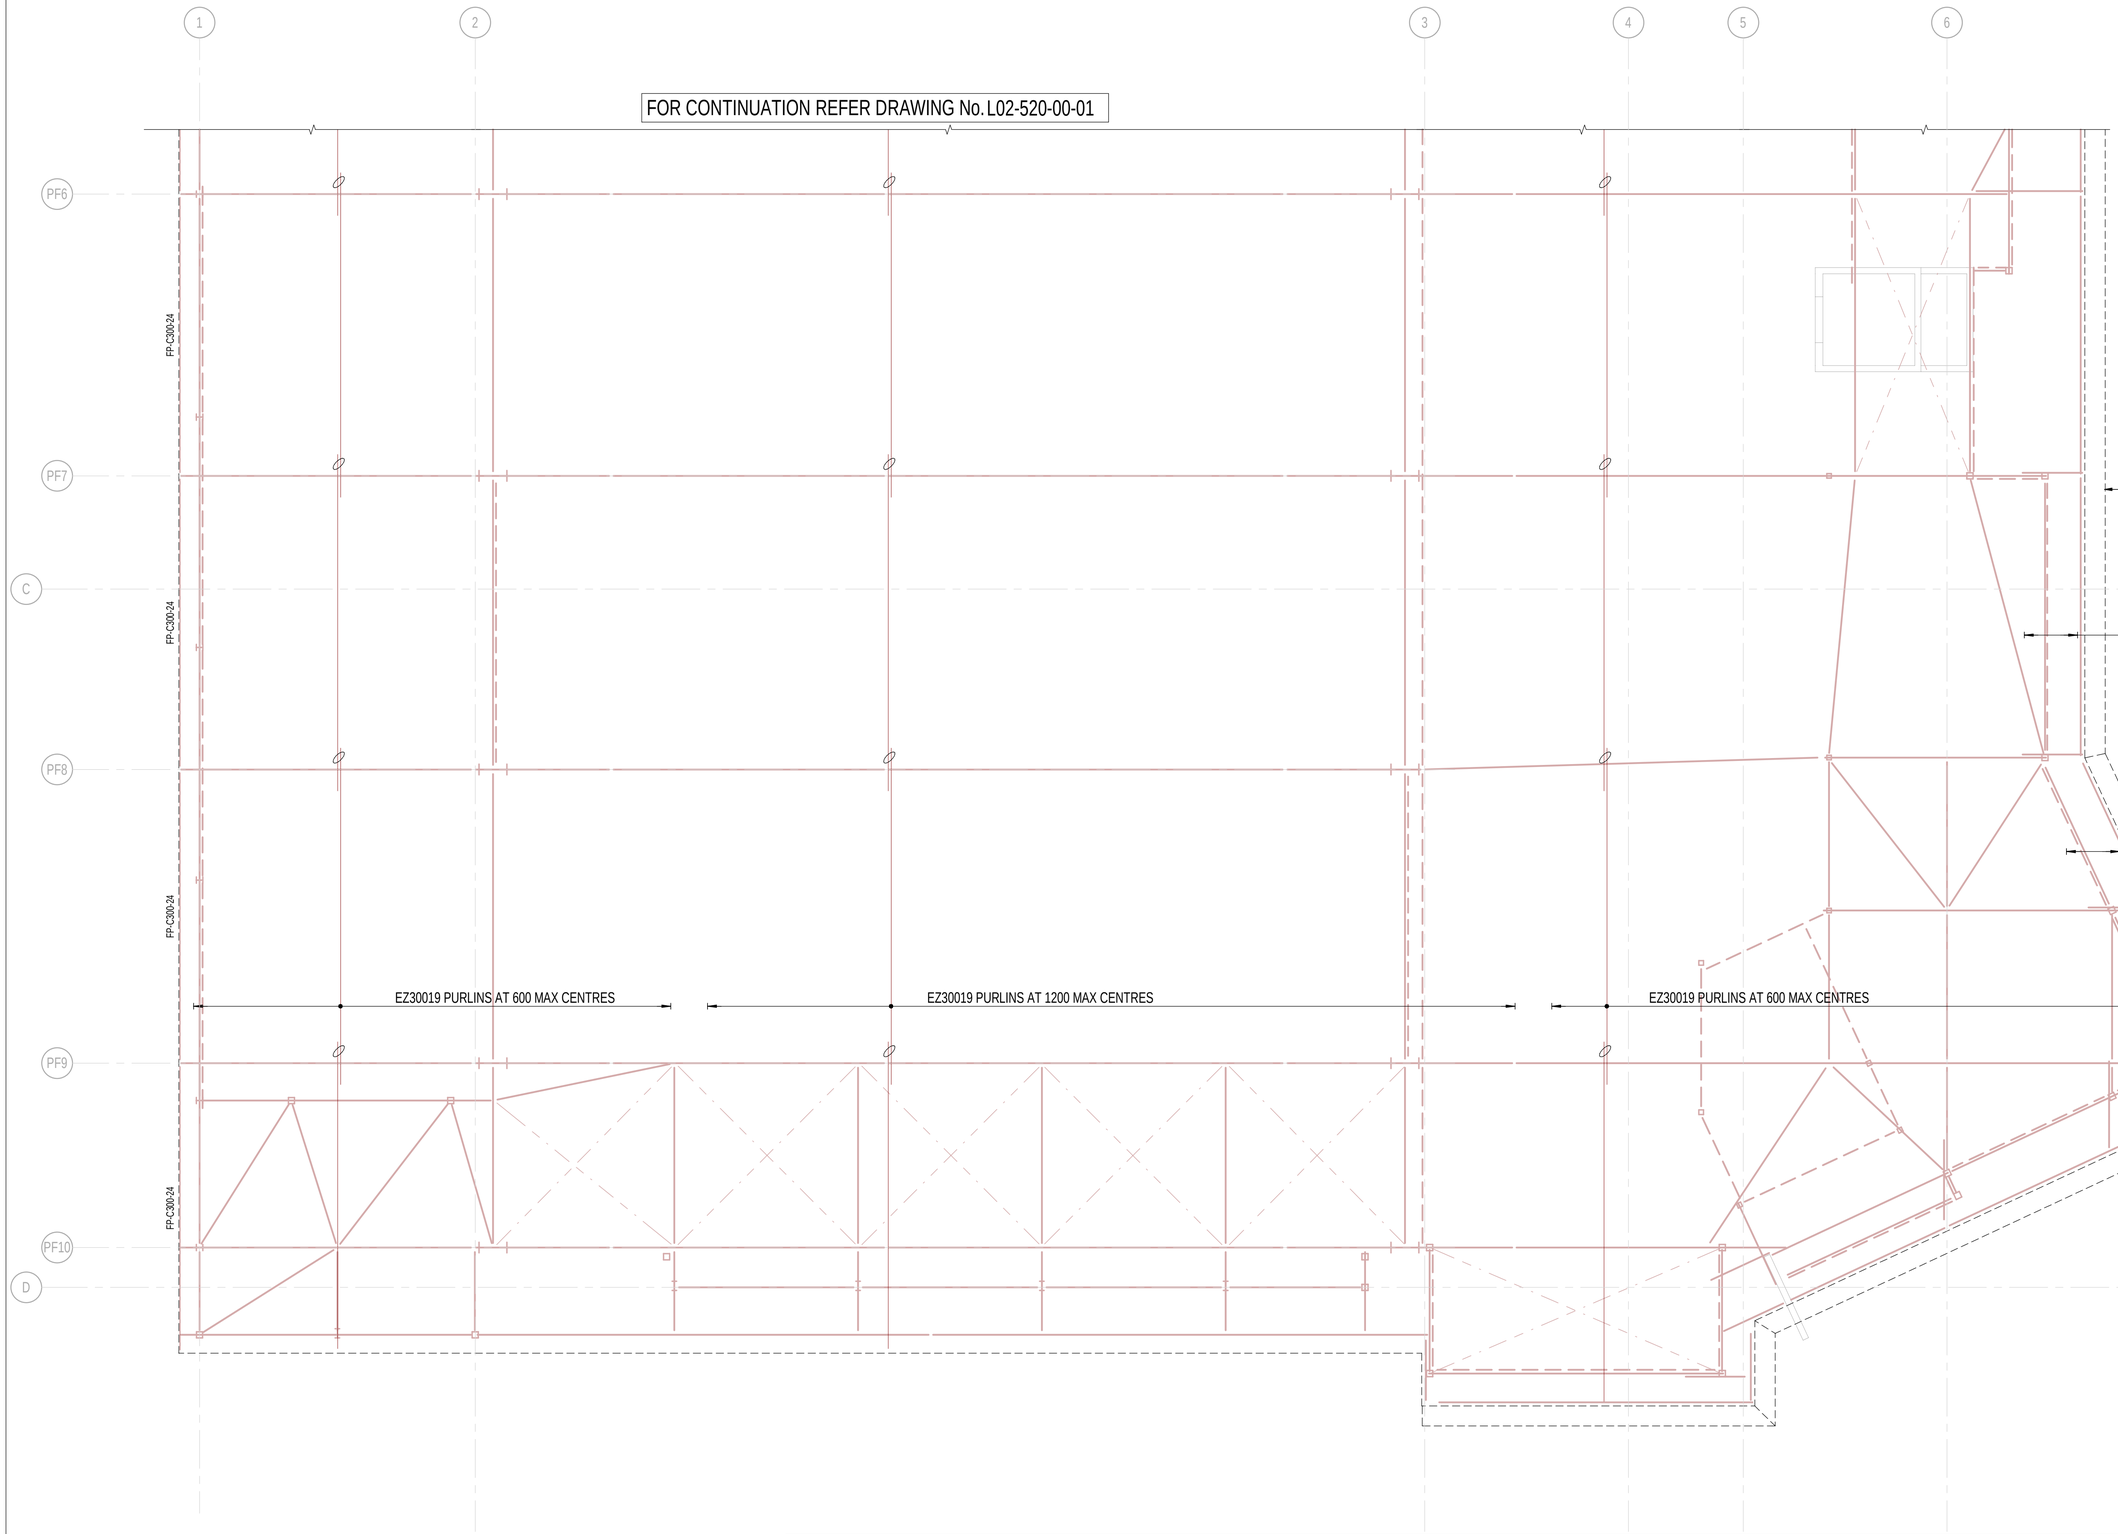

STEELWORK ROOF:

NOTES:

CONTRACTOR TO ALLOW FOR ADDITIONAL PURLIN SUPPORTS UNDER ALL GUTTERS.

CONTRACTOR TO ALLOW FOR ADDITIONAL TRIMMER PURLINS AROUND ALL VOIDS. REFER TO ARCHITECTURAL & SERVICES DRAWINGS FOR FULL EXTENT OF PENETRATIONS THROUGH ROOF.

REFER TO ARCHITECT FOR WATERPROOFING & SET-OUT DETAILS.

STEEL PURLINS:

ALL Z PURLINS TO HAVE STRUCTURAL LAPS EQUAL TO NO LESS THAT 0.15% OF THE GREATEST SPAN
INSTALL ALL PURLINS IN ACCORDANCE WITH MANUFACTURER DETAILS

PURLIN BRIDGING:

IF PURLIN SPAN <4M NO BRIDGING REQUIRED
4M<SPAN<7M 1 ROW OF BRIDGING REQUIRED
7M<SPAN<10M 2 ROWS BRIDGING
SPAN>10M 3 ROWS BRIDGING

INFORMATION REFLECTED ON THIS DRAWING REPRESENTS STRUCTURAL DESIGN DEVELOPED FOR D&C TENDER ADVICE ONLY, AND SHOULD NOT BE REGARDED AS COMPLETE. THE D&C CONTRACTOR SHOULD REFER TO ALL ASSOCIATED ARCHITECTURAL AND OTHER DISCIPLINE DRAWINGS, PROJECT BRIEFS AND CLIENT REQUIREMENTS AND MAKE ADEQUATE ALLOWANCES FOR ALL NECESSARY STRUCTURAL WORKS TO MEET THESE REQUIREMENTS, EQUIPMENT SCHEDULES AND COMPLIANCE WITH THE NCC & APPROPRIATE AUSTRALIAN STANDARDS

REV	DATE	BY	DESCRIPTION	CHK	APP
A	12.02.2026	MSB	ISSUED FOR D&C TENDER	BM	DG
P1	30.01.2026	PJH	DRAFT 60% DD ISSUE FOR REVIEW	BM	DG

DRAWING STATUS: DESIGN DEVELOPMENT

wsp
http://www.wsp.com

CLIENT: CQUniversity AUSTRALIA

ARCHITECT: THOMSON ADSETT + PEDDLE THORP

PROJECT: CQU ROCKHAMPTON TAFE CONSOLIDATION - STAGE 2

TITLE: BuildingName
LEVEL 02 - ROOF PURLIN ARRANGEMENT PLAN - SHEET 02

SCALE @ A1:	CHECKED:	APPROVED:
1:100	BM	DG
PROJECT NUMBER:	DRAWN:	DATE:
PS229518	PJH	14.01.2026

DRAWING No: 92-ST-DR-L02-520-00-02 REV: A

© WSP Australia Pty Ltd

DRAWING CREATED IN REVIT.