


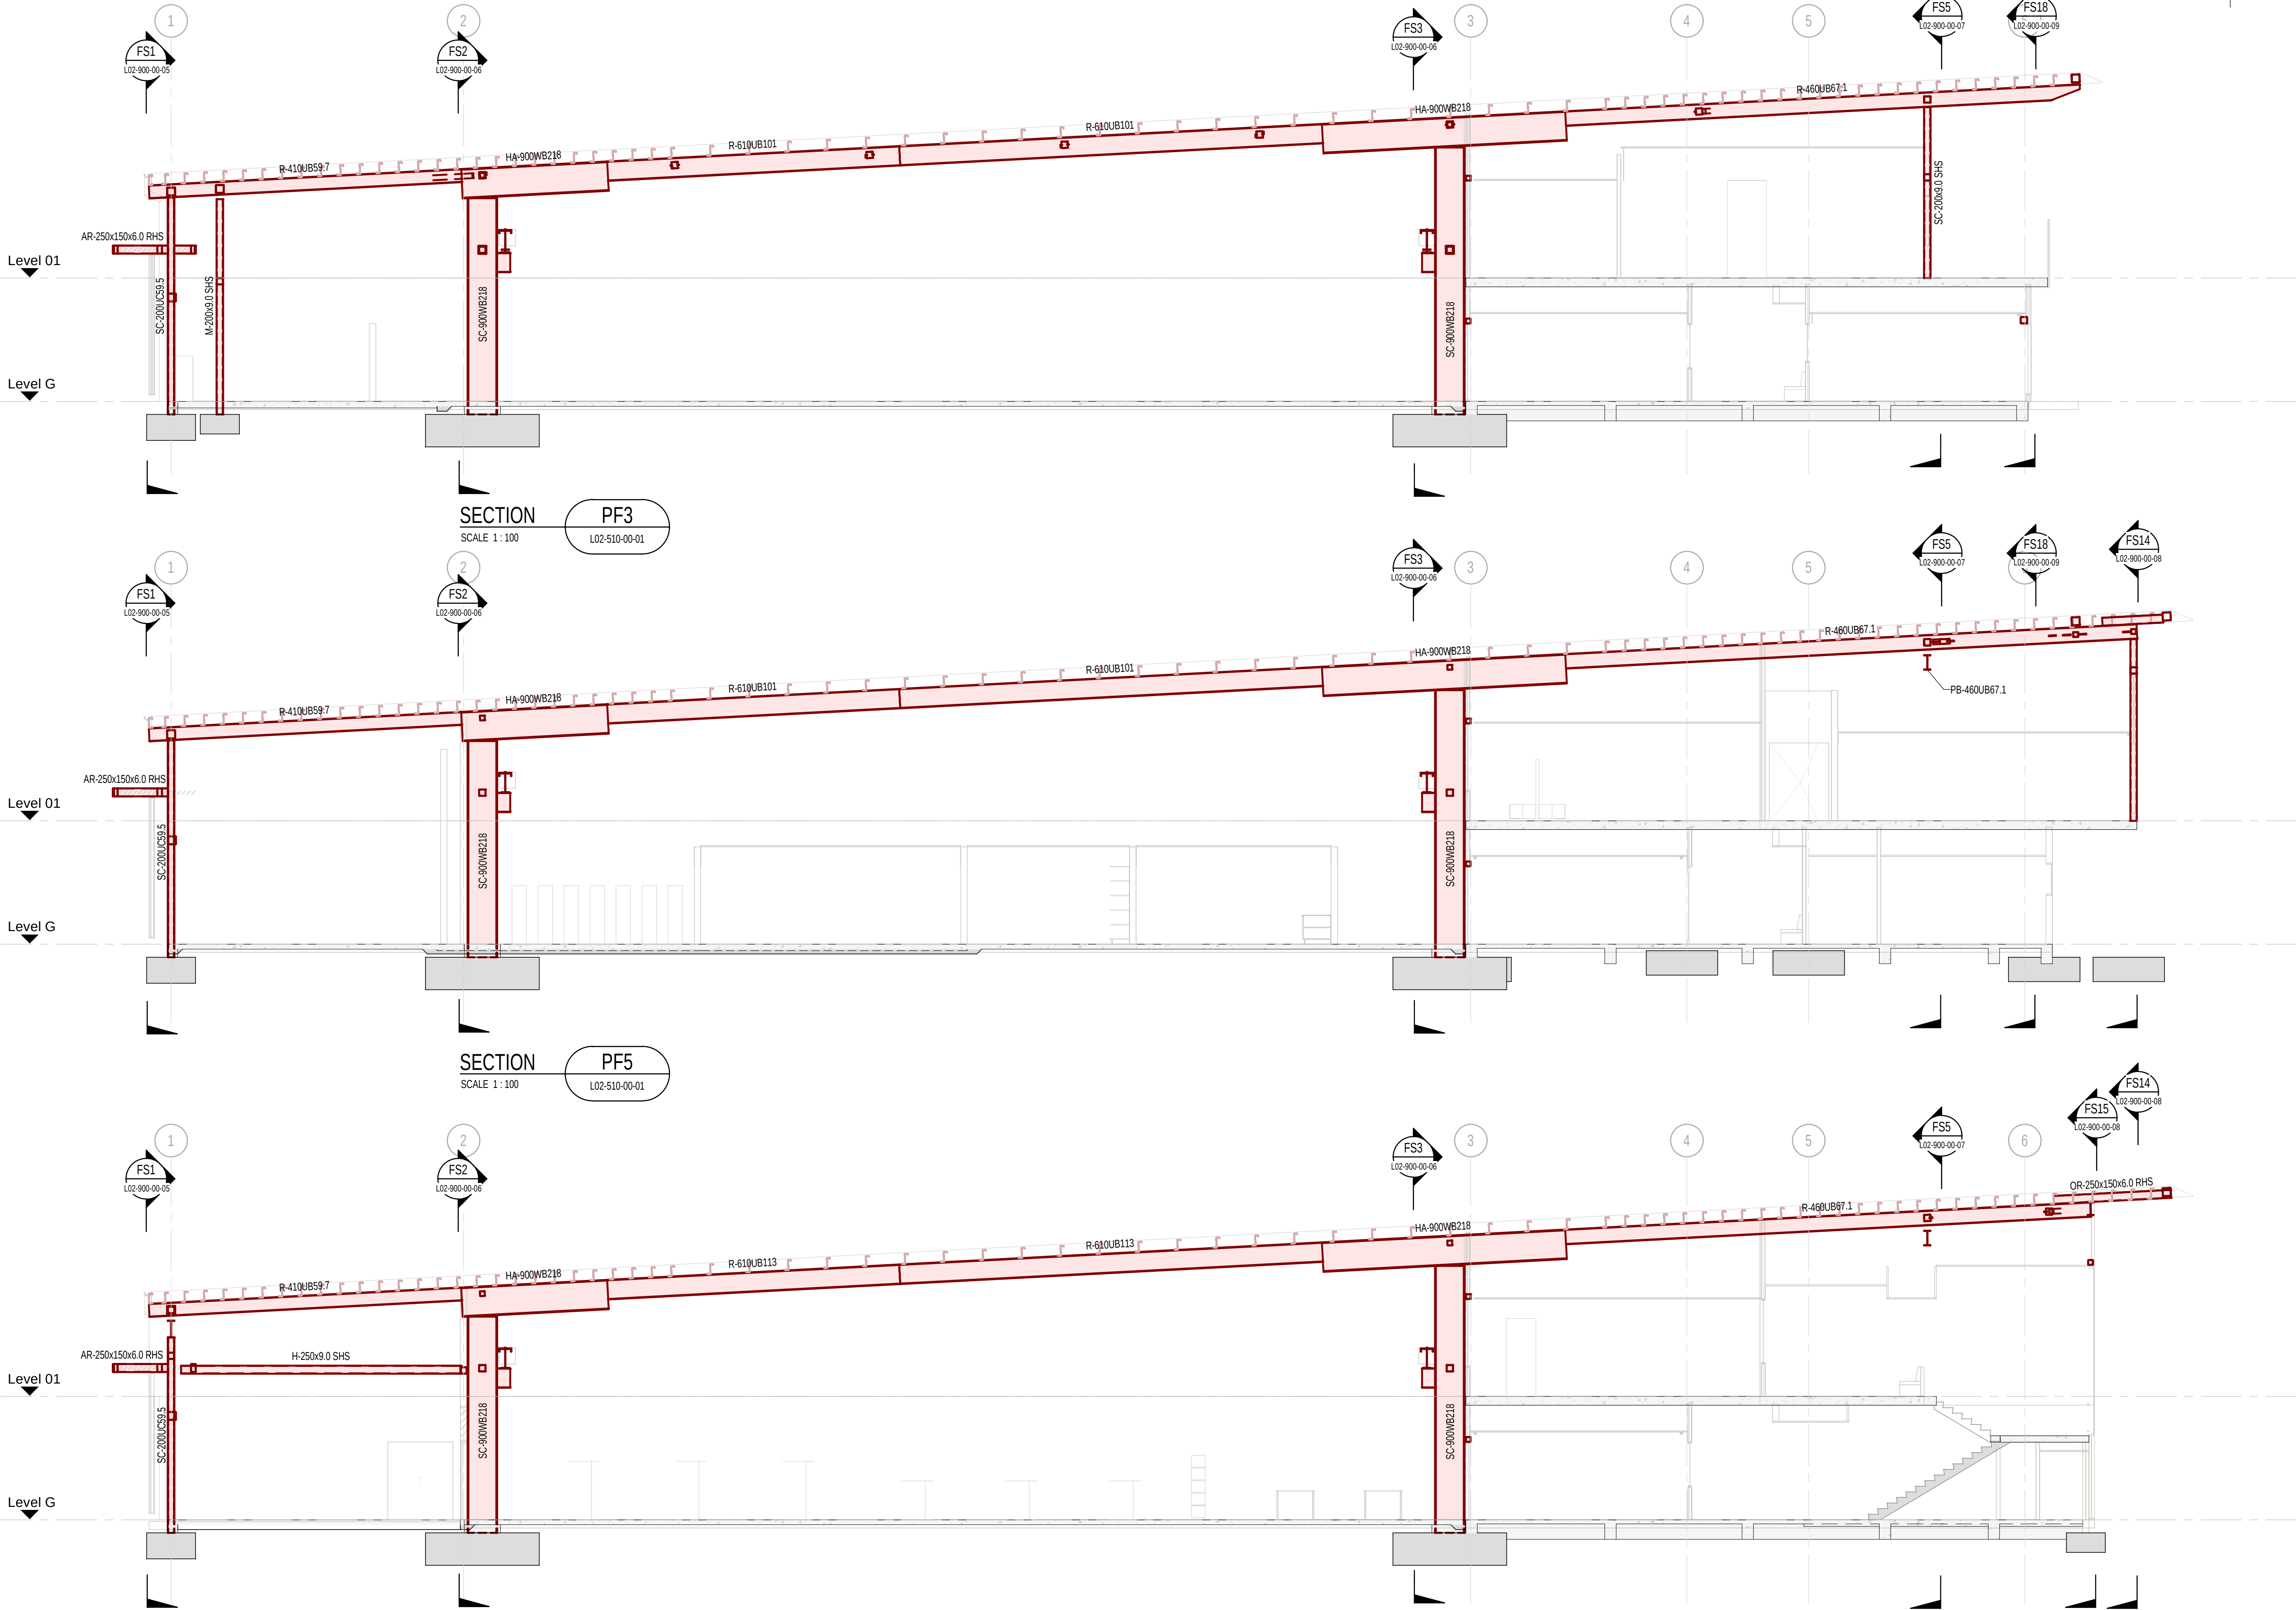

SECTION
SCALE 1:100

PF6

L02-510-00-01

INFORMATION REFLECTED ON THIS DRAWING REPRESENTS STRUCTURAL DESIGN DEVELOPED FOR D&C TENDER ADVICE ONLY, AND SHOULD NOT BE REGARDED AS COMPLETE. THE D&C CONTRACTOR SHOULD REFER TO ALL ASSOCIATED ARCHITECTURAL AND OTHER DISCIPLINE DRAWINGS, PROJECT BRIEFS AND CLIENT REQUIREMENTS AND MAKE ADEQUATE ALLOWANCES FOR ALL NECESSARY STRUCTURAL WORKS TO MEET THESE REQUIREMENTS, EQUIPMENT SCHEDULES AND COMPLIANCE WITH THE NCC & APPROPRIATE AUSTRALIAN STANDARDS

DRAWING STATUS:		DESIGN DEVELOPMENT					
REV	DATE	BY	DESCRIPTION	CHK	APP	BM	DG
A	12.02.2026	MSB	ISSUED FOR D&C TENDER			BM	DG
P1	30.01.2026	PJH	DRAFT 60% DD ISSUE FOR REVIEW			BM	DG



<http://www.wsp.com>

CLIENT:



THOMSON ADSETT + PEDDLE THORP

ARCHITECT:

PROJECT:

CQU ROCKHAMPTON TAFE
CONSOLIDATION - STAGE 2

TITLE:

BuildingName
LEVEL 02 - FRAMING SECTIONS - SHEET 02

SCALE @ A1:

1:100

CHECKED:

BM

APPROVED:

DG

PROJECT NUMBER:

PS229518

DRAWN:

PJH

DATE:

14.01.2016

DRAWING No:

92-ST-DR-L02-900-00-02

REV:

A

© WSP Australia Pty Ltd