




DO NOT SCALE

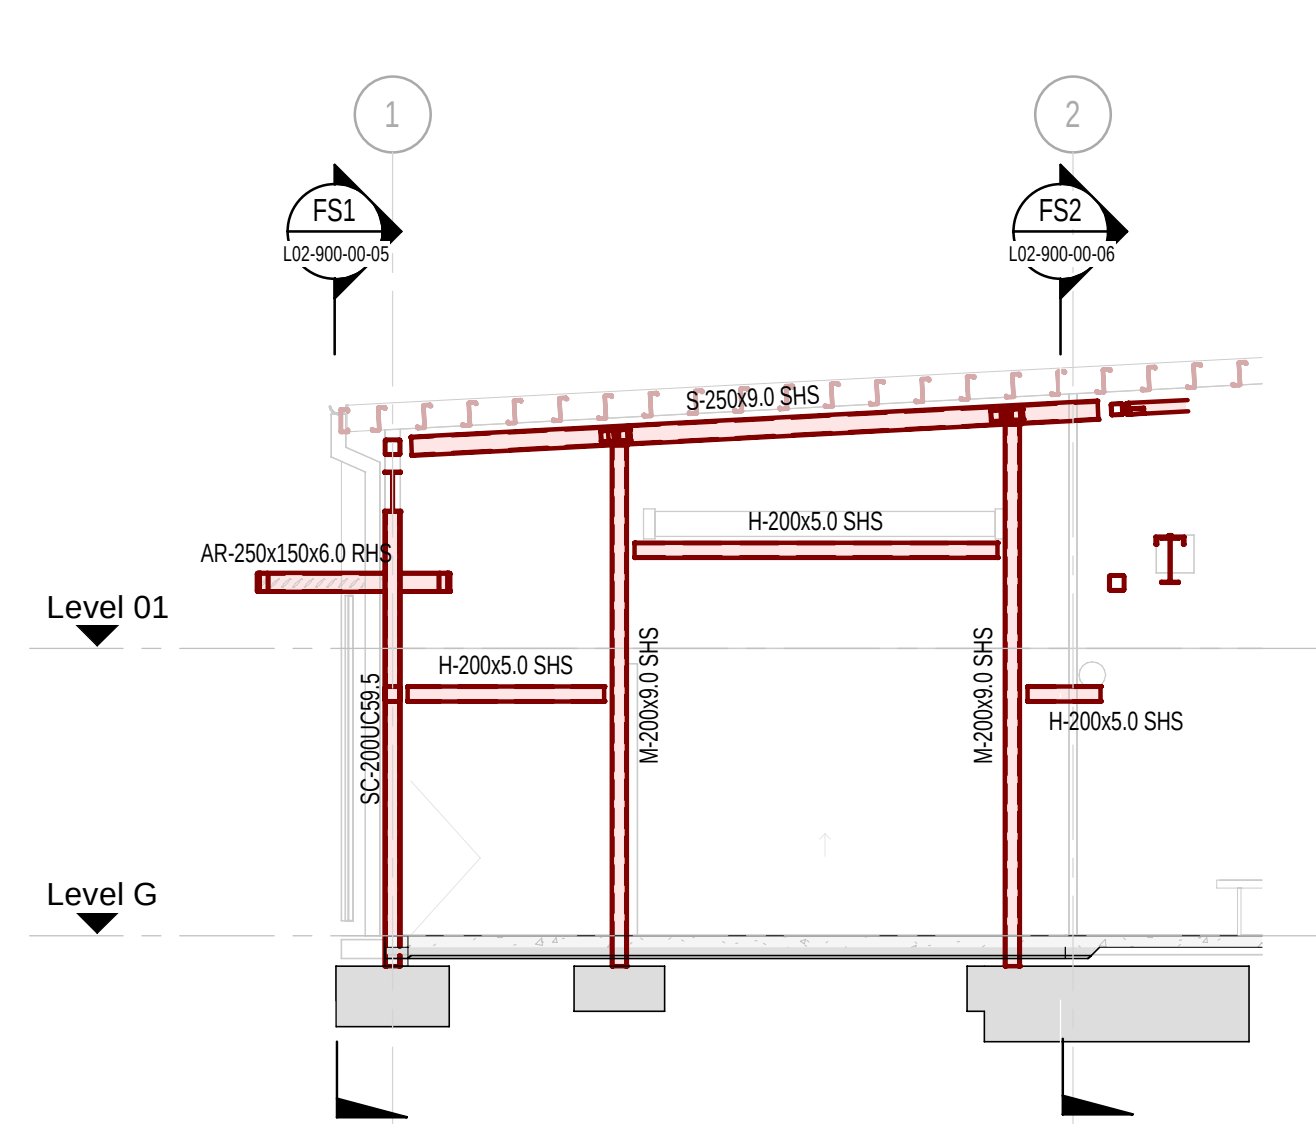


SECTION FS16
SCALE 1 : 100 L02-510-00-02

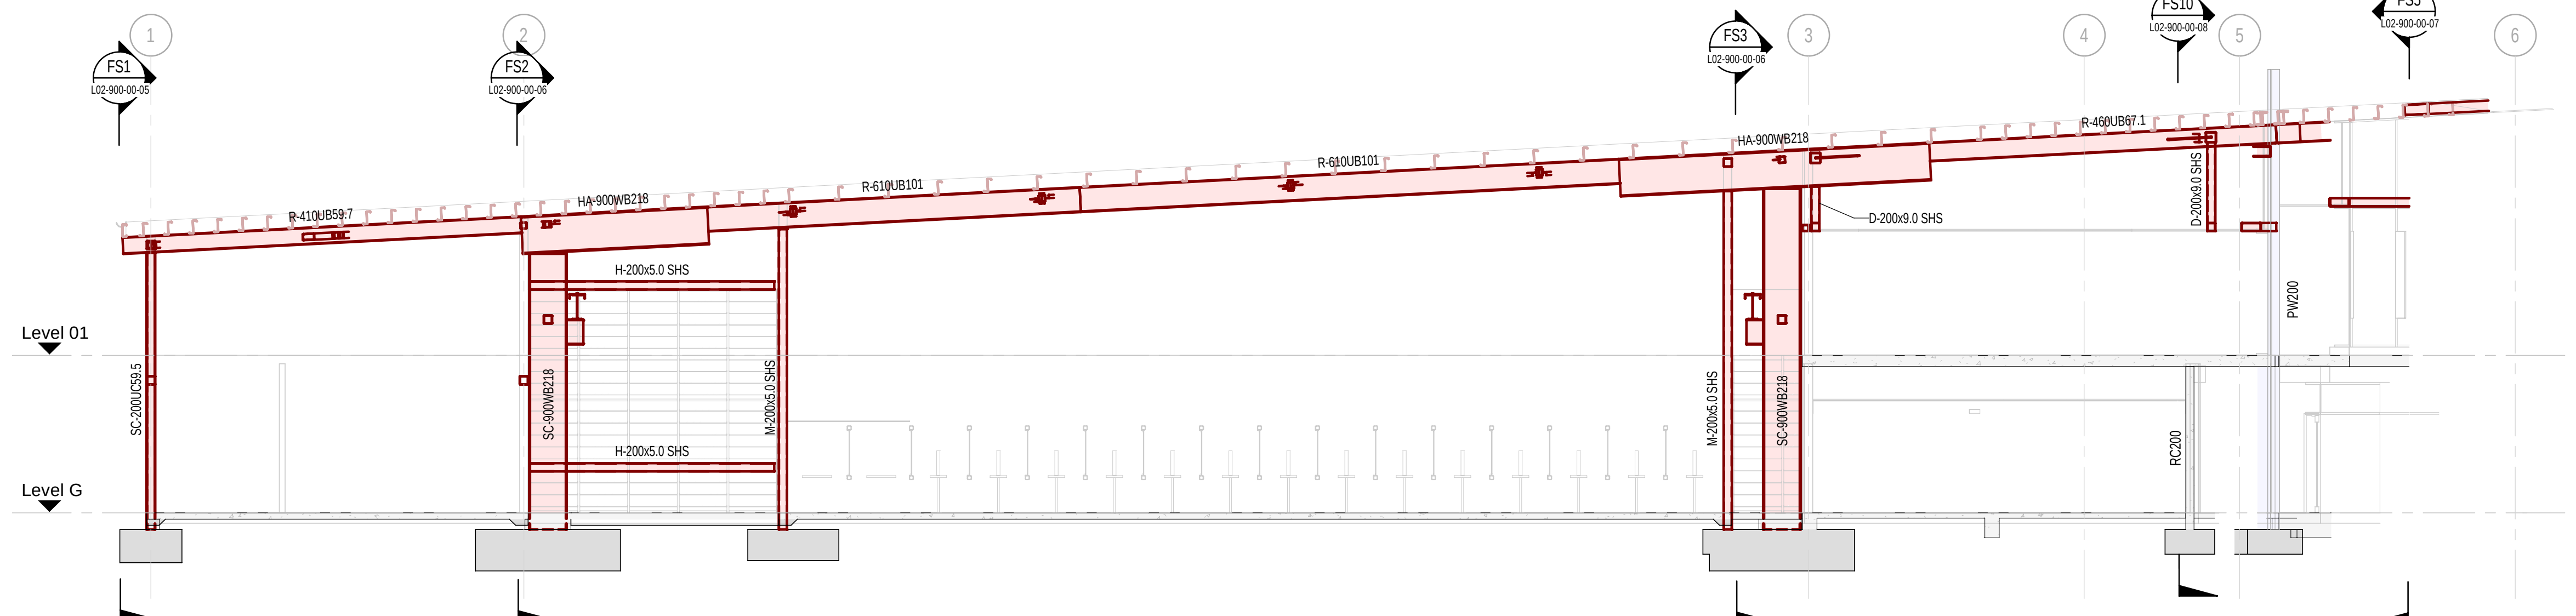

SECTION PF10
SCALE 1:100 102-510-00-02

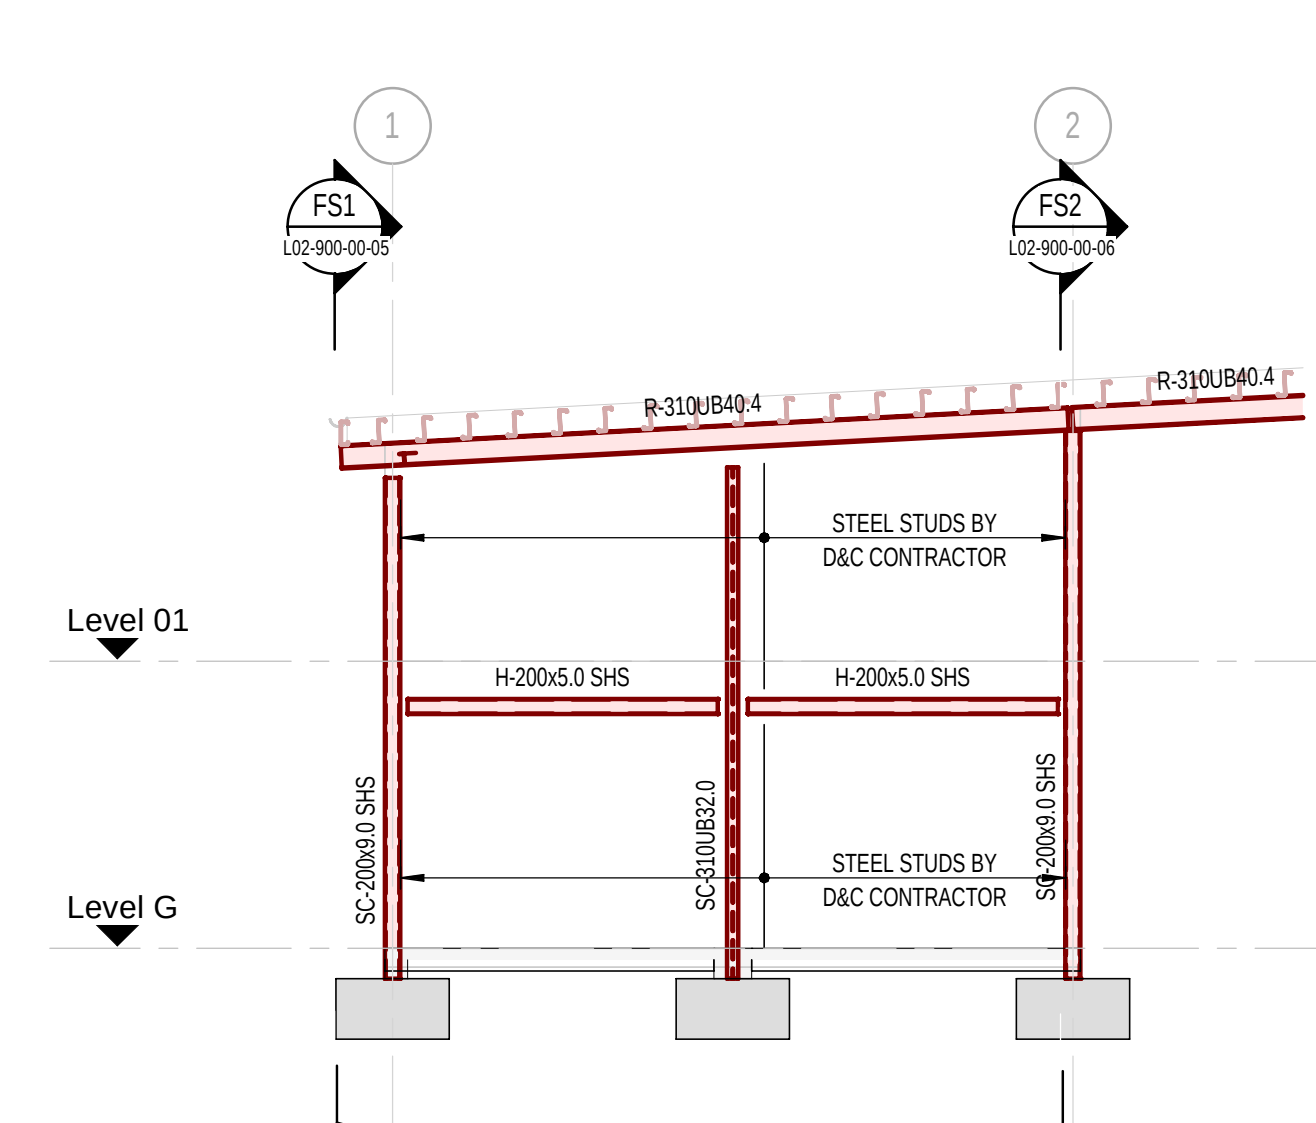

SECTION FS17
SCALE 1 : 100 L02-510-00-02

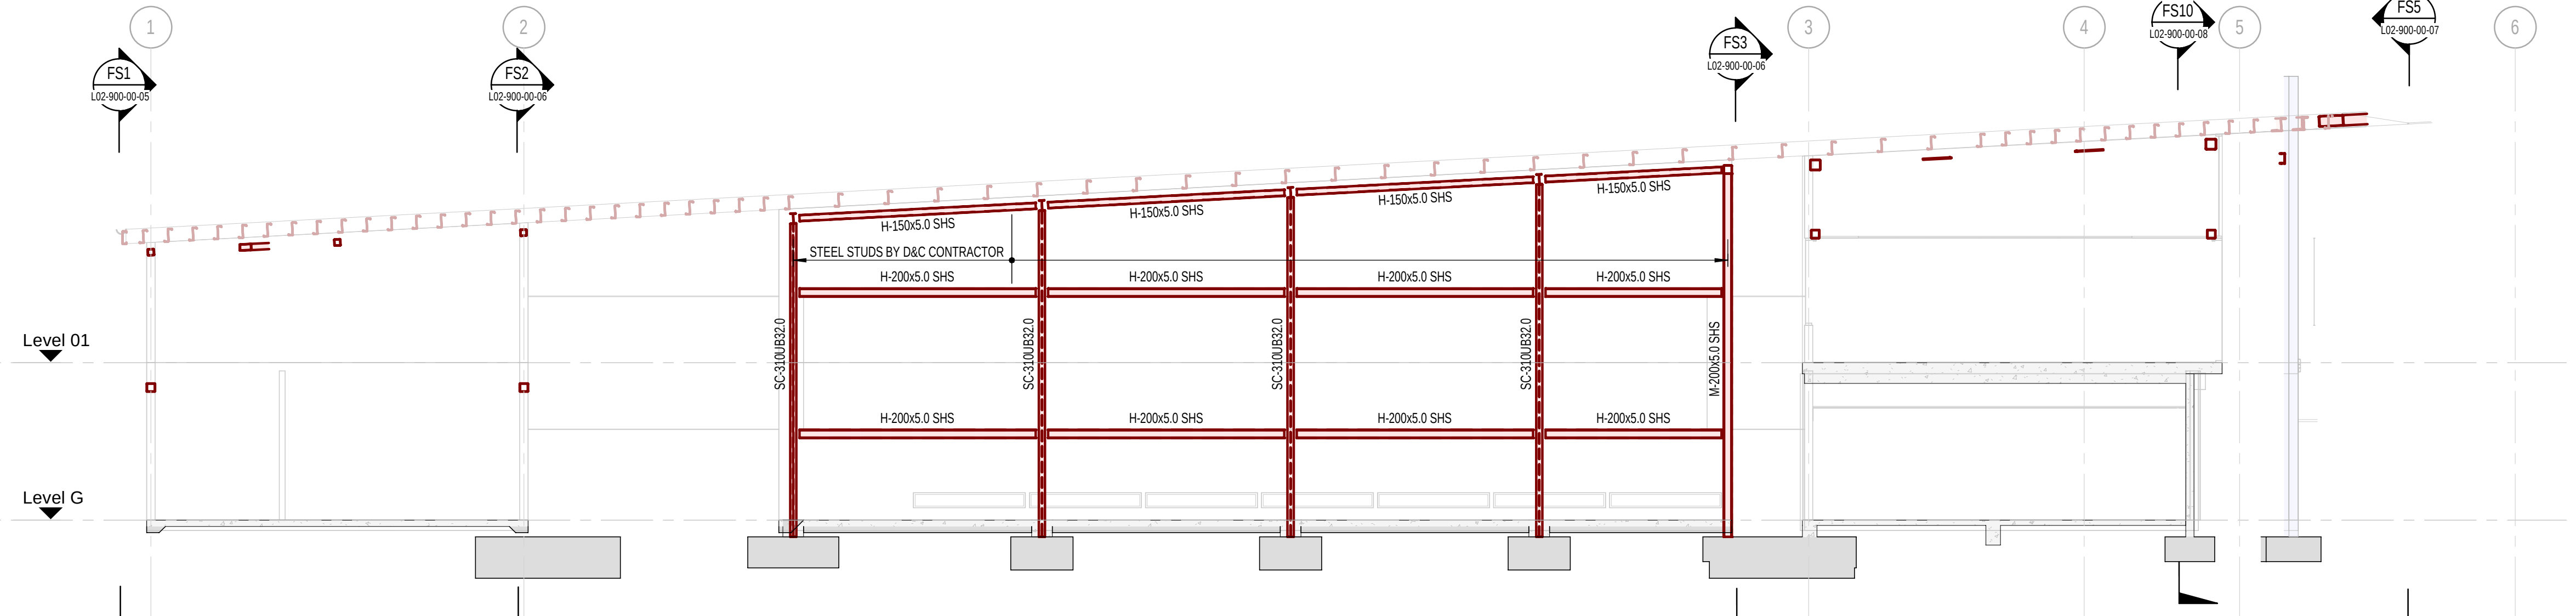

SECTION FSD
SCALE 1:100 L02-510-00-02

INFORMATION REFLECTED ON THIS DRAWING REPRESENTS STRUCTURAL DESIGN DEVELOPED FOR D&C TENDER ADVISE ONLY, AND SHOULD NOT BE REGARDED AS COMPLETE. THE D&C CONTRACTOR SHOULD REFER TO ALL ASSOCIATED ARCHITECTURAL AND OTHER DISCIPLINE DRAWINGS, PROJECT BRIEFS AND CLIENT REQUIREMENTS AND MAKE ADEQUATE ALLOWANCES FOR ALL NECESSARY STRUCTURAL WORKS TO MEET THESE REQUIREMENTS, EQUIPMENT SCHEDULES AND COMPLIANCE WITH THE NCC & APPROPRIATE AUSTRALIAN STANDARDS

A	12.02.2026	MSE	ISSUED FOR DAC TENDER		BM	DC
P1	30.01.2026	PJH	DRAFT 60% DD ISSUE FOR REVIEW		BM	DG
REV	DATE	BY	DESCRIPTION		CHK	APP

DRAWING STATUS:

DESIGN DEVELOPMENT



<http://www.wsp.com>

CLIENT



THOMSON ADSETT + PEDDLE THORP

PROJECT:

CQU ROCKHAMPTON TAFE
CONSOLIDATION - STAGE 2

	TITLE-
--	--------

BuildingName
LEVEL 02 - FRAMING SECTIONS - SHEET 04

SCALE @ A1:

1:100

BM

DRAWN:

PROVED:

DG

TE: _____

DRAWING No:

92-ST-DR-L02-900-00-04

EV:

A

© WSP Australia Pty Ltd