



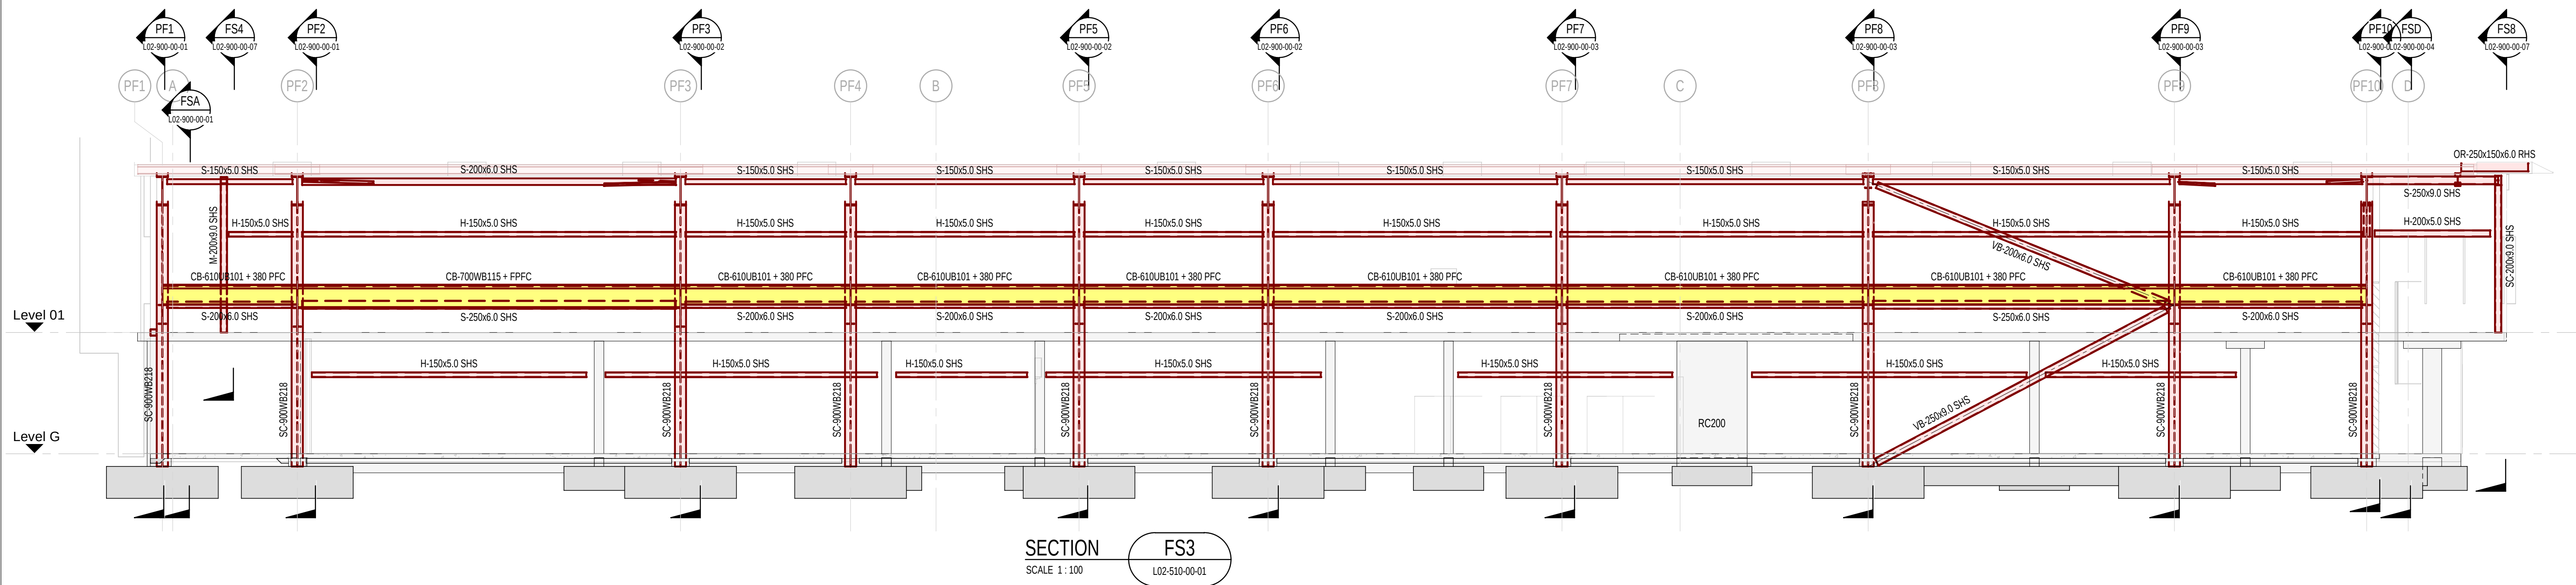

INFORMATION REFLECTED ON THIS DRAWING REPRESENTS STRUCTURAL DESIGN DEVELOPED FOR D&C TENDER ADVISE ONLY, AND SHOULD NOT BE REGARDED AS COMPLETE. THE D&C CONTRACTOR SHOULD REFER TO ALL ASSOCIATED ARCHITECTURAL AND OTHER DISCIPLINE DRAWINGS, PROJECT BRIEFS AND CLIENT REQUIREMENTS AND MAKE ADEQUATE ALLOWANCES FOR ALL NECESSARY STRUCTURAL WORKS TO MEET THESE REQUIREMENTS, EQUIPMENT SCHEDULES AND COMPLIANCE WITH THE NCC & APPROPRIATE AUSTRALIAN STANDARDS

A	12.02.2026	M5B	ISSUED FOR DAC TENDER		BM	DC
P1	30.01.2026	P3H	DRAFT 60% DD ISSUE FOR REVIEW		BM	DG
REV	DATE	BY	DESCRIPTION		CHK	APP
DRAWING STATUS:						
DESIGN DEVELOPMENT						

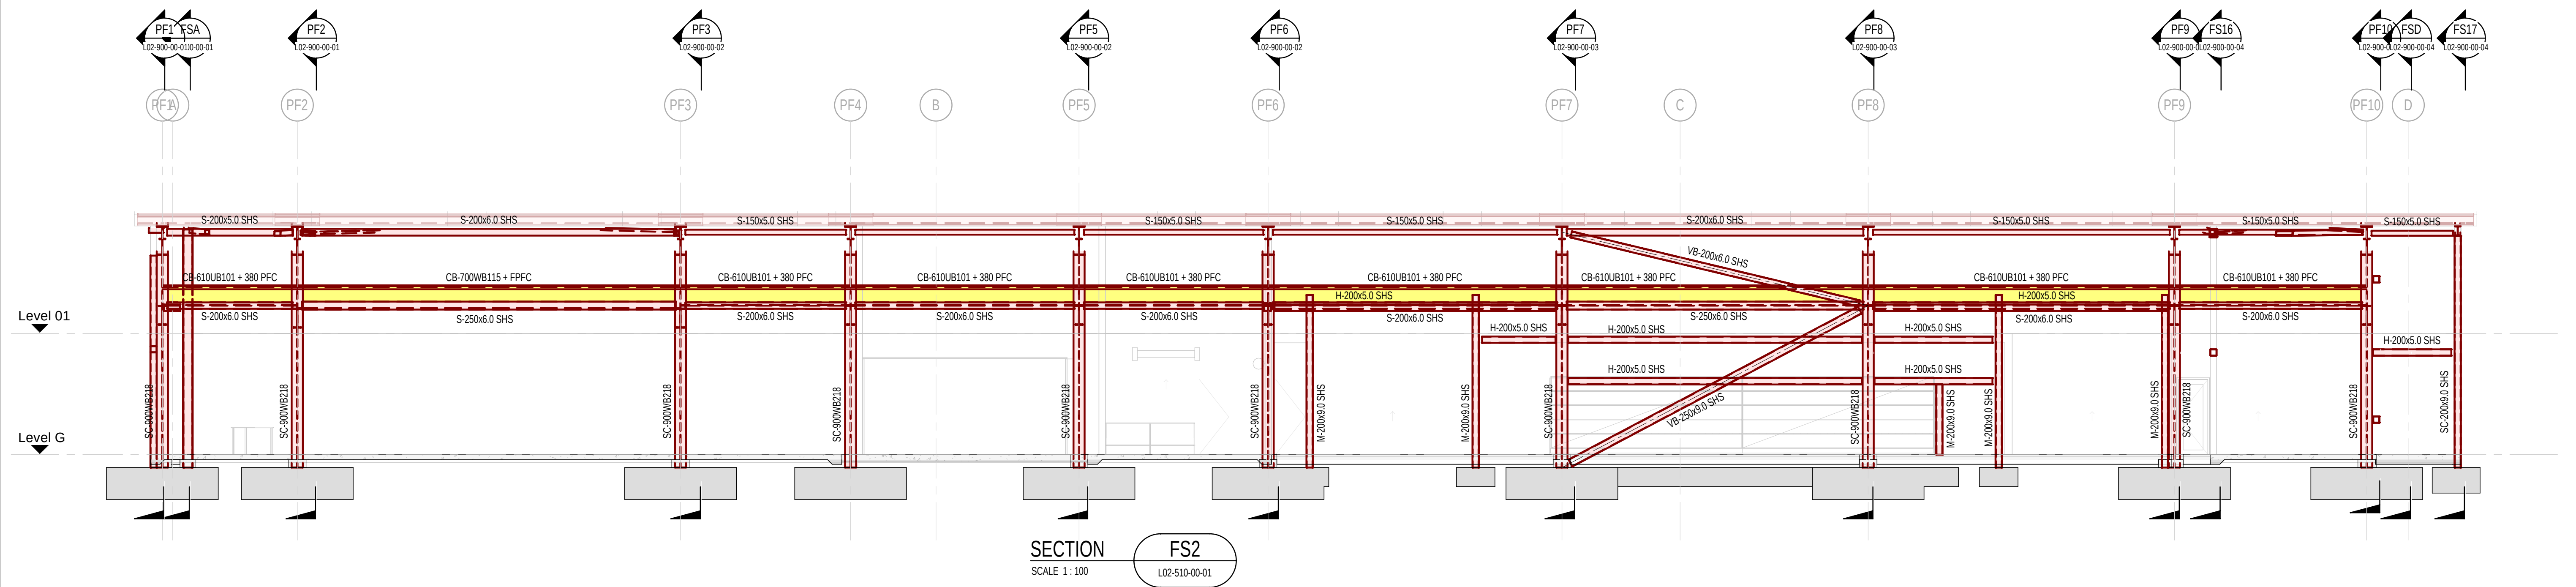

<http://www.wsp.com>

CLIENT



THOMSON ADSETT + PEDDLE THORP

PROJECT:

CQU ROCKHAMPTON TAFE
CONSOLIDATION - STAGE 2

BuildingName
LEVEL 02 - FRAMING SECTIONS - SHEET 06

SCALE @ A1:

1:100

CHECKED:	
----------	--

BM

PROVED:

DG

PJH	14.01.2016
-----	------------

92-ST-DR-L02-900-00-06

A

© WSP Australia Pty Ltd