

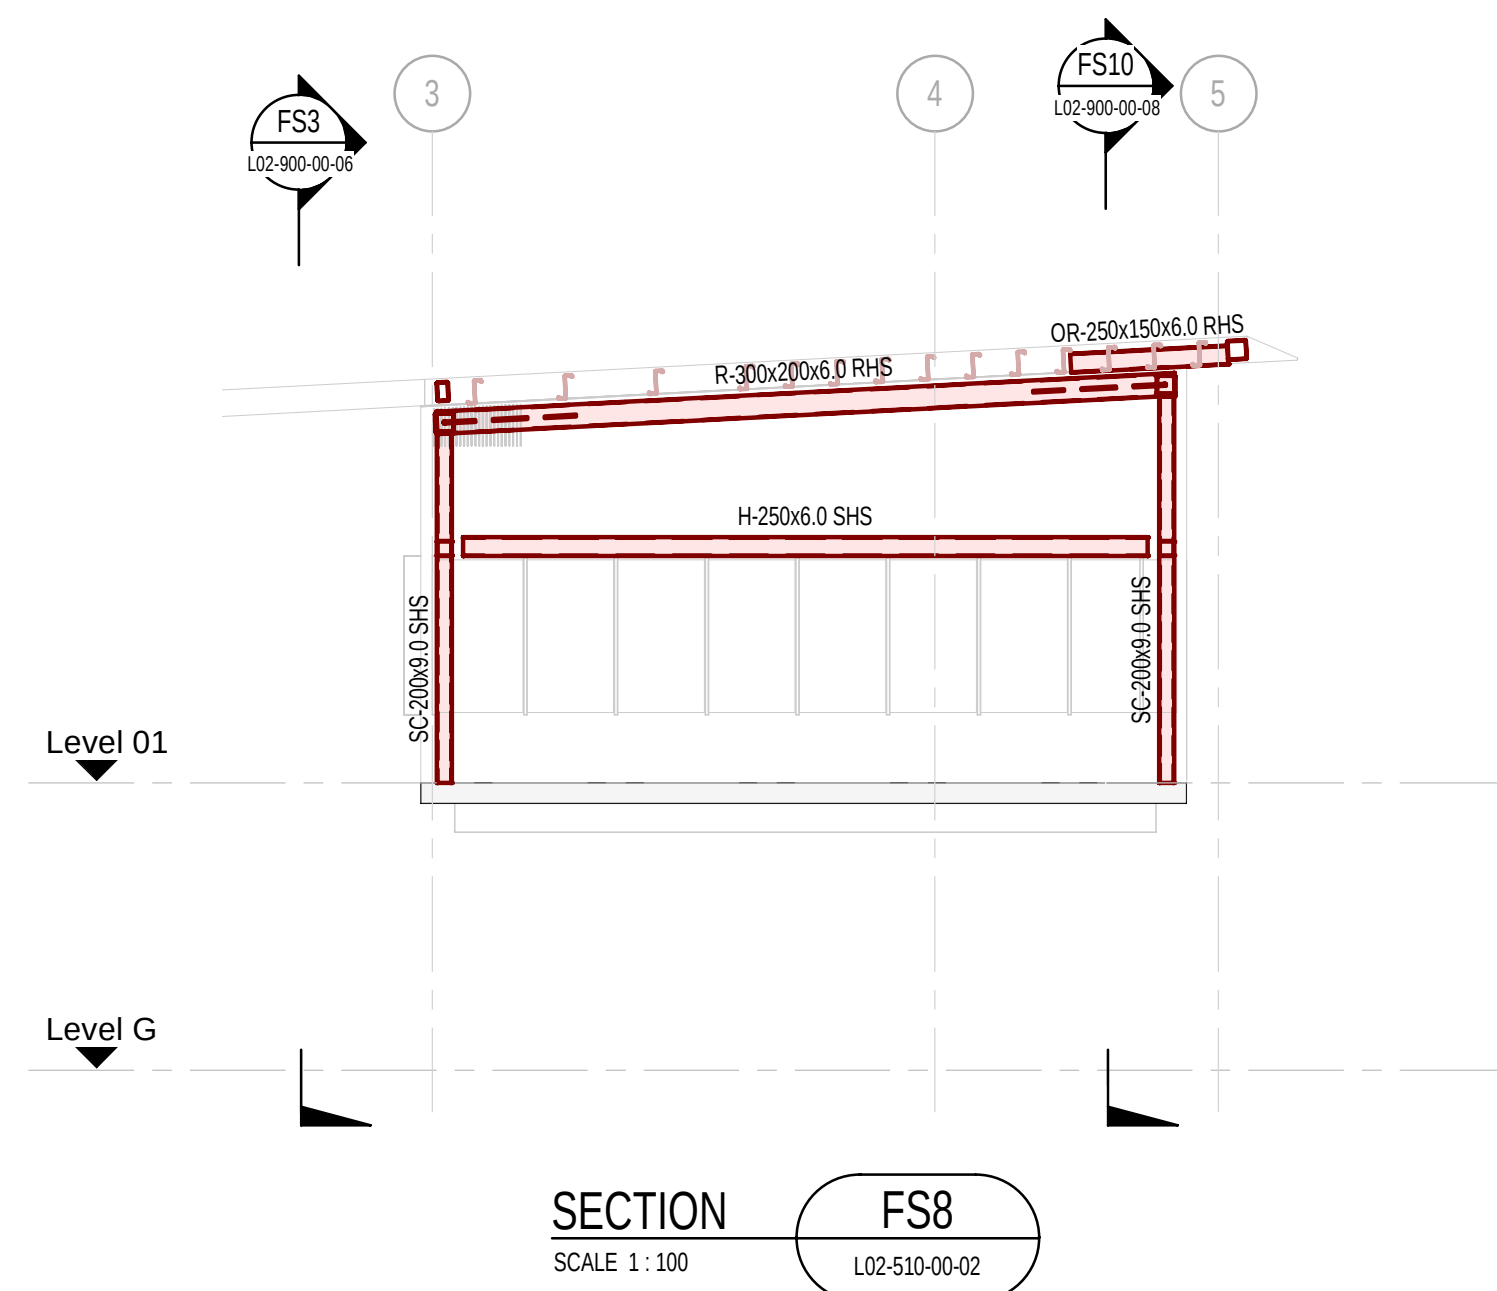
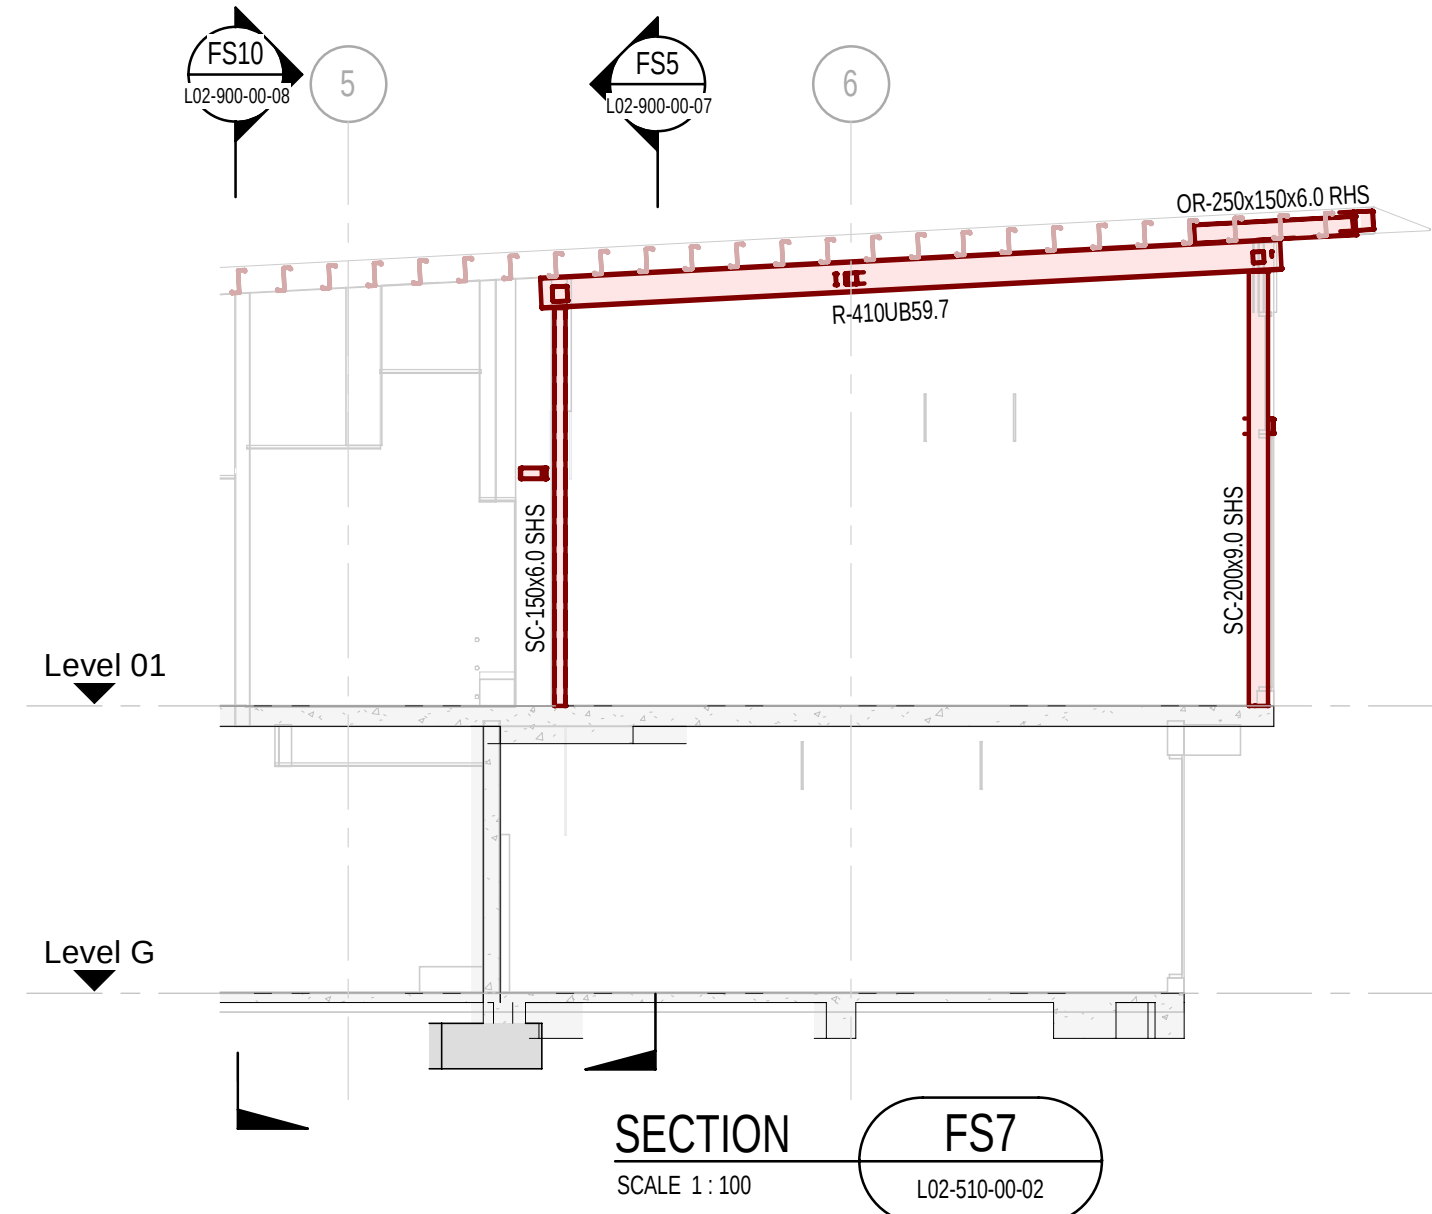
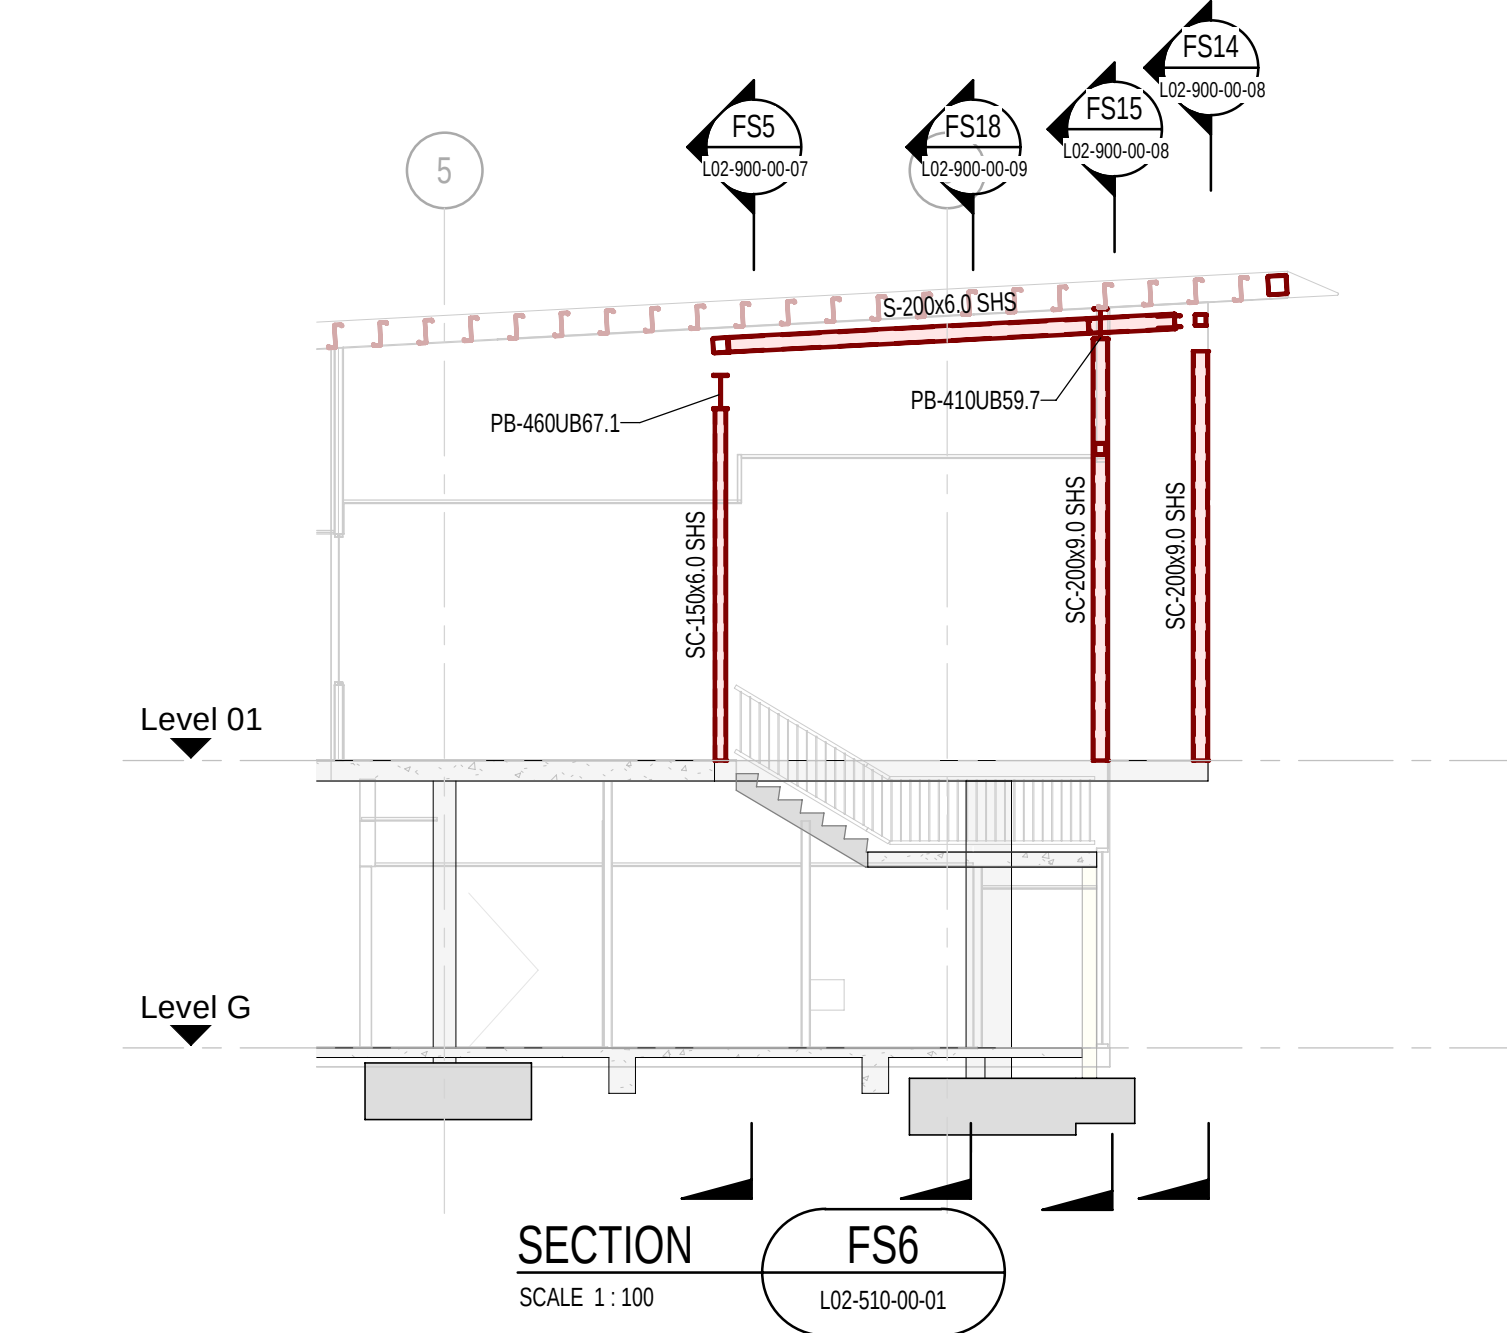


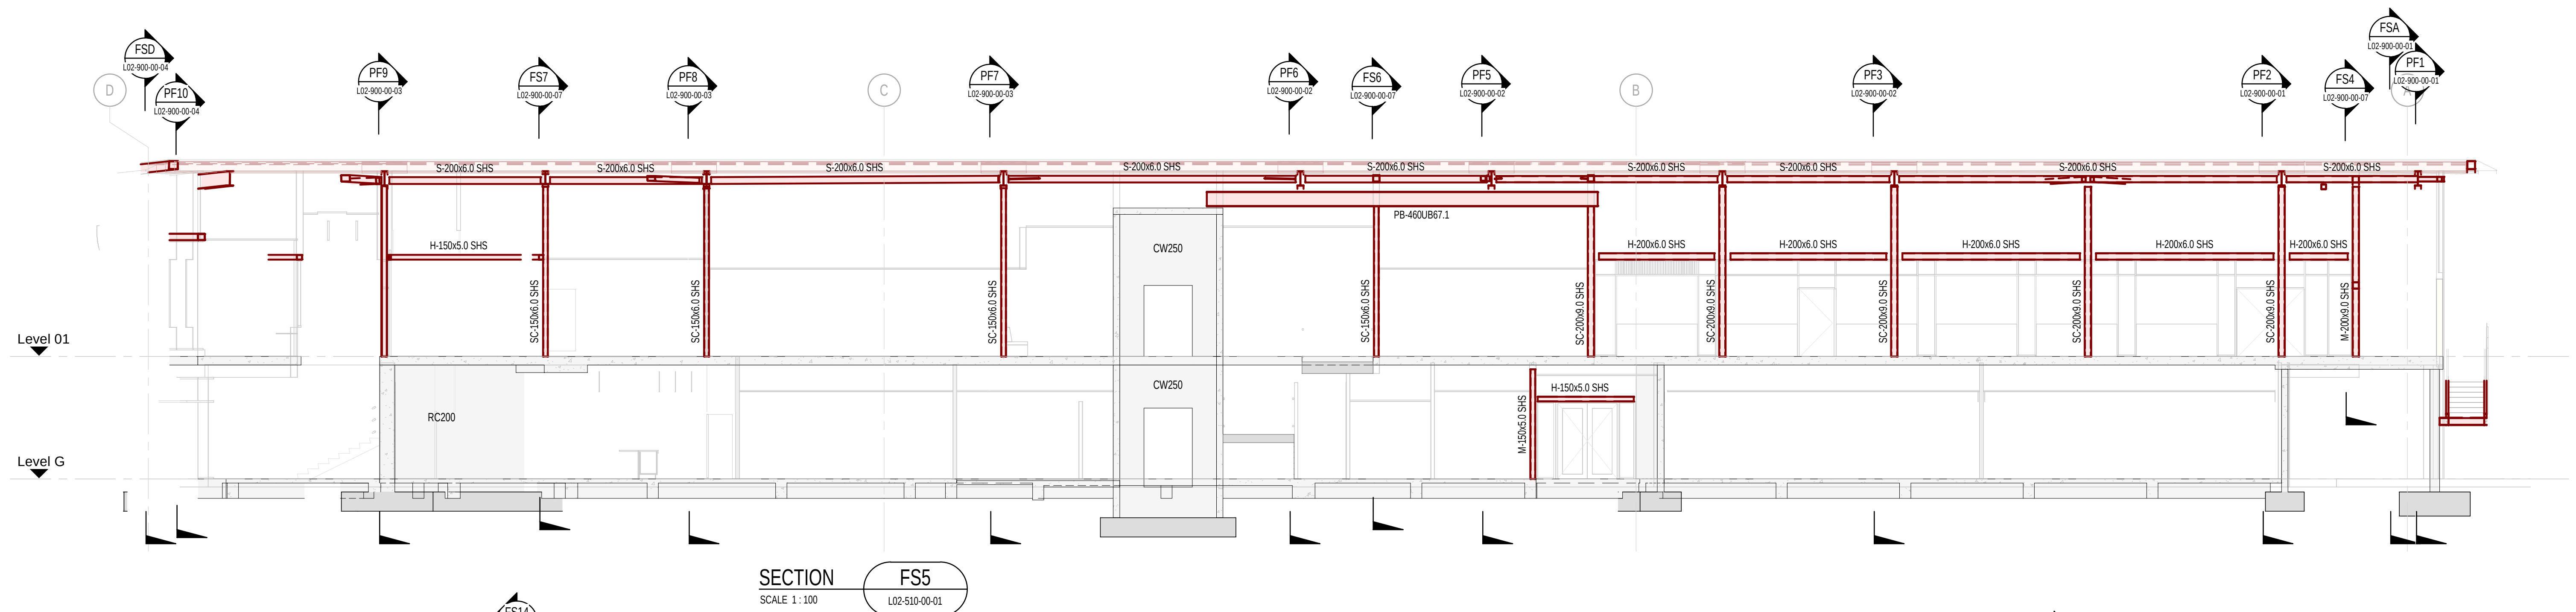

INFORMATION REFLECTED ON THIS DRAWING REPRESENTS STRUCTURAL DESIGN DEVELOPED FOR D&C TENDER ADVICE ONLY, AND SHOULD NOT BE REGARDED AS COMPLETE. THE D&C CONTRACTOR SHOULD REFER TO ALL ASSOCIATED ARCHITECTURAL AND OTHER DISCIPLINE DRAWINGS, PROJECT BRIEFS AND CLIENT REQUIREMENTS AND MAKE ADEQUATE ALLOWANCES FOR ALL NECESSARY STRUCTURAL WORKS TO MEET THESE REQUIREMENTS, EQUIPMENT SCHEDULES AND COMPLIANCE WITH THE NCC & APPROPRIATE AUSTRALIAN STANDARDS

REV	DATE	BY	DESCRIPTION	CHK	APP
A	12.02.2026	MSB	ISSUED FOR D&C TENDER	BM	DG
P1	30.01.2026	PJH	DRAFT 60% DD ISSUE FOR REVIEW	BM	DG
DRAWING STATUS: DESIGN DEVELOPMENT					

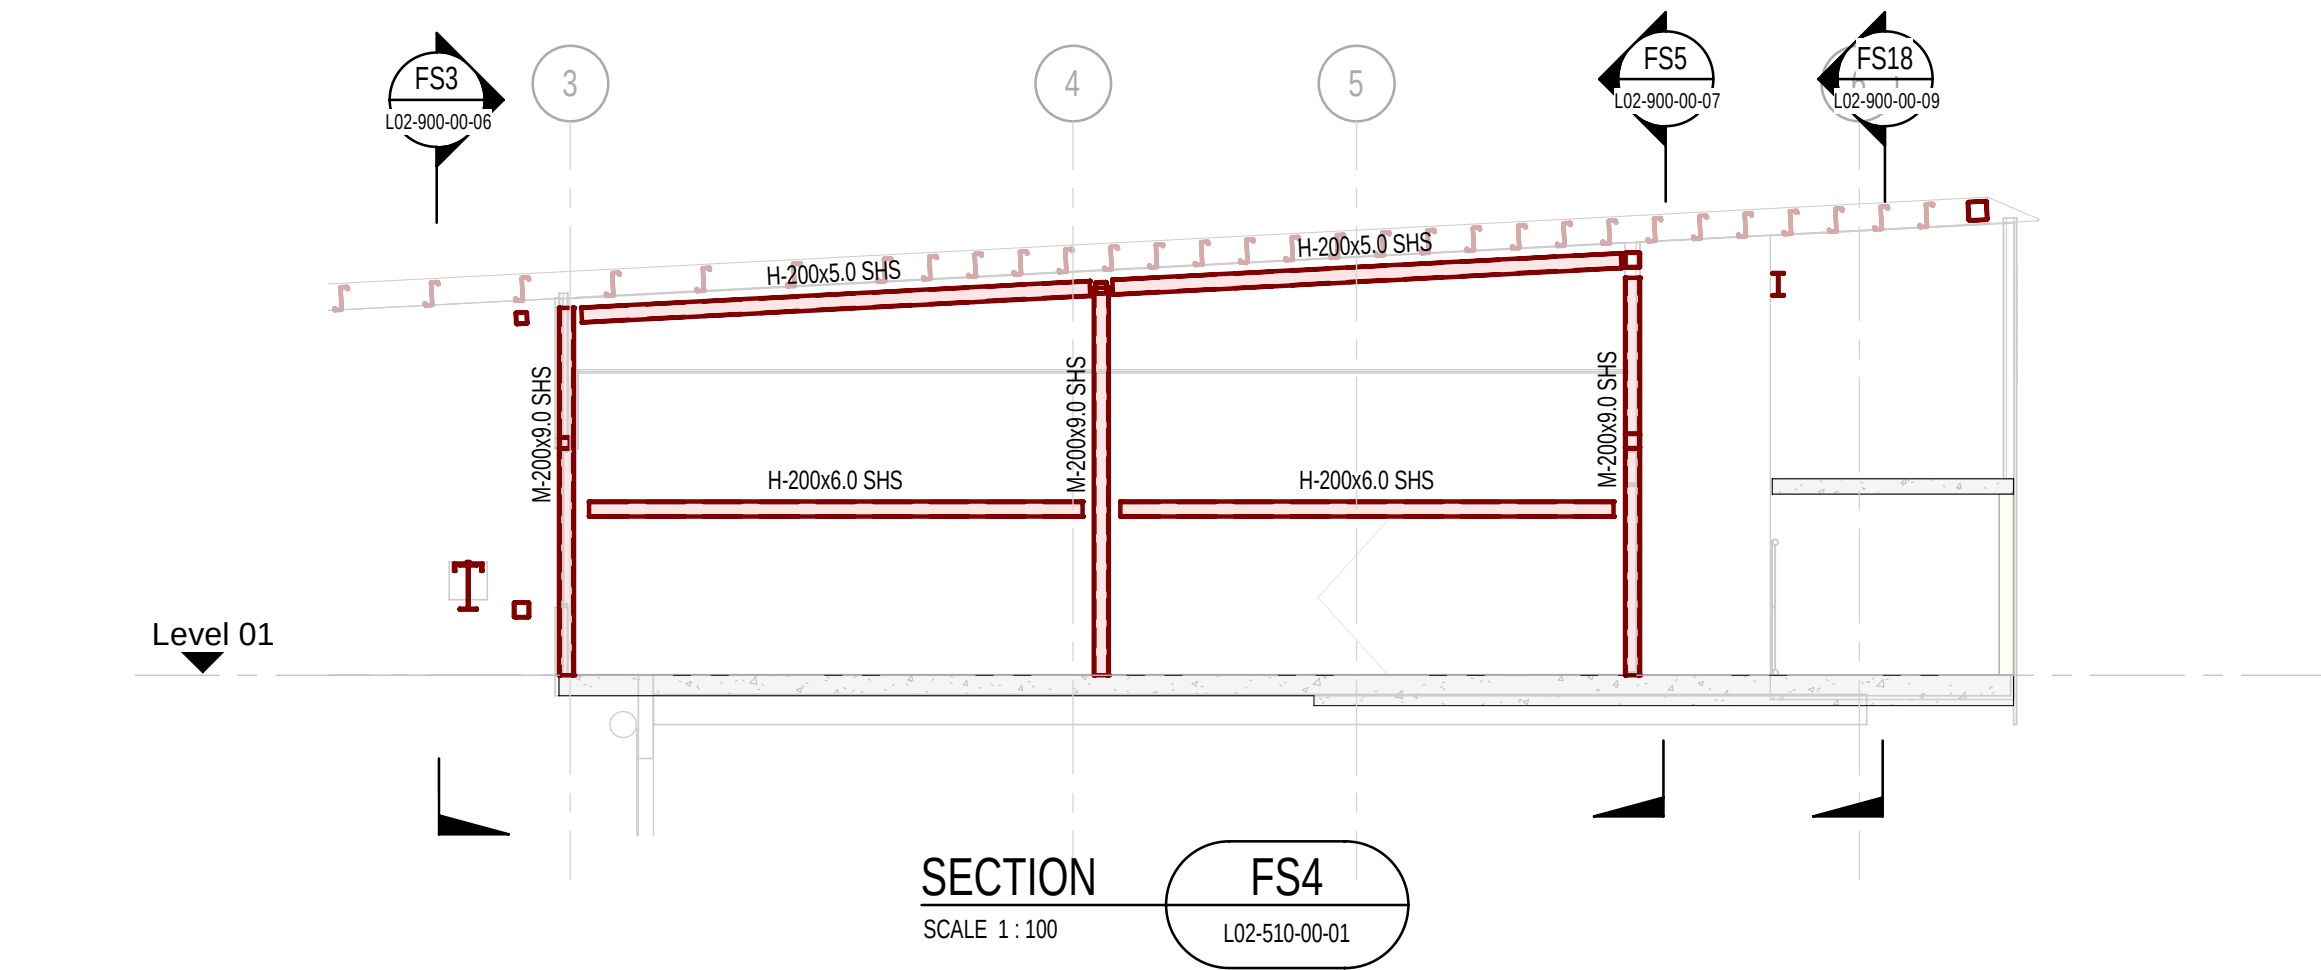

CLIENT:	CQUniversity AUSTRALIA
ARCHITECT:	THOMSON ADSETT + PEDDLE THORP

PROJECT:	CQU ROCKHAMPTON TAFE CONSOLIDATION - STAGE 2
TITLE:	BuildingName LEVEL 02 - FRAMING SECTIONS - SHEET 07

SCALE @ A1:	1:100	CHECKED:	BM	APPROVED:	DG
PROJECT NUMBER:	PS229518	DRAWN:	PJH	DATE:	14.01.2016
DRAWING No:	92-ST-DR-L02-900-00-07	REV:	A	© WSP Australia Pty Ltd	