


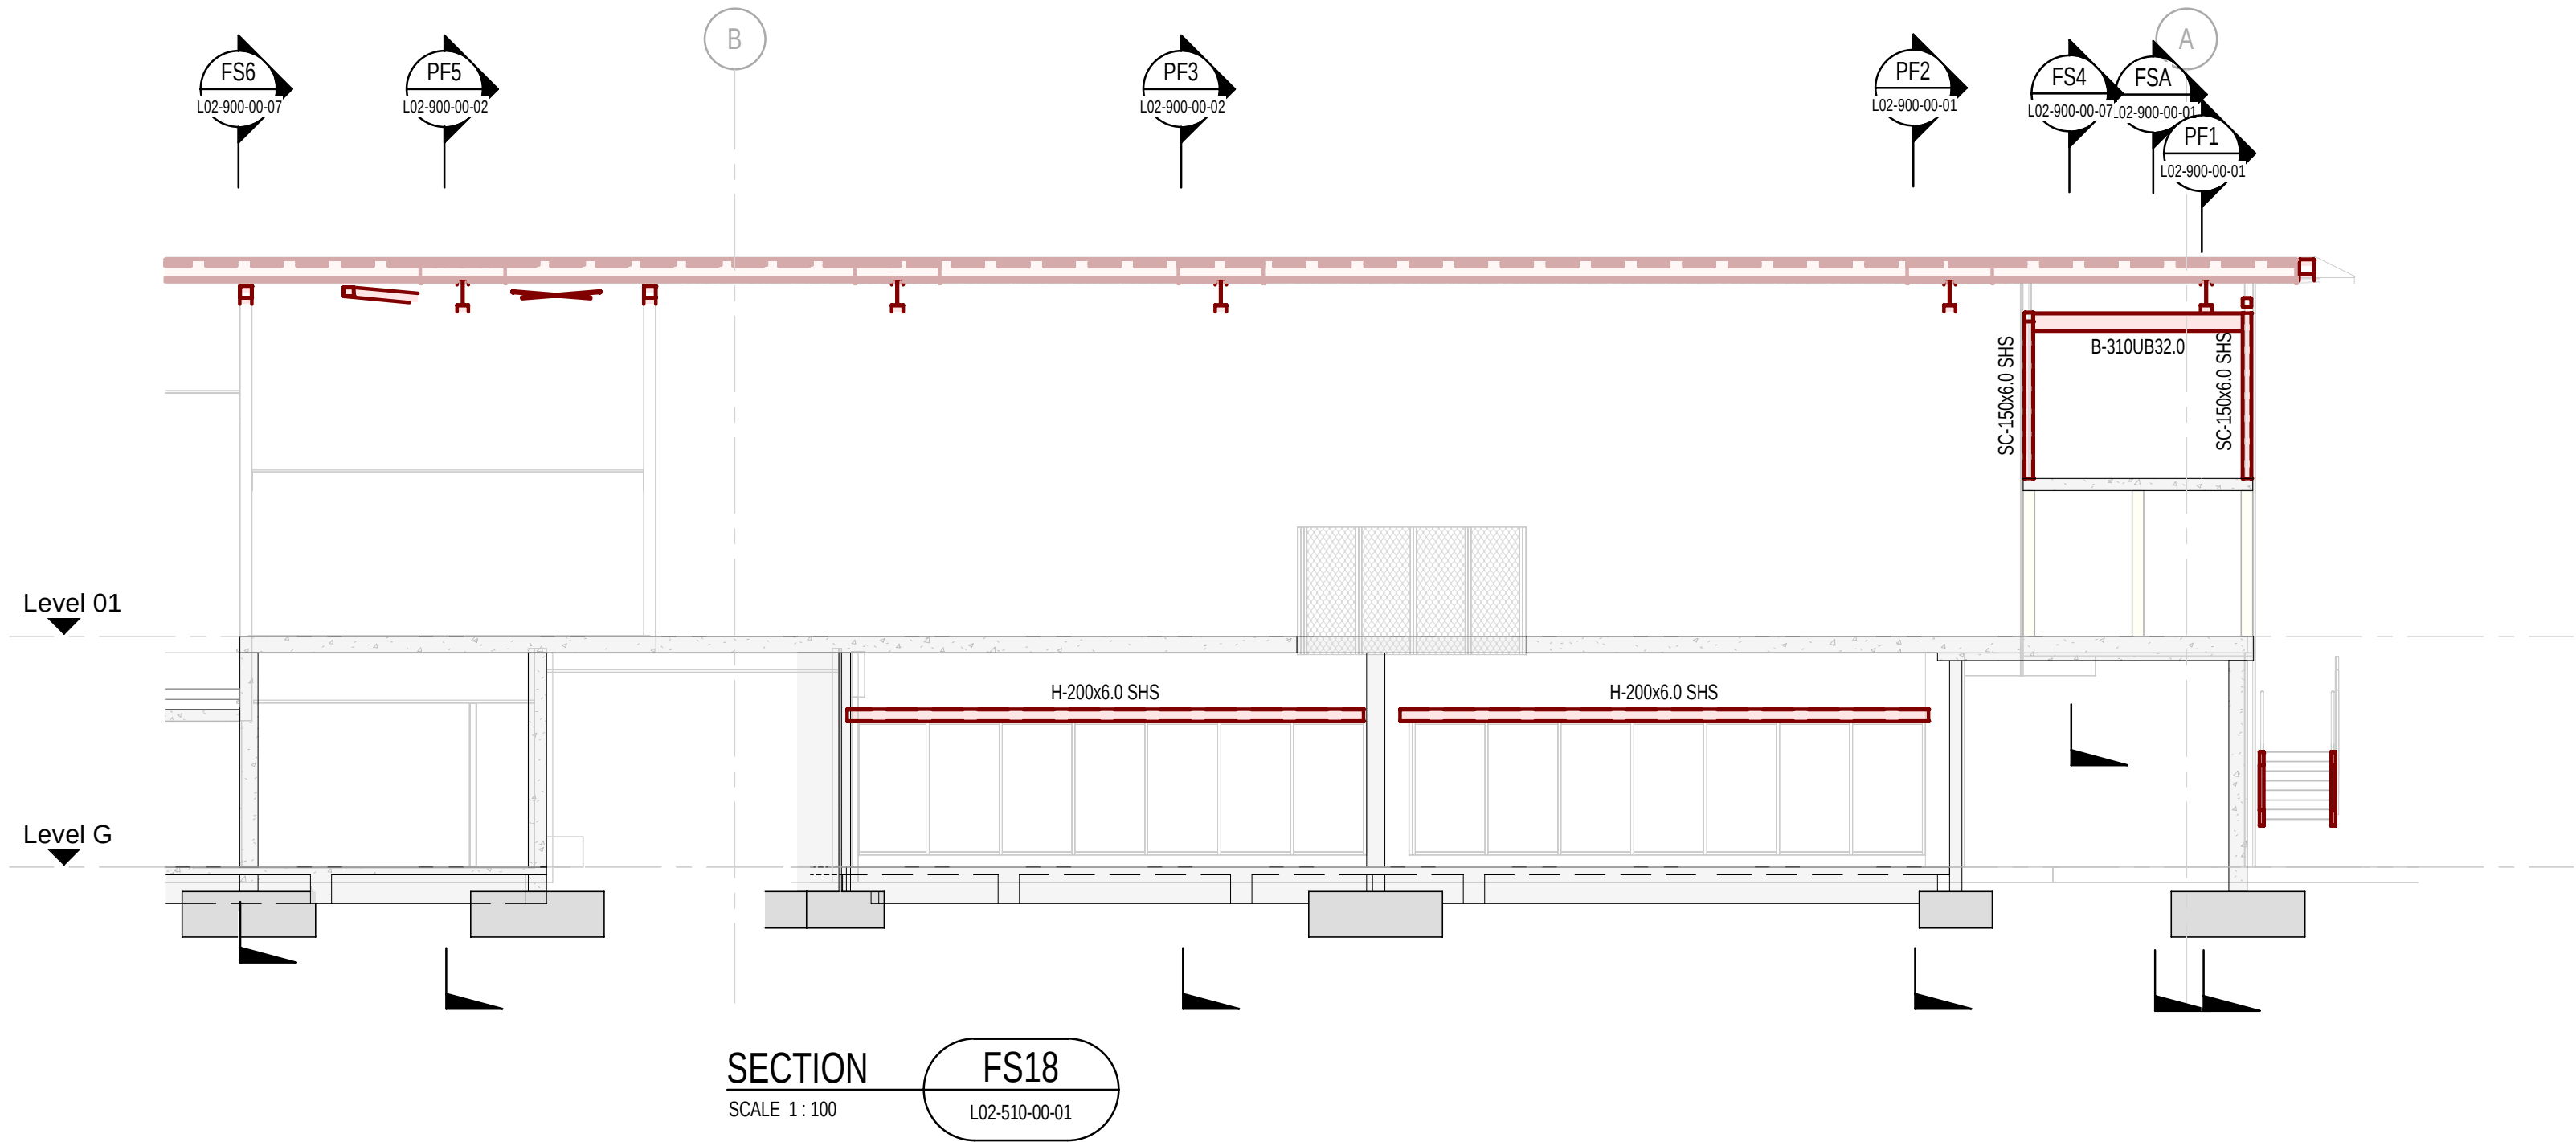

INFORMATION REFLECTED ON THIS DRAWING REPRESENTS STRUCTURAL DESIGN DEVELOPED FOR D&C TENDER ADVICE ONLY, AND SHOULD NOT BE REGARDED AS COMPLETE. THE D&C CONTRACTOR SHOULD REFER TO ALL ASSOCIATED ARCHITECTURAL AND OTHER DISCIPLINE DRAWINGS, PROJECT BRIEFS AND CLIENT REQUIREMENTS AND MAKE ADEQUATE ALLOWANCES FOR ALL NECESSARY STRUCTURAL WORKS TO MEET THESE REQUIREMENTS, EQUIPMENT SCHEDULES AND COMPLIANCE WITH THE NCC & APPROPRIATE AUSTRALIAN STANDARDS

A	12.02.2026	MSB	ISSUED FOR D&C TENDER							BM	DG
P1	30.01.2026	PJH	DRAFT 60% DD ISSUE FOR REVIEW							BM	DG
REV	DATE	BY	DESCRIPTION							CHK	APP
DRAWING STATUS: DESIGN DEVELOPMENT											



<http://www.wsp.com>

CLIENT:



THOMSON ADSETT + PEDDLE THORP

ARCHITECT:

PROJECT:

CQU ROCKHAMPTON TAFE
CONSOLIDATION - STAGE 2

TITLE:

BuildingName
LEVEL 02 - FRAMING SECTIONS - SHEET 09

SCALE @ A1:

1:100

CHECKED:

BM

APPROVED:

DG

PROJECT NUMBER:
PS229518

DRAWN:

PJH

DATE:

14.01.2016

DRAWING No:

92-ST-DR-L02-900-00-09

REV:

A

© WSP Australia Pty Ltd