

CONTRACTOR TO LOCATE AND ASSESS EXISTING
SEWER PUMP STATION PERFORMANCE, CONDITION
AND CAPACITY. CONTRACTOR TO ALLOW ALL COSTS
TO RELOCATE AND REINSTATE SEWER PUMP STATION
AND ALL ASSOCIATED EQUIPMENT AWAY FROM NEW
TRADE'S BUILDING'S FOOTPRINT.

EXISTING SERVICES

SERVICES SHOWN AS EXISTING HAVE BEEN INTERPOLATED FROM RECORD
DRAWINGS. CONTRACTOR TO VERIFY LOCATIONS AND LEVELS PRIOR TO
COMMENCEMENT OF WORK.

INFORMATION REFLECTED ON THIS DRAWING
REPRESENTS HYDRAULIC SERVICES DESIGN
DEVELOPED FOR D&C TENDER ADVICE ONLY, AND
SHOULD NOT BE REGARDED AS COMPLETE. THE D&C
CONTRACTOR SHOULD REFER TO ALL ASSOCIATED
ARCHITECTURAL AND OTHER DISCIPLINE DRAWINGS,
PROJECT BRIEFS AND CLIENT REQUIREMENTS AND
MAKE ADEQUATE ALLOWANCES FOR ALL NECESSARY
HYDRAULIC SERVICES WORKS TO MEET THESE
REQUIREMENTS, EQUIPMENT SCHEDULES AND
COMPLIANCE WITH THE NCC & APPROPRIATE
AUSTRALIAN STANDARDS

A	REVIS	SM	ISSUED FOR D&C TENDER	AA	SM
REV	DATE	BY	DESCRIPTION	CHK	APP

DRAWING STATUS: DESIGN DEVELOPMENT



900 Ann Street, Level 12, Fortitude Valley 4006
Tel: +61-7-3854-6200 Fax: +61-7-3854-6500
<http://www.wsp.com>

CLIENT: CQU

ARCHITECT: THOMSON ADSETT / PEDDLE THORP

PROJECT: CQU ROCKHAMPTON TAFE CONSOLIDATION

TITLE: HYDRAULIC SERVICES
HYDRAULIC SERVICES - PROPOSED SITE PLAN

SCALE @ A1: 1:1000	CHECKED: AA	APPROVED: SM
PROJECT NUMBER: PS229518	DRAWN: SH	DATE: JAN 2026

DRAWING NO: 00-HY-DR-300-A00-00-00	REV: A
------------------------------------	--------


© WSP Australia Pty Ltd

CQU ROCKHAMPTON TAFE CONSOLIDATION

HYDRAULIC SERVICES

HYDRAULIC DRAWING INDEX

00-HY-DR-000-A00-00-00	COVER SHEET & DRAWING INDEX
00-HY-DR-010-A00-00-00	GENERAL NOTES, LEGENDS & SYMBOLS
00-HY-DR-100-A00-00-01	EQUIPMENT SCHEDULE
00-HY-DR-100-A00-00-02	TYPICAL DETAILS
00-HY-DR-300-A00-00-00	HYDRAULIC SERVICES - PROPOSED SITE PLAN
B19-HY-DR-510-L03-00-00	BUILDING 19 - LEVEL 03 - DRAINAGE LAYOUT
B19-HY-DR-520-L03-00-00	BUILDING 19 - LEVEL 03 - WATER LAYOUT
B33-HY-DR-510-L00-00-00	BUILDING 33 - GROUND LEVEL - DRAINAGE LAYOUT
B33-HY-DR-510-L01-00-00	BUILDING 33 - LEVEL 01 - DRAINAGE LAYOUT
B33-HY-DR-510-L02-00-00	BUILDING 33 - LEVEL 02 - DRAINAGE LAYOUT
B33-HY-DR-510-LRF-00-00	BUILDING 33 - ROOF LEVEL - DRAINAGE LAYOUT
B33-HY-DR-520-L01-00-00	BUILDING 33 - LEVEL 01 - WATER SERVICES LAYOUT
B33-HY-DR-520-L02-00-00	BUILDING 33 - LEVEL 02 - WATER SERVICES LAYOUT
B34-HY-DR-510-L00-00-00	BUILDING 34 - GROUND LEVEL - DRAINAGE AND WATER SERVICES LAYOUT
B36-HY-DR-510-L00-00-00	BUILDING 36 - GROUND LEVEL - DRAINAGE LAYOUT
B36-HY-DR-510-L01-00-00	BUILDING 36 - LEVEL 01 - DRAINAGE LAYOUT
B36-HY-DR-510-LRF-00-00	BUILDING 36 - ROOF LEVEL - DRAINAGE LAYOUT
B36-HY-DR-520-L00-00-00	BUILDING 36 - GROUND LEVEL - WATER SERVICES LAYOUT
B36-HY-DR-520-L01-00-00	BUILDING 36 - LEVEL 01 - WATER SERVICES LAYOUT
B76-HY-DR-510-L00-00-00	HORTICULTURE BUILDING - GROUND LEVEL - DRAINAGE LAYOUT
B76-HY-DR-510-LRF-00-00	HORTICULTURE BUILDING - ROOF LEVEL - DRAINAGE LAYOUT
B76-HY-DR-520-L00-00-00	HORTICULTURE BUILDING - GROUND LEVEL - WATER SERVICES LAYOUT
ENG-HY-DR-510-L00-00-00	ENGINEERING BUILDING - GROUND LEVEL - DRAINAGE LAYOUT
ENG-HY-DR-520-L00-00-00	ENGINEERING BUILDING - GROUND LEVEL - WATER SERVICES LAYOUT
NTB-HY-DR-510-L00-00-00	NEW TRADES BUILDING - GROUND LEVEL - DRAINAGE LAYOUT
NTB-HY-DR-510-L01-00-00	NEW TRADES BUILDING - LEVEL 01 - DRAINAGE LAYOUT
NTB-HY-DR-510-LRF-00-00	NEW TRADES BUILDING - ROOF LEVEL - DRAINAGE LAYOUT
NTB-HY-DR-520-L00-00-00	NEW TRADES BUILDING - GROUND LEVEL - WATER SERVICES LAYOUT
NTB-HY-DR-520-L01-00-00	NEW TRADES BUILDING - LEVEL 01 - WATER SERVICES LAYOUT

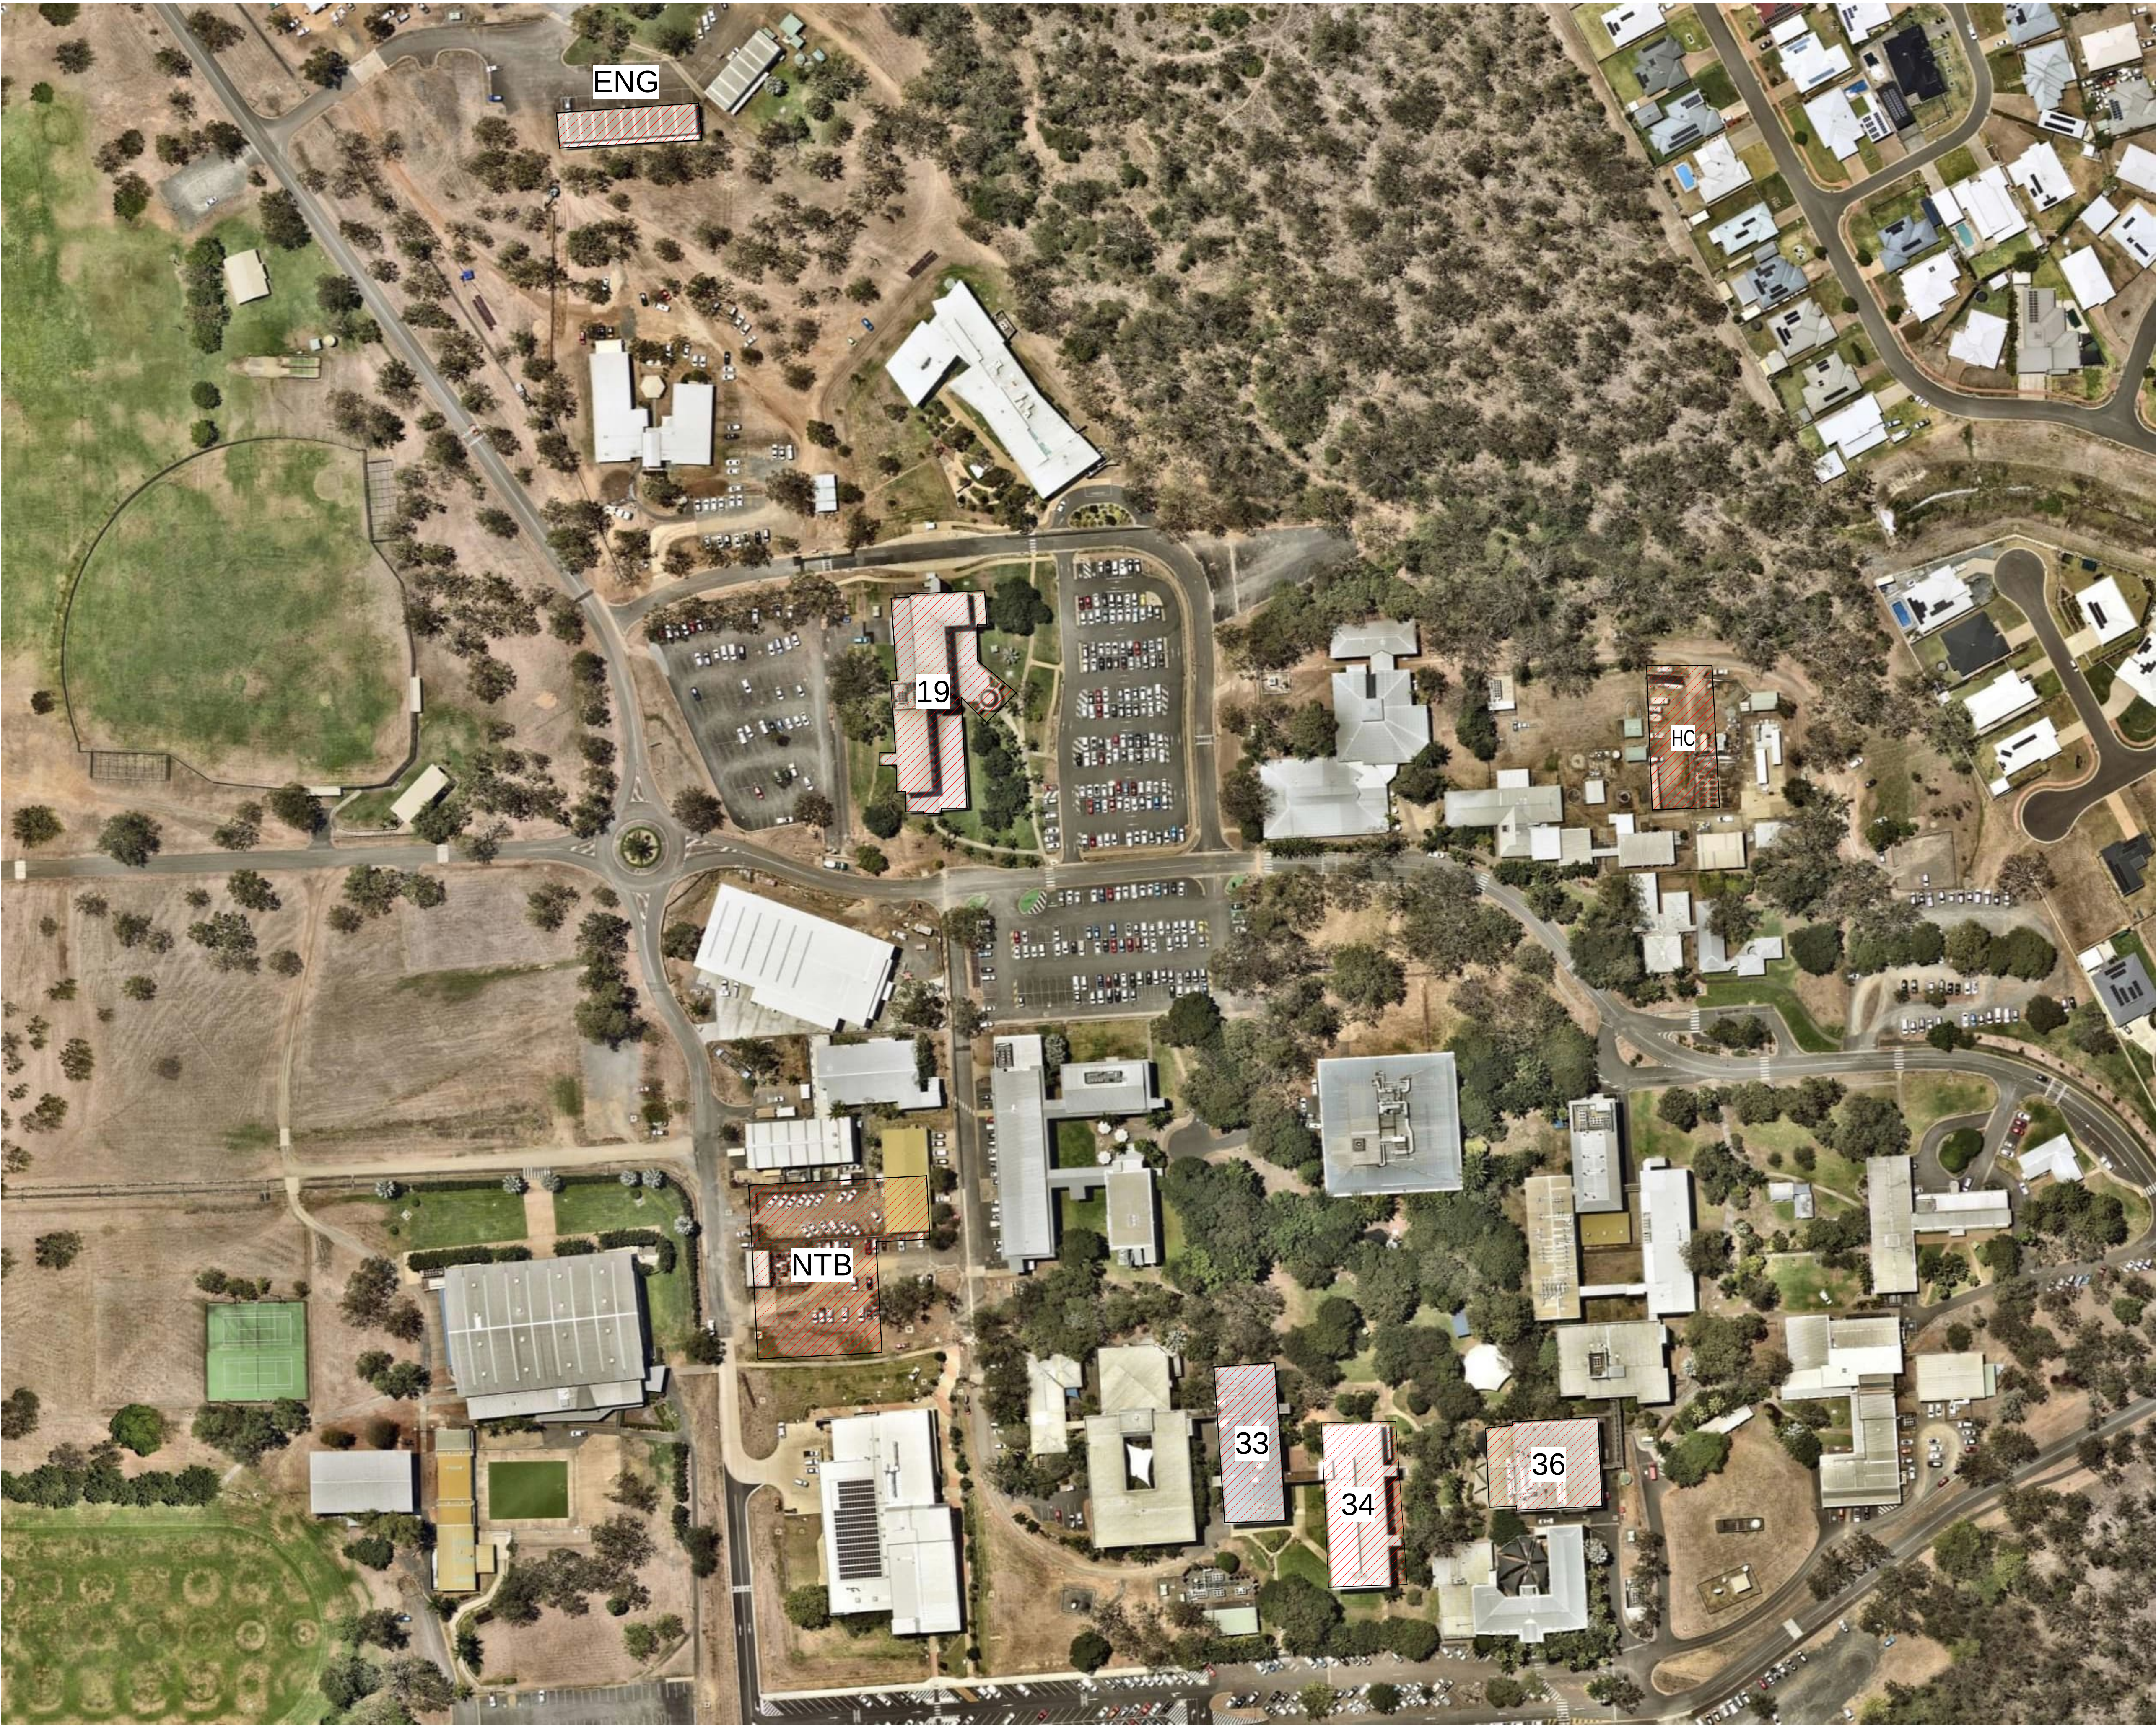

LOCALITY PLAN
N.T.S.

INFORMATION REFLECTED ON THIS DRAWING REPRESENTS HYDRAULIC SERVICES DESIGN DEVELOPED FOR D&C TENDER ADVISE ONLY, AND SHOULD NOT BE REGARDED AS COMPLETE. THE D&C CONTRACTOR SHOULD REFER TO ALL ASSOCIATED ARCHITECTURAL AND OTHER DISCIPLINE DRAWINGS, PROJECT BRIEFS AND CLIENT REQUIREMENTS AND MAKE ADEQUATE ALLOWANCES FOR ALL NECESSARY HYDRAULIC SERVICES WORKS TO MEET THESE REQUIREMENTS, EQUIPMENT SCHEDULES AND COMPLIANCE WITH THE NCC & APPROPRIATE AUSTRALIAN STANDARDS

B	12.02.2026	SH	ISSUED FOR D&C TENDER	AA	SM
A	10.02.2026	SH	ISSUED FOR D&C TENDER	AA	SM

REV	DATE	BY	DESCRIPTION	CHK	APP
-----	------	----	-------------	-----	-----

DRAWING STATUS	DESIGN DEVELOPMENT
----------------	--------------------



900 Ann Street, Level 12, Fortitude Valley 4006
Tel: +61-7-3854-6200 Fax: +61-7-3854-6500
<http://www.wsp.com>

CLIENT:	CQU
---------	-----

ARCHITECT:	THOMSON ADSETT / PEDDLE THORP
------------	-------------------------------

PROJECT:	CQU ROCKHAMPTON TAFE CONSOLIDATION
----------	------------------------------------

TITLE:	HYDRAULIC SERVICES COVER SHEET & DRAWING INDEX
--------	---

SCALE @ A0	N.T.S.	CHECKED:	AA	APPROVED:	SM
PROJECT NUMBER:	PS229518	DRAWN:	SH	DATE:	JAN 2026

DRAWING NO:	00-HY-DR-000-A00-00-00	REV:	B
-------------	------------------------	------	---

Diagram illustrating the components of a callout marker:

- CALLOUT MARKER**: The dashed line connecting the marker to the text.
- VIEW DIRECTION**: The arrow pointing from the marker to the view.
- VIEW NUMBER**: The number '1' inside the marker.
- DRAWING NUMBER**: The text 'WSP-DWG-H001' below the marker.

	CAP
	CONTINUATION
	CHANGE IN SIZE / GRADE / MATERIAL
	CUT-IN / PIPE BREAK
	CONTROL PANEL
	FLOW DIRECTION
	RISER / DROPPER / TEE
	ACCESS PANEL
	VALVE BOX - IN-GROUND

	BALANCING VALVE
	ISOLATION VALVE
	CONTROL VALVE - FLOAT
	CONTROL VALVE - SOLENOID
	DOUBLE CHECK VALVE
	EMERGENCY EYEWASH
	EMERGENCY SHOWER
	EXPANSION CONTROL VALVE
	FILTER

- H BAYONET POINT
- EXPANSION FITTING
- FILTER
- GAS METER (AUTHORITY)
- ISOLATION VALVE
- PRESSURE REGULATOR
- PRESSURE REGULATOR WITH OVER-PRESSURE PROTECTION
- SLAM SHUT BUTTON
- SLAM SHUT VALVE

	AIR ADMITTANCE VALVE
	REFLEX VALVE
	INSPECTION CHAMBER
	GRADED TRENCH DRAIN
	STORMWATER PIT
	FLOOR WASTE / GRADED OUTLET
	FLOOR WASTE - BASKET TRAP
	PLANTER DRAIN OUTLET
	OVERFLOW RELIEF GULLY / DISCONNECTOR GULLY
	INSPECTION OPENING TO SURFACE
	RAINWATER OUTLET
	TUNDISH / TRAPPED TUNDISH
	TUNDISH / TRAPPED TUNDISH - IN-WALL

B	BASIL / VANITY BASIN / HANDBASIN
BCWU	BOILING CHILLED WATER UNIT
BCHWU	BOILING CHILLED HOT WATER UNIT
BDO	BALCONY DRAIN OUTLET
BFW	BASKET FLOOR WASTE
BV	BALANCING VALVE
CD	CONDENSATE DRAIN
CHV	CHAMBER VENT
CI	CAST IRON
CIS	CAST IN SLAB
CP	CONTROL PANEL
CSK	CLEANERS SINK
CTE	CONNECT TO EXISTING
CV	CHECK VALVE
CW	COLD WATER

DCHV	DOUBLE CHECK VALVE
DCW	DRINKING COLD WATER
DF	DRINKING FOUNTAIN
DG	DISCONNECTOR GULLY
DWG	DRAWING
DW	DISH WASHER
ECV	EXPANSION CONTROL VALVE
EJ	EXPANSION JOINT
EPD	ELEVATED PIPEWORK DROPPER
EEW	EMERGENCY EYE WASH
e	EXISTING

GCP	GAS CONTROL PANEL
GIT	GREASE INTERCEPTOR TRAP
GO	GRATED OUTLET
GSSB	GAS SLAM SHUT BUTTON
GTD	GRATED TRENCH DRAIN
HDPE	HIGH DENSITY POLYETHYLENE
HL	HIGH LEVEL
HP	HIGH POINT
HSW	HARVESTED STORMWATER
HT	HOSE TAP
HW	HOT WATER
HWCP	HOT WATER CIRCULATION PUMP
HWF	HOT WATER FLOW
HWP	HOT WATER PLANT
HWR	HOT WATER RETURN
HWU	HOT WATER UNIT

IL	INVERT LEVEL
IO	INSPECTION OPENING
IOS	INSPECTION OPENING TO SUR
IV	ISOLATING VALVE
JU	JUMP UP

kPa	KILOPASCALS
kW	KILOWATTS
L	LITRES
LL	LOW LEVEL

ND	NON DRINKING
NDWC	NON DRINKING WATER
NP	NON POTABLE
OF	OVERFLOW
ORG	OVERFLOW RELIEF GULL
OWS	OIL/WATER SEPARATOR
PCW	POTABLE COLD WATER
PDO	PLANTER DRAIN OUTLET
PE	POLYETHYLENE
PEX	CROSS LINKED POLYETH
PFW	PLANT ROOM FLOOR WAS
PPR	POLYPROPYLENE
PRV	PRESSURE REDUCTION V
PVC	POLYVINYL CHLORIDE
PWD	PERSON WITH DISABILITY

RCP	REINFORCED CONCRETE PIPE
RL	REDUCED LEVEL
RM	RIISING MAIN
RPZD	REDUCED PRESSURE ZONE DEVICE
RWT	RAINWATER HARVESTING TANK
RWP	RAIN WATER PUMP(S)
RV	RELIEF VENT

SAC	SEWER ACCESS CHAMBER
SCVT	TESTABLE SINGLE CHECK VALVE
SD	SANITARY DRAINAGE
SDPS	SANITARY DRAINAGE PUMP STATION
SDRM	SANITARY DRAINAGE RISING MAIN
SHR	SHOWER
SK	SINK

SV	SLUICE VALVE
SW	STORMWATER
SWD	STORMWATER DROPPER
SWAC	STORMWATER ACCESS CHAMBER
SWGP	STORMWATER GULLY PIT
TA	TO ABOVE
TB	TO BELOW
TD	TUNDISH
TTD	TRAPPED TUNDISH
TMV	THERMOSTATIC MIXING VALVE
TPD	TRAP PRIMING DEVICE
TPRV	TEMPERATURE & PRESSURE RELIEF VALVE
TR	TROUGH
TV	TEMPERING VALVE
TW	TRADE WASTE
TWD	TRADE WASTE DROPPER

TWV	TRADE WASTE VENT
UR	URINAL
US	UNDERSIDE
UG	UNDERGROUND
uPVC	UNPLASTISED POLY(VINYL CHLORIDE)
UTW	UNTRAPPED WASTE

VP	VENT PIPE
WC	WATER CLOS
WM	WASHING MAC
WW	WARM WATER

WHERE AN IOS TERMINATES INSIDE A BUILDING THE IOS IS TO BE CHROME PLATED BRASS

8. DEPTH OF SERVICES
CLEAR COVER OVER PIPEWORK TO BE IN ACCORDANCE WITH THE RELEVANT AUSTRALIAN STANDARD RELATING TO THE SERVICE

1. VALVE REQUIREMENTS
REFER TO SCHEMATICS FOR FULL EXTENT OF VALVE REQUIREMENTS
2. STANDARDS
THE INSTALLATION IS TO BE IN ACCORDANCE WITH AS/NZS3500.1, AND LOCAL AUTHORITY REQUIREMENTS, UNLESS THIS SPECIFICATION NOMINATES OTHERWISE AND EXCEEDS THE MINIMUM STANDARD REQUIREMENT

3. PROVISION FOR EXPANSION/MOVEMENT
ALL PIPEWORK SHALL BE INSTALLED SO AS TO ALLOW EXPANSION/CONTRACTION IN ACCORDANCE WITH AS5601.1.

NEW	EXISTING	ABBREV.	PIPE SYSTEM TYPE
		HSW	HARVESTED STORMWATER
		SD	SANITARY DRAINAGE
		SDP	SANITARY DRAINAGE PUMP OUT
		SW	STORMWATER DRAINAGE
		TW	TRADE WASTE
		TWPO	TRADE WASTE PUMP OUT
		VP	VENT PIPE
		CHP	VENT PIPE - CHAMBER
		QTY	VENT PIPE - GREASE TRAP
		RV	VENT PIPE - RELIEF
		TWW	VENT PIPE - TRADE WASTE

NEW (>04)	EXISTING (>04)	NEW (<04)	EXISTING (<04)	ABBREV.	PPE SYSTEM TYPE
				CCW	CIVIL WATER
				DHW	DOMESTIC HOT WATER FLOW
				DHW	DOMESTIC HOT WATER RETURN
				HW	DOMESTIC WARM WATER
				DCW	DRINKING COLD WATER
				GS	GAS
				NDCW	NON DRINKING COLD WATER
				RW	RECYCLED RAINWATER

INFORMATION REFLECTED ON THIS DRAWING REPRESENTS HYDRAULIC SERVICES DESIGN DEVELOPED FOR D&C TENDER ADVISE ONLY, AND SHOULD NOT BE REGARDED AS COMPLETE. THE D&C CONTRACTOR SHOULD REFER TO ALL ASSOCIATED ARCHITECTURAL AND OTHER DISCIPLINE DRAWINGS, PROJECT BRIEFS AND CLIENT REQUIREMENTS AND MAKE ADEQUATE ALLOWANCES FOR ALL NECESSARY HYDRAULIC SERVICES WORKS TO MEET THESE REQUIREMENTS, EQUIPMENT SCHEDULES AND COMPLIANCE WITH THE NCC & APPROPRIATE AUSTRALIAN STANDARDS

NOTES

1. EXPANSION JOINT WRAPPED IN A SUITABLE MATERIAL TO ALLOW FLUID MOVEMENT AND TO PREVENT THE INGRESS OF FOREIGN MATTER.
MINIMUM THICKNESS:
"H1" 70mm

2. EXPANSION JOINT WRAPPED IN A SUITABLE MATERIAL TO ALLOW FLUID MOVEMENT AND TO PREVENT THE INGRESS OF FOREIGN MATTER. INSTALLED TO MEET MANUFACTURER SPECIFICATIONS.


IF VERTICAL DROU (GREATER THAN 100MM) THEN EXPANSION JOINT TO BE INSTALLED.

3. JOINTS TO BE MINIMUM 200MM TO 250MM FOR A MINIMUM DISTANCE OF 800MM DOWNSTREAM OF EXISTING STRUCTURAL SLAB. ALL TRENCHING TO BE GRADED UNIFORMLY WITH PIPEWORK TO ENSURE TRENCH DRAINAGE.


EXPANSION JOINTS DOWNSTREAM OF EVERY JUNCTION (TYPICAL) & CHANGE IN DIRECTION (45°) FOR HL SITES. A COMBINATION SWIVEL/EXPANSION JOINT MAY BE UTILISED.

4. COMPACTED CLAY SOILS OR EQUIVALENT IN TRENCH TO FORM (TYPICAL) "PLUG" TO PREVENT THE INGRESS OF WATER THROUGH TRENCHING AS PER ASSOCIATED DESIGN DETAIL. DESIGNER MUST PREPARE IN CONJUNCTION WITH MANUFACTURER AND QUALITY REGISTRATION, TO SATISFY THE REQUIREMENTS OF THE PLUMBING AND DRAINAGE REGULATION 2013 SCHEDULE D.











5. TRENCHES MUST BE FULLY INSULATED TO PREVENT THE INGRESS TO CONTRACTOR INSTALLATION, UNLESS WRITTEN APPROVAL IS PROVIDED BY WSP CERTIFIED ENGINEER OR THEIR APPROPRIATE REPRESENTATIVE.

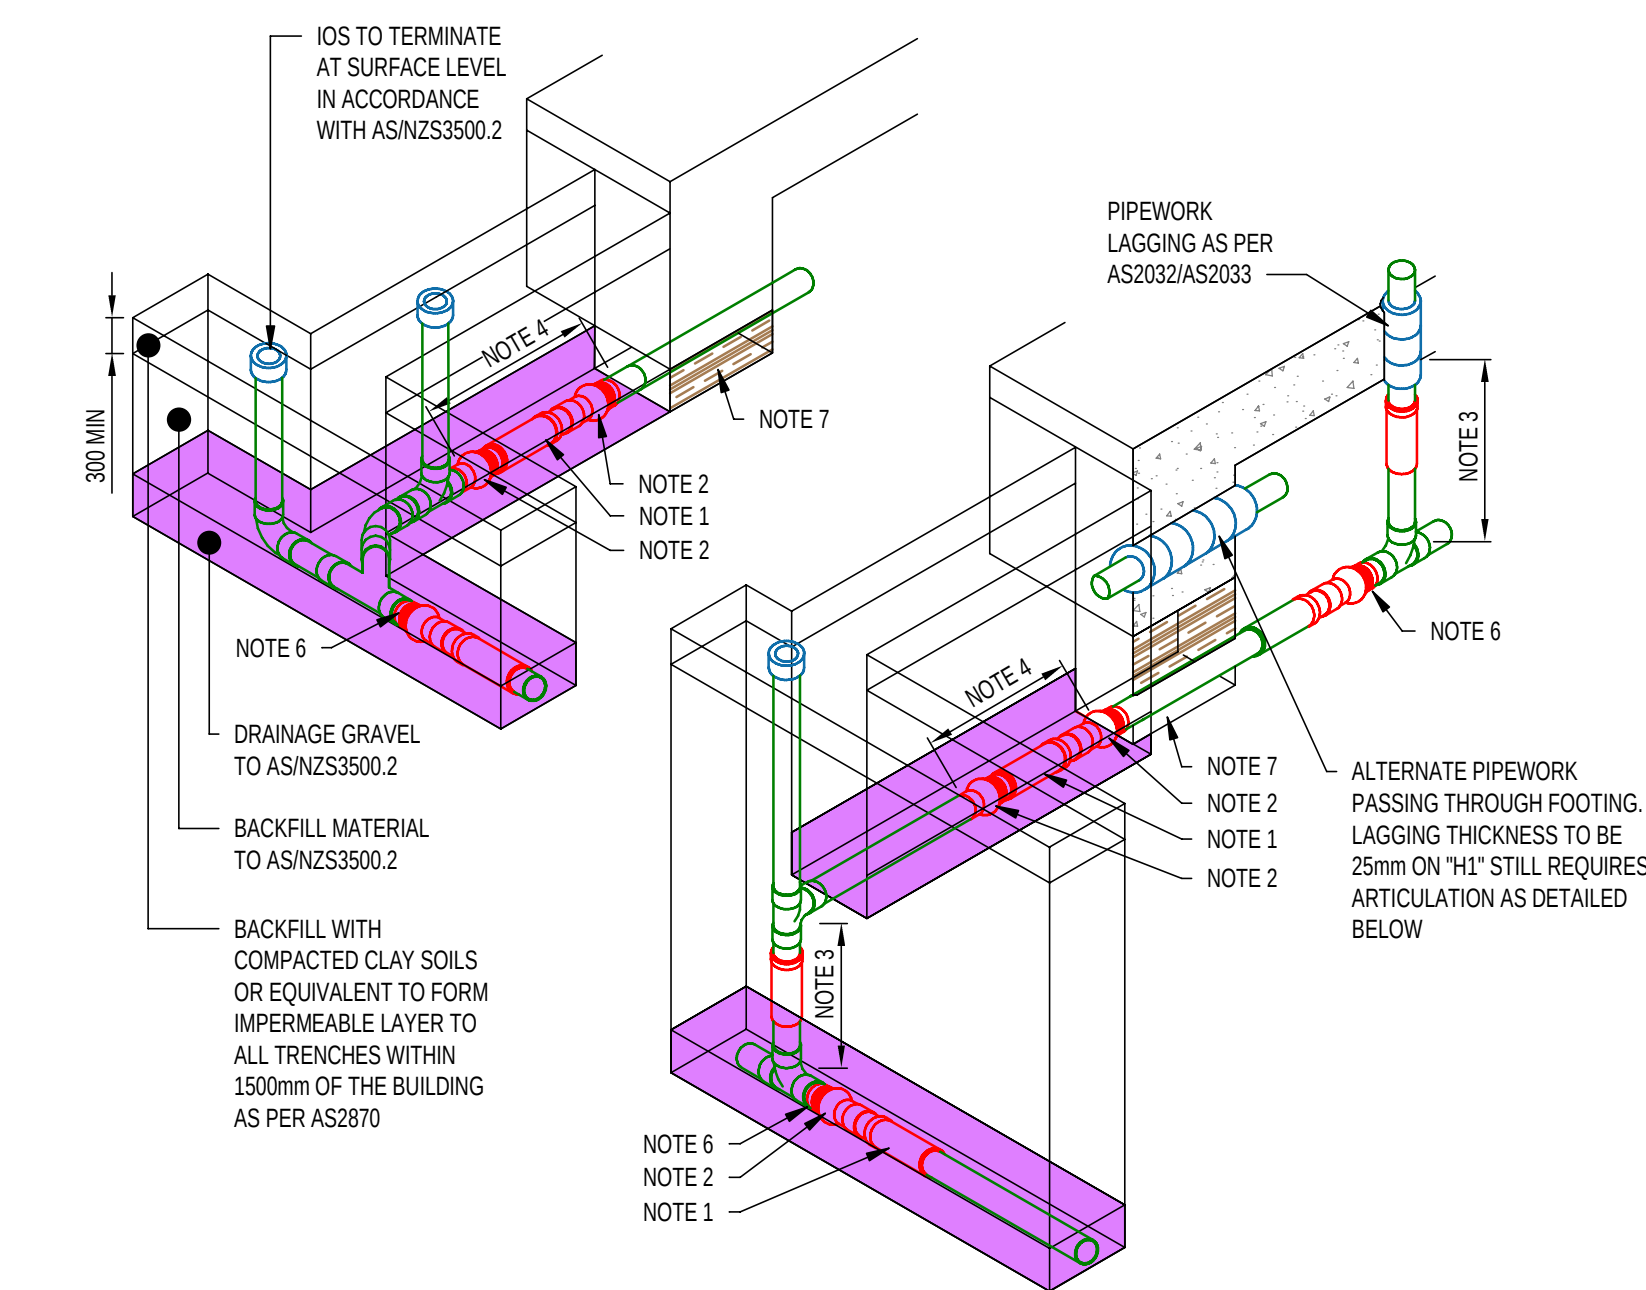

1 IN GROUND DRAINAGE (STORMWATER & SANITARY)
NTS

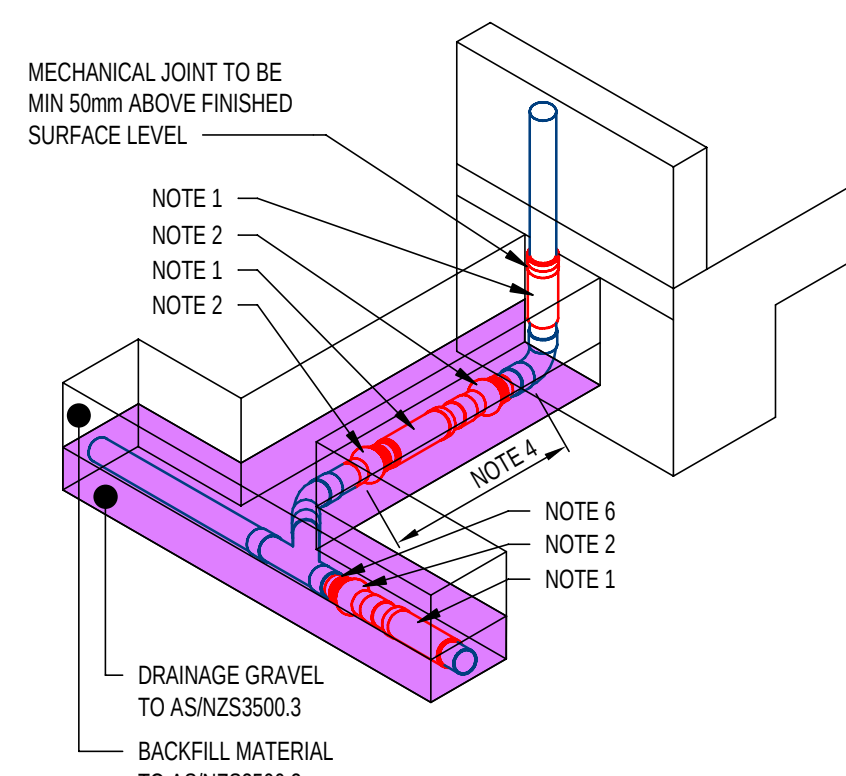


2 STORMWATER DOWNPIPES

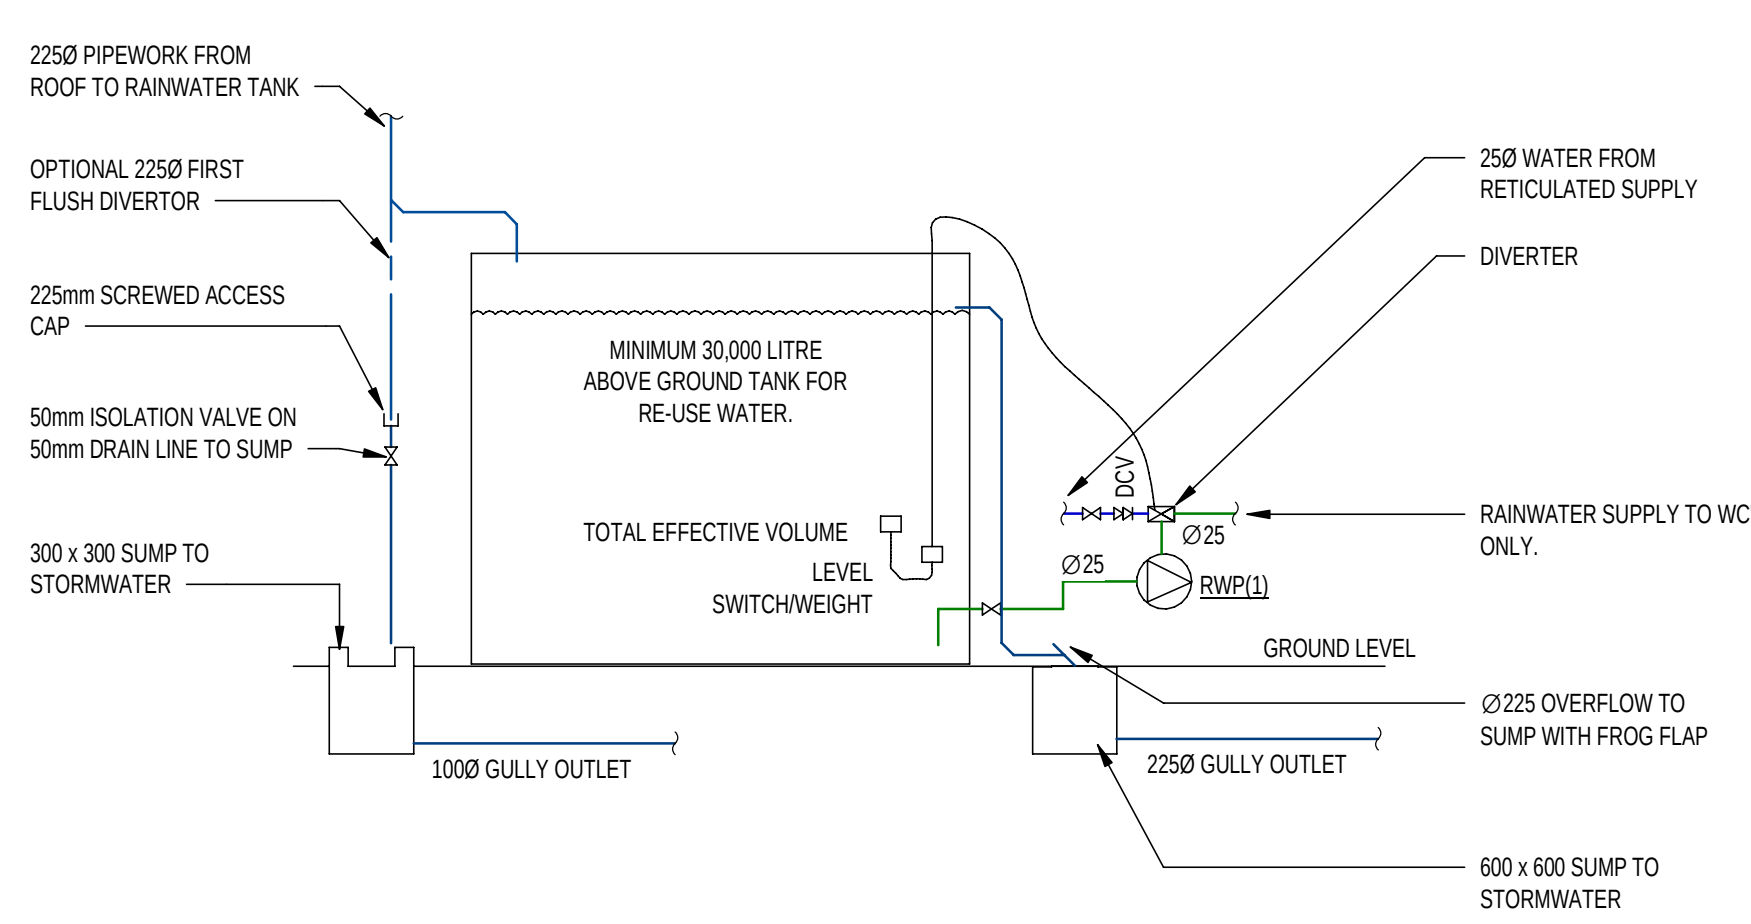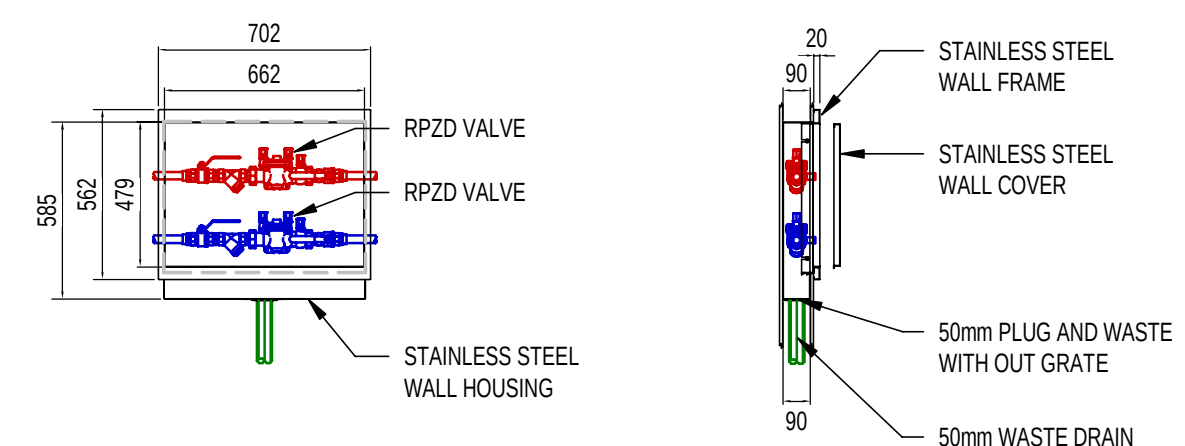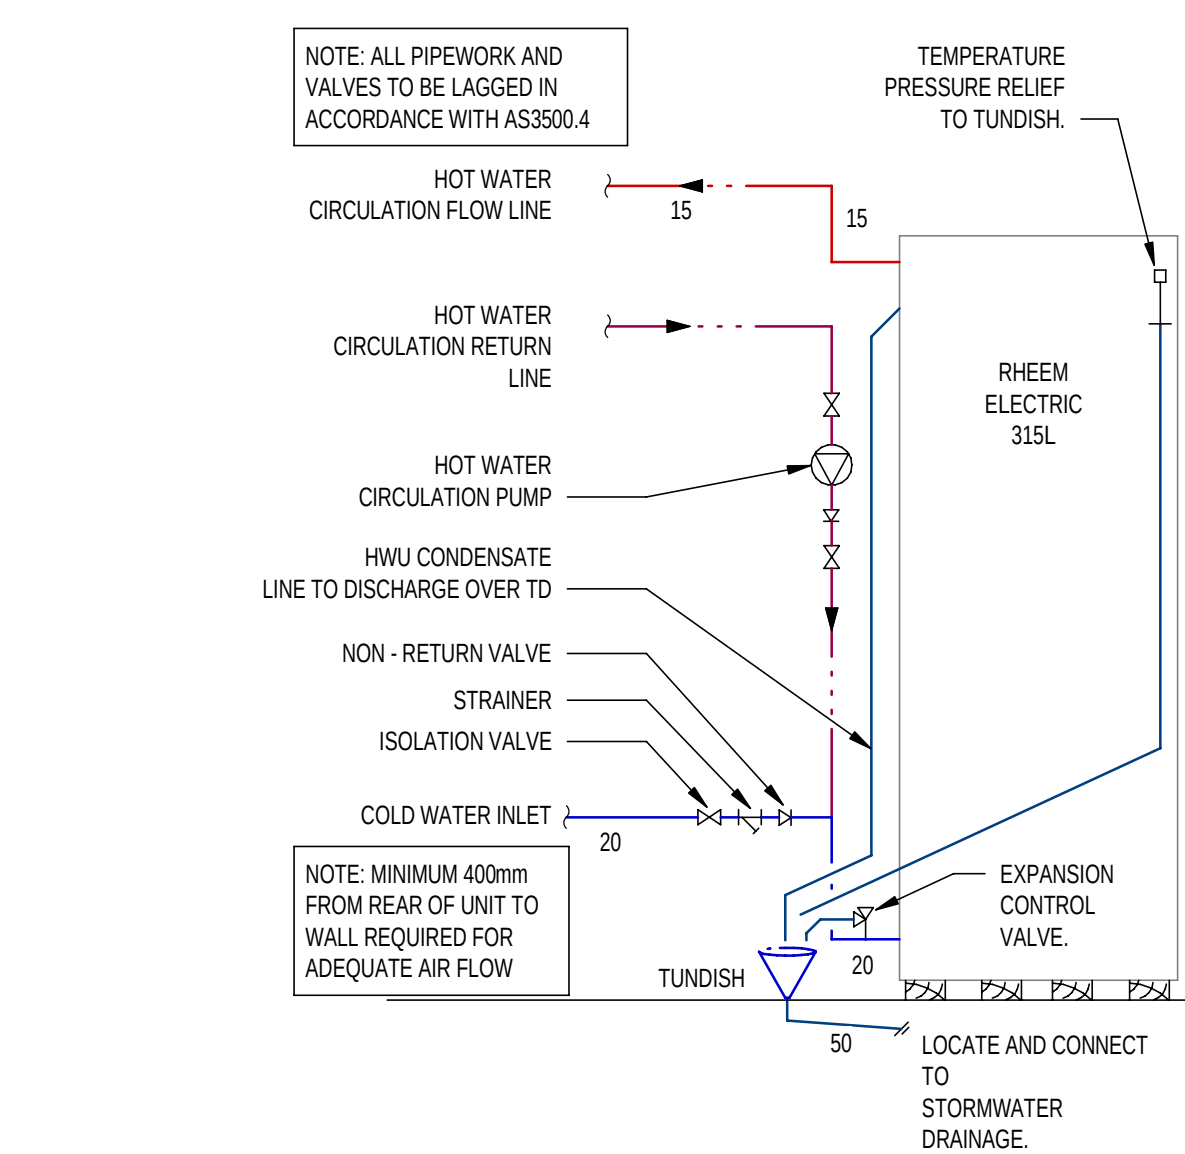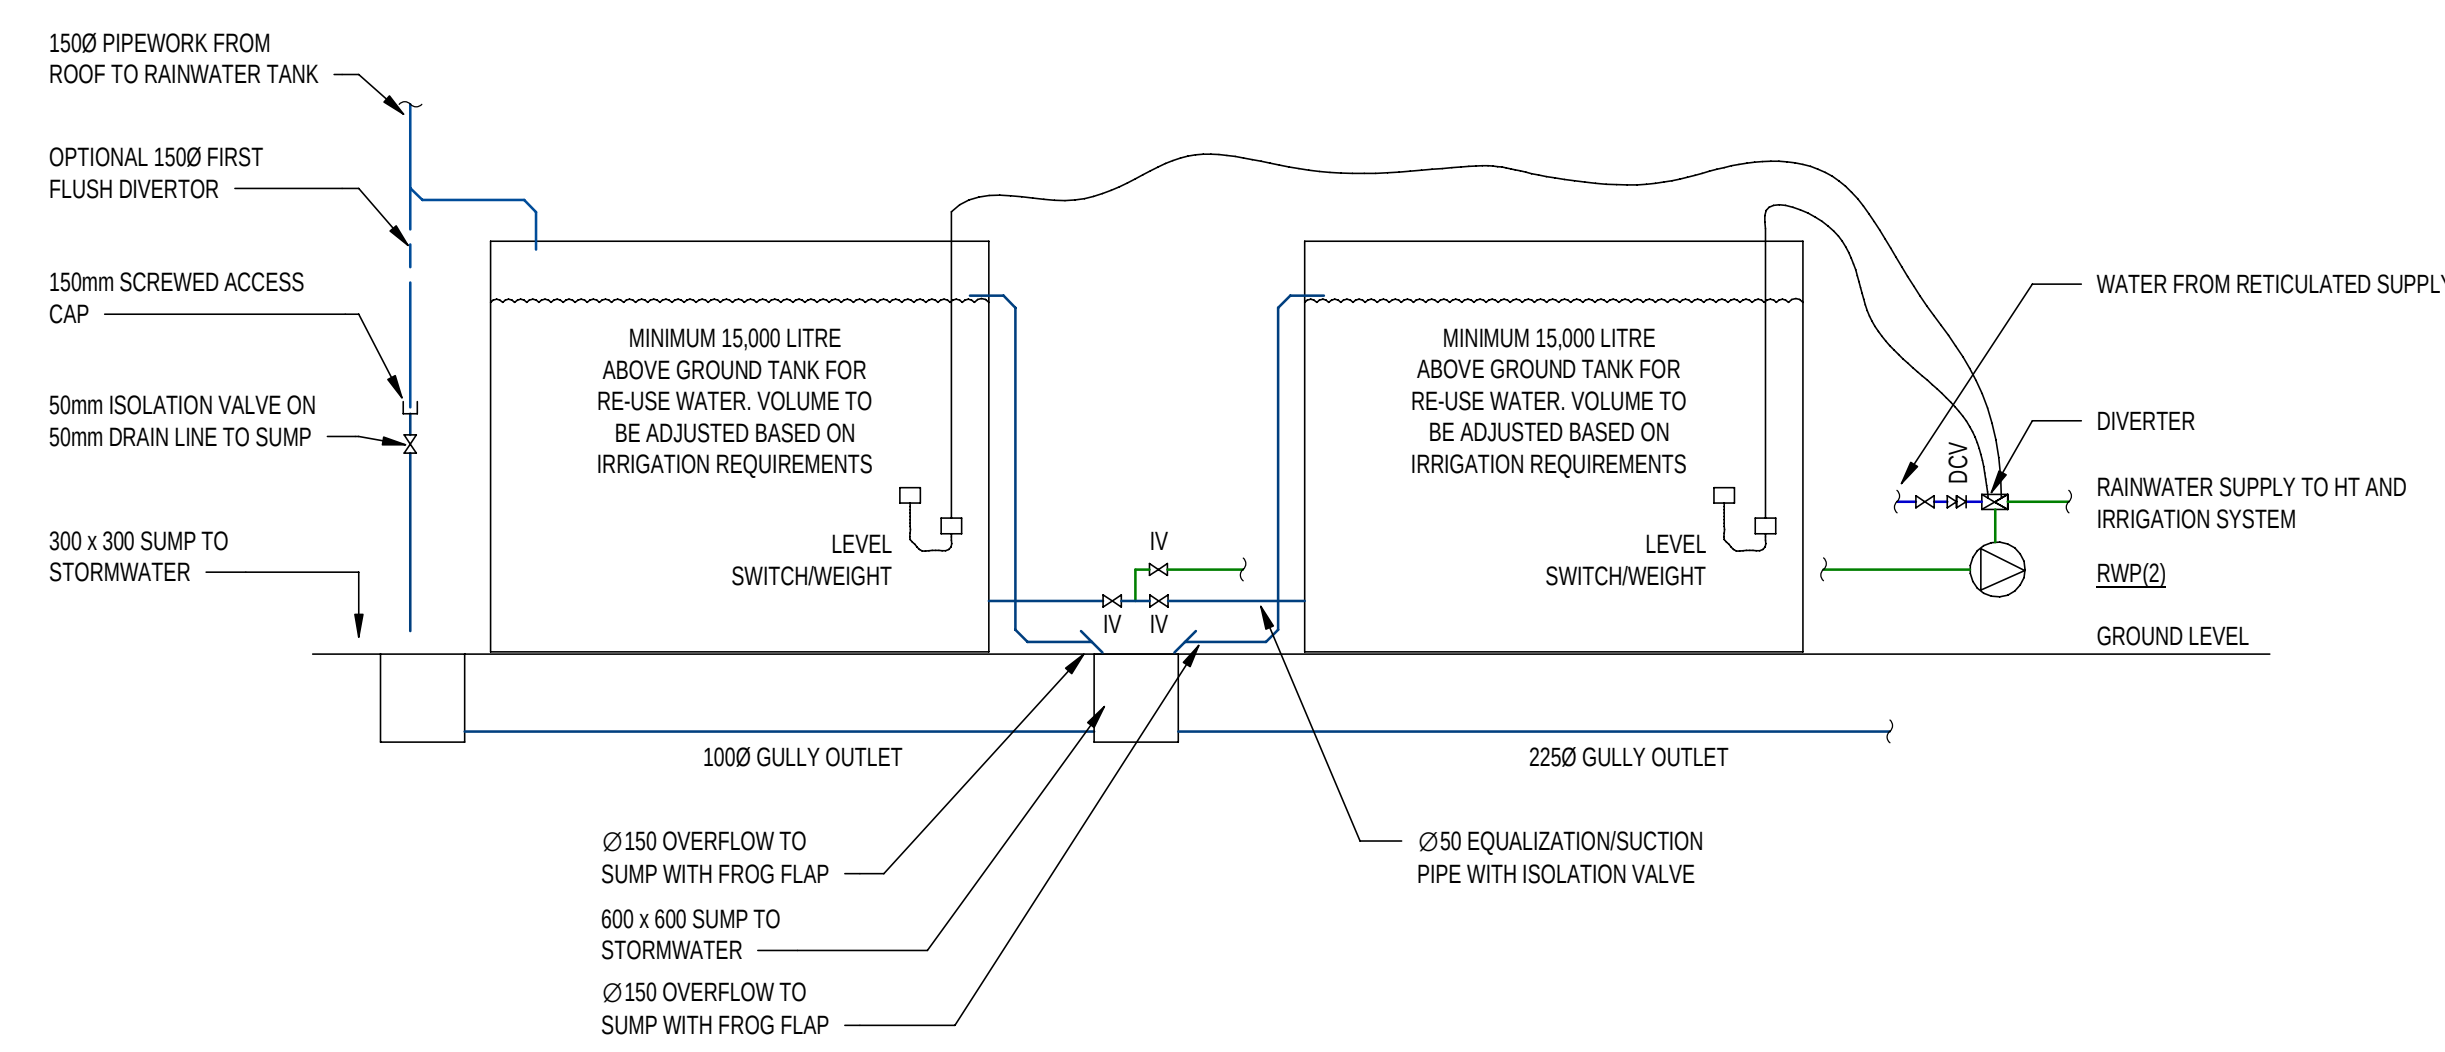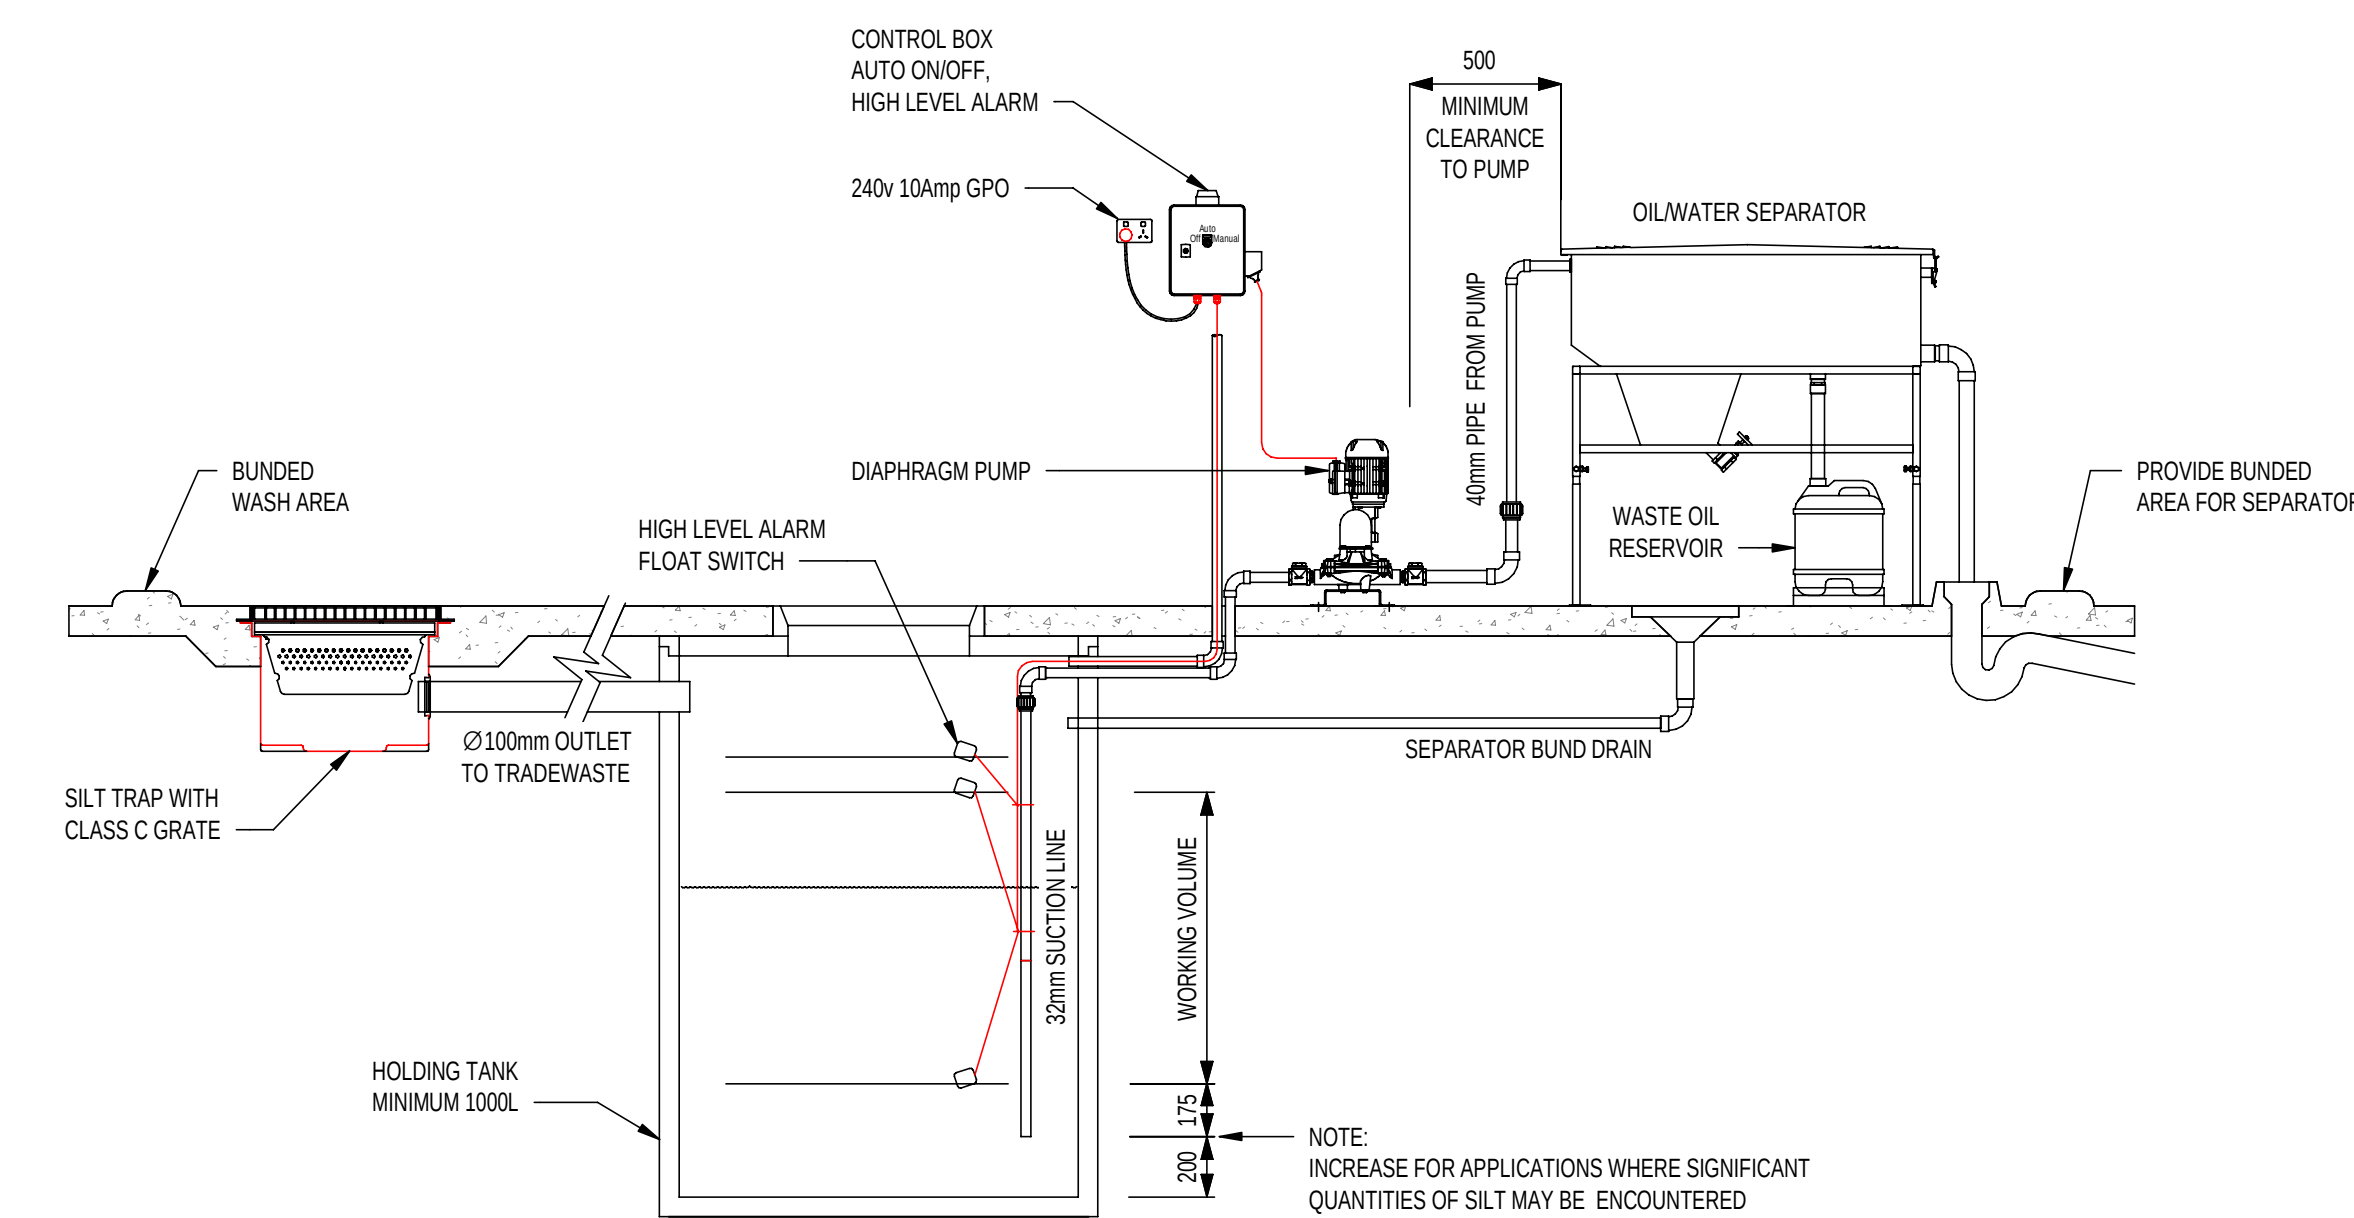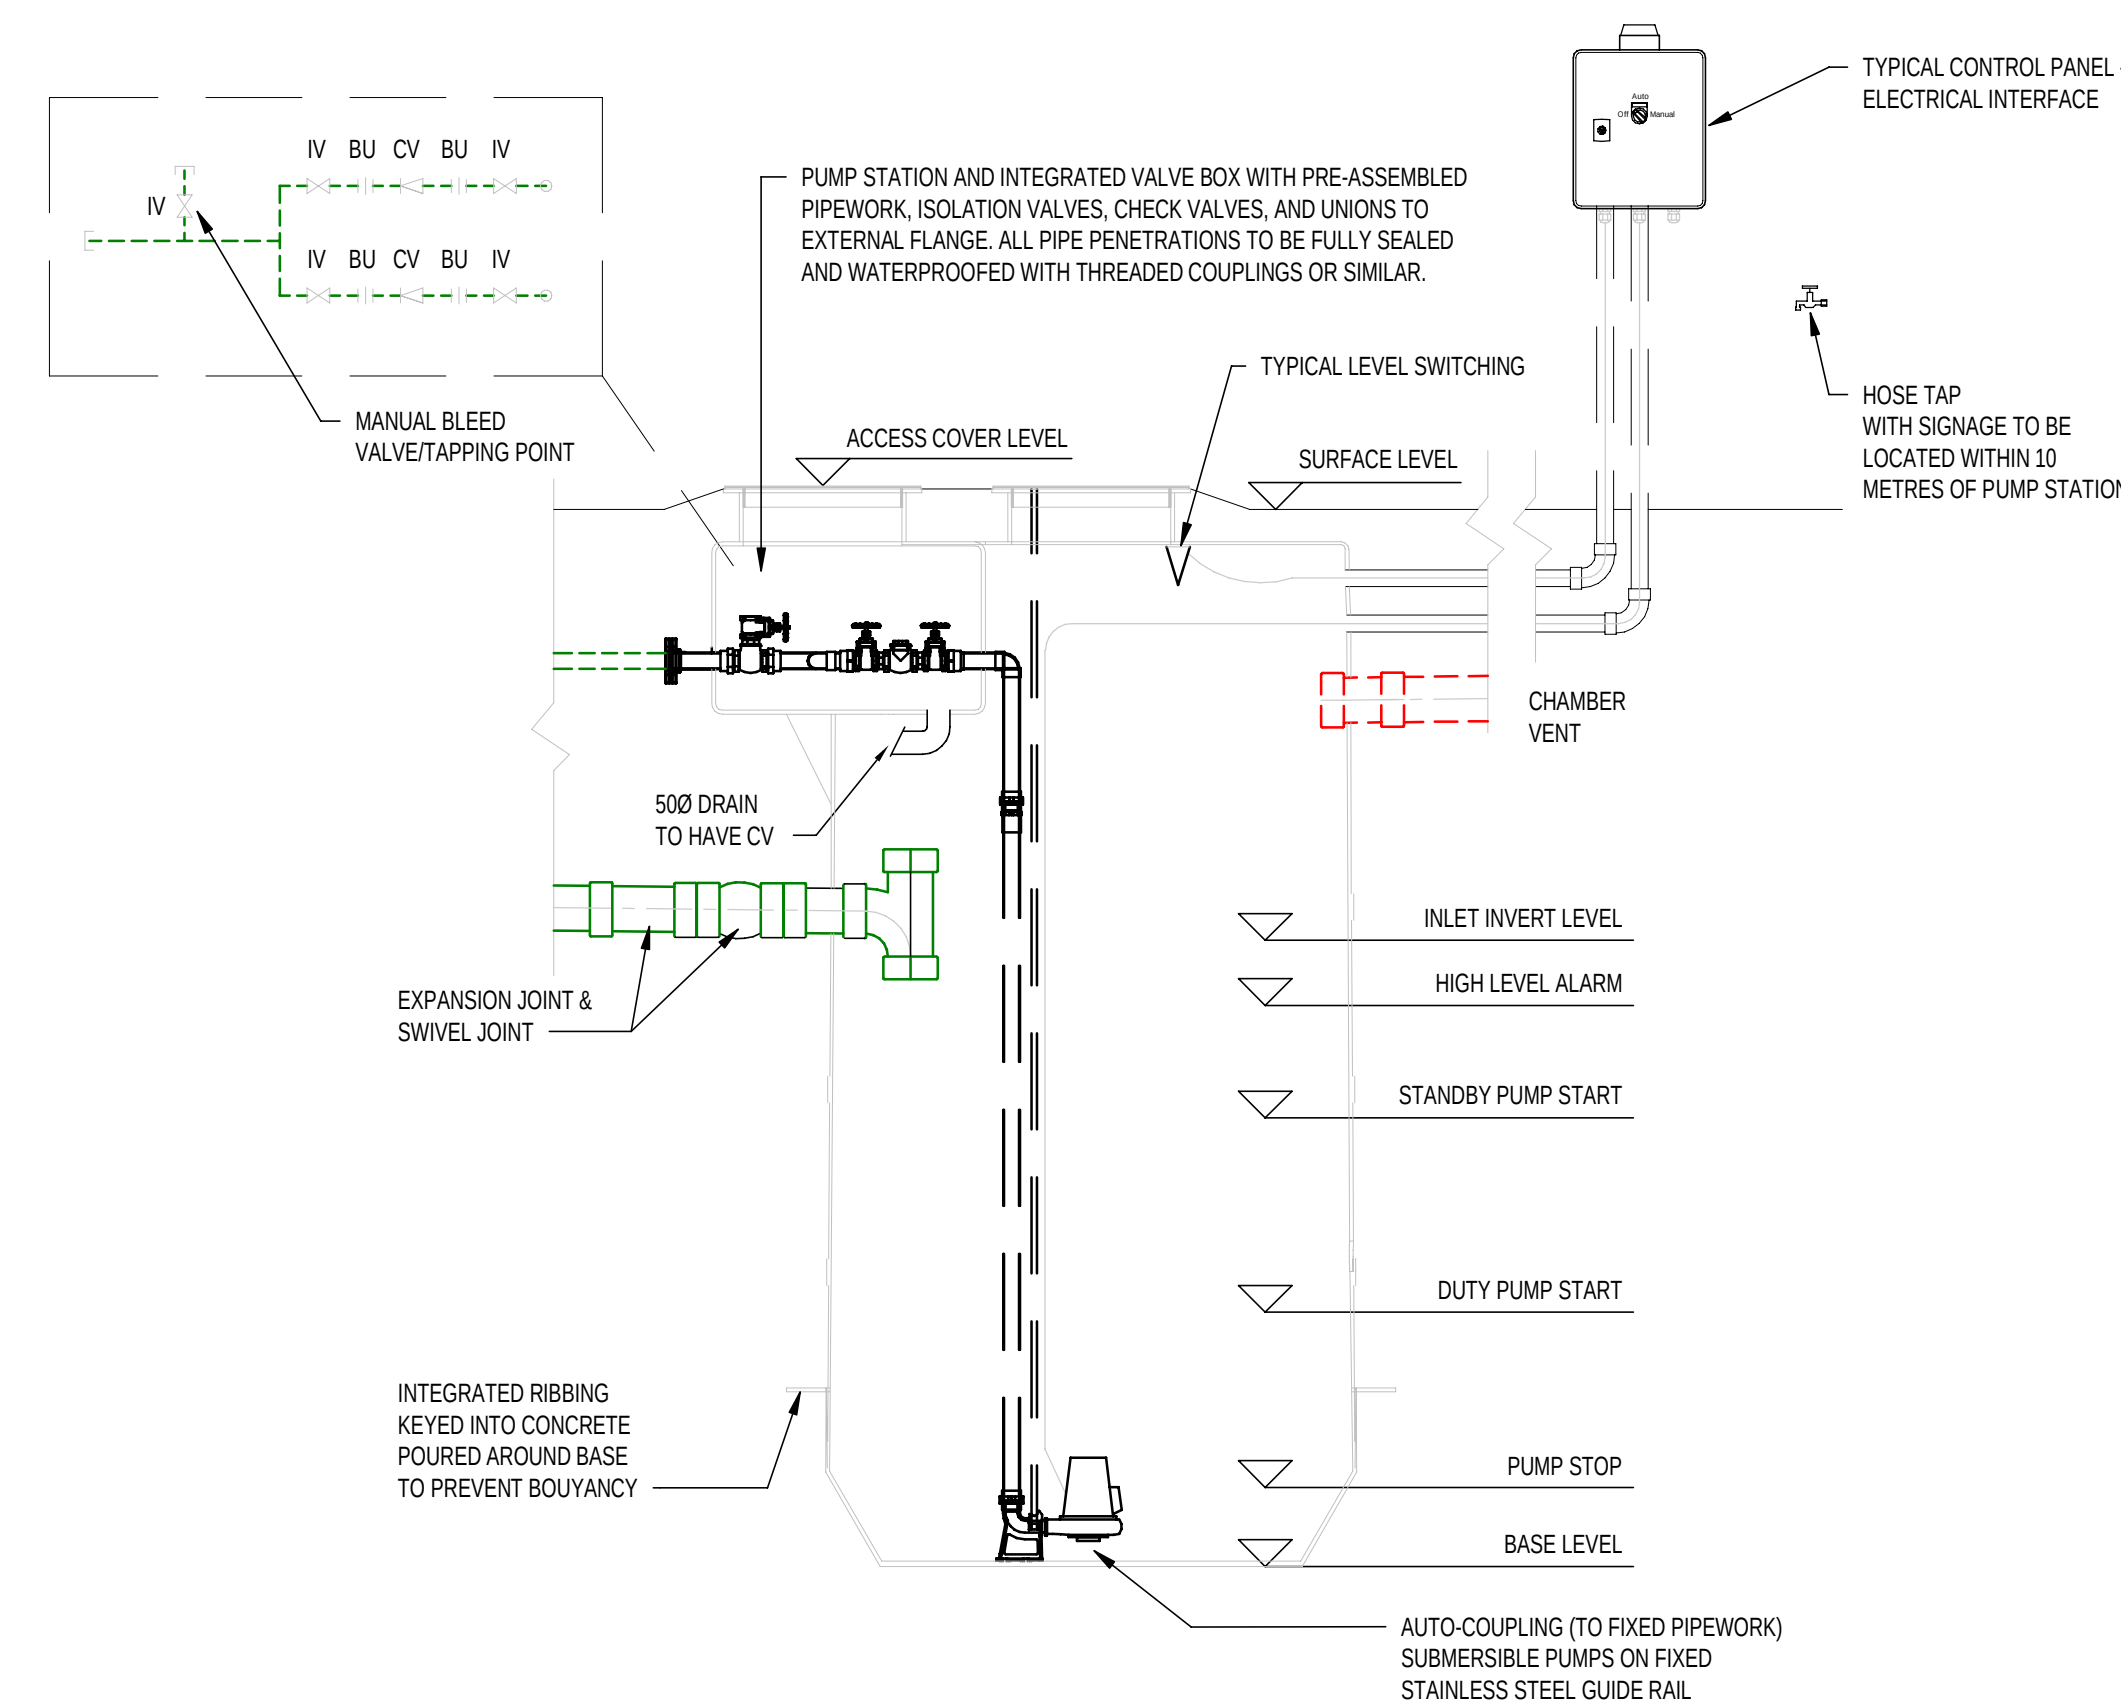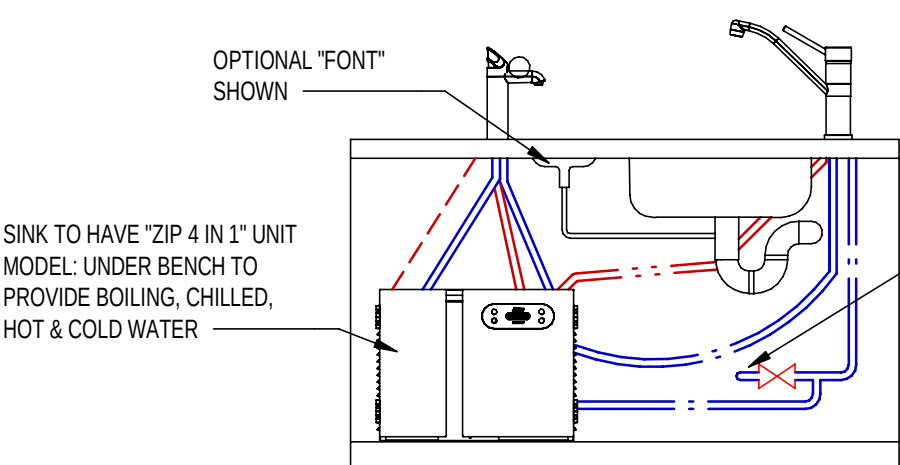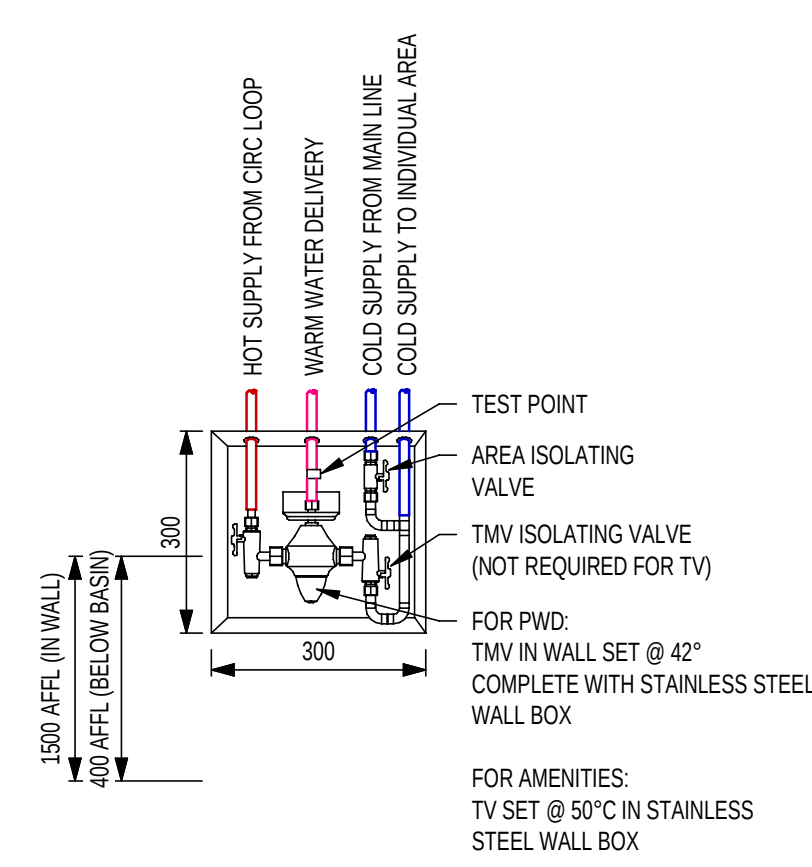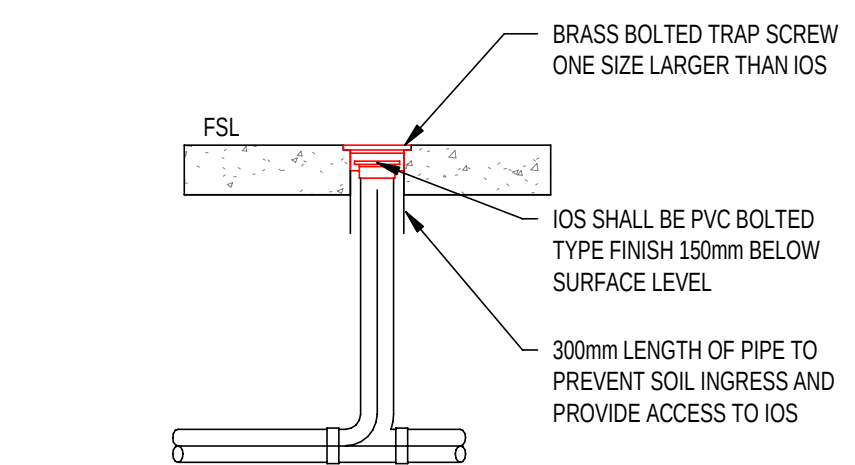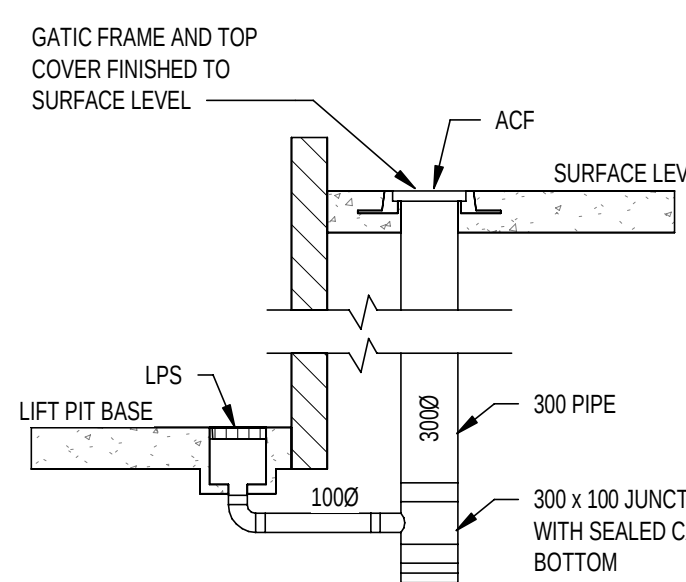

INFORMATION REFLECTED ON THIS DRAWING REPRESENTS HYDRAULIC SERVICES DESIGN DEVELOPED FOR D&C TENDER ADVISE ONLY, AND SHOULD NOT BE REGARDED AS COMPLETE. THE D&C CONTRACTOR SHOULD REFER TO ALL ASSOCIATED ARCHITECTURAL AND OTHER DISCIPLINE DRAWINGS, PROJECT BRIEFS AND CLIENT REQUIREMENTS AND MAKE ADEQUATE ALLOWANCES FOR ALL NECESSARY HYDRAULIC SERVICES WORKS TO MEET THESE REQUIREMENTS, EQUIPMENT SCHEDULES AND COMPLIANCE WITH THE NCC & APPROPRIATE AUSTRALIAN STANDARDS

A		12.08.2020		SH		ISSUED FOR BIC TENDER		AA		SM	
REV		DATE		BY		DESCRIPTION		CHK		APP	
DRAWING STATUS											
DESIGN DEVELOPMENT											
											
900 Ann Street, Level 12, Fortitude Valley 4006 Tel: +61-7-3854-6200 Fax: +61-7-3854-6500 http://www.wsp.com											
CLIENT											
CQU											
ARCHITECT											
THOMSON ADSETT / PEDDLE THORP											
PROJECT											
CQU ROCKHAMPTON TAFE CONSOLIDATION											
TITLE											
HYDRAULIC SERVICES TYPICAL DETAILS											
SCALE @ A1		N.T.S		CHECKED		AA		APPROVED		SM	
PROJECT NUMBER		P5229518		DRAWN		SH		DATE		JAN 2006	
DRAWING NO.										REV	
00-HY-DR-100-A00-00-02										A	
© WSP Australia Pty Ltd											

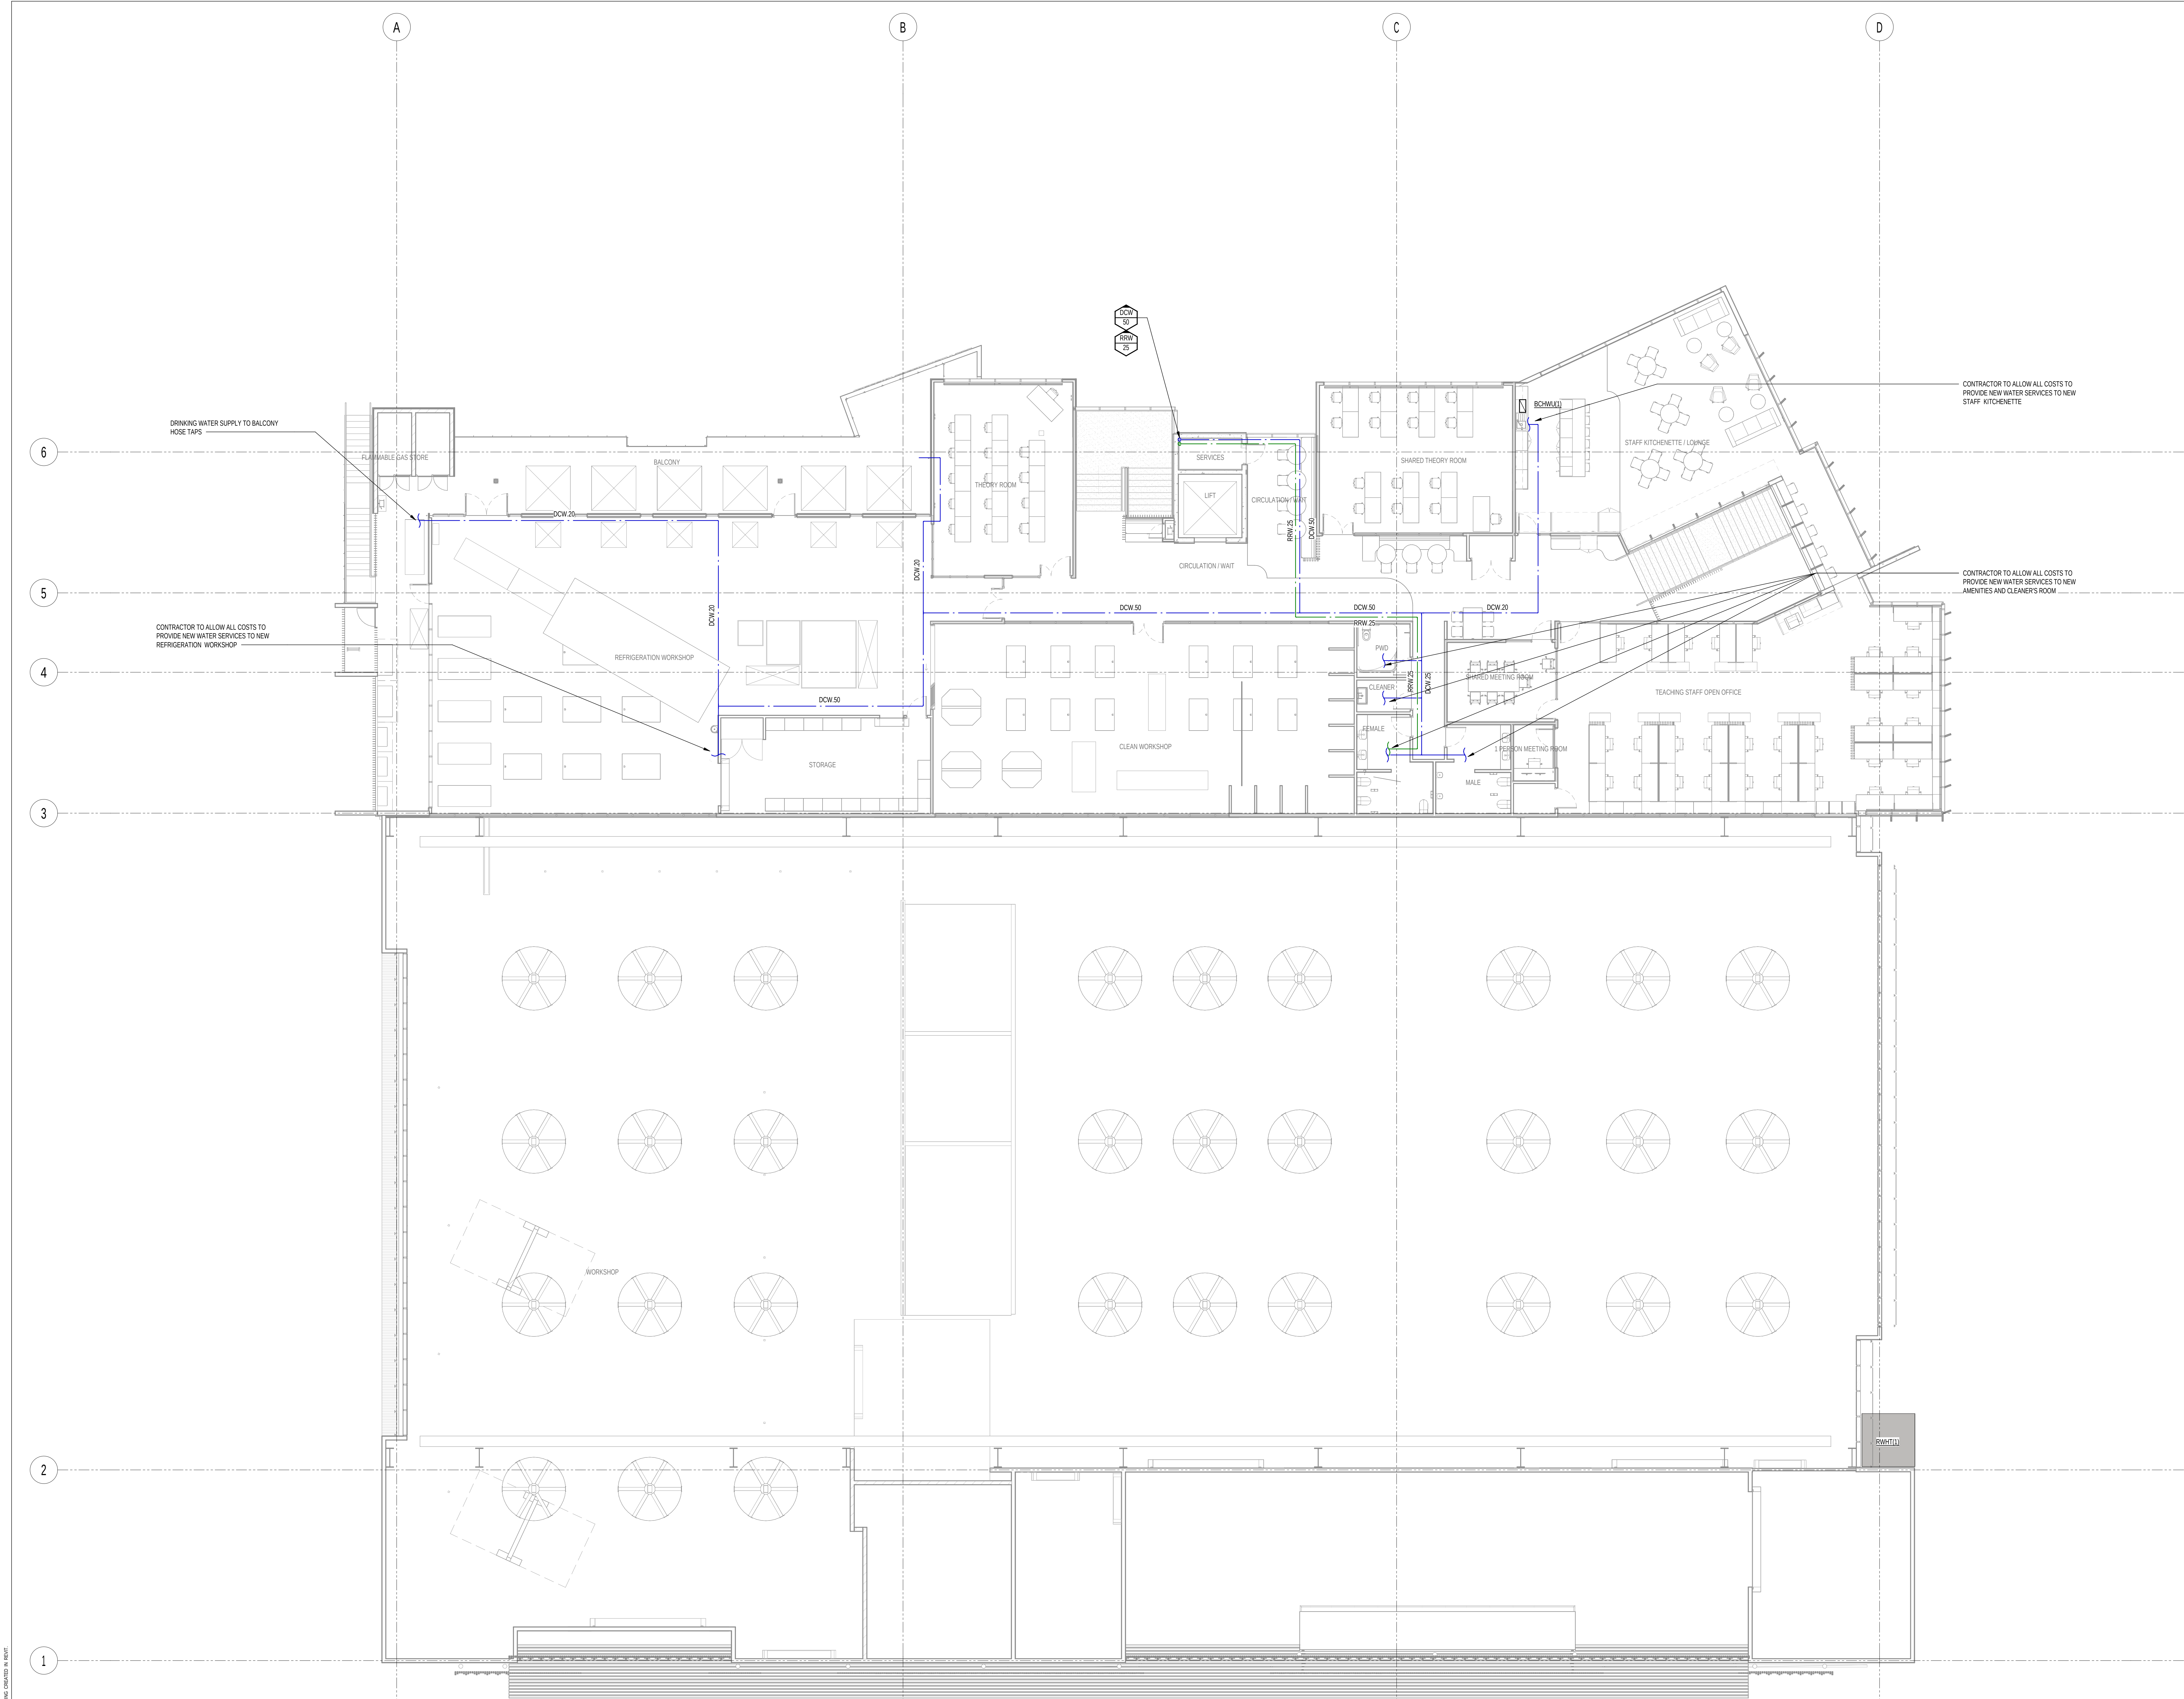

INFORMATION REFLECTED ON THIS DRAWING REPRESENTS HYDRAULIC SERVICES DESIGN DEVELOPED FOR D&C TENDER ADVICE ONLY, AND SHOULD NOT BE REGARDED AS COMPLETE. THE D&C CONTRACTOR SHOULD REFER TO ALL ASSOCIATED ARCHITECTURAL AND OTHER DISCIPLINE DRAWINGS, PROJECT BRIEFS AND CLIENT REQUIREMENTS AND MAKE ADEQUATE ALLOWANCES FOR ALL NECESSARY HYDRAULIC SERVICES WORKS TO MEET THESE REQUIREMENTS, EQUIPMENT SCHEDULES AND COMPLIANCE WITH THE NCC & APPROPRIATE AUSTRALIAN STANDARDS

WATER NOTES:

1. ALLOW ALL COSTS TO RETICULATE ALL HOT AND COLD WATER FROM AREA ISOLATION OR TMV TO FIXTURES WITHIN THE ROOM.
2. ALL FIXTURES ARE TO HAVE MINI ISOLATION VALVES AT POINT OF CONNECTION FOR TAPWARE WITH FLEXIBLE HOSES, OR ARE TO BE ISOLATED BY MEANS OF ISOLATING ONLY THE ROOM INDEPENDENTLY FROM THE REMAINDER OF THE BUILDING.
3. ALL PENETRATIONS OR CAST THROUGH CONCRETE STRUCTURE ARE TO BE APPROVED BY THE STRUCTURAL ENGINEER.
4. ALL REDUNDANT PENETRATIONS THROUGH STRUCTURAL ELEMENTS ARE TO BE MADE GOOD TO THE SATISFACTION OF THE STRUCTURAL ENGINEER.
5. SERVICES PASSING THROUGH A FIRE RATED STRUCTURE SHALL HAVE FIRE COLLARS (OR OTHER APPROVED FIRE PROTECTION METHOD) RATED TO THE MINIMUM FRL OF THE STRUCTURE IT IS PENETRATING.
6. WHERE METAL PIPEWORK PASSES THROUGH STRUCTURE WHICH IS TO BE FIRE RATED, MINIMISE THE PENETRATION SIZE AND PACK AROUND PIPEWORK WITH APPROVED INTUMESCENT SEALANT TO THE NCC C4D15 AND THE MANUFACTURERS REQUIREMENTS TO ENSURE OPENINGS ARE COMPLETELY CLOSED IN THE EVENT OF A FIRE.
7. DOCUMENTATION MAY NOT INDICATE ALL LOCATIONS OF REQUIRED VALVING. FINAL REQUIREMENTS TO BE DOCUMENTED IN FURTHER DESIGN DEVELOPMENT.
8. WHERE REQUIRED PROVIDE CEILING ACCESS PANELS TO MAINTAIN ACCESS TO ALL VALVING, METERS, TMV'S ETC.
9. PROVIDE BACKFLOW PREVENTION DEVICES AS REQUIRED TO ENSURE THAT ZONE PROTECTION IS RETAINED IN ACCORDANCE WITH AS/NZS3500.1 AND LOCAL AUTHORITY REQUIREMENTS.
10. SERVICES PASSING THROUGH A FIRE RATED STRUCTURE SHALL HAVE FIRE COLLARS (OR OTHER APPROVED FIRE PROTECTION METHOD) RATED TO THE MINIMUM FRL OF THE STRUCTURE IT IS PENETRATING.
11. WHERE METAL PIPEWORK PASSES THROUGH STRUCTURE WHICH IS TO BE FIRE RATED, MINIMISE THE PENETRATION SIZE AND PACK AROUND PIPEWORK WITH APPROVED INTUMESCENT SEALANT TO THE NCC C4D15 AND THE MANUFACTURERS REQUIREMENTS TO ENSURE OPENINGS ARE COMPLETELY CLOSED IN THE EVENT OF A FIRE.
12. CONTRACTOR TO REFER TO STRUCTURAL DRAWINGS BEFORE PENETRATING THROUGH SLAB. ALLOW ALL COSTS FOR PENETRATIONS AND REINSTATEMENT AS REQUIRED.
13. CONTRACTOR TO COORDINATE PROVISIONS WITH FINAL FFEE LAYOUT PROVIDED BY ARCHITECT.

B	12.02.2026	SH	ISSUED FOR D&C TENDER	AA	SM
A	10.02.2026	SH	ISSUED FOR D&C TENDER	AA	SM
REV	DATE	BY	DESCRIPTION	CHK	APP

DESIGN DEVELOPMENT



900 Ann Street, Level 12, Fortitude Valley 4006
Tel: +61-7-3854-6200 Fax: +61-7-3854-6500
<http://www.wsp.com>

CLIENT: CQU

ARCHITECT: THOMSON ADSETT / PEDDLE THORP

PROJECT: CQU ROCKHAMPTON TAFE CONSOLIDATION


TITLE: HYDRAULIC SERVICES
NEW TRADES BUILDING - LEVEL 01 - WATER
SERVICES LAYOUT

SCALE: B/A1	CHECKED: AA	APPROVED: SM
PROJECT NUMBER: PS229518	DRAWN: SH	DATE: JAN 2026

DRAWING NO: NTB-HY-DR-520-L01-00-00

REV: B

© WSP Australia Pty Ltd

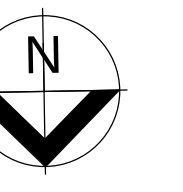

INFORMATION REFLECTED ON THIS DRAWING REPRESENTS HYDRAULIC SERVICES DESIGN DEVELOPED FOR D&C TENDER ADVISE ONLY, AND SHOULD NOT BE REGARDED AS COMPLETE. THE D&C CONTRACTOR SHOULD REFER TO ALL ASSOCIATED ARCHITECTURAL AND OTHER DISCIPLINE DRAWINGS, PROJECT BRIEFS AND CLIENT REQUIREMENTS AND MAKE ADEQUATE ALLOWANCES FOR ALL NECESSARY HYDRAULIC SERVICES WORKS TO MEET THESE REQUIREMENTS, EQUIPMENT SCHEDULES AND COMPLIANCE WITH THE NCC & APPROPRIATE AUSTRALIAN STANDARDS

DRAINAGE NOTES:

1. ALLOW ALL COSTS TO CONNECT SANITARY DRAINAGE TO ALL FIXTURES AS REQUIRED.
2. CO-ORDINATE ALL FLOOR WASTE LOCATIONS WITH ARCHITECT AND IN COMPLIANCE WITH THE NCC, AS/NZS3500.2, AS4298.1
3. ALLOW FOR PROVISION OF AN IOS IN COMPLIANCE WITH AS/NZS3500.2 AND TO ALLOW COMPLETE DRAIN ACCESS TO ALL DRAIN LINES COLLECTING MULTIPLE FIXTURES.
4. DOCUMENTATION MAY NOT INDICATE ALL VENTING REQUIREMENTS AND SHALL BE FINALISED DURING FURTHER DESIGN DEVELOPMENT. VENTING REQUIREMENTS TO BE IN ACCORDANCE WITH AS/NZS3500.2
5. ALL PENETRATIONS OR CAST THROUGH CONCRETE STRUCTURE ARE TO BE APPROVED BY THE STRUCTURAL ENGINEER.
6. ALLOW FOR DRAINAGE ARTICULATION AS REQUIRED AND SUBJECT TO THE FINAL SITE SOIL CLASSIFICATION IN ACCORDANCE WITH AS2870
7. VERIFY THAT ALL MECHANICAL DISCHARGE TEMPERATURES DO NOT EXCEED THE MAXIMUM ASSOCIATED WITH THE PREVIOUS MATERIAL. MECHANICAL CONTRACTOR TO PROVIDE DRAIN TEMPERING VALVE PRIOR TO DISCHARGE AS REQUIRED.
8. CO-ORDINATE WITH ARCHITECT, AND PROVIDE THRESHOLD PROTECTION AT ALL ENTRY POINTS TO THE BUILDING AS REQUIRED TO PREVENT THE INGRESS OF WIND DRIVEN RAIN.
9. CONTRACTOR TO CO-ORDINATE PROVISIONS WITH FINAL FF&E LAYOUT PROVIDED BY ARCHITECT.

EXISTING SERVICES

SERVICES SHOWN AS EXISTING HAVE BEEN INTERPOLATED FROM RECORD DRAWINGS. CONTRACTOR TO VERIFY LOCATIONS AND LEVELS PRIOR TO COMMENCEMENT OF WORK.

B	12.02.2024	SH	ISSUED FOR D&C TENDER	AA	SM
A	10.12.2023	SH	DRAWN WITH 2D DESIGN FOR REVIEW	NB	SM
REV	DATE	BY	DESCRIPTION	CHK	APP

DESIGN DEVELOPMENT



900 Ann Street, Level 12, Fortitude Valley 4006
Tel: +61-7-3854-6200 Fax: +61-7-3854-6500
<http://www.wsp.com>

CLIENT: CQU

ARCHITECT: THOMSON ADSETT / PEDDLE THORP

PROJECT: CQU ROCKHAMPTON TAFE CONSOLIDATION

TITLE: HYDRAULIC SERVICES
NEW TRADES BUILDING - GROUND LEVEL -
DRAINAGE LAYOUT


SCALE @ R/F: 1:100
PROJECT NUMBER: PS229518
DRAWN: SH
DATE: JAN 2024



DESIGNED: AA
APPROVED: SM

DRAWING NO: NTB-HY-DR-510-100-00-00

REV: B

© WSP Australia Pty Ltd

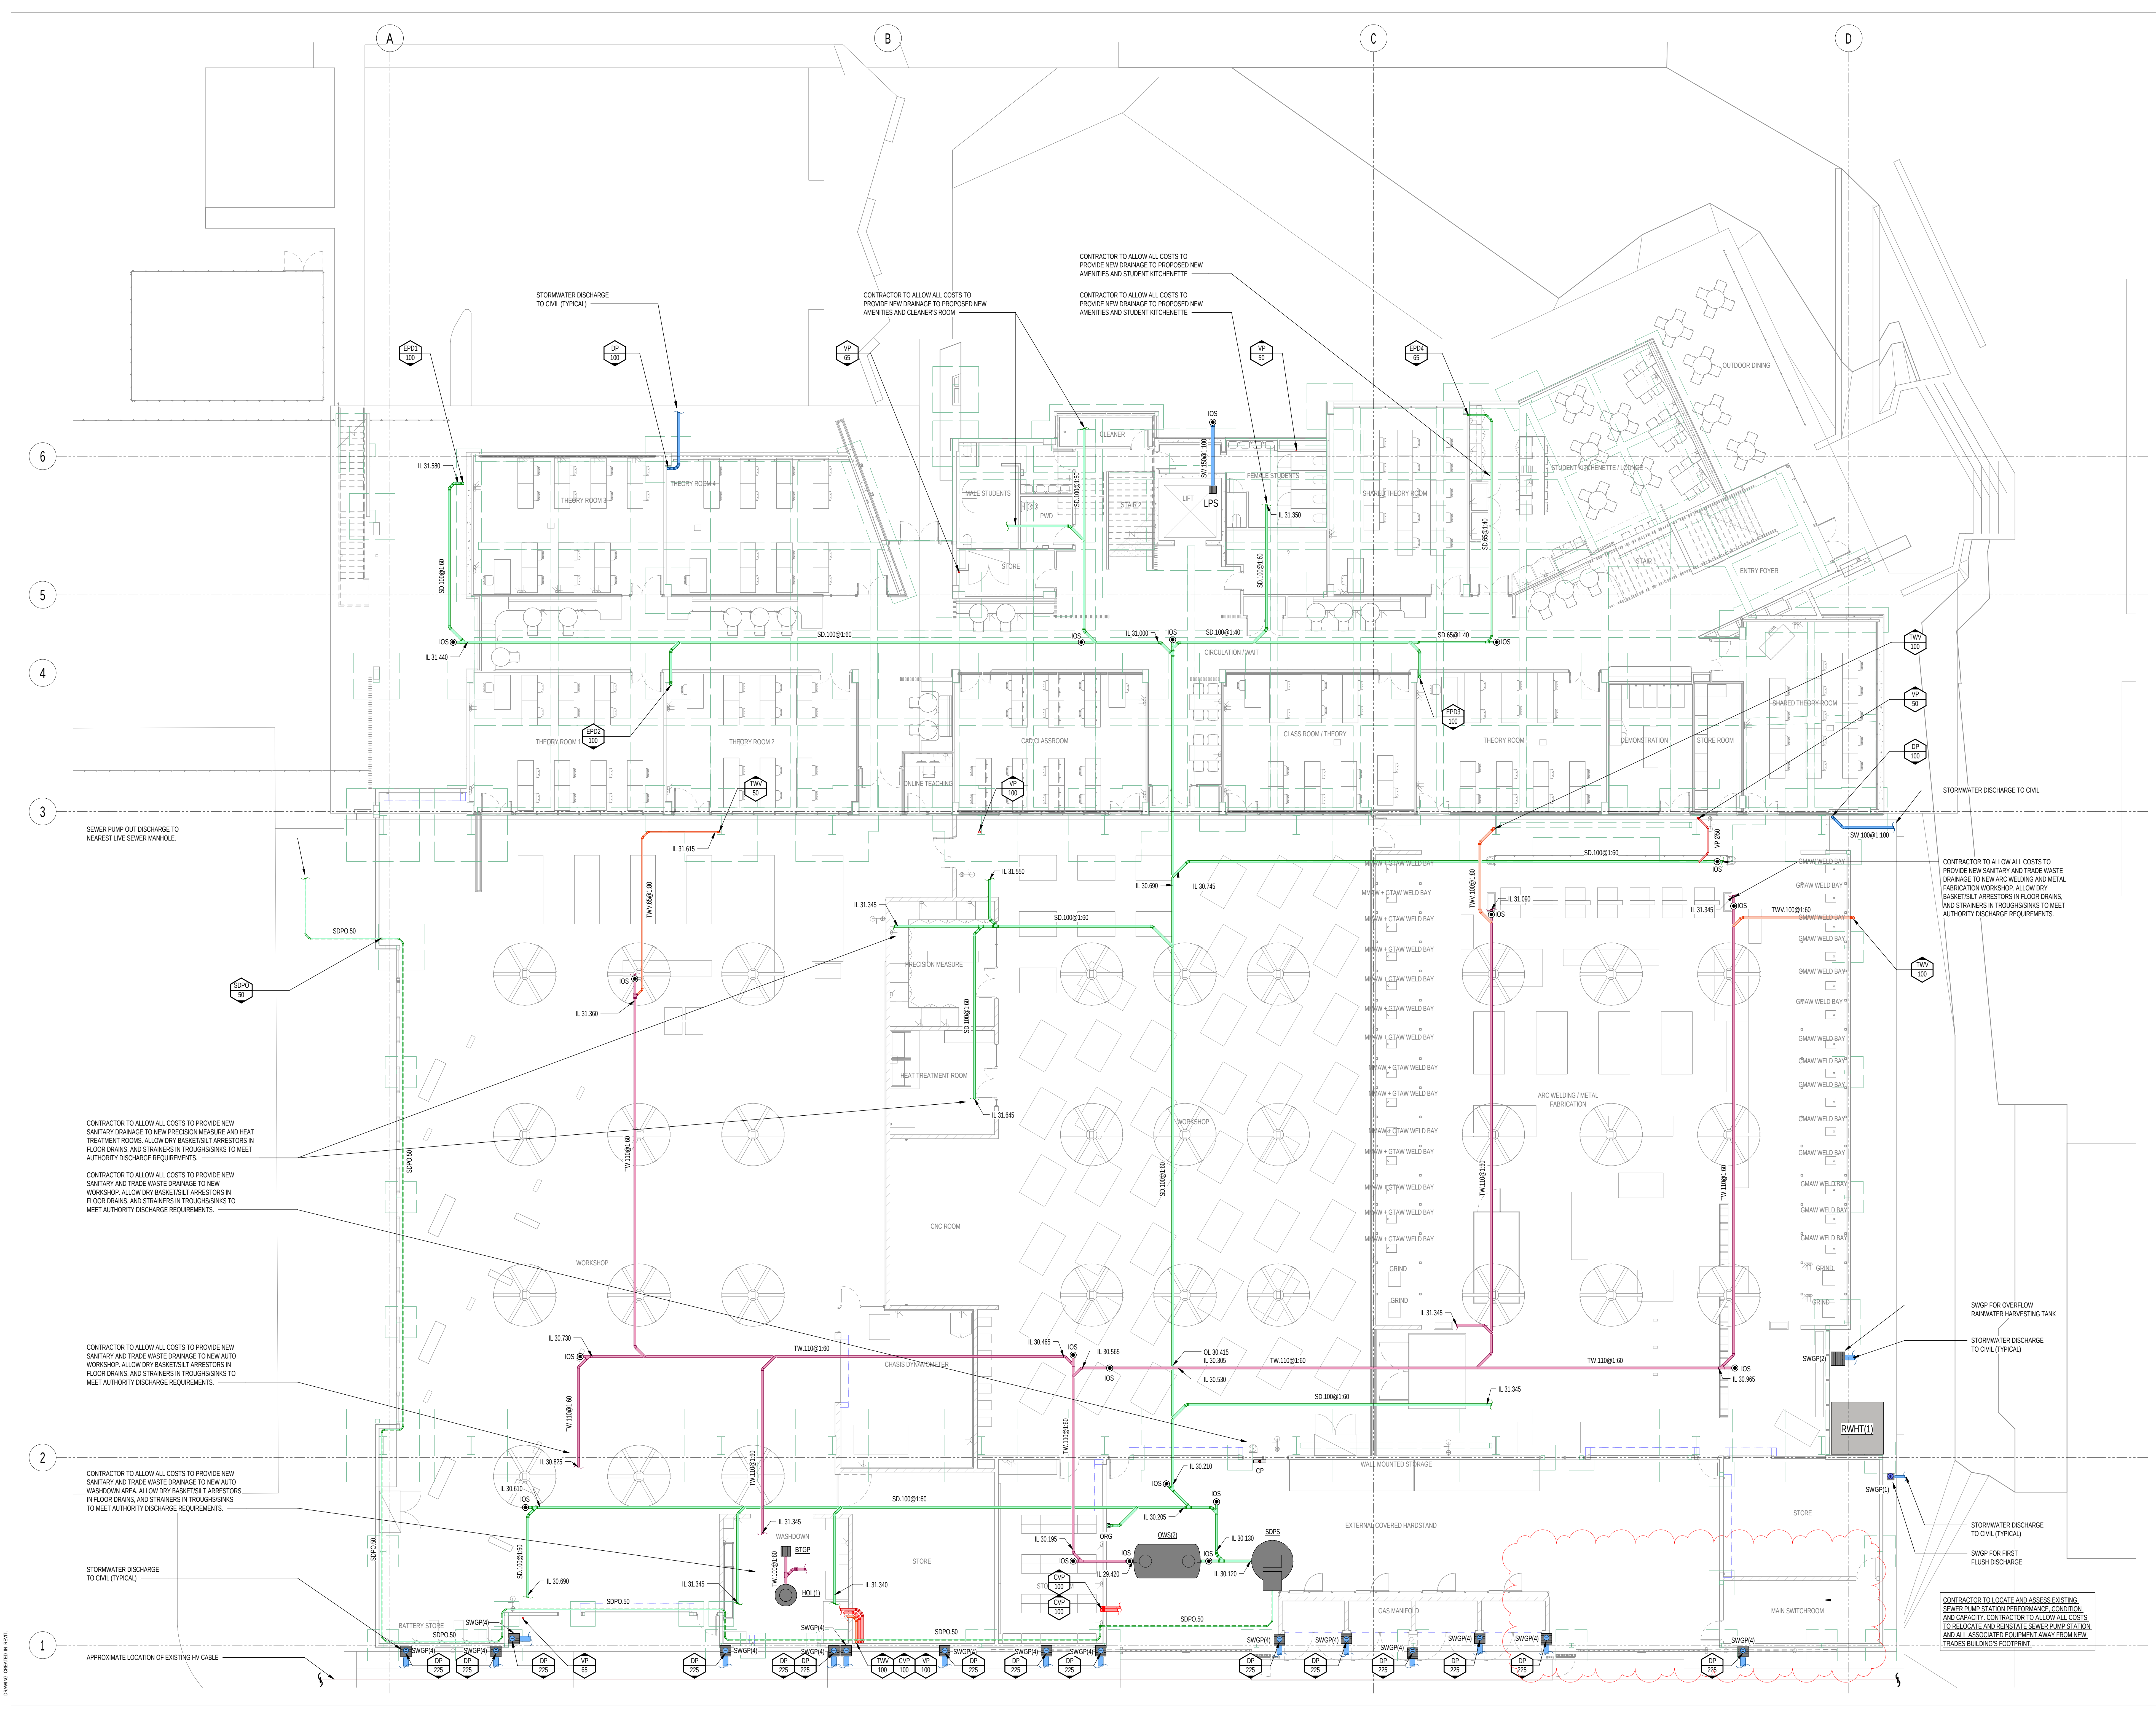

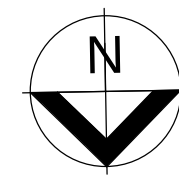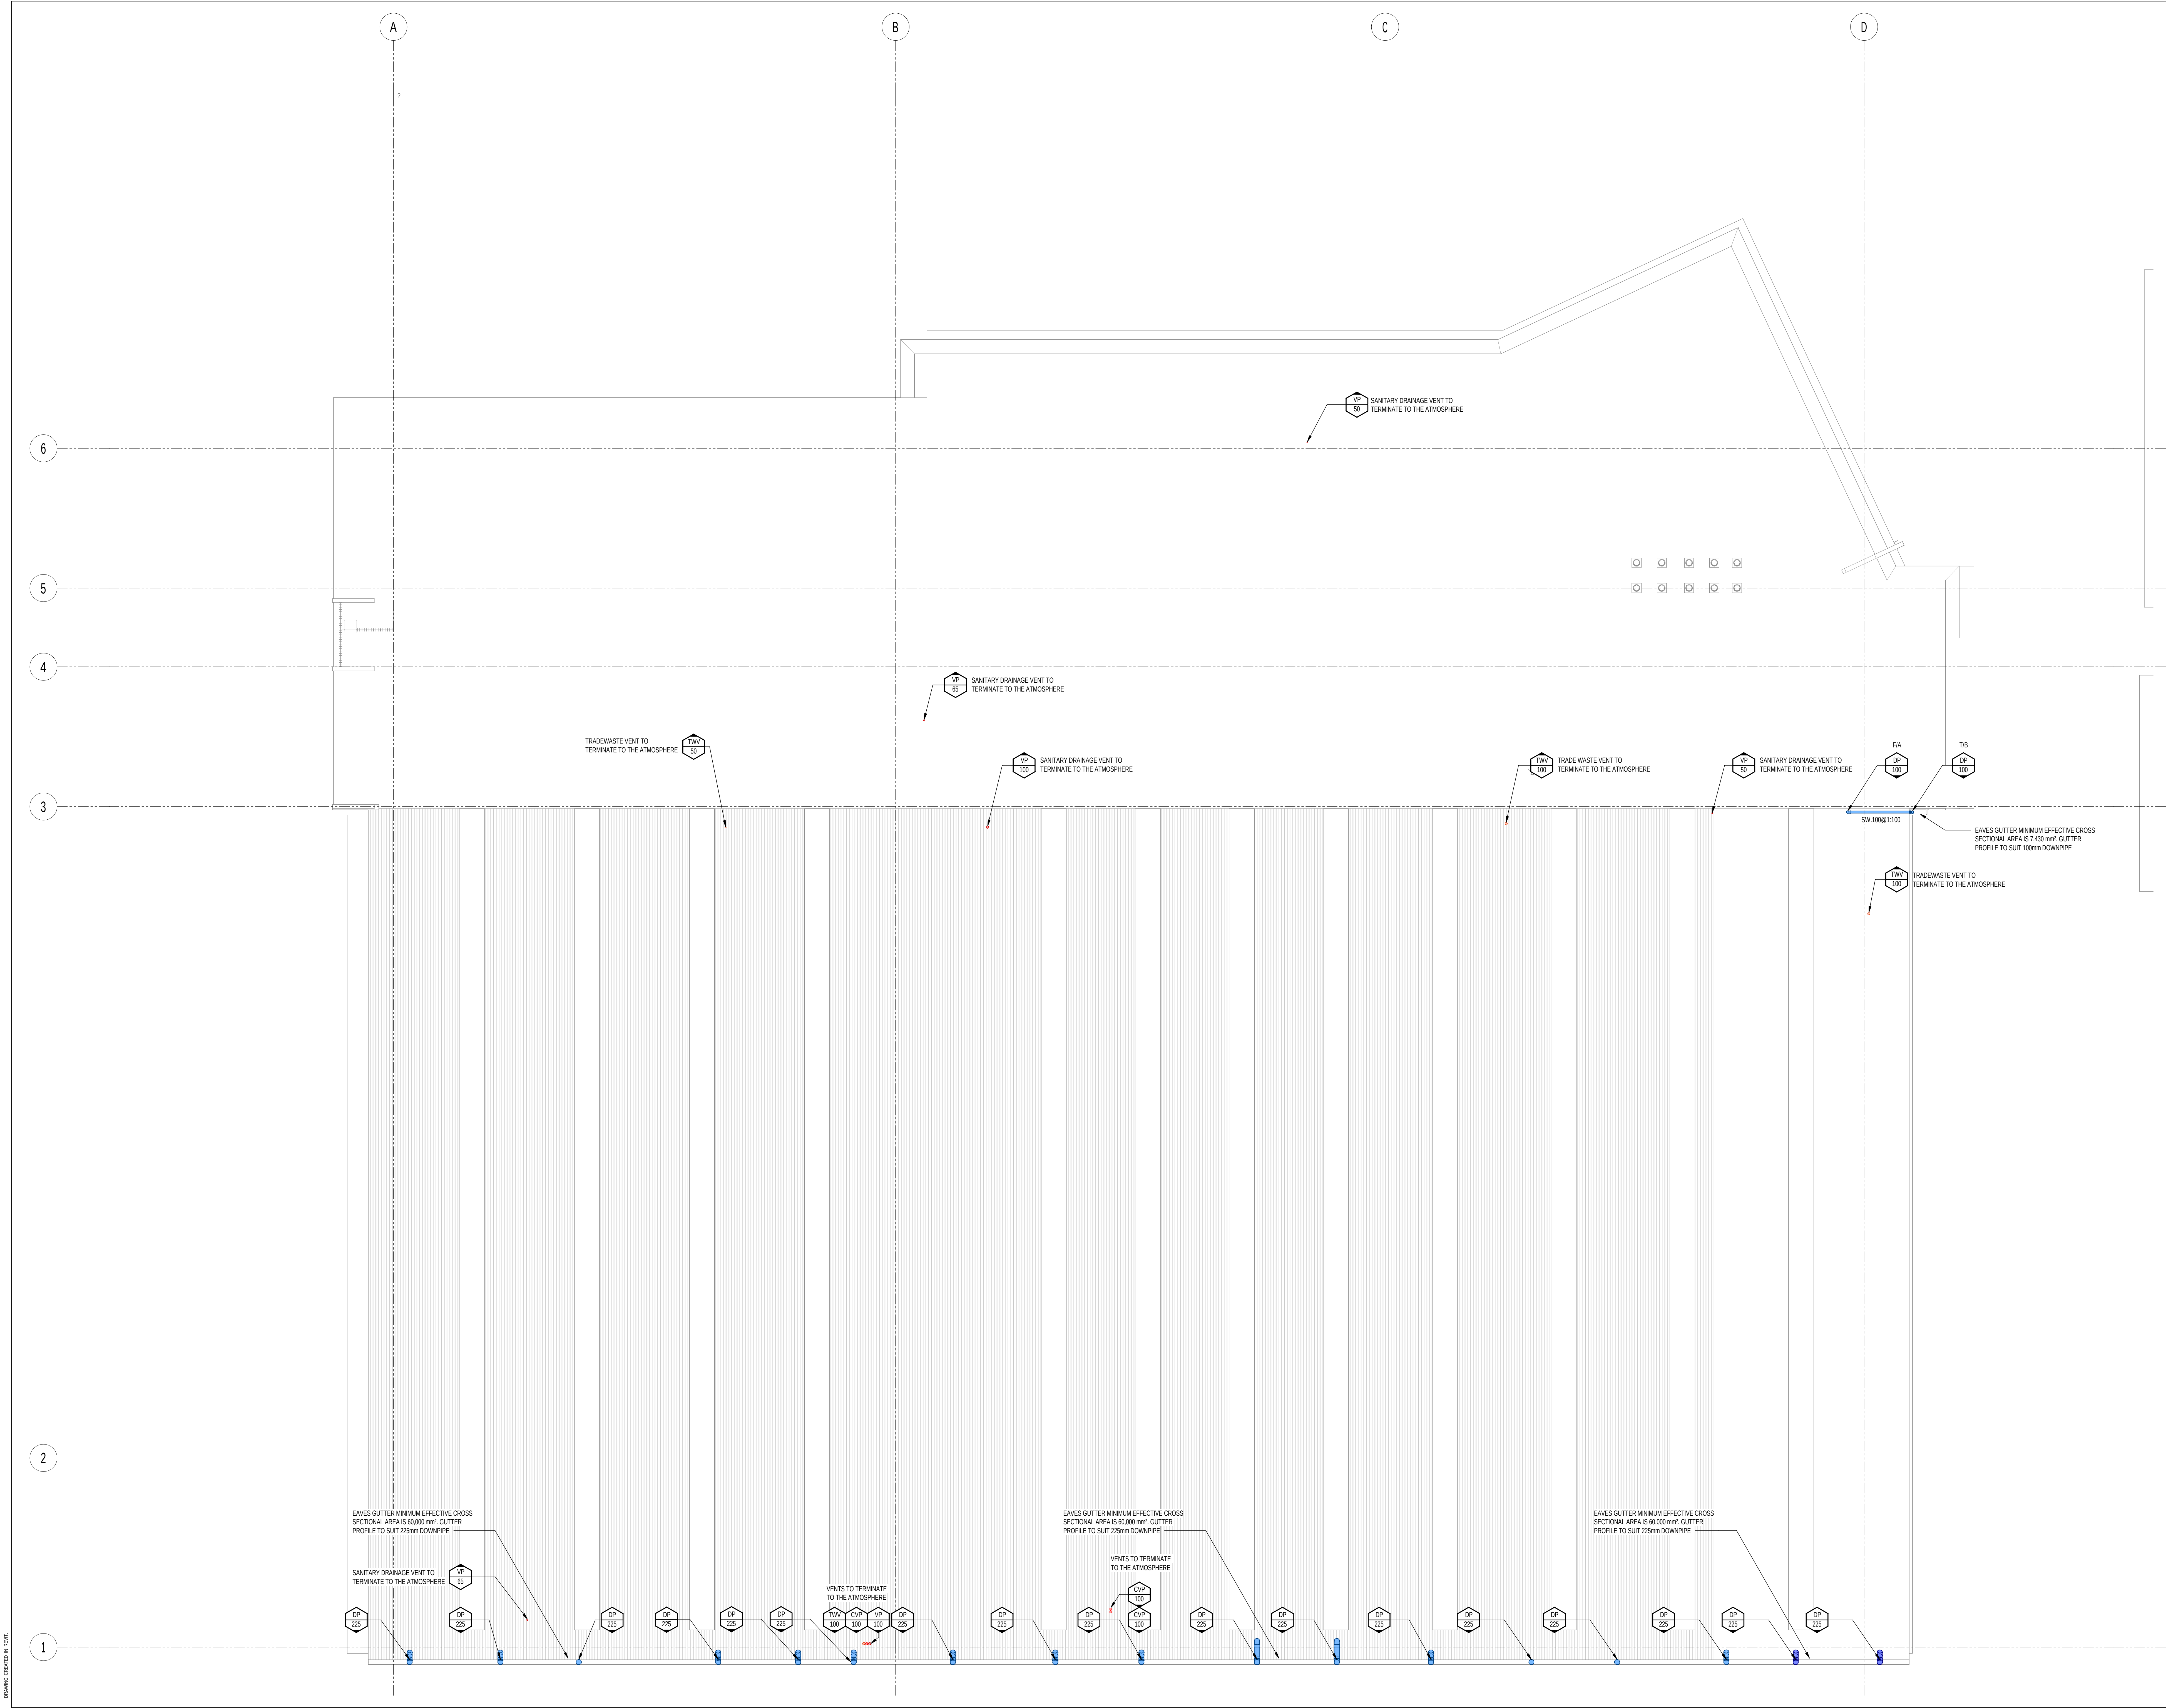

INFORMATION REFLECTED ON THIS DRAWING REPRESENTS HYDRAULIC SERVICES DESIGN DEVELOPED FOR D&C TENDER ADVISE ONLY, AND SHOULD NOT BE REGARDED AS COMPLETE. THE D&C CONTRACTOR SHOULD REFER TO ALL ASSOCIATED ARCHITECTURAL AND OTHER DISCIPLINE DRAWINGS, PROJECT BRIEFS AND CLIENT REQUIREMENTS AND MAKE ADEQUATE ALLOWANCES FOR ALL NECESSARY HYDRAULIC SERVICES WORKS TO MEET THESE REQUIREMENTS, EQUIPMENT SCHEDULES AND COMPLIANCE WITH THE NCC & APPROPRIATE AUSTRALIAN STANDARDS

DRAINAGE NOTES:

1. DOCUMENTATION MAY NOT INDICATE ALL VENTING REQUIREMENTS AND SHALL BE FINALISED DURING FURTHER DESIGN DEVELOPMENT. VENTING REQUIREMENTS TO BE IN ACCORDANCE WITH AS/NZS3500.2.
2. PROVIDE BACKFLOW PREVENTION DEVICES AS REQUIRED TO ENSURE THAT ZONE PROTECTION IS RETAINED IN ACCORDANCE WITH AS/NZS3550.1 AND LOCAL AUTHORITY REQUIREMENTS.
3. ALL WORKS TO BE CO-ORDINATED ON SITE WITH MECHANICAL CONTRACTOR PRIOR TO INSTALLING.
4. FINAL LOCATION OF ALL FITTINGS AND FIXTURES TO BE CO-ORDINATED ON SITE WITH ALL SERVICES.

B	12.02.2026	SH	ISSUED FOR D&C TENDER	AA	SM
A	18.03.2026	SH	ISSUED FOR D&C TENDER	AA	SM
REV	DATE	BY	DESCRIPTION	CHK	APP

DESIGN DEVELOPMENT



900 Ann Street, Level 12, Fortitude Valley 4006
Tel: +61-7-3854-6200 Fax: +61-7-3854-6500
<http://www.wsp.com>

CLIENT:

CQU

ARCHITECT:

THOMSON ADSETT / PEDDLE THORP

PROJECT:

CQU ROCKHAMPTON TAFE CONSOLIDATION

TITLE:

HYDRAULIC SERVICES
NEW TRADES BUILDING - ROOF LEVEL - DRAINAGE
LAYOUT

SCALE @ A1:

1:100

CHECKED:

AA

APPROVED:

SM

PROJECT NUMBER:

PS229518

DRAWN:

SH

DATE:

JAN 2026

DRAWING NO:

NTB-HY-DR-510-LRF-00-00

REV:

B

© WSP Australia Pty Ltd



WATER NOTES:

- ## EXISTING SERVICES

SERVICES SHOWN AS EXISTING HAVE BEEN
INTERPOLATED FROM RECORD DRAWINGS.
CONTRACTOR TO VERIFY LOCATIONS AND LEVELS
PRIOR TO COMMENCEMENT OF WORK.

B	12.02.2026	SH	ISSUED FOR DAC TENDER	AA	S
A	30.01.2026	SH	DRAFT 60% DD ISSUE FOR REVIEW	AA	S
REV	DATE	BY	DESCRIPTION	CHK	APPROVED

DESIGN DEVELOPMENT

WSN

900 Ann Street, Level 12, Fortitude Valley 4006
Tel: +61-7-3854-6200 Fax: +61-7-3854-6500
<http://www.wsp.com>

COLL

THOMSON ADSETT / REDDIE THORP

CQU ROCKHAMPTON TAFE CONSOLIDATION

HYDRAULIC SERVICES
NEW TRADES BUILDING - GROUND LEVEL - WATER
SERVICES LAYOUT

SCALE @ A0: 1:100	CHECKED: AA	APPROVED: SM
PROJECT NUMBER: PS229518	DRAWN: SH	DATE: JAN 2026

NTB-HY-DR-520-L00-00-00

© WSP Australia Pty Ltd

DRAWING CREATED IN REVIT.