

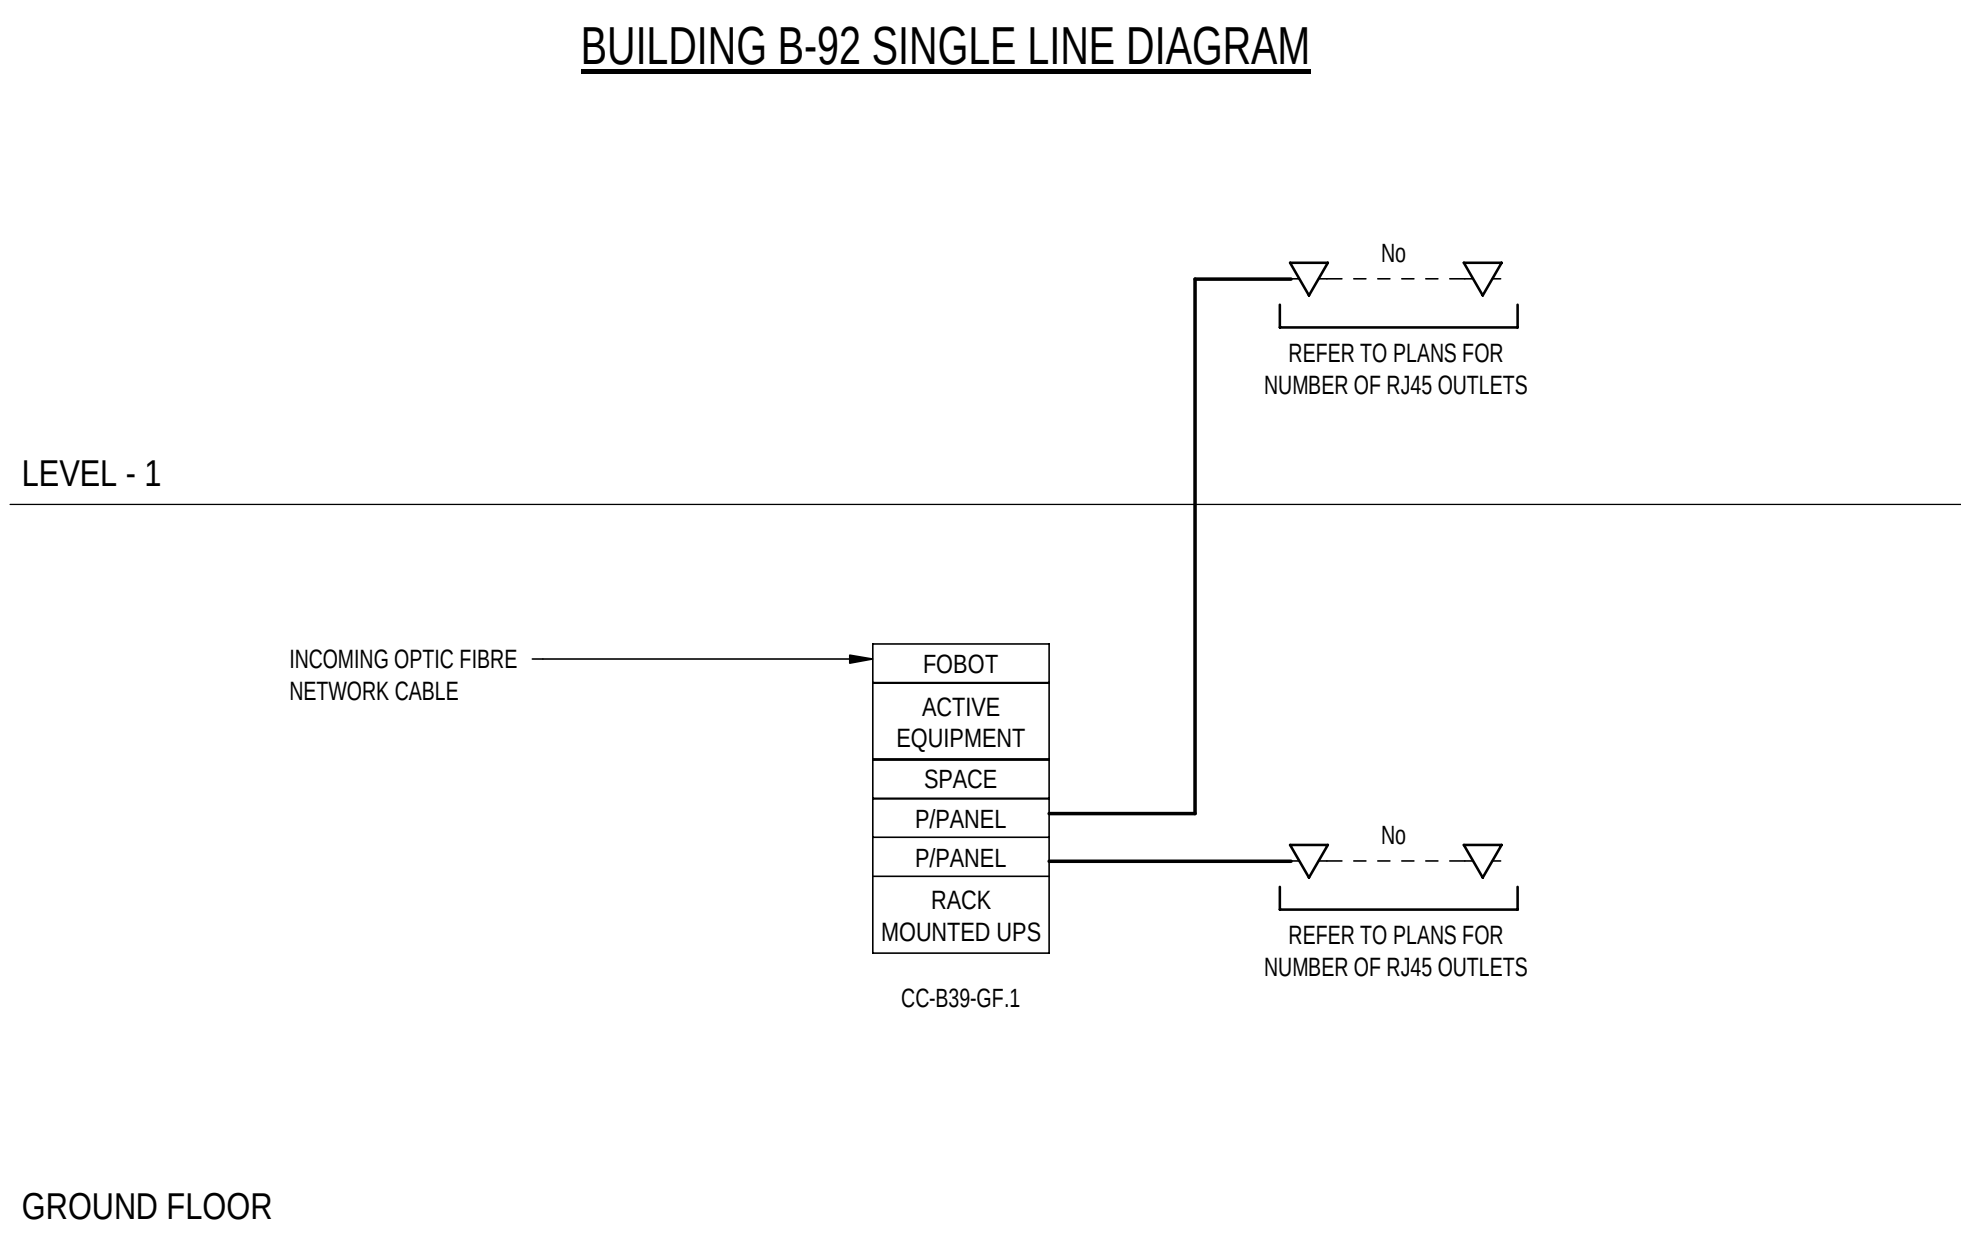
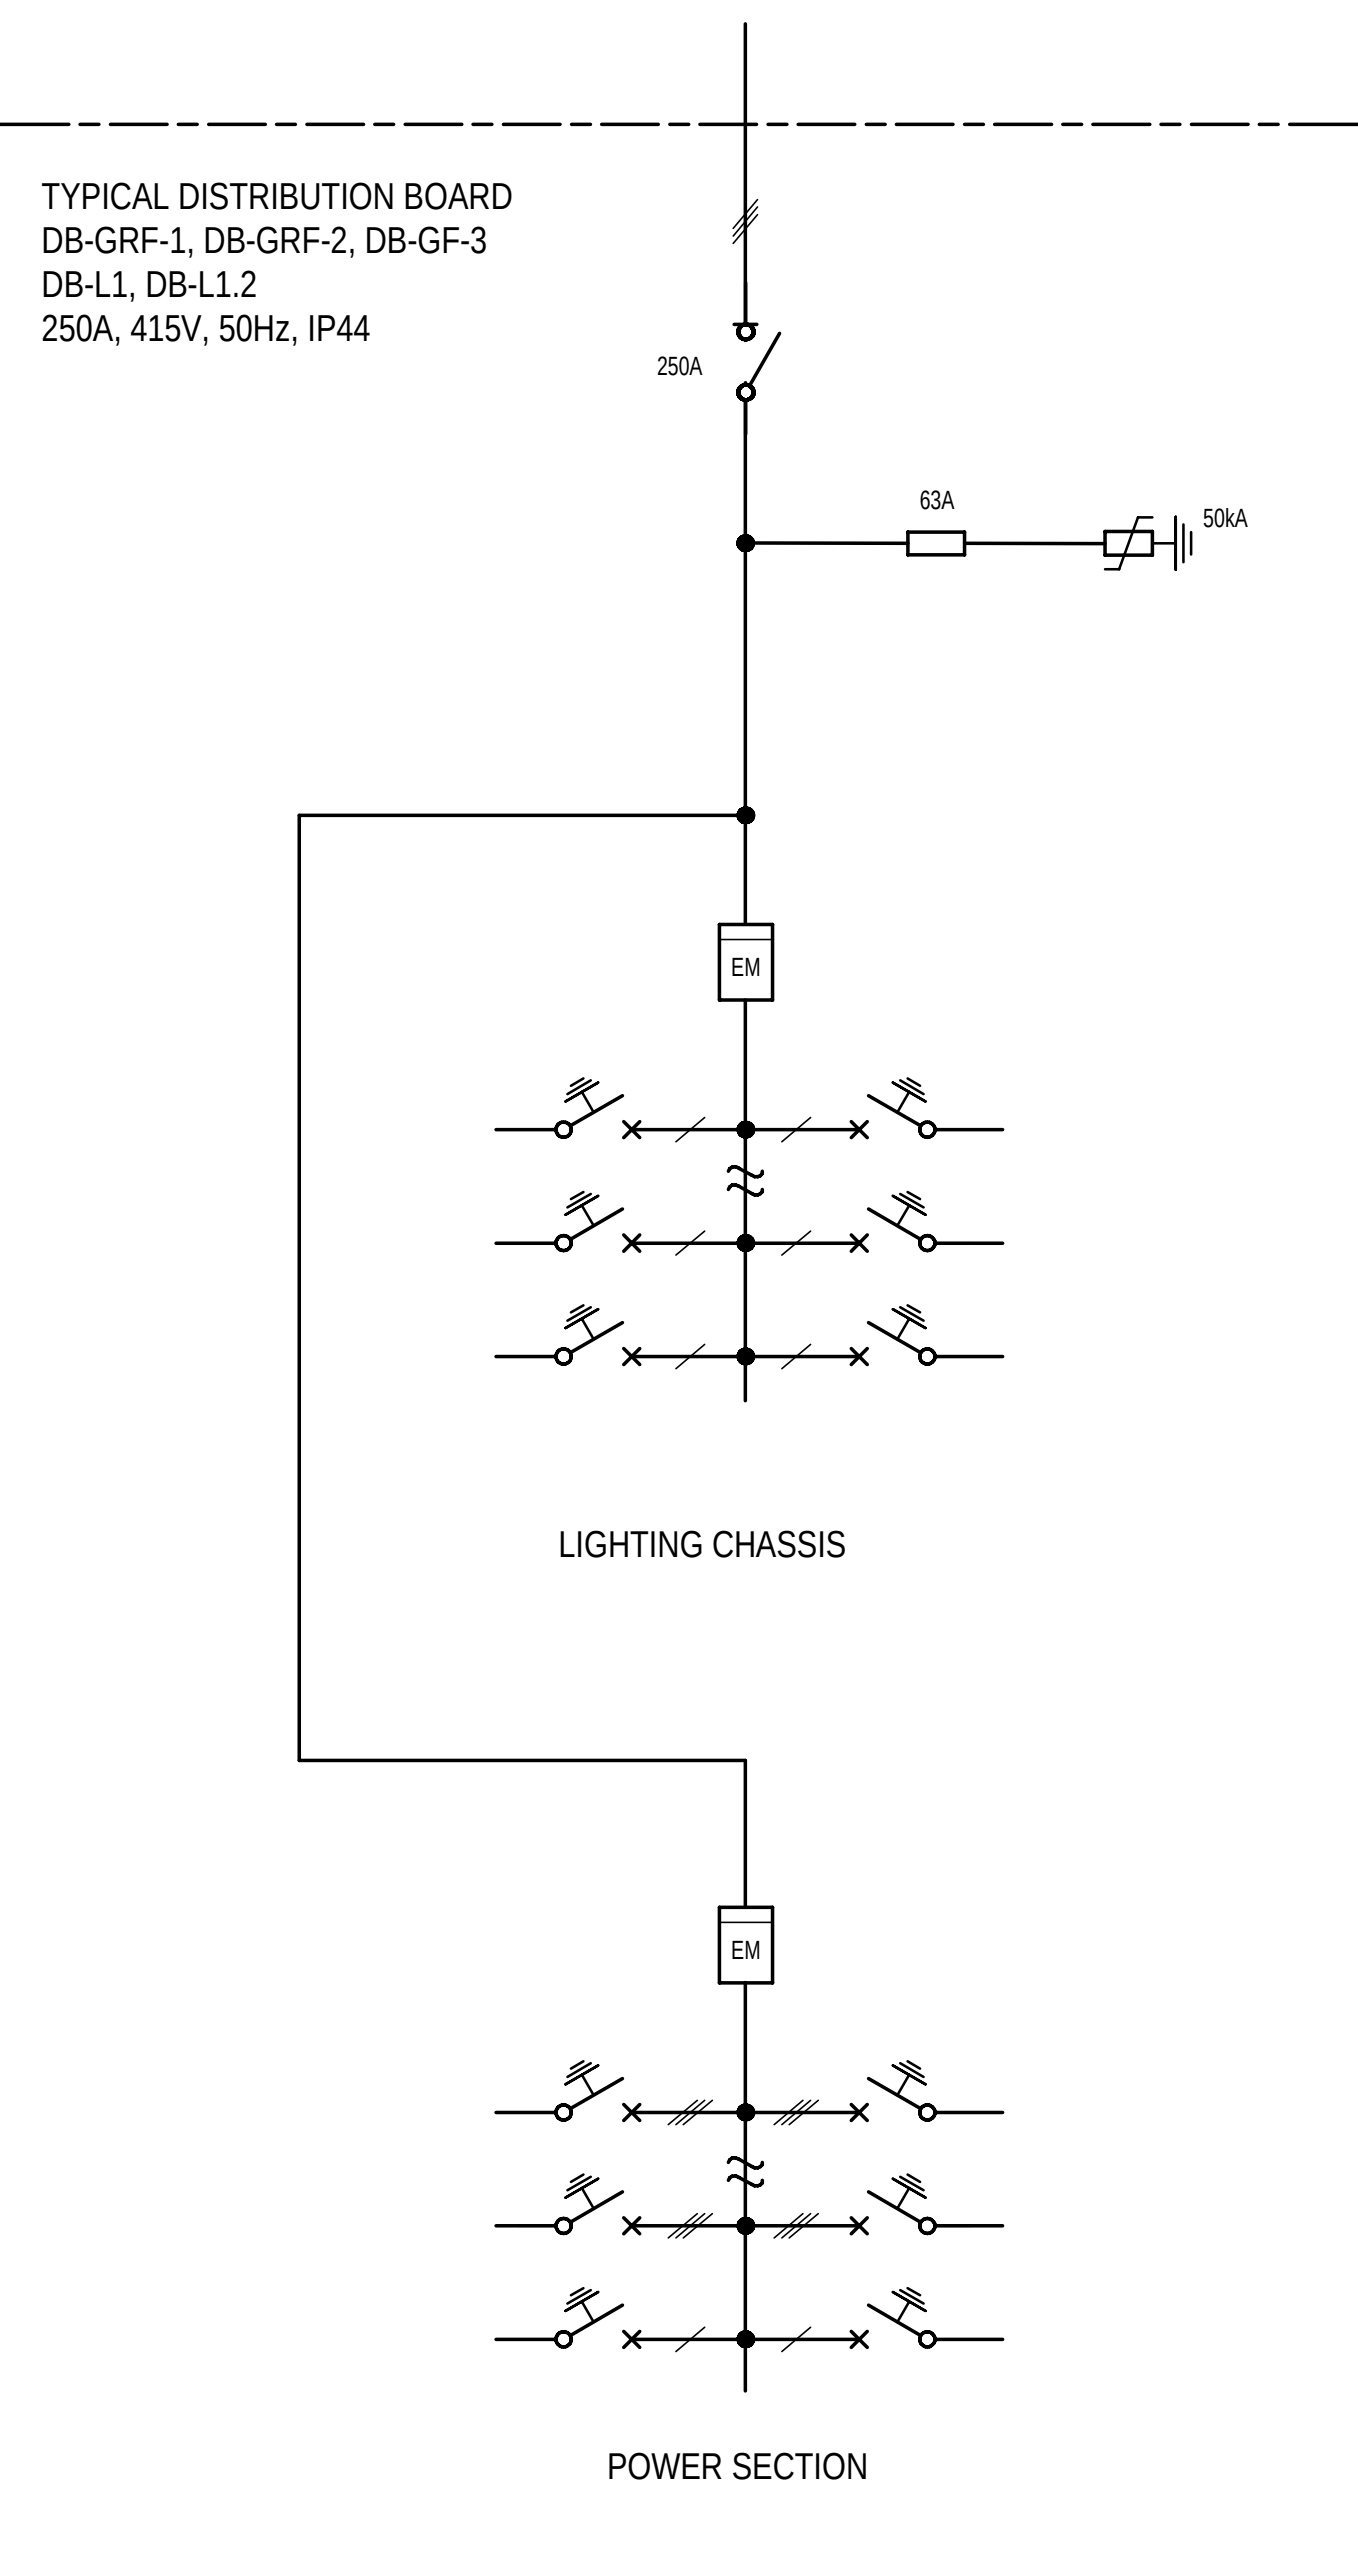
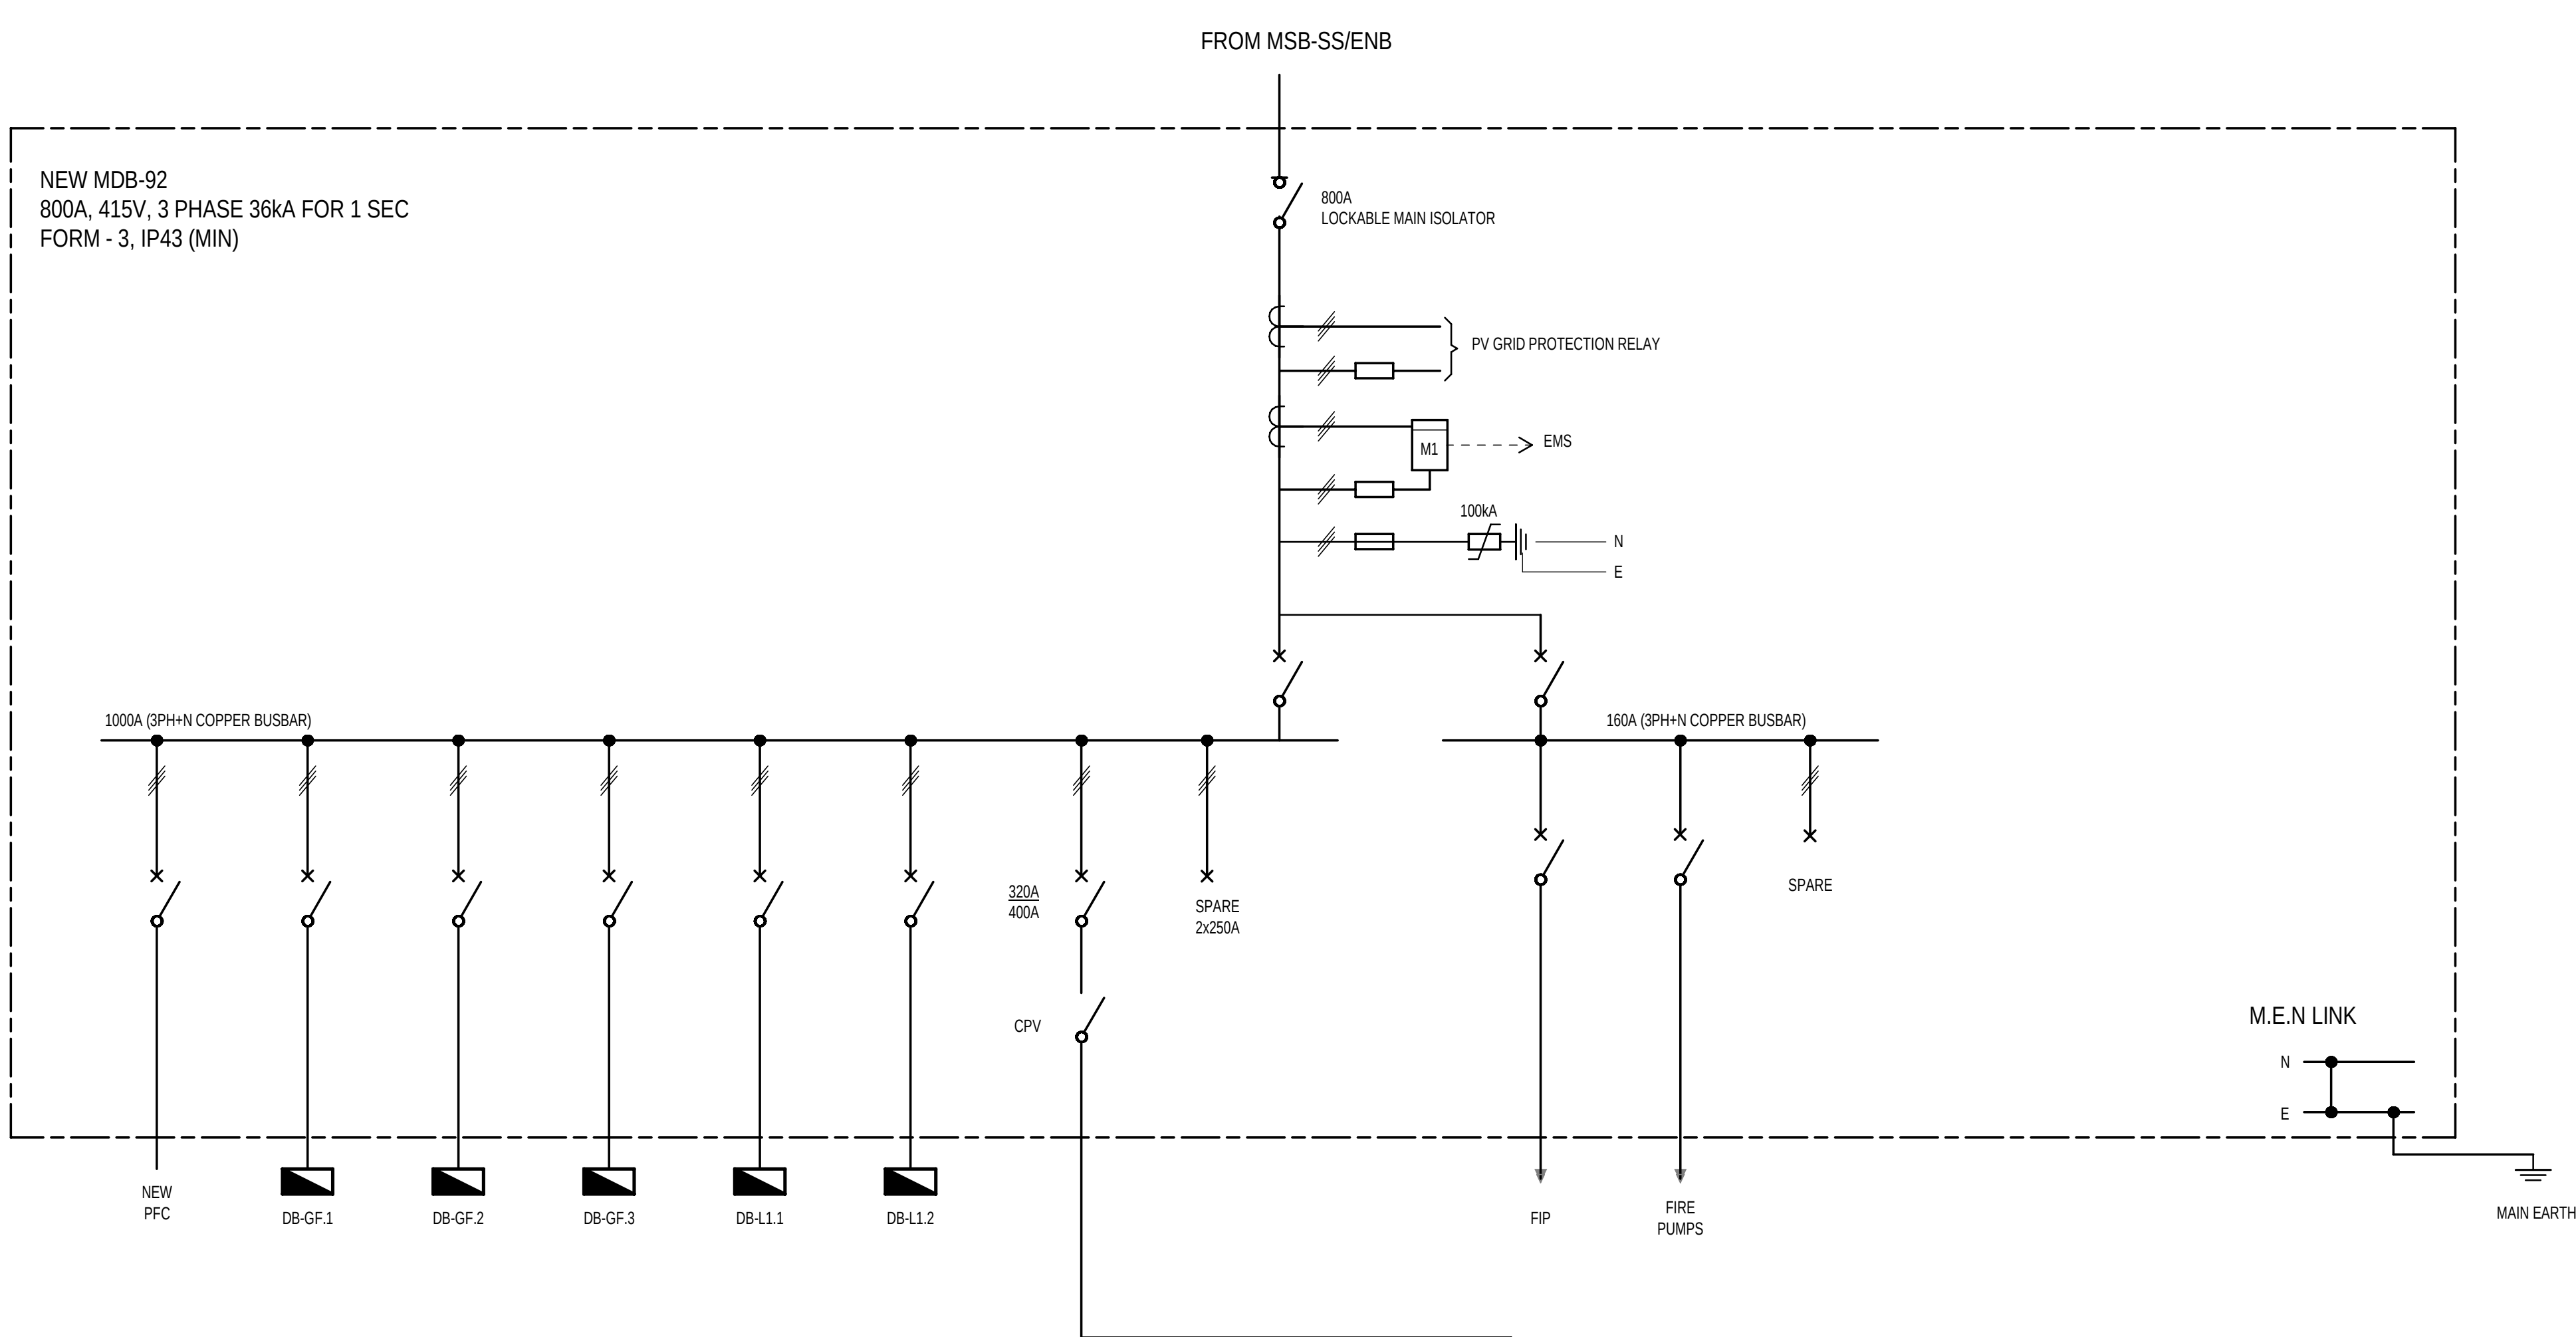


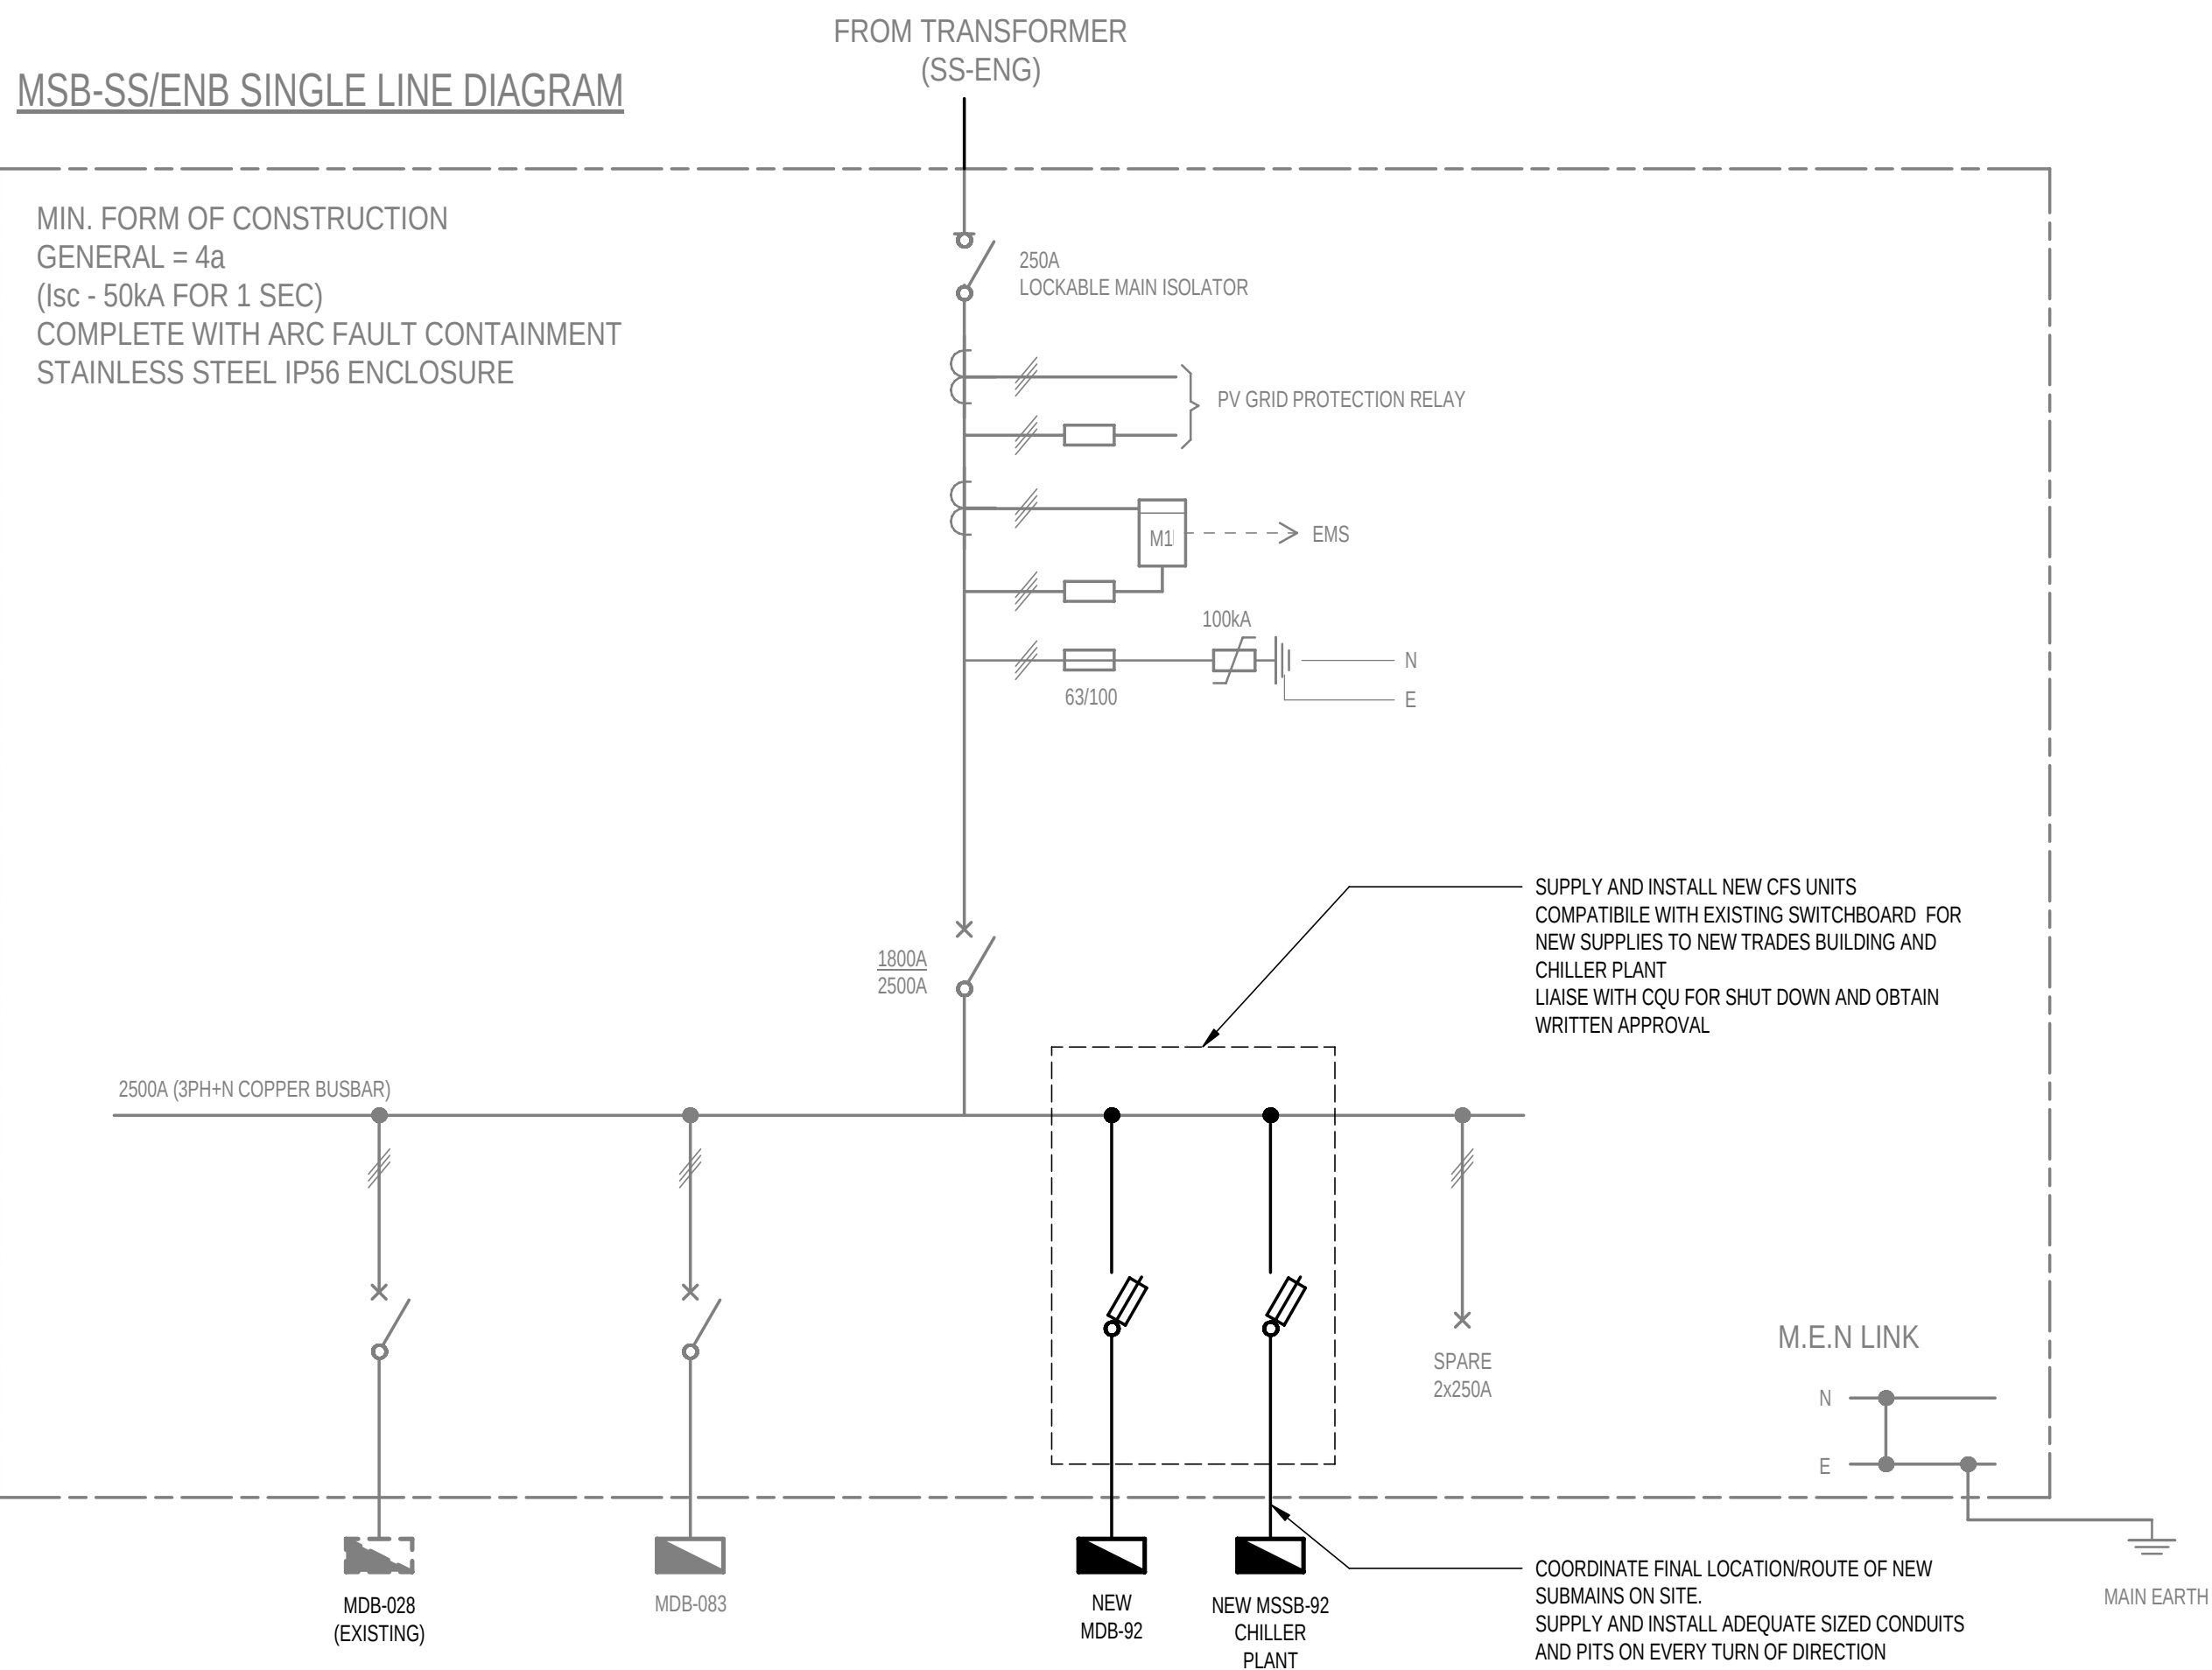

BUILDING B-92 COMMUNICATIONS DIAGRAM

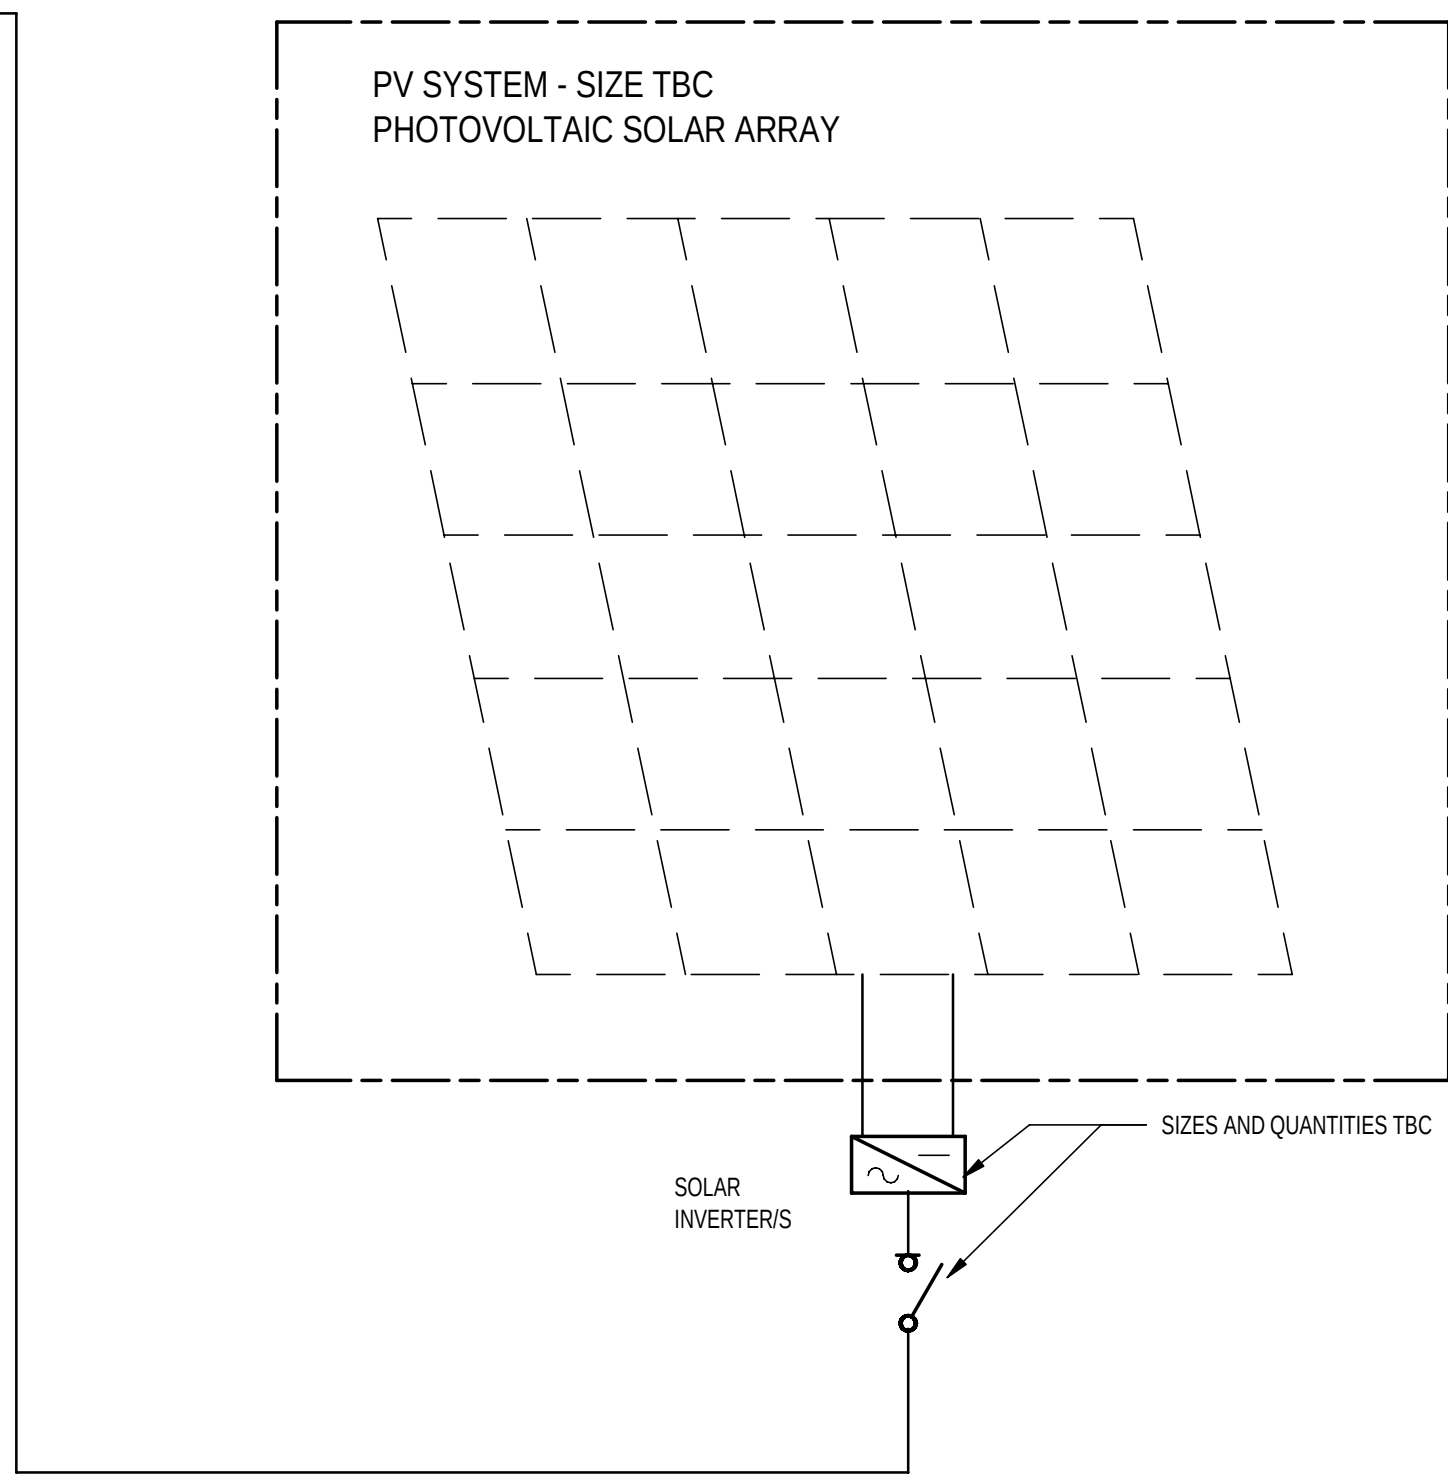

BUILDING B92 SCHEMATICS

INFORMATION REFLECTED ON THIS DRAWING REPRESENTS ELECTRICAL SERVICES DESIGN DEVELOPED FOR D&C TENDER ADVISE ONLY, AND SHOULD NOT BE REGARDED AS COMPLETE. THE D&C CONTRACTOR SHOULD REFER TO ALL ASSOCIATED ARCHITECTURAL AND OTHER DISCIPLINE DRAWINGS, PROJECT BRIEFS AND CLIENT REQUIREMENTS AND MAKE ADEQUATE ALLOWANCES FOR ALL NECESSARY ELECTRICAL SERVICES WORKS TO MEET THESE REQUIREMENTS, EQUIPMENT SCHEDULES AND COMPLIANCE WITH THE NCC & APPROPRIATE AUSTRALIAN STANDARDS

|     |            |    |                       |     |     |
|-----|------------|----|-----------------------|-----|-----|
| B   | 12.02.2026 | MM | ISSUED FOR D&C TENDER | TP  | SM  |
| A   | 18.02.2026 | MM | ISSUED FOR D&C TENDER | TP  | SM  |
| REV | DATE       | BY | DESCRIPTION           | CHK | APP |

DESIGN DEVELOPMENT



900 Ann Street, Level 12, Fortitude Valley 4006  
Tel: +61-7-3854-6200 Fax: +61-7-3854-6500  
http://www.wsp.com

CLIENT: CQU

ARCHITECT: THOMSON ADSETT / PEDDLE THORP

PROJECT: CQU ROCKHAMPTON TAFE CONSOLIDATION

TITLE: ELECTRICAL SERVICES  
NEW TRADES BUILDING - SCHEMATICS

|                |          |         |    |          |          |
|----------------|----------|---------|----|----------|----------|
| SCALE @ A1     | N.T.S    | CHECKED | TP | APPROVED | SM       |
| PROJECT NUMBER | PS229518 | DRAWN   | MM | DATE     | JAN 2026 |

|             |                         |      |   |
|-------------|-------------------------|------|---|
| DRAWING NO. | B92-EL-DR-200-A00-00-00 | REV. | B |
|-------------|-------------------------|------|---|

© WSP Australia Pty Ltd