


DESIGN CRITERIA & GENERAL NOTES:

1. DRAWINGS TO BE READ IN CONJUNCTION WITH THE FIRE ENGINEERING BRIEF (FEB) AND CERTIFIER'S ICA ASSESSMENT REPORT.
2. DRAWINGS TO BE READ IN CONJUNCTION WITH THE FIRE PROTECTION SERVICES REPORT, ARCHITECTURAL, STRUCTURAL, CIVIL AND ALL OTHER BUILDING SERVICES DOCUMENTATION.
3. FIRE SERVICES TO BE PROVIDED IN ACCORDANCE WITH NCC 2022 AND FIRE SAFETY ENGINEERING BRIEF.
4. FIRE HYDRANT SYSTEM TO BE PROVIDED IN ACCORDANCE WITH AS 2419.1:2021.
5. FIRE HOSE REELS TO BE PROVIDED IN ACCORDANCE WITH AS 2442:2005.

INFORMATION REFLECTED ON THIS DRAWING REPRESENTS FIRE SERVICES DESIGN DEVELOPED FOR D&C TENDER ADVICE ONLY, AND SHOULD NOT BE REGARDED AS COMPLETE. THE D&C CONTRACTOR SHOULD REFER TO ALL ASSOCIATED ARCHITECTURAL AND OTHER DISCIPLINE DRAWINGS, PROJECT BRIEFS AND CLIENT REQUIREMENTS AND MAKE ADEQUATE ALLOWANCES FOR ALL NECESSARY FIRE SERVICES WORKS TO MEET THESE REQUIREMENTS, EQUIPMENT SCHEDULES AND COMPLIANCE WITH THE NCC & APPROPRIATE AUSTRALIAN STANDARDS

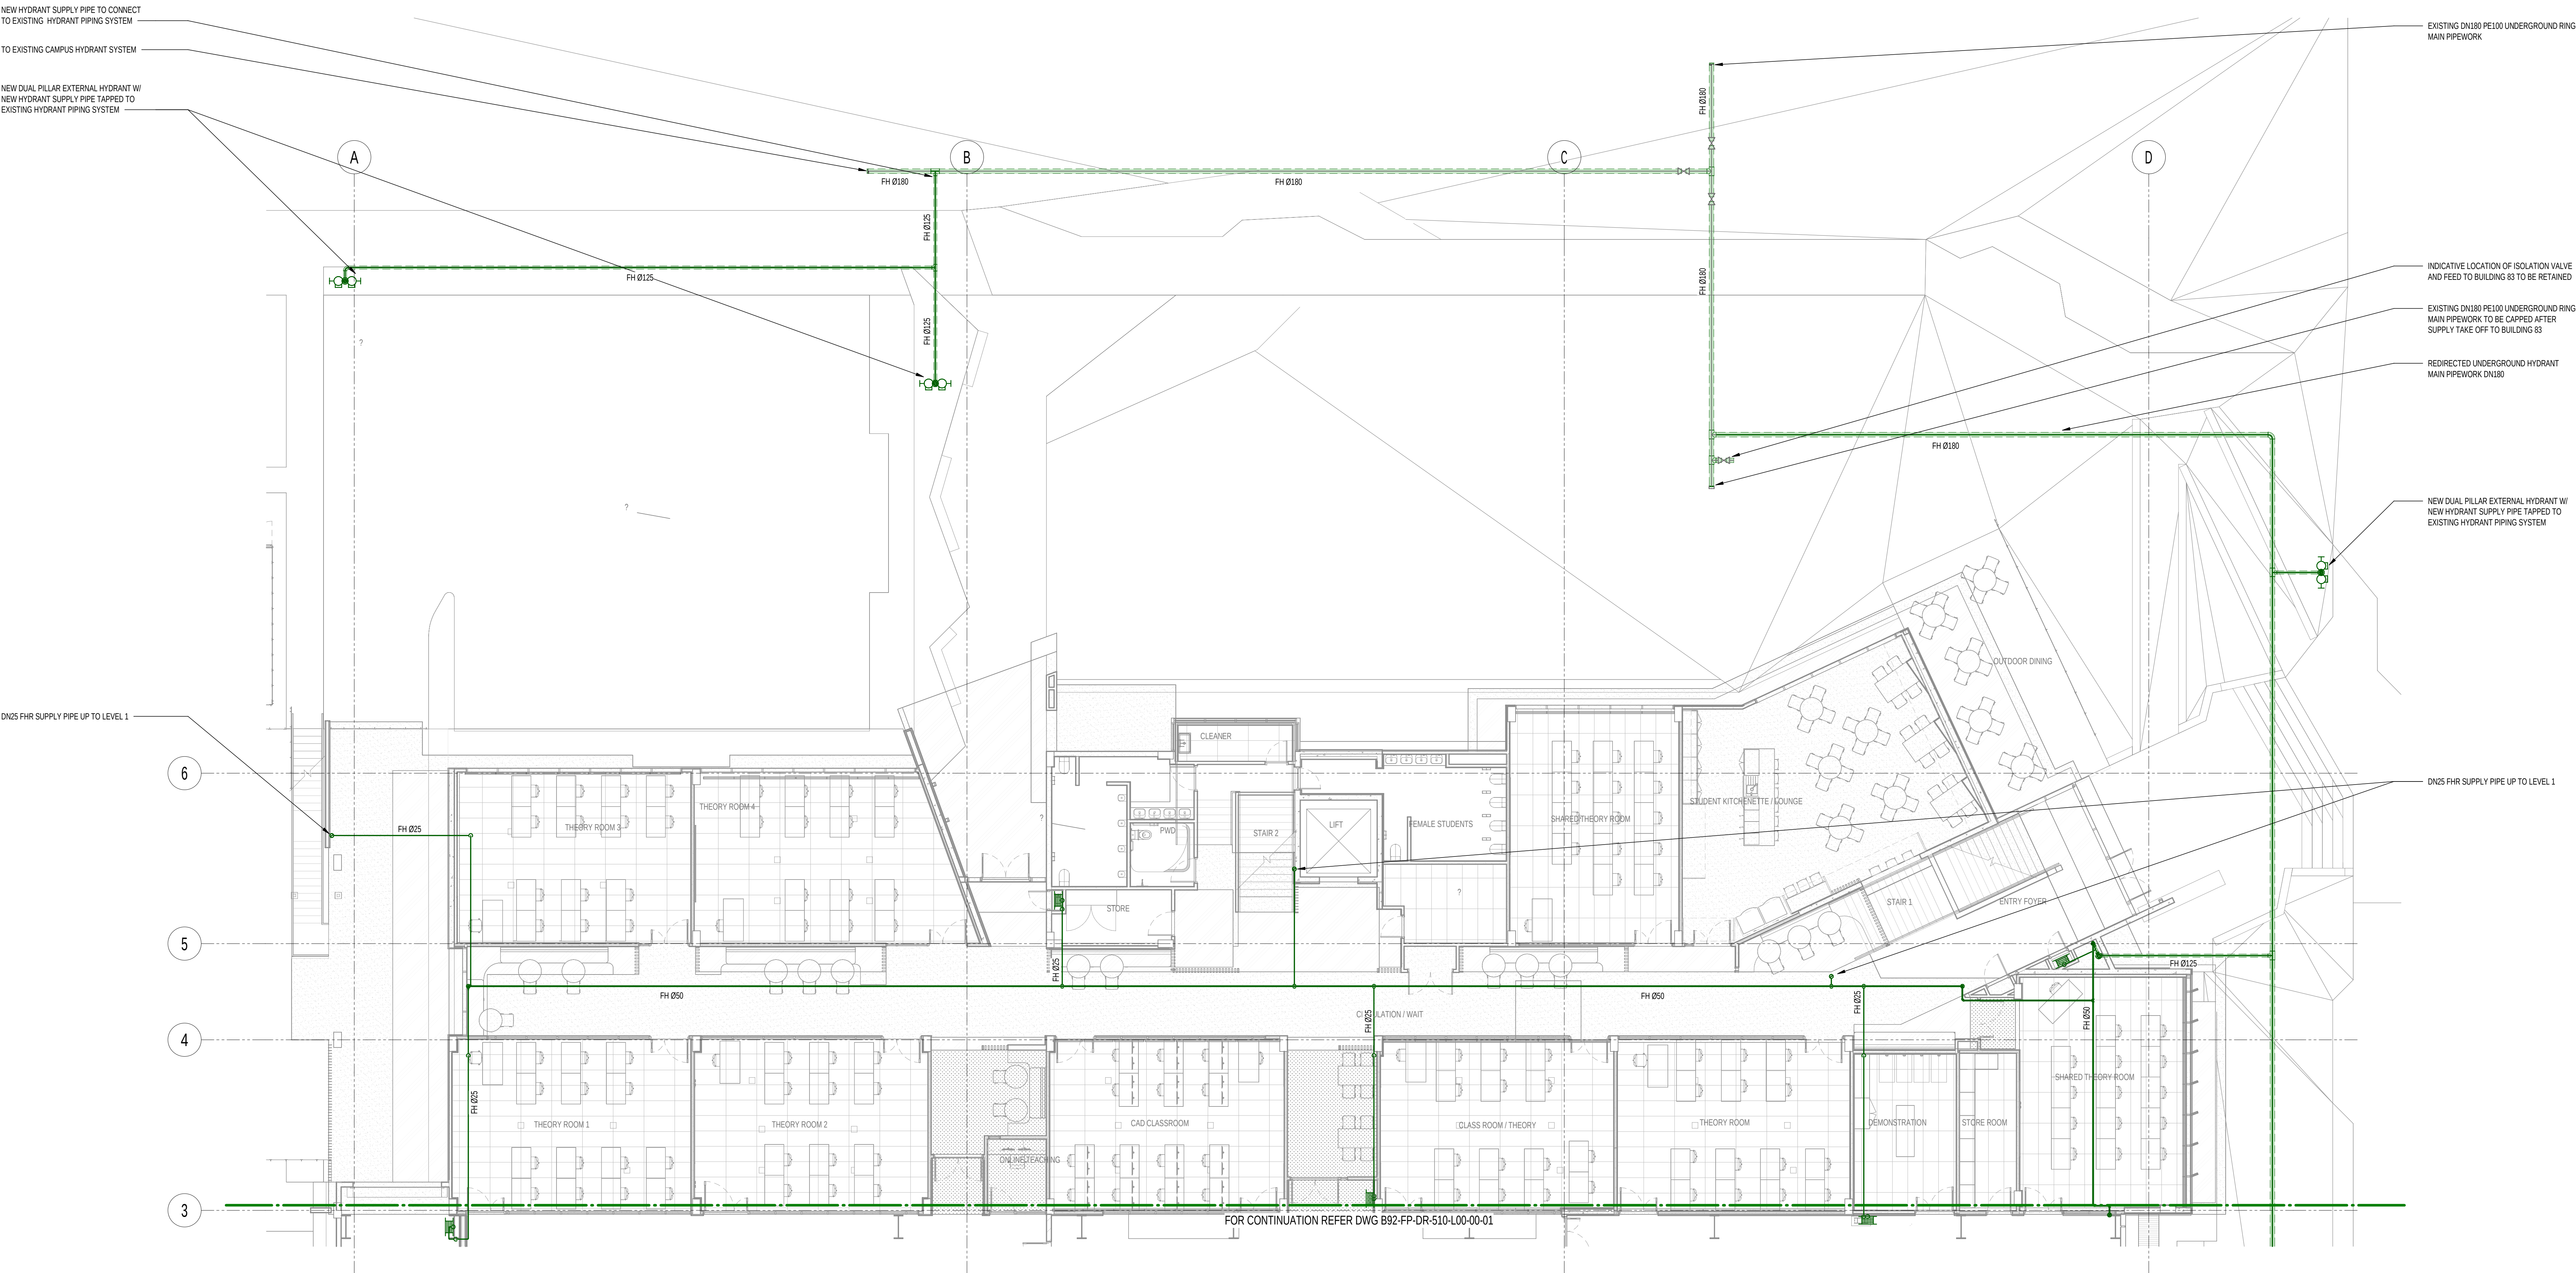

B	12.02.2026	RG	ISSUED FOR D&C TENDER	JS	SM
A	19.02.2026	RG	DRAWING FOR REVIEW	JS	SM
REV	DATE	BY	DESCRIPTION	CHK	APP

DESIGN DEVELOPMENT



900 Ann Street, Level 12, Fortitude Valley 4006
Tel: +61-7-3854-6200 Fax: +61-7-3854-6500
<http://www.wsp.com>

CLIENT: CQU

ARCHITECT: THOMSON ADSETT / PEDDLE THORP

PROJECT: CQU ROCKHAMPTON TAFE CONSOLIDATION

TITLE: FIRE PROTECTION SERVICES
NEW TRADES BUILDING - GROUND LEVEL - WET
FIRE LAYOUT - SHEET 1

SCALE @ A1	CHECKED:	APPROVED:
1:100	JS	SM
PROJECT NUMBER:	DRAWN:	DATE:
PS229518	RG	JAN 2026

DRAWING NO:	REV:
B92-FP-DR-510-L00-00-00	B

© WSP Australia Pty Ltd