


NOTE:

1. ARCHITECTURE AND STRUCTURAL SERVICES TO PROVIDE ROOF MAINTENANCE ACCESS FOR EQUIPMENT AT THE ROOF.
2. ALL EXTERNAL DUCTWORK TO BE CROSS BROKEN AND MASTIC SEALED TO PREVENT WATER INGRESS.

INFORMATION REFLECTED ON THIS DRAWING REPRESENTS MECHANICAL SERVICES DESIGN DEVELOPED FOR D&C TENDER ADVISE ONLY, AND SHOULD NOT BE REGARDED AS COMPLETE. THE D&C CONTRACTOR SHOULD REFER TO ALL ASSOCIATED ARCHITECTURAL AND OTHER DISCIPLINE DRAWINGS, PROJECT BRIEFS AND CLIENT REQUIREMENTS AND MAKE ADEQUATE ALLOWANCES FOR ALL NECESSARY MECHANICAL SERVICES WORKS TO MEET THESE REQUIREMENTS, EQUIPMENT SCHEDULES AND COMPLIANCE WITH THE NCC & APPROPRIATE AUSTRALIAN STANDARDS

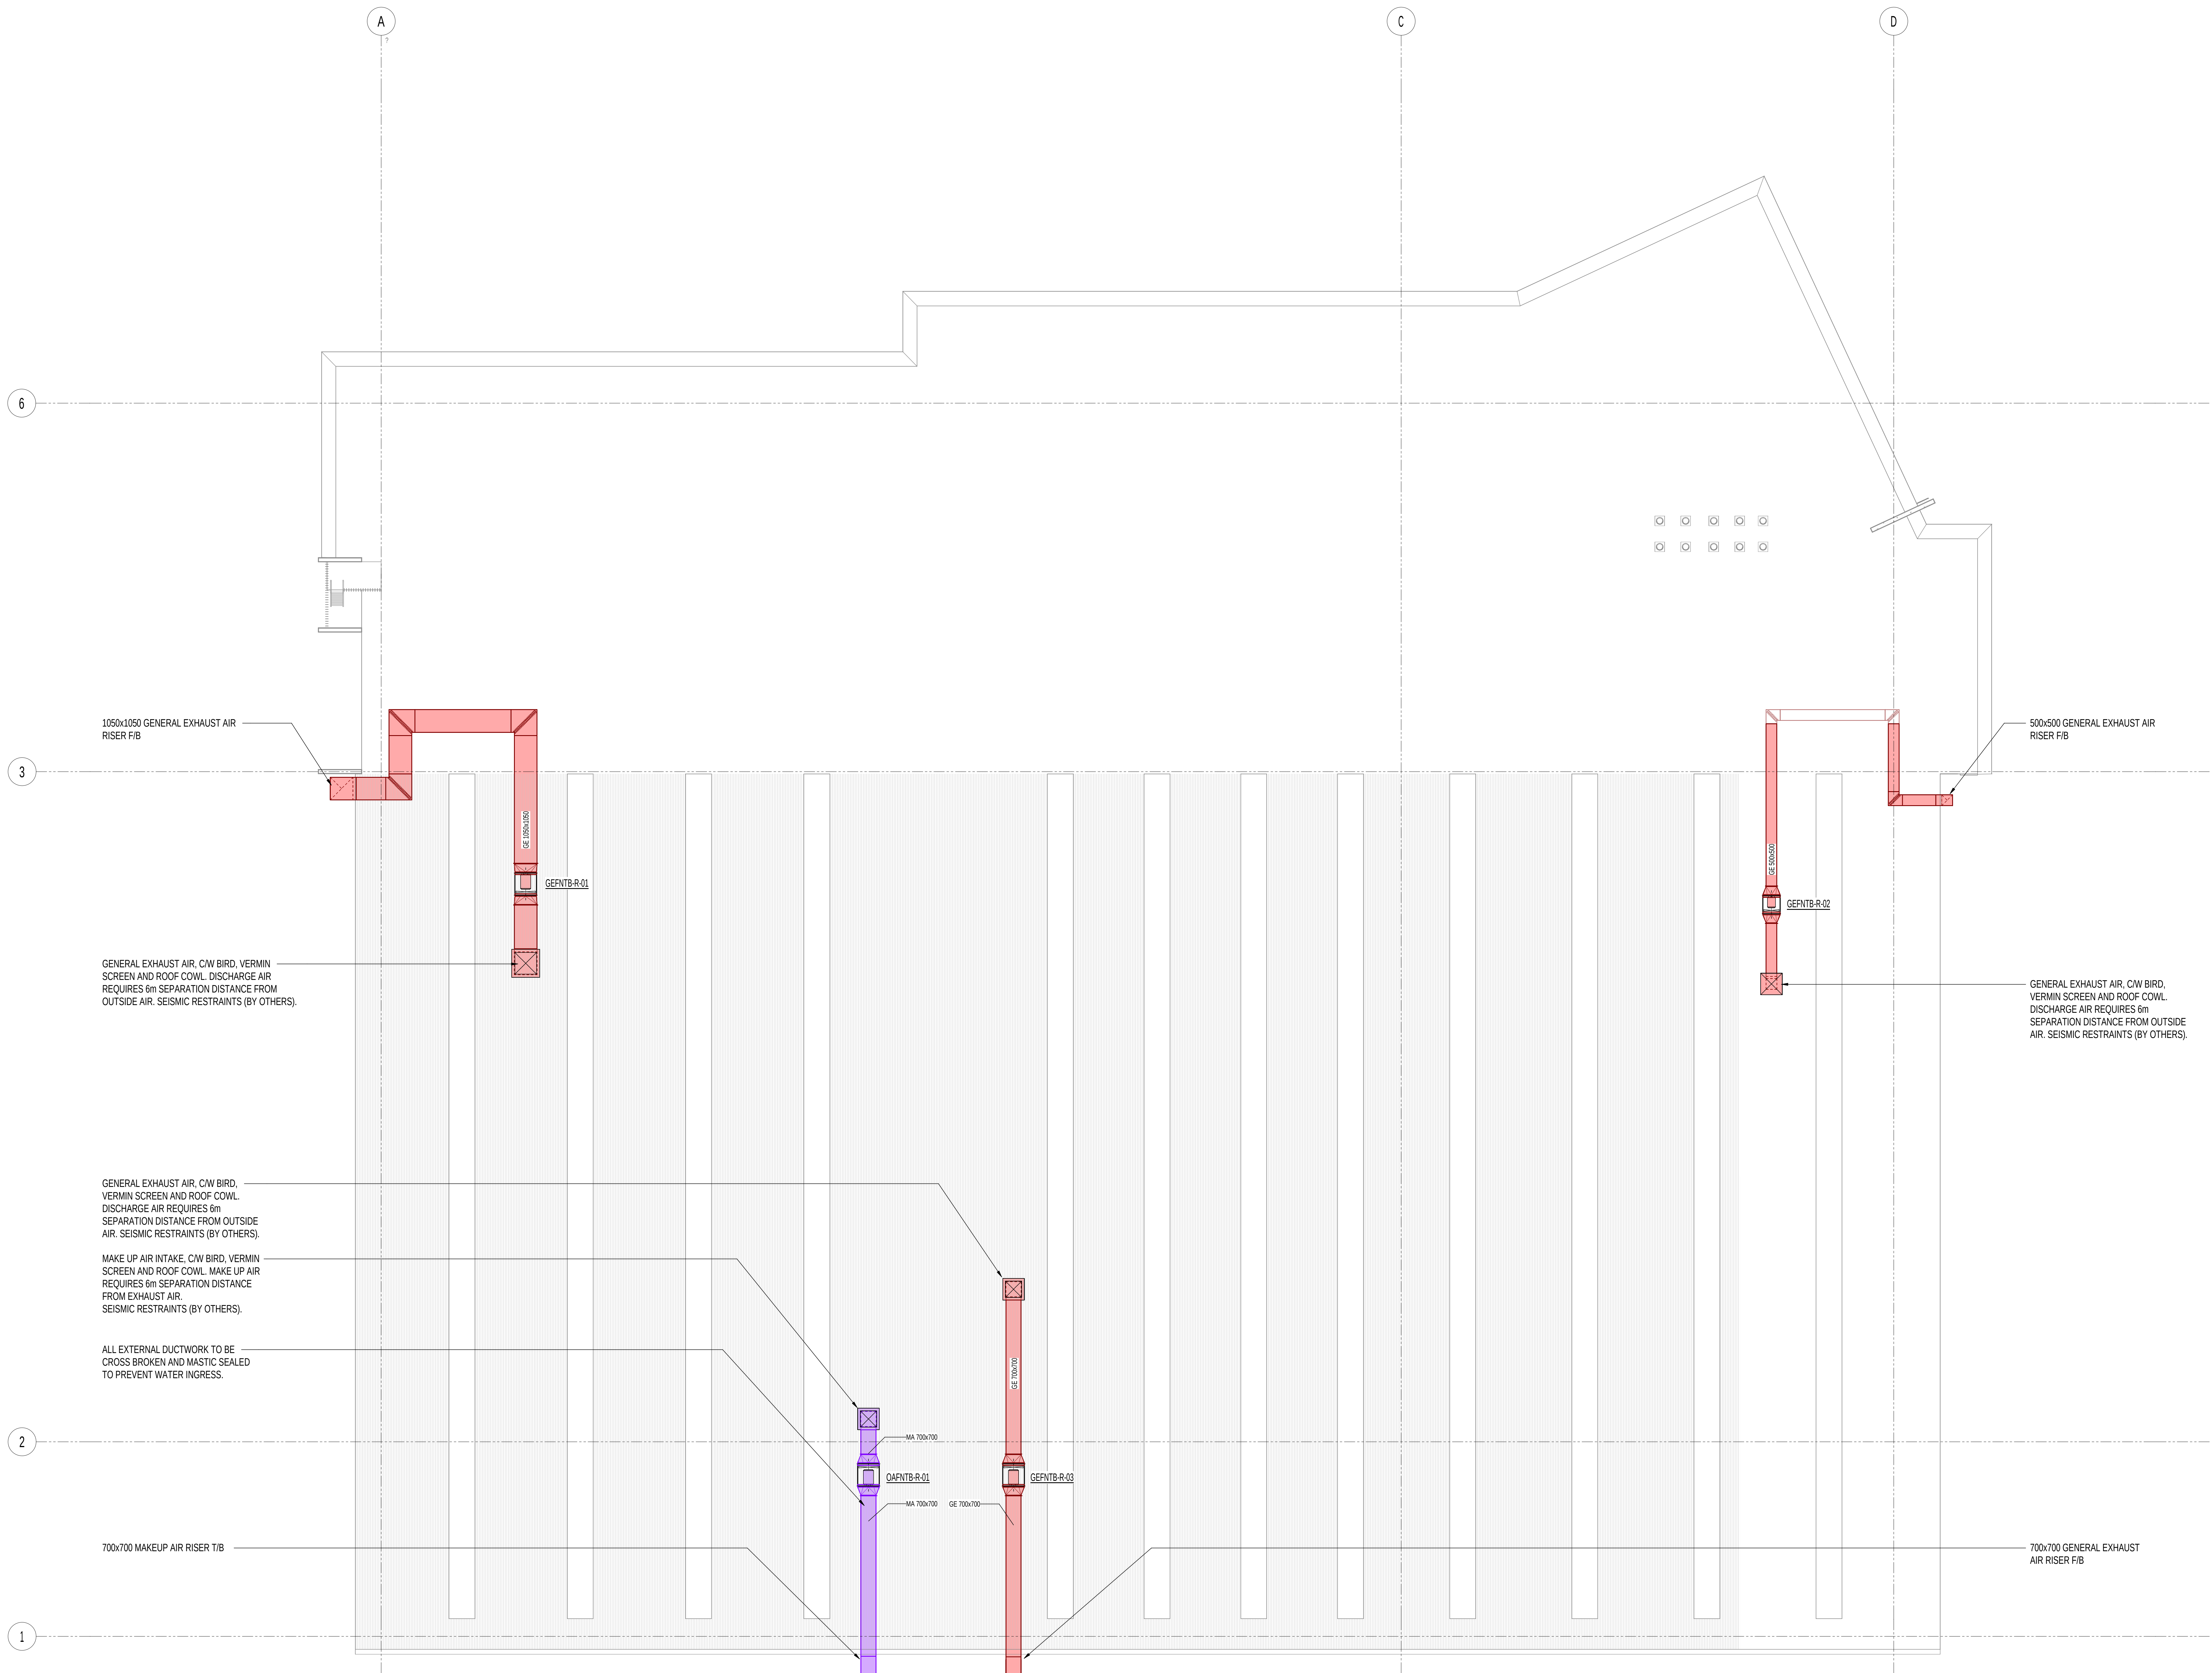

B	12/02/2020	RD	ISSUED FOR OAC TENDER	MS	SA
A	03/01/2020	RD	DRAFT 02% DO ISSUE FOR REVIEW	MS	DA
REV	DRAFT	RT	DISPOSITION	OK	APP

DESIGN DEVELOPMENT



900 Ann Street, Level 12, Fortitude Valley 4006
Tel: +61-7-3854-6200 Fax: +61-7-3854-6500
<http://www.wsp.com>

CLIENT:

QU

ARCHITECT

THOMSON ADSETT / PEDDLE THORP

PROJECT

CQU ROCKHAMPTON TAFE CONSOLIDATION

TITLE:

MECHANICAL SERVICES
NEW TRADES BUILDING - ROOF LEVEL - HVAC
LAYOUT

SCALE @ A0: 1:100	CHECKED: MB	APPROVED: SM
PROJECT NUMBER: PS229518	DRAWN: RD	DATE: FEB 2026

NTB-ME-DR-510-LRF-00-00

© WSP Australia Pty Ltd