



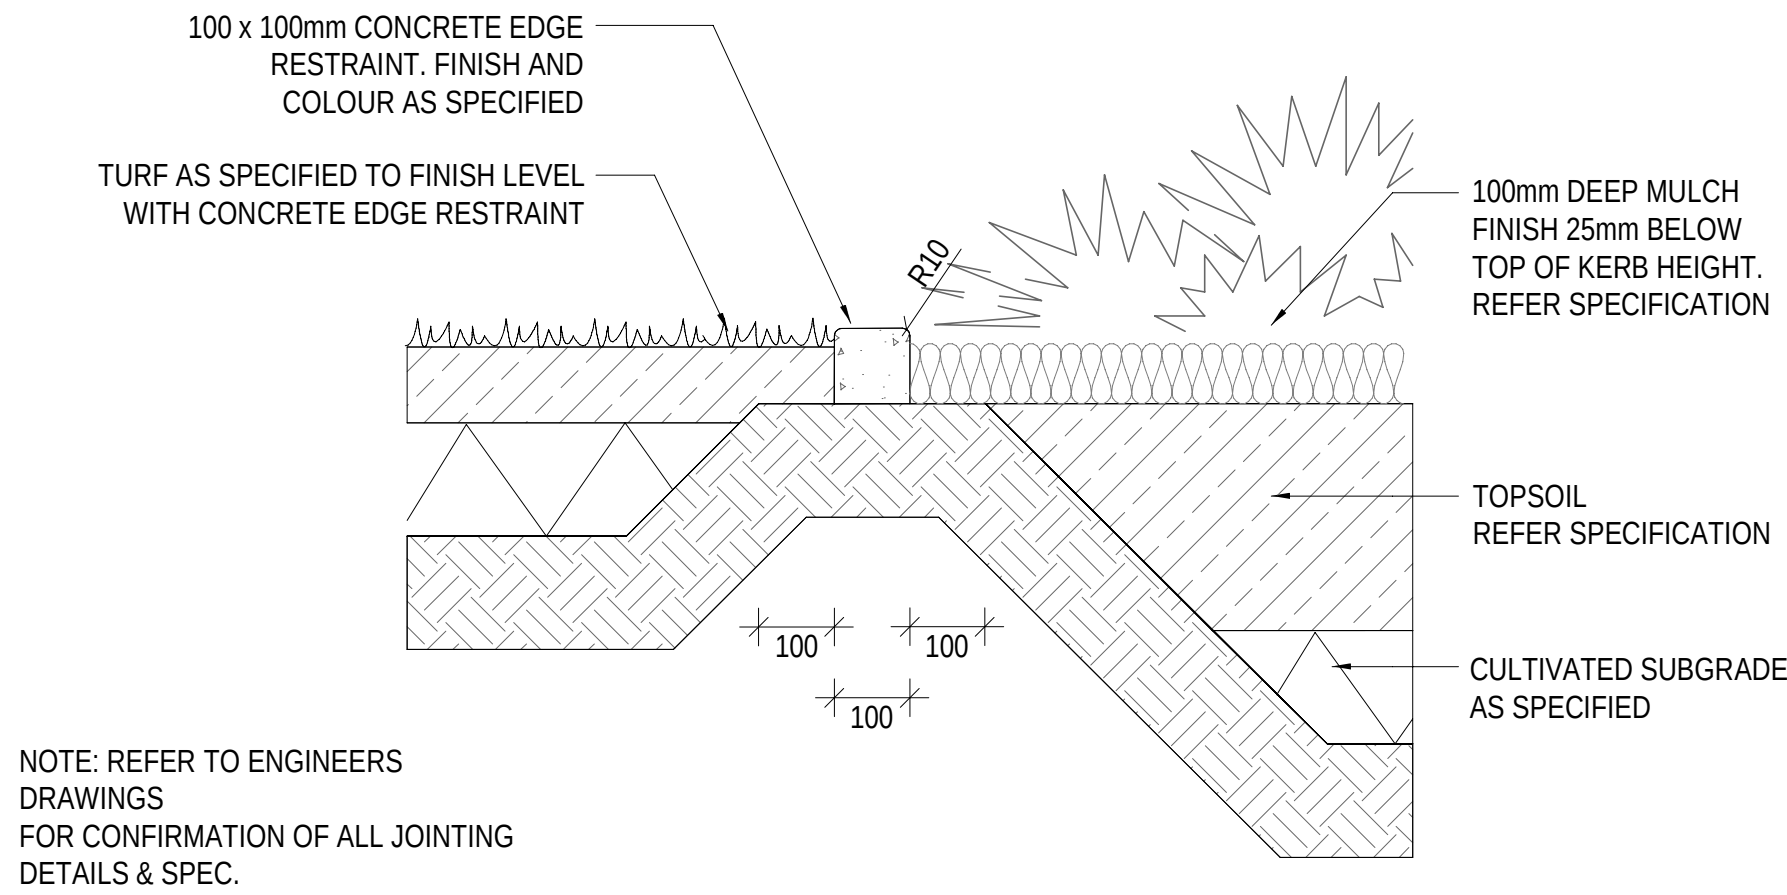


1 EDGE TYPE 1 - CONCRETE EDGE (TYPICAL)  
SCALE - 1 : 10

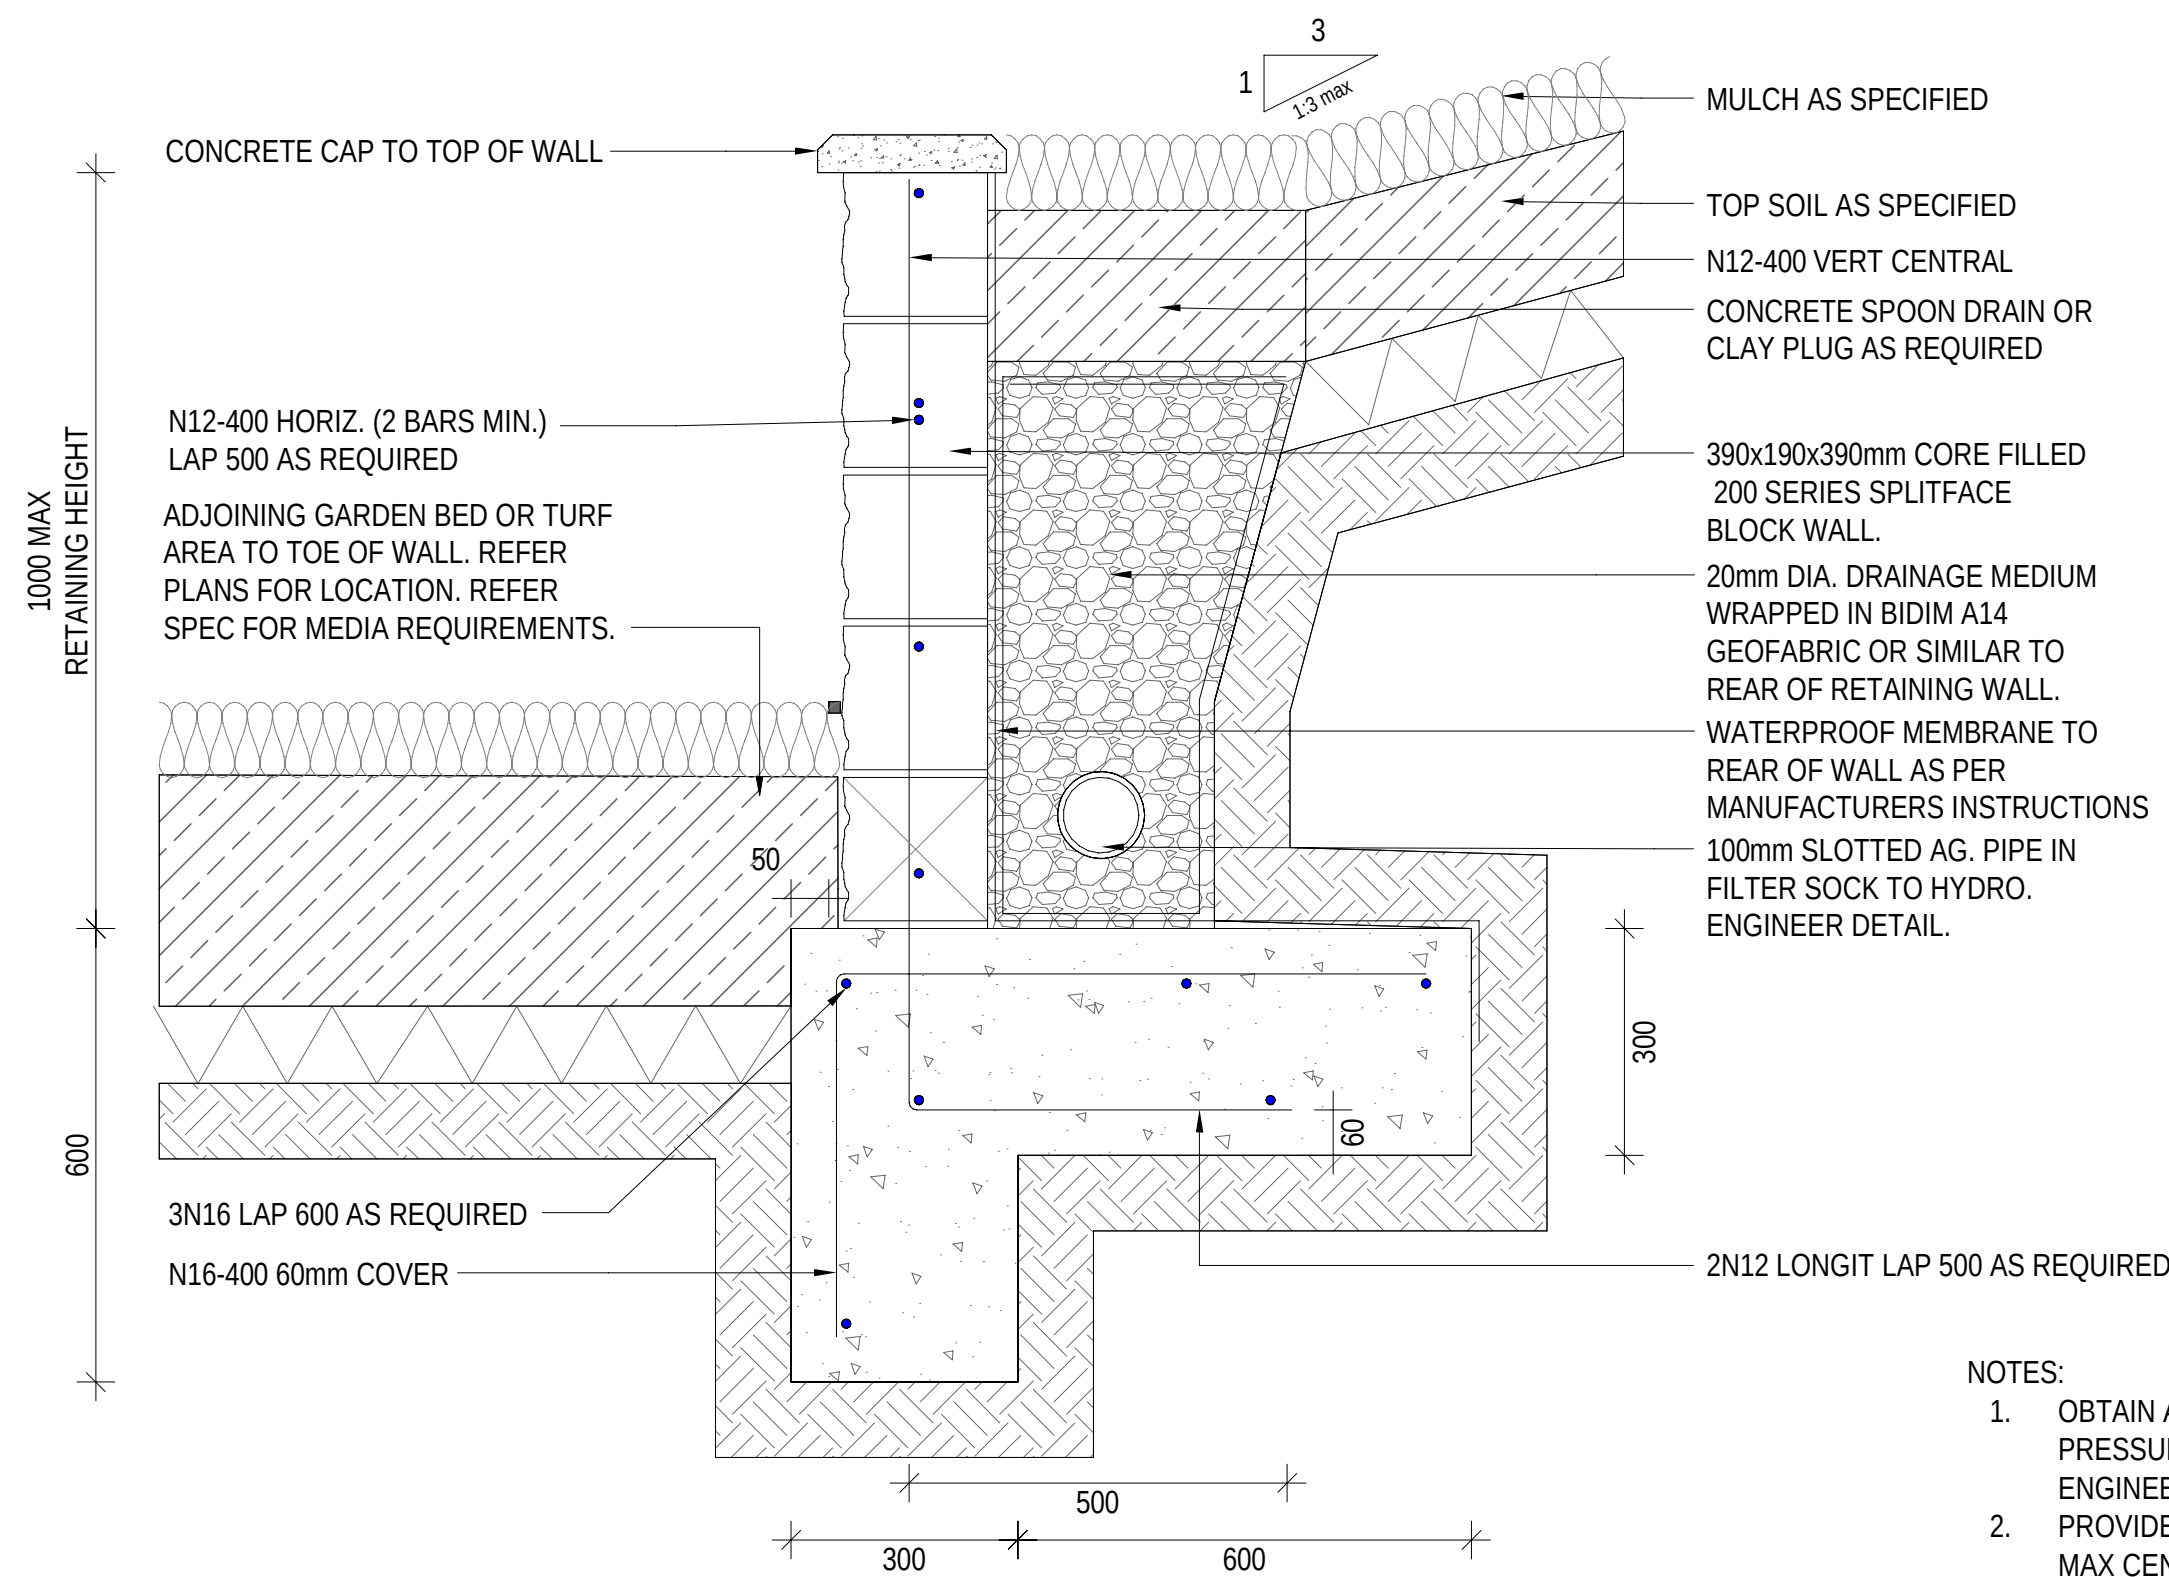

- NOTES:
- OBTAIN AN ALLOWABLE BEARING PRESSURE OF 150kPA TO GEOTECHNICAL ENGINEERS APPROVAL ON SITE
  - PROVIDE BLOCK CONTROL JOINTS AT 6m MAX CENTERS OR AT CHANGE OF WALL HEIGHT
  - REFER TO STRUCTURAL DRAWINGS FOR TYPICAL BLOCK DETAILS (I.E. CORNER JUNCTIONS AND JOINT DETAILS ETC.)

2 WALL TYPE 2 - SPLIT FACED BLOCKWORK WALL - SOFTSCAPE INTERFACE  
SCALE - 1 : 10

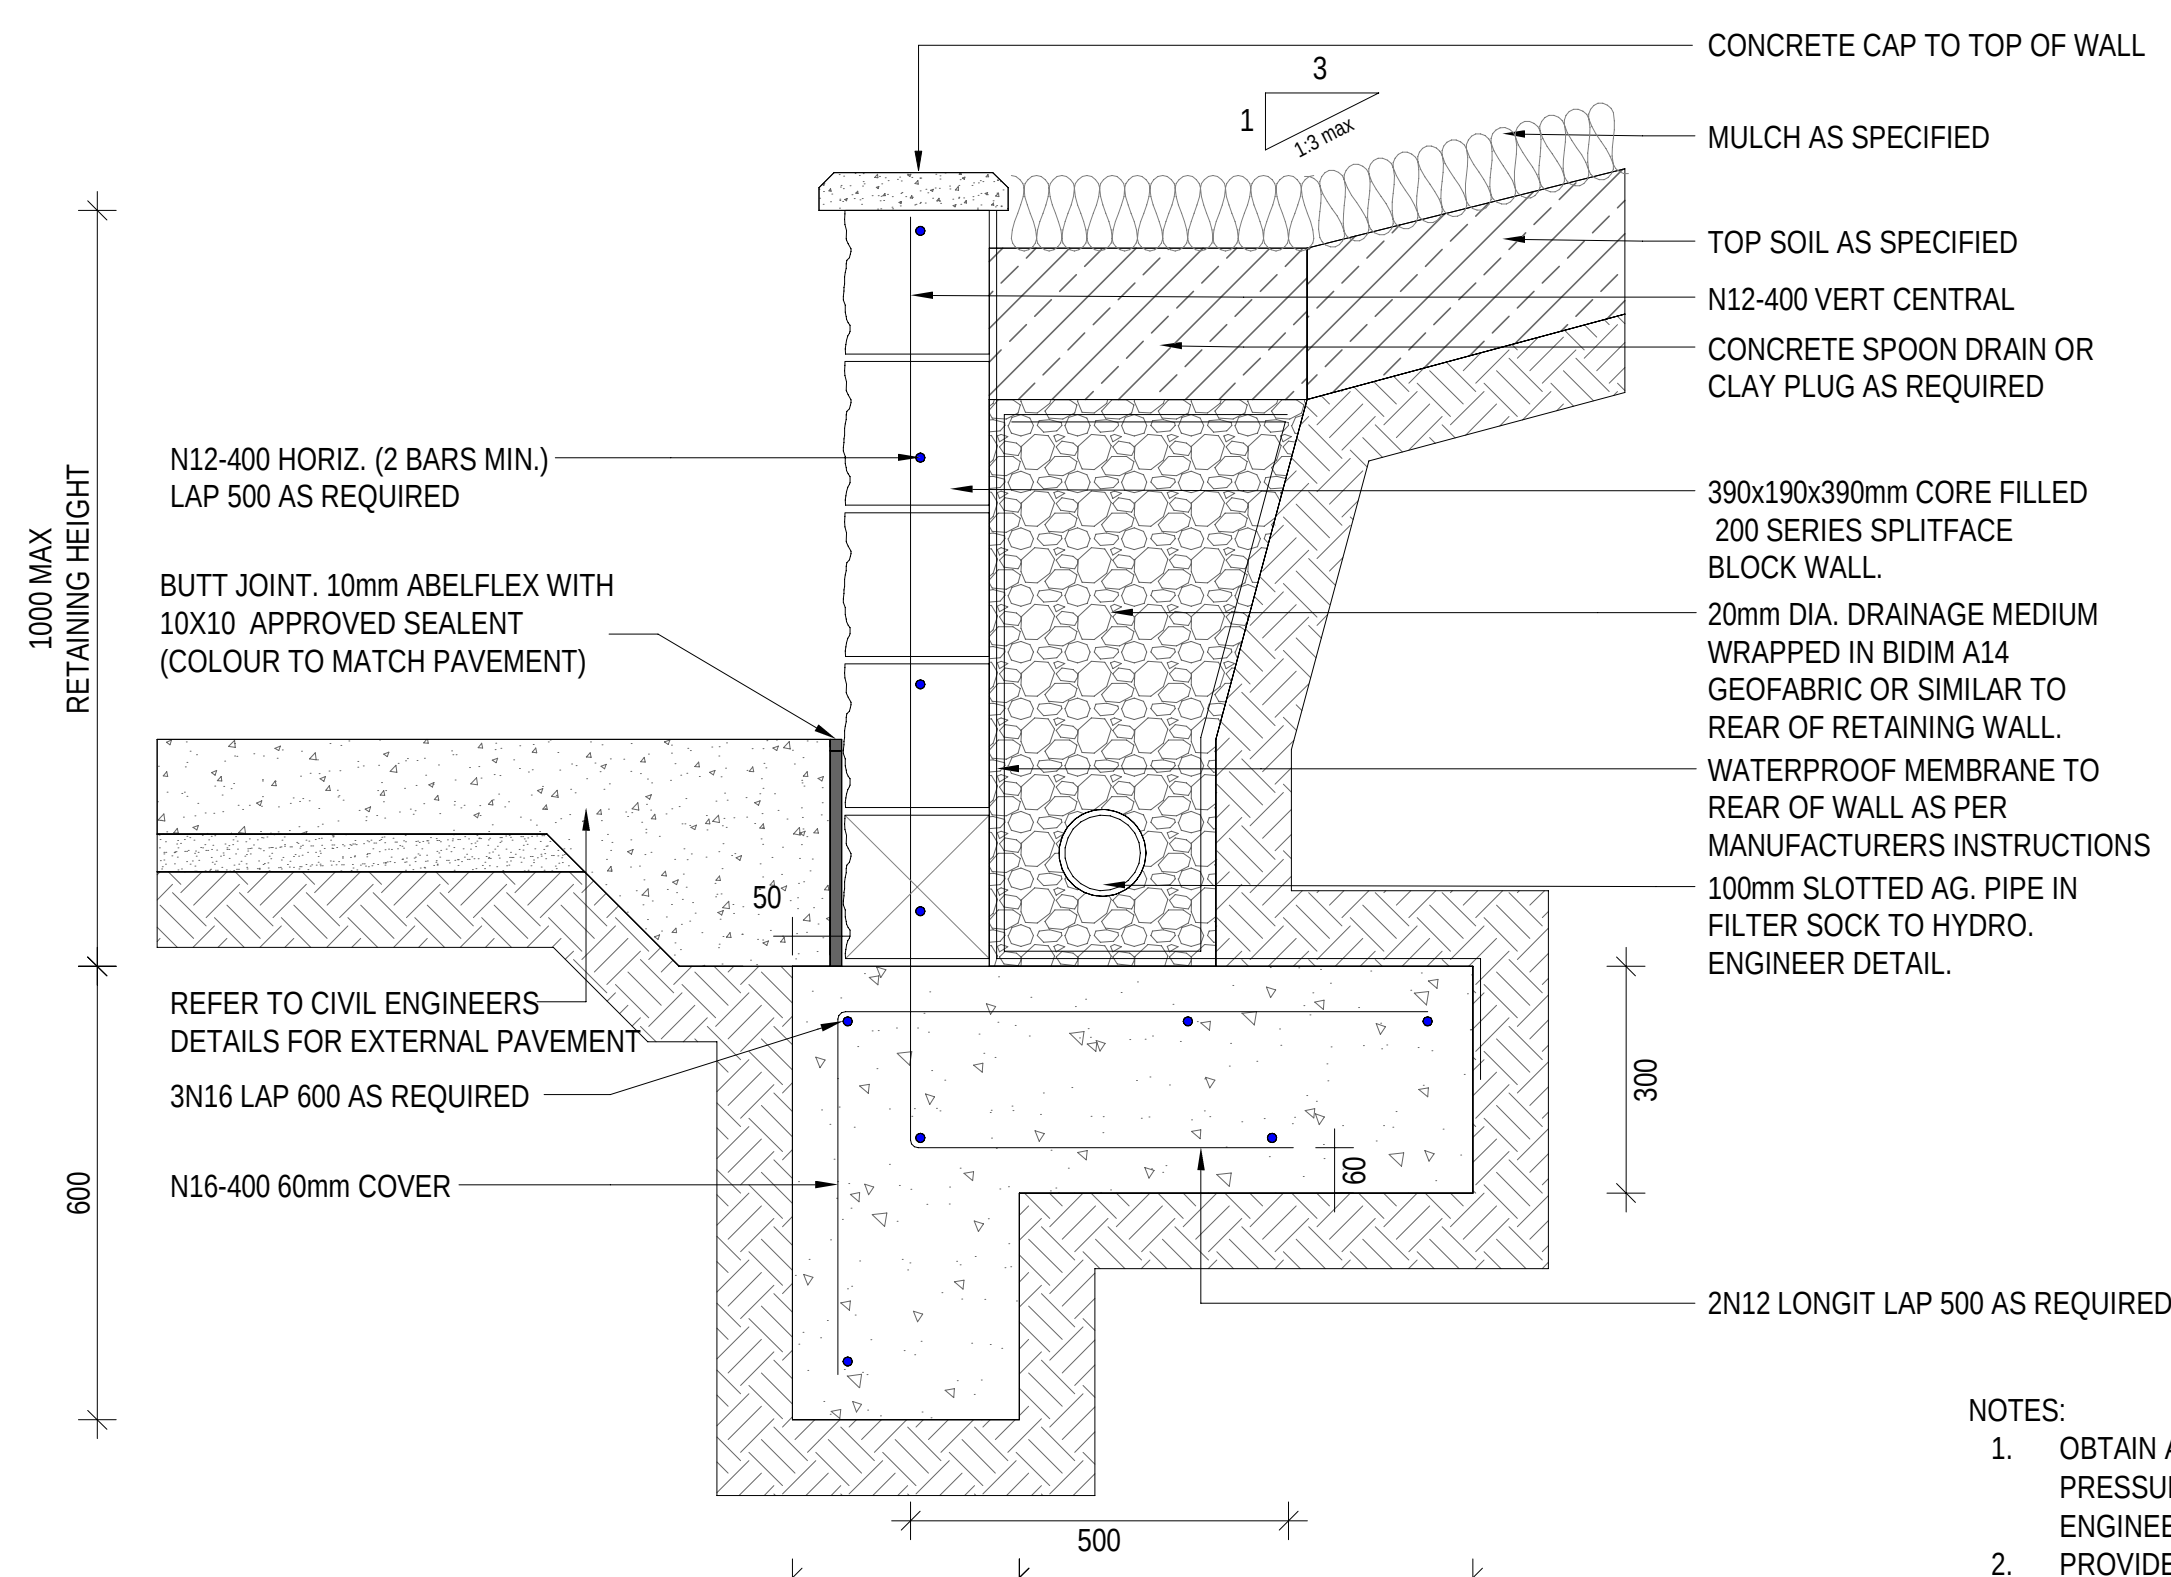

- NOTES:
- OBTAIN AN ALLOWABLE BEARING PRESSURE OF 150kPA TO GEOTECHNICAL ENGINEERS APPROVAL ON SITE
  - PROVIDE BLOCK CONTROL JOINTS AT 6m MAX CENTERS OR AT CHANGE OF WALL HEIGHT
  - REFER TO STRUCTURAL DRAWINGS FOR TYPICAL BLOCK DETAILS (I.E. CORNER JUNCTIONS AND JOINT DETAILS ETC.)

3 WALL TYPE 2 - SPLIT FACED BLOCKWORK WALL - HARDSTAND INTERFACE  
SCALE - 1 : 10

#### GENERAL NOTES

- DO NOT SCALE DRAWINGS. FIGURED DIMENSIONS HAVE PREFERENCE OVER SCALED DIMENSIONS.
- ANY DISCREPANCIES MUST BE REPORTED IMMEDIATELY TO THE SUPERINTENDENT.
- THESE DRAWINGS ARE TO BE READ IN CONJUNCTION WITH THE DETAILS, SPECIFICATIONS AND ENGINEERING DOCUMENTS.
- LOCATE AND PROTECT ALL UNDERGROUND SERVICES PRIOR TO ANY EXCAVATION. MAKE GOOD ALL DAMAGE TO EXISTING WORKS CAUSED BY THE ACTIVITY OF THESE WORKS.
- THESE DRAWINGS ARE TO BE PRINTED IN COLOUR.

These designs, plans and specifications and the copyright therein are the property of TRACT CONSULTANTS PTY. LTD. and must not be used, reproduced or copied, wholly or in part, without the written permission of TRACT CONSULTANTS PTY. LTD.

#### 60% DD NOT FOR CONSTRUCTION

| REV | DESCRIPTION | DATE       | DRWN | CHKD |
|-----|-------------|------------|------|------|
| 1   | Revision 1  | Date 1     | STa  | BM   |
| 2   | Draft Issue | 30/01/2026 | STa  | BM   |
| 3   | 60% DD      | 11/02/2026 | STa  | BM   |
|     |             |            |      |      |
|     |             |            |      |      |
#### Tract Landscape Architects Urban Designers Town Planners

Melbourne P: 03 9429 6133  
Brisbane P: 07 3002 6400  
Sydney P: 02 9954 3733  
Geelong P: 03 5221 0105  
Adelaide P: 08 8223 1324  
www.tract.com.au

#### PROJECT

CENTRAL QUEENSLAND UNIVERSITY  
(CQU) ROCKHAMPTON NORTH  
CAMPUS

#### CLIENT

CENTRAL QUEENSLAND UNIVERSITY  
(CQU)

#### DRAWING TITLE

DETAILS - SHEET 01

| DRAWING NUMBER      | REVISION |
|---------------------|----------|
| 725-0085-L-00-DR901 | 3        |

| DRAWN | CHECKED | APPROVED | DATE       |
|-------|---------|----------|------------|
| STa   | BM      | BM       | 11/02/2026 |

SCALE  
AS SHOWN A1