




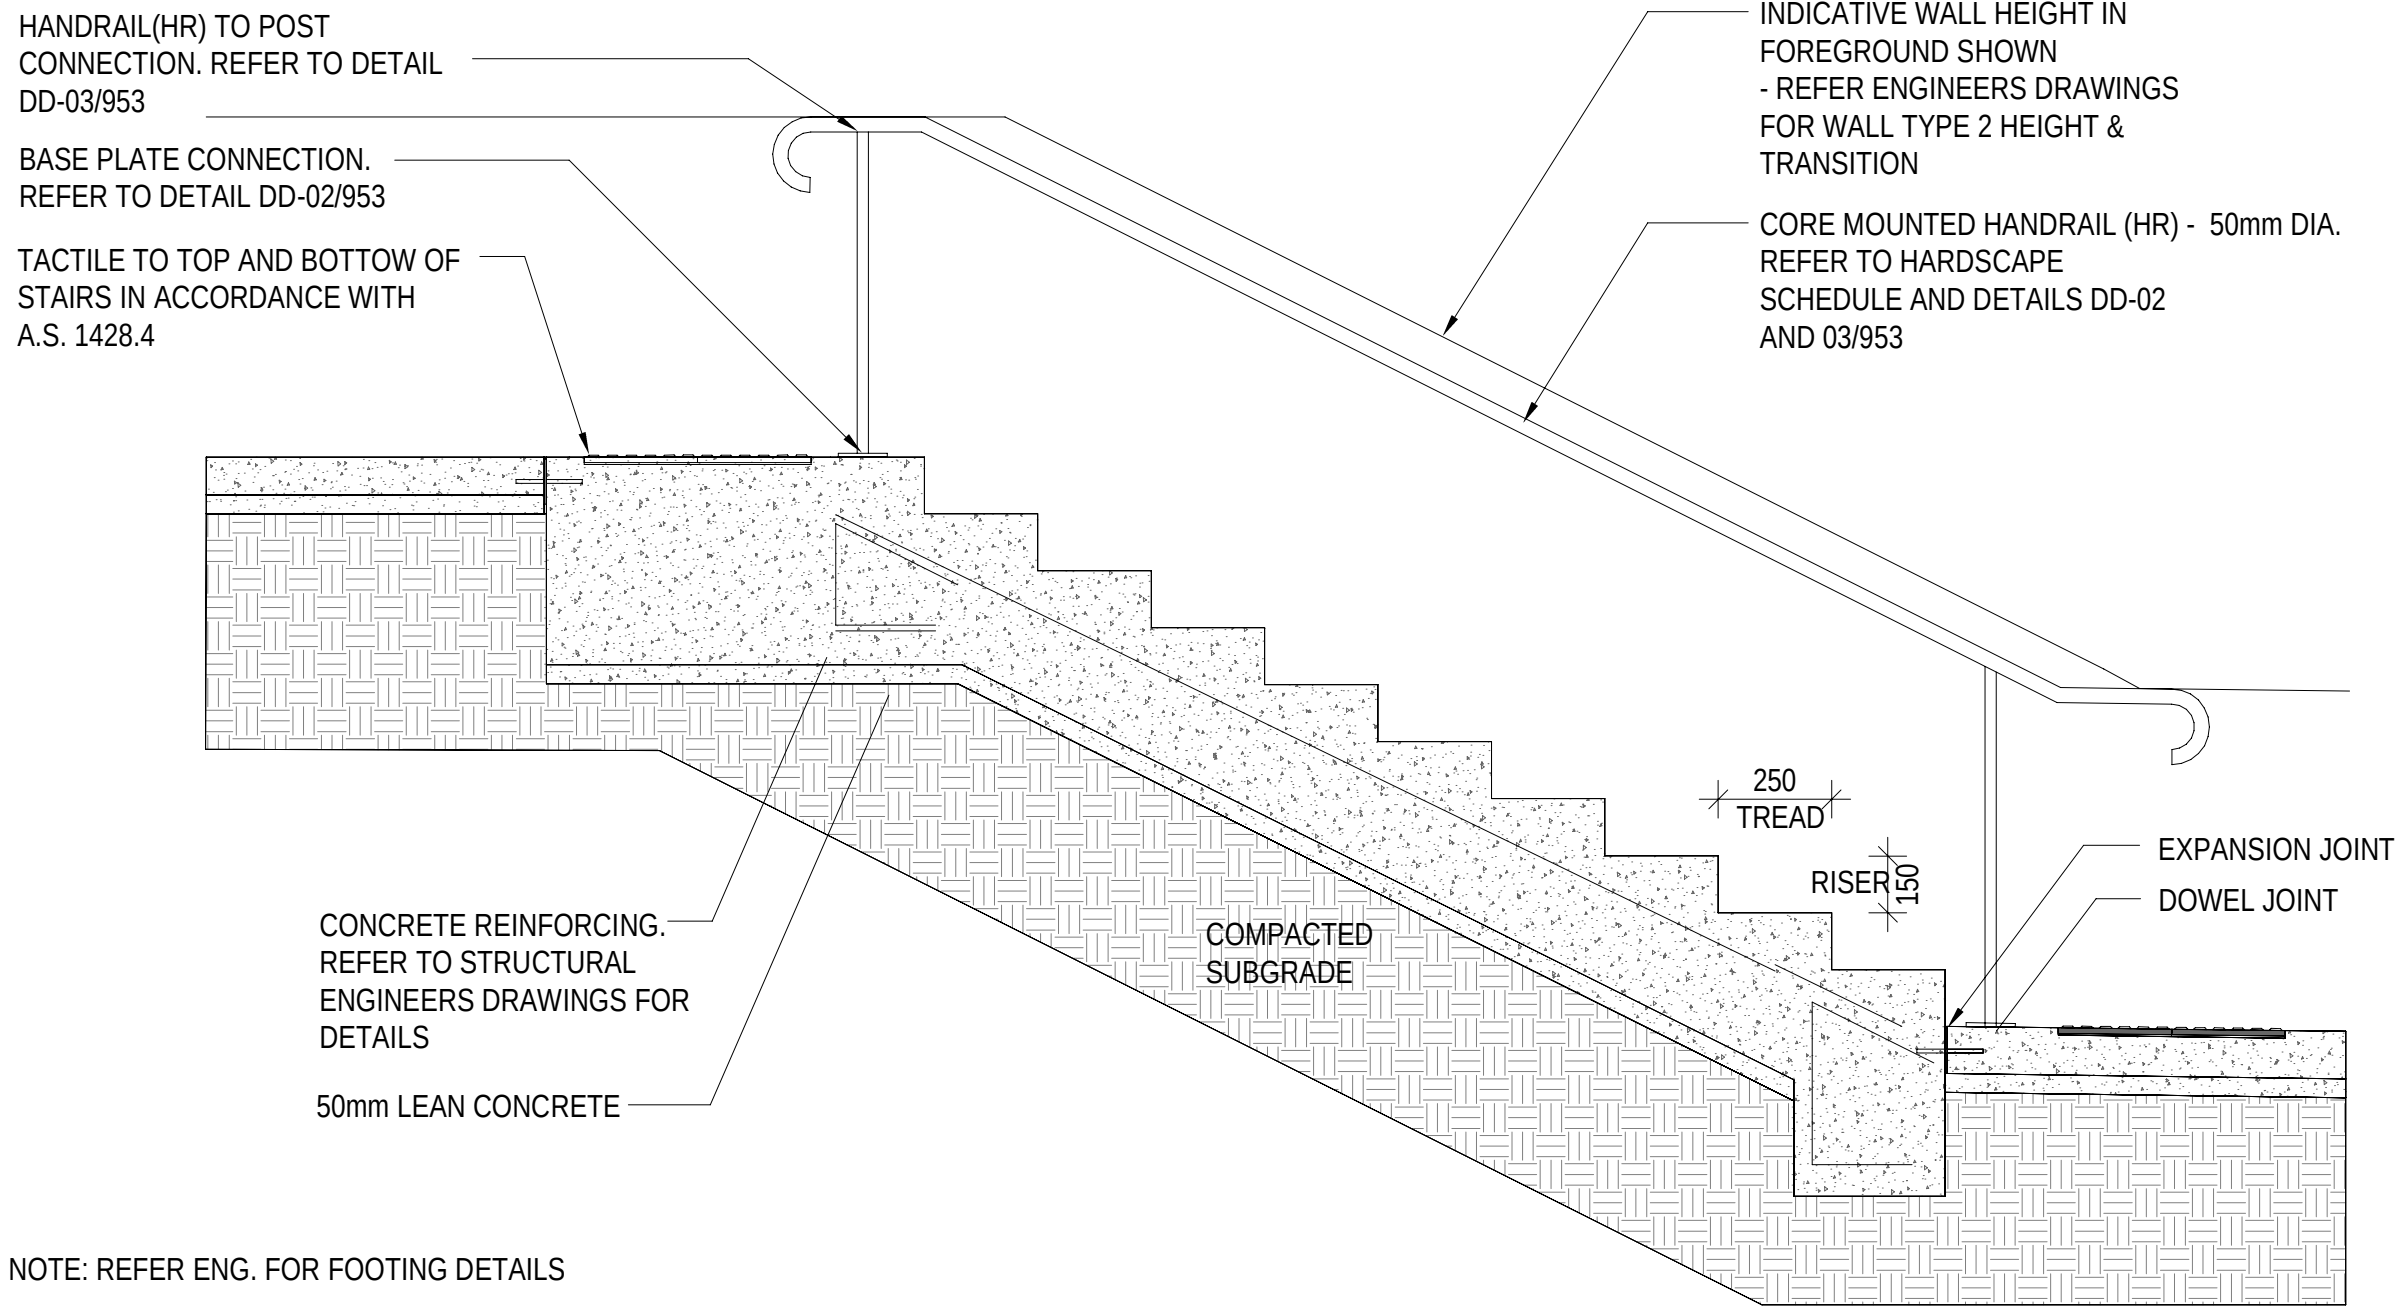

1 STR - INSITU CONCRETE STAIR - TYPICAL DETAIL
SCALE - 1 : 20

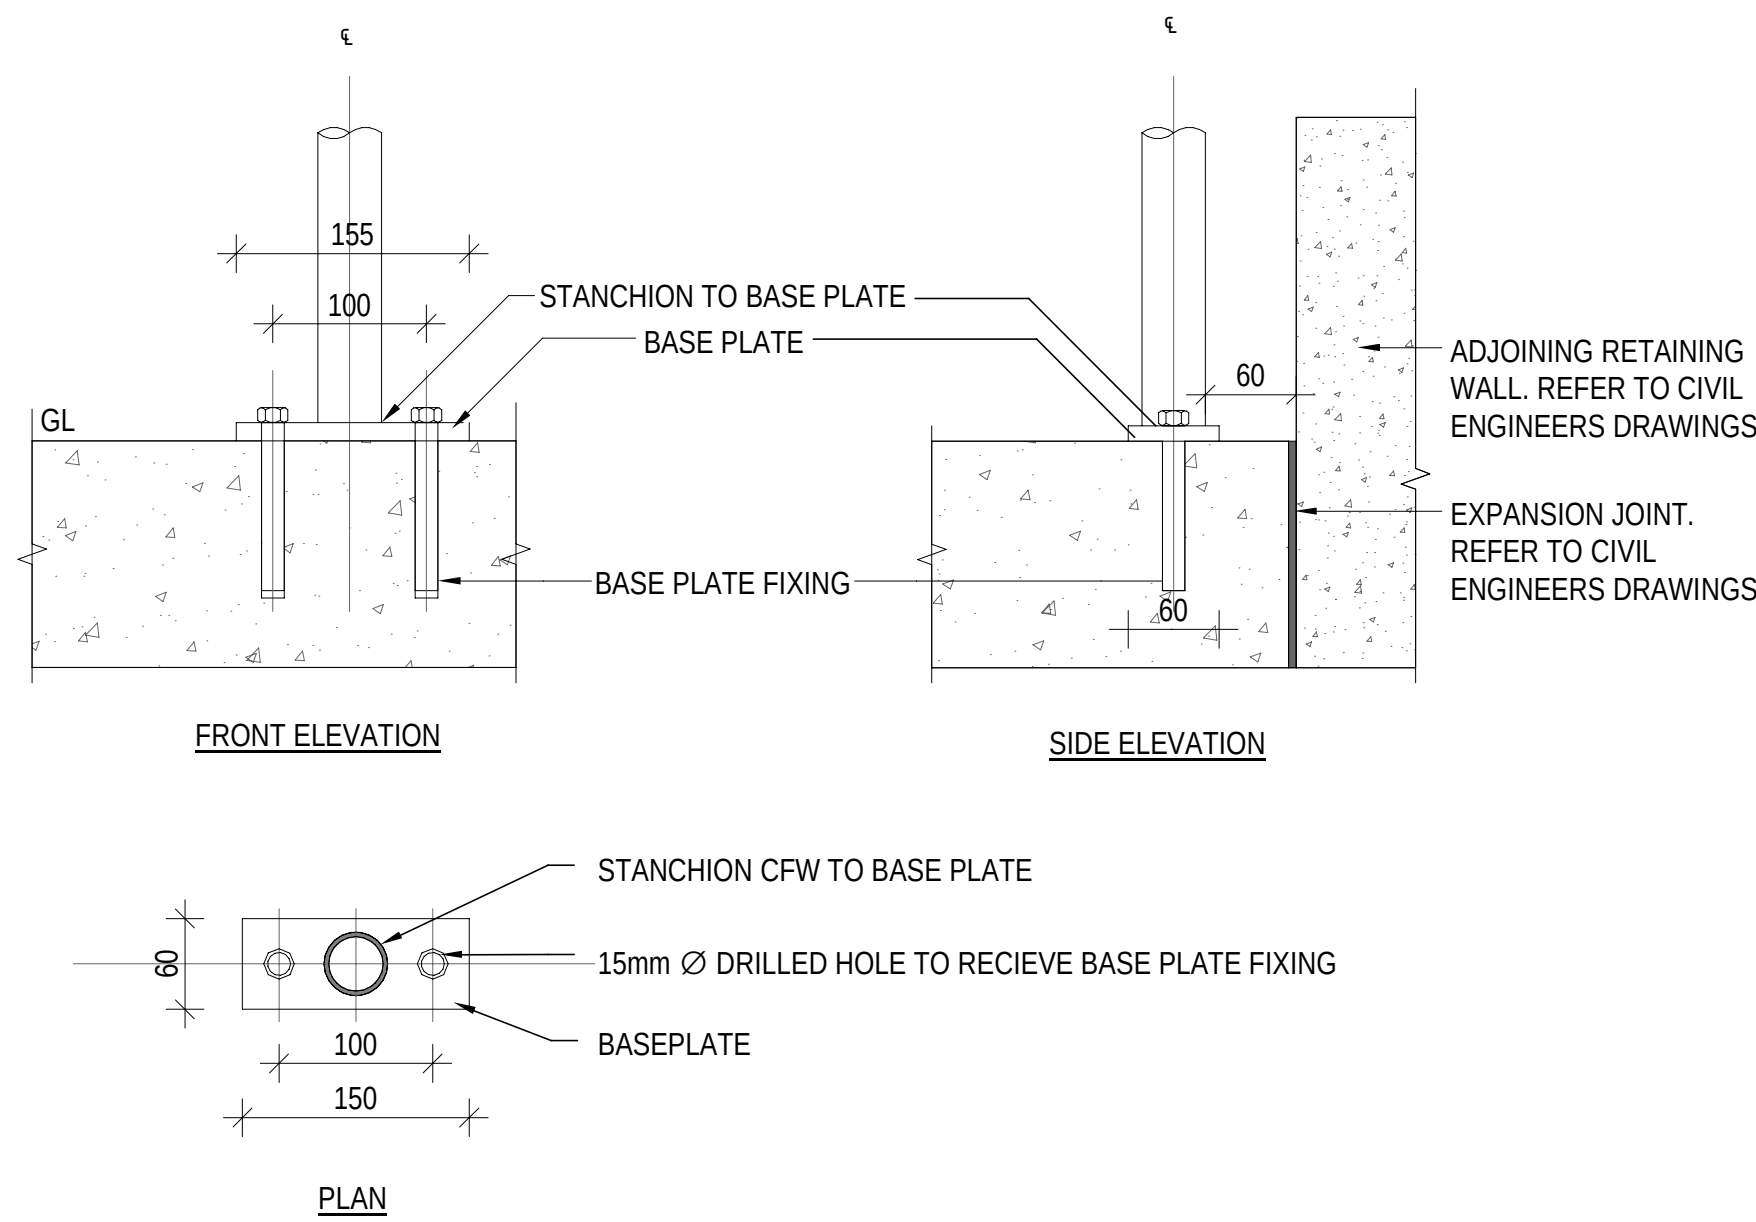

2 HANDRAIL(HR) - BASE PLATE
SCALE - 1 : 5

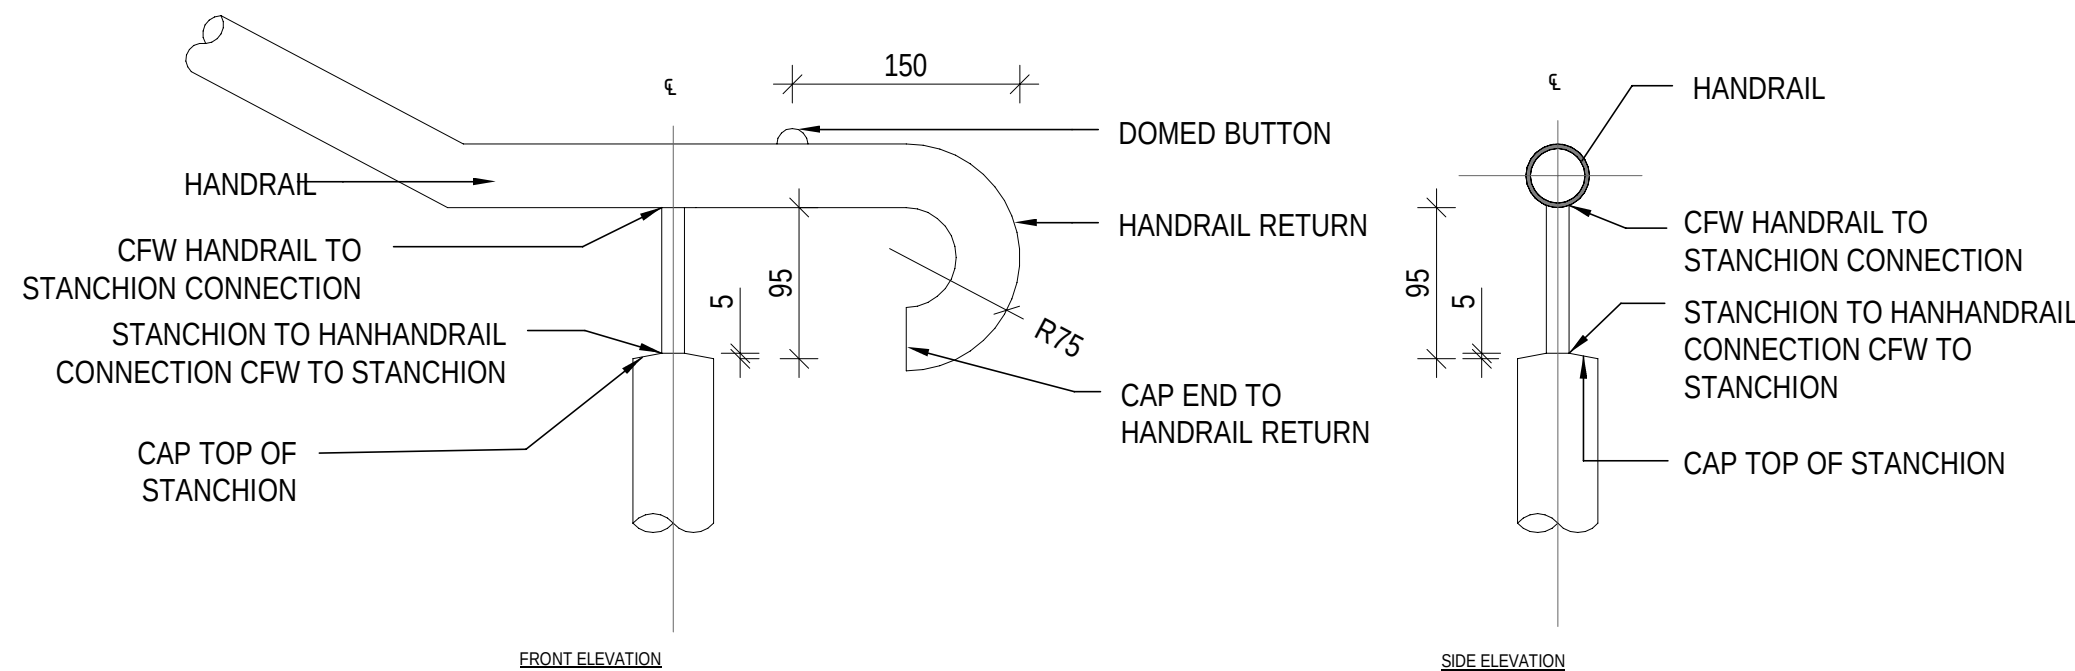

3 HANDRAIL(HR) - RETURN & STANCHION CONNECTION
SCALE - 1 : 5

Handrail (HR) - Schedule			
Description	Material	Size	Finish
Handrail	SS316L	42.16 mm OD 2.77 mm wall thickness	Refer Materials & Finishes Schedule
Stanchion	SS316L	42.16 mm OD 2.77 mm wall thickness	
Stanchion to handrail connection	SS316L	15 mm OD 2.00 mm wall thickness	
Base plate	SS316L	60 x 150 x 10 mm thick	-
Base plate fixing - Dynabolt Plus Sleeve Hexhead bolt or approved equal	SS316	M12x90 mm	

GENERAL NOTES

- DO NOT SCALE DRAWINGS. FIGURED DIMENSIONS HAVE PREFERENCE OVER SCALED DIMENSIONS.
- ANY DISCREPANCIES MUST BE REPORTED IMMEDIATELY TO THE SUPERINTENDENT.
- THESE DRAWINGS ARE TO BE READ IN CONJUNCTION WITH THE DETAILS, SPECIFICATIONS AND ENGINEERING DOCUMENTS.
- LOCATE AND PROTECT ALL UNDERGROUND SERVICES PRIOR TO ANY EXCAVATION. MAKE GOOD ALL DAMAGE TO EXISTING WORKS CAUSED BY THE ACTIVITY OF THESE WORKS.
- THESE DRAWINGS ARE TO BE PRINTED IN COLOUR.

These designs, plans and specifications and the copyright therein are the property of TRACT CONSULTANTS PTY. LTD. and must not be used, reproduced or copied, wholly or in part, without the written permission of TRACT CONSULTANTS PTY. LTD.

60% DD NOT FOR CONSTRUCTION

REV	DESCRIPTION	DATE	DRWN	CHKD
1	Revision 1	Date 1	STa	BM
2	Draft Issue	30/01/2026	STa	BM
3	60% DD	11/02/2026	STa	BM

Tract Landscape Architects Urban Designers Town Planners

Melbourne P: 03 9429 6133
Brisbane P: 07 3002 6400
Sydney P: 02 9954 3733
Geelong P: 03 5221 0105
Adelaide P: 08 8223 1324

www.tract.com.au

PROJECT

CENTRAL QUEENSLAND UNIVERSITY
(CQU) ROCKHAMPTON NORTH
CAMPUS

CLIENT

CENTRAL QUEENSLAND UNIVERSITY
(CQU)

DRAWING TITLE

DETAILS - SHEET 03

DRAWING NUMBER	REVISION
725-0085-L-00-DR903	3

DRAWN	CHECKED	APPROVED	DATE
STa	BM	BM	11/02/2026

SCALE
AS SHOWN A1