




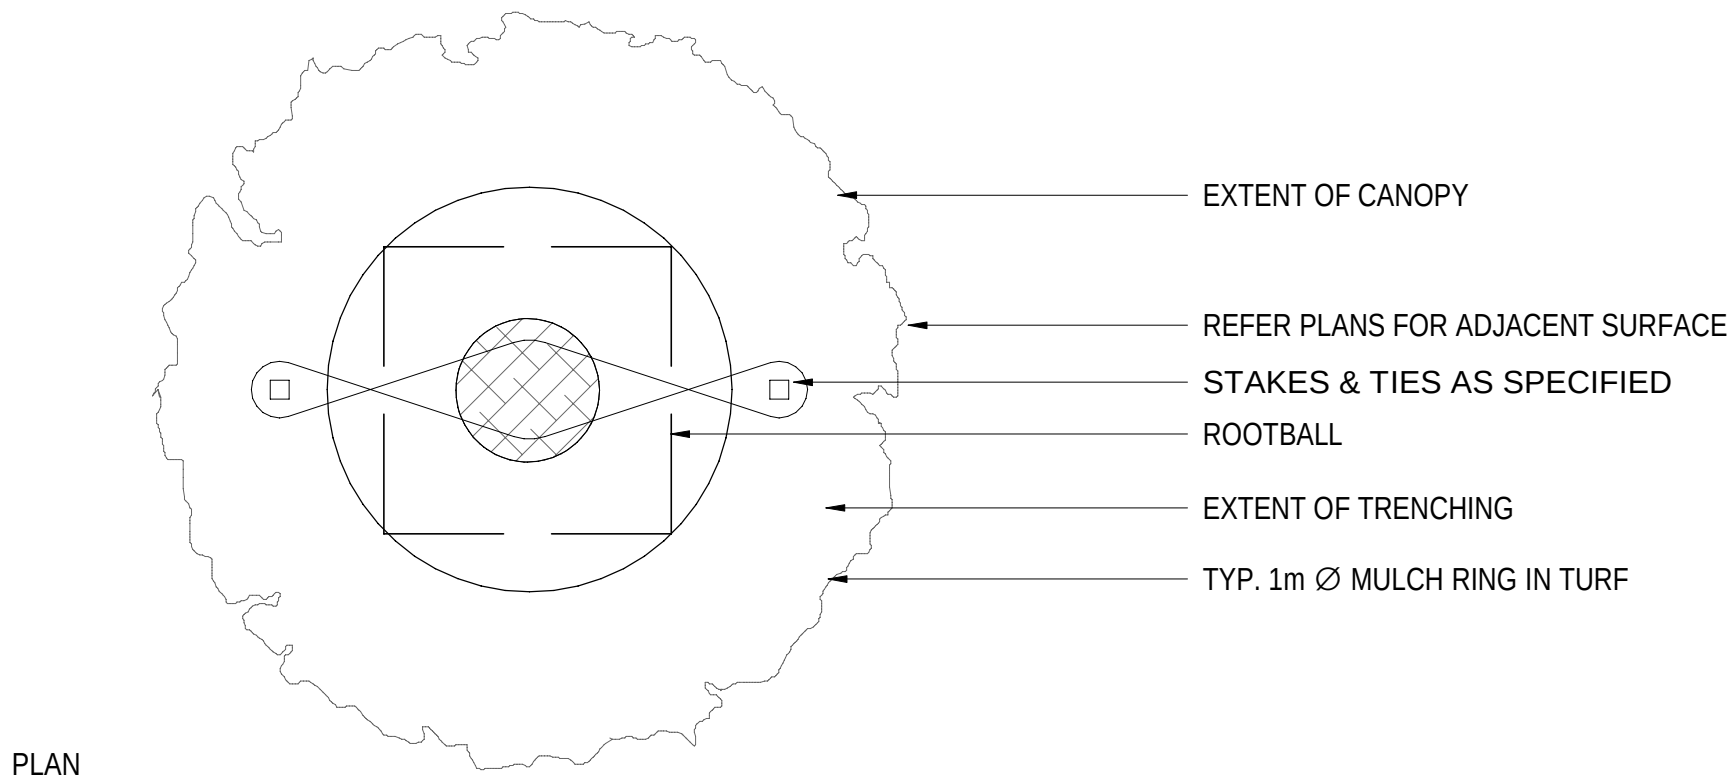


PLAN

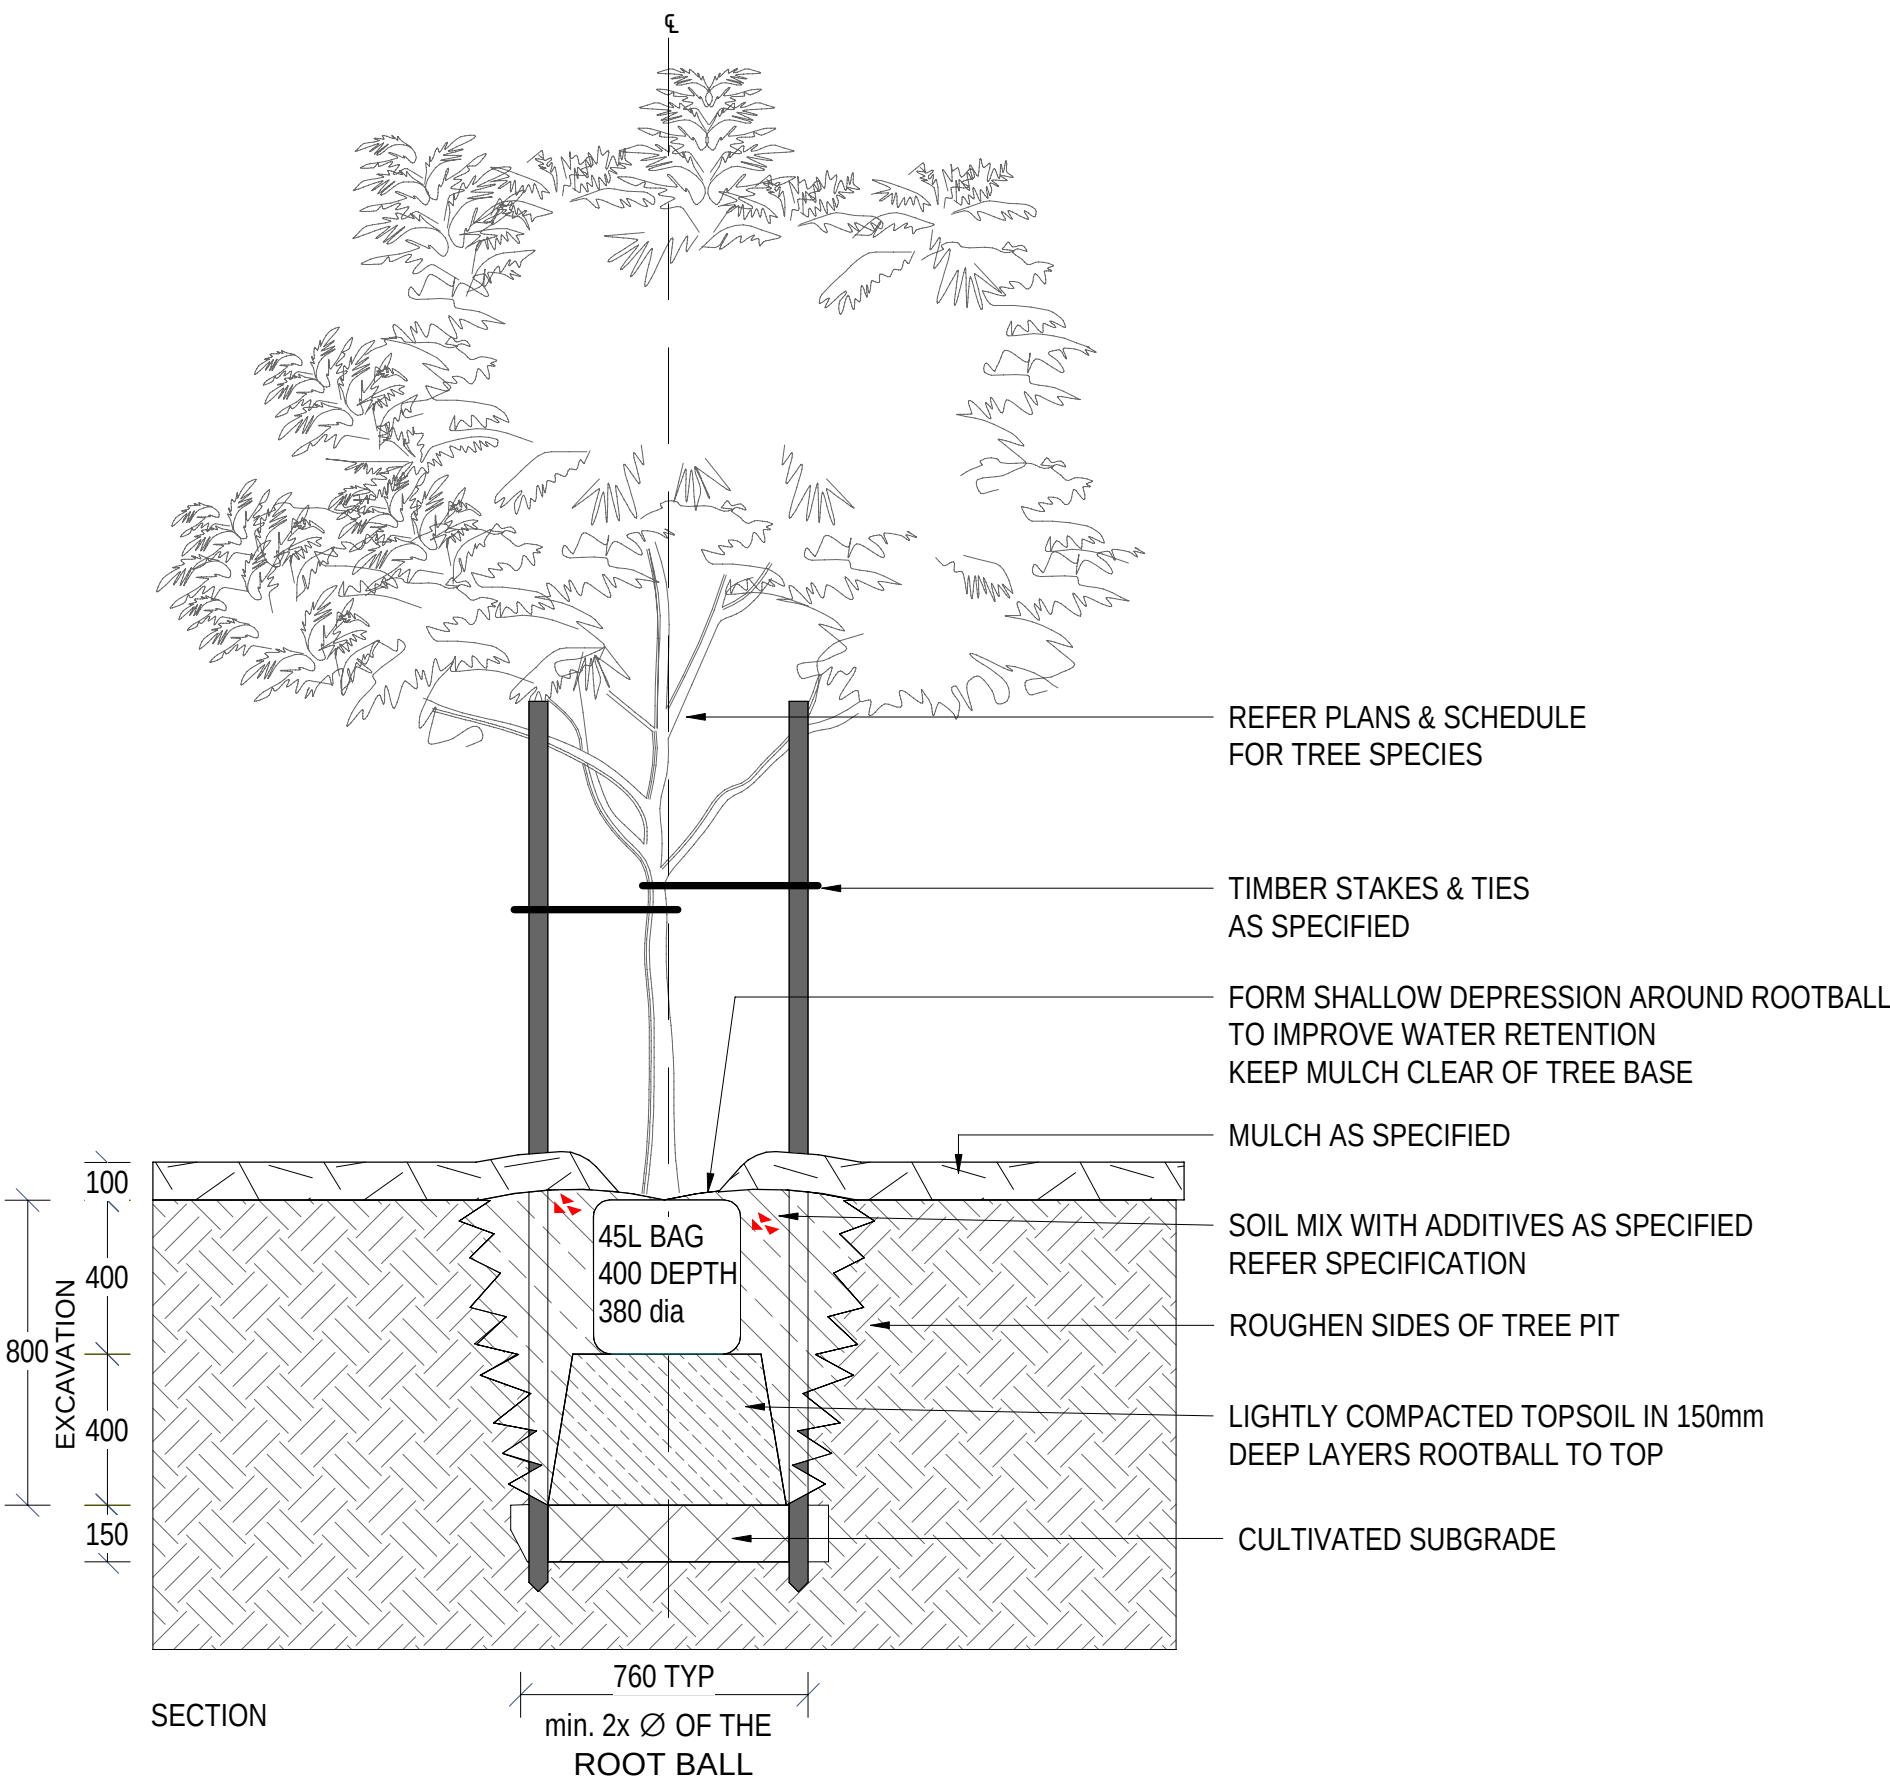

1 45L TREE IN PLANTING IN NATURAL GROUND
SCALE - 1 : 20

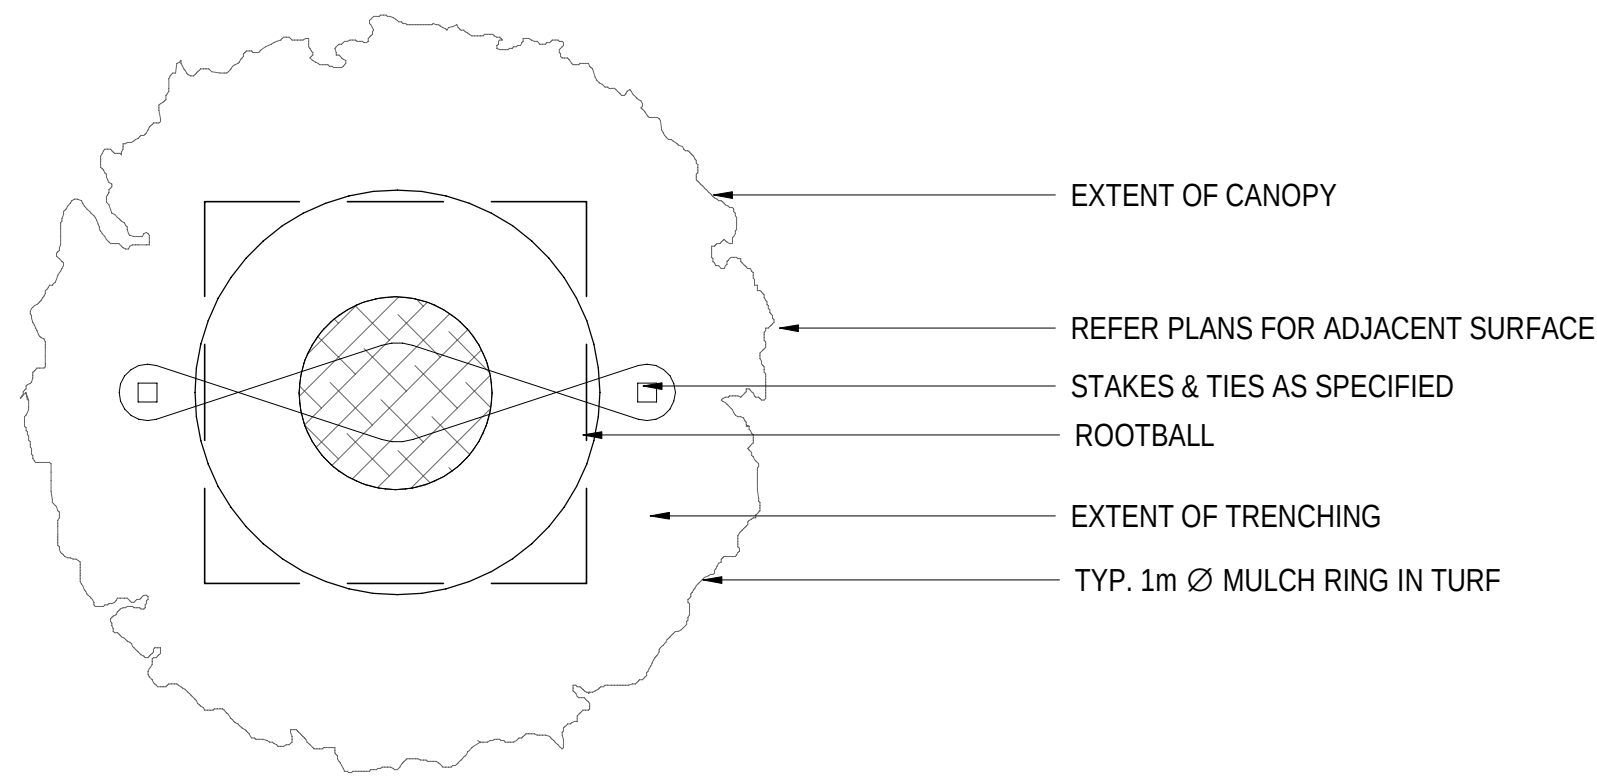

PLAN

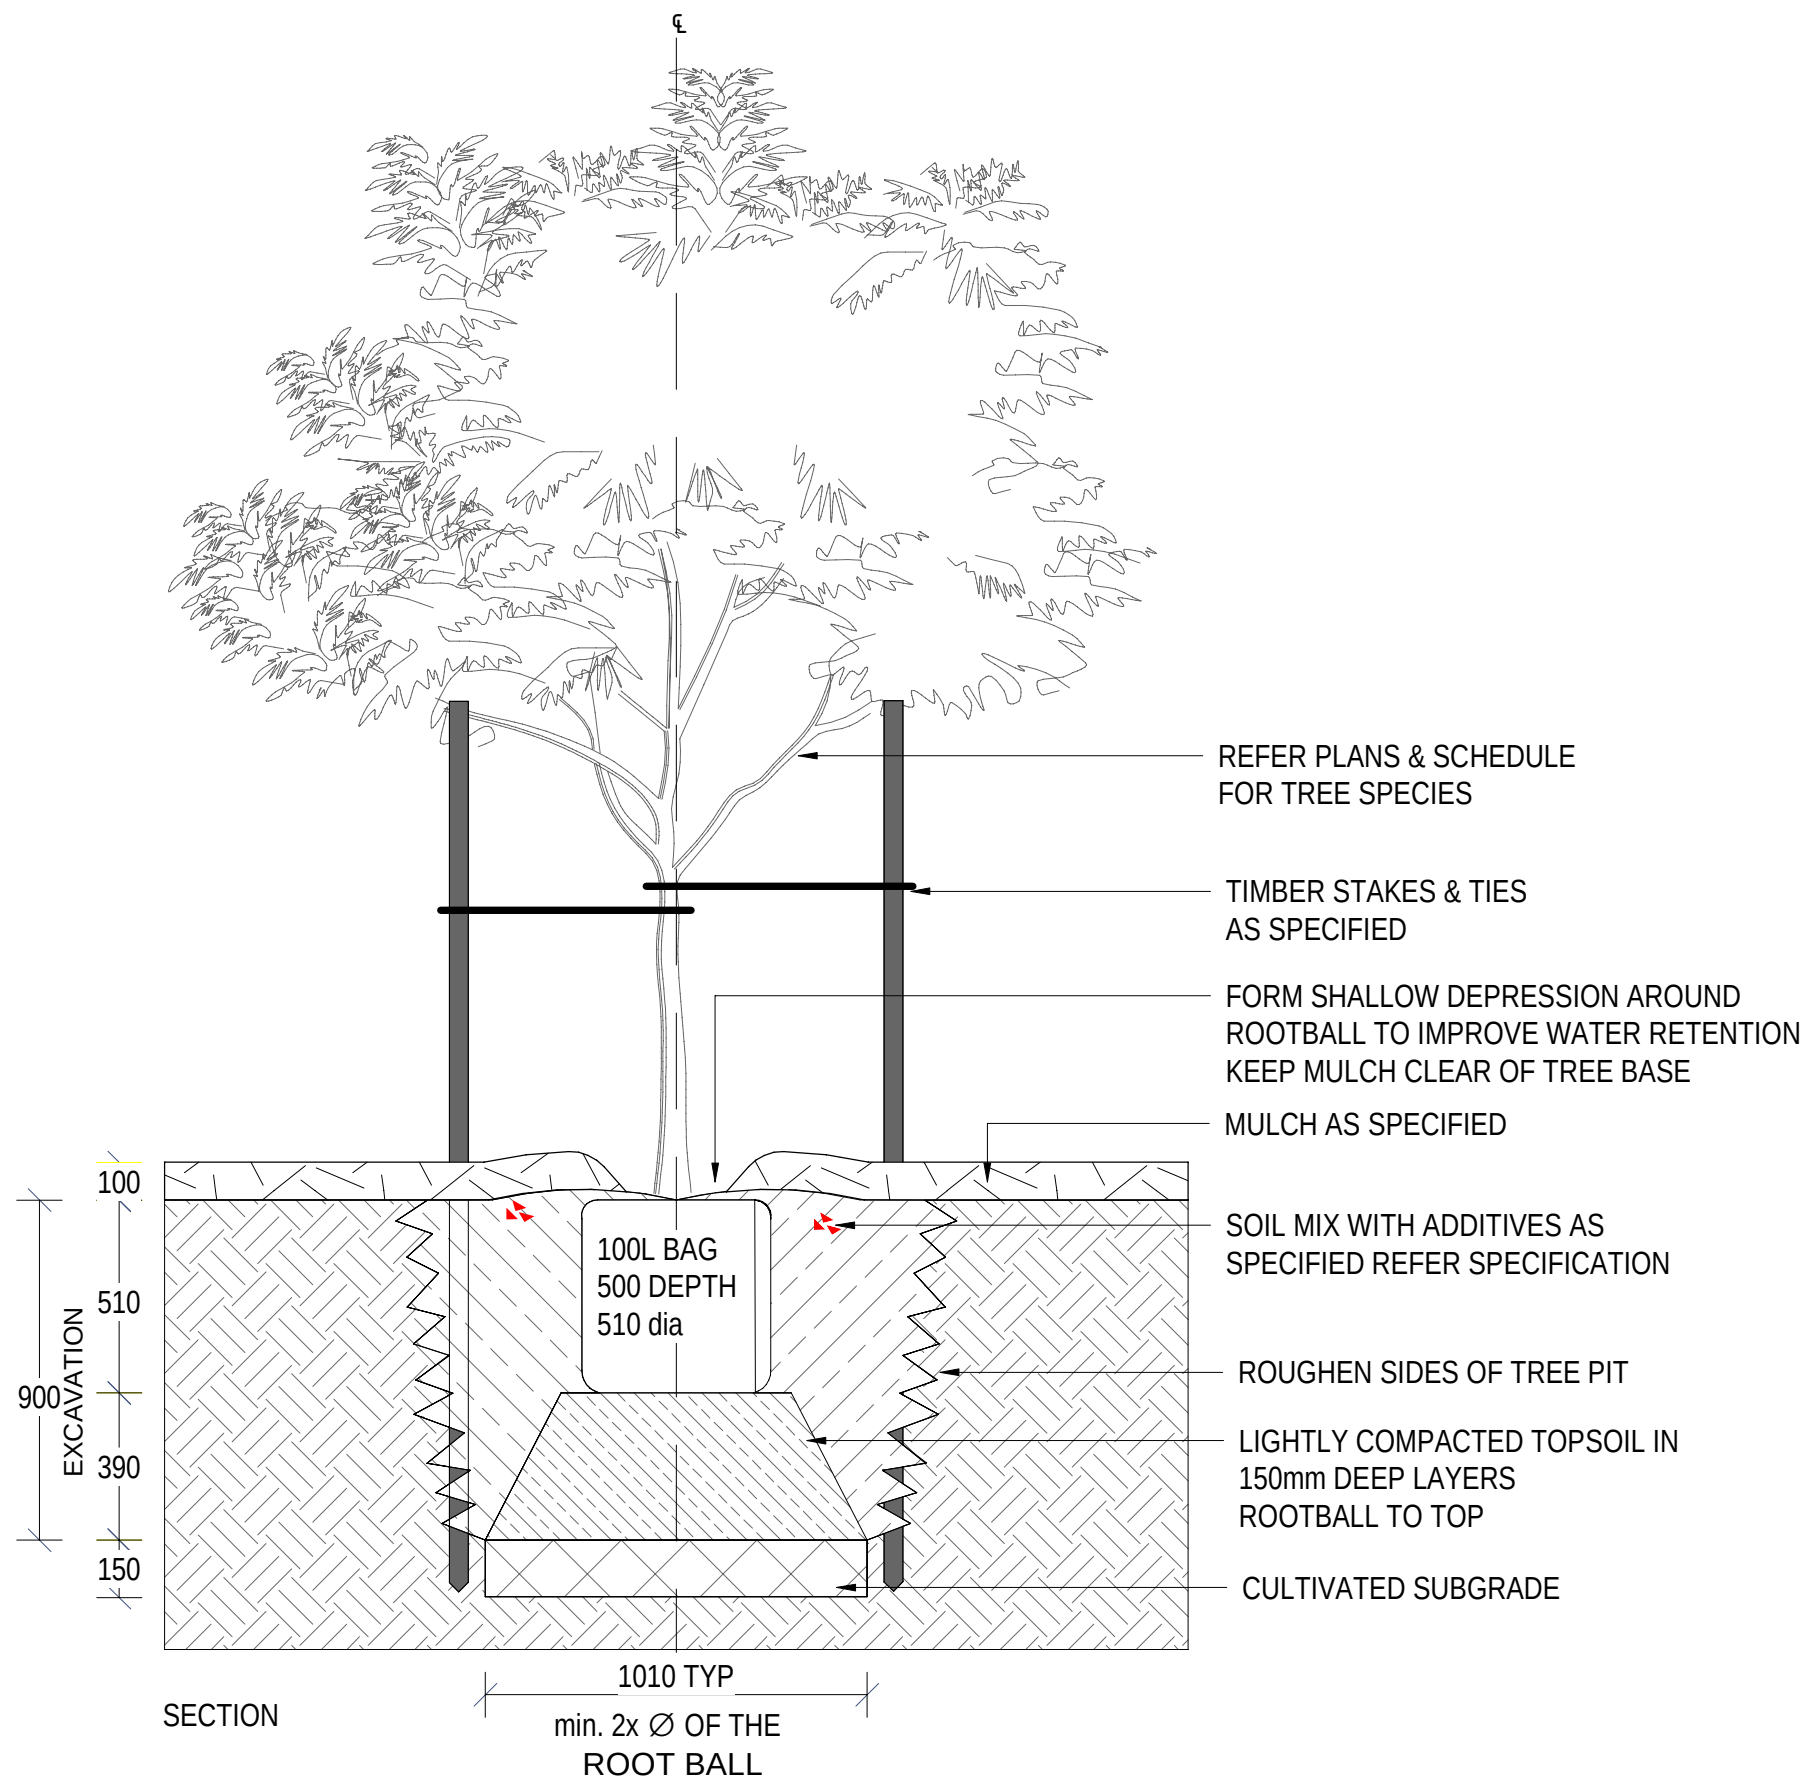

2 100L TREE IN PLANTING IN NATURAL GROUND
SCALE - 1 : 20

GENERAL NOTES

- DO NOT SCALE DRAWINGS. FIGURED DIMENSIONS HAVE PREFERENCE OVER SCALED DIMENSIONS.
- ANY DISCREPANCIES MUST BE REPORTED IMMEDIATELY TO THE SUPERINTENDENT.
- THESE DRAWINGS ARE TO BE READ IN CONJUNCTION WITH THE DETAILS, SPECIFICATIONS AND ENGINEERING DOCUMENTS.
- LOCATE AND PROTECT ALL UNDERGROUND SERVICES PRIOR TO ANY EXCAVATION. MAKE GOOD ALL DAMAGE TO EXISTING WORKS CAUSED BY THE ACTIVITY OF THESE WORKS.
- THESE DRAWINGS ARE TO BE PRINTED IN COLOUR.

These designs, plans and specifications and the copyright therein are the property of TRACT CONSULTANTS PTY. LTD. and must not be used, reproduced or copied, wholly or in part, without the written permission of TRACT CONSULTANTS PTY. LTD.

60% DD
NOT FOR CONSTRUCTION

REV	DESCRIPTION	DATE	DRWN	CHKD
1	Revision 1	Date 1	STa	BM
2	Draft Issue	30/01/2026	STa	BM
3	60% DD	11/02/2026	STa	BM

Tract
Landscape Architects
Urban Designers
Town Planners

Melbourne P: 03 9429 6133
Brisbane P: 07 3002 6400
Sydney P: 02 9954 3733
Geelong P: 03 5221 0105
Adelaide P: 08 8223 1324
www.tract.com.au

PROJECT
CENTRAL QUEENSLAND UNIVERSITY
(CQU) ROCKHAMPTON NORTH
CAMPUS

CLIENT
CENTRAL QUEENSLAND UNIVERSITY
(CQU)

DRAWING TITLE
DETAILS - SHEET 04

DRAWING NUMBER
725-0085-L-00-DR904

REVISION
3

DRAWN
STa

CHECKED
BM

APPROVED
BM

DATE
11/02/2026

SCALE
AS SHOWN A1