


.....

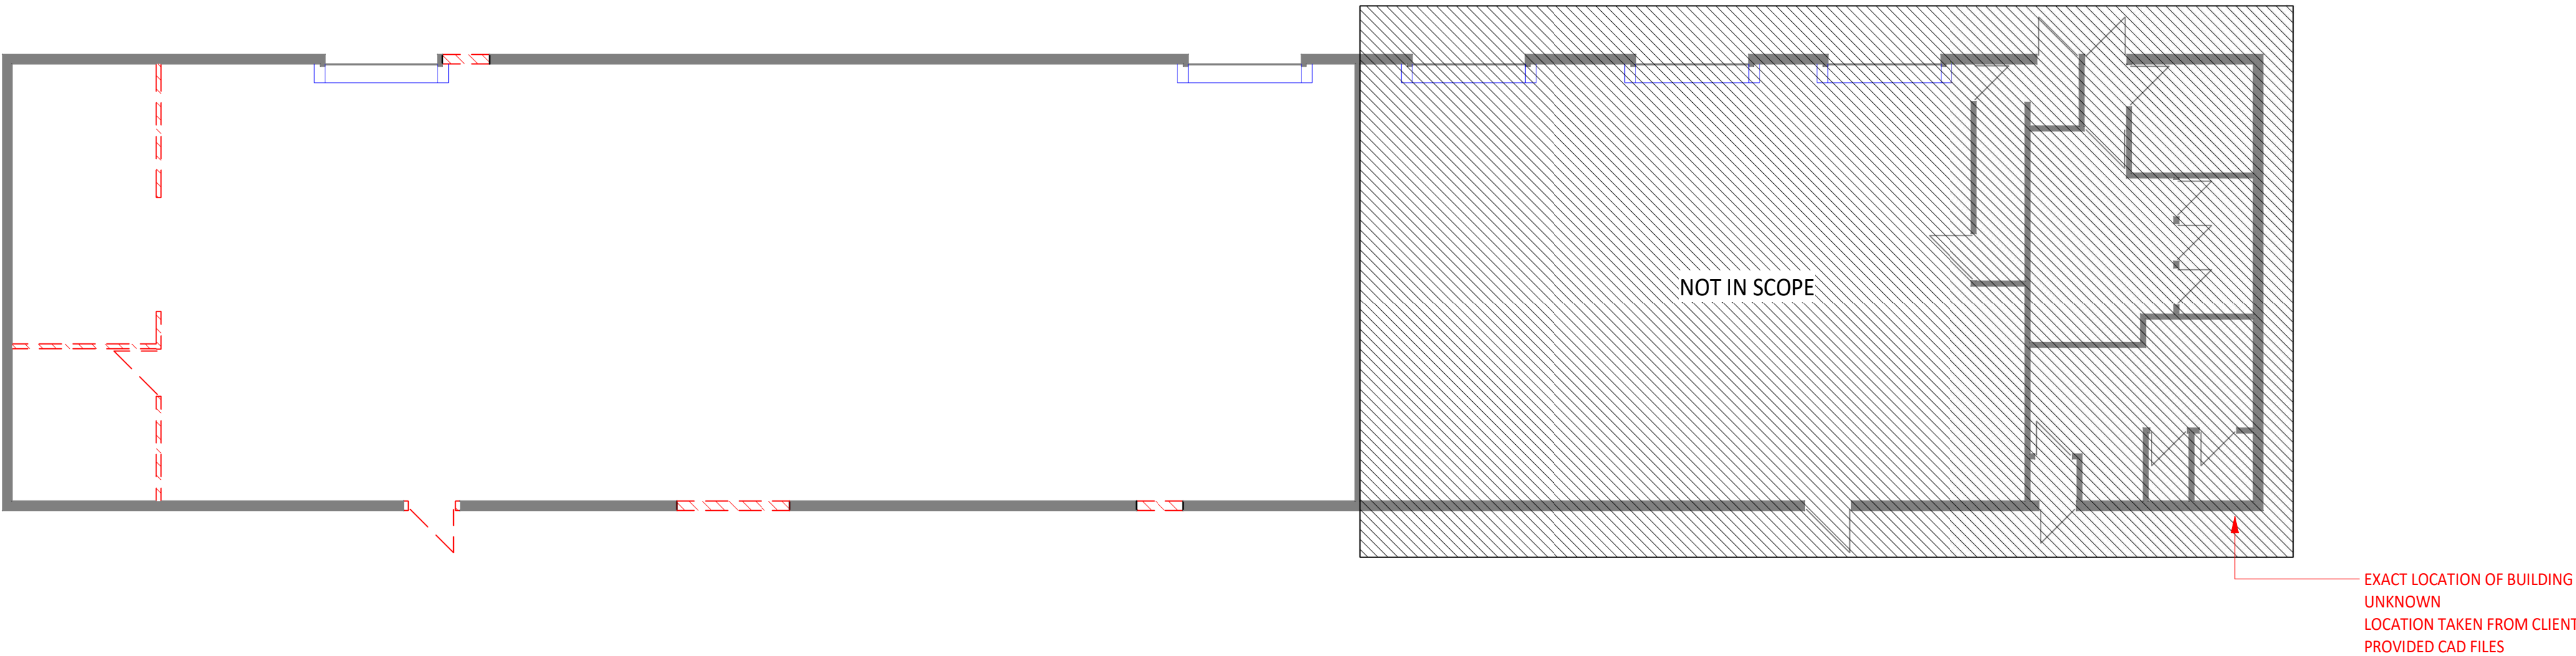

DEMOLITION LEGEND

GREY HATCH INDICATES EXISTING ROADS

GREY HATCH INDICATES EXISTING BUILDING NOT IN SCOPE

RED HATCH AND LINE INDICATES BUILDING ELEMENTS TO BE DEMOLISHED

OTHER PROJECT STAGE

NOTE: REFER TO SERVICES ENGINEERS DOCUMENTATION FOR EXTENT OF DEMOLITION OF EXISTING BUILDING SERVICES.

PLANS TO BE PRINTED IN COLOUR

ISSUED FOR TENDER

© Copyright
These drawings and designs and the copyright thereof are the property of Thomson Adsett Pty Ltd and must not be used, retained or copied without written permission of Thomson Adsett Pty Ltd. ABN 76 105 314 654 Trading as ThomsonAdsett. Dimensions take precedence over scaling. Do not measure off drawings as print sizes may vary

**CQU ROCKHAMPTON
TAFE
CONSOLIDATION -
STAGE 2**
ROCKHAMPTON, QUEENSLAND



A	12/02/26	ISSUED FOR TENDER	BS
1	30/01/26	DRAFT 60% ISSUE	BS
rev	date	details	init.

drawn	date
BS	30/01/26
checked	date
BS	30/01/26
verified	date
BS	30/01/26

scale

**ENGINEERING
DEPARTMENT DEMOLITION
PLAN**

scale
1 : 100 @ A1

project no.
260018

revision
A

sheet no.
CQU-ROK-21A-G-ARC-20-01