


INFORMATION REFLECTED ON THIS DRAWING REPRESENTS HYDRAULIC SERVICES DESIGN DEVELOPED FOR D&C TENDER ADVISE ONLY, AND SHOULD NOT BE REGARDED AS COMPLETE. THE D&C CONTRACTOR SHOULD REFER TO ALL ASSOCIATED ARCHITECTURAL AND OTHER DISCIPLINE DRAWINGS, PROJECT BRIEFS AND CLIENT REQUIREMENTS AND MAKE ADEQUATE ALLOWANCES FOR ALL NECESSARY HYDRAULIC SERVICES WORKS TO MEET THESE REQUIREMENTS, EQUIPMENT SCHEDULES AND COMPLIANCE WITH THE NCC & APPROPRIATE AUSTRALIAN STANDARDS

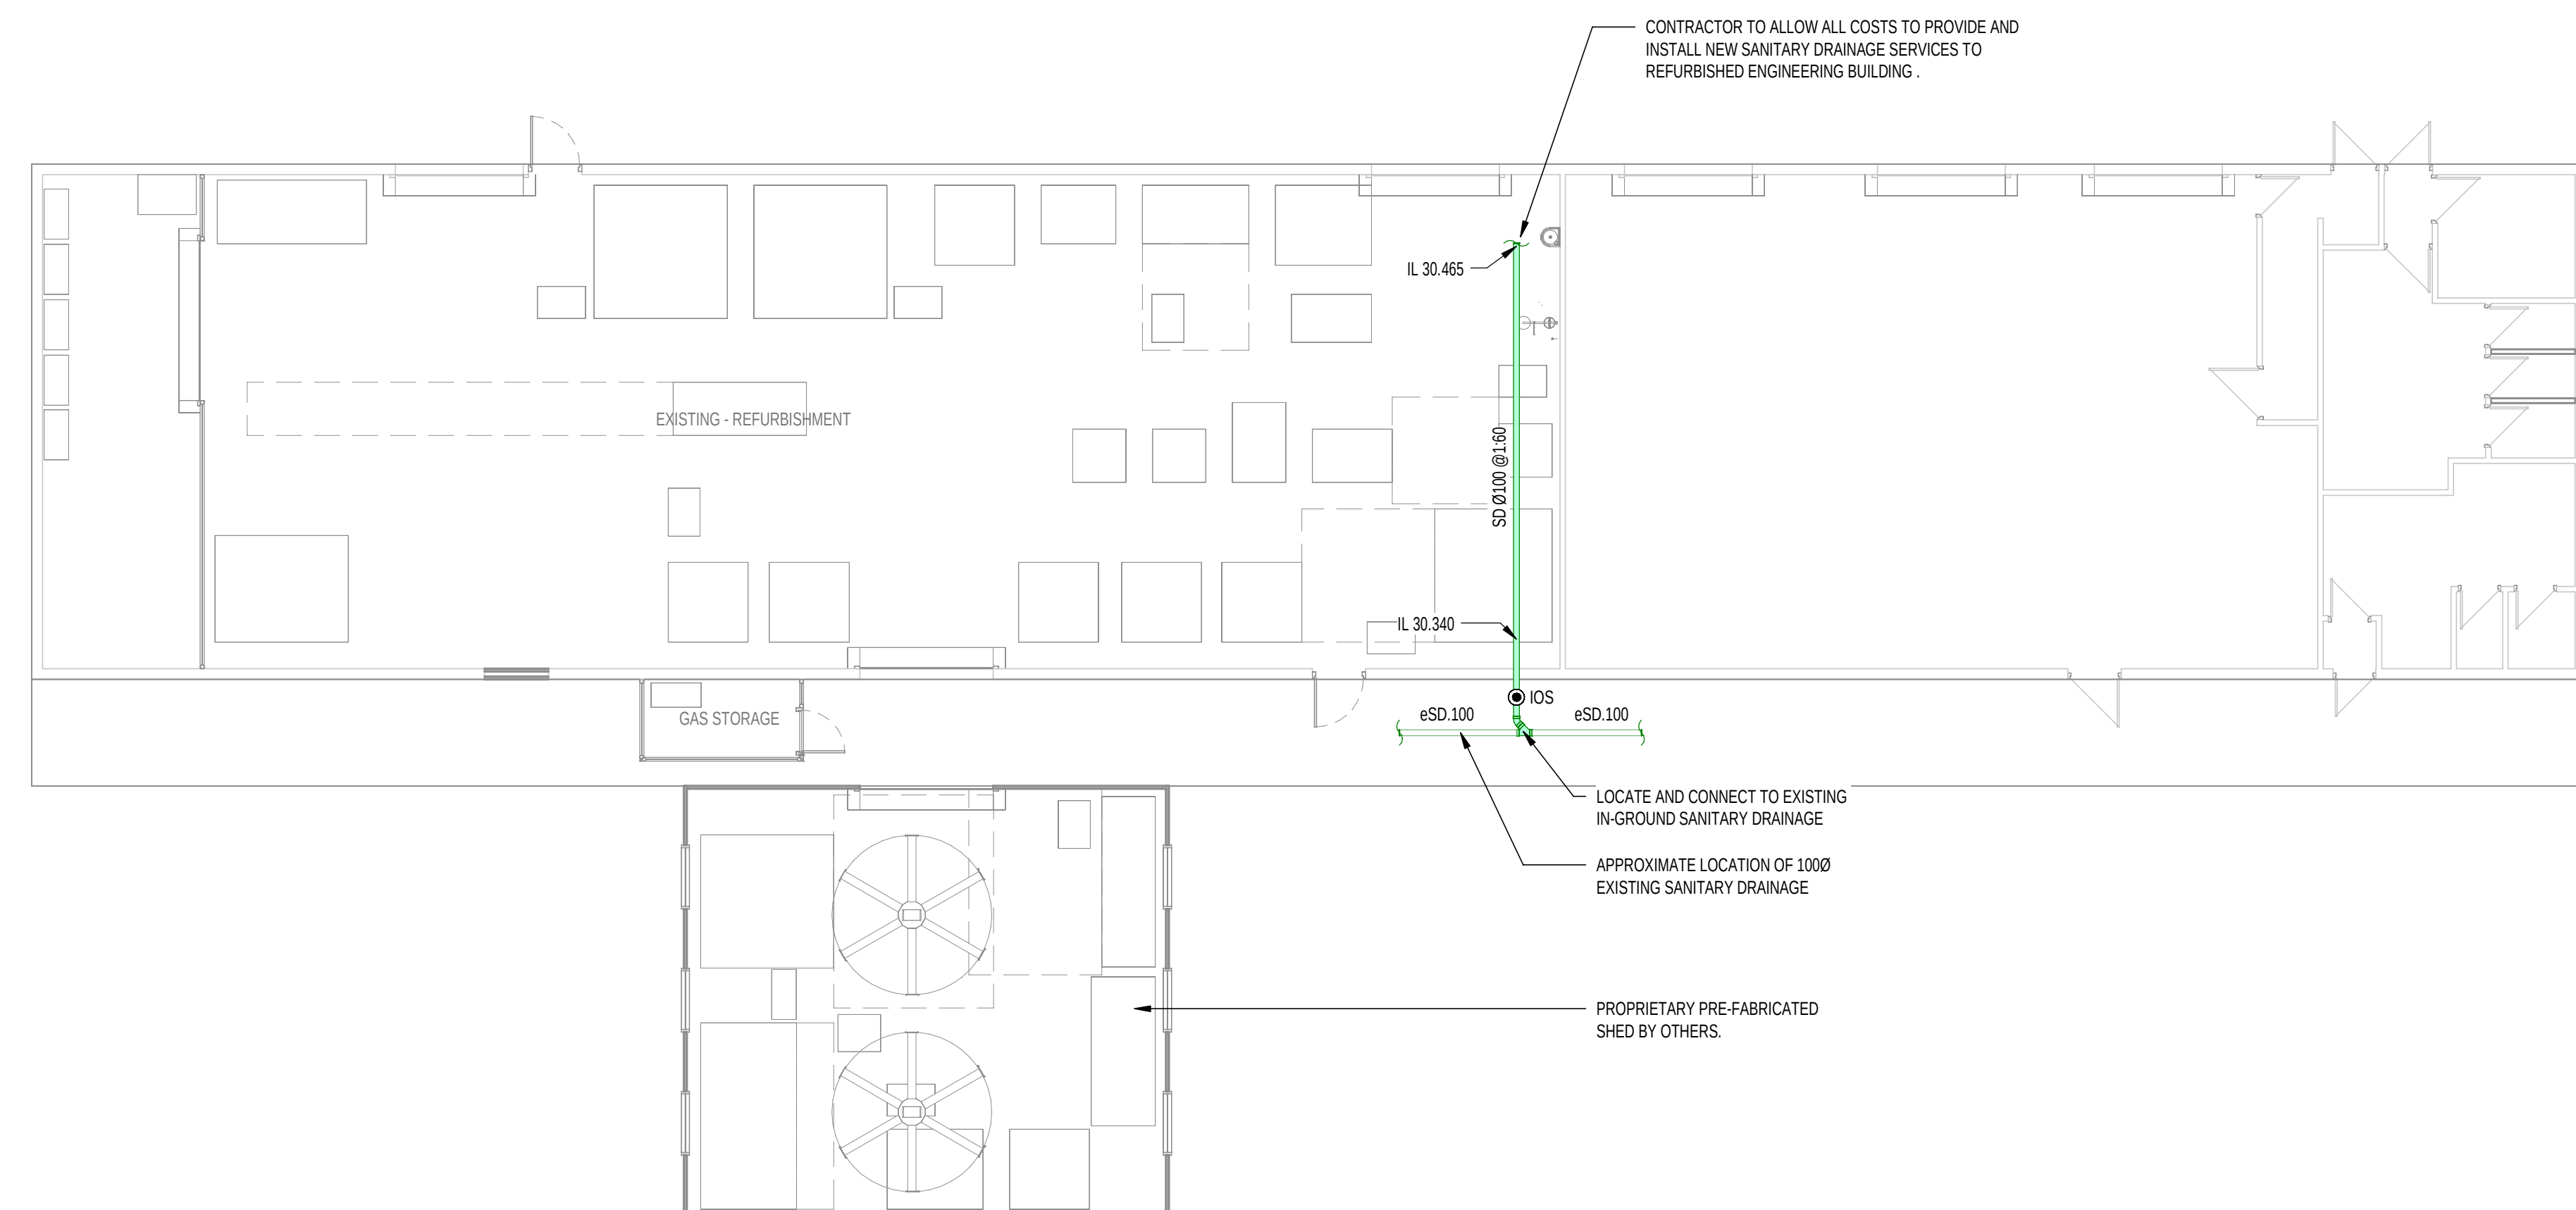

EXISTING SERVICES

SERVICES SHOWN AS EXISTING HAVE BEEN INTERPOLATED FROM RECORD DRAWINGS. CONTRACTOR TO VERIFY LOCATIONS AND LEVELS PRIOR TO COMMENCEMENT OF WORK.

- DRAINAGE NOTES:

1. ALLOW ALL ACCESS TO CONNECT SANITARY DRAINAGE TO ALL FIXTURES AS REQUIRED.
2. CO-ORDINATE ALL FLOOR WASTE LOCATIONS WITH ARCHITECT AND IN COMPLIANCE WITH THE NCC, ASSN6050.1, A3148.1.
3. ALLOW FOR PROVISION OF A JOG IN COMPLIANCE WITH ASSN6050.1 AND TO ALLOW COMPLETE BRAN ACCESS TO ALL DRAIN LINES COLLECTING MULTIPLE FIXTURES.
4. DOCUMENTATION MAY NOT INDICATE ALL VENTING REQUIREMENTS SHALL BE FINISHED DURING FURTHER DEVELOPMENT. VENTING REQUIREMENTS TO BE IN ACCORDANCE WITH ASSN6050.1
5. ALL PENETRATIONS OR CAST THROUGH CONCRETE STRUCTURE ARE TO BE APPROVED BY THE STRUCTURAL ENGINEER.
6. ALLOW FOR DRAINAGE ARTIFICIALITY AS REQUIRED AND SUBMIT TO THE FINAL SITE SLOP CLASSIFICATION IN ACCORDANCE WITH A3148.2
7. VERIFY THAT ALL MECHANICAL DISCHARGES WITH THE PIPEWORK MATERIAL MAXIMUM CONTRACTOR TO PROVIDE WITHOUT DISCHARGING VALUE PRIOR TO DISCHARGE AS REQUIRED.
8. CO-ORDINATE WITH ARCHITECT AND PROVIDE THRESHOLD PROTECTION AT ALL ENTRY POINTS TO THE BUILDING AS REQUIRED TO PREVENT THE INGRESS OF WIND DRIVEN RAIN.

B	12.02.2026	SH	ISSUED FOR D&C TENDER	AA	SM
A	30.01.2026	SH	DRAFT 60% DD ISSUE FOR REVIEW	AA	SM
REV	DATE	BY	DESCRIPTION	CHK	APP

DRAWING STATUS: REGIONAL DEVELOPMENT

DESIGN DEVELOPMENT

WSN

100 Ann Street, Level 12, Fortitude Valley 4006
Tel: +61-7-3854-6200 Fax: +61-7-3854-6500
<http://www.wsp.com>

CQU

THOMSON ADSETT / PEDDLE THORP

PROJECT:

CQU ROCKHAMPTON TAFE CONSOLIDATED

TITLE:

HYDRAULIC SERVICES

ENGINEERING BUILDING - GROUND LEV DRAINAGE LAYOUT

SCALE @ A0:	CHECKED:	APPROVED:
1:100	AA	

PROJECT NUMBER:	DRAWN:	DATE:
PS229518	SH	10/1/01

DRAWING No: _____

ENG-TIT-DR-310-L00-00-00