


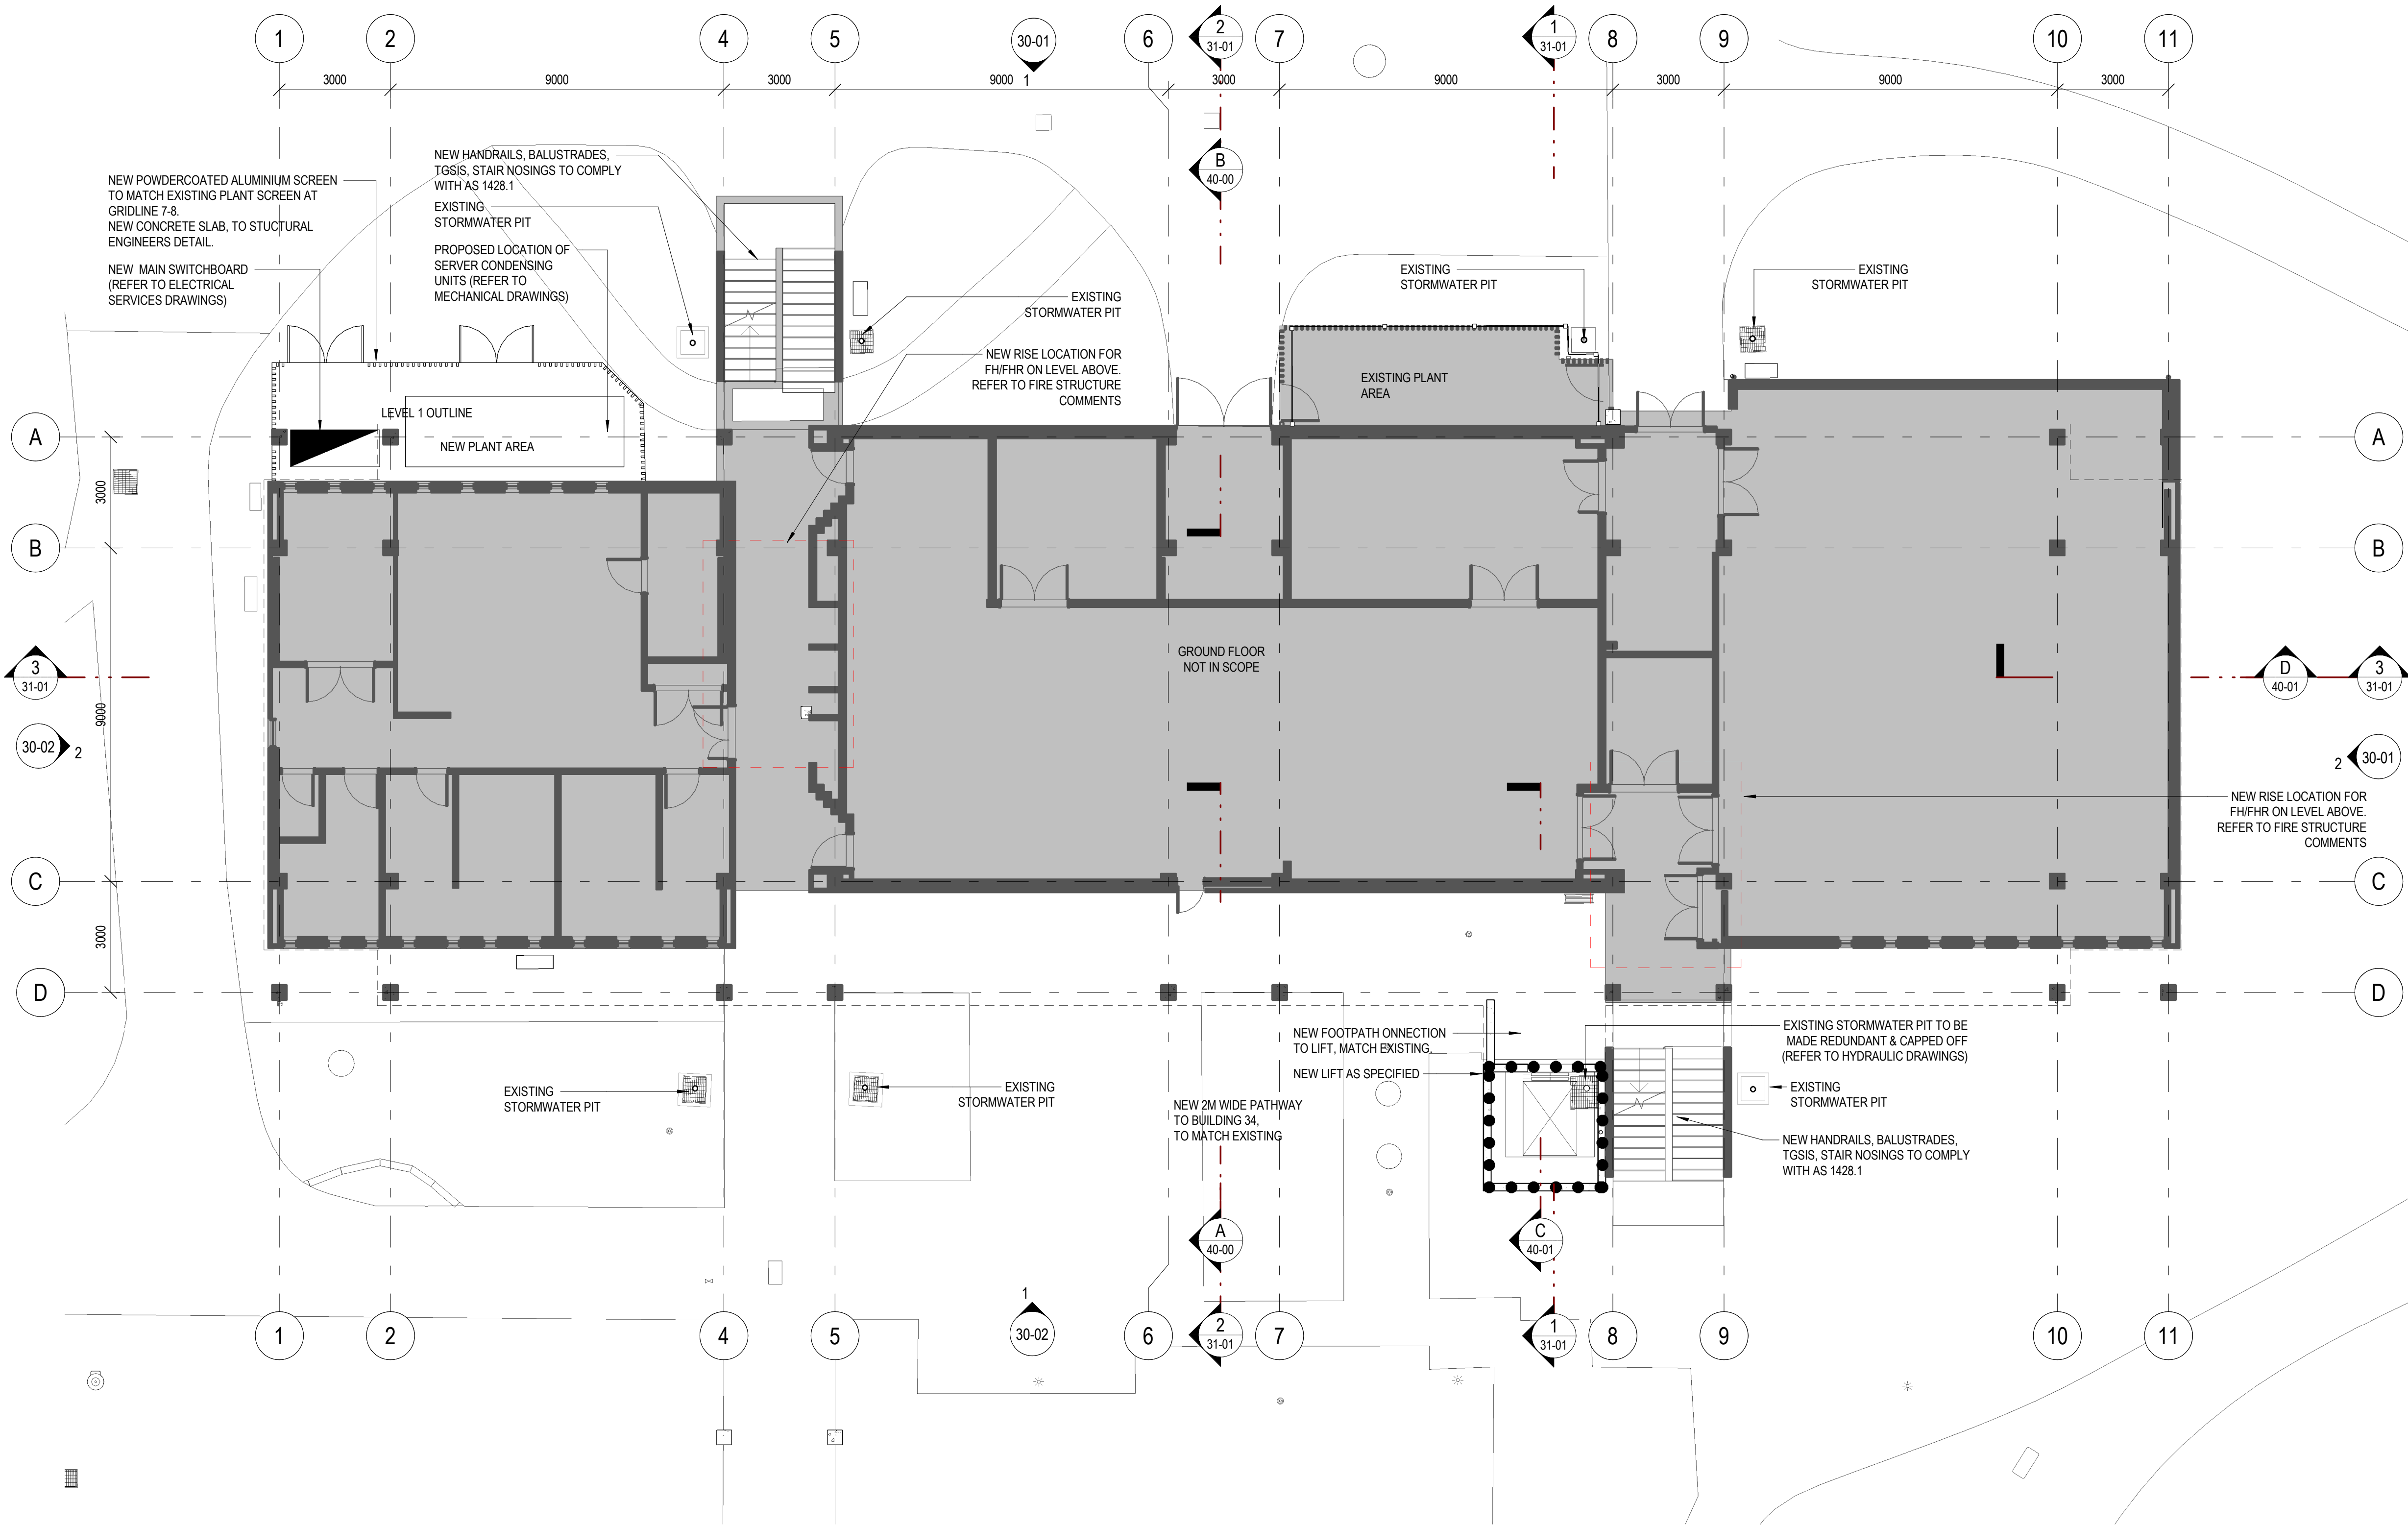

LEGEND	
	OUTSIDE OF SCOPE
	REFER TO CERTIFIER'S COMMENT FOR FRL REQUIREMENT

GENERAL NOTE	
• CONTRACTOR TO CONFIRM EXISTING STRUCTURE & SERVICES ON SITE PRIOR TO BUILDING WORKS. MAKE GOOD AS REQUIRED.	
• REFER TO CQU DESIGN GUIDELINES FOR DESIGN AND CONSTRUCTION REQUIREMENTS.	
• DRAWINGS TO BE READ IN CONJUNCTION WITH SERVICES, CIVIL AND STRUCTURAL DRAWINGS.	
EXTERNAL DETAILS	
• SITE DETAILS SHOWN IN HALF TONE, NOTED FOR REFERENCE ONLY	

ISSUED FOR TENDER

FLOOR PLAN - GROUND - PROPOSED

scale
1 : 100 @ A1

project no.
25.0236.17

revision

B

sheet no.

CQU-ROK-033-01-ARC-21-00

original sheet size - A1 (594mm x 841mm)

thomson
adsett



Telephone +61 7 3840 9999
bne@thomsonadsett.com
Level 9, 470 St Pauls Terrace
Fortitude Valley
Qld 4006 Australia
thomsonadsett.com

© Copyright
These drawings and designs and the copyright thereof are the property of Thomson Adsett Pty Ltd and must not be used, retained or copied without written permission of Thomson Adsett Pty Ltd. ABN 76 105 314 654 Trading as ThomsonAdsett. Dimensions take precedence over scaling. Do not measure off drawings as print sizes may vary

CQU ROCKHAMPTON TAFE CONSOLIDATION - STAGE 2

554/700 Yaamba Rd, Norman
Gardens QLD 4701

for



B	2026-03-05	ISSUED FOR TENDER	BC
A	2026-02-12	ISSUED FOR TENDER	BC
2	2026-01-30	60% DRAFT ISSUE	BC
1	2026-01-23	CONSULTANT ISSUES	BC

rev	date	details	init.

drawn	date
JS/BC	19/01/2026
checked	date
SS	12/02/2026
verified	date

