

**CQU ROCKHAMPTON
TAFE
CONSOLIDATION -
STAGE 2**554/700 Yaamba Rd, Norman
Gardens QLD 4701


for



B	2026-03-05	ISSUED FOR TENDER	BC
A	2026-02-12	ISSUED FOR TENDER	BC
5	2026-01-30	60% DRAFT ISSUE	BC
4	2026-01-23	CONSULTANT ISSUES	BC
3	2025-12-19	UPDATED ISSUE	BC
2	2025-12-15	CONSULTANT ISSUES	BC
1	2025-11-24	50% COSTING ISSUE	PT

rev	date	details	init.
-----	------	---------	-------

drawn	date
JS/BC	19/01/2026
checked	date
SS	12/02/2026
verified	date

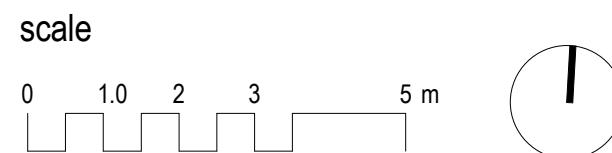**FLOOR PLAN - ROOF -
PROPOSED**scale
1 : 100 @ A1project no.
25.0236.17


revision

B

sheet no.

CQU-ROK-033-RF-ARC-21-03

original sheet size - A1 (594mm x 841mm)

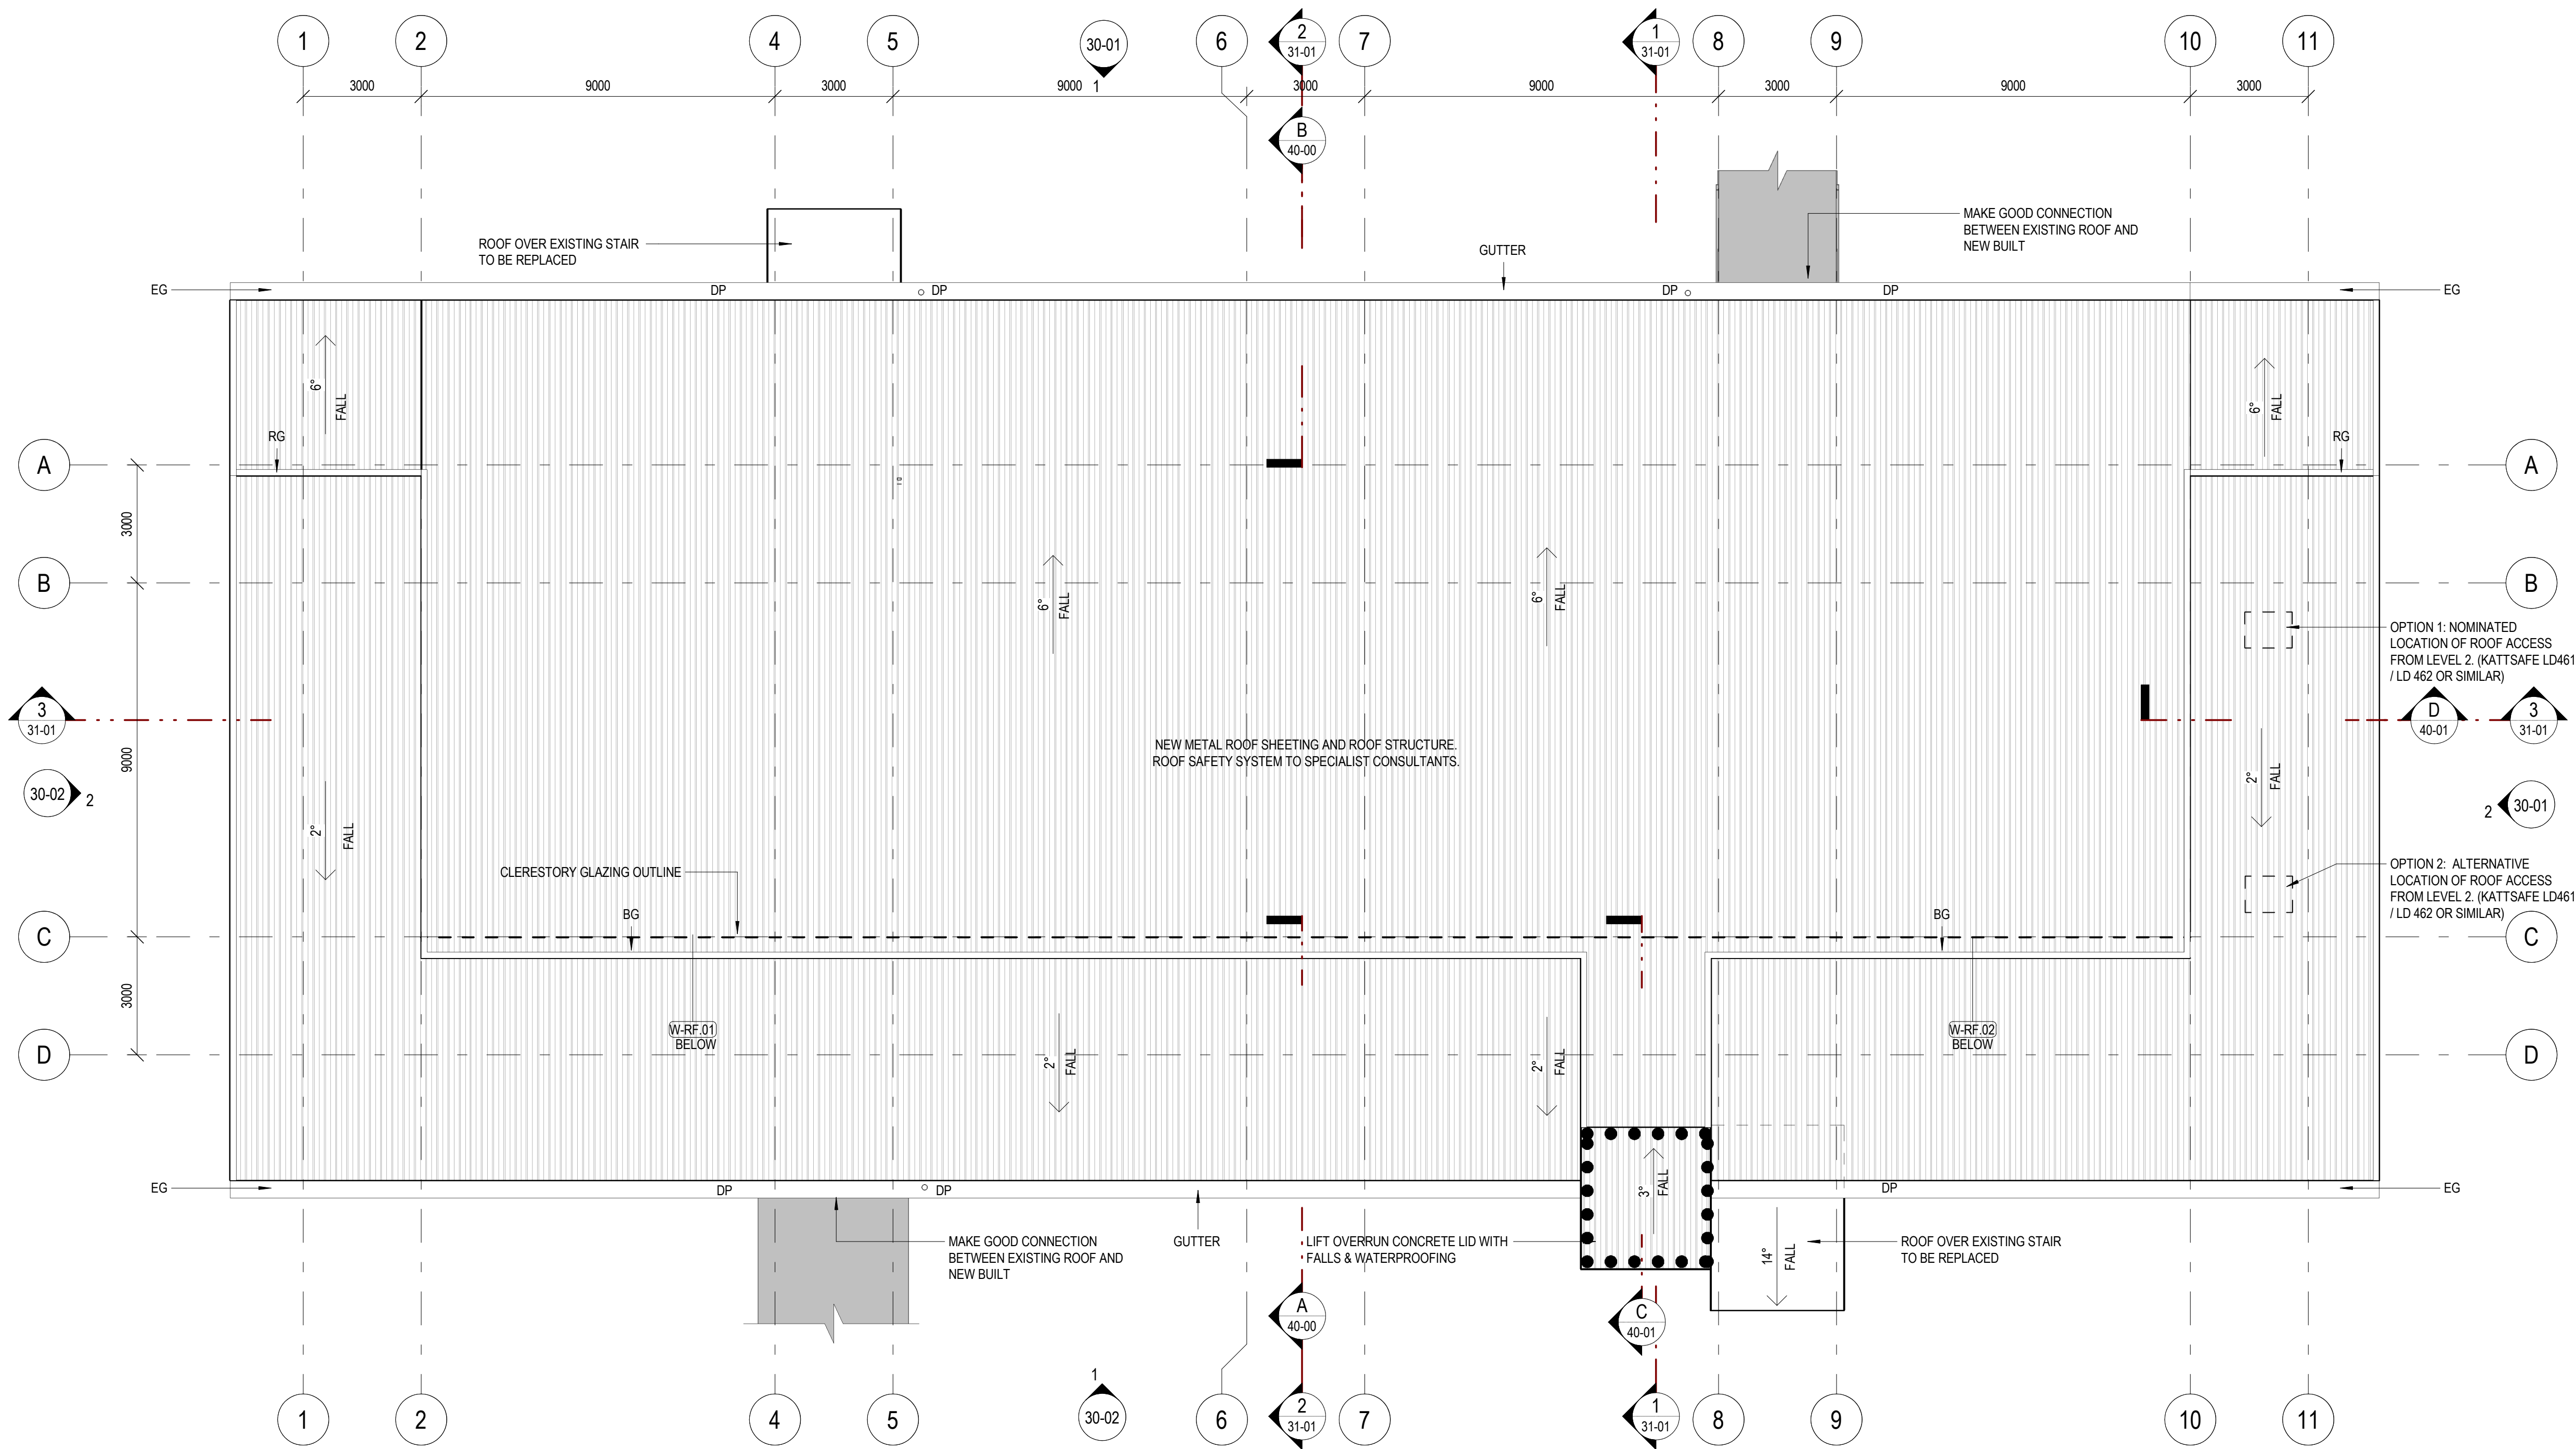

LEGEND	
BG	BARGE CAPPING
EG	EAVES GUTTER
RC	RIDGE CAPPING
DP	DOWNPIPE
● ● ●	REFER TO CERTIFIER'S COMMENT FOR FRL REQUIREMENT

WINDOW SCHEDULE BUILDING 33 - ROOF LEVEL				
NAME	LEVEL	LENGTH	SILL HEIGHT	OVERALL HEIGHT
W-RF.01	ROOF LEVEL	29296	1205	800
W-RF.02	ROOF LEVEL	12000	1205	800

GENERAL NOTE

- CONTRACTOR TO CONFIRM EXISTING STRUCTURE & SERVICES ON SITE PRIOR BUILDING WORKS.
- REFER TO CQU DESIGN GUIDELINES FOR DESIGN AND CONSTRUCTION REQUIREMENTS.
- DRAWINGS TO BE READ IN CONJUNCTION WITH SERVICES, CIVIL AND STRUCTURAL DRAWINGS.
- STRUCTURE
 - CROSS REFERENCE WITH ENGINEERS DRAWINGS FOR STRUCTURAL MEMBER SIZE
- PITCHING HEIGHT
 - REFER TO SECTIONS FOR ROOF PITCHING HEIGHTS
- ROOF SAFETY
 - ROOF ACCESS SYSTEM TO BE DESIGNED AND INSTALLED BY BUILDER. ACCESS TO BE PROVIDED TO GUTTER, SKYLIGHTS & ROOF WINDOWS (CLERESTORY), SOLAR PANELS, ROOF MOUNTED PLANT & ALL PENETRATIONS.

ISSUED FOR TENDER