

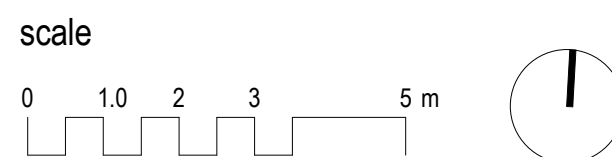
**CQU ROCKHAMPTON
TAFE
CONSOLIDATION -
STAGE 2**554/700 Yaamba Rd, Norman
Gardens QLD 4701

for



B	2026-03-05	ISSUED FOR TENDER	BC
A	2026-02-12	ISSUED FOR TENDER	BC
1	2026-01-30	60% DRAFT ISSUE	BC
rev	date	details	init.

drawn	date
JS/BC	19/01/2026
checked	date
SS	12/02/2026
verified	date

**PARTITION PLAN - LEVEL 1**scale
As indicated @ A1project no.
25.0236.17

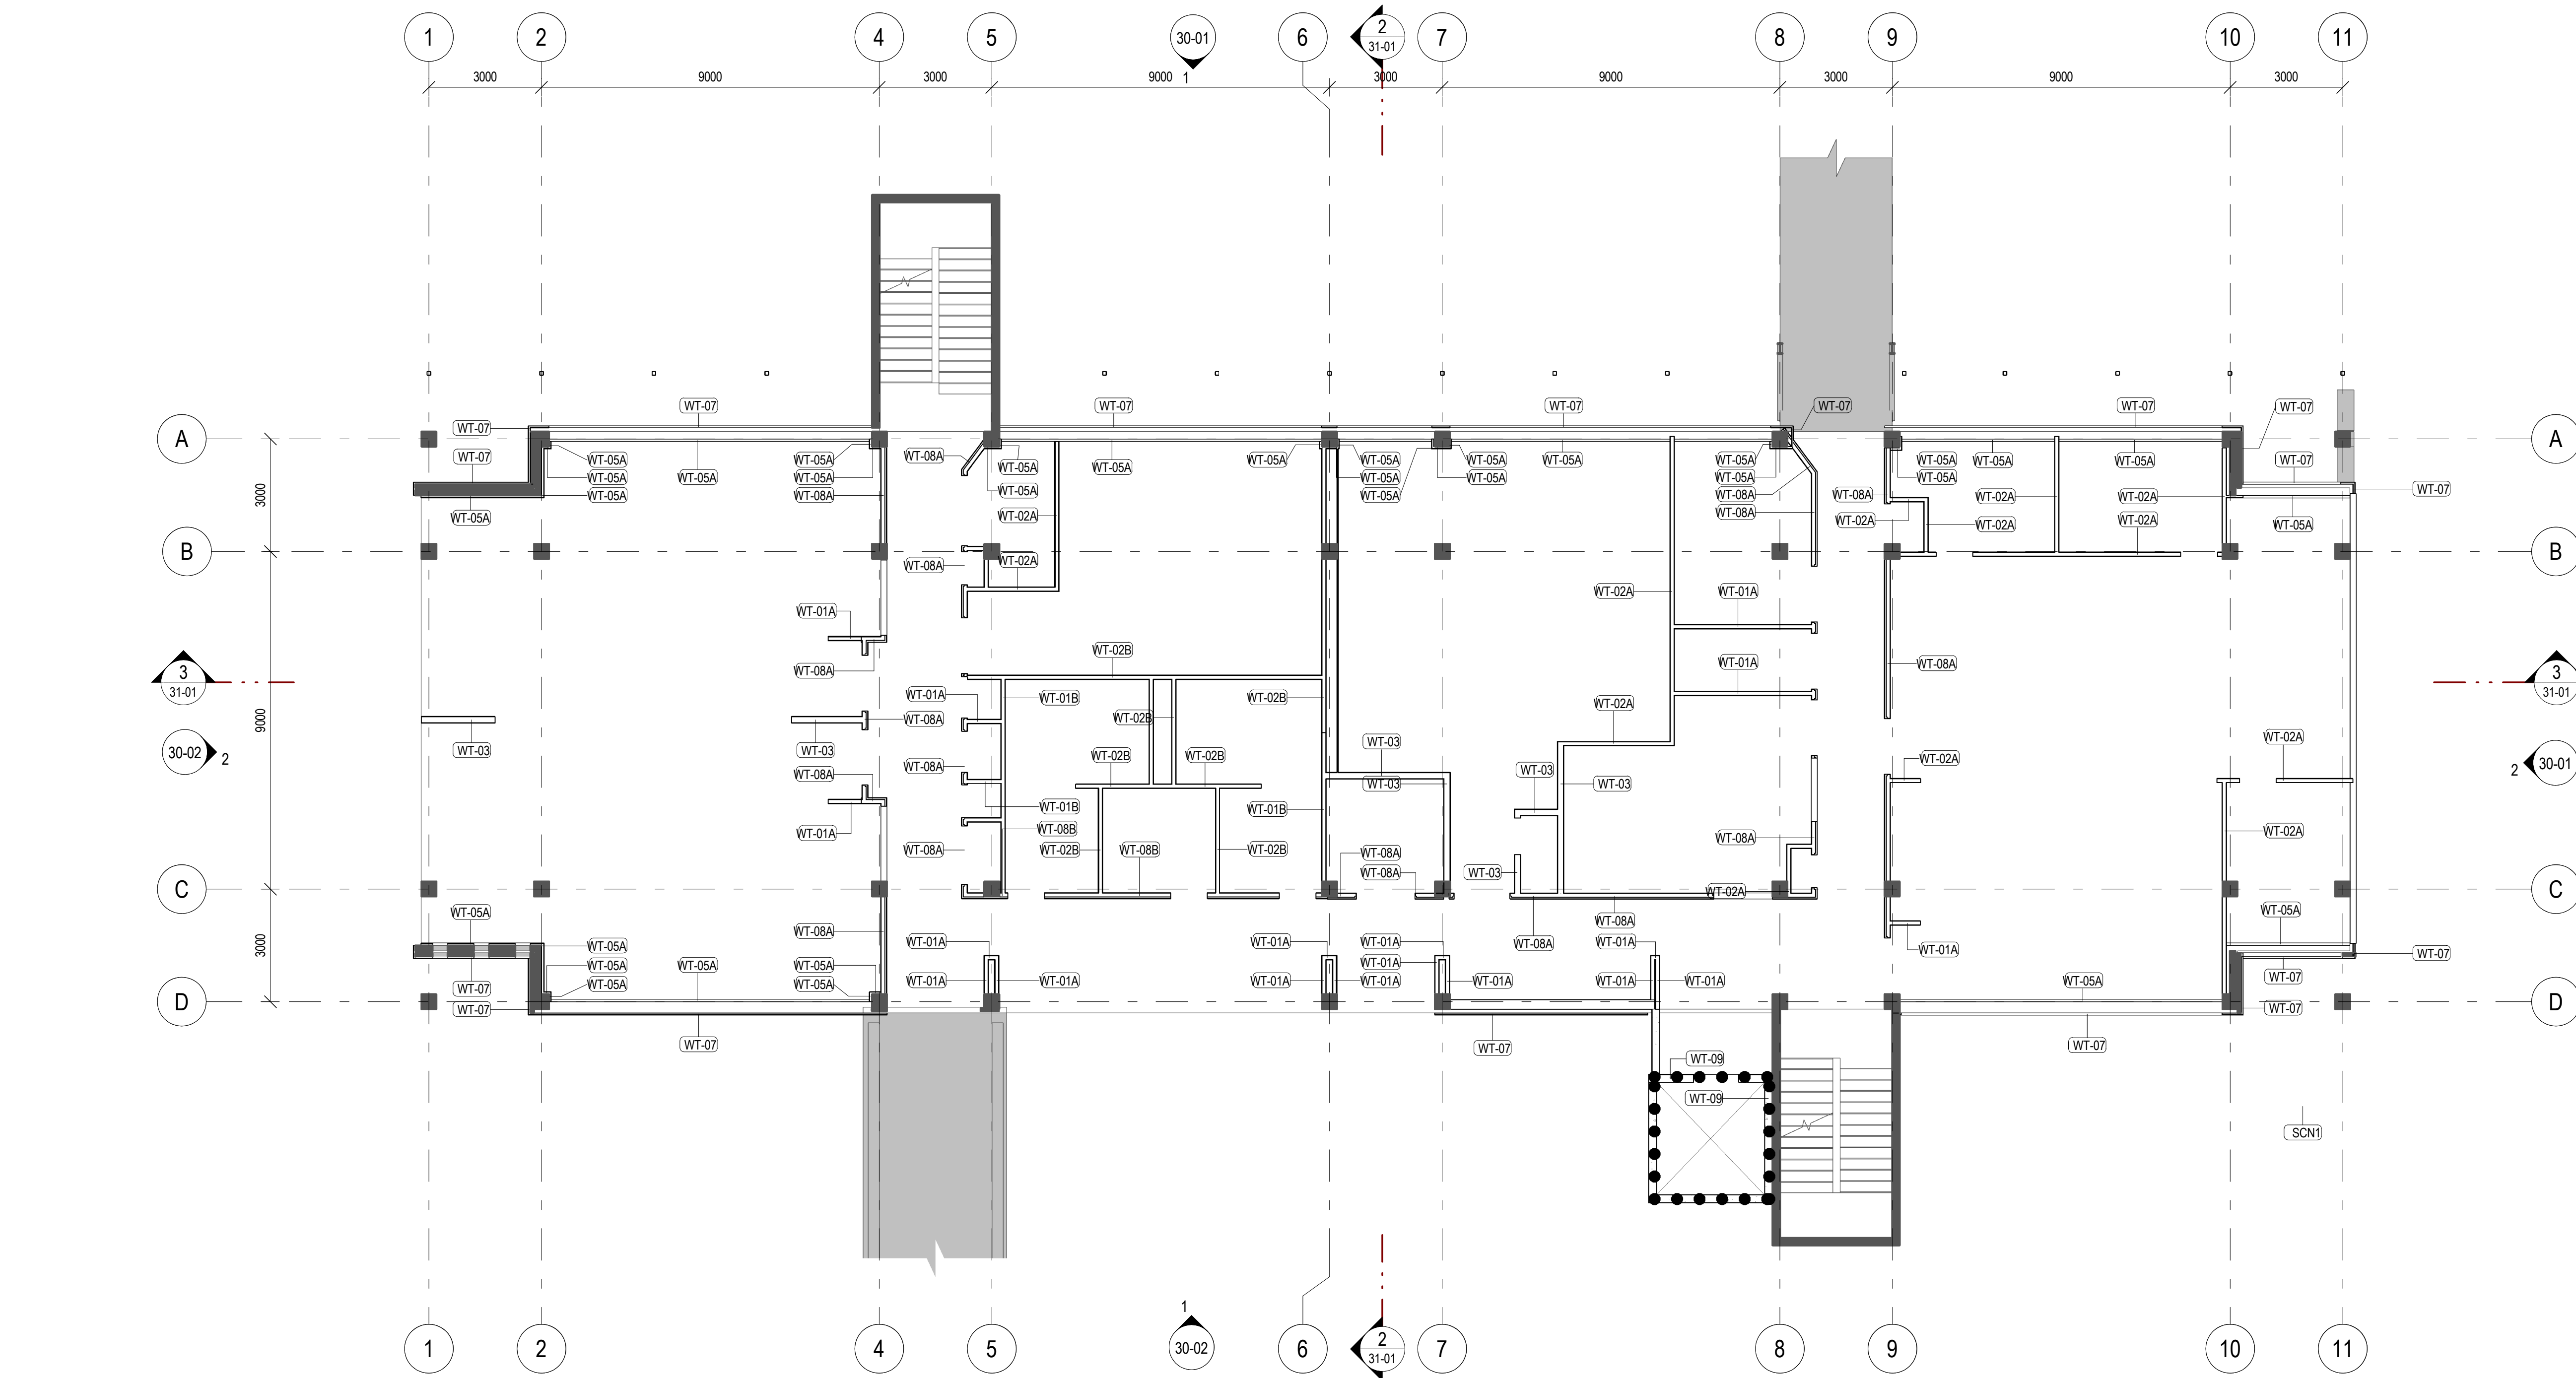
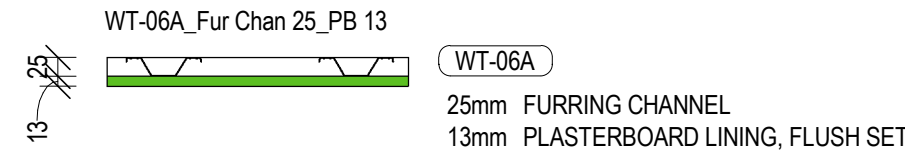
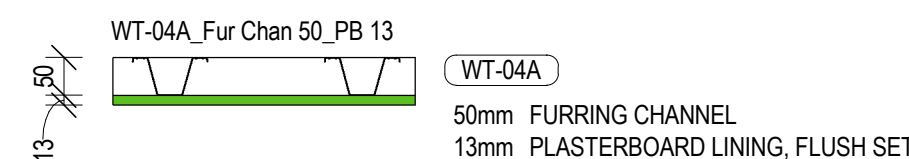
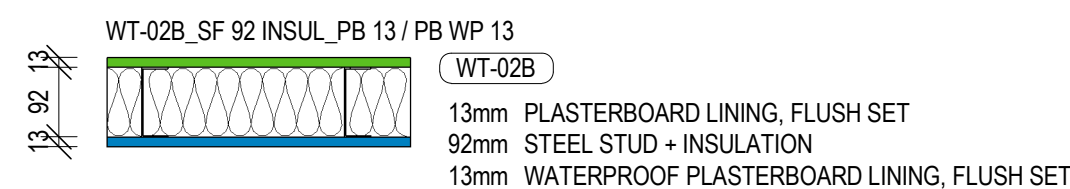
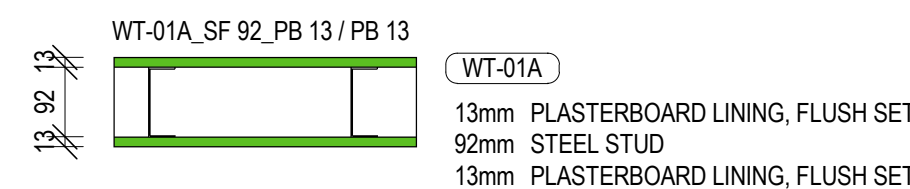
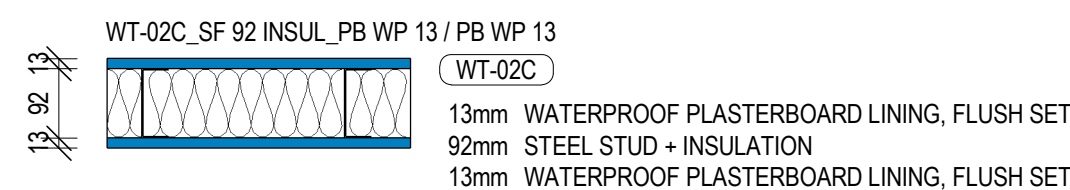
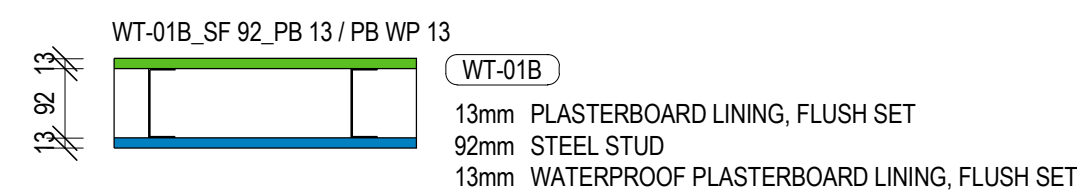
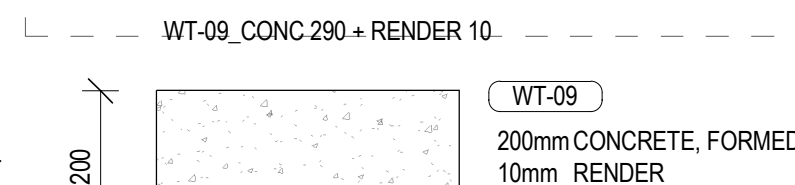
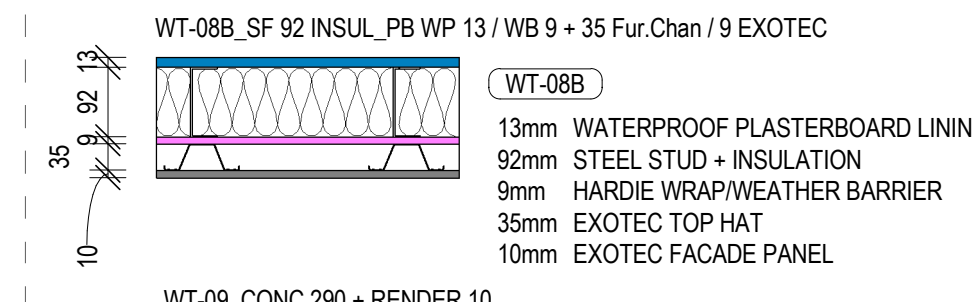
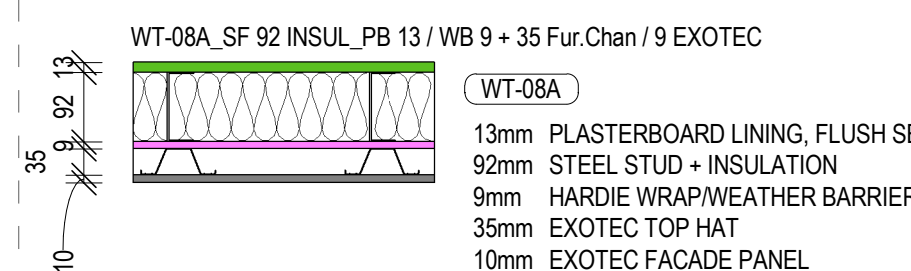
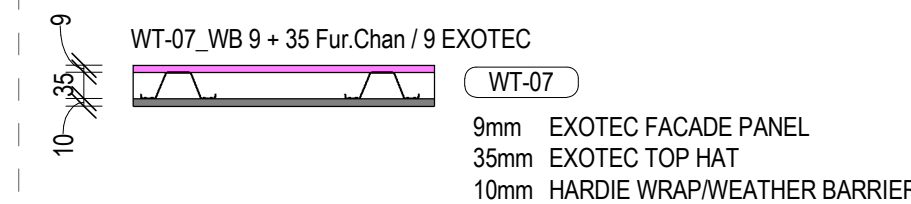
revision

B

sheet no.

CQU-ROK-033-01-ARC-25-01

original sheet size - A1 (594mm x 841mm)

**WALL TYPES LEGEND****EXTERNAL WALL LINING****EXTERNAL WALL LINING****INSULATION NOTES**

- COMPLY WITH ACOUSTIC REPORT TO ACHIEVE THE NOMINATED ACOUSTIC RATING AND SECTION J REPORT FOR THE REQUIRED EXTERNAL WALLS R VALUES.
- COMPLY WITH THE CQU DESIGN GUIDELINES FOR MINIMUM ACOUSTIC SEPARATION BETWEEN ROOMS. WHERE THE ACOUSTIC REPORT NOMINATES HIGHER PERFORMANCE REQUIREMENTS, THE HIGHER RW RATINGS ARE TO APPLY.
- NEW STUD TO GO UP TO UNDERSIDE OF SLAB, UNLESS SPECIFIED.

ISSUED FOR TENDER