

554/700 Yaamba Rd, Norman
Gardens QLD 4701



drawn	date
JS/BC	19/01/2020
checked	date
SS	12/02/2020
verified	date


PARTITION PLAN - LEVEL 2

B

sheet no.

CQU-ROK-033-02-ARC-25-02

original sheet size - A1 (594mm x 841mm)

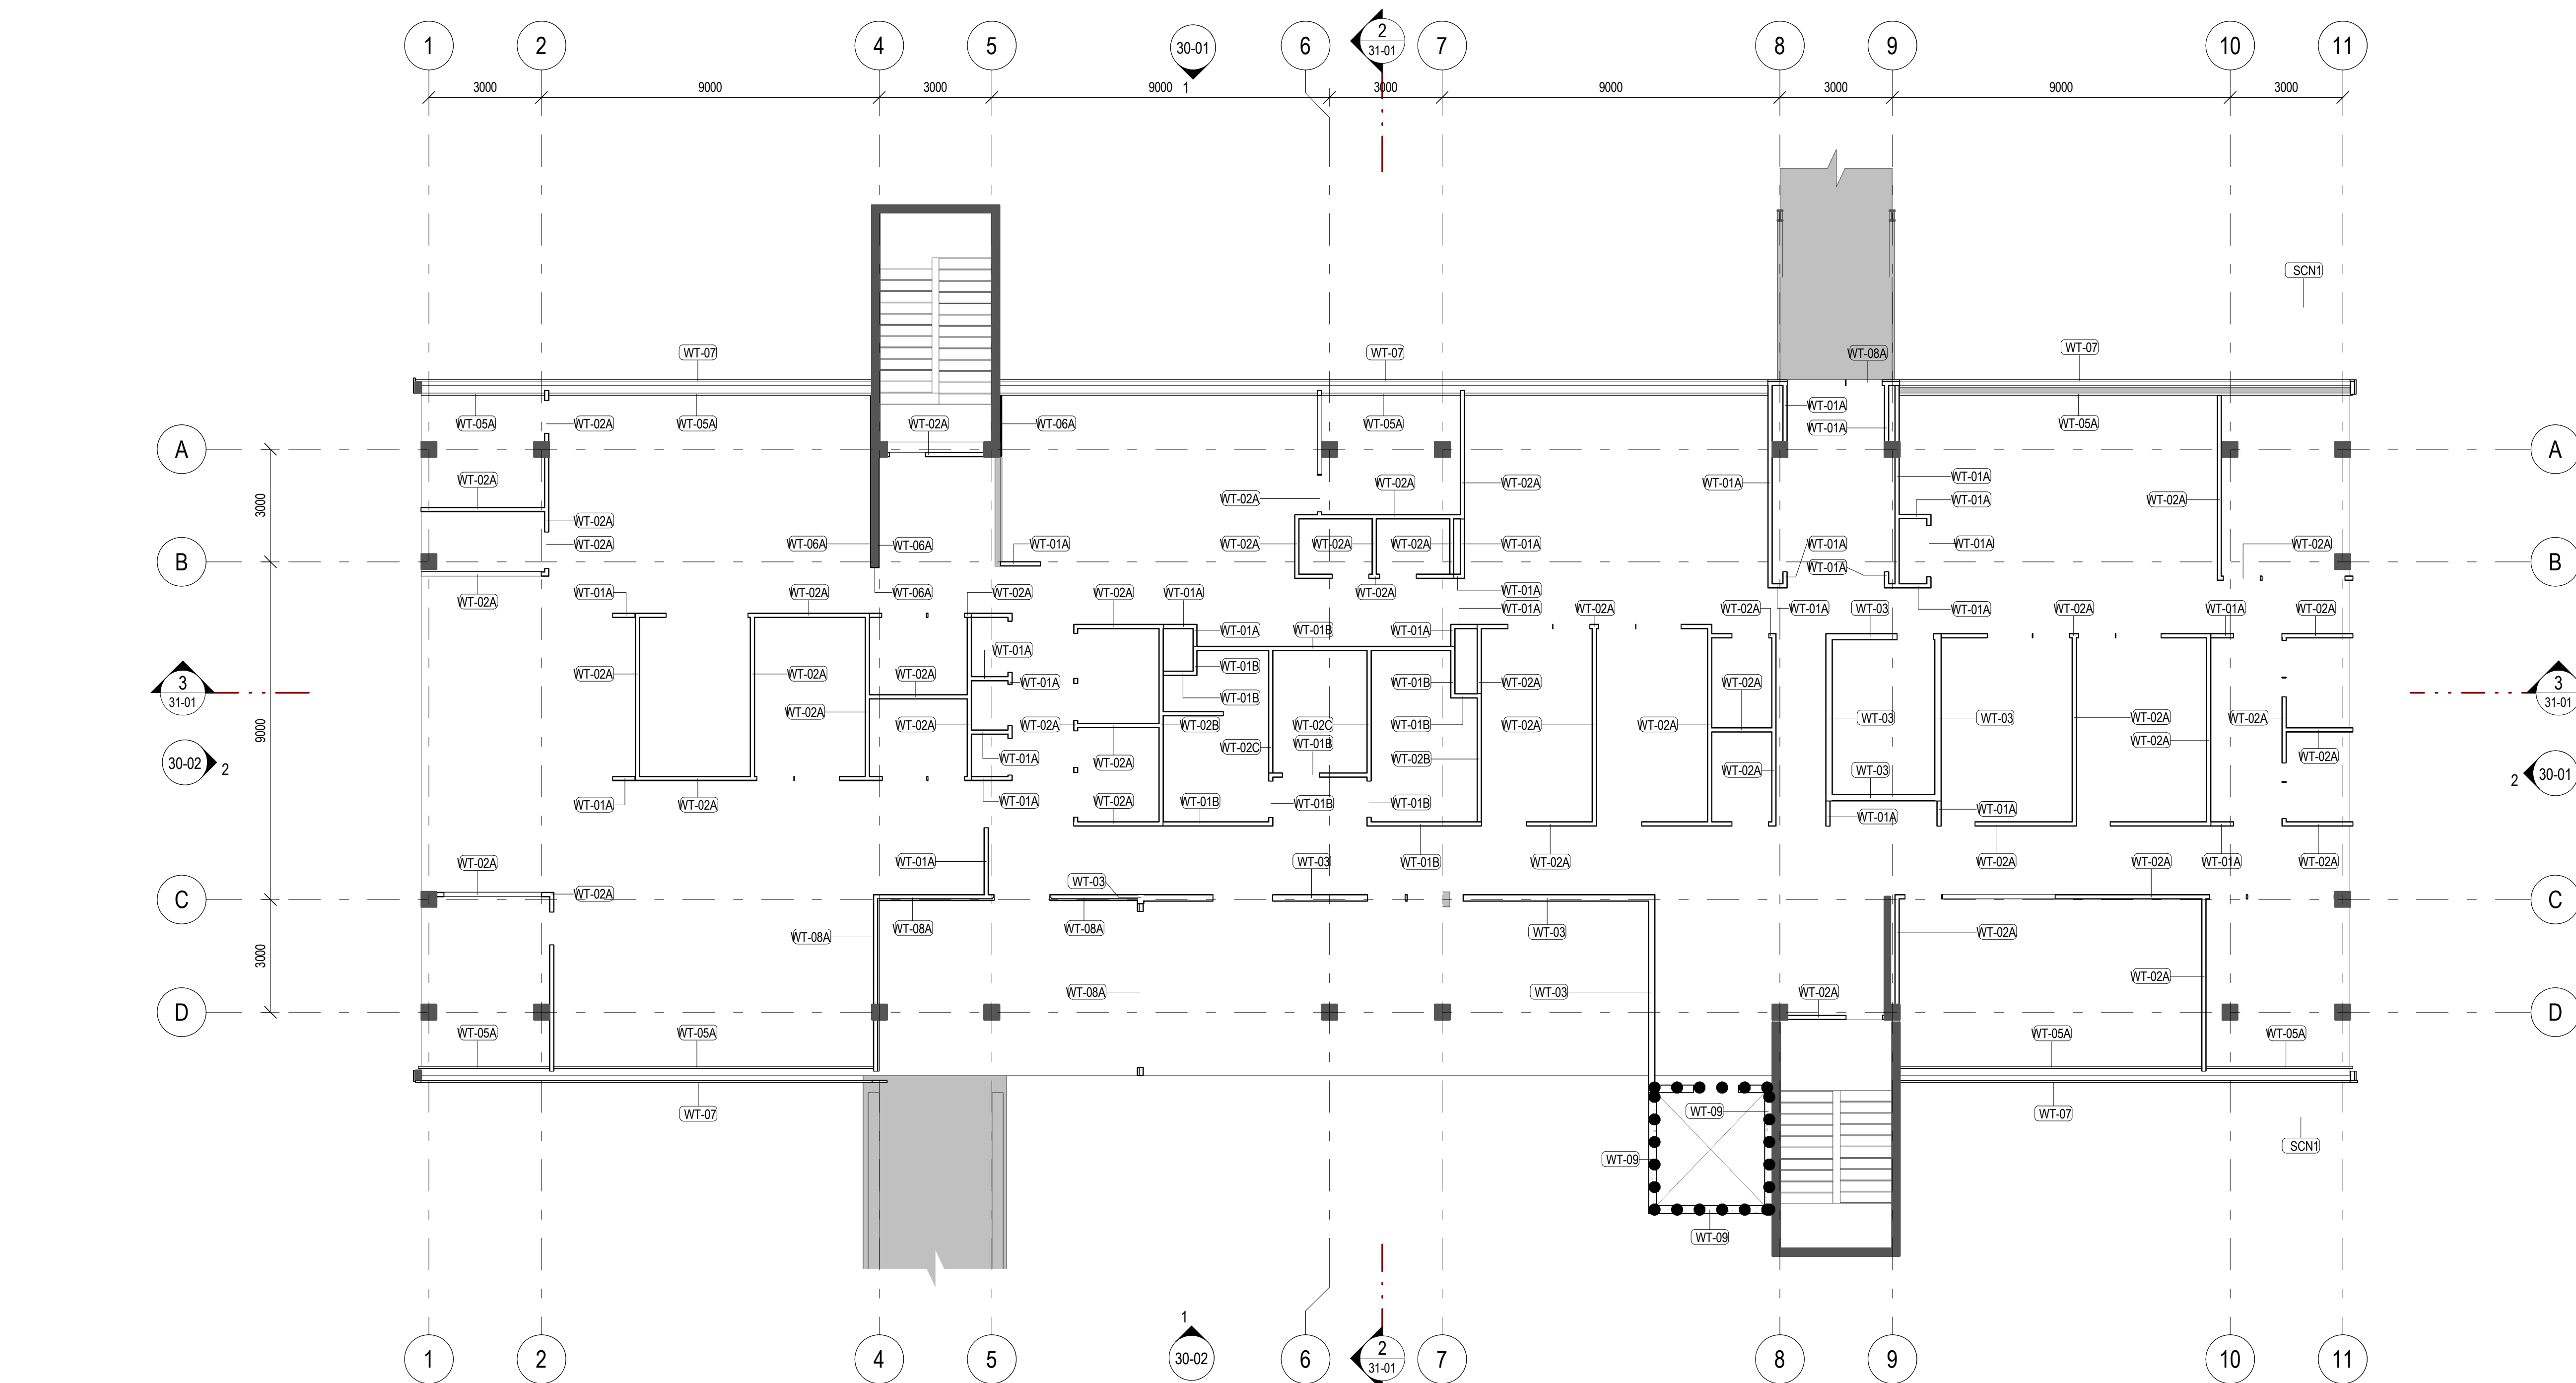

WT-01A_SF 92_PB 13 / PB 13

WT-01A

- 13mm PLASTERBOARD LINING, FLUSH SET
- 92mm STEEL STUD
- 13mm PLASTERBOARD LINING, FLUSH SET

WT-01B_SF 92_PB 13 / PB WP 13

WT-01B

- 13mm PLASTERBOARD LINING, FLUSH SET
- 92mm STEEL STUD
- 13mm WATERPROOF PLASTERBOARD LINING, FLUSH SET

WT-01C_SF 92_PB WP 13 / PB WP 13





WT-01C

- 13mm WATERPROOF PLASTERBOARD LINING, FLUSH SET
- 92mm STEEL STUD
- 13mm WATERPROOF PLASTERBOARD LINING, FLUSH SET

WT-02A_SF 92_INSUL_PB 13 / PB 13

WT-02A

- 13mm PLASTERBOARD LINING, FLUSH SET
- 92mm STEEL STUD + INSULATION
- 13mm PLASTERBOARD LINING, FLUSH SET

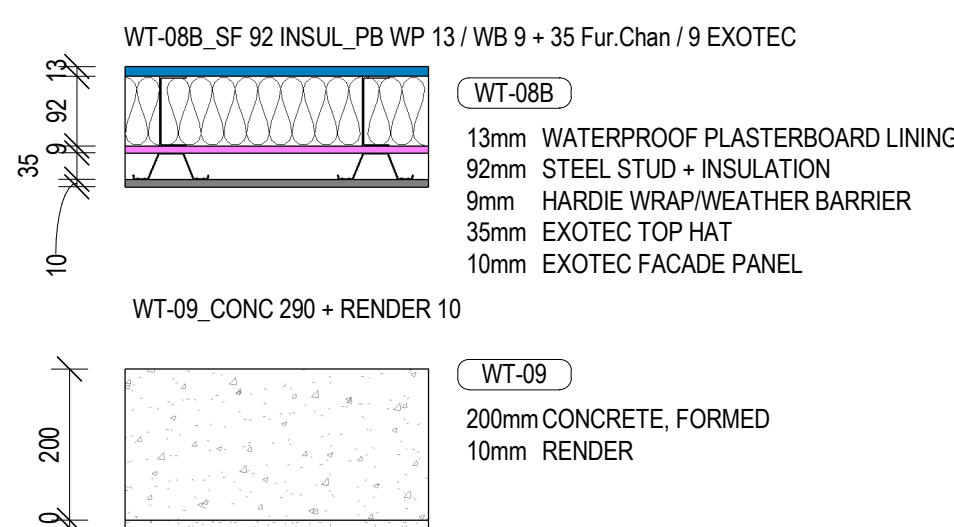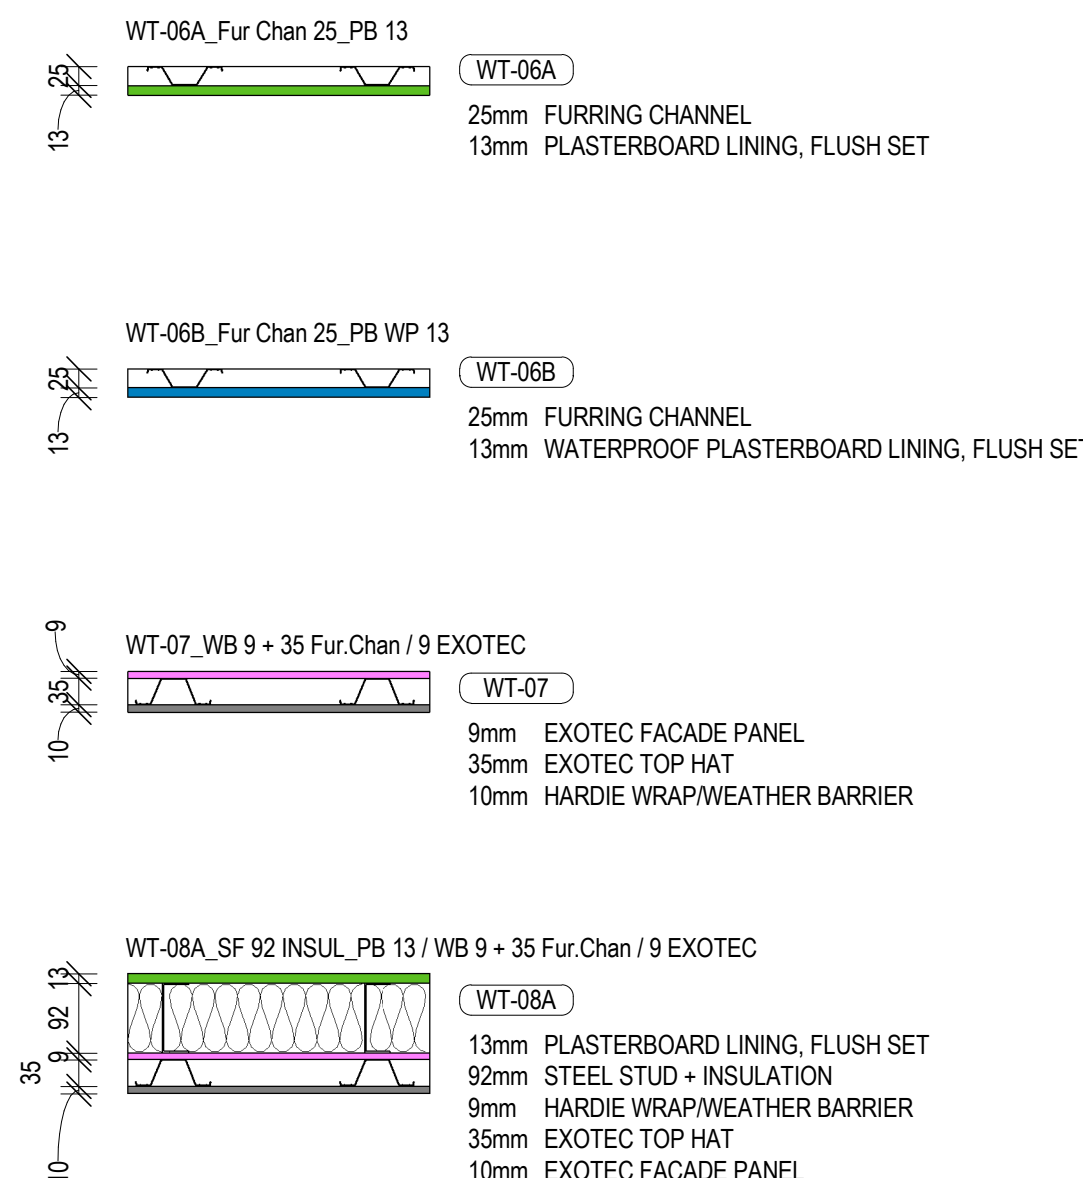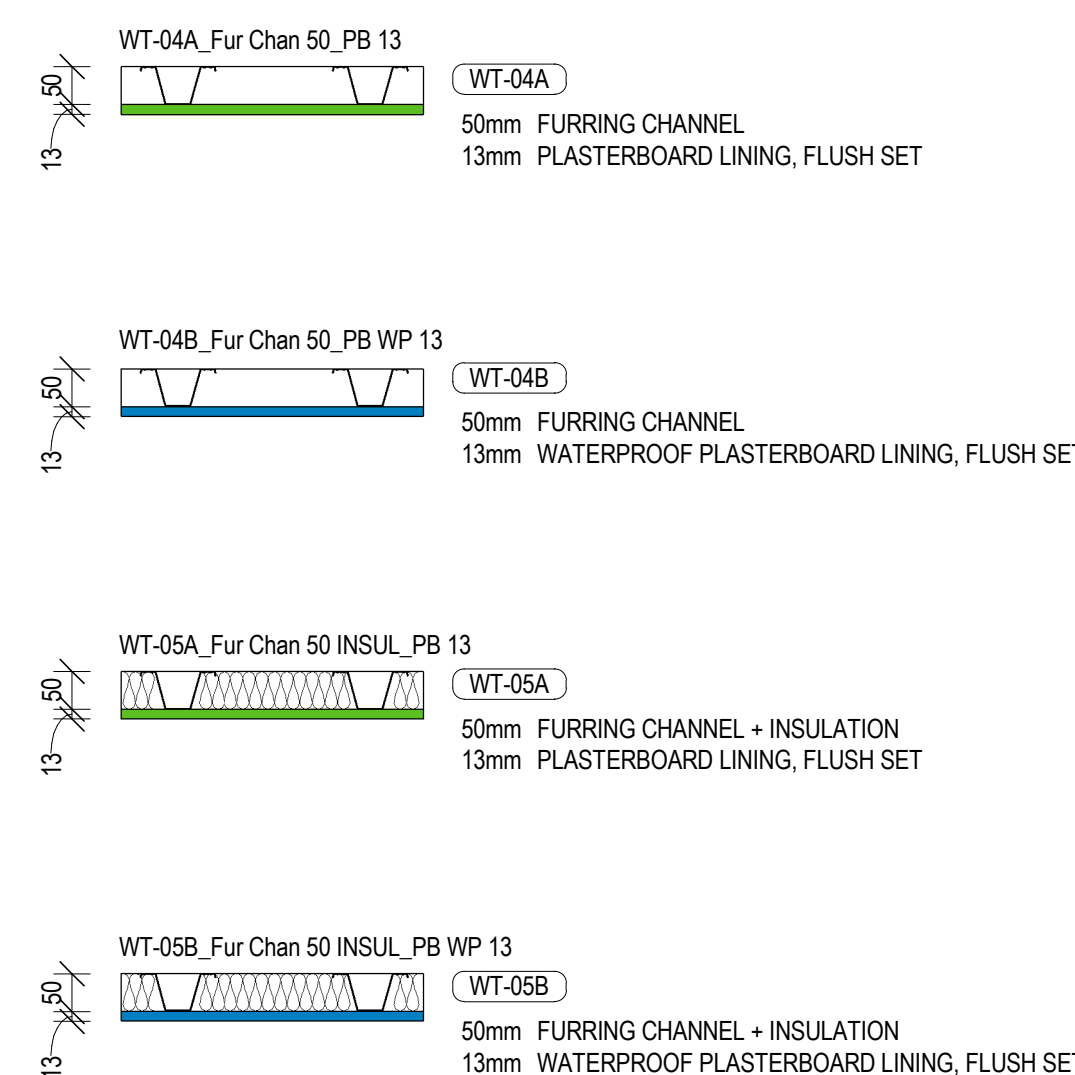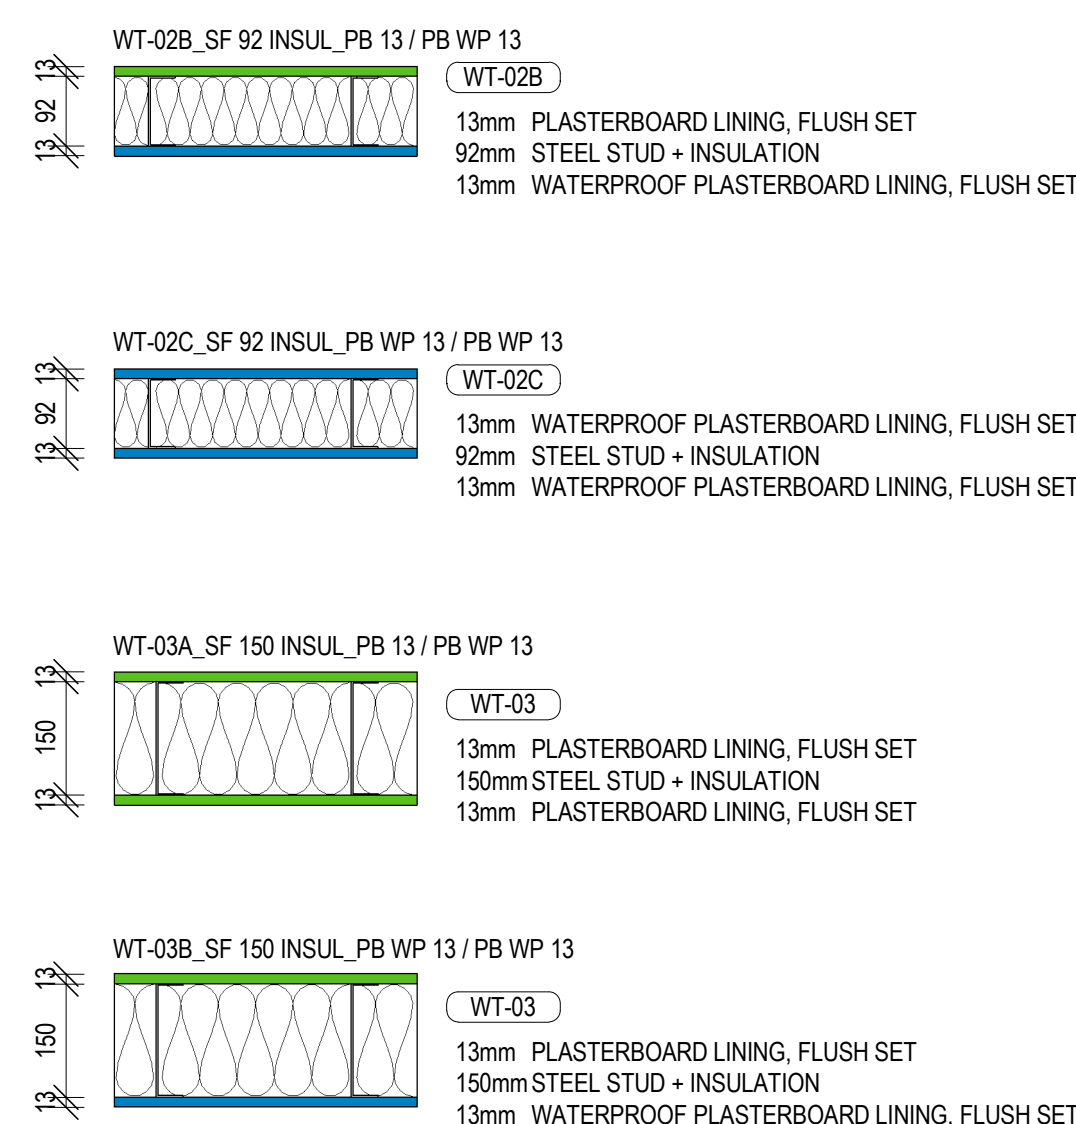

- COMPLY WITH ACOUSTIC REPORT TO ACHIEVE THE NOMINATED ACOUSTIC RATING AND SECTION J REPORT FOR THE REQUIRED EXTERNAL WALLS R VALUES.
- COMPLY WITH THE CQU DESIGN GUIDELINES FOR MINIMUM ACOUSTIC SEPARATION BETWEEN ROOMS. WHERE THE ACOUSTIC REPORT NOMINATES HIGHER PERFORMANCE REQUIREMENTS, THE HIGHER RW RATINGS ARE TO APPLY.
- NEW STUD TO GO UP TO UNDERSIDE OF SLAB, UNLESS SPECIFIED.