


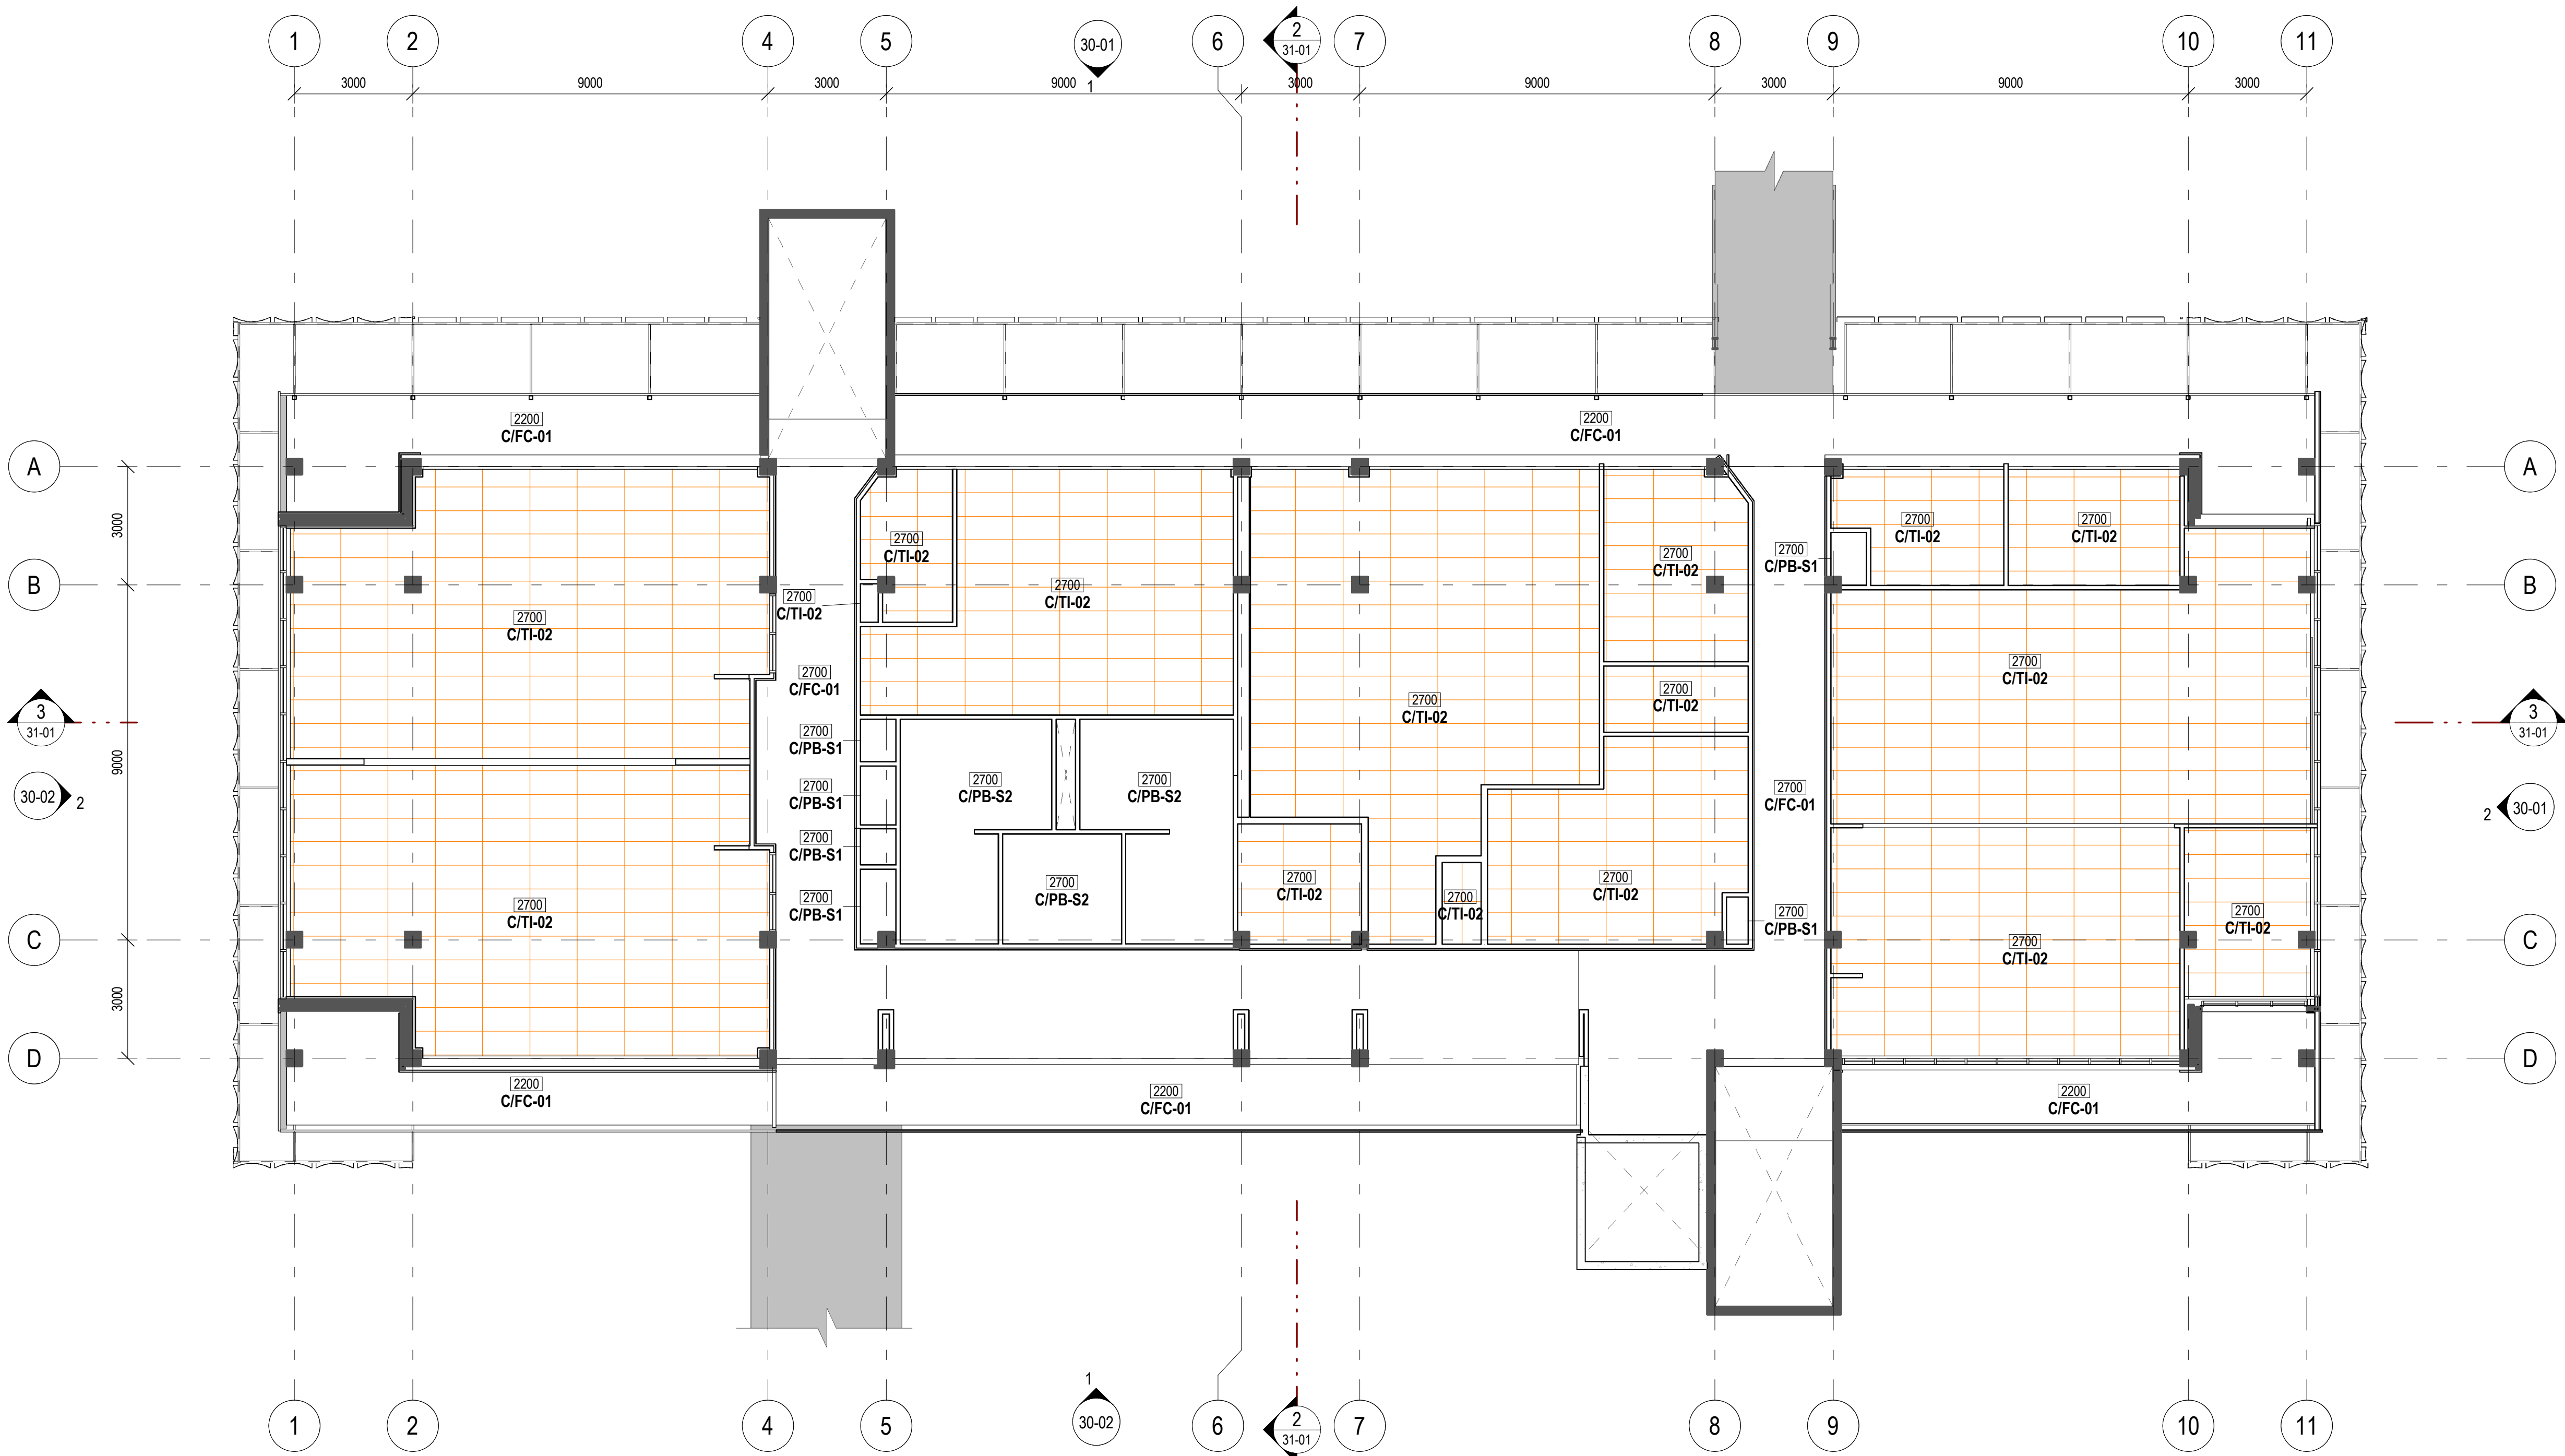

CEILING LEGEND	
2700	CEILING HEIGHT ABOVE FFL
CT1	CEILING FINISHES
CEILING LEGEND	
C/TI-01	1200x600 CEILING TILES
C/TI-02	1200x600 ACOUSTIC CEILING TILES
C/PB-S1	FLUSH SET PLASTERBOARD SHEETING
C/PB-S2	WATERPROOF PLASTERBOARD SHEETING
C/FC-01	FLUSH SET FIBRE CEMENT SHEETING

GENERAL NOTES	
• CONTRACTOR TO CONFIRM EXISTING STRUCTURE & SERVICES ON SITE PRIOR BUILDING WORKS.	
• ALL REFLECTED CEILING PLANS ARE TO BE READ IN CONJUNCTION WITH SERVICE ENGINEERING DRAWINGS FOR MECHANICAL, FIRE, ELECTRICAL AND ALIKE.	
• CEILING REQUIREMENTS TO BE IN ACCORDANCE WITH CQU DESIGN GUIDELINES	
• REFER TO OUTLINE SPECIFICATION & SCHEDULE FOR FF&E AND FINISHES	
• SETOUT OF CEILING TILES TO BE CONFIRMED	

ISSUED FOR TENDER

CEILING PLAN - LEVEL 1 PROPOSED

scale
1 : 100 @ A1

revision
B

sheet no.
CQU-ROK-033-01-ARC-26-01

original sheet size - A1 (594mm x 841mm)

thomson
adsett



Telephone +61 7 3840 9999
bne@thomsonadsett.com
Level 9, 470 St Pauls Terrace
Fortitude Valley
Qld 4006 Australia
thomsonadsett.com

© Copyright
These drawings and designs and the copyright thereof are the property of Thomson Adsett Pty Ltd and must not be used, retained or copied without written permission of Thomson Adsett Pty Ltd. ABN 76 105 314 654 Trading as ThomsonAdsett. Dimensions take precedence over scaling. Do not measure off drawings as print sizes may vary

CQU ROCKHAMPTON TAFE CONSOLIDATION - STAGE 2

554/700 Yaamba Rd, Norman Gardens QLD 4701




B	2026-03-05	ISSUED FOR TENDER	BC
A	2026-02-12	ISSUED FOR TENDER	BC
5	2026-01-30	60% DRAFT ISSUE	BC
4	2026-01-23	CONSULTANT ISSUES	BC
3	2025-12-19	UPDATED ISSUE	BC
2	2025-12-15	CONSULTANT ISSUES	BC
1	2025-11-24	50% COSTING ISSUE	PT

rev	date	details	init.
-----	------	---------	-------

drawn	date
JS/BC	19/01/2026

checked	date
SS	12/02/2026

verified	date
----------	------

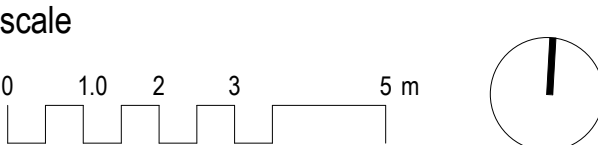

5/03/2026 12:30:55 PM Autodesk Docs://CQU ROK TAFE25 0236 17 CQU BLDG-33_2025.rvt