


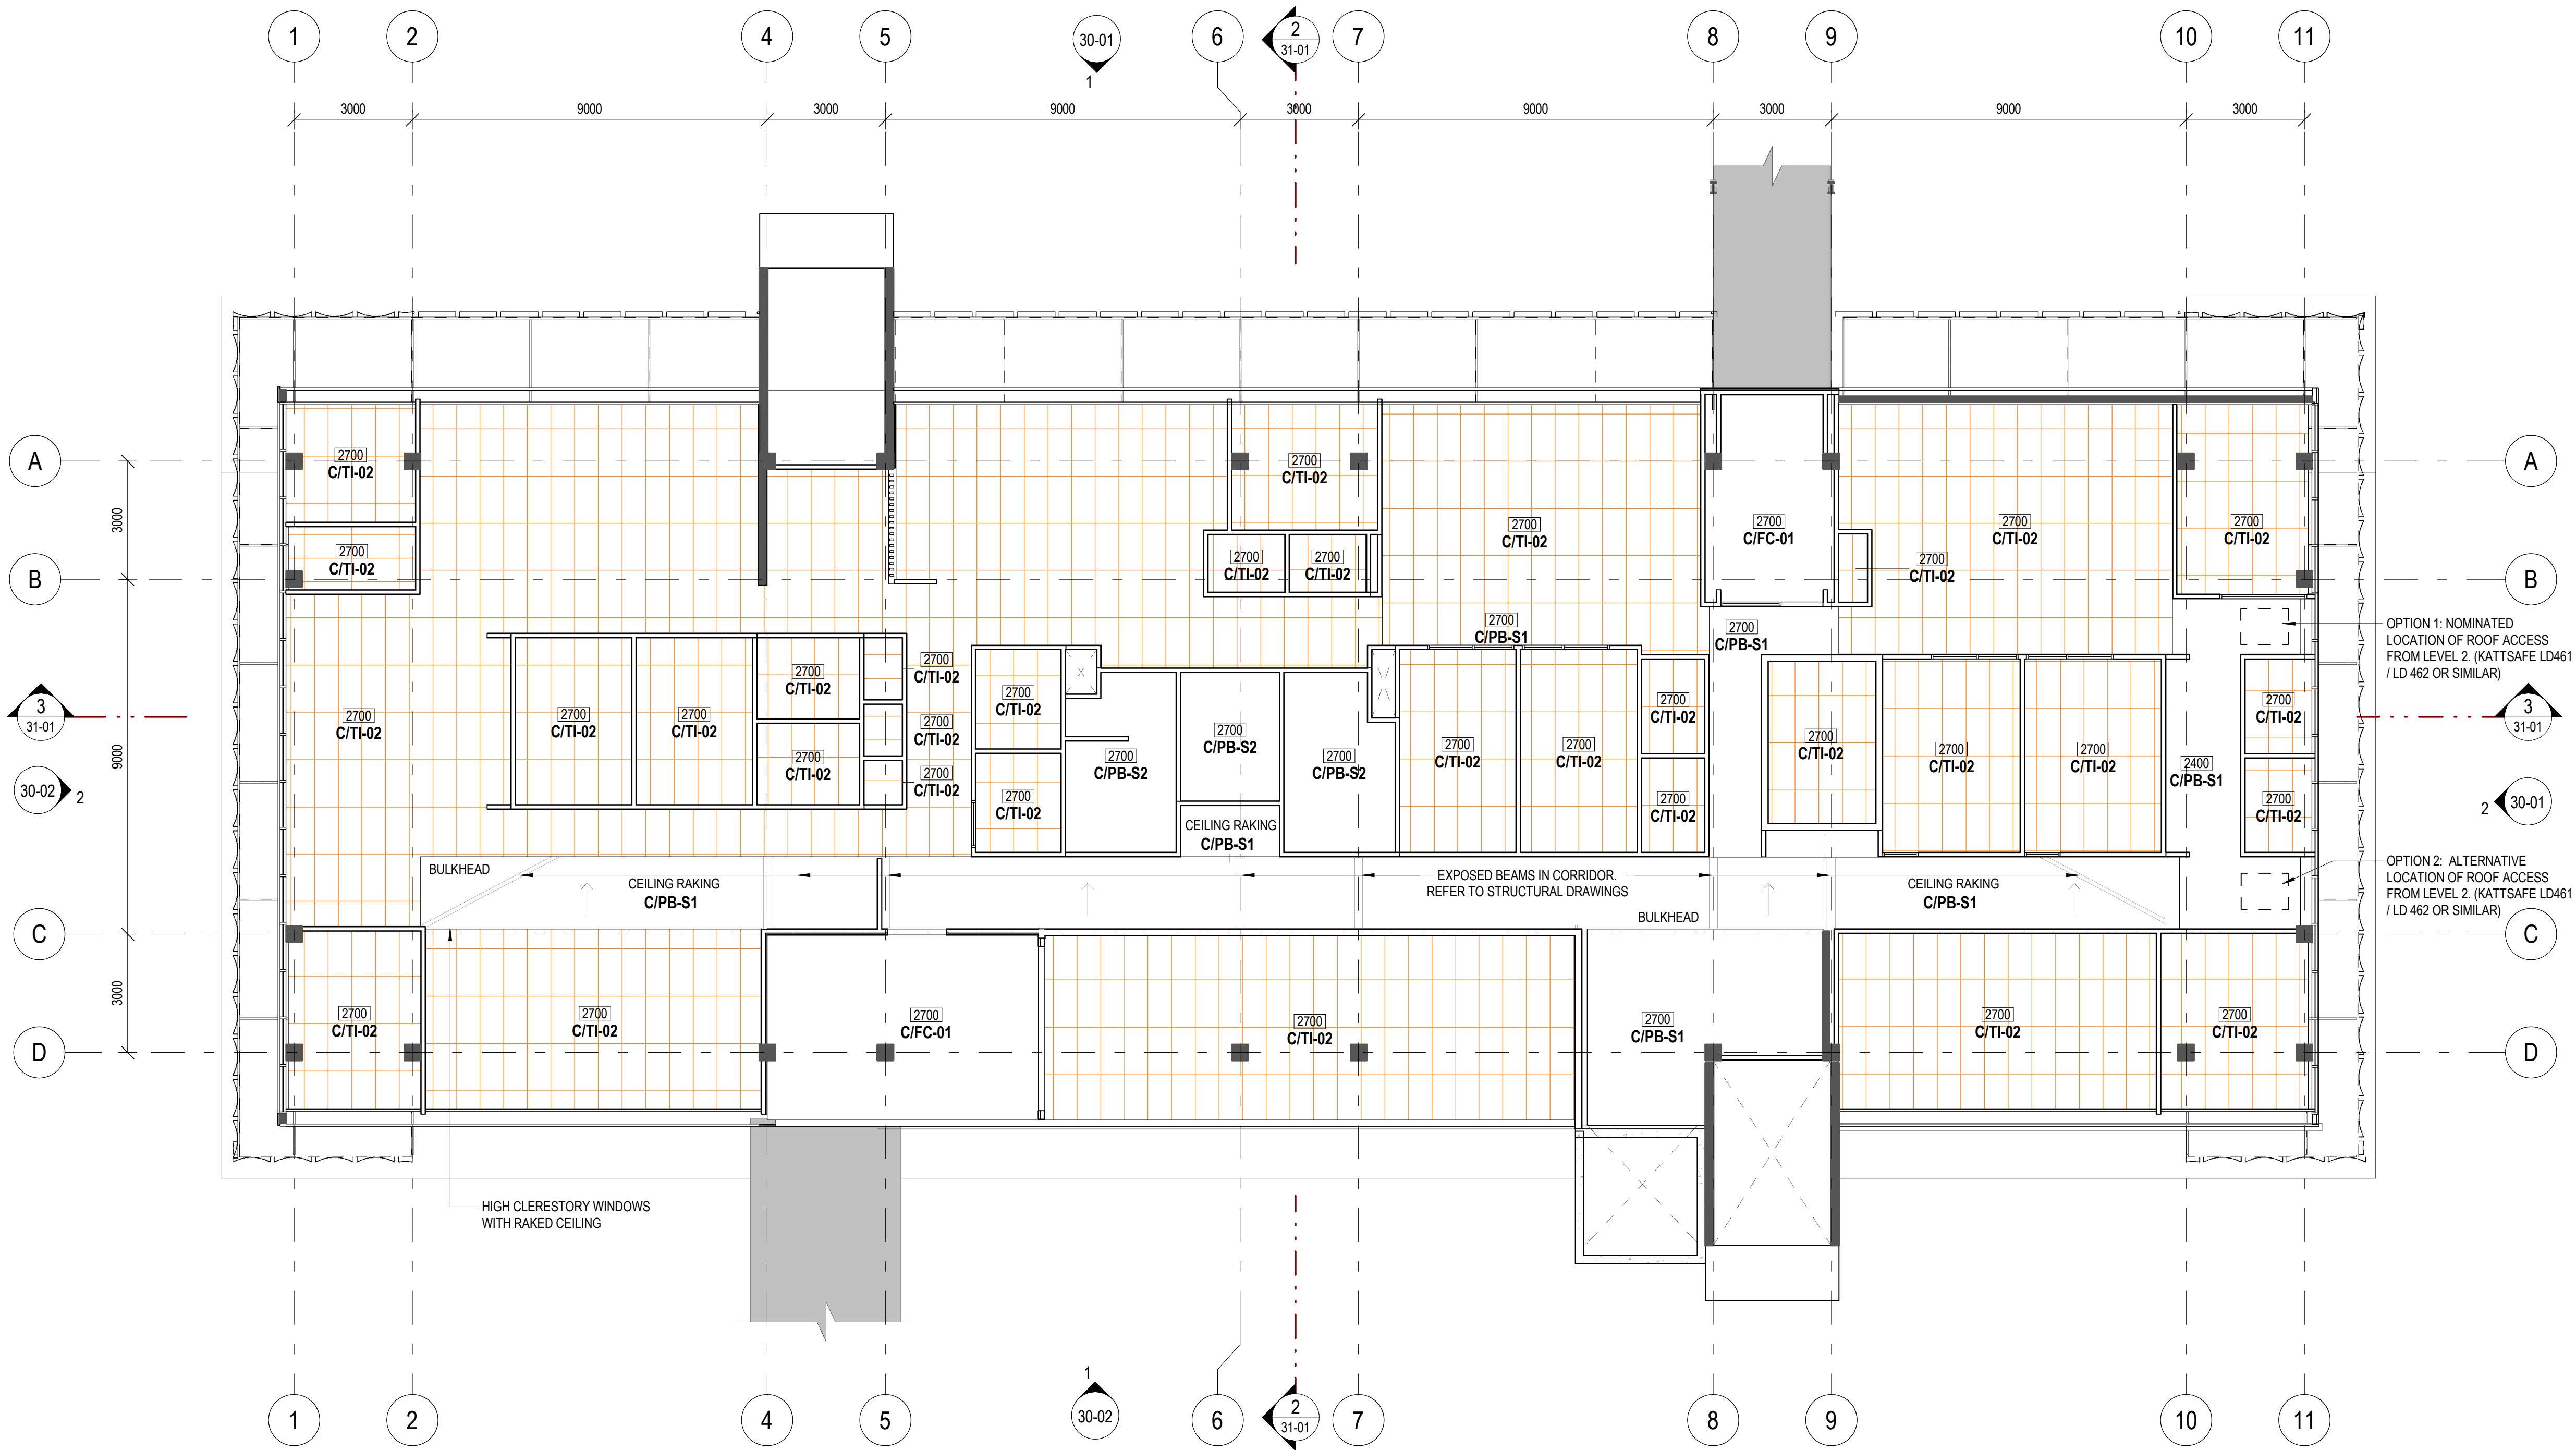

| CEILING LEGEND |                                  |
|----------------|----------------------------------|
| 2700           | CEILING HEIGHT ABOVE FFL         |
| CT1            | CEILING FINISHES                 |
| CEILING LEGEND |                                  |
| C/TI-01        | 1200x600 CEILING TILES           |
| C/TI-02        | 1200x600 ACOUSTIC CEILING TILES  |
| C/PB-S1        | FLUSH SET PLASTERBOARD SHEETING  |
| C/PB-S2        | WATERPROOF PLASTERBOARD SHEETING |
| C/FC-01        | FLUSH SET FIBRE CEMENT SHEETING  |

| GENERAL NOTES   |  |
|---|--|
| • CONTRACTOR TO CONFIRM EXISTING STRUCTURE & SERVICES ON SITE PRIOR BUILDING WORKS.                                                       |  |
| • ALL REFLECTED CEILING PLANS ARE TO BE READ IN CONJUNCTION WITH SERVICE ENGINEERING DRAWINGS FOR MECHANICAL, FIRE, ELECTRICAL AND ALIKE. |  |
| • CEILING REQUIREMENTS TO BE IN ACCORDANCE WITH CQU DESIGN GUIDELINES                                                                     |  |
| • REFER TO OUTLINE SPECIFICATION & SCHEDULE FOR FF&E AND FINISHES                                                                         |  |
| • SETOUT OF CEILING TILES TO BE CONFIRMED                                                                                                 |  |

ISSUED FOR TENDER

## CEILING PLAN - LEVEL 2 PROPOSED

scale 1 : 100 @ A1 project no. 25.0236.17

revision B sheet no. CQU-ROK-033-02-ARC-26-02

original sheet size - A1 (594mm x 841mm)

thomson  
adsett



Telephone +61 7 3840 9999  
bne@thomsonadsett.com  
Level 9, 470 St Pauls Terrace  
Fortitude Valley  
Qld 4006 Australia  
thomsonadsett.com

© Copyright  
These drawings and designs and the copyright thereof are the property of Thomson Adsett Pty Ltd and must not be used, retained or copied without written permission of Thomson Adsett Pty Ltd. ABN 76 105 314 654 Trading as ThomsonAdsett. Dimensions take precedence over scaling. Do not measure off drawings as print sizes may vary

## CQU ROCKHAMPTON TAFE CONSOLIDATION - STAGE 2


554/700 Yaamba Rd, Norman Gardens QLD 4701



|   |            |                   |    |
|---|------------|-------------------|----|
| B | 2026-03-05 | ISSUED FOR TENDER | BC |
| A | 2026-02-12 | ISSUED FOR TENDER | BC |
| 5 | 2026-01-30 | 60% DRAFT ISSUE   | BC |
| 4 | 2026-01-23 | CONSULTANT ISSUES | BC |
| 3 | 2025-12-19 | UPDATED ISSUE     | BC |
| 2 | 2025-12-15 | CONSULTANT ISSUES | BC |
| 1 | 2025-11-24 | 50% COSTING ISSUE | PT |

| rev | date | details | init. |
|-----|------|---------|-------|
|-----|------|---------|-------|

|          |            |
|----------|------------|
| drawn    | date       |
| JS/BC    | 19/01/2026 |
| checked  | date       |
| SS       | 12/02/2026 |
| verified | date       |

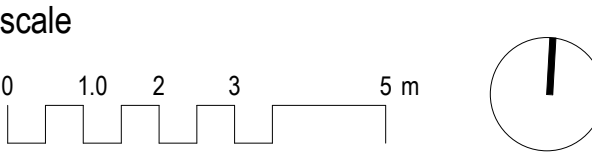

5/03/2026 12:31:18 PM Autodesk Docs://CQU ROK TAFE/25.0236.17\_CQU\_BLDG-33\_2025.rvt