



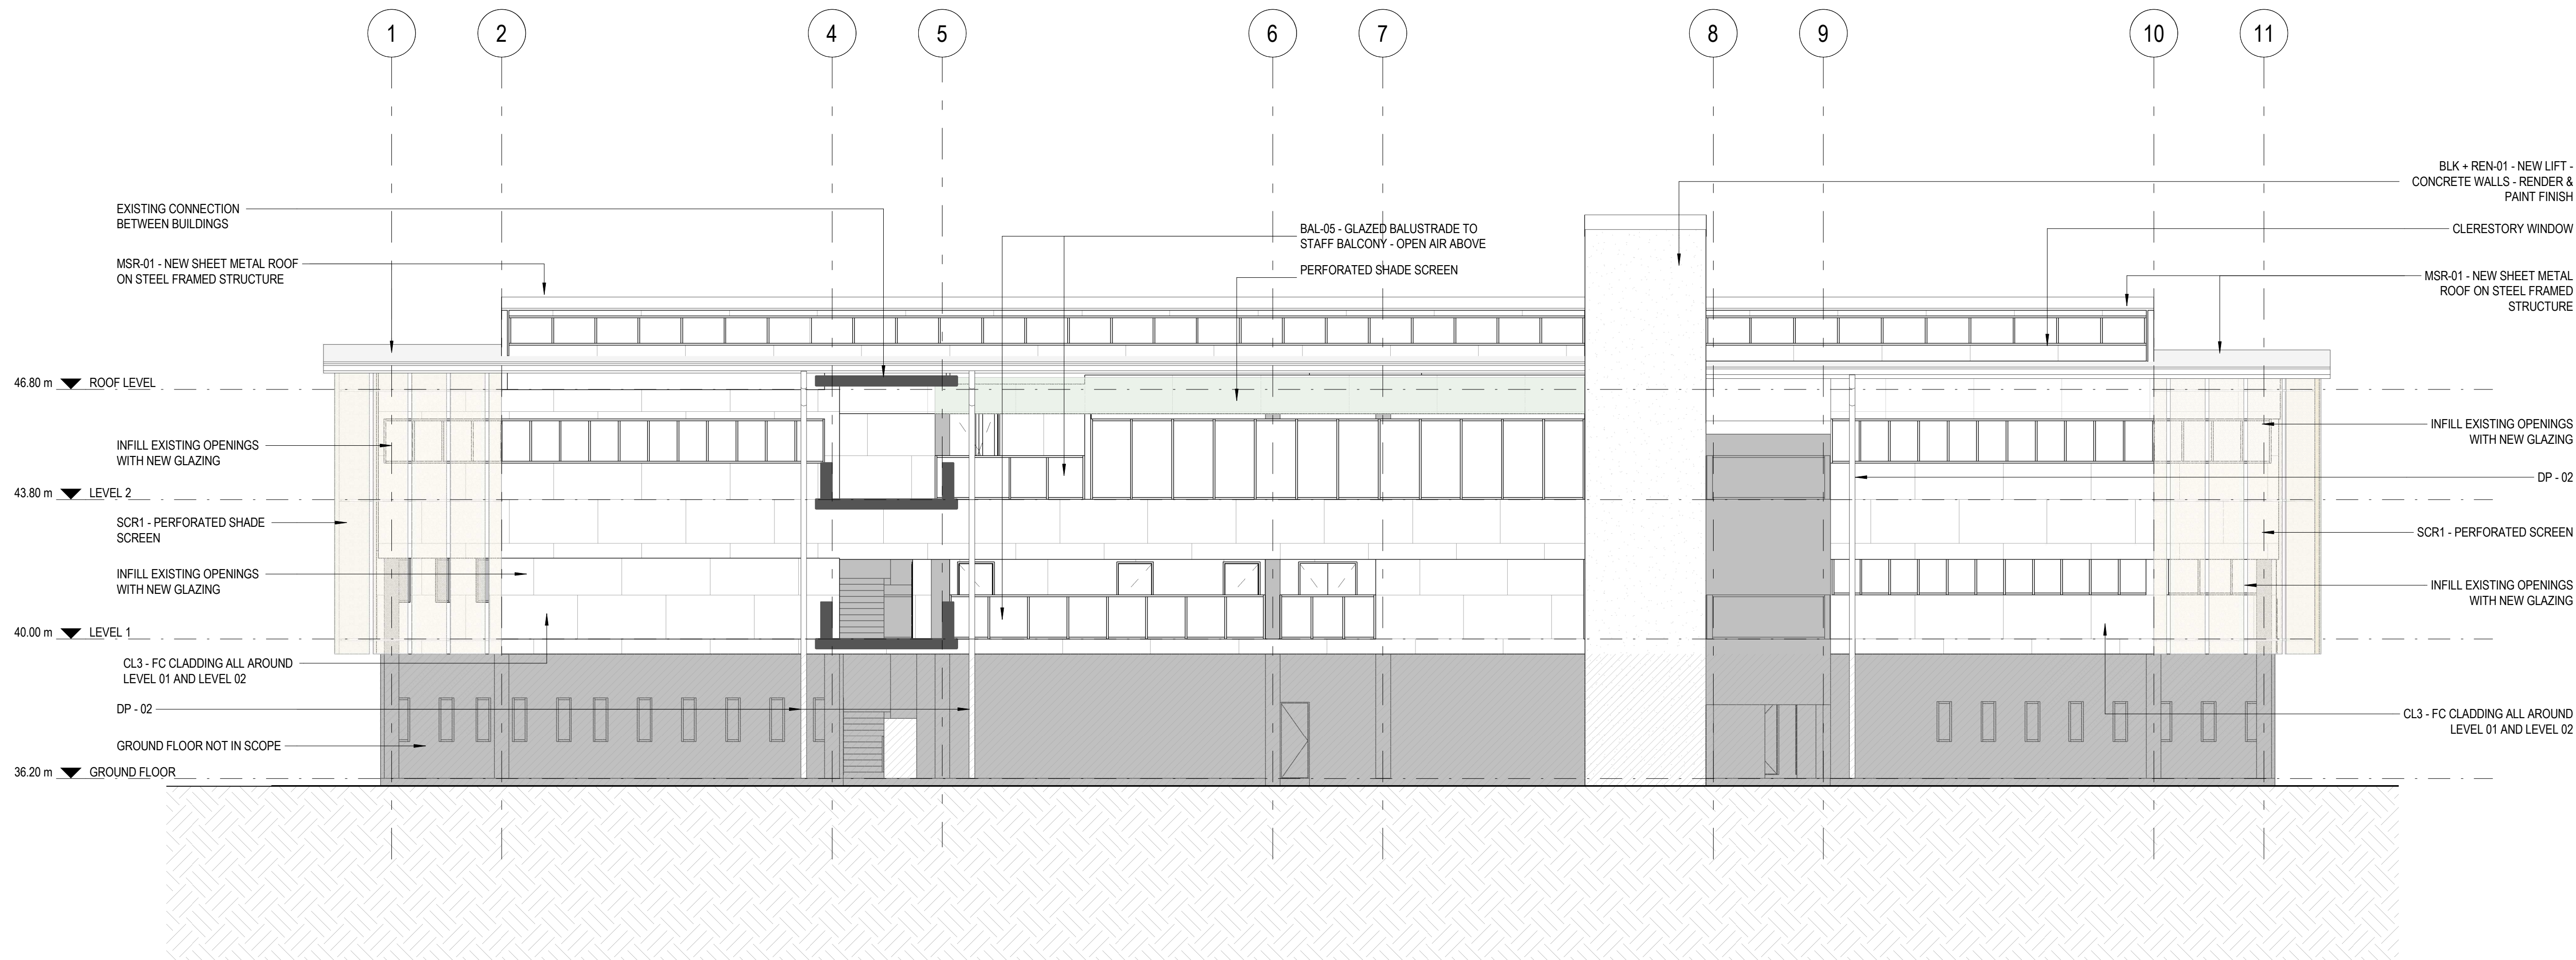

1 SOUTH ELEVATION -PROPOSED
1 : 100

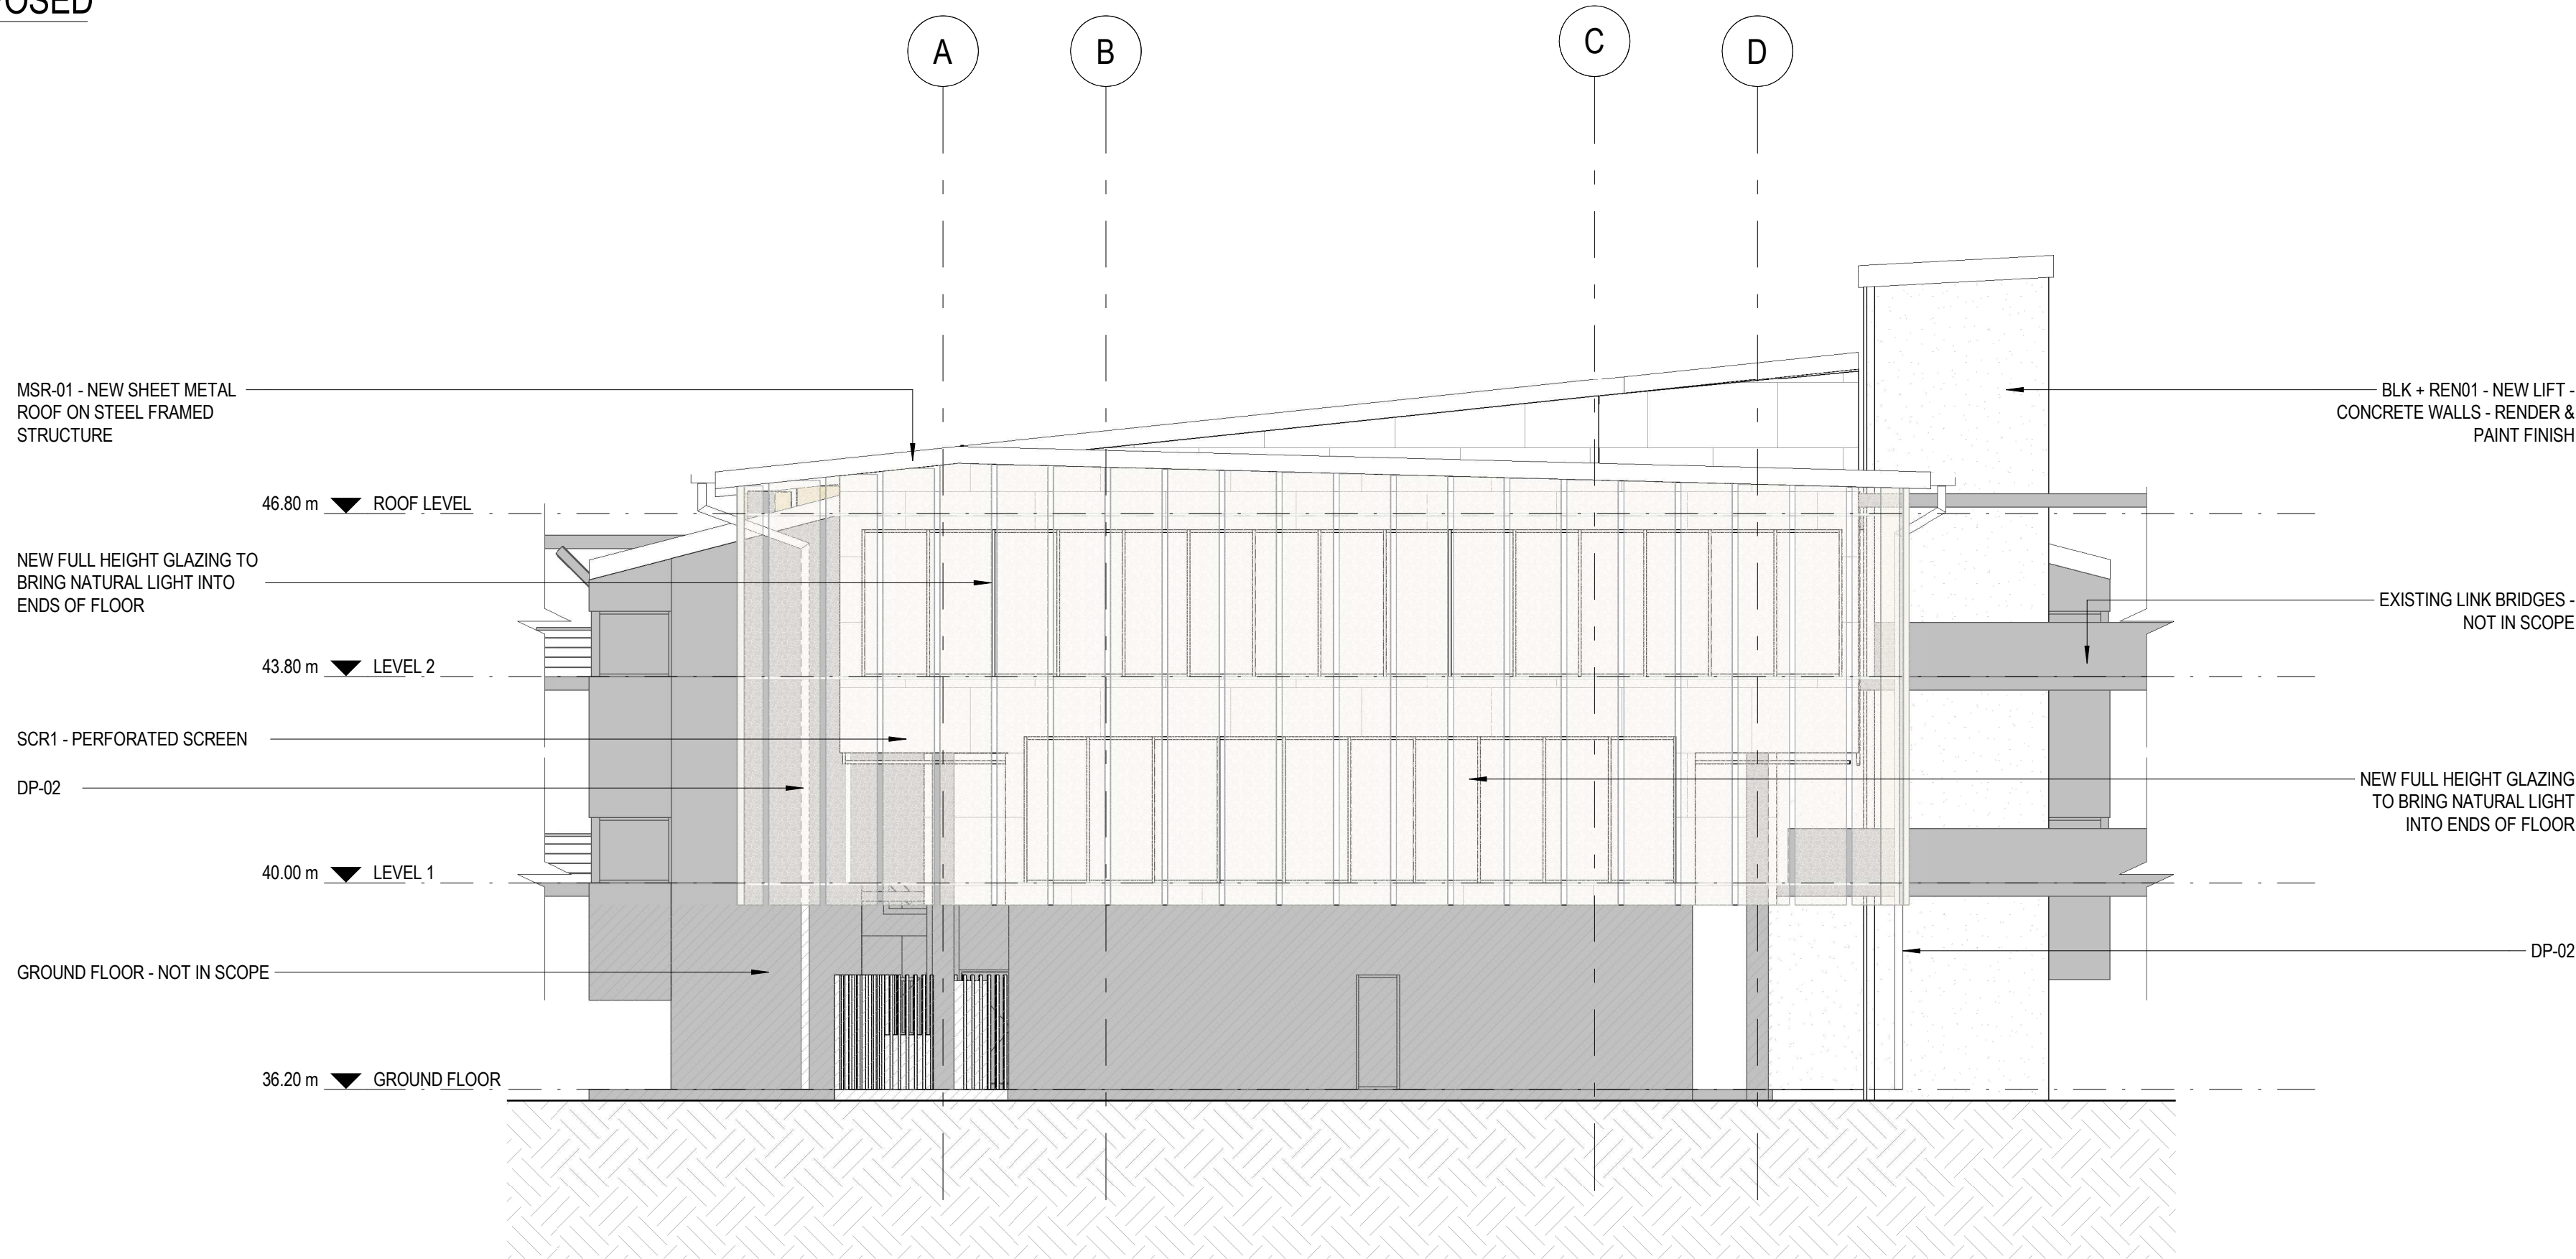

2 WEST ELEVATION - PROPOSED
1 : 100

GENERAL NOTE

- REFER TO CQU DESIGN GUIDELINES FOR DESIGN AND CONSTRUCTION REQUIREMENTS.
- REFER TO OUTLINE SPECIFICATION & SCHEDULE FOR FF&E AND FINISHES

© Copyright
These drawings and designs and the copyright thereof are the property of Thomson Adsett Pty Ltd and must not be used, retained or copied without written permission of Thomson Adsett Pty Ltd. ABN 76 105 314 654 Trading as ThomsonAdsett. Dimensions take precedence over scaling. Do not measure off drawings as print sizes may vary


**CQU ROCKHAMPTON
TAFE
CONSOLIDATION -
STAGE 2**

554/700 Yaamba Rd, Norman
Gardens QLD 4701



B	2026-03-05	ISSUED FOR TENDER	BC
A	2026-02-12	ISSUED FOR TENDER	BC
3	2026-01-30	60% DRAFT ISSUE	BC
2	2026-01-27	ELEVATION ISSUE	BC
1	2025-12-19	UPDATED ISSUE	BC

rev	date	details	init.
drawn	date		
JS/BC	19/01/2026		
checked	date		
BC	12/02/2026		
verified	date		

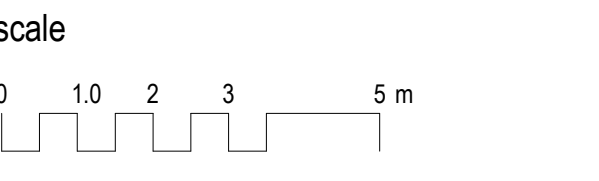

**BUILDING ELEVATIONS -
PROPOSED**

scale project no.
1 : 100 @ A1 25.0236.17

revision
B
sheet no.
CQU-ROK-033-00-ARC-30-02

ISSUED FOR TENDER