



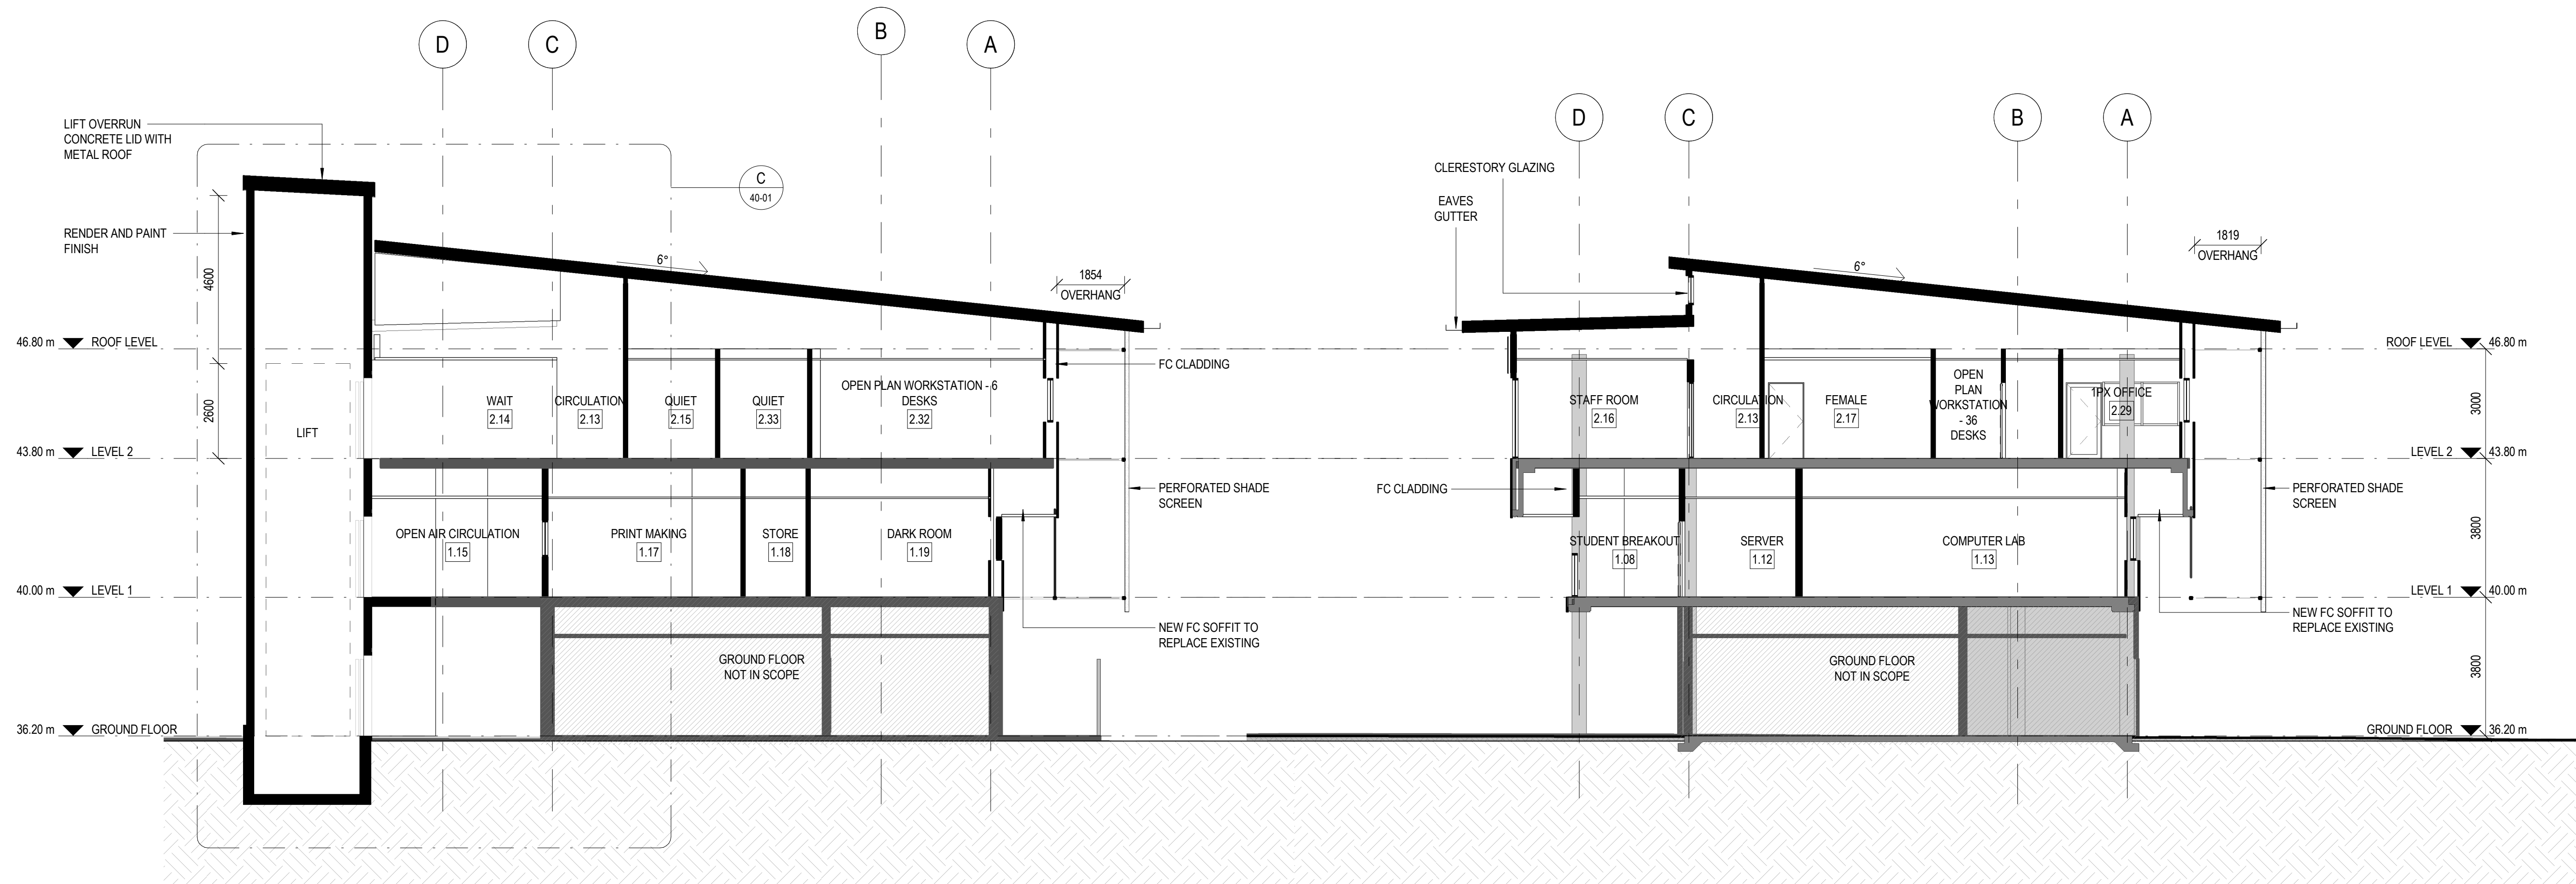

1 TRANSVERSAL SECTION 1 - PROPOSED
1 : 100

2 TRANSVERSAL SECTION 2 - PROPOSED
1 : 100

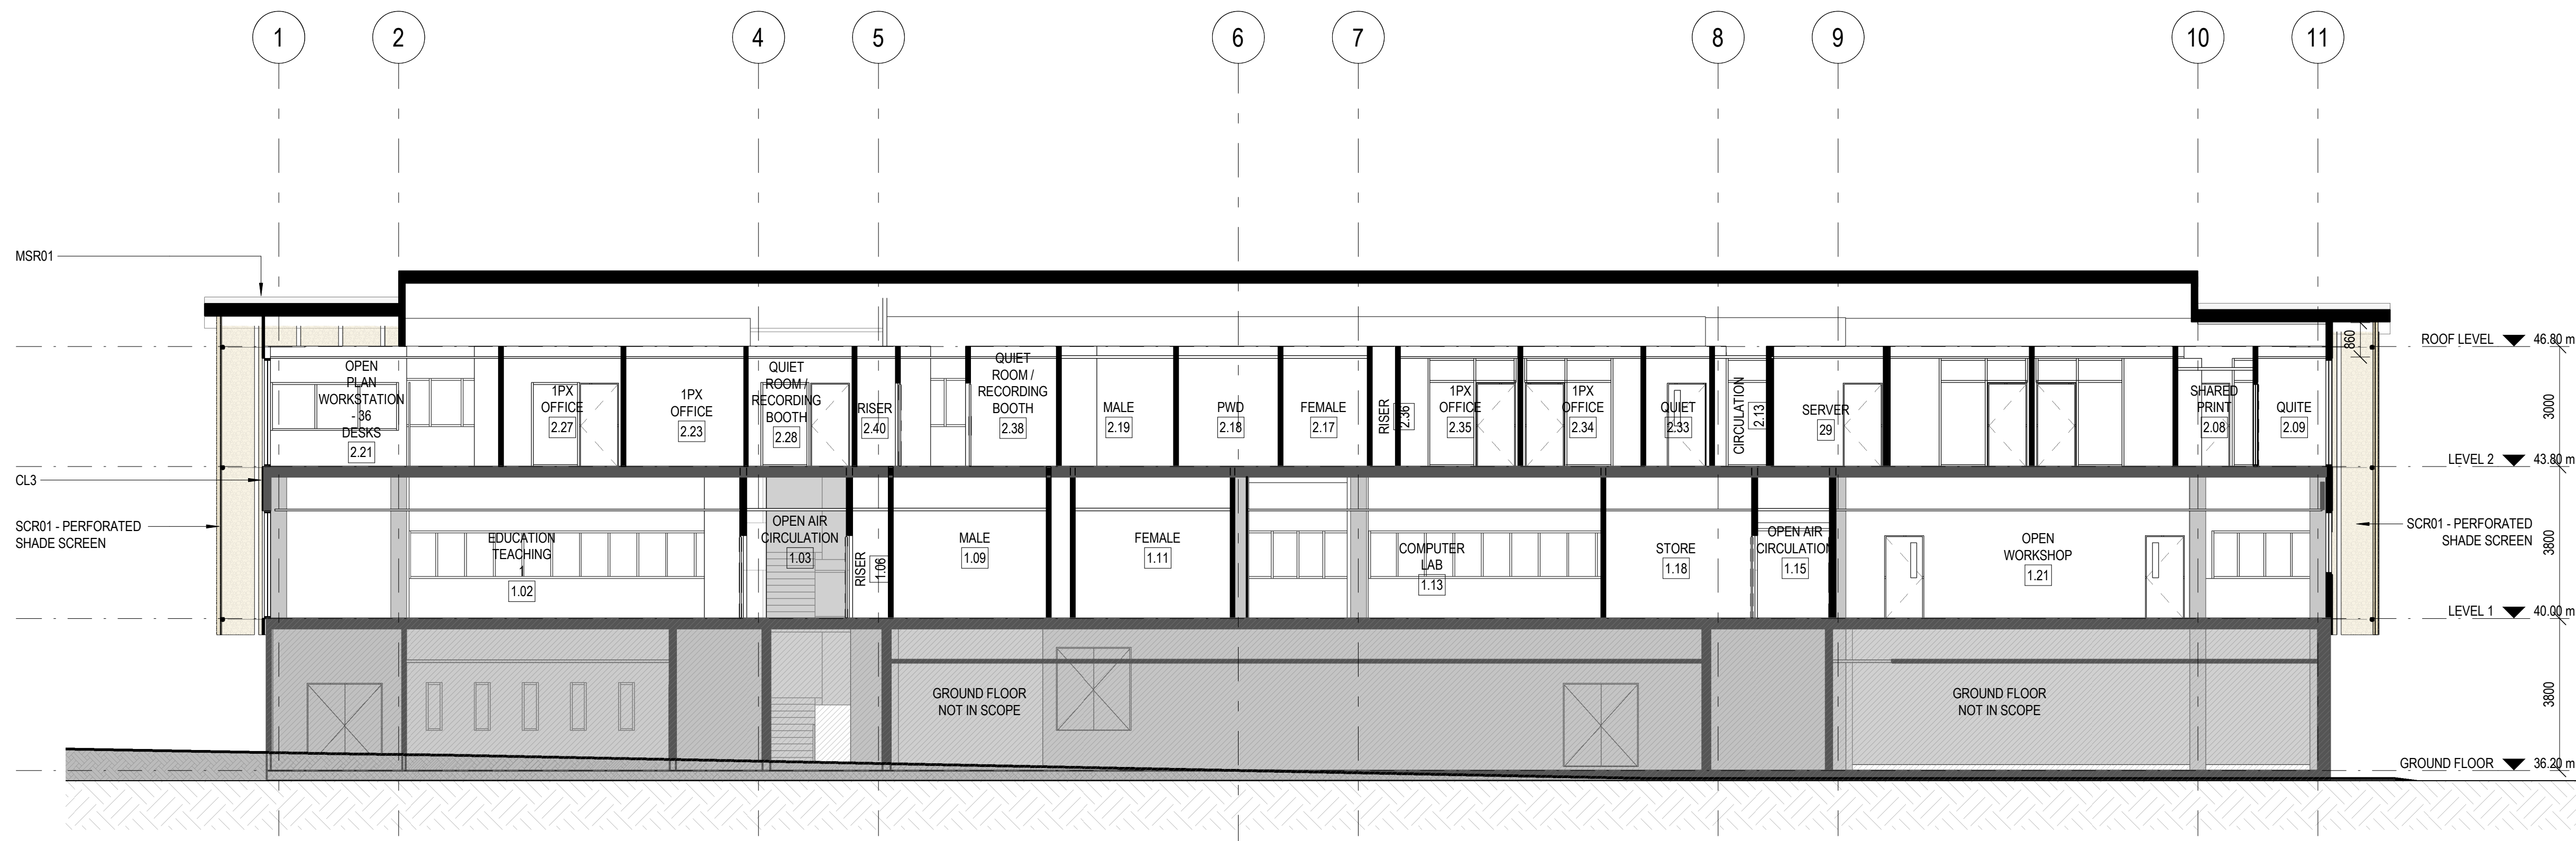

3 LONGITUDINAL SECTION - PROPOSED
1 : 100

GENERAL NOTE

- REFER TO CQU DESIGN GUIDELINES FOR DESIGN AND CONSTRUCTION REQUIREMENTS.
- REFER TO OUTLINE SPECIFICATION & SCHEDULE FOR FF&E AND FINISHES

**CQU ROCKHAMPTON
TAFE
CONSOLIDATION -
STAGE 2**

554/700 Yaamba Rd, Norman
Gardens QLD 4701


for



B	2026-03-05	ISSUED FOR TENDER	BC
A	2026-02-12	ISSUED FOR TENDER	BC
2	2026-01-30	60% DRAFT ISSUE	BC
1	2025-12-19	UPDATED ISSUE	BC

rev	date	details	init.
-----	------	---------	-------

drawn	date
JS/BC	19/01/2026
checked	date
BC	12/02/2026
verified	date

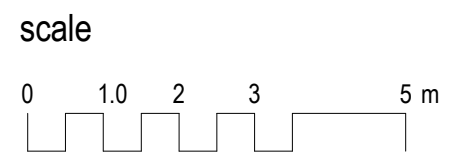

**BUILDING SECTIONS -
PROPOSED**

scale
1 : 100 @ A1

project no.
25.0236.17

revision

B

sheet no.

CQU-ROK-033-00-ARC-31-01