


CQU ROCKHAMPTON TAFE CONSOLIDATION - STAGE 2


554/700 Yaamba Rd, Norman
Gardens QLD 4701

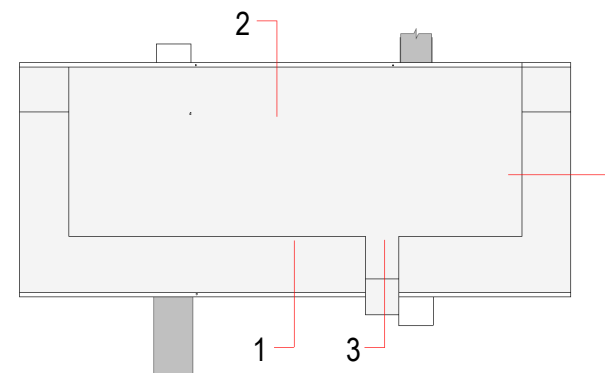

B	2026-03-05	ISSUED FOR TENDER	BC
A	2026-02-12	ISSUED FOR TENDER	BC
1	2026-01-30	60% DRAFT ISSUE	BC

rev	date	details	init.
-----	------	---------	-------

drawn	date
JS/BC	19/01/2026
checked	date
BC	12/02/2026
verified	date

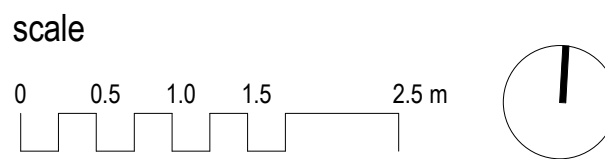

CONSTRUCTION DETAILS

scale
As indicated @ A1

project no.
25.0236.17


revision
B

sheet no.
CQU-ROK-033-00-ARC-40-01

ISSUED FOR TENDER

GENERAL NOTE

- REFER TO CQU DESIGN GUIDELINES FOR DESIGN AND CONSTRUCTION REQUIREMENTS.
- REFER TO OUTLINE SPECIFICATION & SCHEDULE FOR FINISHES
- INSTALL FIRE SEAL TO GAPS BEHIND CLADDING BETWEEN FLOOR LEVELS TO ACHIEVE FRL REQUIREMENT, BASE ON CERTIFIER'S REPORT.

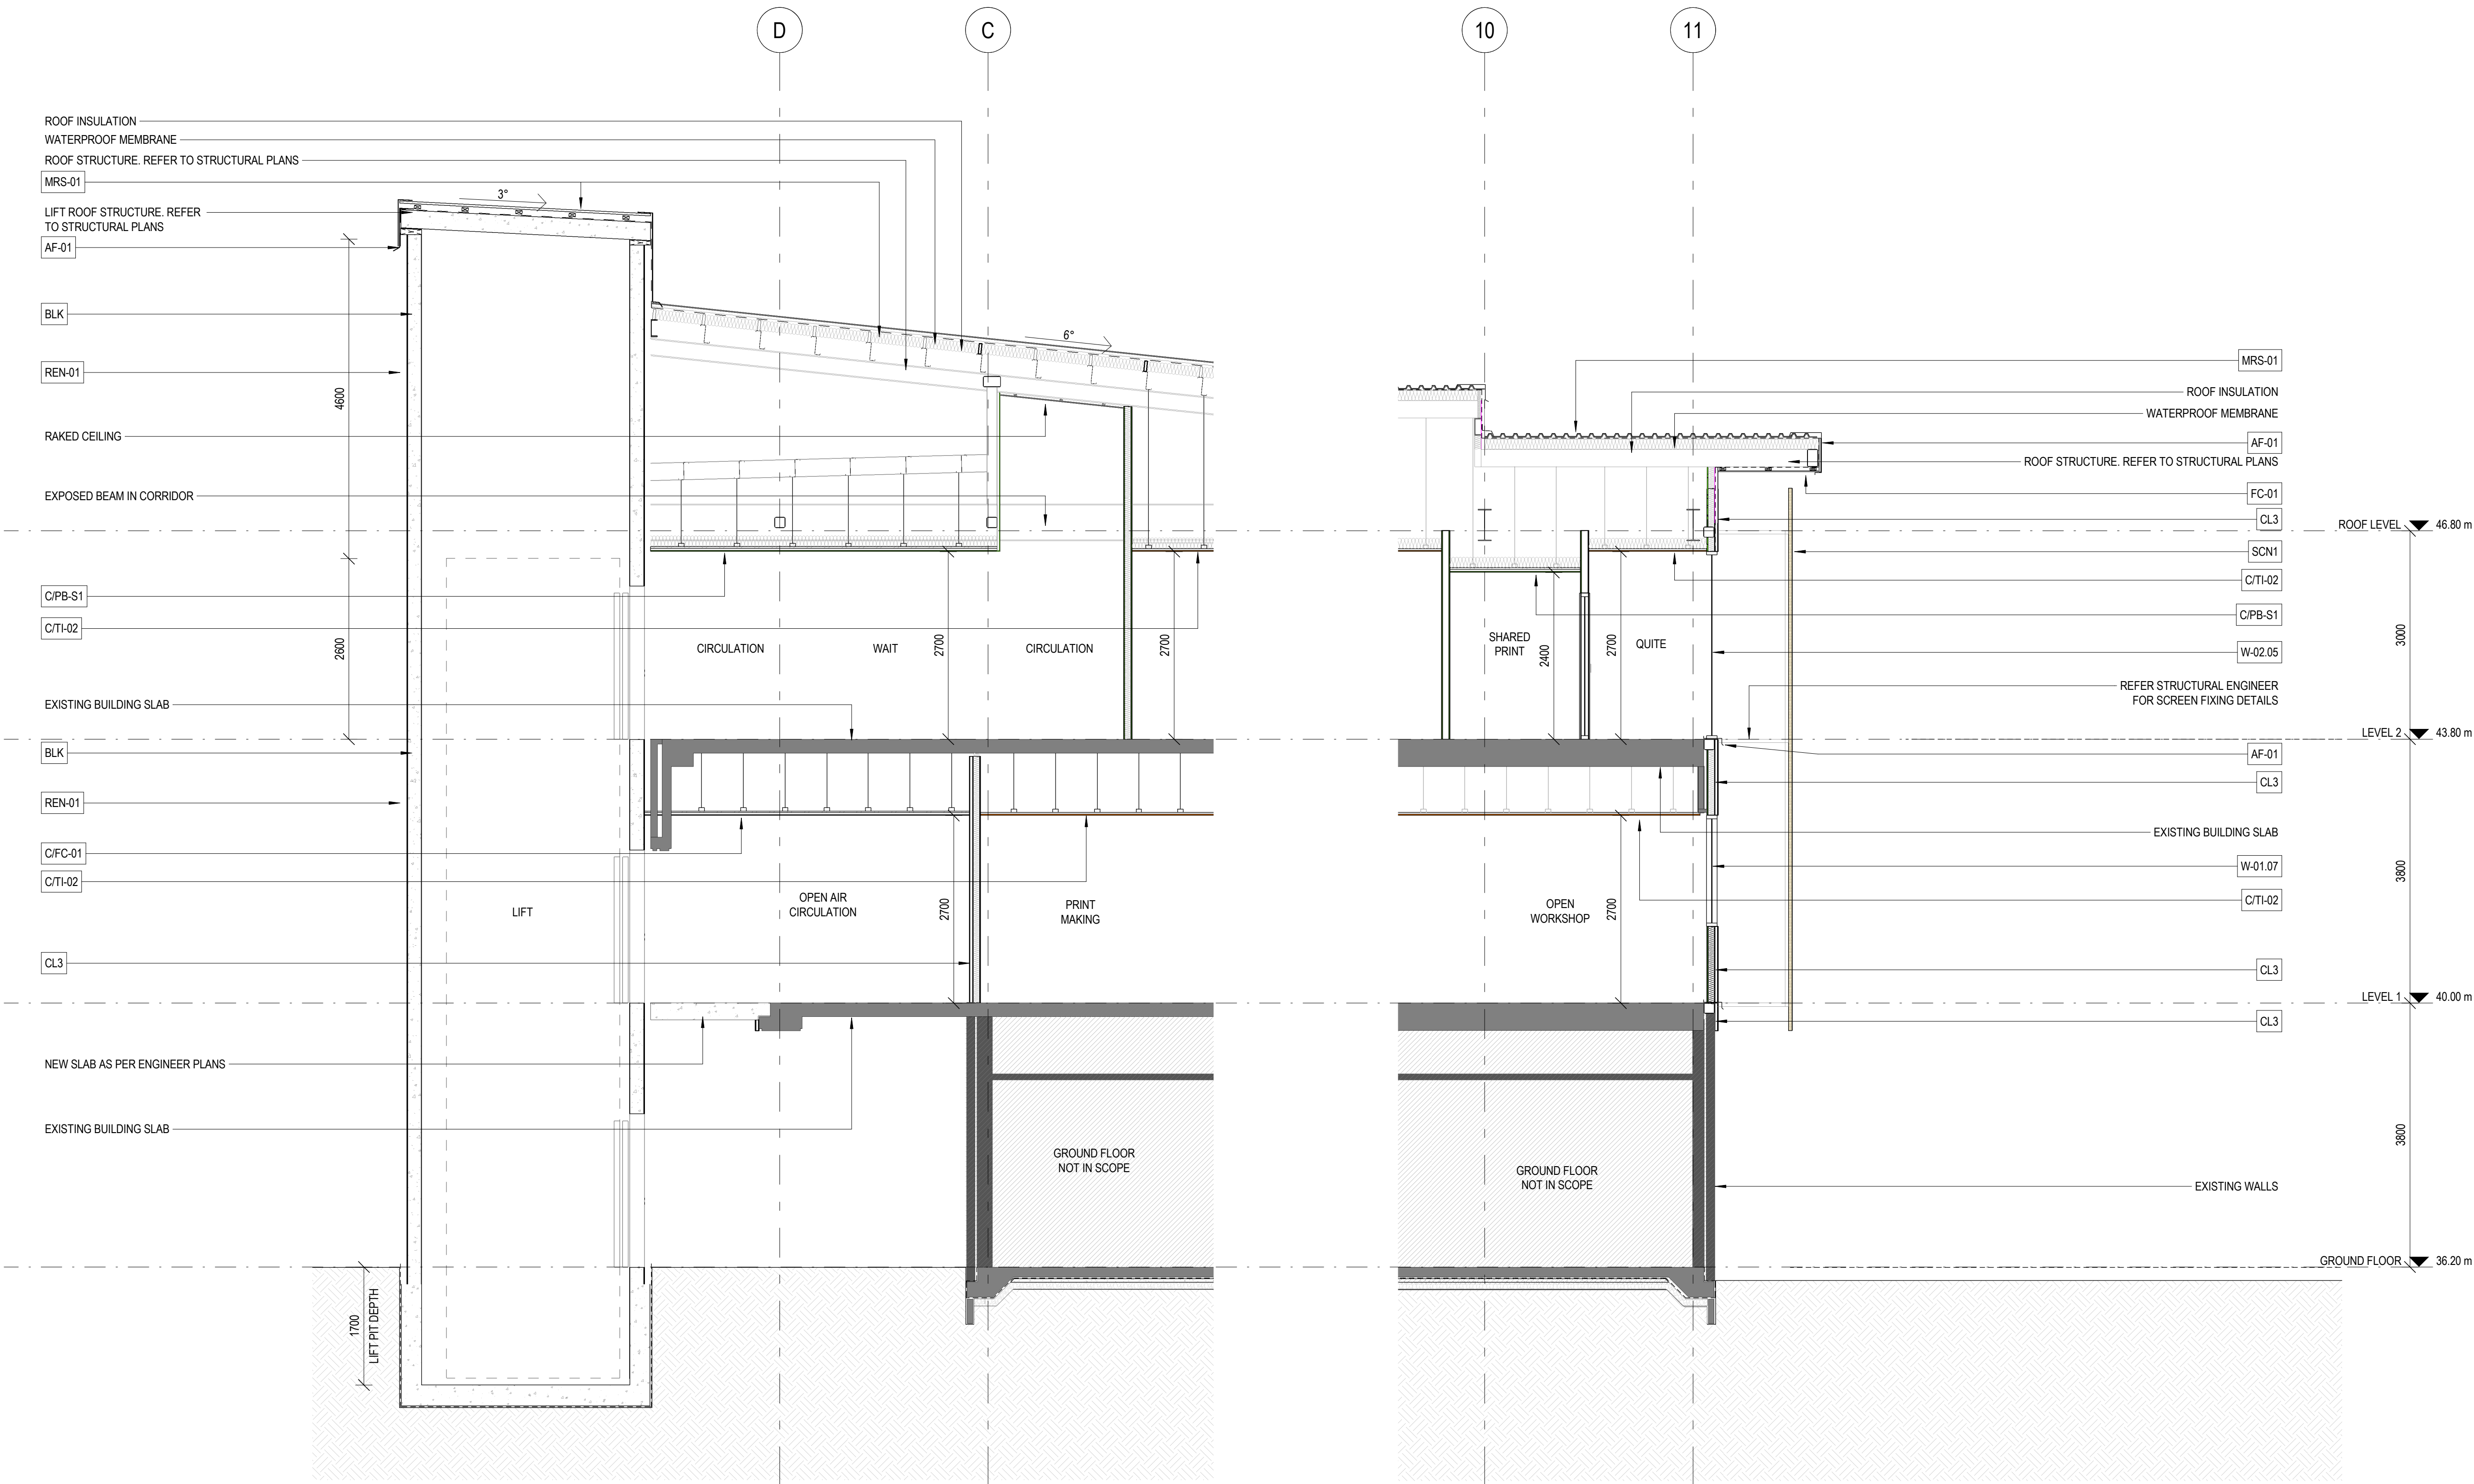

C WALL SECTION 3
21-00 1 : 50

D WALL SECTION 4
21-00 1 : 50