

**CQU ROCKHAMPTON
TAFE
CONSOLIDATION -
STAGE 2**554/700 Yaamba Rd, Norman
Gardens QLD 4701

for



A	12/02/26	ISSUED FOR TENDER	SM
2	30/01/26	60% DRAFT ISSUE	SM
1	23/01/26	FOR COORDINATION ISSUE	SM

rev	date	details	init.
-----	------	---------	-------

drawn	date
PT/TA	19/12/25
checked	date
JT	19/12/25
verified	date
JT	19/12/25

scale
0 0.5 1.0 1.5 2.5 m**RLS - BLD33-L1 -
EDUCATION TEACHING 1 &
2**scale project no.
1 : 50 @ A1 260018revision
A
sheet no.
CQU-ROK-033-01-ARC-60-01

original sheet size - A1 (594mm x 841mm)

EARLY CHILDHOOD
REQUIRED SPACE - 42 STUDENTS
SEATS ACCOMMODATED - 42 SEATS + 7 EXTRA BAR STOOLS TO WORK BENCH**GENERAL LEARNING**
REQUIRED SPACE - 42 STUDENTS
SEATS ACCOMMODATED - 42 SEATS + 7 EXTRA BAR STOOLS TO WORK BENCH**40-LEGEND FFE - EDUCATIONAL TEACHING 1.02**

Code	Description	Group	Count
AV20A	Video Conferencing - Mobile Teleconferencing Screen. Refer To AV Consultant's Documentation for Specification	1	1
CL7C	Double Roller Blinds - Blockout	1	11
CL8C	Single Block Out Blind	1	2
SK18A	Sink - Single bowl Overmount Care Accessible	1	1
TB17A	Table - Rectangular	1	8
TB55B	Podion Orion 1 Lectern	1	1
TPA	Mixer - Sink Accessible	1	1
CH6T	Chair - Stackable Student Transferred	2T	43
CH2A	Chair - Stool Footring With Gas Lift Height Adjustment	3	7

60-LEGEND JOINERY - EDUCATION TEACHING 1&2

FFE_Mark	Comments
J.33.01	Benchtop, Underbench Cupboards, Underbench Open Shelving, Knee Clearance Unit, Gables, Kick

PROMETHEAN BOARDS
CONFIRMED AS ONLY AV
REQUIREMENT BY
EDUCATION STAKEHOLDERS
& CQU PM**FF&E LEGEND**

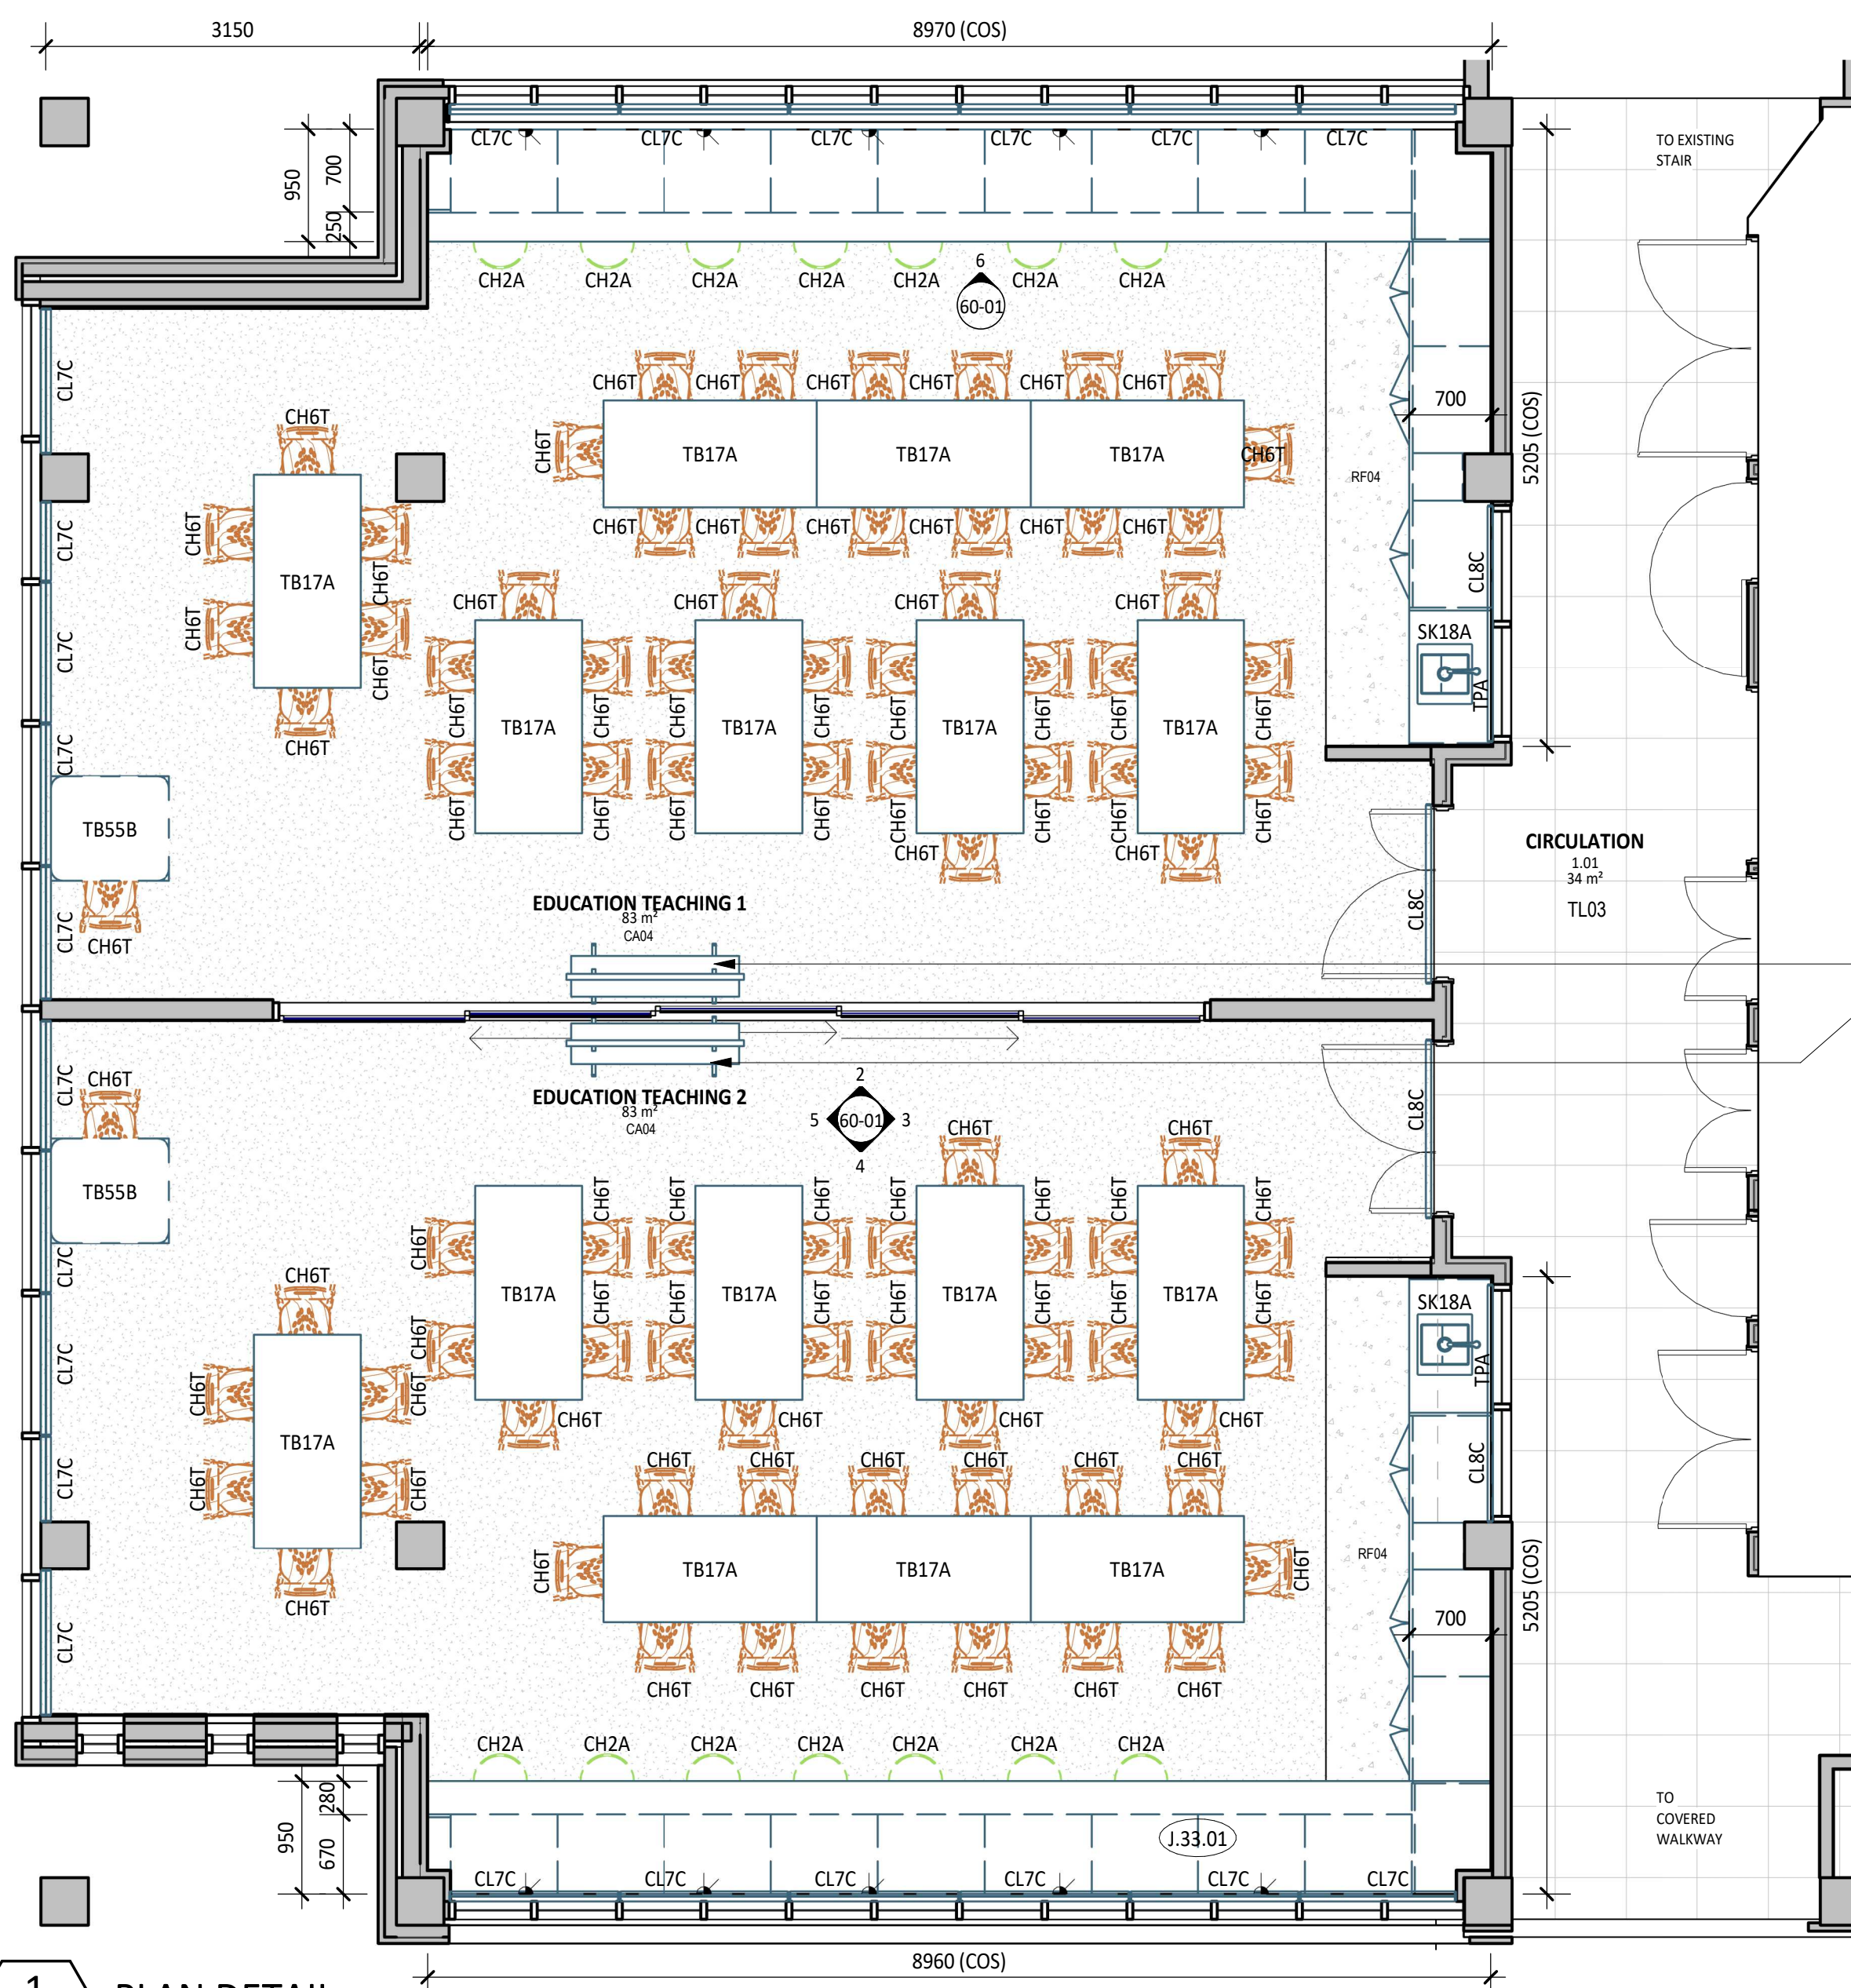
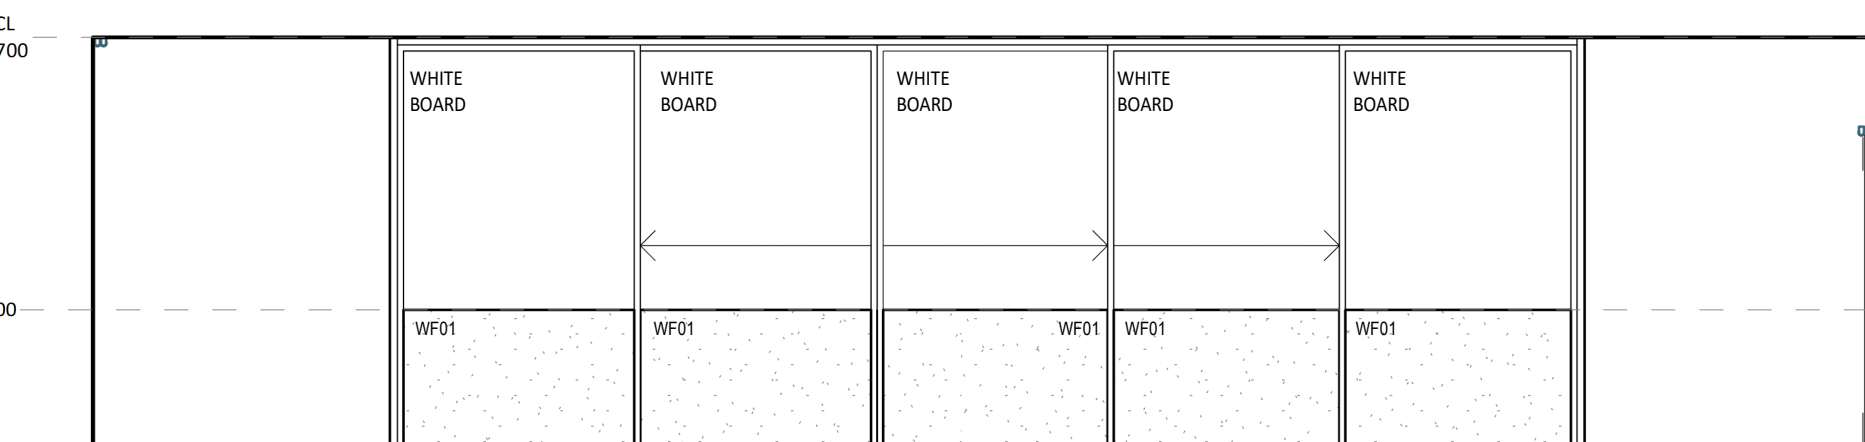
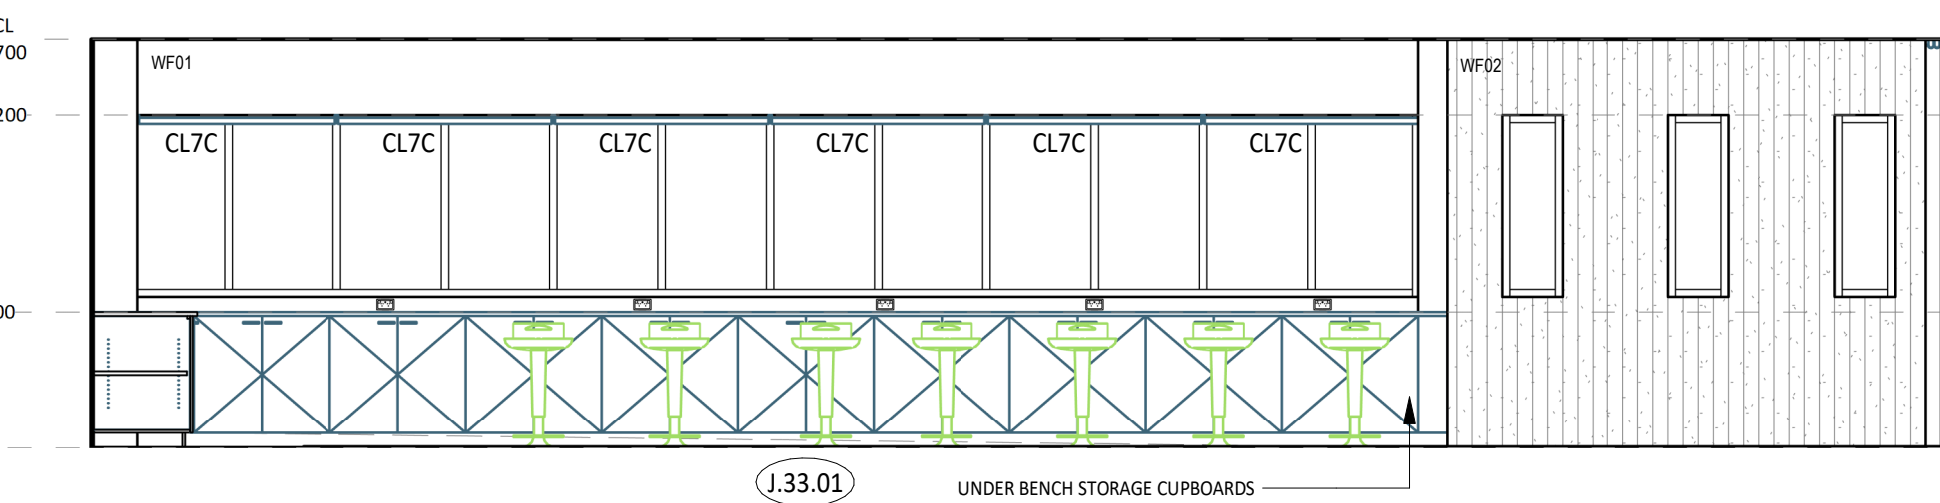
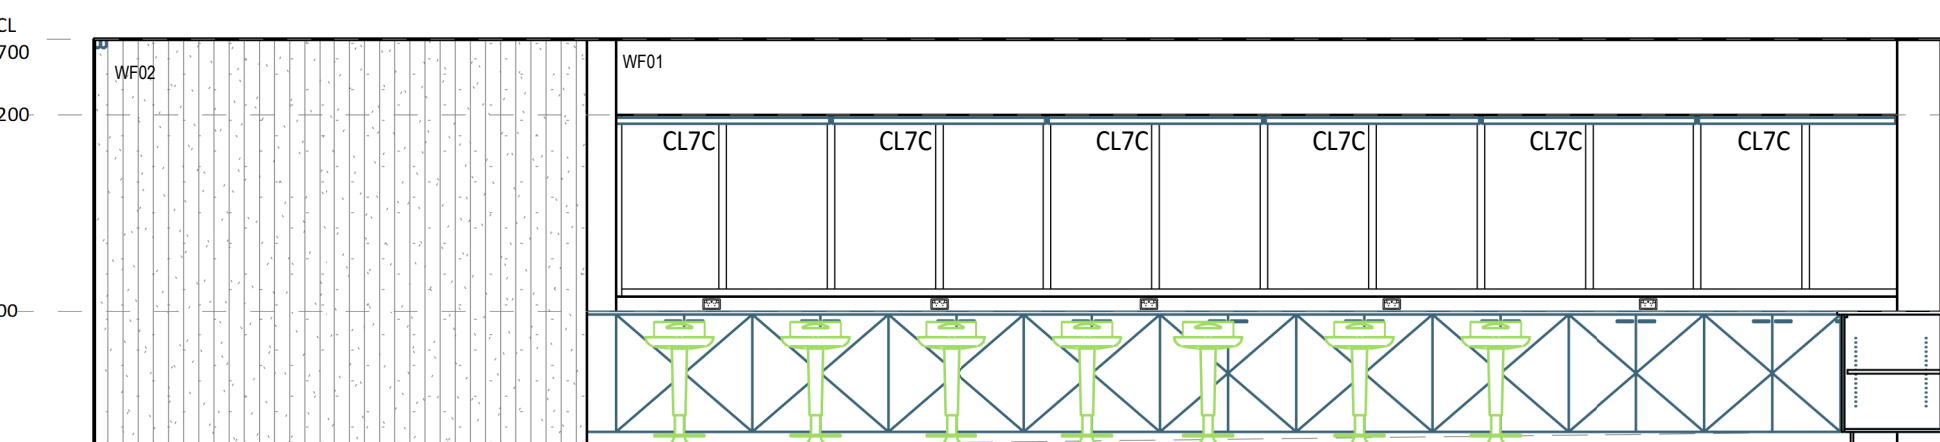
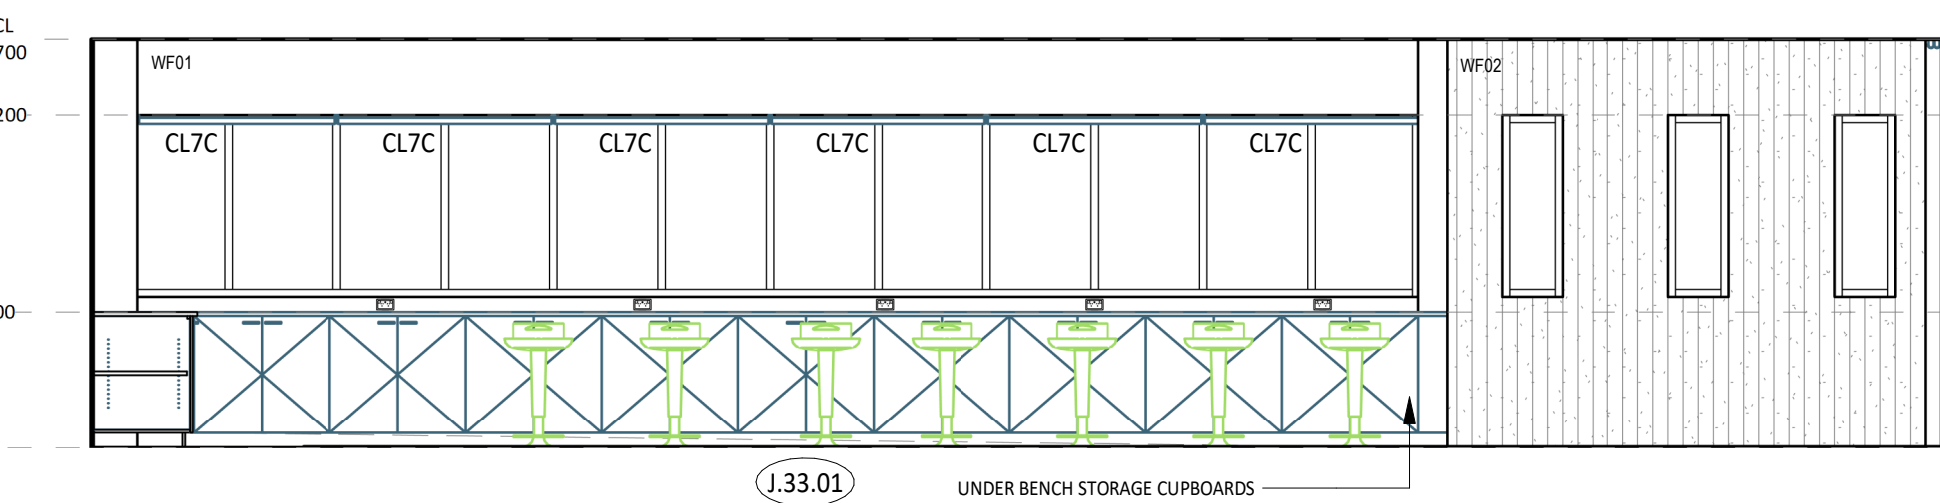
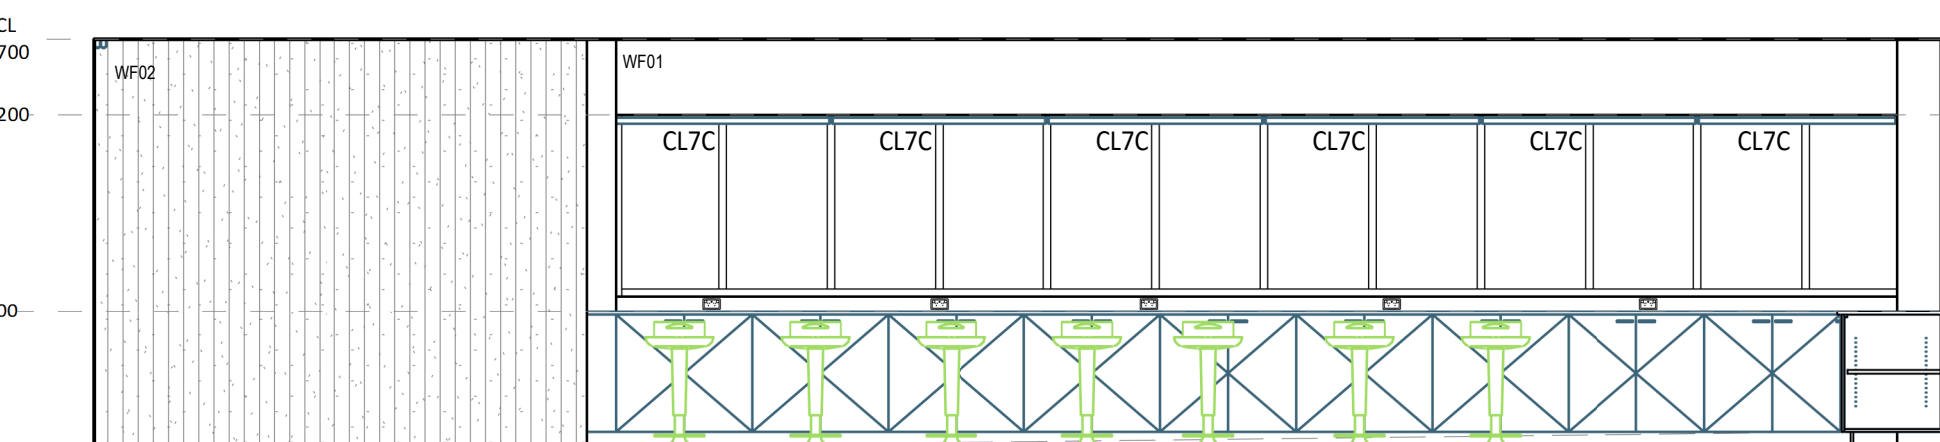
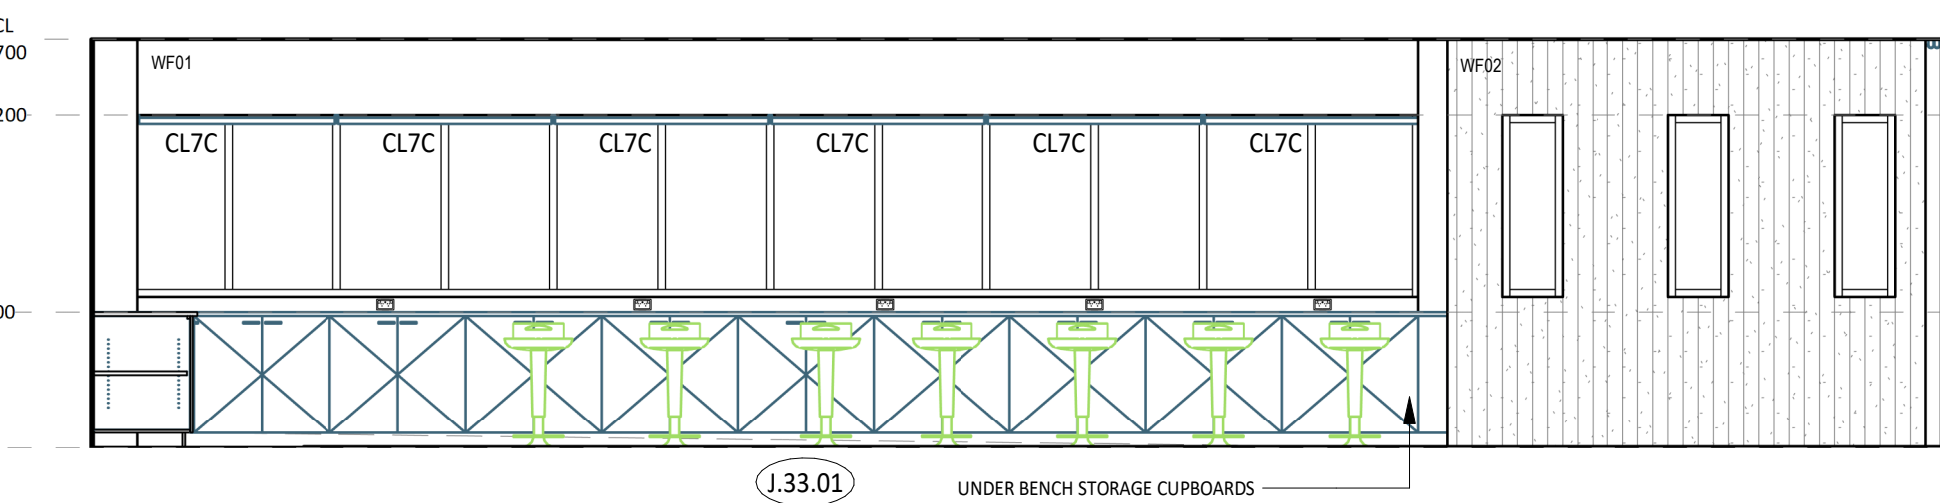
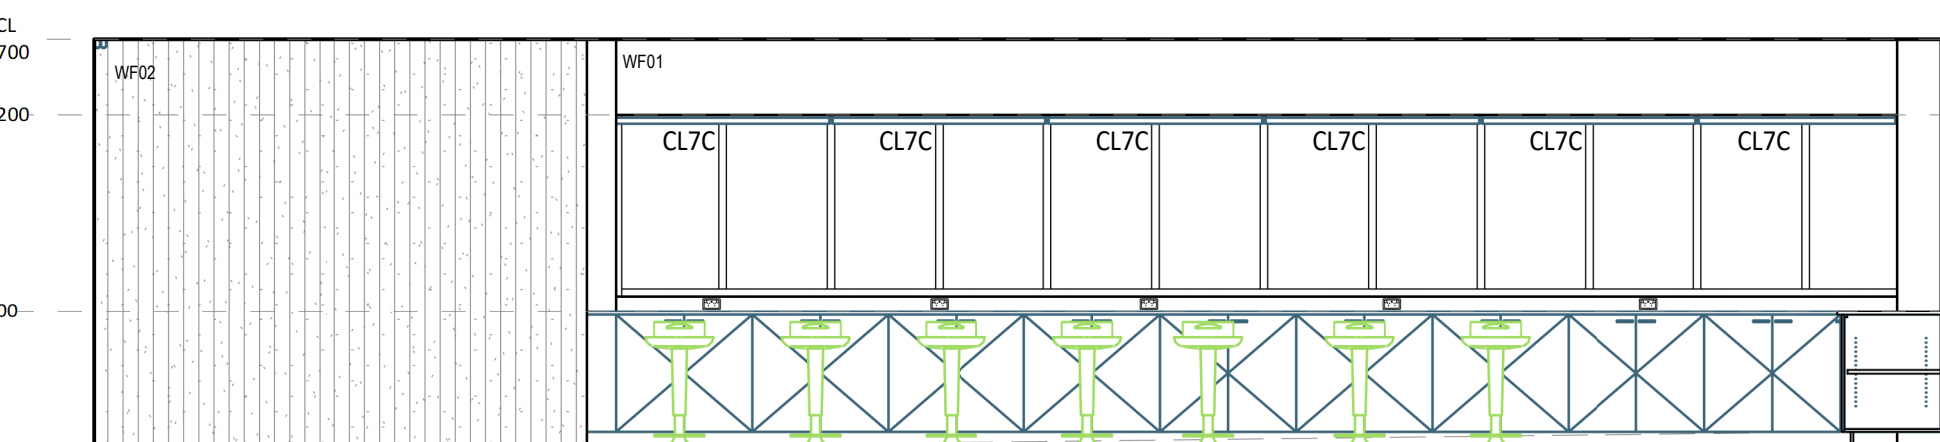
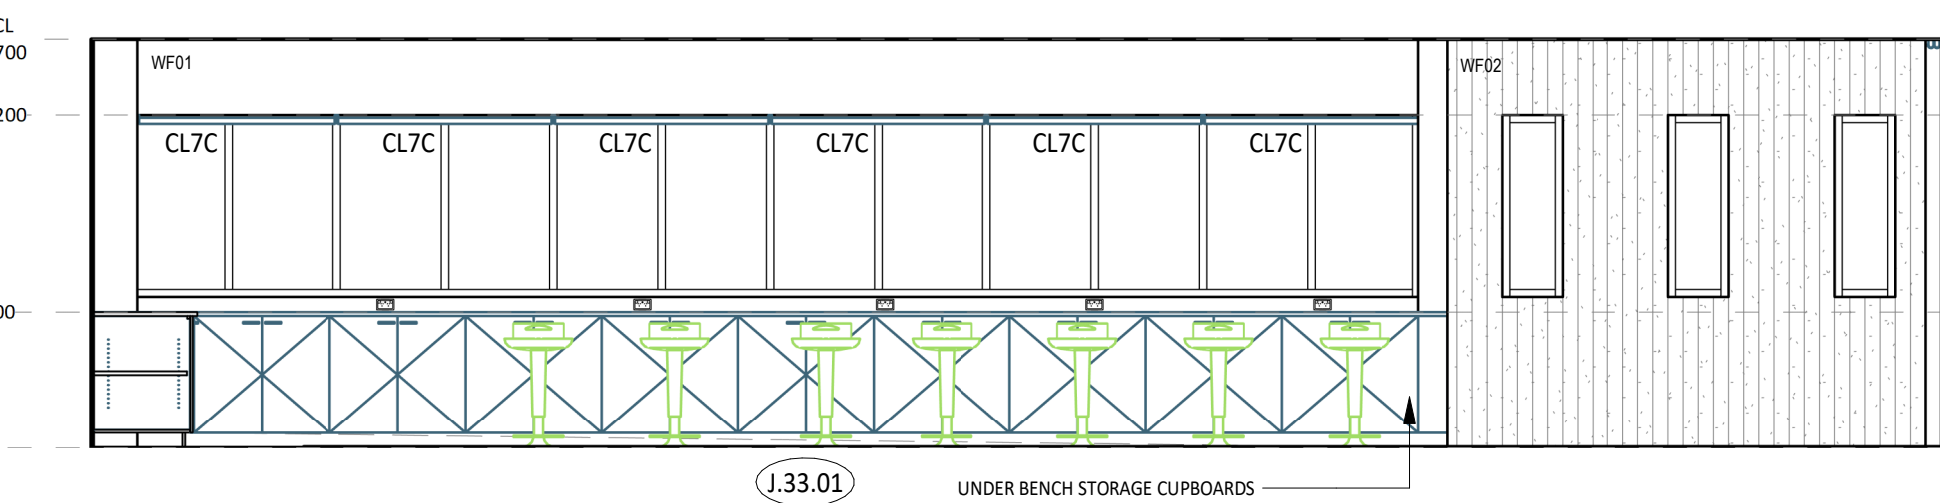
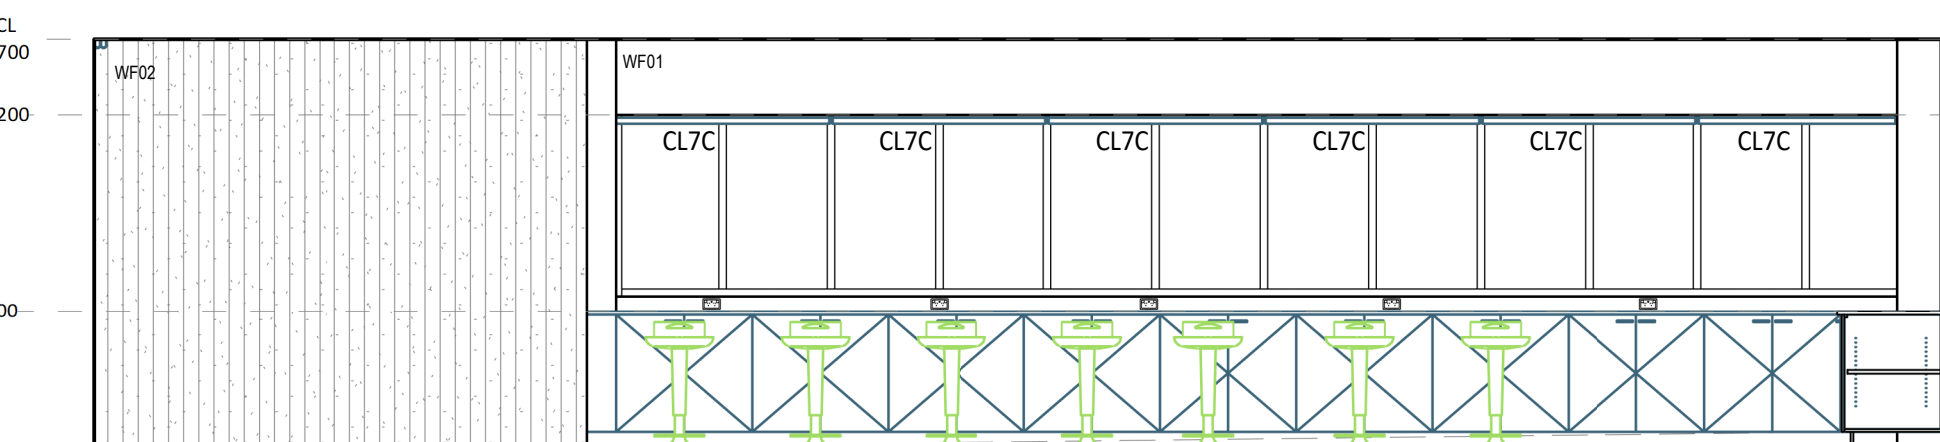
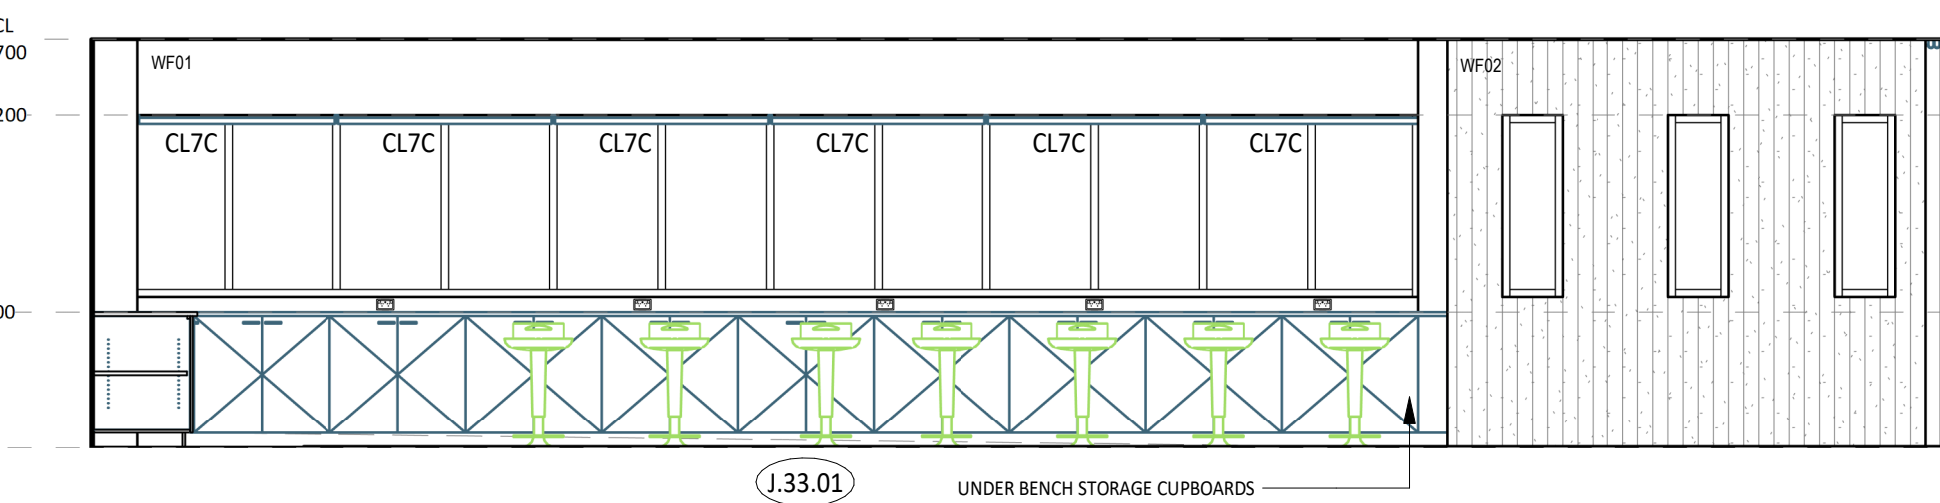
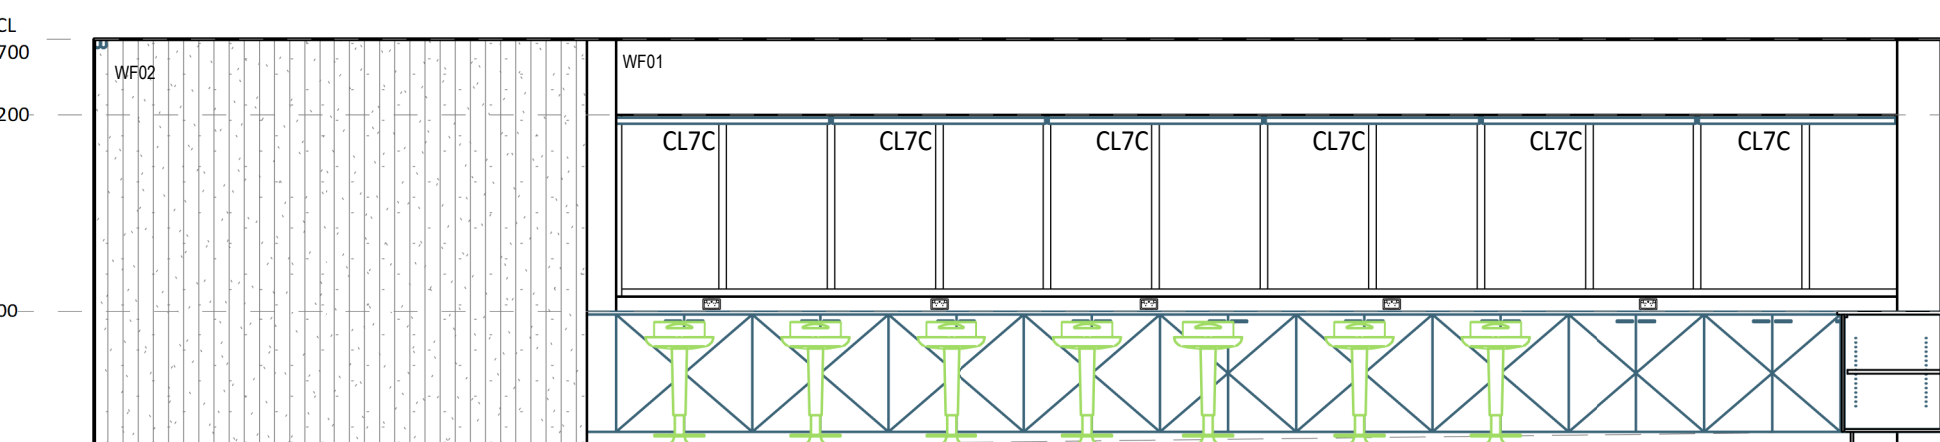
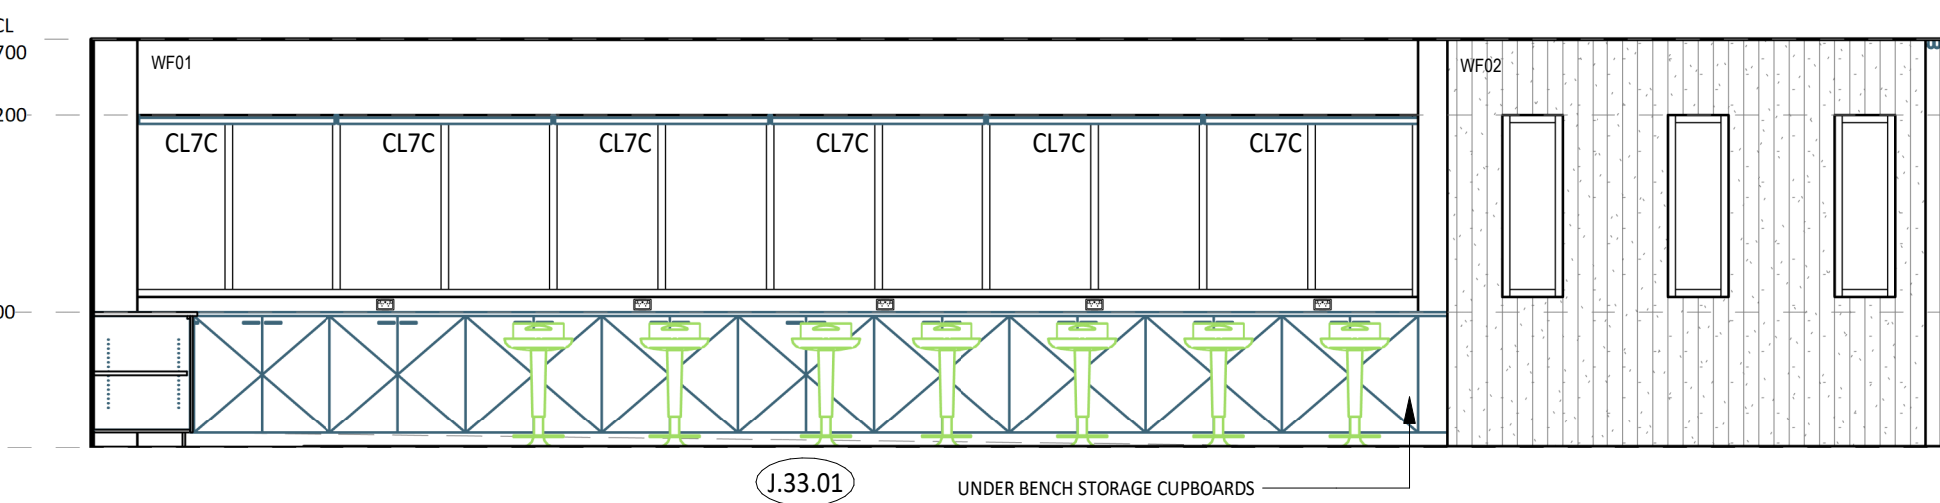
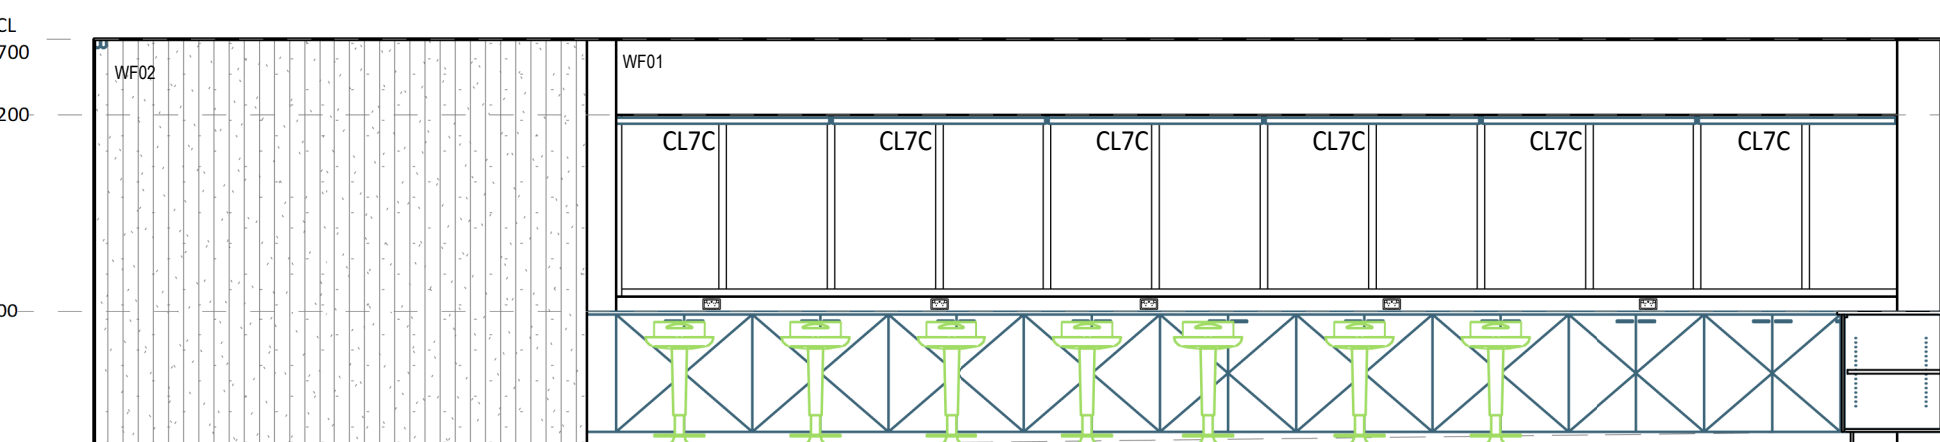
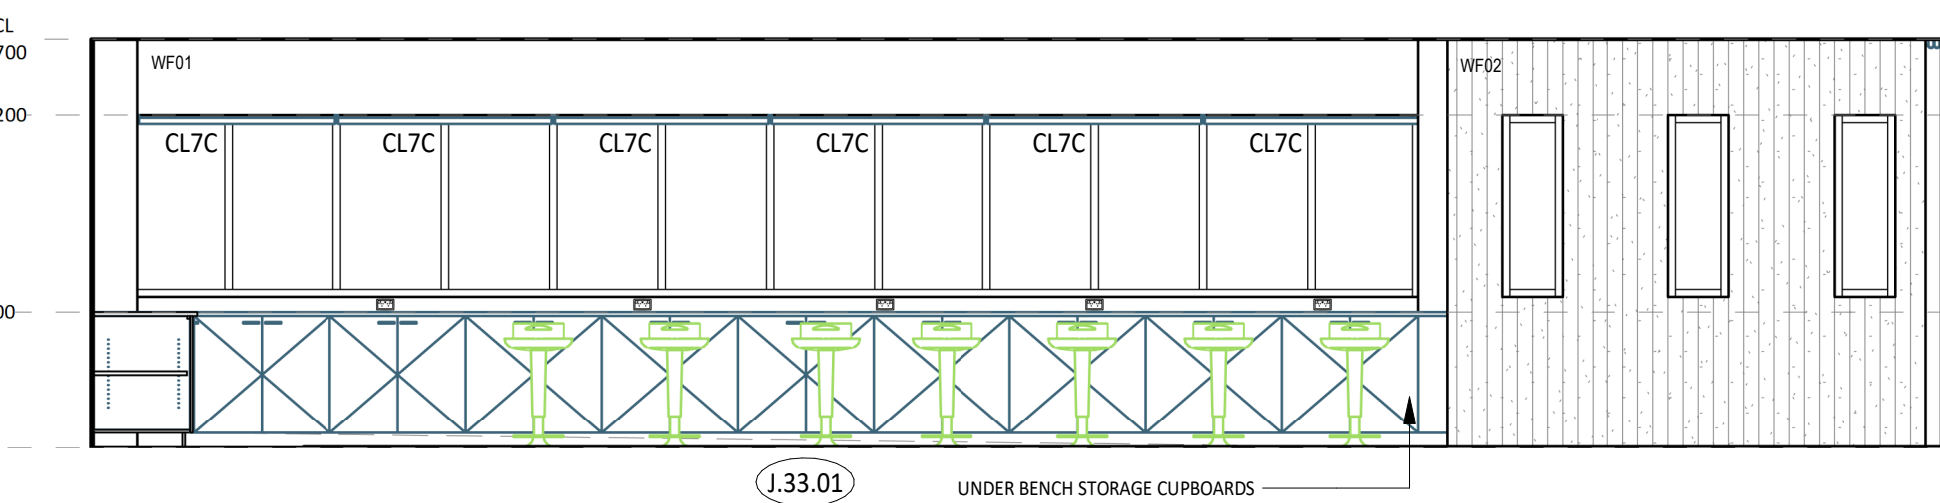
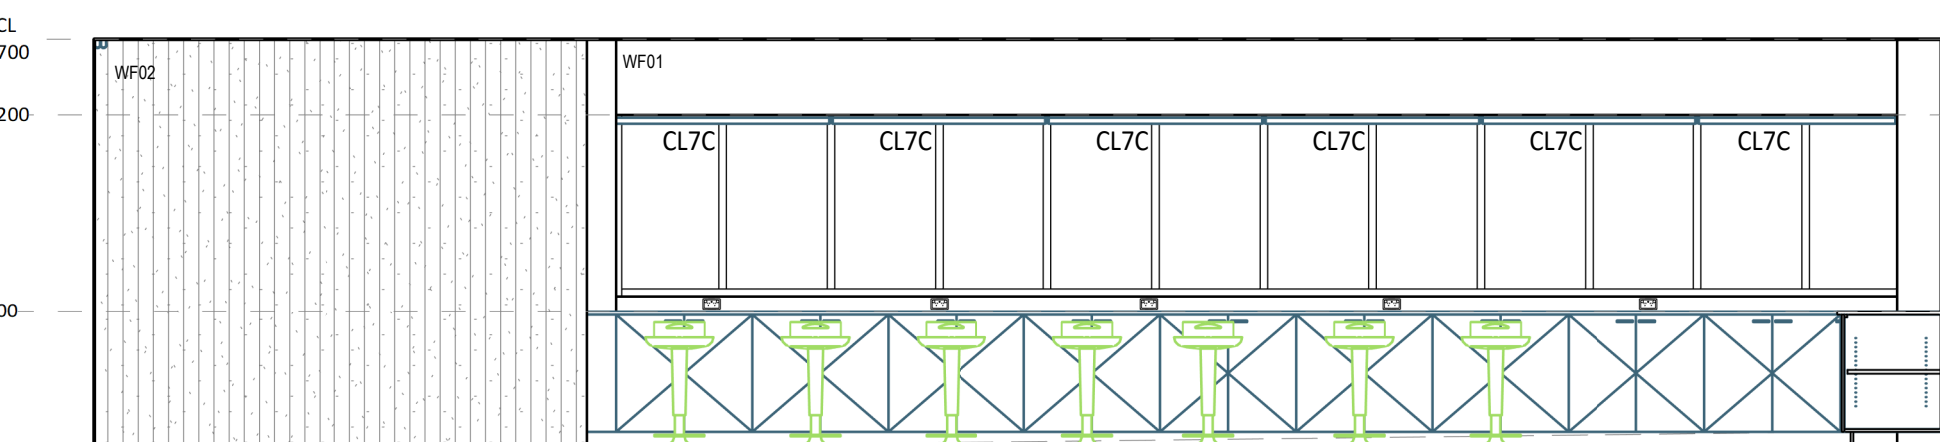
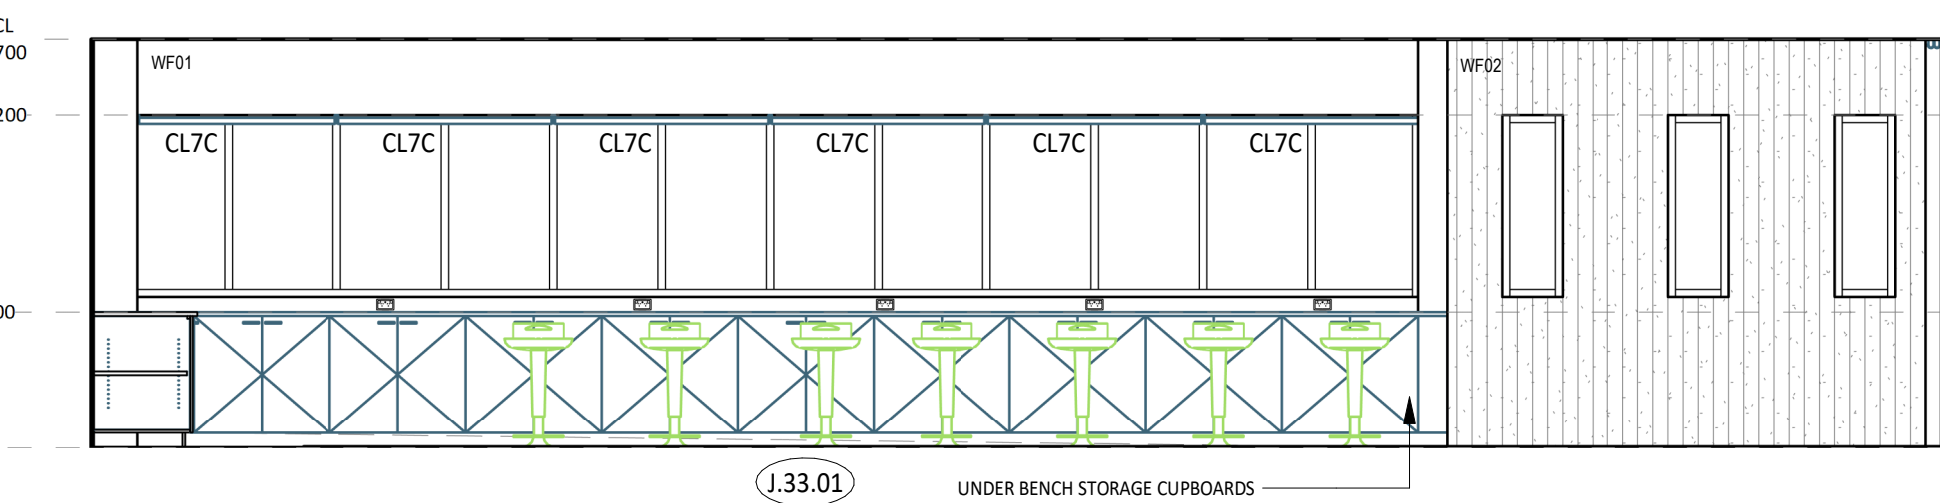
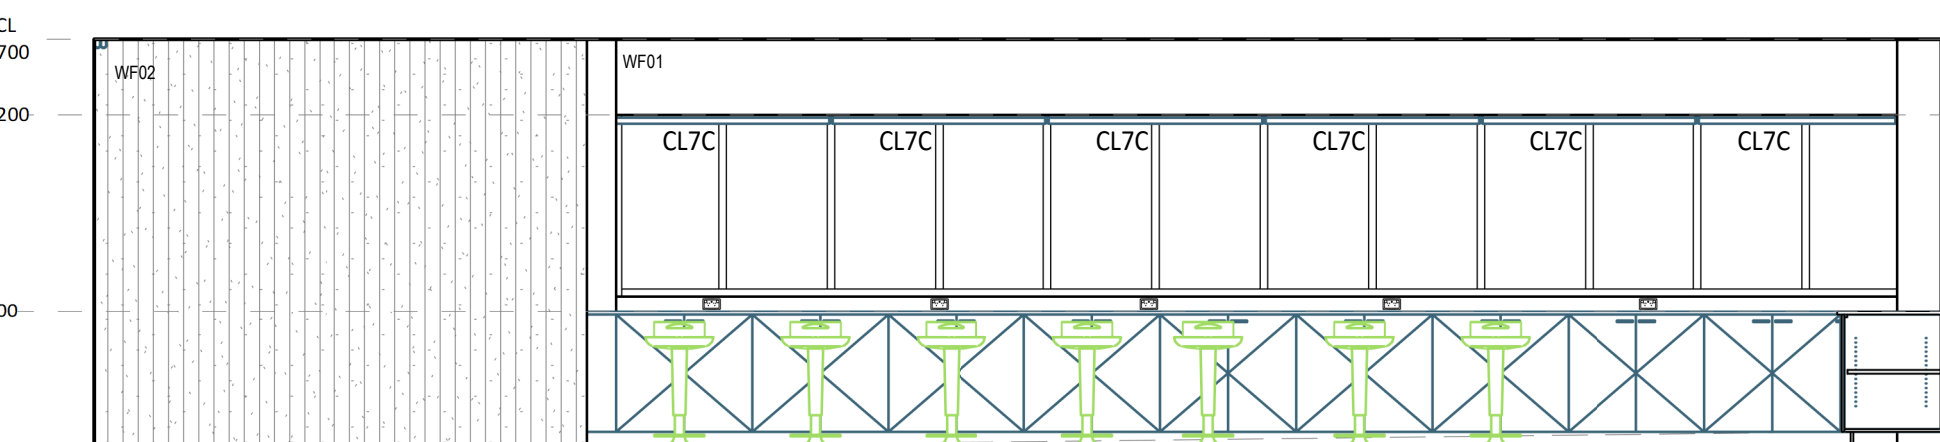
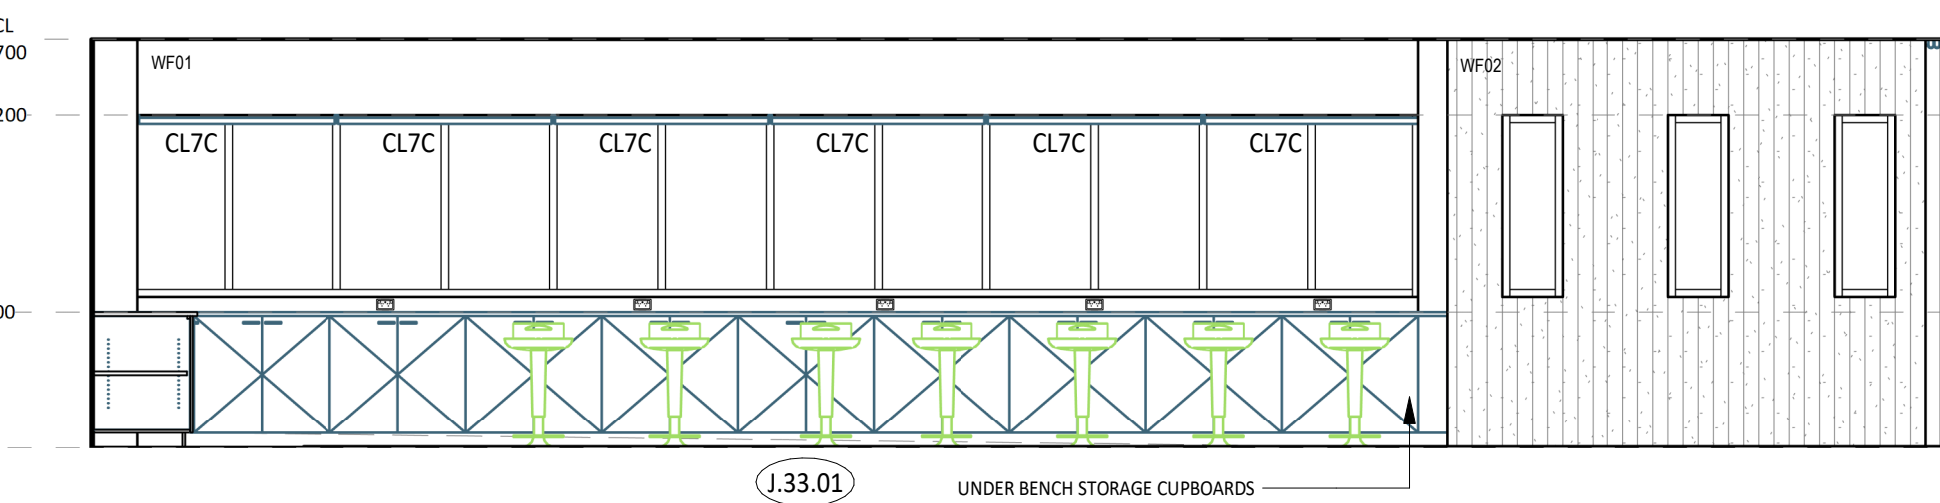
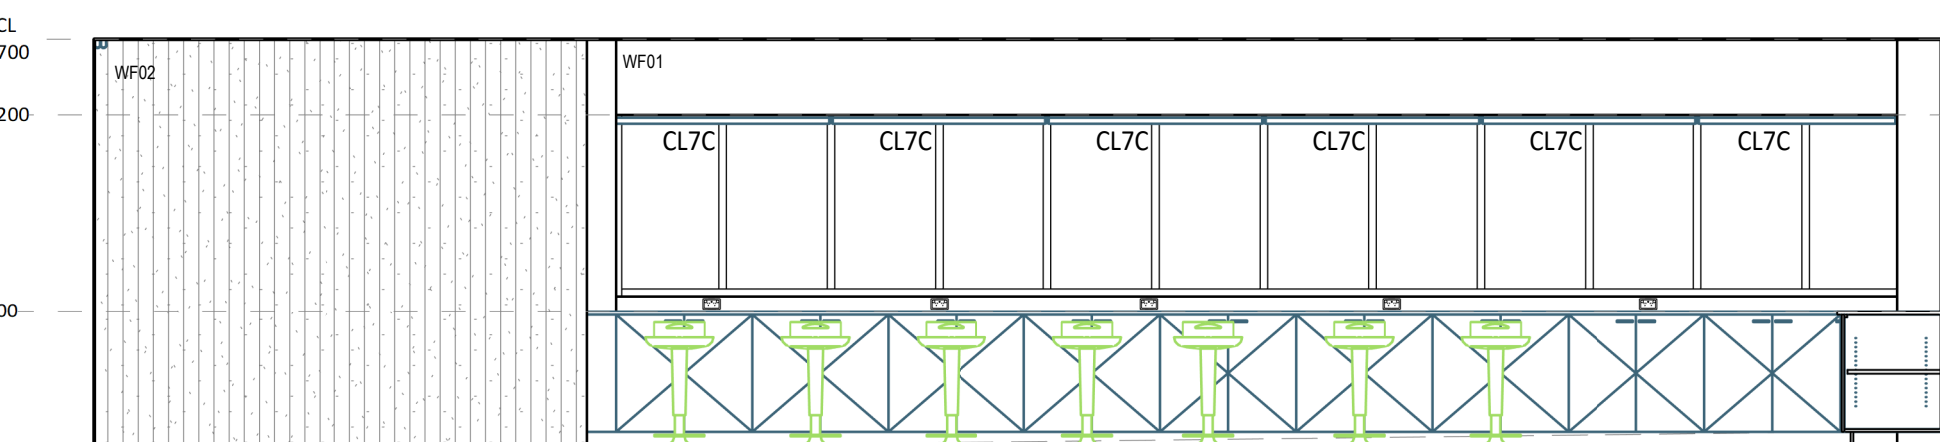
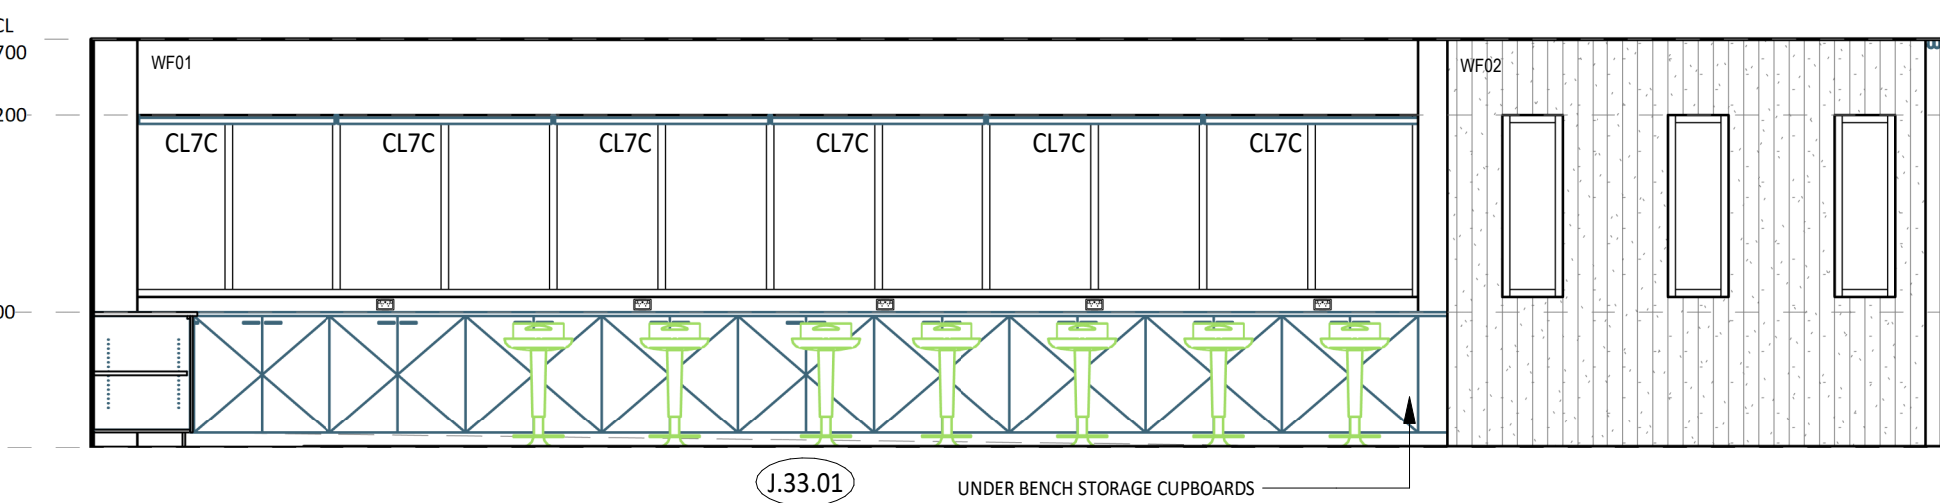
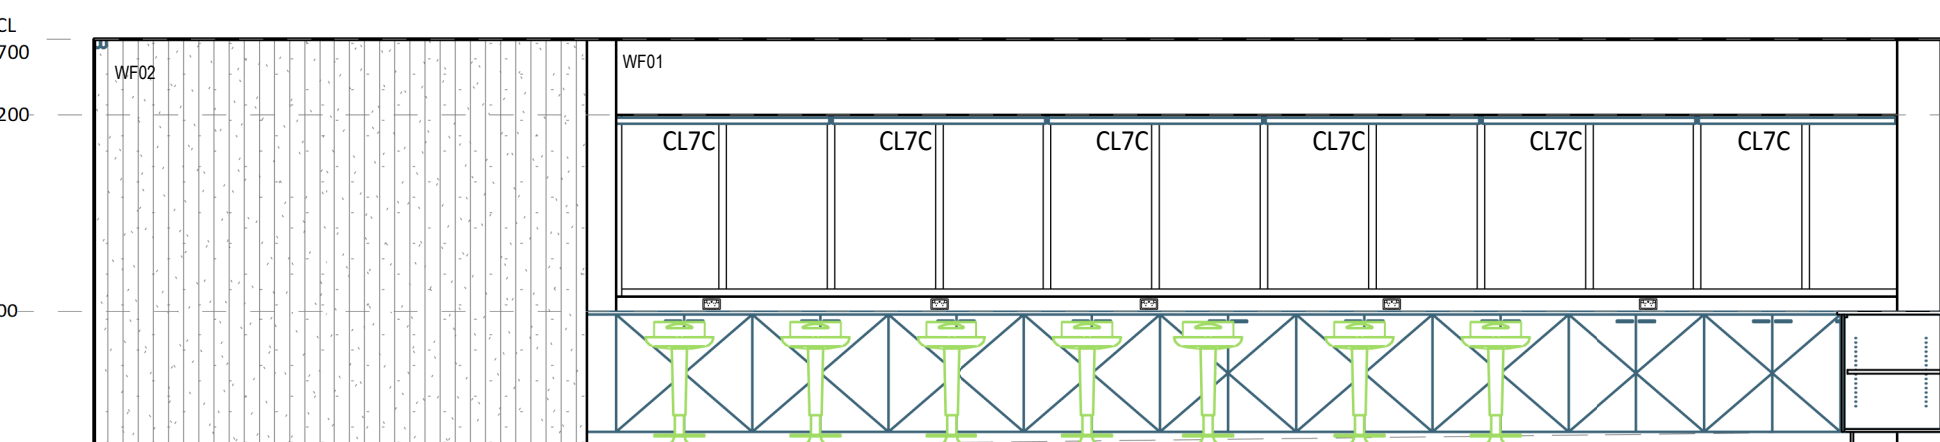
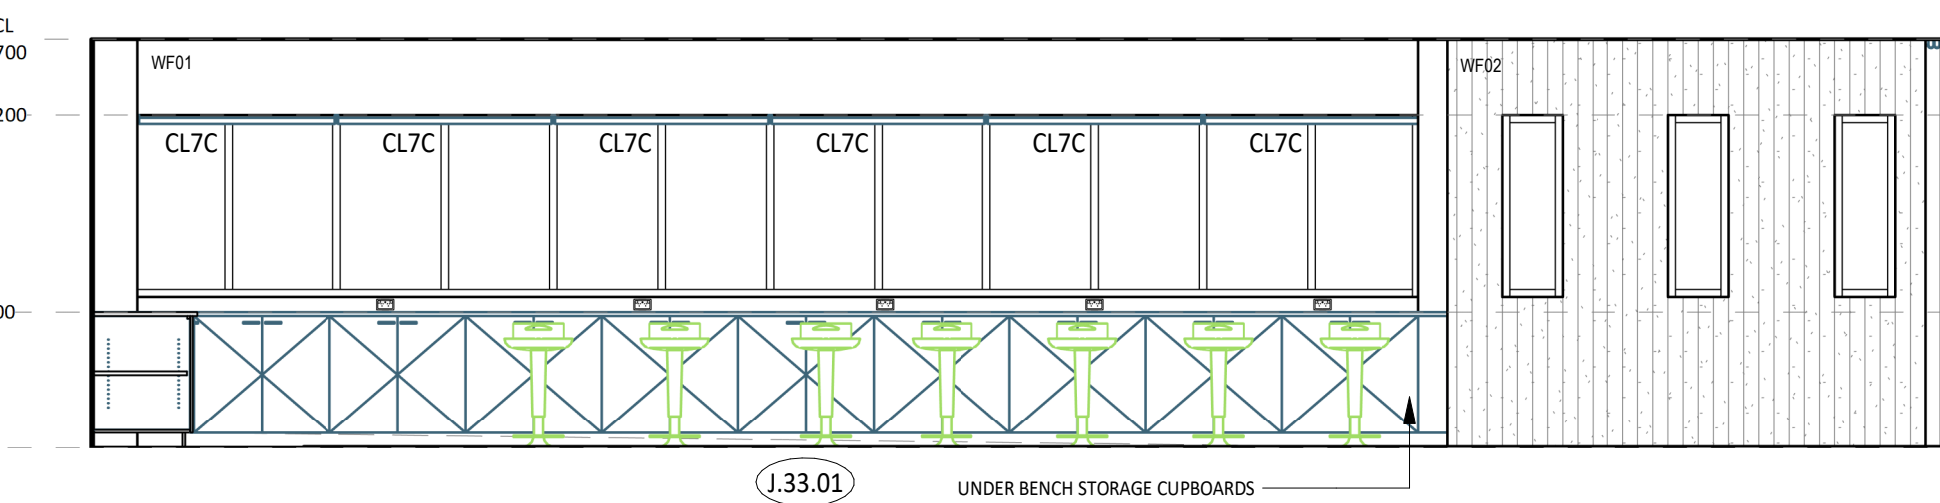
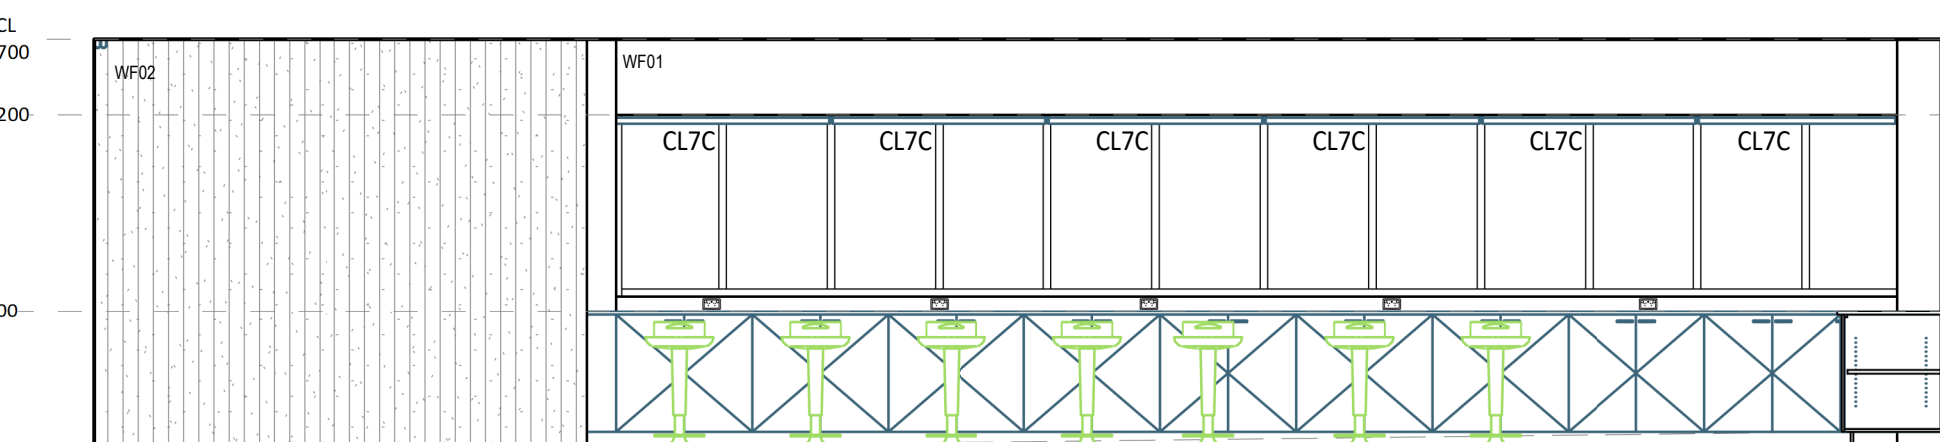
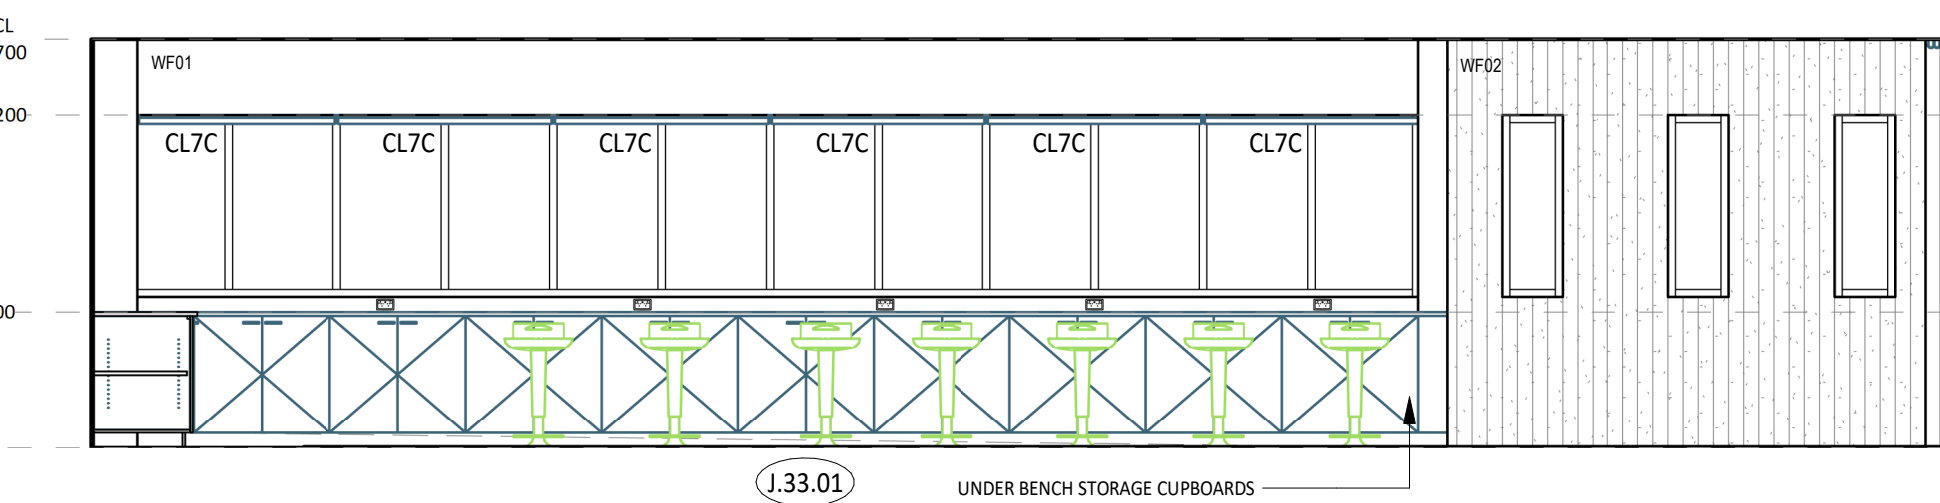
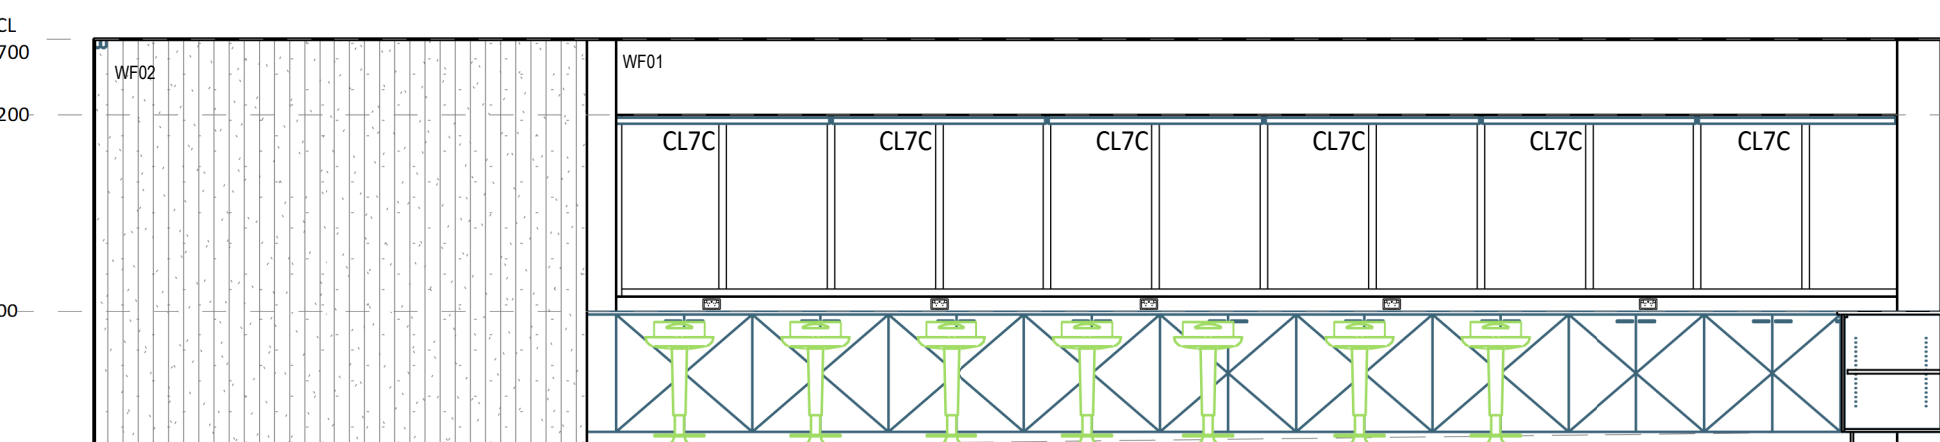
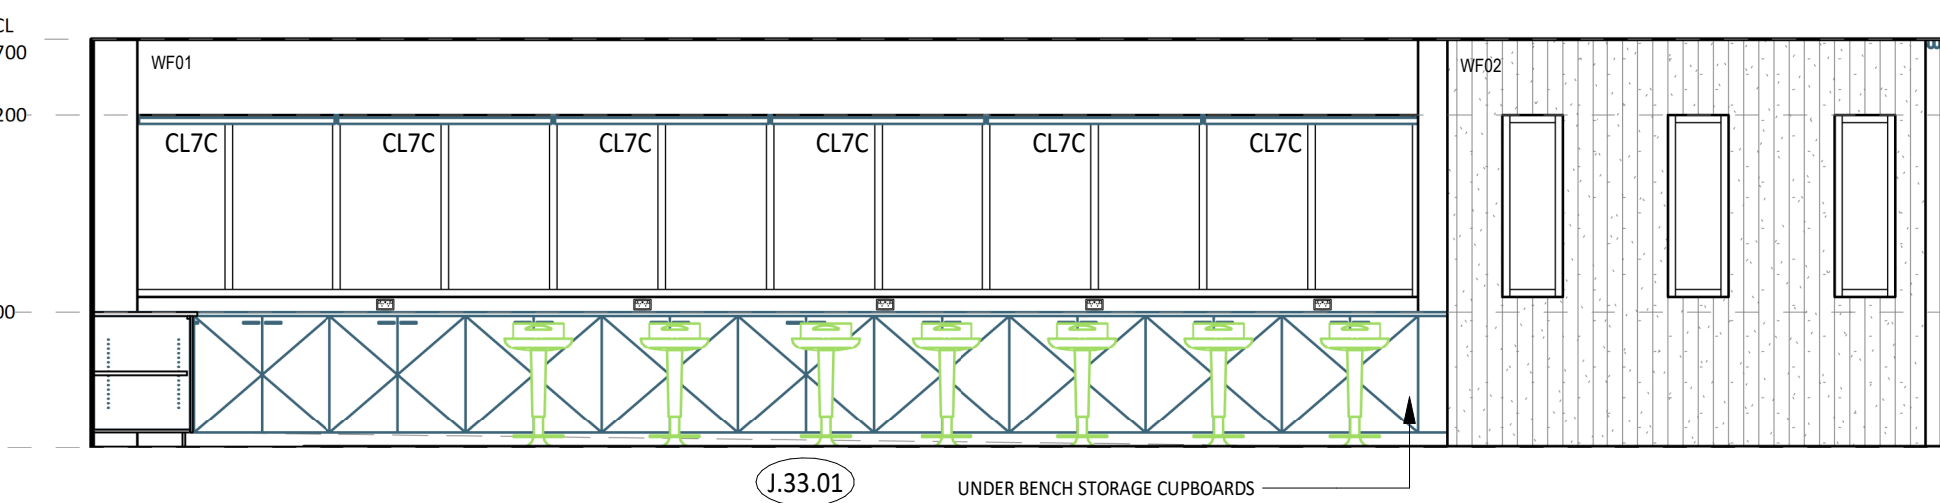
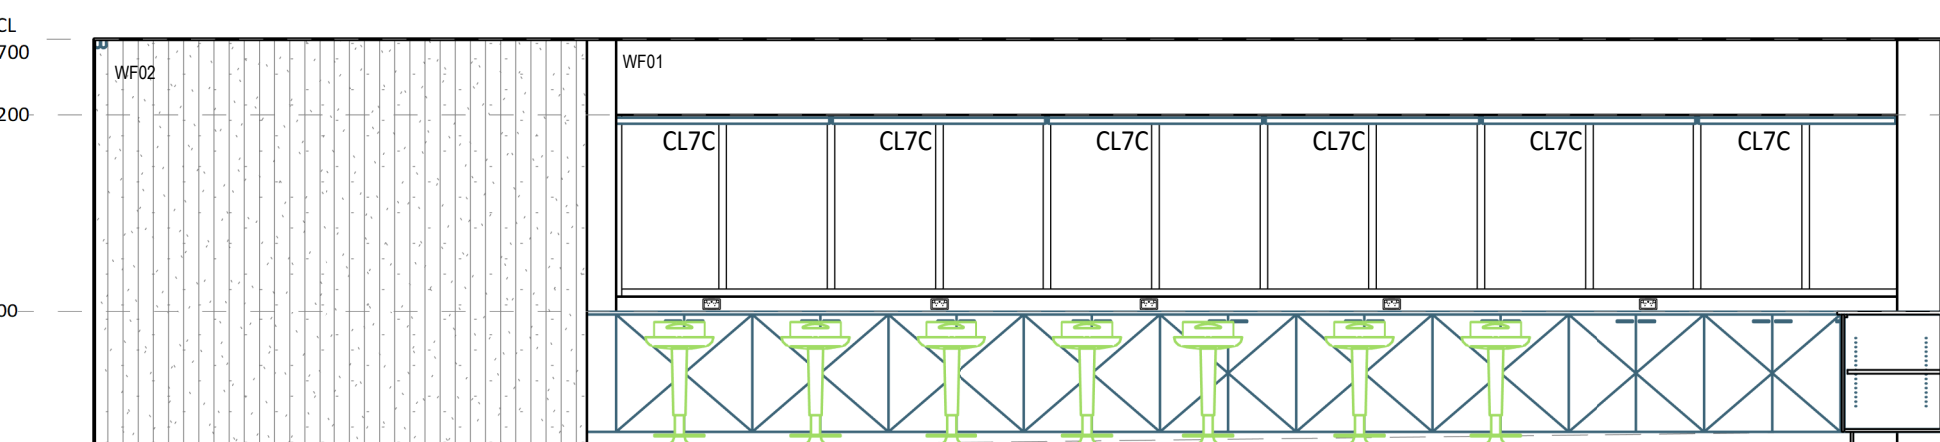
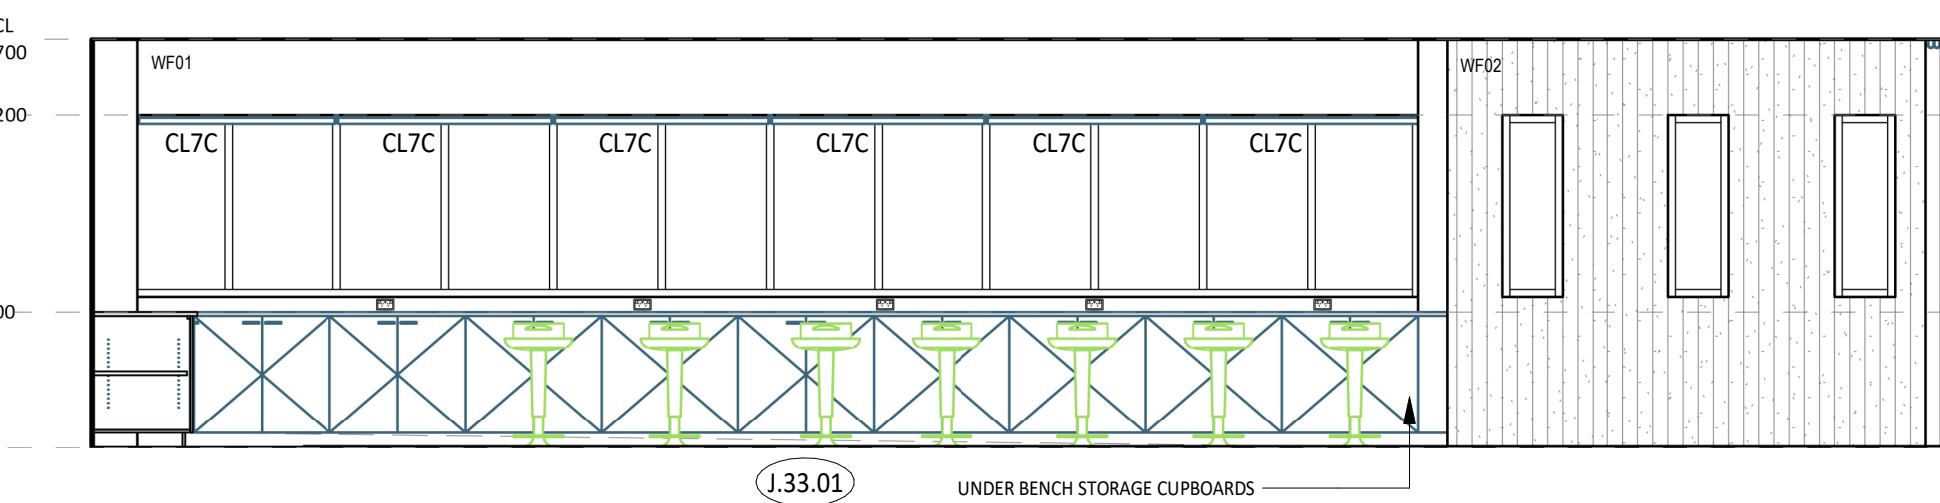
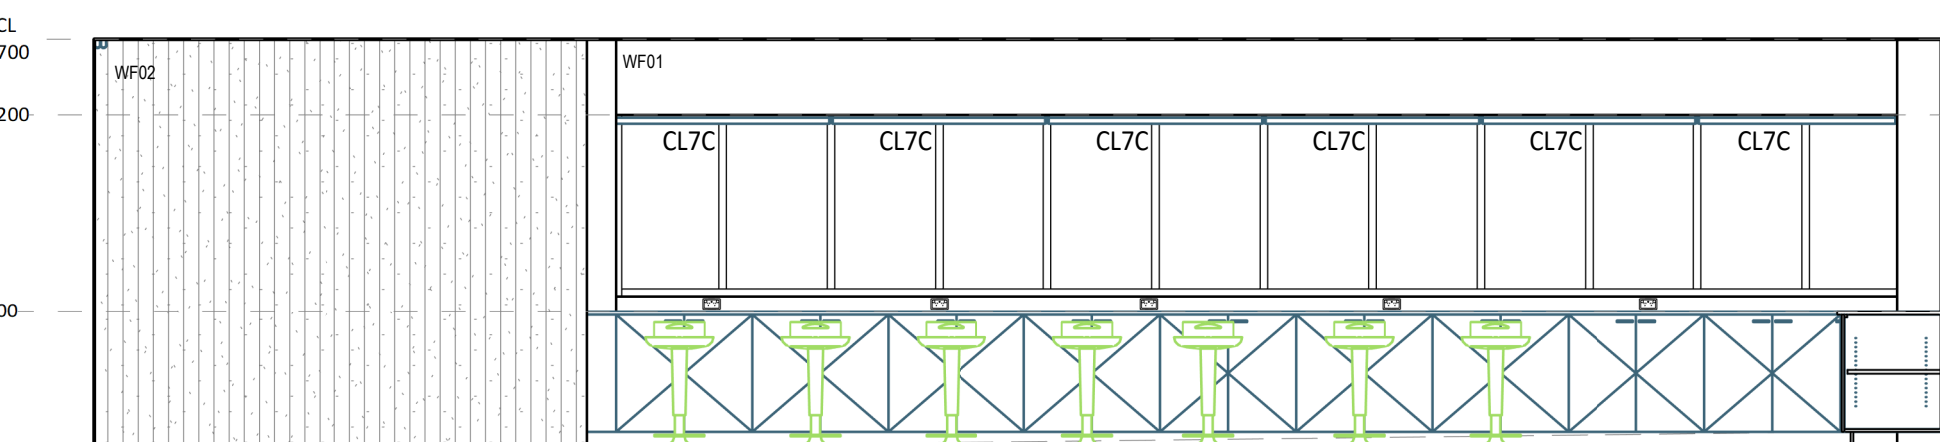
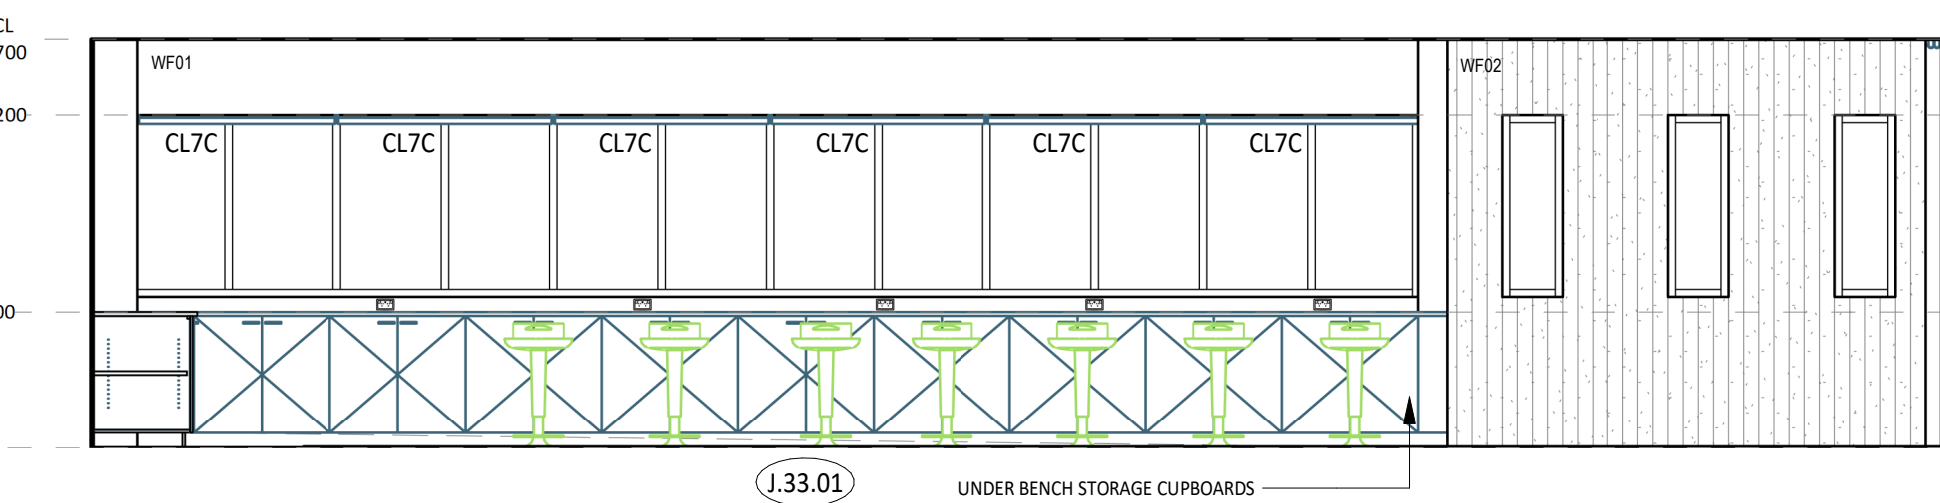
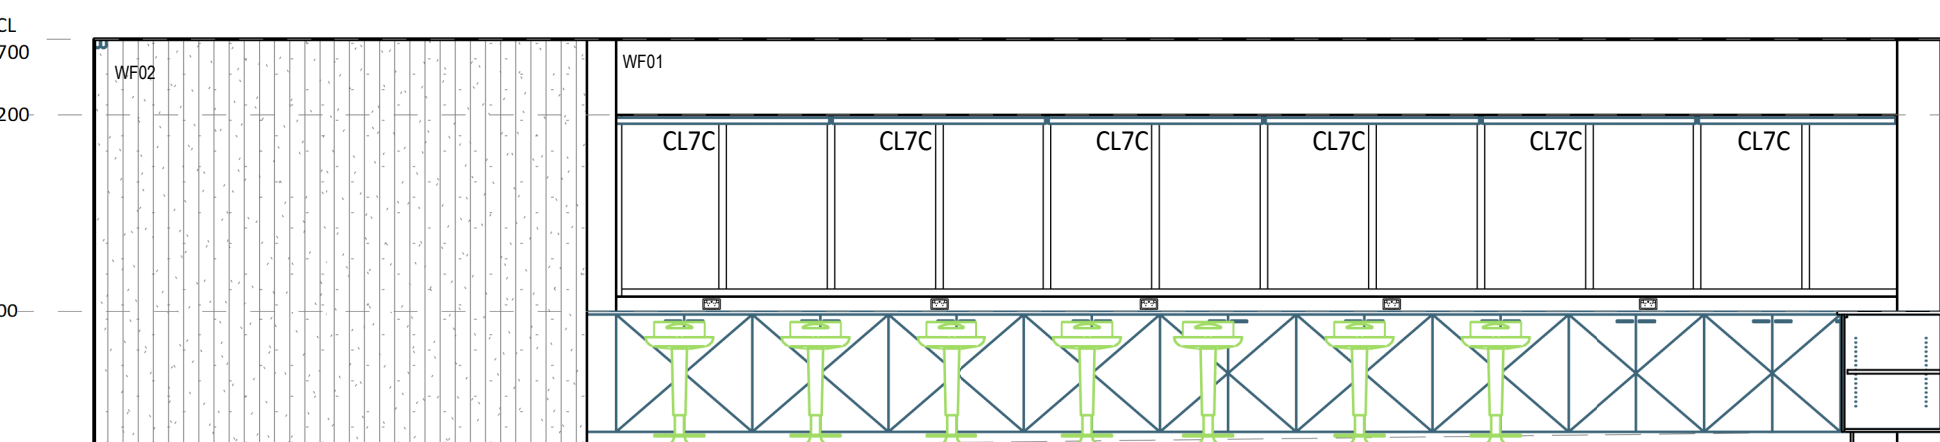
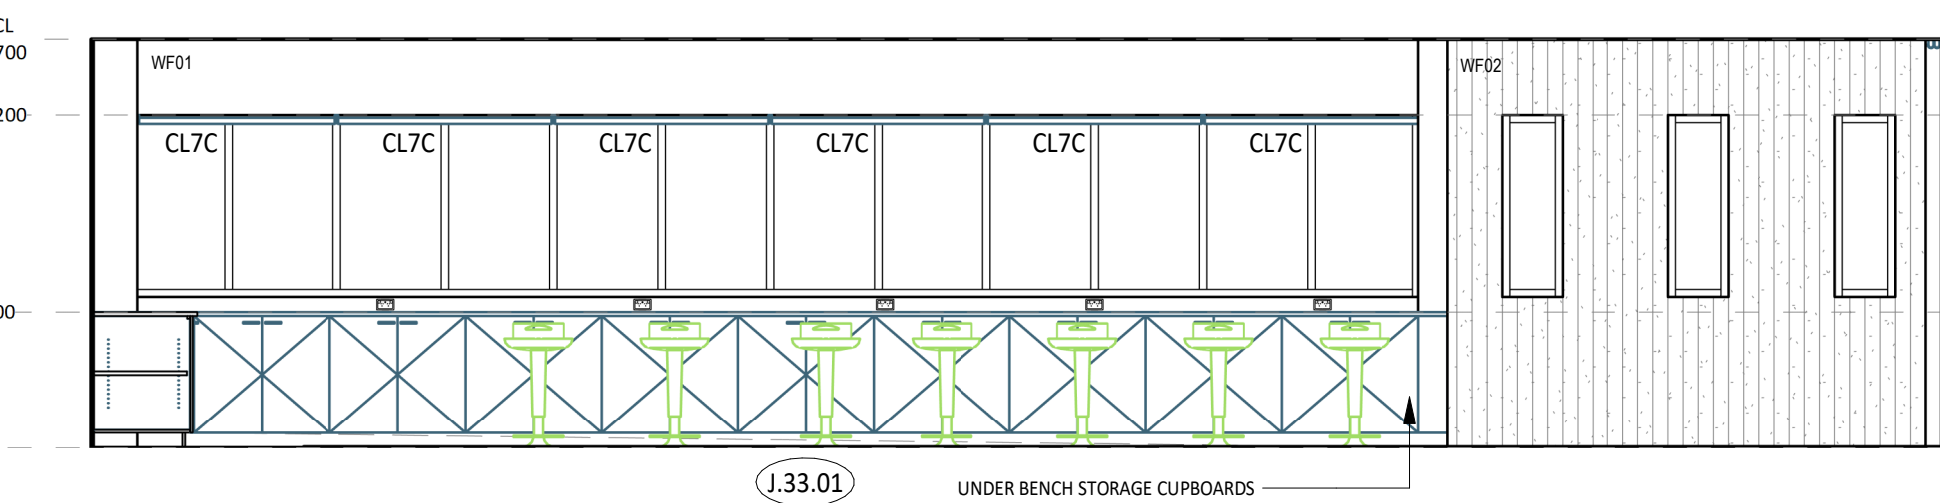
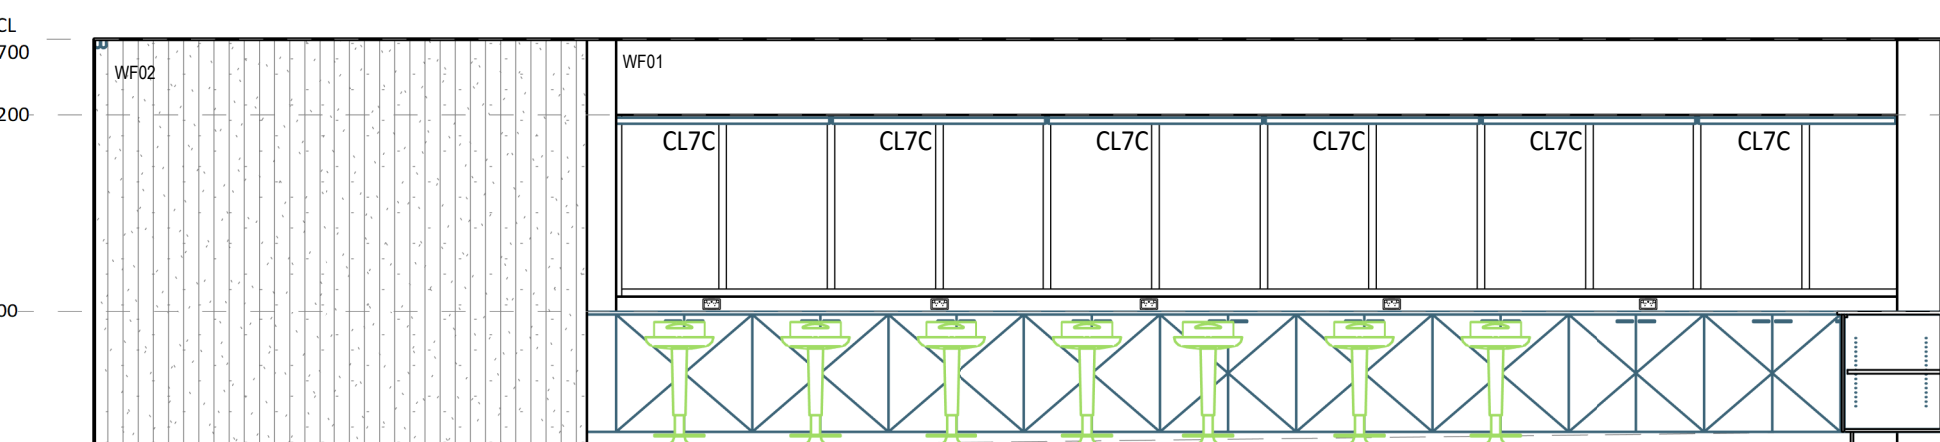
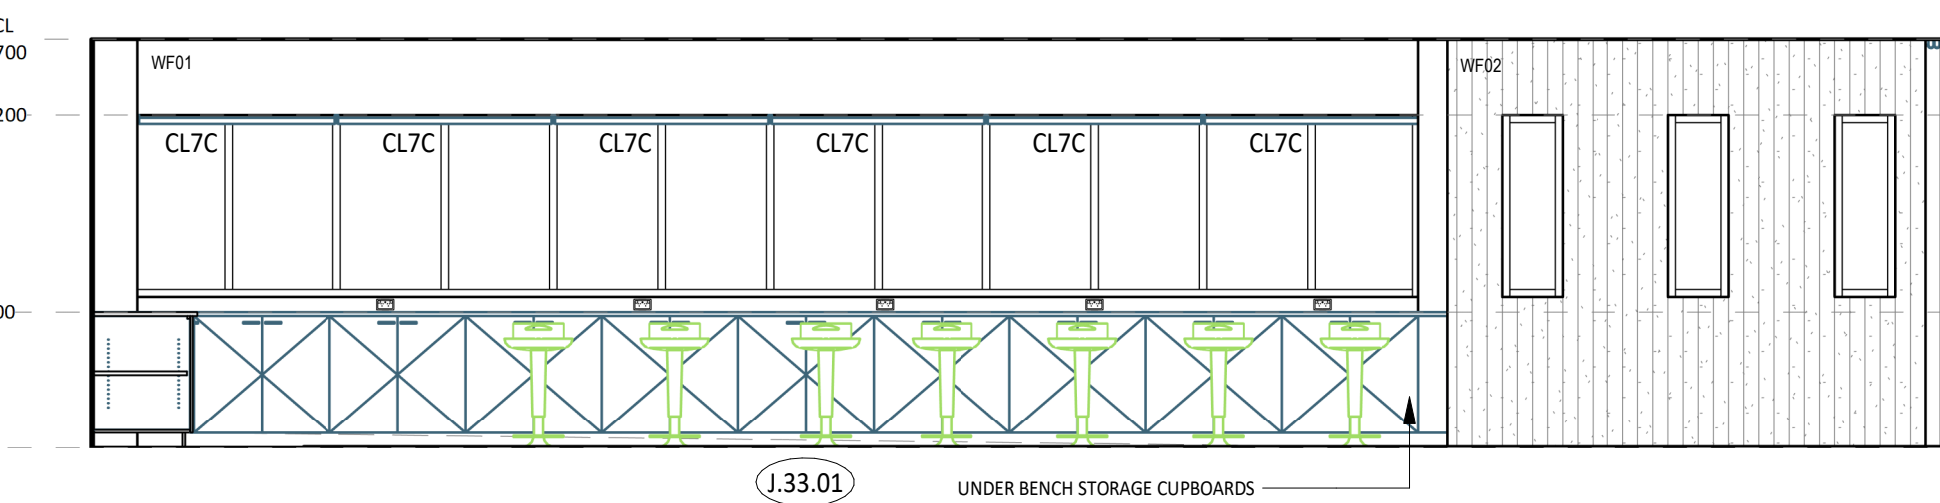
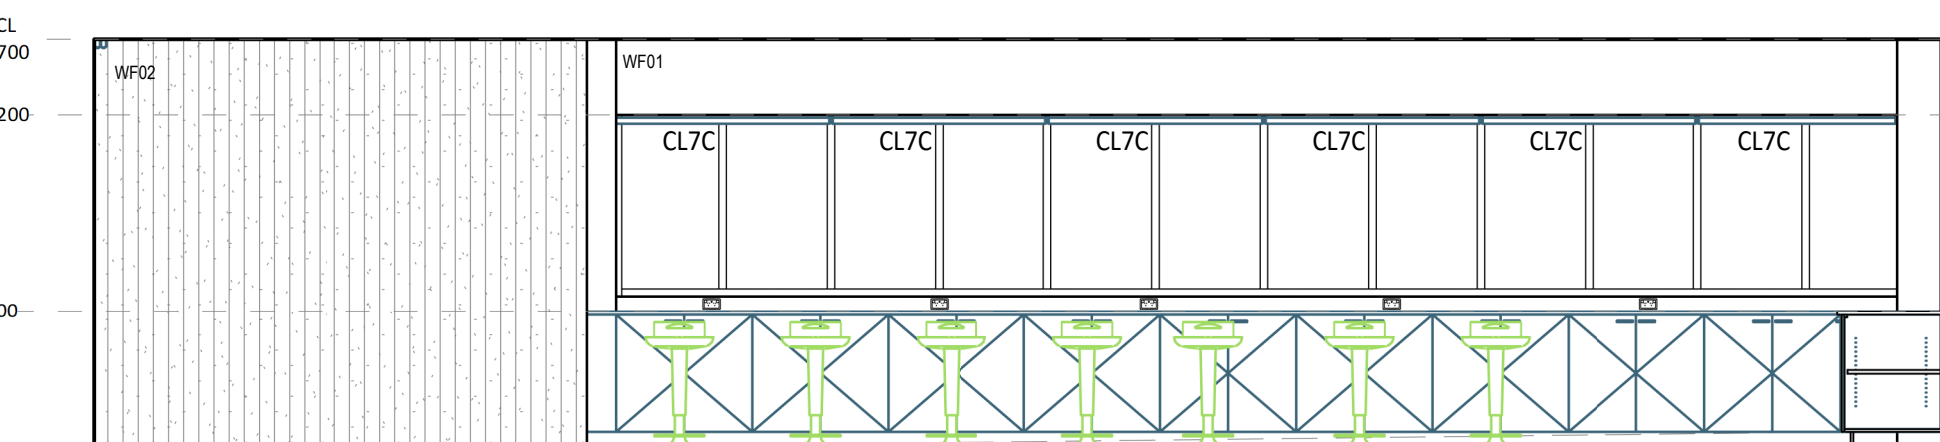
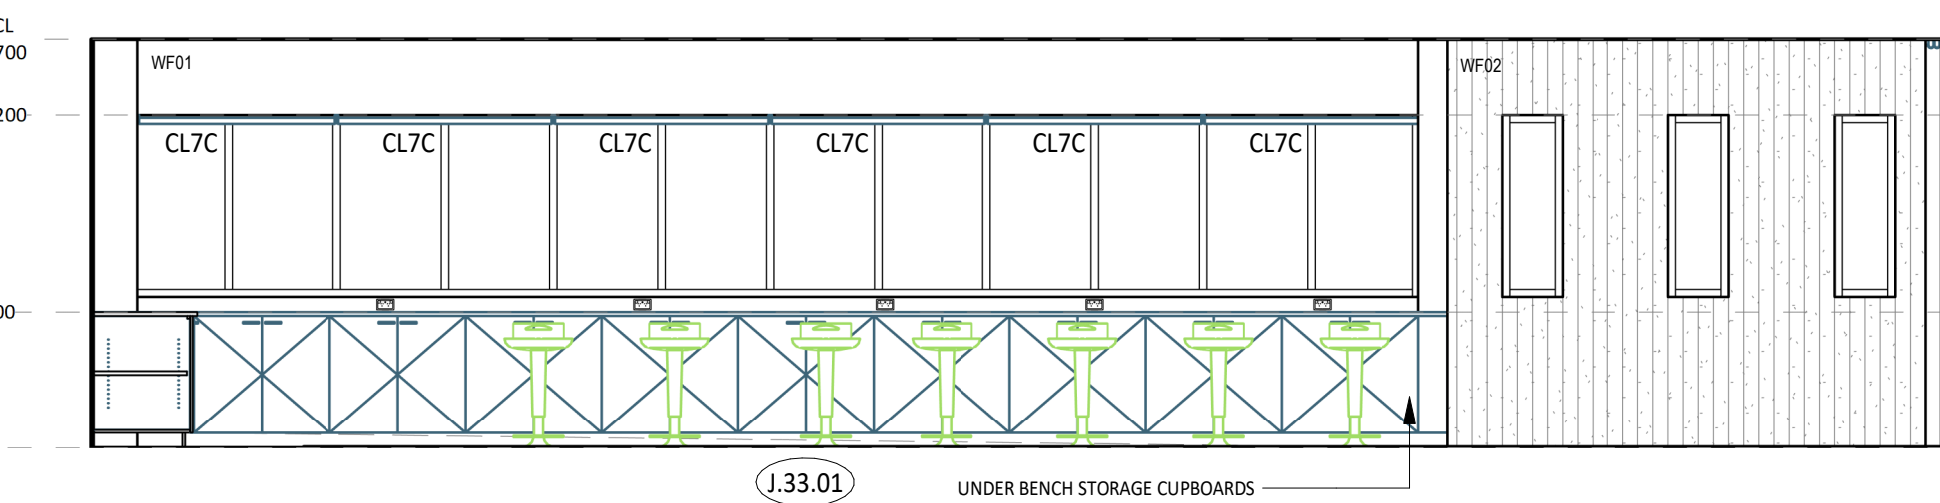
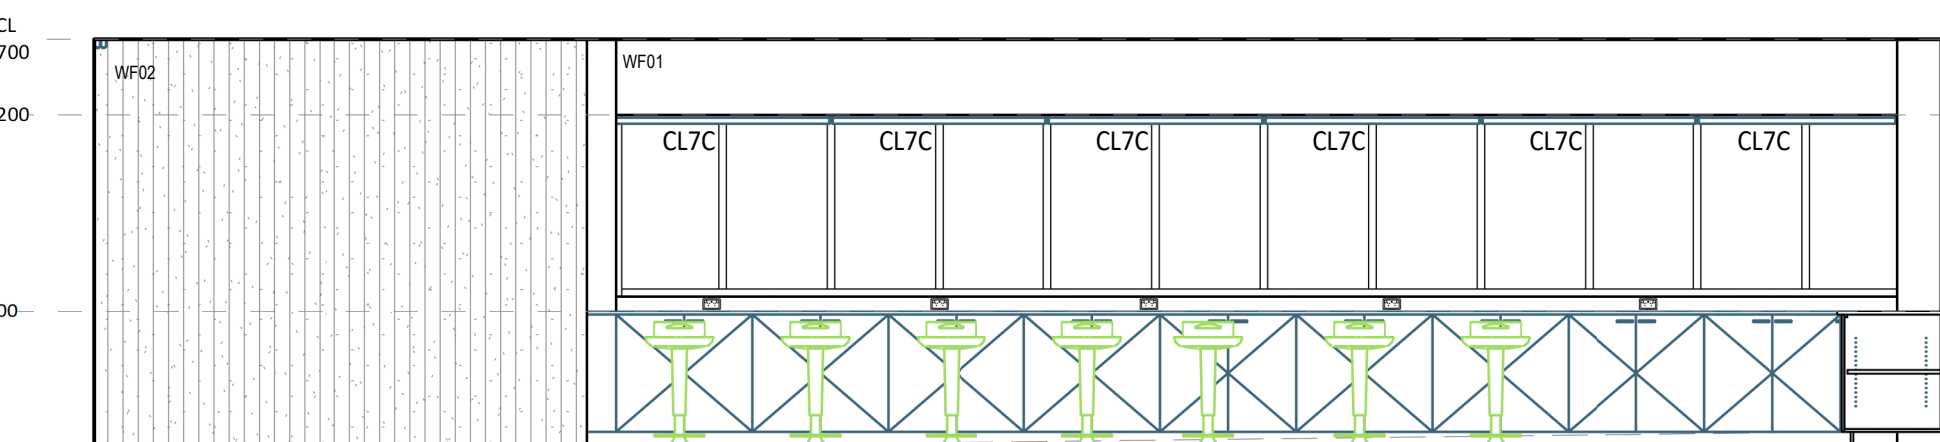
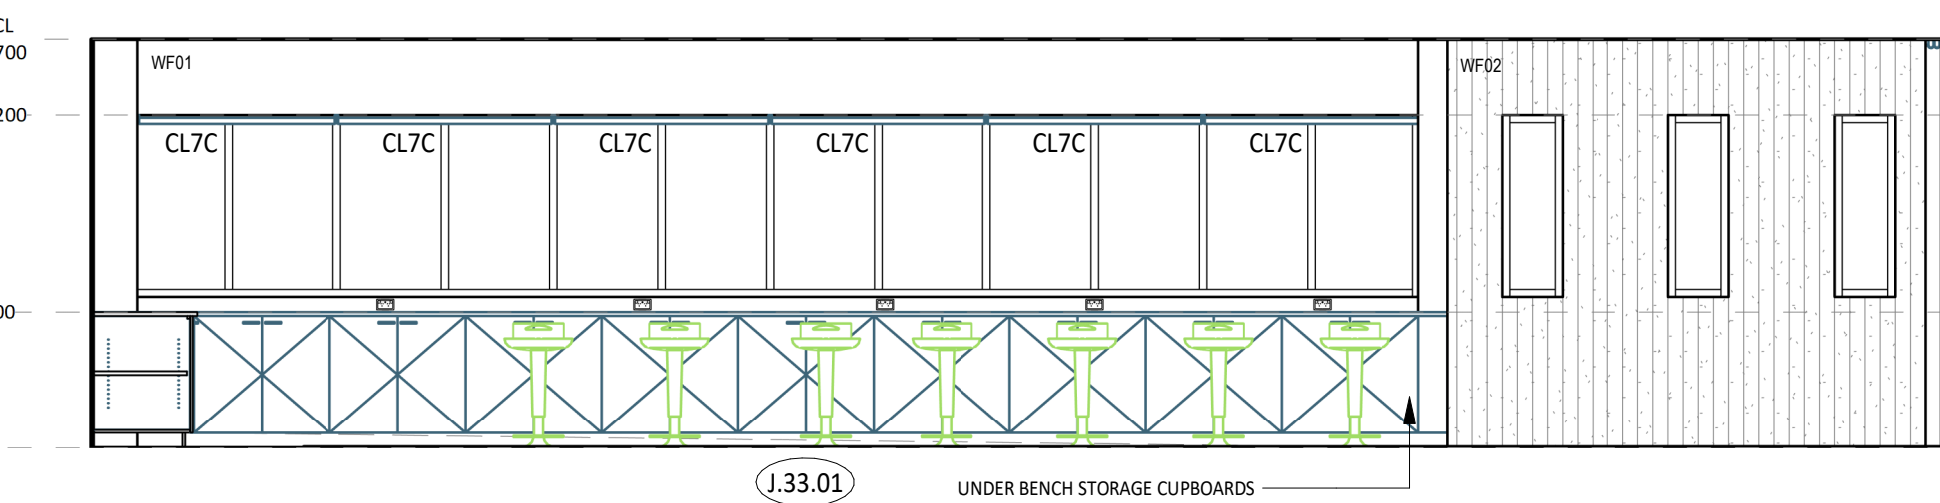
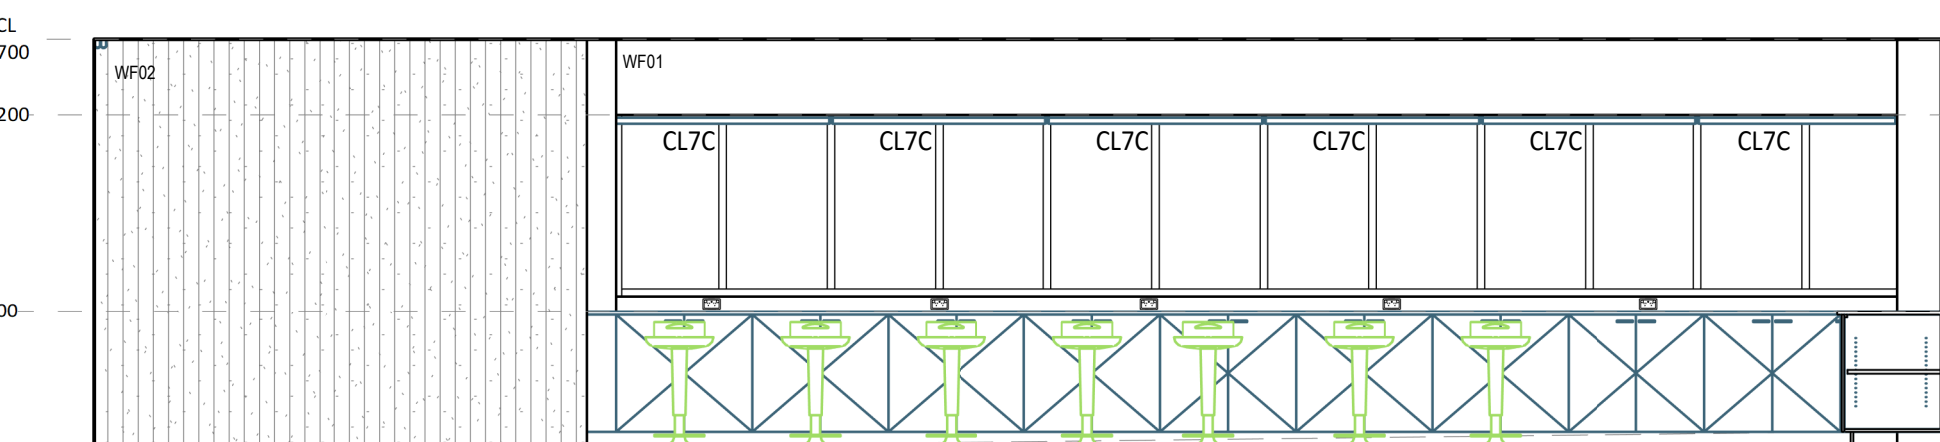
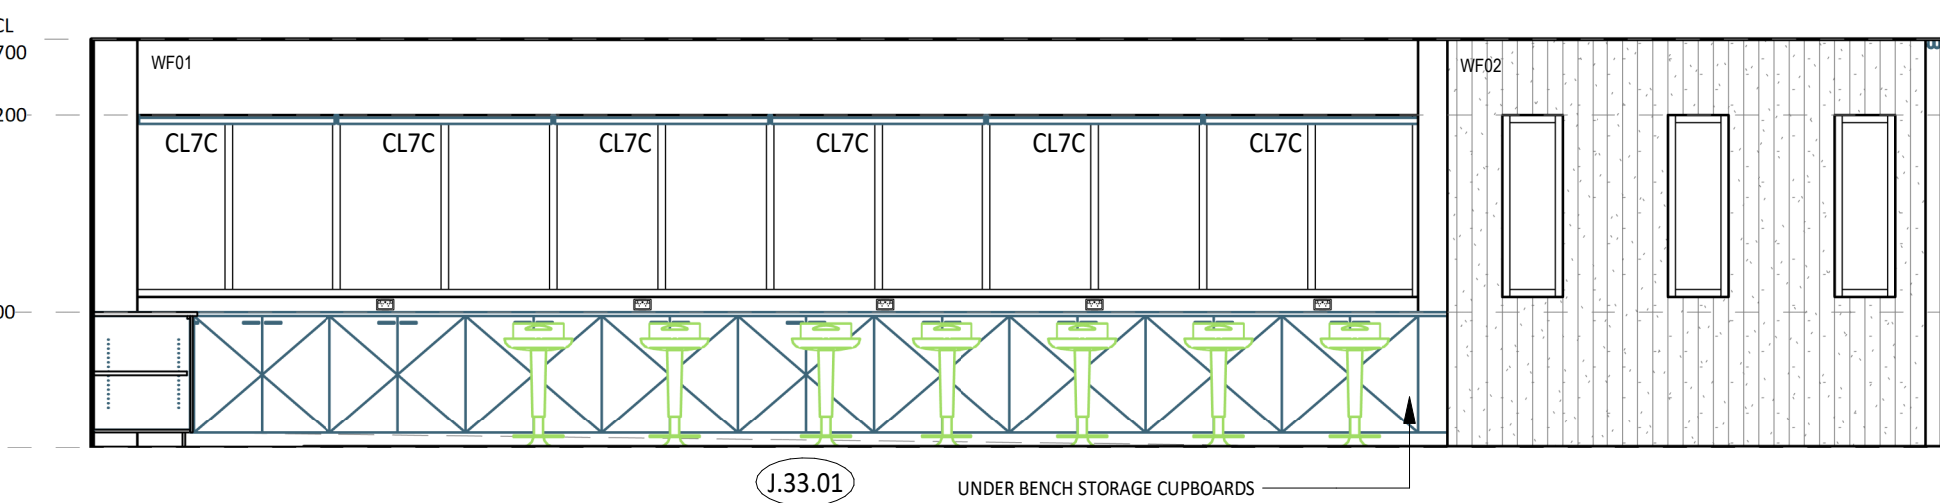
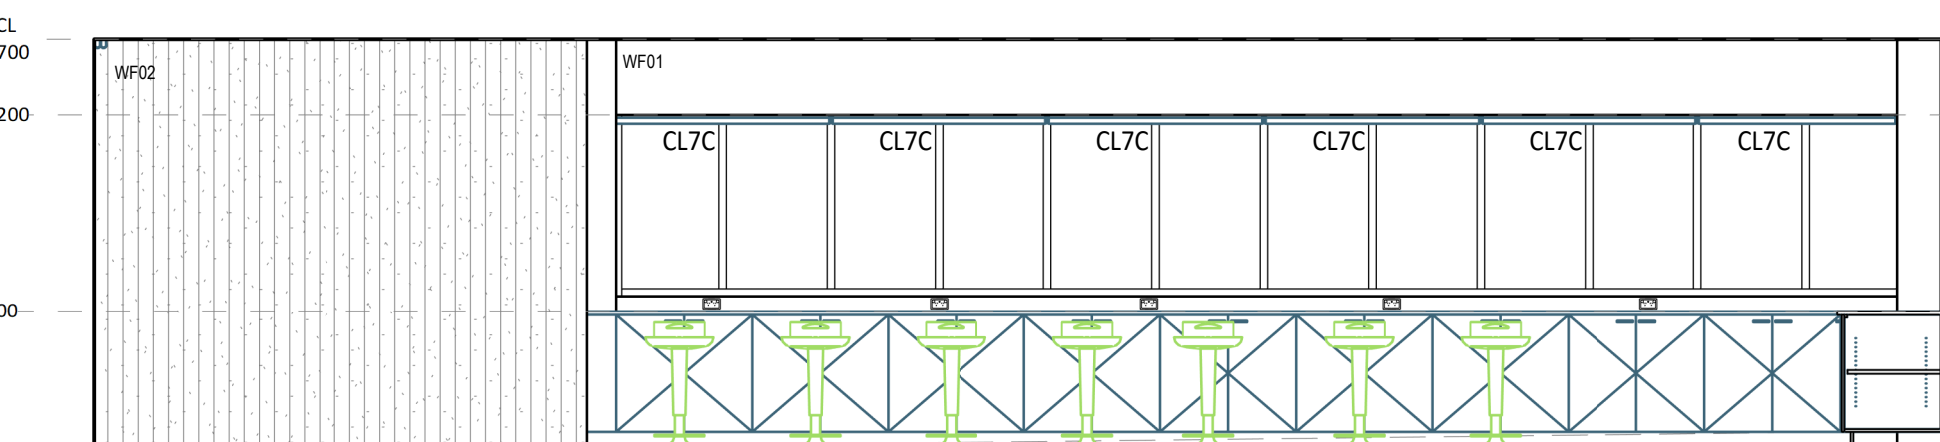
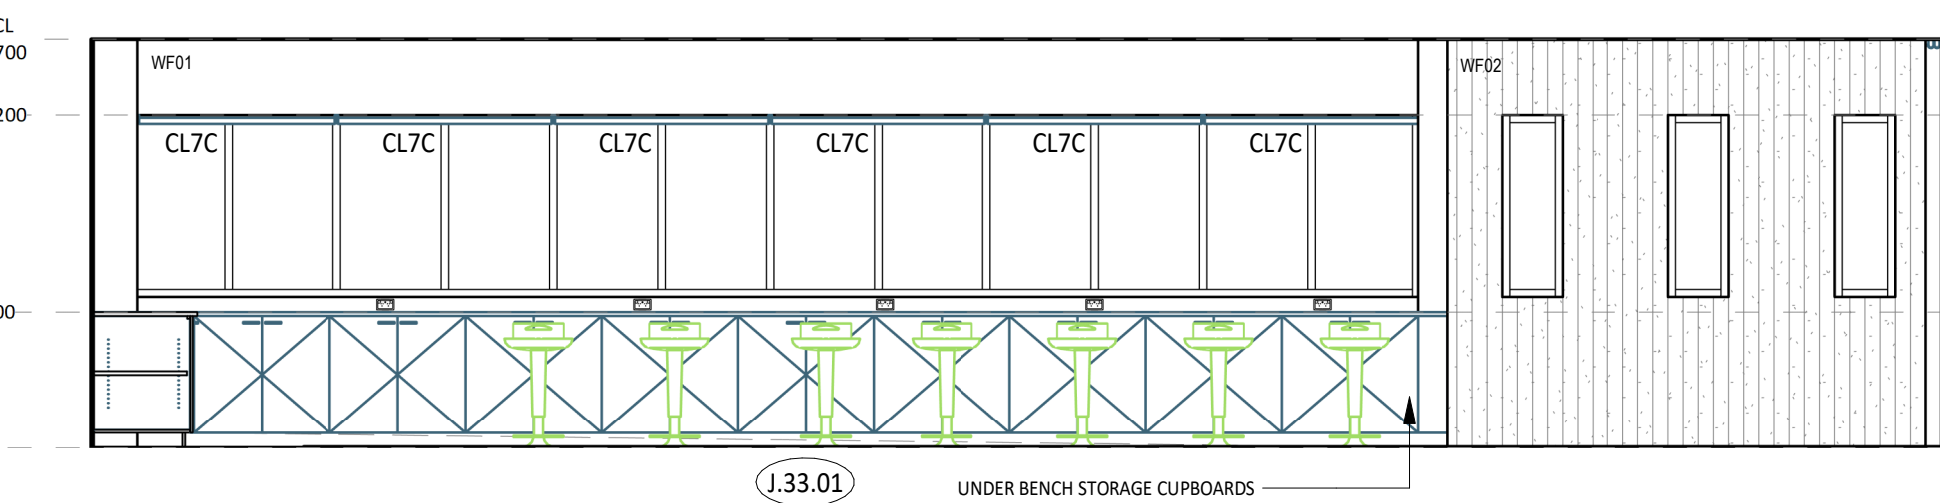
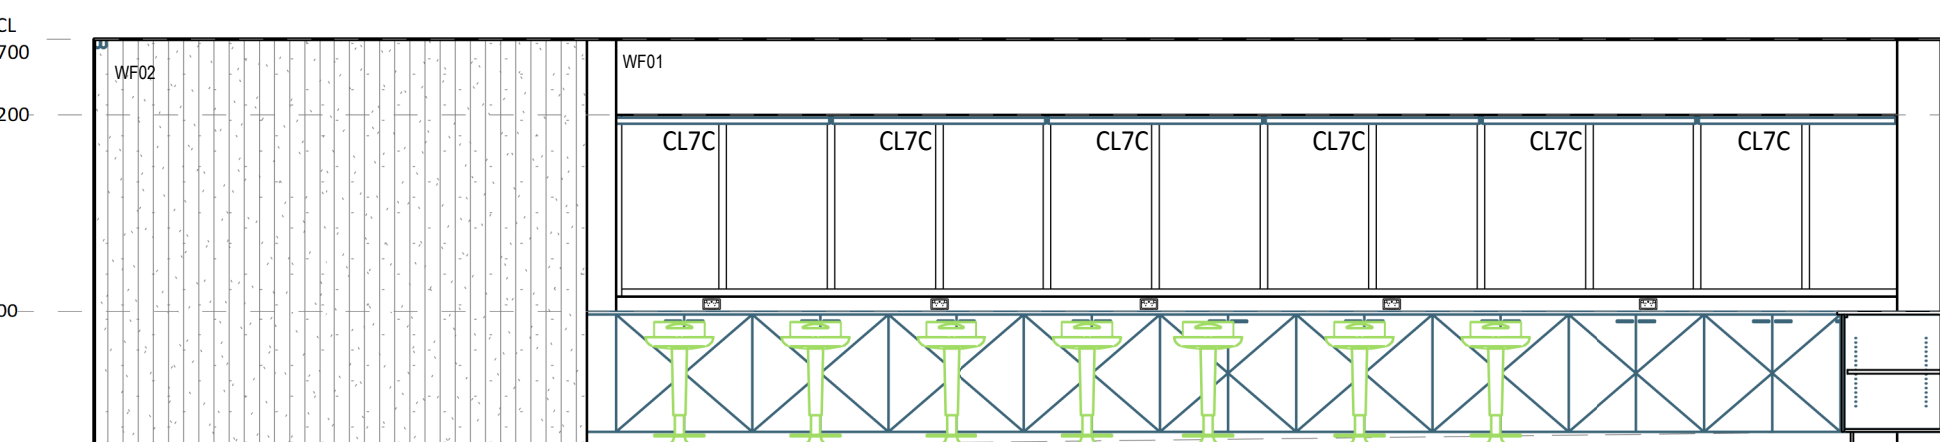
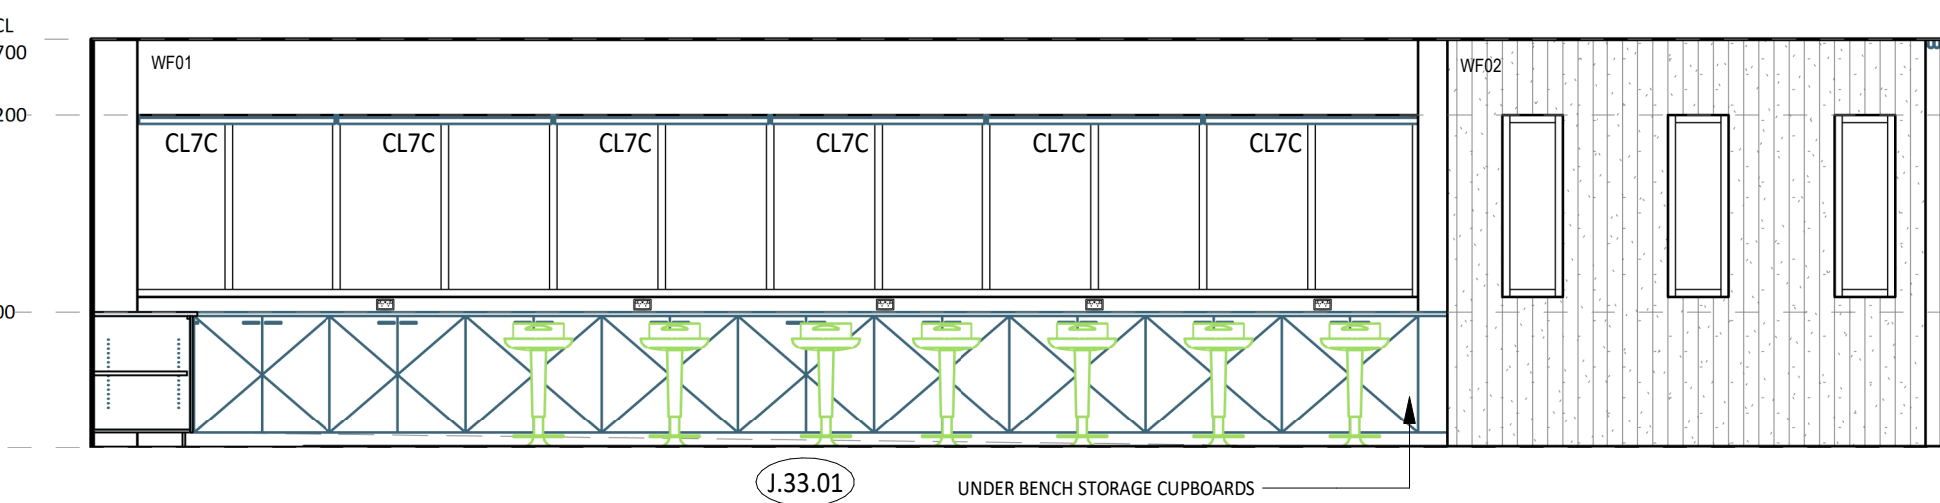
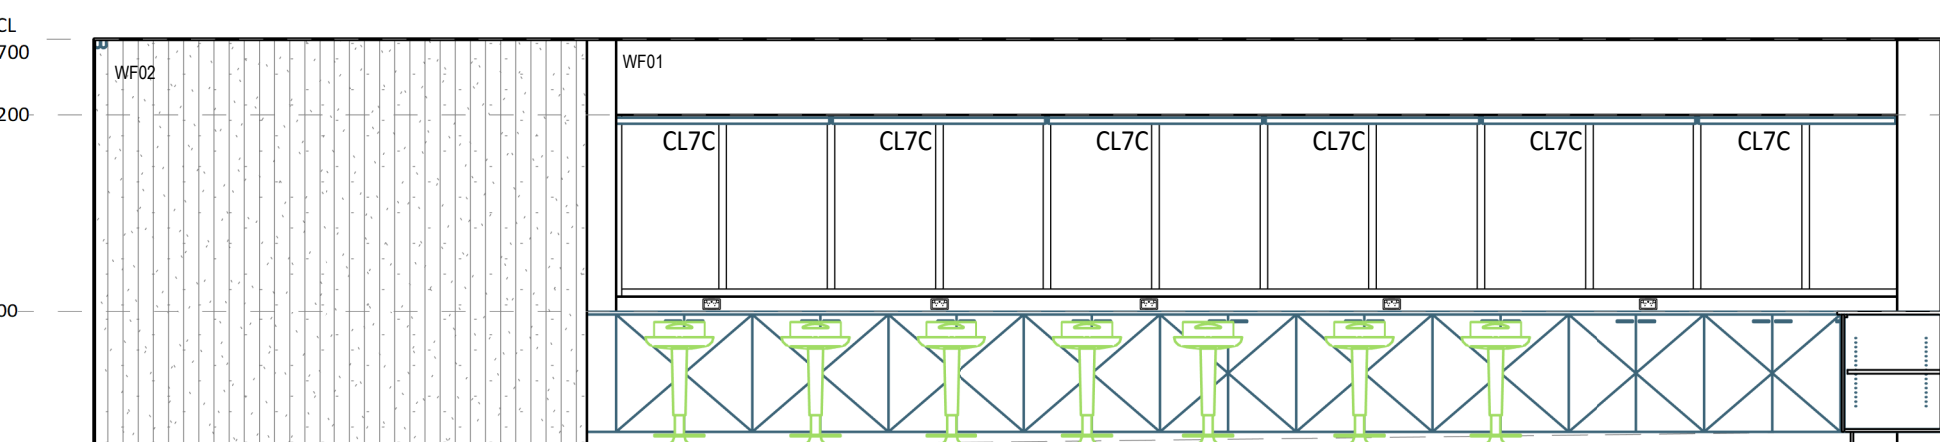
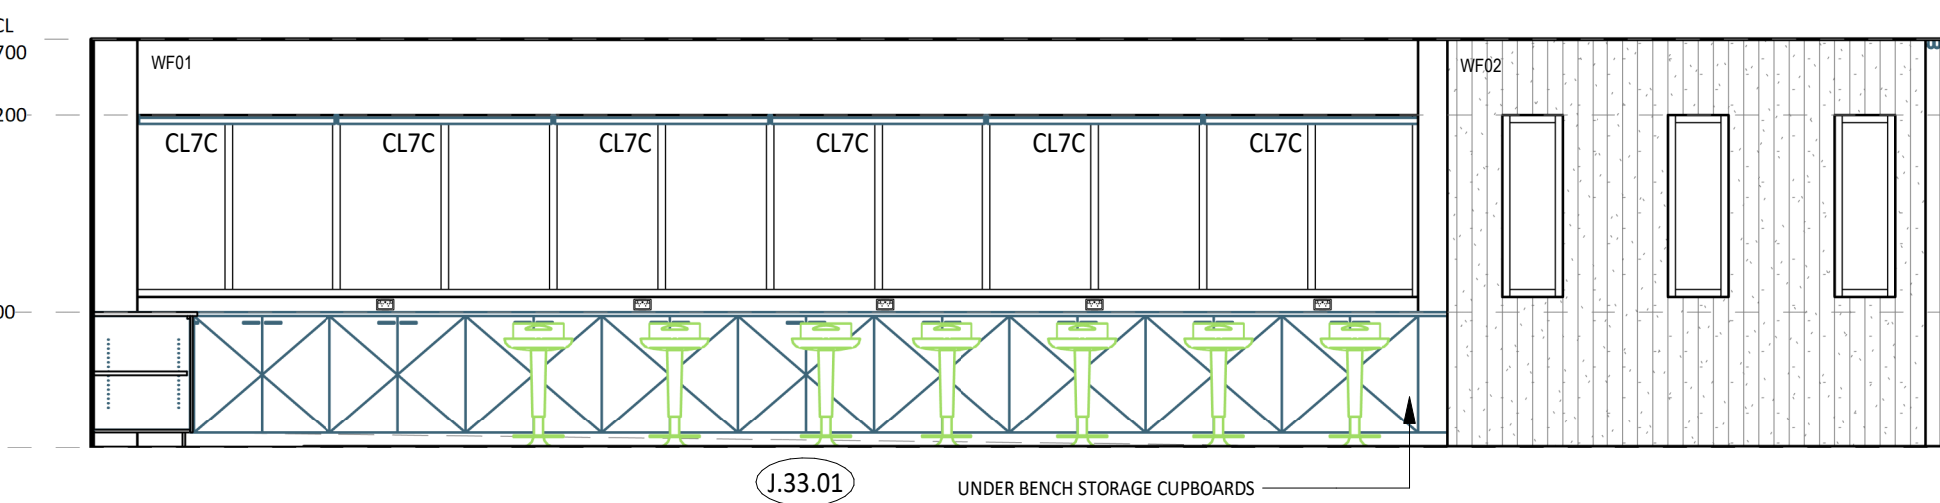
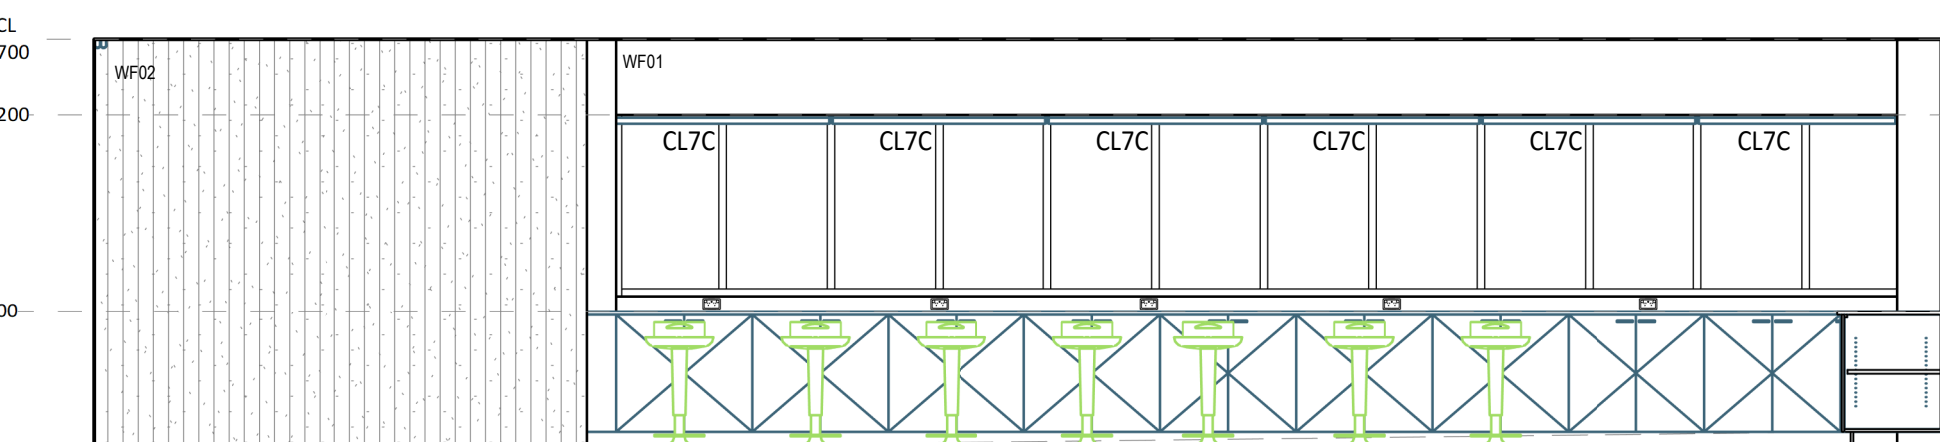
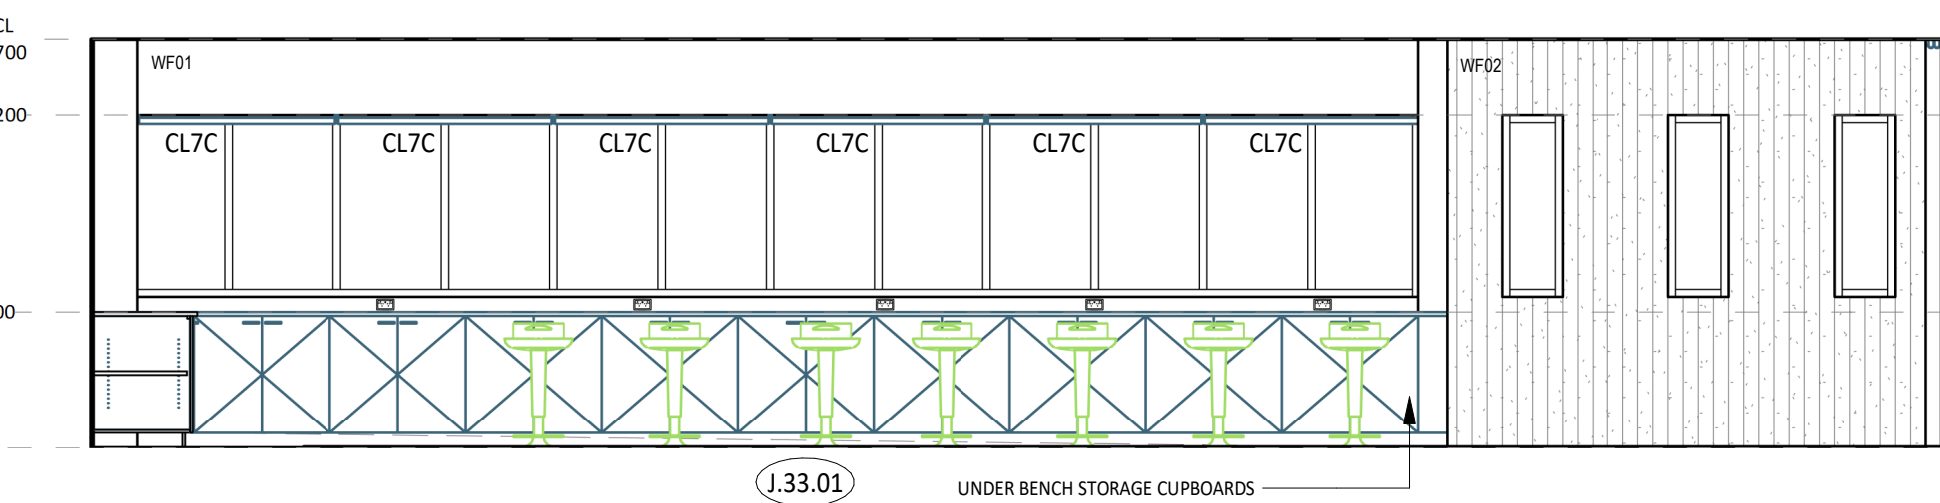
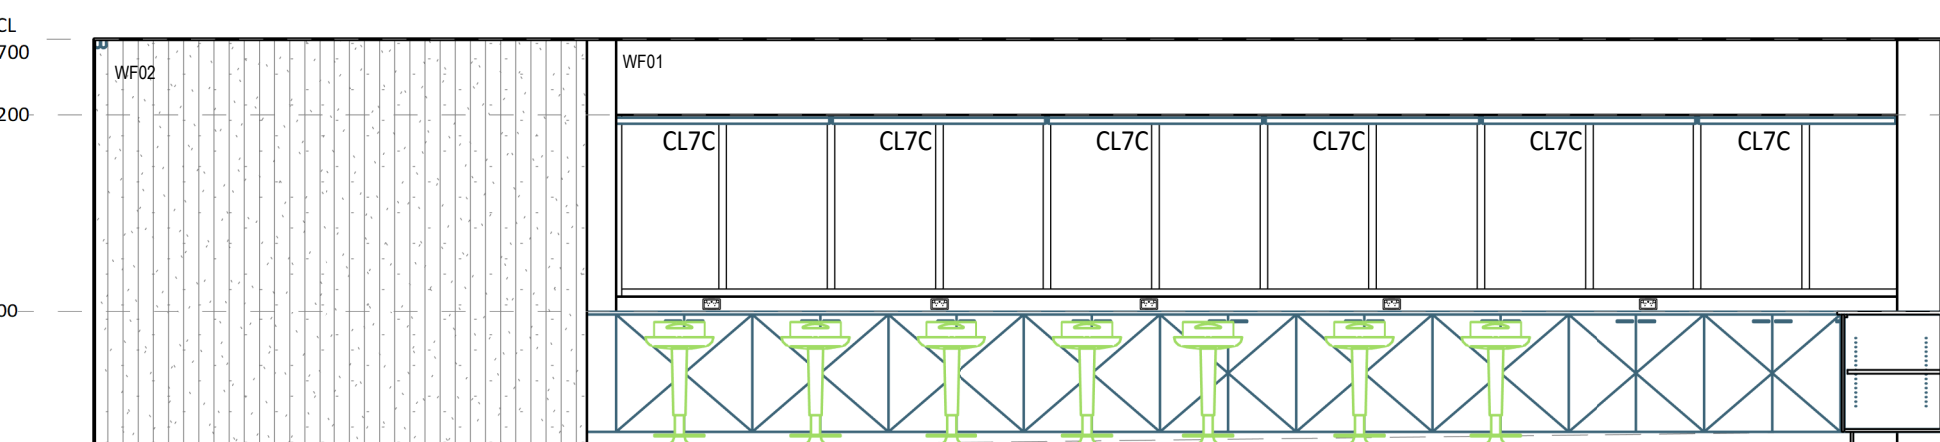
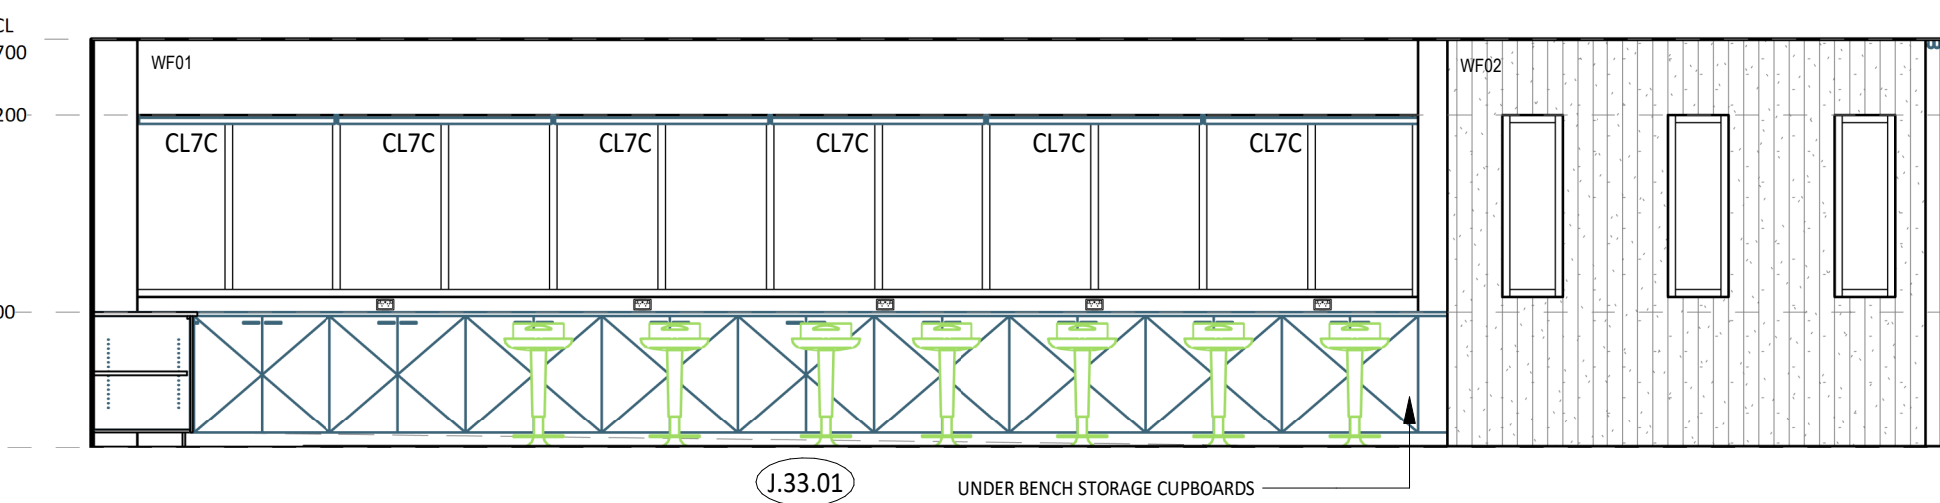
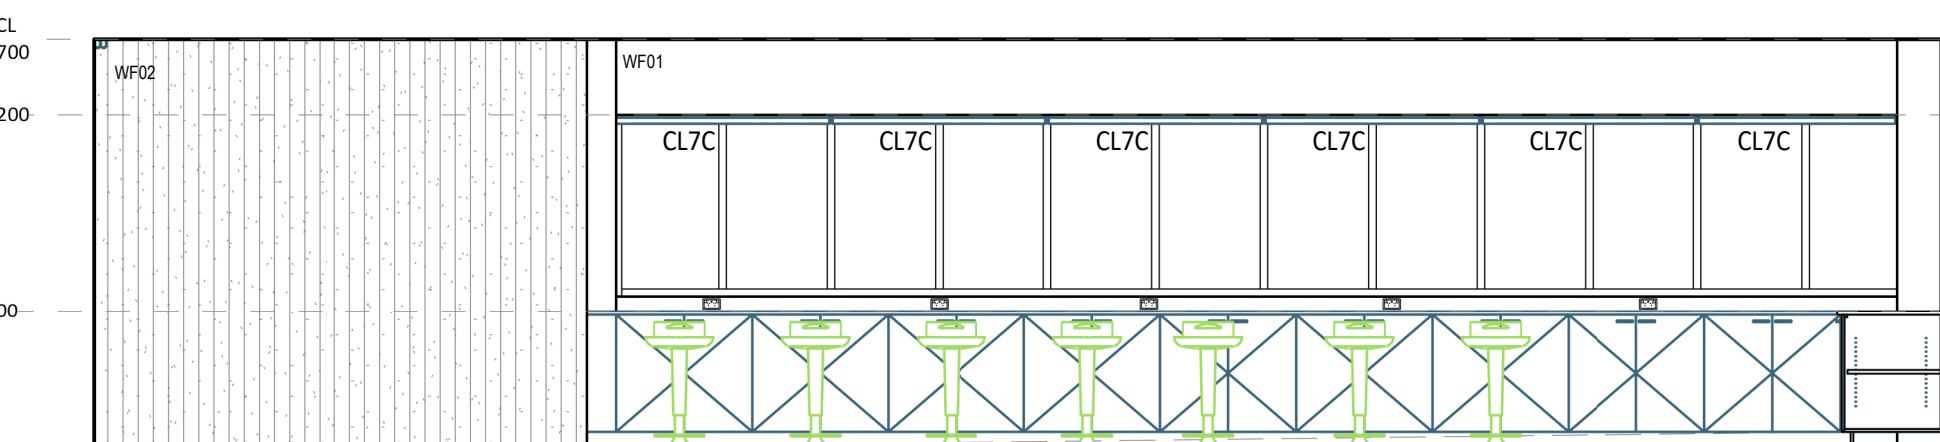
- GROUP 1 ITEMS
(PROVIDED & FITTED UNDER CONTRACT)
- GROUP 2 ITEMS
(PROVIDED BY CLIENT & FITTED UNDER CONTRACT)
- GROUP 2T ITEMS - EXISTING EQUIPMENT
(PROVIDED BY CLIENT & FITTED UNDER CONTRACT)
- GROUP 3 ITEMS
(PROVIDED & INSTALLED BY CLIENT)
- PLANS TO BE PRINTED IN COLOUR
- SCH_Code FFE TAG
- JO.PROC JOINERY TAG

ELECTRICAL LEGEND

- SINGLE POWER OUTLET
- DOUBLE POWER OUTLET
- SINGLE DATA
- DOUBLE DATA
- LIGHT SWITCH
- TV
- FLOOR BOX (FB)
- REFER TO ELECTRICAL ENGINEER'S
DRAWINGS FOR DETAILS

RLS NOTES

- ALL ARCHITECTURAL DRAWINGS TO BE READ IN CONJUNCTION WITH OTHER DISCIPLINES.
- REFER TO FF&E, SANITARYWARE SCHEDULES FOR ALL FURNITURE, FIXTURES, AND EQUIPMENT.
- REFER TO HYDRAULIC ENGINEER'S DRAWINGS FOR HYDRAULIC SERVICES. FINISH OF VALVE/BOX COVERS TO MATCH ADJACENT WALL/JOINERY FINISH.
- REFER TO ELECTRICAL DOCUMENTATION FOR OUTLET DETAILS (ie. POWER, DATA, COMMS etc.)
- REFER TO AUDIO VISUAL DOCUMENTATION (VideoPro) FOR AV REQUIREMENTS AND DETAILS.
- AV SUPPLIER TO CONFIRM EXACT POSITIONS OF EQUIPMENT ON SITE
- ALL FF&E ITEMS ARE TO BE READ IN CONJUNCTION WITH FF&E SCHEDULES AND CQU DESIGN MANUAL.
- ALL FF&E AND TRANSFER ITEMS TO BE REVIEWED AND CONFIRMED WITH CLIENT PRIOR TO COMMENCING ON SITE.
- PROVIDE ALLOWANCE AND ADD SUPPORT TO WALLS, WHERE FITTINGS ARE WALL MOUNTED. THIS INCLUDES BUT NOT LIMITED TO HANDBASINS, HANDRAILS, SCREENS, PROJECTORS, etc.
- FF&E COUNT IS FOR INFORMATION ONLY. THE TOTAL NUMBER OF FF&E ITEMS ARE TO BE CONFIRMED WITH CLIENT AND ARCHITECTS BEFORE PURCHASE OF ITEMS.
- CONFIRM ALL DIMENSIONS ON SITE FOR JOINERY ITEMS.
- ALL SANITARY FIXINGS & FIXTURES IN PWD TOILETS TO BE INSTALLED IN ACCORDANCE WITH AS1428.1
- ALLOW FOR FIRE EXTINGUISHERS & FIRE BLANKETS AS PER AS2444 2001
- POWER AND DATA POINTS SHOWN ON THE ROOM LAYOUT SHEETS WERE SHOWN AND DISCUSSED DURING USER GROUP BRIEFING. THESE RELATE TO PARTICULAR EQUIPMENT THAT WAS DISCUSSED AS REQUIRING POWER AND DATA. THESE REFLECT STAKEHOLDER EXPECTATIONS FOR SPECIFIC POWER AND DATA POINTS AND HAVE REMAINED IN THE DOCUMENTATION AS A USEFUL REFERENCE FOR THE CONTRACTOR. THESE ARE NOT A COMPLETE QUANTITY AND SPECIFICATION OF POWER AND DATA. THE CONTRACTOR IS TO REFER TO ELECTRICAL ENGINEER'S DOCUMENTATION FOR ALLOWANCE. REFER TO ELECTRICAL DOCUMENTATION FOR AMPS AND 3 PHASE POWER REQUIREMENTS. REFER TO AUDIO VISUAL (VIDEOPRO) DOCUMENTATION FOR ADDITIONAL POWER AND DATA REQUIREMENTS
- ALLOW FOR STRUCTURAL PLY BACKING BEHIND PLASTERBOARD FOR FULL EXTENT OF WALLS WITH MOUNTED AUDIO VISUAL EQUIPMENT. REFER TO AUDIO VISUAL (VIDEOPRO) DOCUMENTATION FOR LOCATIONS OF WALL MOUNTED EQUIPMENT.
- ALLOW FOR PRIVACY FILM TO ALL INTERNAL GLAZING (DOORS AND WINDOWS) TO OFFICES AND MEETING ROOMS. CONFIRM SET OUT PRIOR TO INSTALLATION
- ALLOW FOR DOUBLE BLOCK OUT BLINDS TO ALL WINDOWS UNLESS NOTED OTHERWISE
- ALL INTERNAL DOORS ARE TO BE SOLID CORE DOORS WITHIN ALUMINIUM FRAMED SUITES UNLESS NOTED OTHERWISE.
- FLOOR BOXES MUST BE COORDINATED WITH BOTH THE STRUCTURAL AND ELECTRICAL ENGINEERS. BEFORE ANY CUTTING OF THE EXISTING SLAB OCCURS, CONFIRM THE EXACT LOCATIONS AND REQUIREMENTS WITH THE STRUCTURAL ENGINEER.
- HEARING AUGMENTATION TO AUSTRALIAN STANDARDS - REFER VIDEOPRO AND ELECTRICAL SPECIFICATION

**1 PLAN DETAIL**
1 : 50**2 TYP. ELEVATION DETAIL**
1 : 50**2 TYP. ELEVATION DETAIL**
1 : 50**4 ELEVATION DETAIL**
1 : 50**6 GENERAL LEARNING - ELEVATION - 4 - B33-L1-01**
1 : 50**4 ELEVATION DETAIL**
1 : 50**6 GENERAL LEARNING - ELEVATION - 4 - B33-L1-01**
1 : 50**4 ELEVATION DETAIL**
1 : 50

<