


OPEN WORKSHOP, PAPER STORE & ONLINE FILM

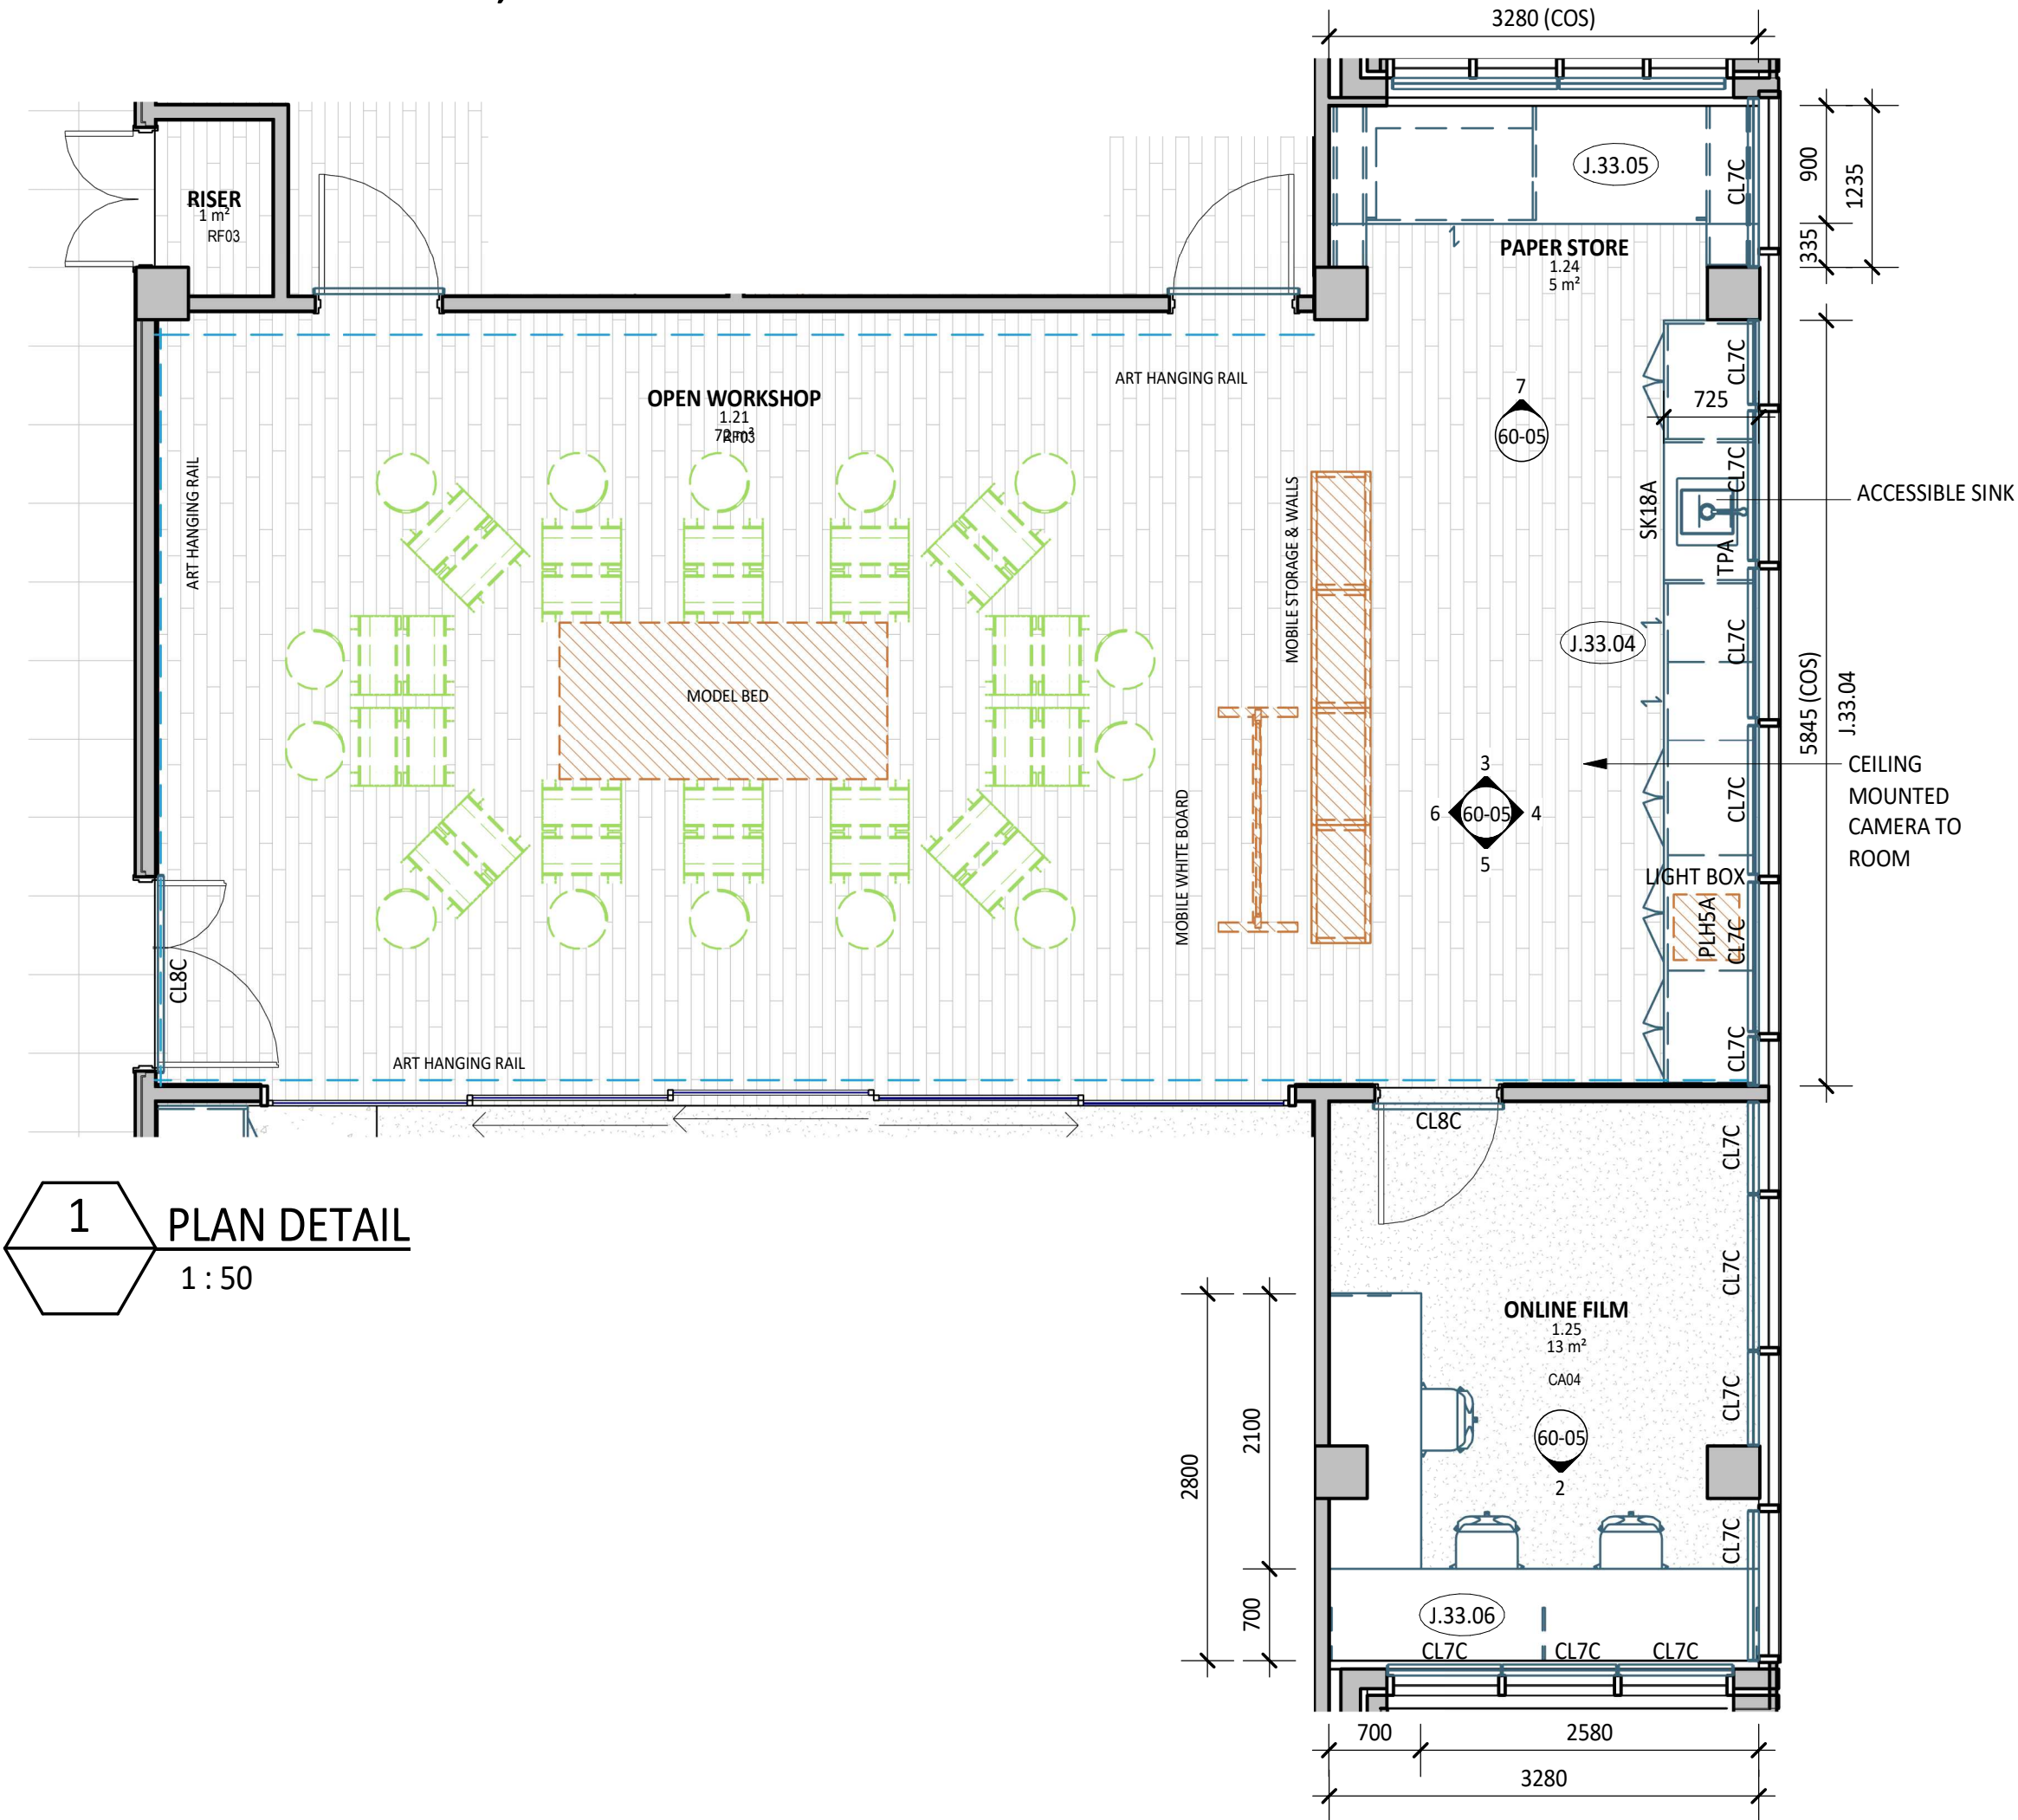

40-LEGEND FFE - OPEN WORKSHOP 1.21			
Code	Description	Group	Count
CL7C	Double Roller Blinds - Blockout	1	6
CL8C	Single Block Out Blind	1	1
CR19A	Art Hanging Rail	1	3
SK18A	Sink - Single bowl Overmount Care Accessible	1	1
TPA	Mixer - Sink Accessible	1	1
BD10B	Whiteboard - Mobile	2T	1
MB6B	Bed - Plinth Single Width	2T	1
PLH5A	Electrical Equipment - Light Box	2T	1
ST52D	Shelving - Movable	2T	4
BD12A	Easel - Double Sided	3	14
CH3A	Chair - Stool Height Adjustment	3	14

40-LEGEND FFE - ONLINE FILM CLASSROOM 1.25			
Code	Description	Group	Count
CH11A	Chair - Ergonomic	1	3
CL7C	Double Roller Blinds - Blockout	1	4
CL8C	Single Block Out Blind	1	1

60-LEGEND JOINERY - OPEN WORKSHOP	
FFE_Mark	Comments
J.33.04	Benchtop, Underbench Cupboards, Knee Clearance Unit, Underbench Drawers, Kick Board, Gables

60-LEGEND JOINERY - PAPER STORE	
FFE_Mark	Comments
J.33.05	Benchtop, Underbench Cupboards, Underbench Drawers, Kick Board, Gables, Overbench Paper Shelving Unit.


60-LEGEND JOINERY - ONLINE FILM	
FFE_Mark	Comments
J.33.06	Benchtop, Gables

FF&E LEGEND	
	GROUP 1 ITEMS (PROVIDED & FITTED UNDER CONTRACT)
	GROUP 2 ITEMS (PROVIDED BY CLIENT & FITTED UNDER CONTRACT)
	GROUP 2T ITEMS - EXISTING EQUIPMENT (PROVIDED BY CLIENT & FITTED UNDER CONTRACT)
	GROUP 3 ITEMS (PROVIDED & INSTALLED BY CLIENT)
PLANS TO BE PRINTED IN COLOUR	
SCH_Code	FF&E TAG
	JOINERY TAG


ELECTRICAL LEGEND	
	SINGLE POWER OUTLET
	DOUBLE POWER OUTLET
	SINGLE DATA
	DOUBLE DATA
REFER TO ELECTRICAL ENGINEER'S DRAWINGS FOR DETAILS	
	LIGHT SWITCH
	TV
	FLOOR BOX (FB)

- RLS NOTES**
- ALL ARCHITECTURAL DRAWINGS TO BE READ IN CONJUNCTION WITH OTHER DISCIPLINES.
 - REFER TO FF&E, SANITARYWARE SCHEDULES FOR ALL FURNITURE, FIXTURES, AND EQUIPMENT.
 - REFER TO HYDRAULIC ENGINEER'S DRAWINGS FOR HYDRAULIC SERVICES. FINISH OF VALVE/BOX COVERS TO MATCH ADJACENT WALL/JOINERY FINISH.
 - REFER TO ELECTRICAL DOCUMENTATION FOR OUTLET DETAILS (ie. POWER, DATA, COMMS etc.)
 - REFER TO AUDIO VISUAL DOCUMENTATION (VideoPro) FOR AV REQUIREMENTS AND DETAILS.
 - AV SUPPLIER TO CONFIRM EXACT POSITIONS OF EQUIPMENT ON SITE
 - ALL FF&E ITEMS ARE TO BE READ IN CONJUNCTION WITH FF&E SCHEDULES AND CQU DESIGN MANUAL.
 - ALL FF&E AND TRANSFER ITEMS TO BE REVIEWED AND CONFIRMED WITH CLIENT PRIOR TO COMMENCING ON SITE.
 - PROVIDE ALLOWANCE AND ADD SUPPORT TO WALLS, WHERE FITTINGS ARE WALL MOUNTED. THIS INCLUDES BUT NOT LIMITED TO HANDBASINS, HANDRAILS, SCREENS, PROJECTORS, etc.
 - FF&E COUNT IS FOR INFORMATION ONLY. THE TOTAL NUMBER OF FF&E ITEMS ARE TO BE CONFIRMED WITH CLIENT AND ARCHITECTS BEFORE PURCHASE OF ITEMS.
 - CONFIRM ALL DIMENSIONS ON SITE FOR JOINERY ITEMS.
 - ALL SANITARY FIXINGS & FIXTURES IN PWD TOILETS TO BE INSTALLED IN ACCORDANCE WITH AS1428.1
 - ALLOW FOR FIRE EXTINGUISHERS & FIRE BLANKETS AS PER AS2444.2001
 - POWER AND DATA POINTS SHOWN ON THE ROOM LAYOUT SHEETS WERE SHOWN AND DISCUSSED DURING USER GROUP BRIEFING. THESE RELATE TO PARTICULAR EQUIPMENT THAT WAS DISCUSSED AS REQUIRING POWER AND DATA. THESE REFLECT STAKEHOLDER EXPECTATIONS FOR SPECIFIC POWER AND DATA POINTS AND HAVE REMAINED IN THE DOCUMENTATION AS A USEFUL REFERENCE FOR THE CONTRACTOR. THESE ARE NOT A COMPLETE QUANTITY AND SPECIFICATION OF POWER AND DATA. THE CONTRACTOR IS TO REFER TO ELECTRICAL ENGINEER'S DOCUMENTATION FOR ALLOWANCE. REFER TO ELECTRICAL DOCUMENTATION FOR AMPS AND 3 PHASE POWER REQUIREMENTS. REFER TO AUDIO VISUAL (VIDEOPRO) DOCUMENTATION FOR ADDITIONAL POWER AND DATA REQUIREMENTS
 - ALLOW FOR STRUCTURAL PLY BACKING BEHIND PLASTERBOARD FOR FULL EXTENT OF WALLS WITH MOUNTED AUDIO VISUAL EQUIPMENT. REFER TO AUDIO VISUAL (VIDEOPRO) DOCUMENTATION FOR LOCATIONS OF WALL MOUNTED EQUIPMENT.
 - ALLOW FOR PRIVACY FILM TO ALL INTERNAL GLAZING (DOORS AND WINDOWS) TO OFFICES AND MEETING ROOMS. CONFIRM SET OUT PRIOR TO INSTALLATION
 - ALLOW FOR DOUBLE BLOCK OUT BLINDS TO ALL WINDOWS UNLESS NOTED OTHERWISE
 - ALL INTERNAL DOORS ARE TO BE SOLID CORE DOORS WITHIN ALUMINIUM FRAMED SUITES UNLESS NOTED OTHERWISE.
 - FLOOR BOXES MUST BE COORDINATED WITH BOTH THE STRUCTURAL AND ELECTRICAL ENGINEERS. BEFORE ANY CUTTING OF THE EXISTING SLAB OCCURS, CONFIRM THE EXACT LOCATIONS AND REQUIREMENTS WITH THE STRUCTURAL ENGINEER.
 - HEARING AUGMENTATION TO AUSTRALIAN STANDARDS – REFER VIDEOPRO AND ELECTRICAL SPECIFICATION


1 PLAN DETAIL
1 : 50

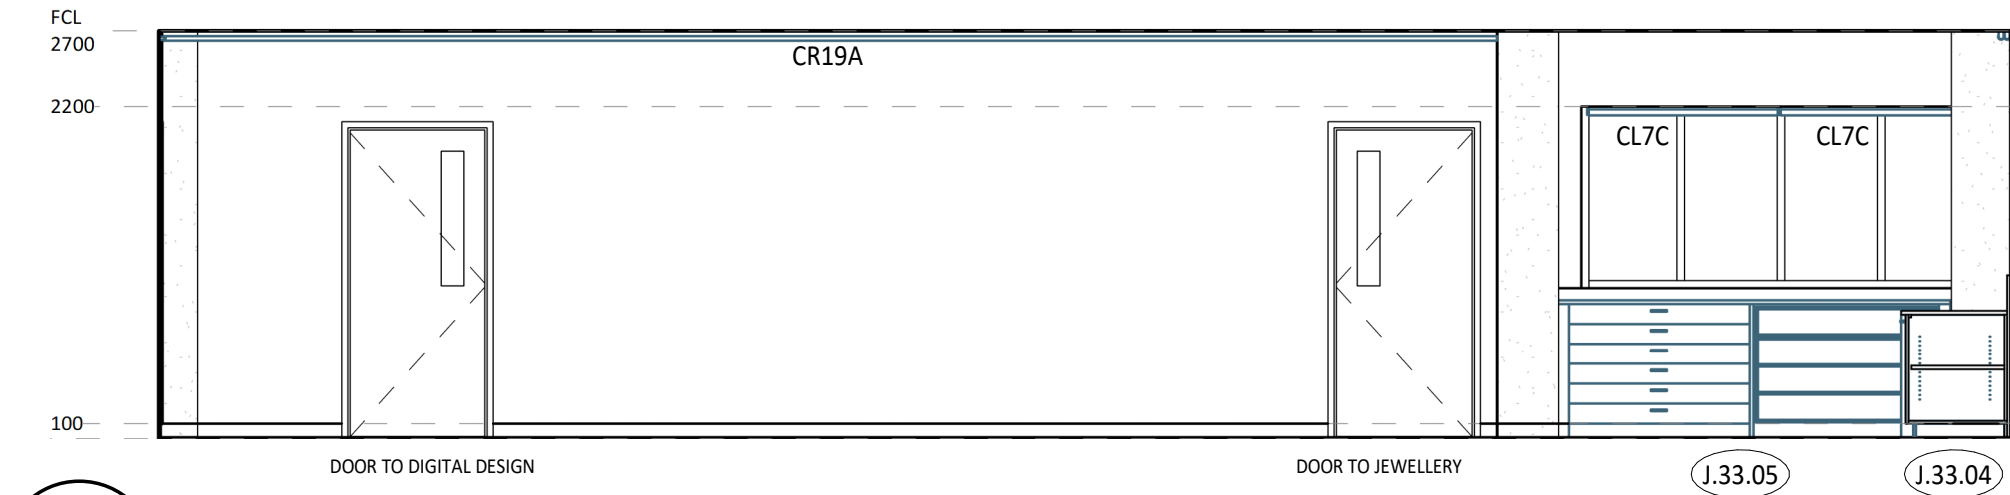


3 ELEVATION DETAIL
1 : 50

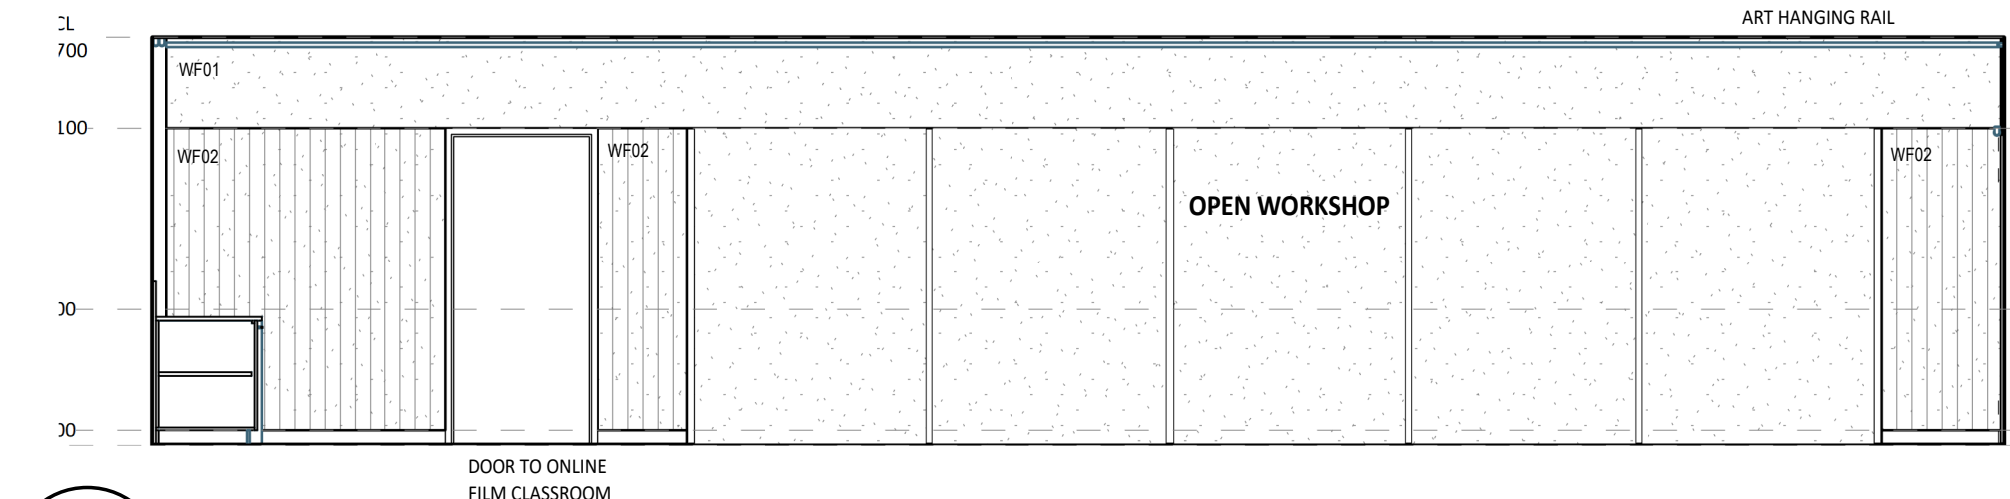

5 ELEVATION DETAIL
1 : 50

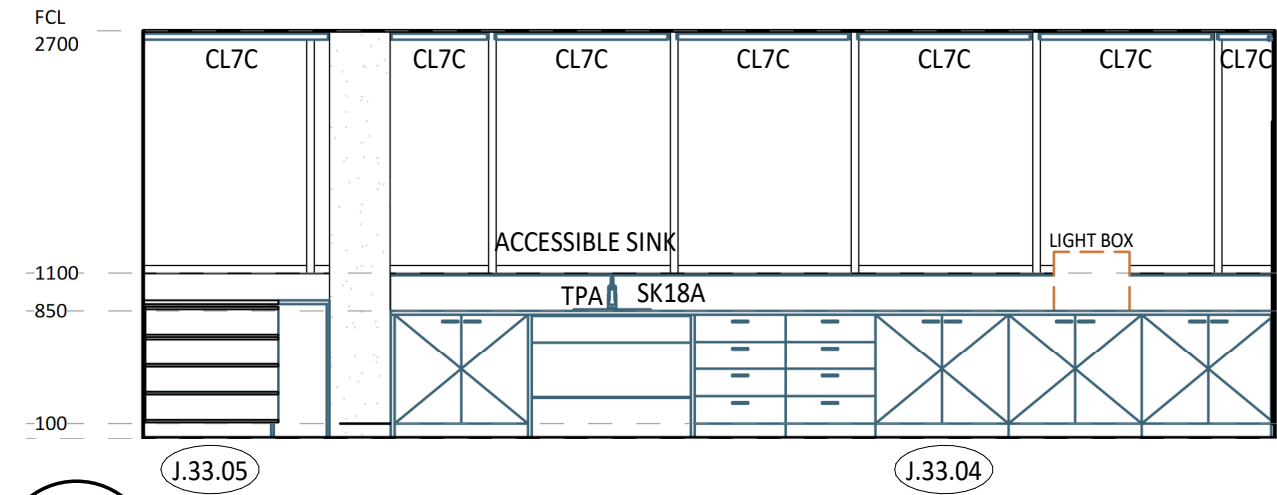


4 ELEVATION DETAIL
1 : 50

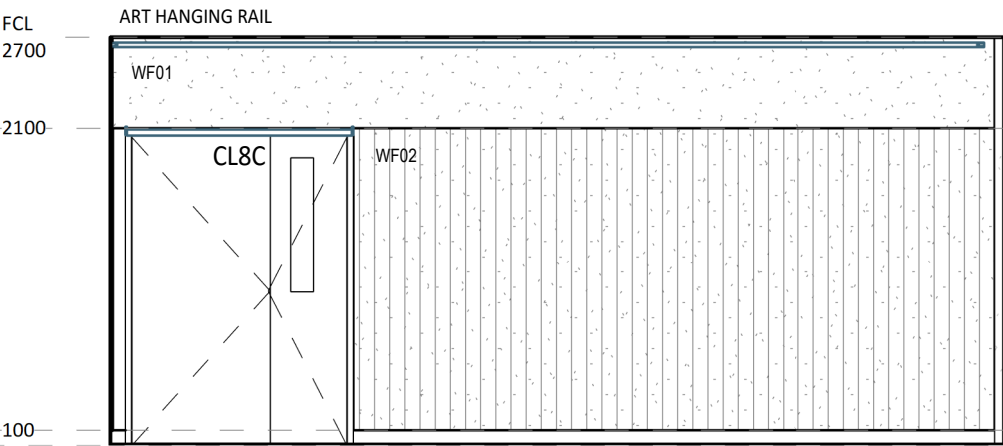


6 ELEVATION DETAIL
1 : 50

PAPER STORE

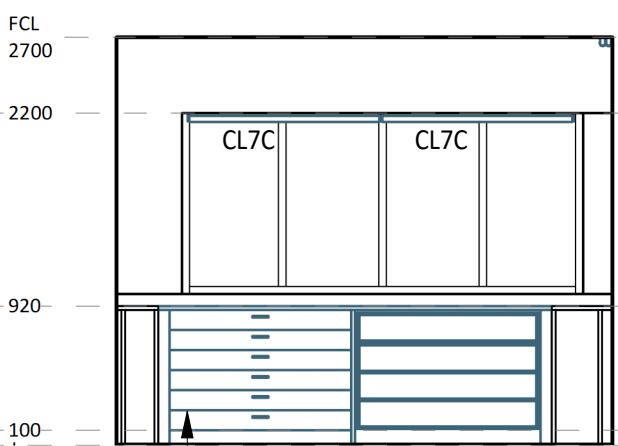

7 ELEVATION DETAIL
1 : 50

ONLINE FILM

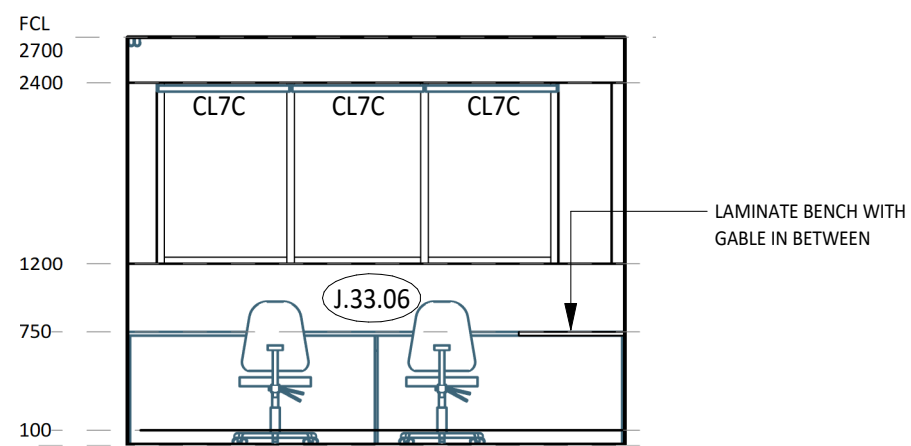

2 ELEVATION DETAIL
1 : 50

thomson
adsett

PEDDLE THORP
architecture | interiors | health | planning

Telephone +61 7 3840 9999
bne@thomsonadsett.com
Level 9, 470 St Pauls Terrace
Fortitude Valley
Qld 4006 Australia
thomsonadsett.com

© Copyright
These drawings and designs and the copyright thereof are the property of Thomson Adsett Pty Ltd and must not be used, retained or copied without written permission of Thomson Adsett Pty Ltd. AEN 76 105 314 654 Trading as ThomsonAdsett. Dimensions take precedence over scaling. Do not measure off drawings as print sizes may vary

CQU ROCKHAMPTON
TAFE
CONSOLIDATION -
STAGE 2

554/700 Yaamba Rd, Norman
Gardens QLD 4701

for

A	12/02/26	ISSUED FOR TENDER	SM
2	30/01/26	60% DRAFT ISSUE	SM
1	23/01/26	FOR COORDINATION ISSUE	SM
rev/	date	details	init.

drawn	date
PT/TA	19/12/25
checked	date
JT	19/12/25
verified	date
JT	19/12/25

scale

RLS - BLD33-L1 - OPEN
WORKSHOP, ONLINE FILM

scale project no.
1 : 50 @ A1 260018

revision
A

sheet no.
CQU-ROK-033-01-ARC-60-05

ISSUE FOR TENDER