

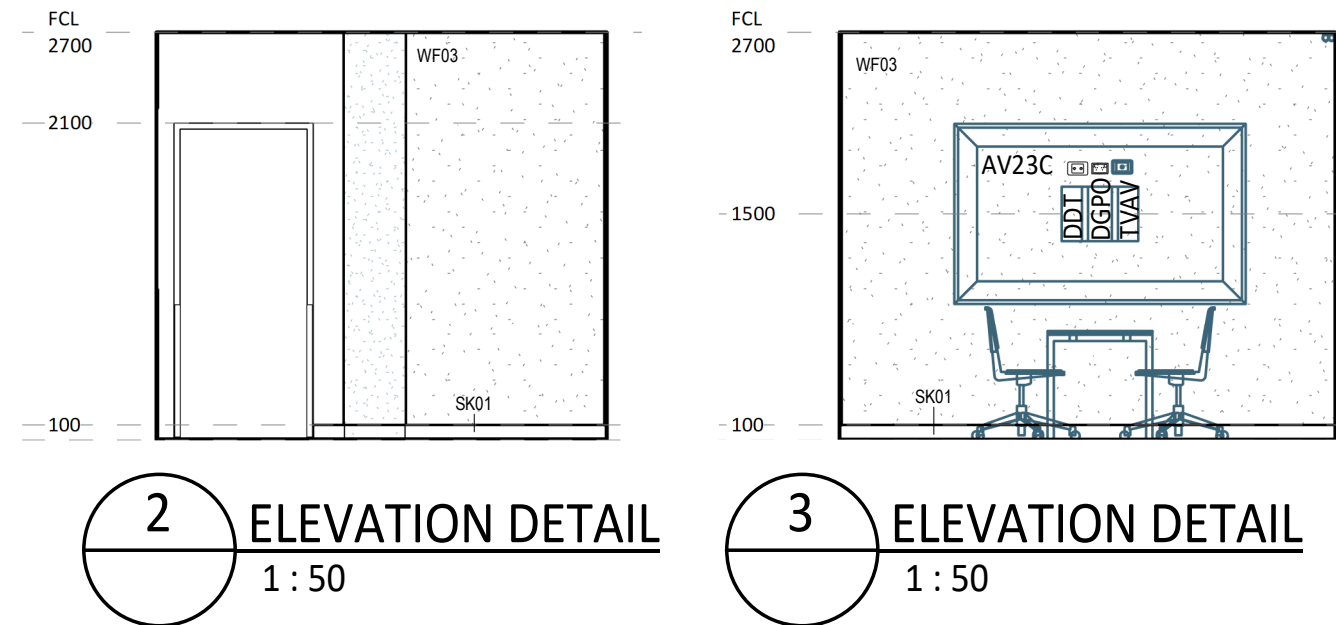
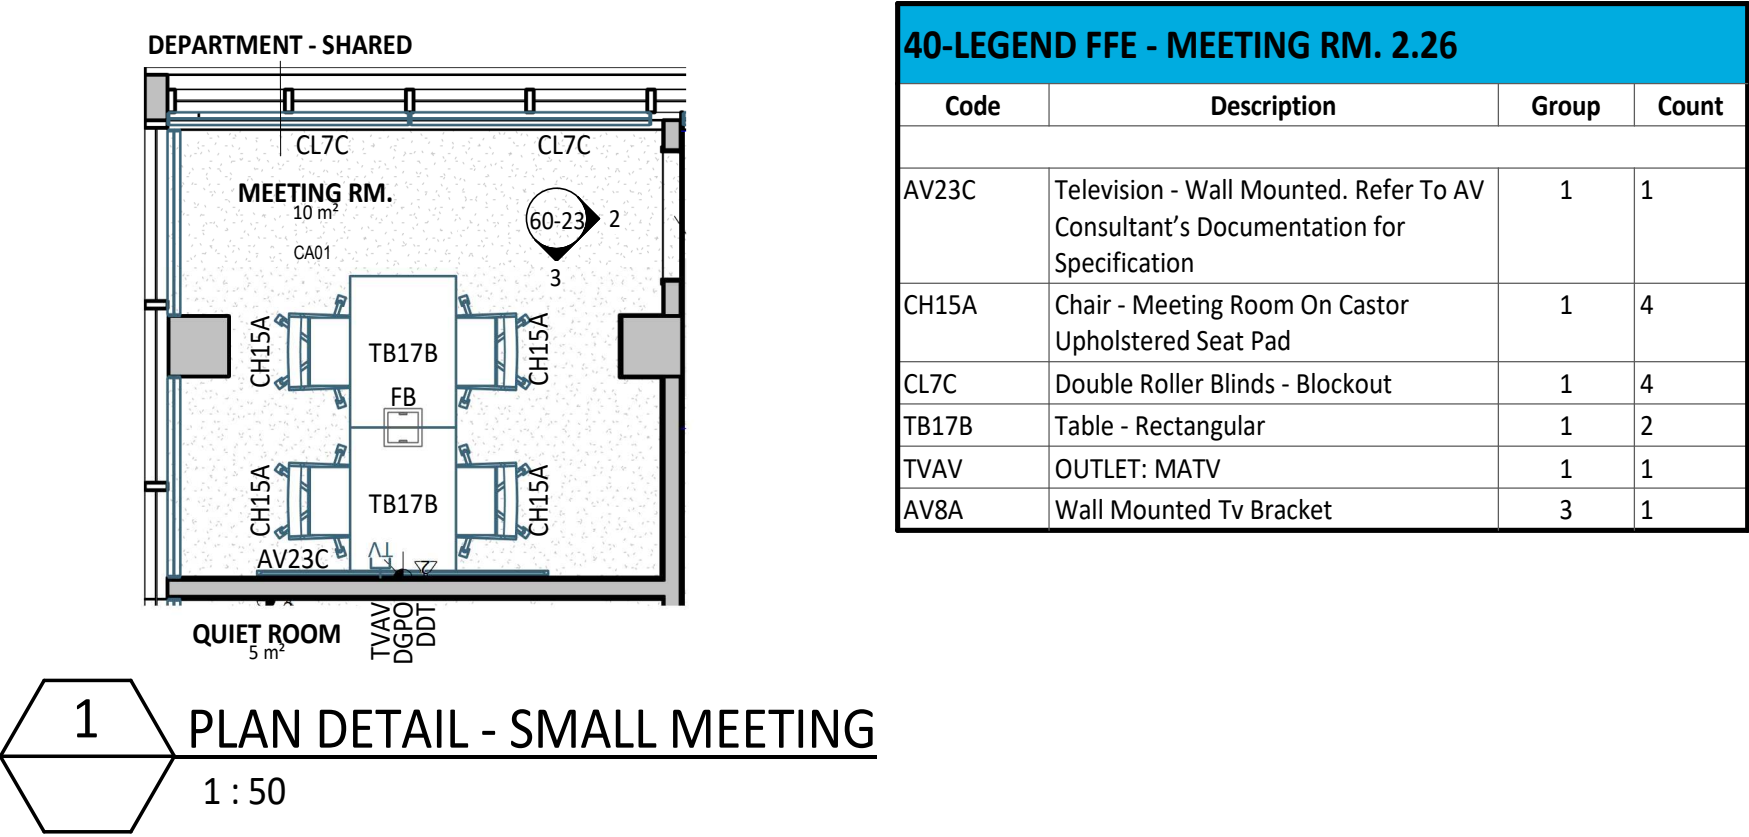






SMALL MEETING ROOM

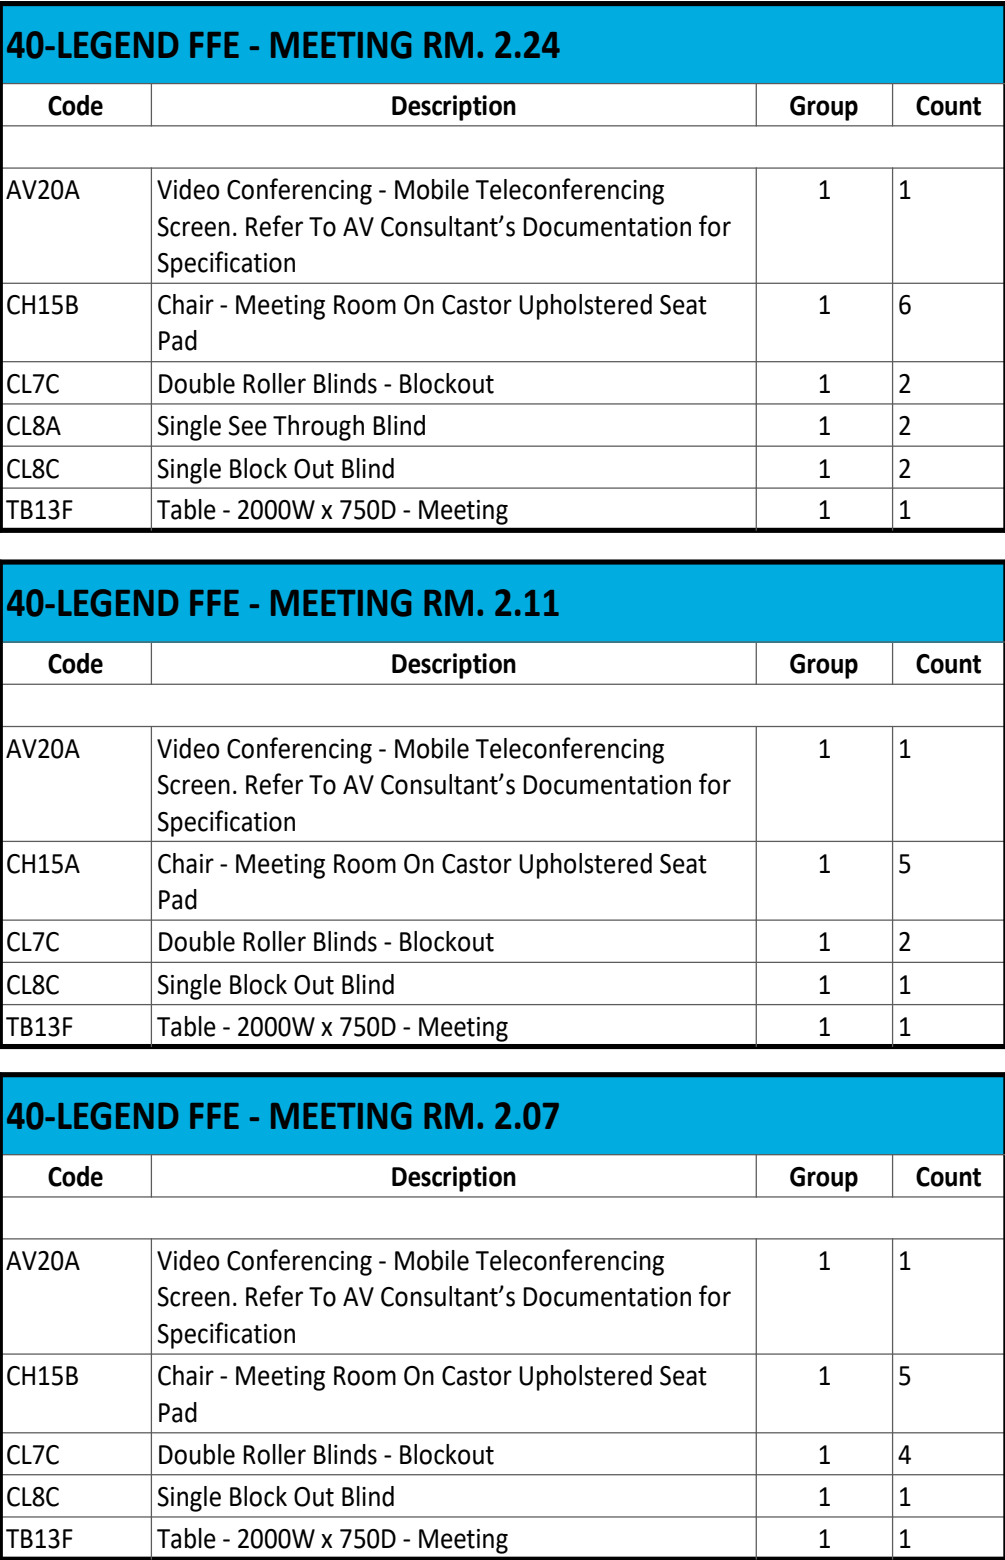

MEETING ROOMS

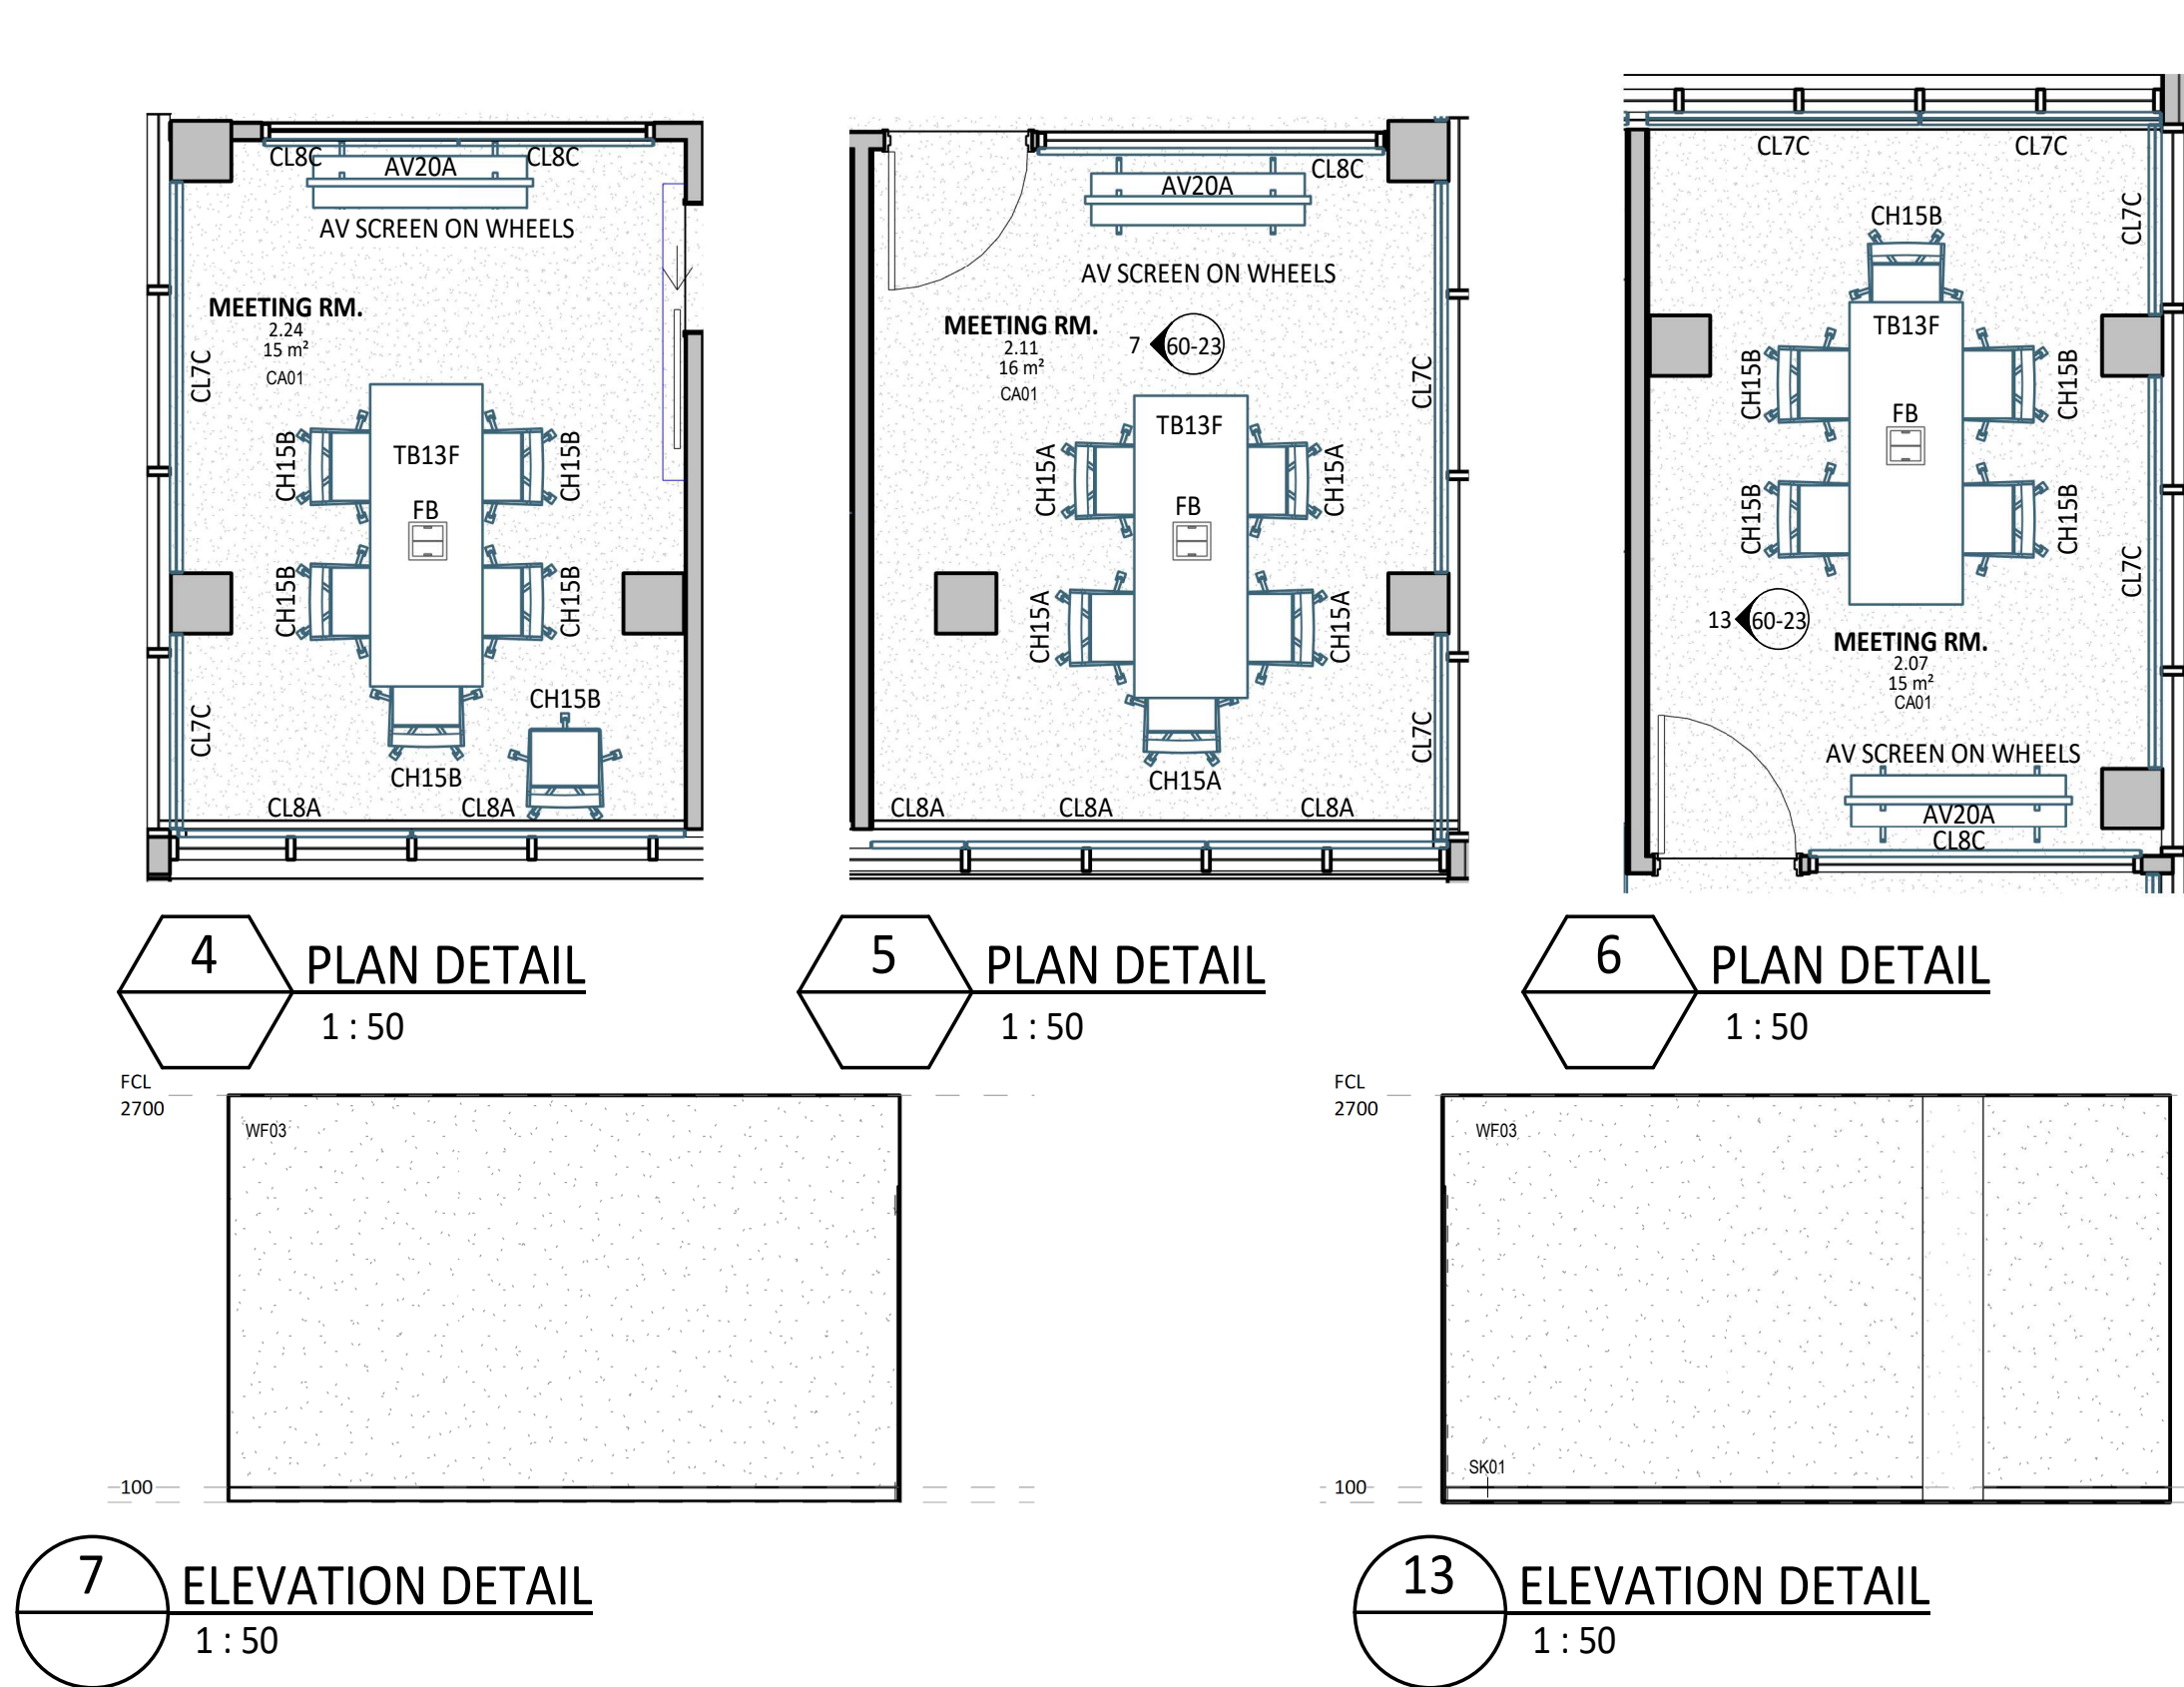

LARGE MEETING ROOM

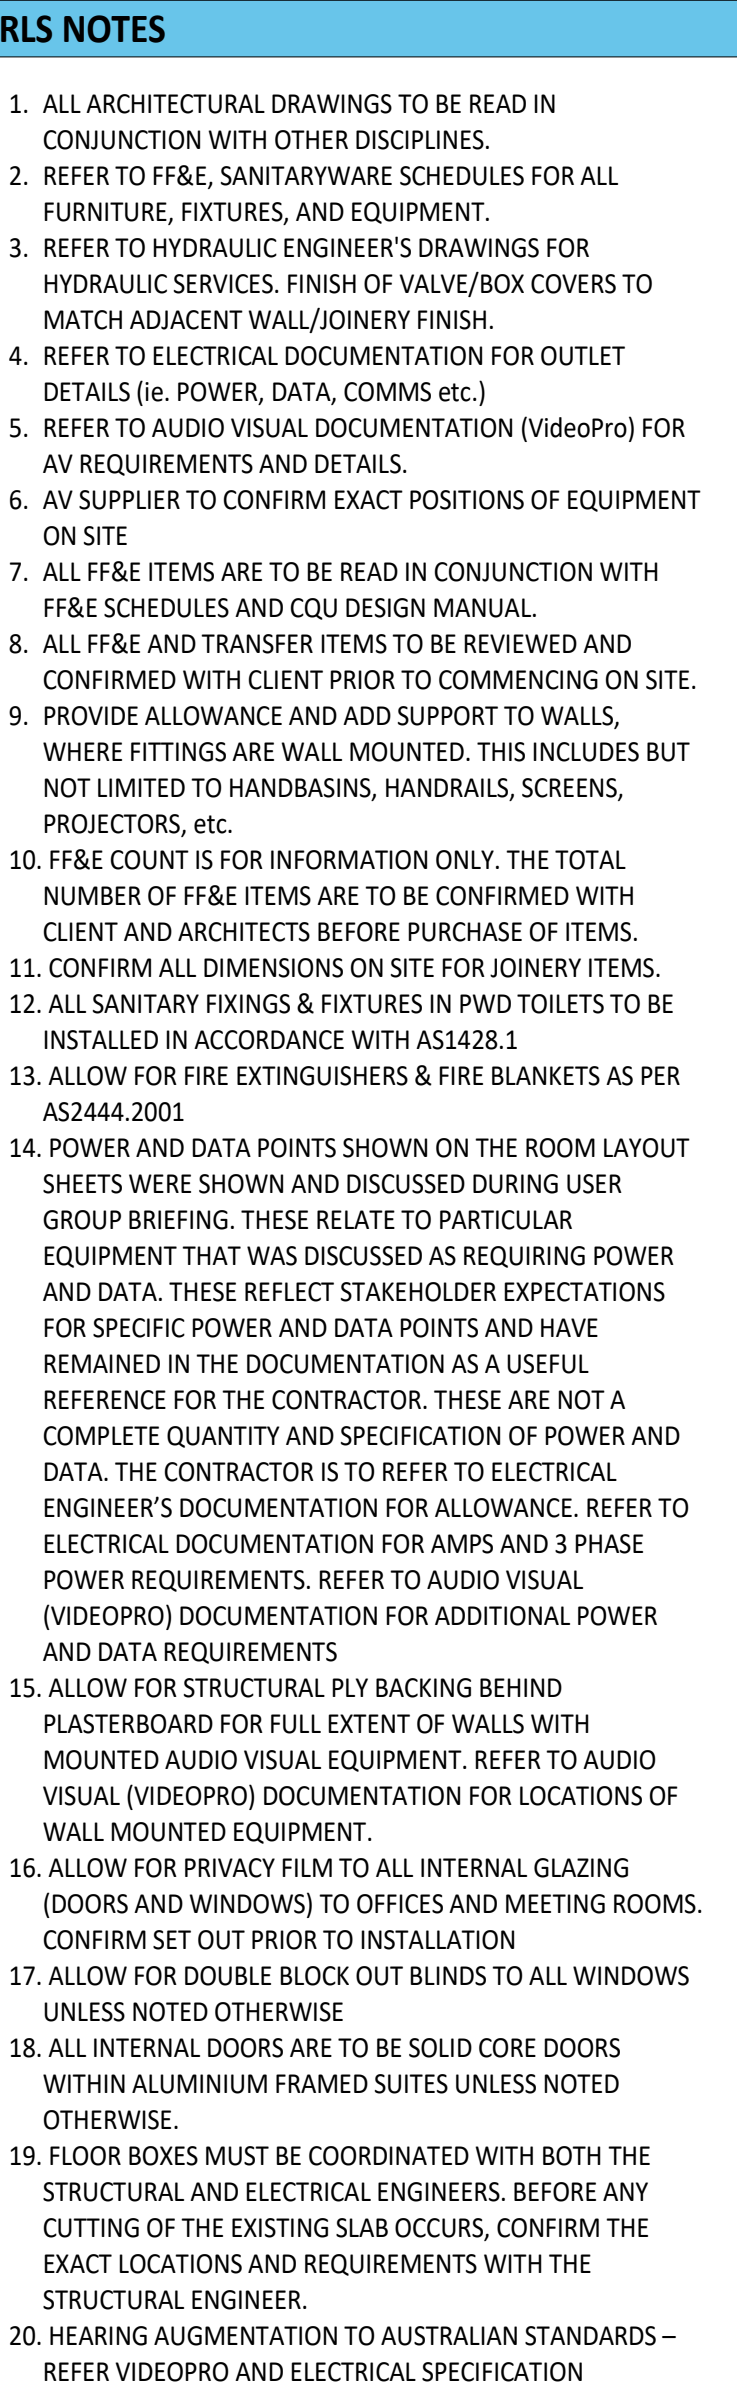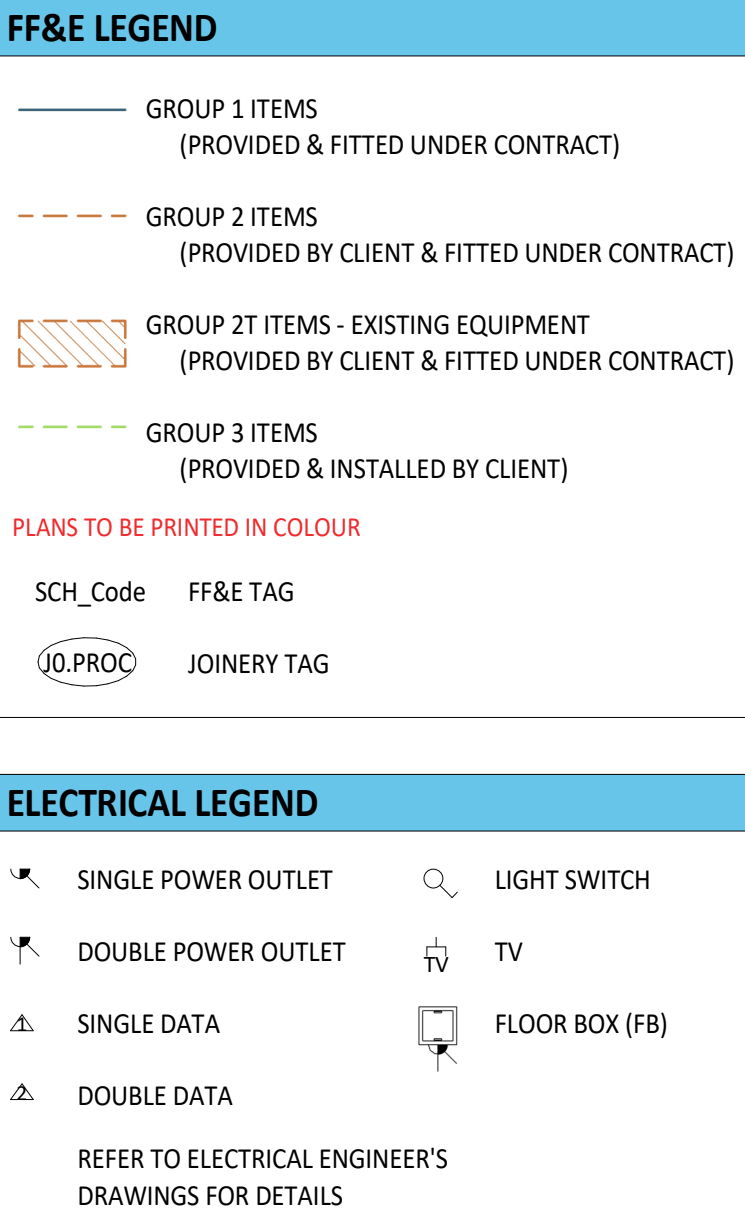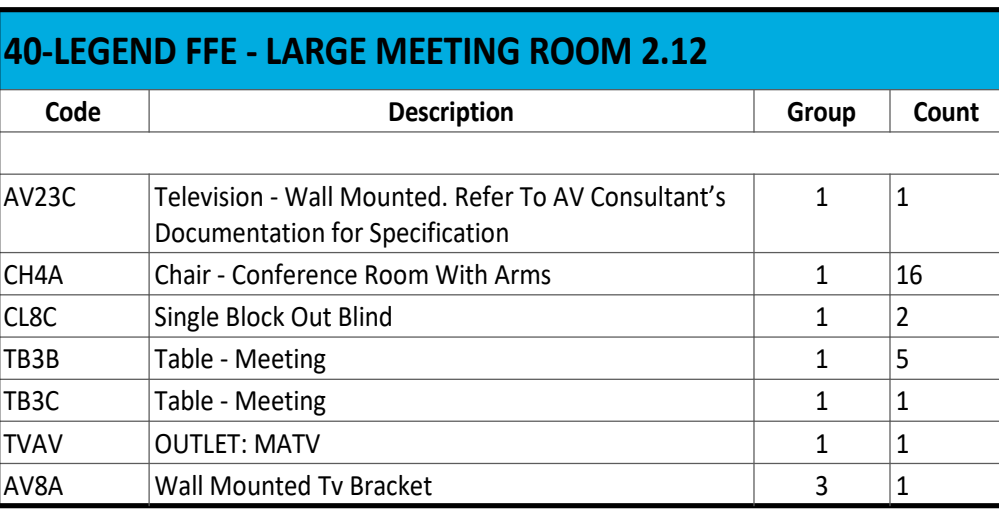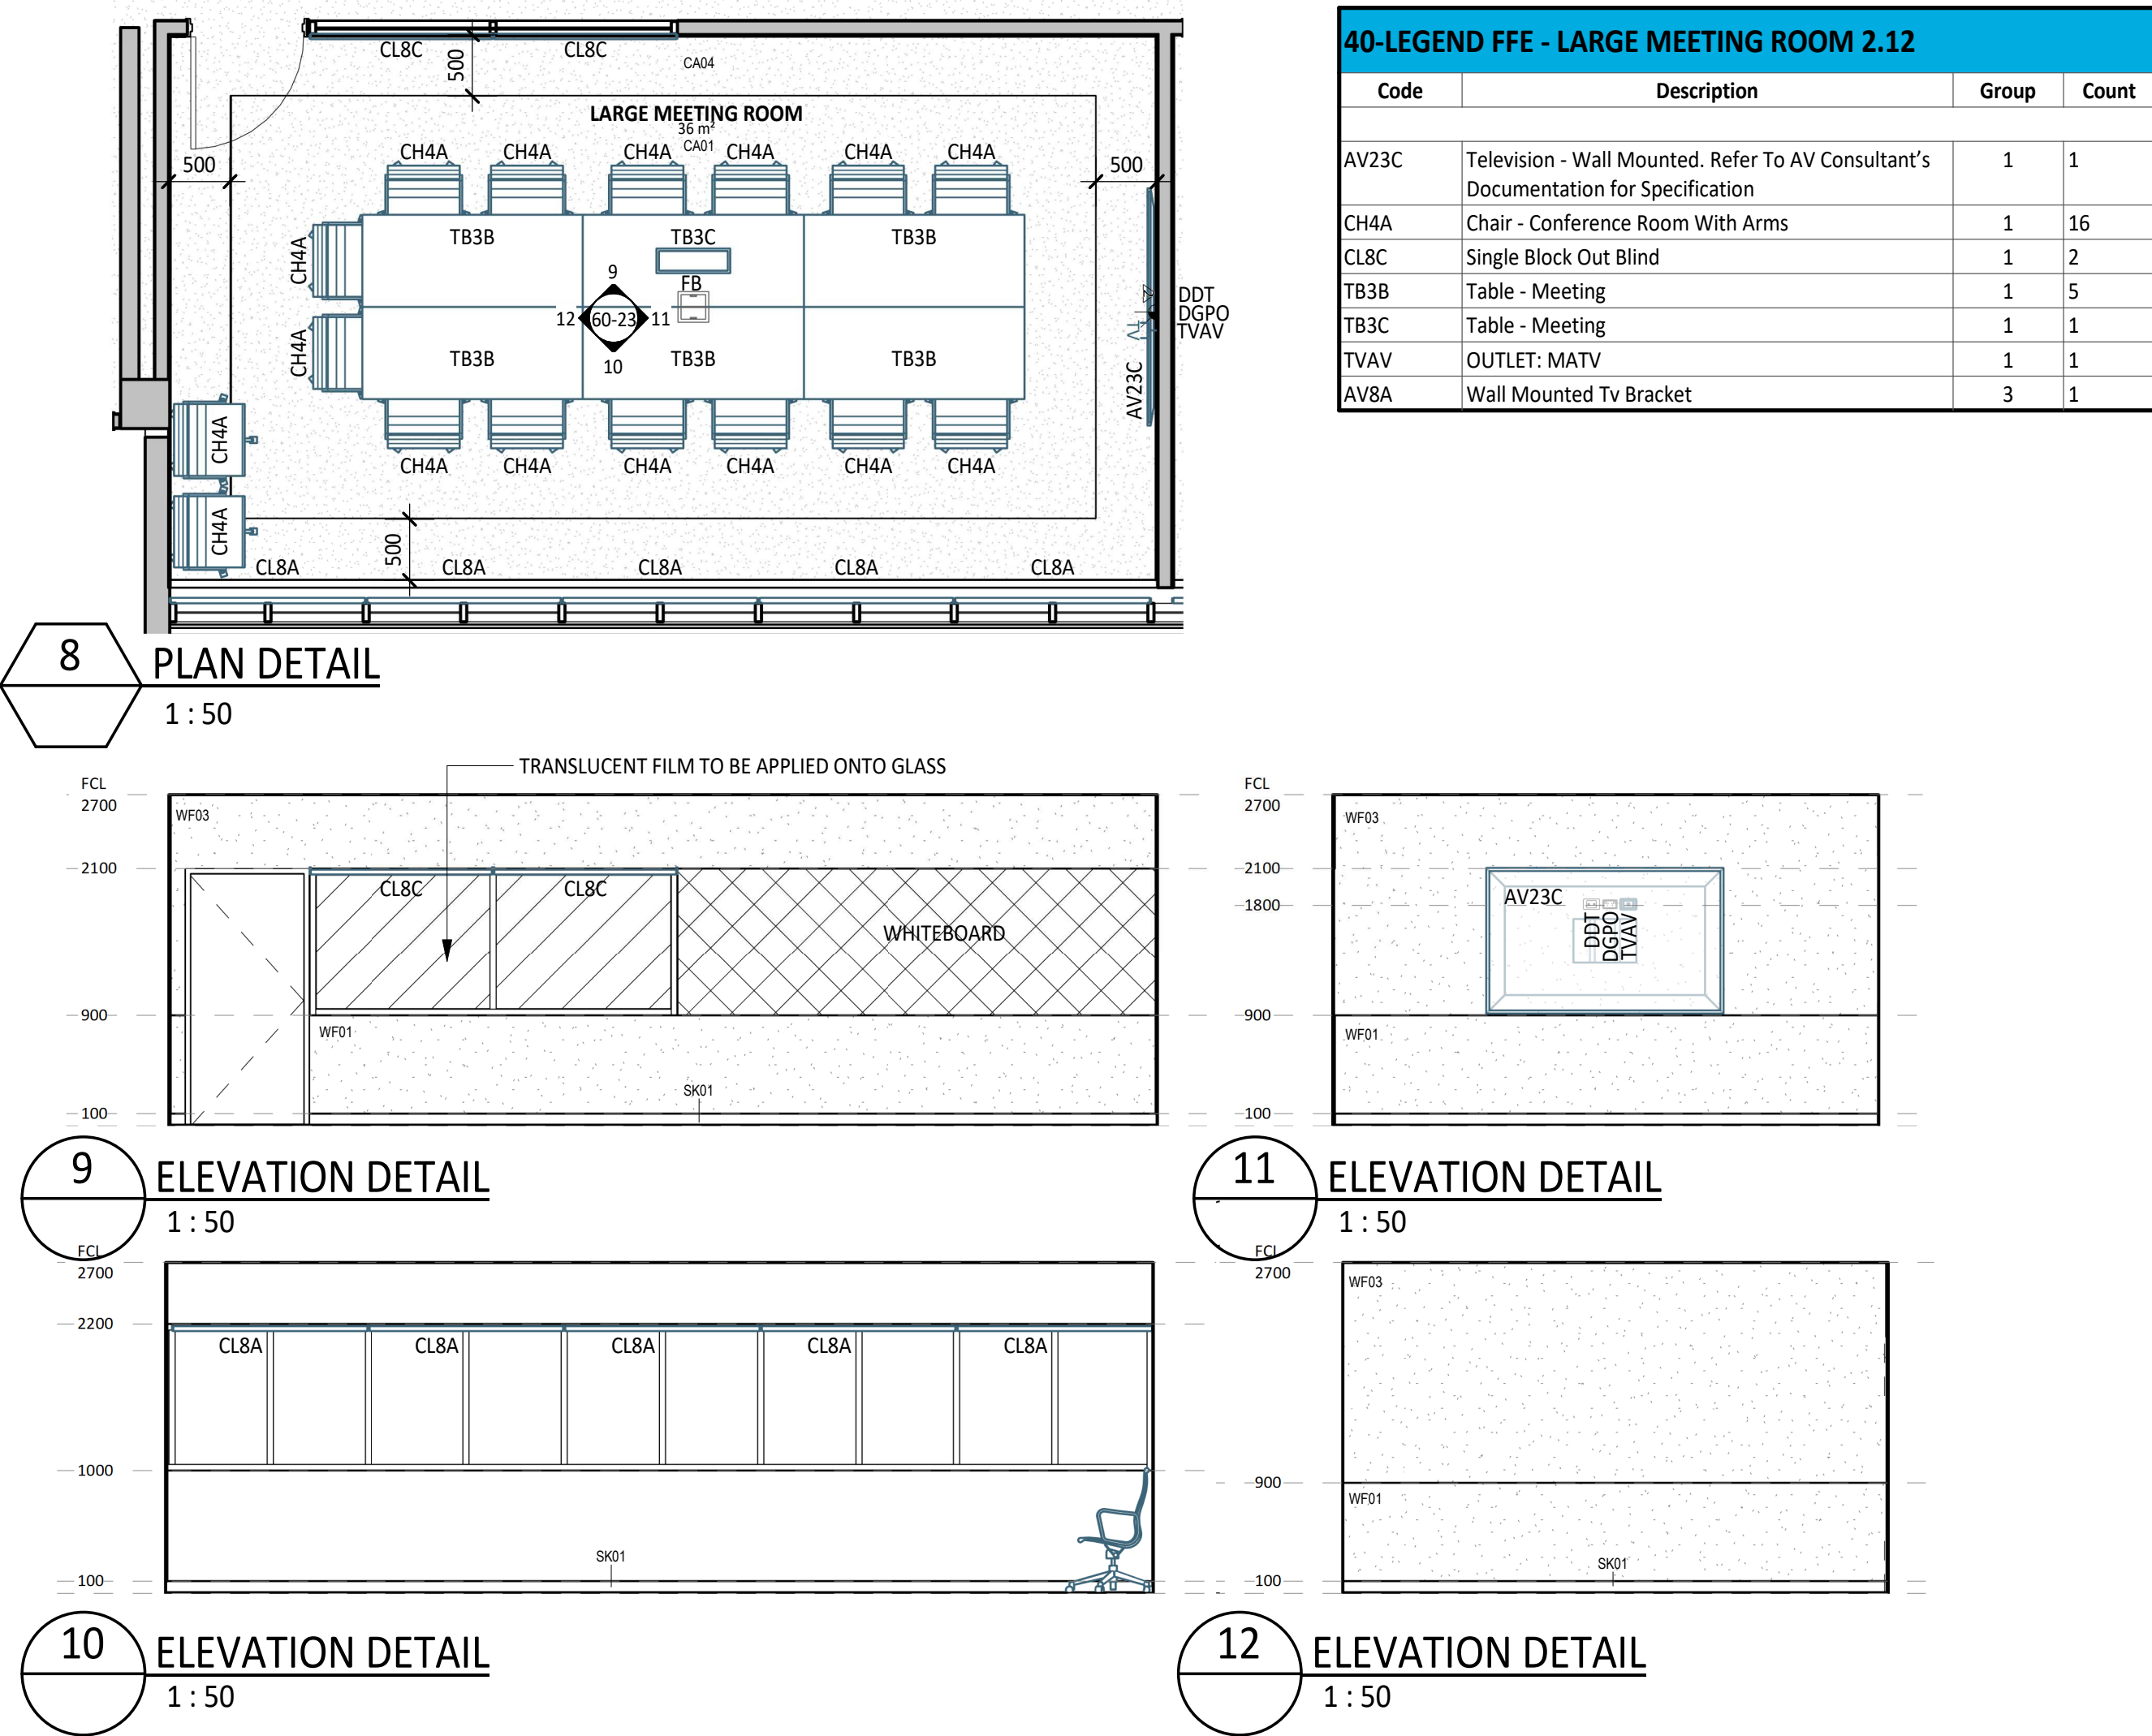

A	12/02/26	ISSUED FOR TENDER	SM
2	30/01/26	60% DRAFT ISSUE	SM
1	23/01/26	FOR COORDINATION ISSUE	SM
rev/	date	details	init.

drawn	date
PT/TA	19/12/25
checked	date
JT	19/12/25
verified	date
JT	19/12/25

scale

RLS - BLD33-L2 - MEETING ROOMS

scale	project no.
1 : 50 @ A1	260018
revision	
A	
sheet no.	
CQU-ROK-033-02-ARC-60-23	

ISSUE FOR TENDER