


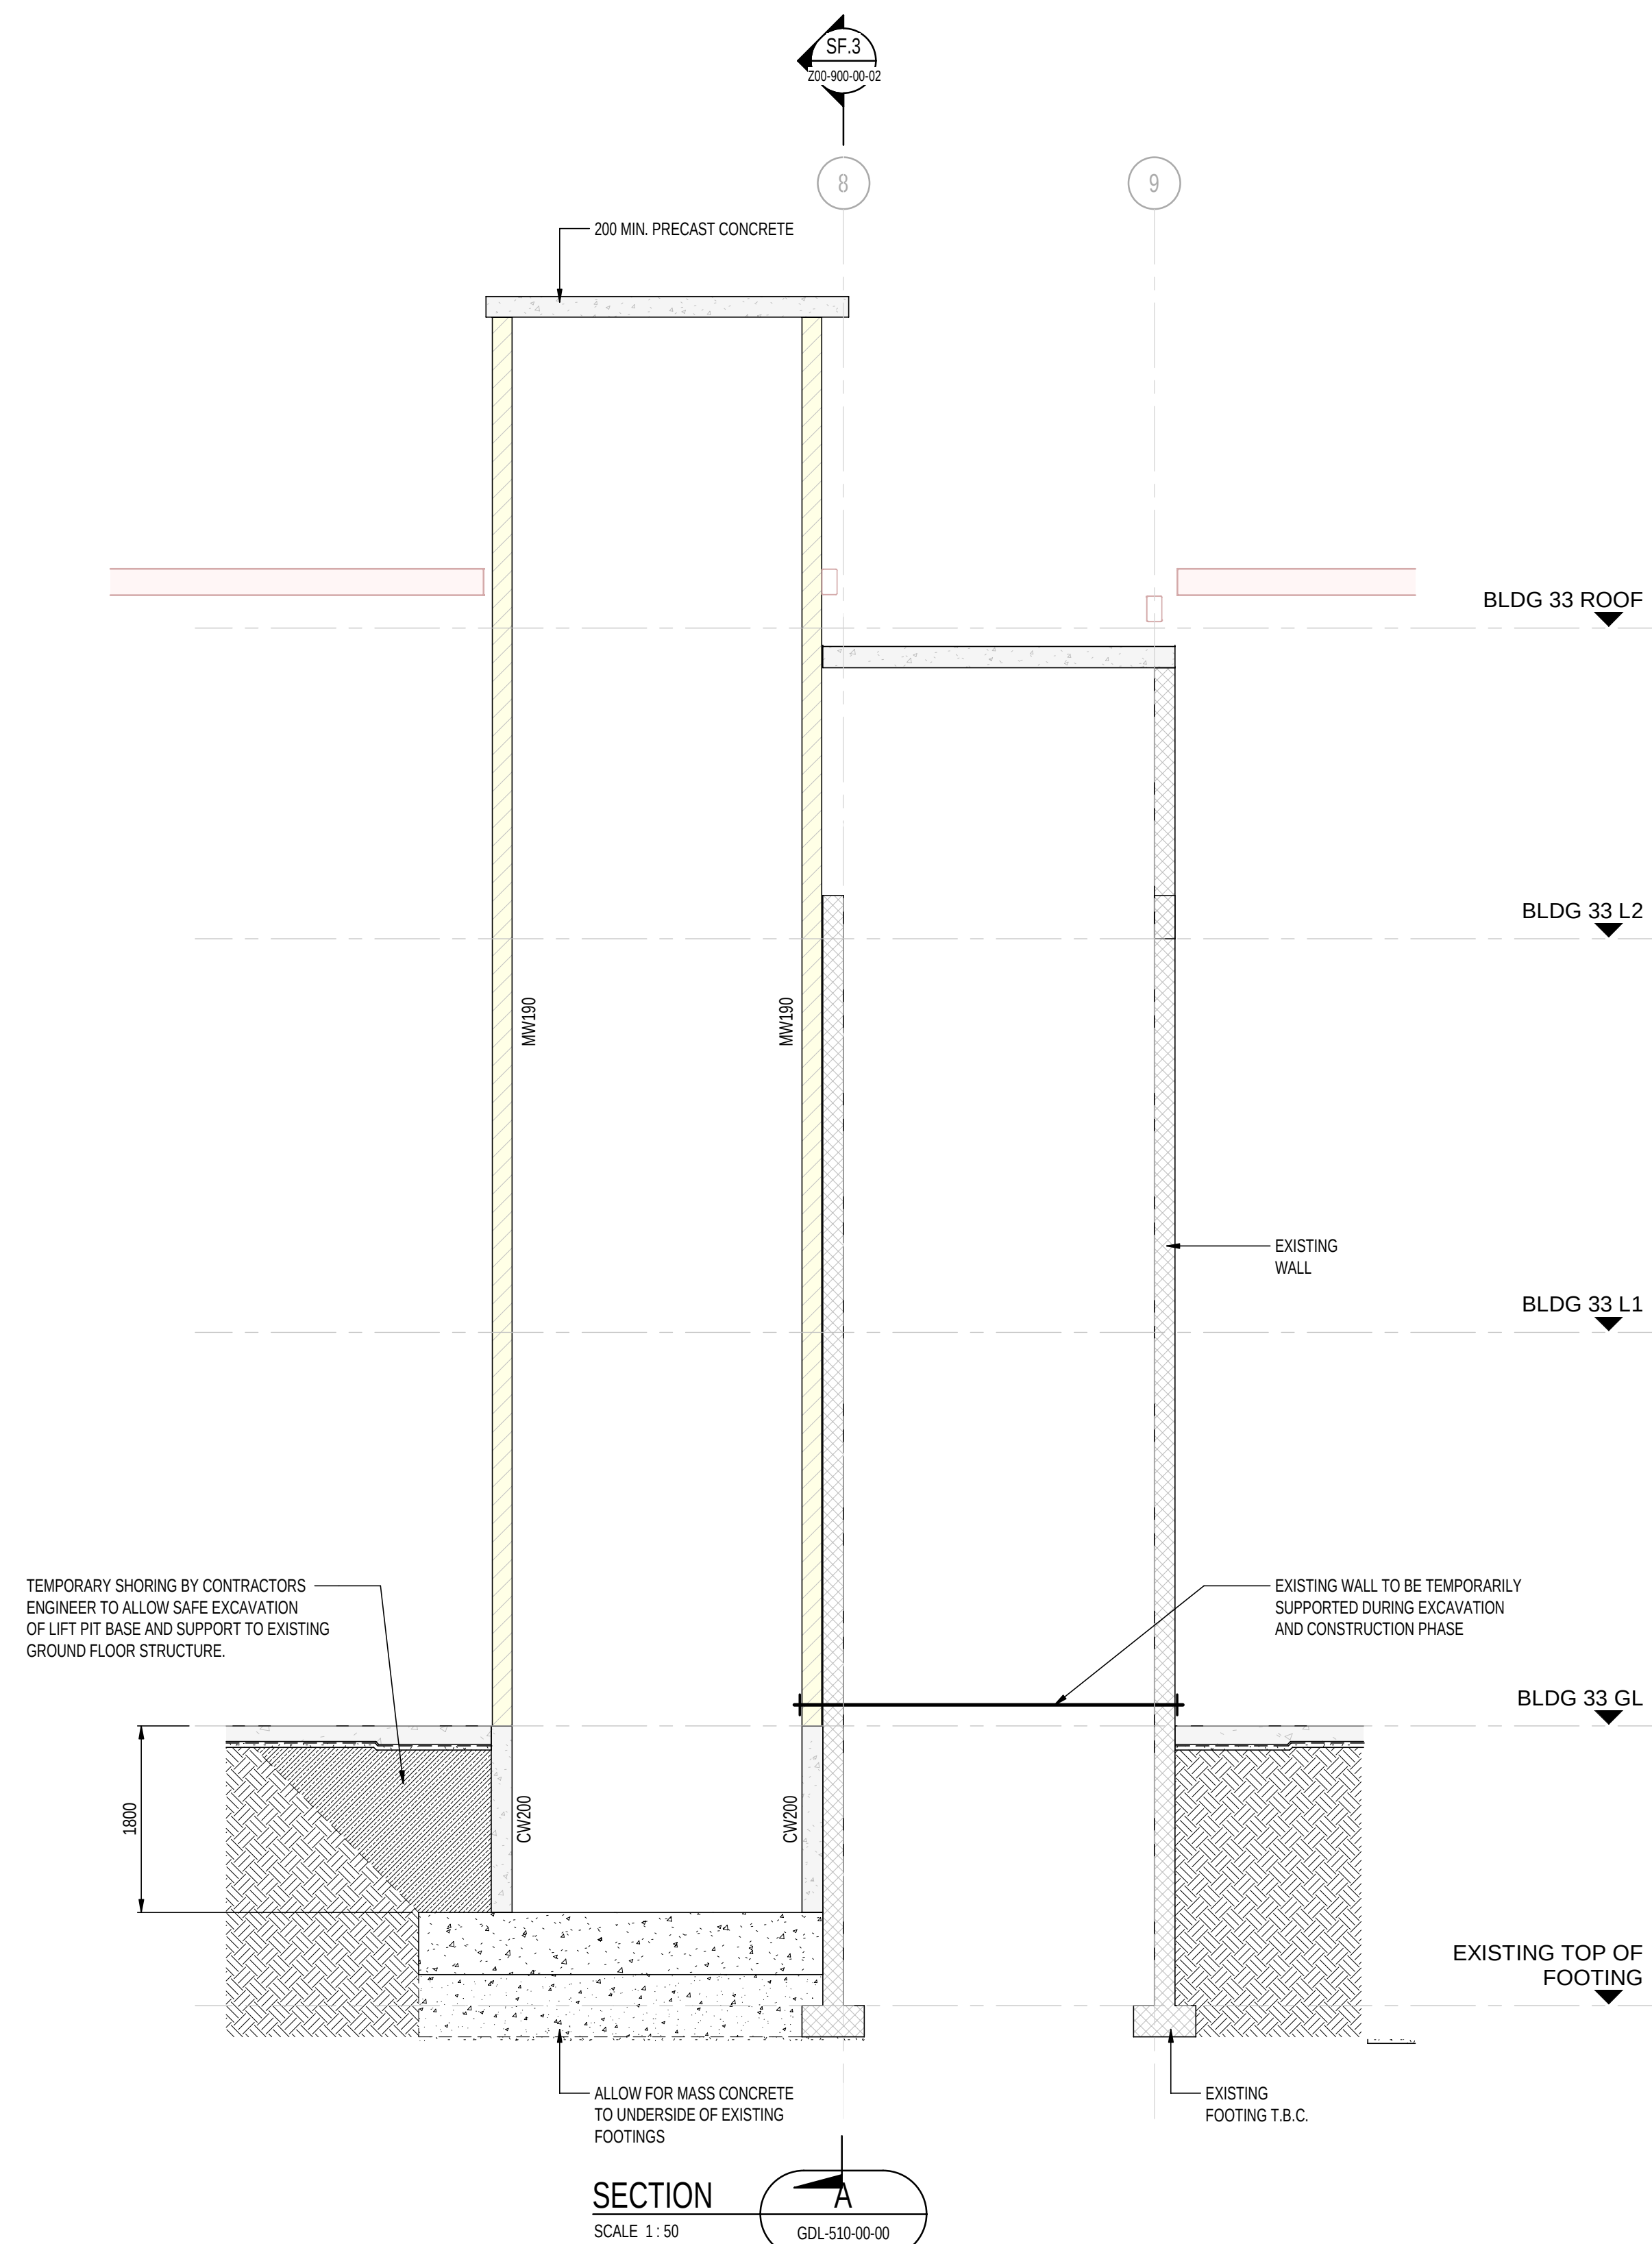

INFORMATION REFLECTED ON THIS DRAWING REPRESENTS STRUCTURAL DESIGN DEVELOPED FOR D&C TENDER ADVICE ONLY, AND SHOULD NOT BE REGARDED AS COMPLETE. THE D&C CONTRACTOR SHOULD REFER TO ALL ASSOCIATED ARCHITECTURAL AND OTHER DISCIPLINE DRAWINGS, PROJECT BRIEFS AND CLIENT REQUIREMENTS AND MAKE ADEQUATE ALLOWANCES FOR ALL NECESSARY STRUCTURAL WORKS TO MEET THESE REQUIREMENTS, EQUIPMENT SCHEDULES AND COMPLIANCE WITH THE NCC & APPROPRIATE AUSTRALIAN STANDARDS

A	12.02.2006	MSB	ISSUED FOR OAC TENDER					BM	DC
P1	30.01.2006	FB	DRAFT 60% DD ISSUE FOR REVIEW					JZ	DC
REV	DATE	BY	DESCRIPTION					CHK	APP
DRAWING STATUS: DESIGN DEVELOPMENT									



<http://www.wsp.com>

CLIENT:



THOMSON ADSETT + PEDDLE THORP

PROJECT:

CQU ROCKHAMPTON TAFE
CONSOLIDATION - STAGE 2

	TITLE:
--	--------

BUILDING 33
LEVEL G - SECTION AND DETAILS - SHEET 01

SCALE @ A1:

1:50

PROJECT NUMBER:
PS229518

CHECKED:

JZ

DRAWN:	DATE:
EGB	15.12.25

PROVED:

DG

TE:

15.12.25

A

© WSP Australia Pty Ltd