


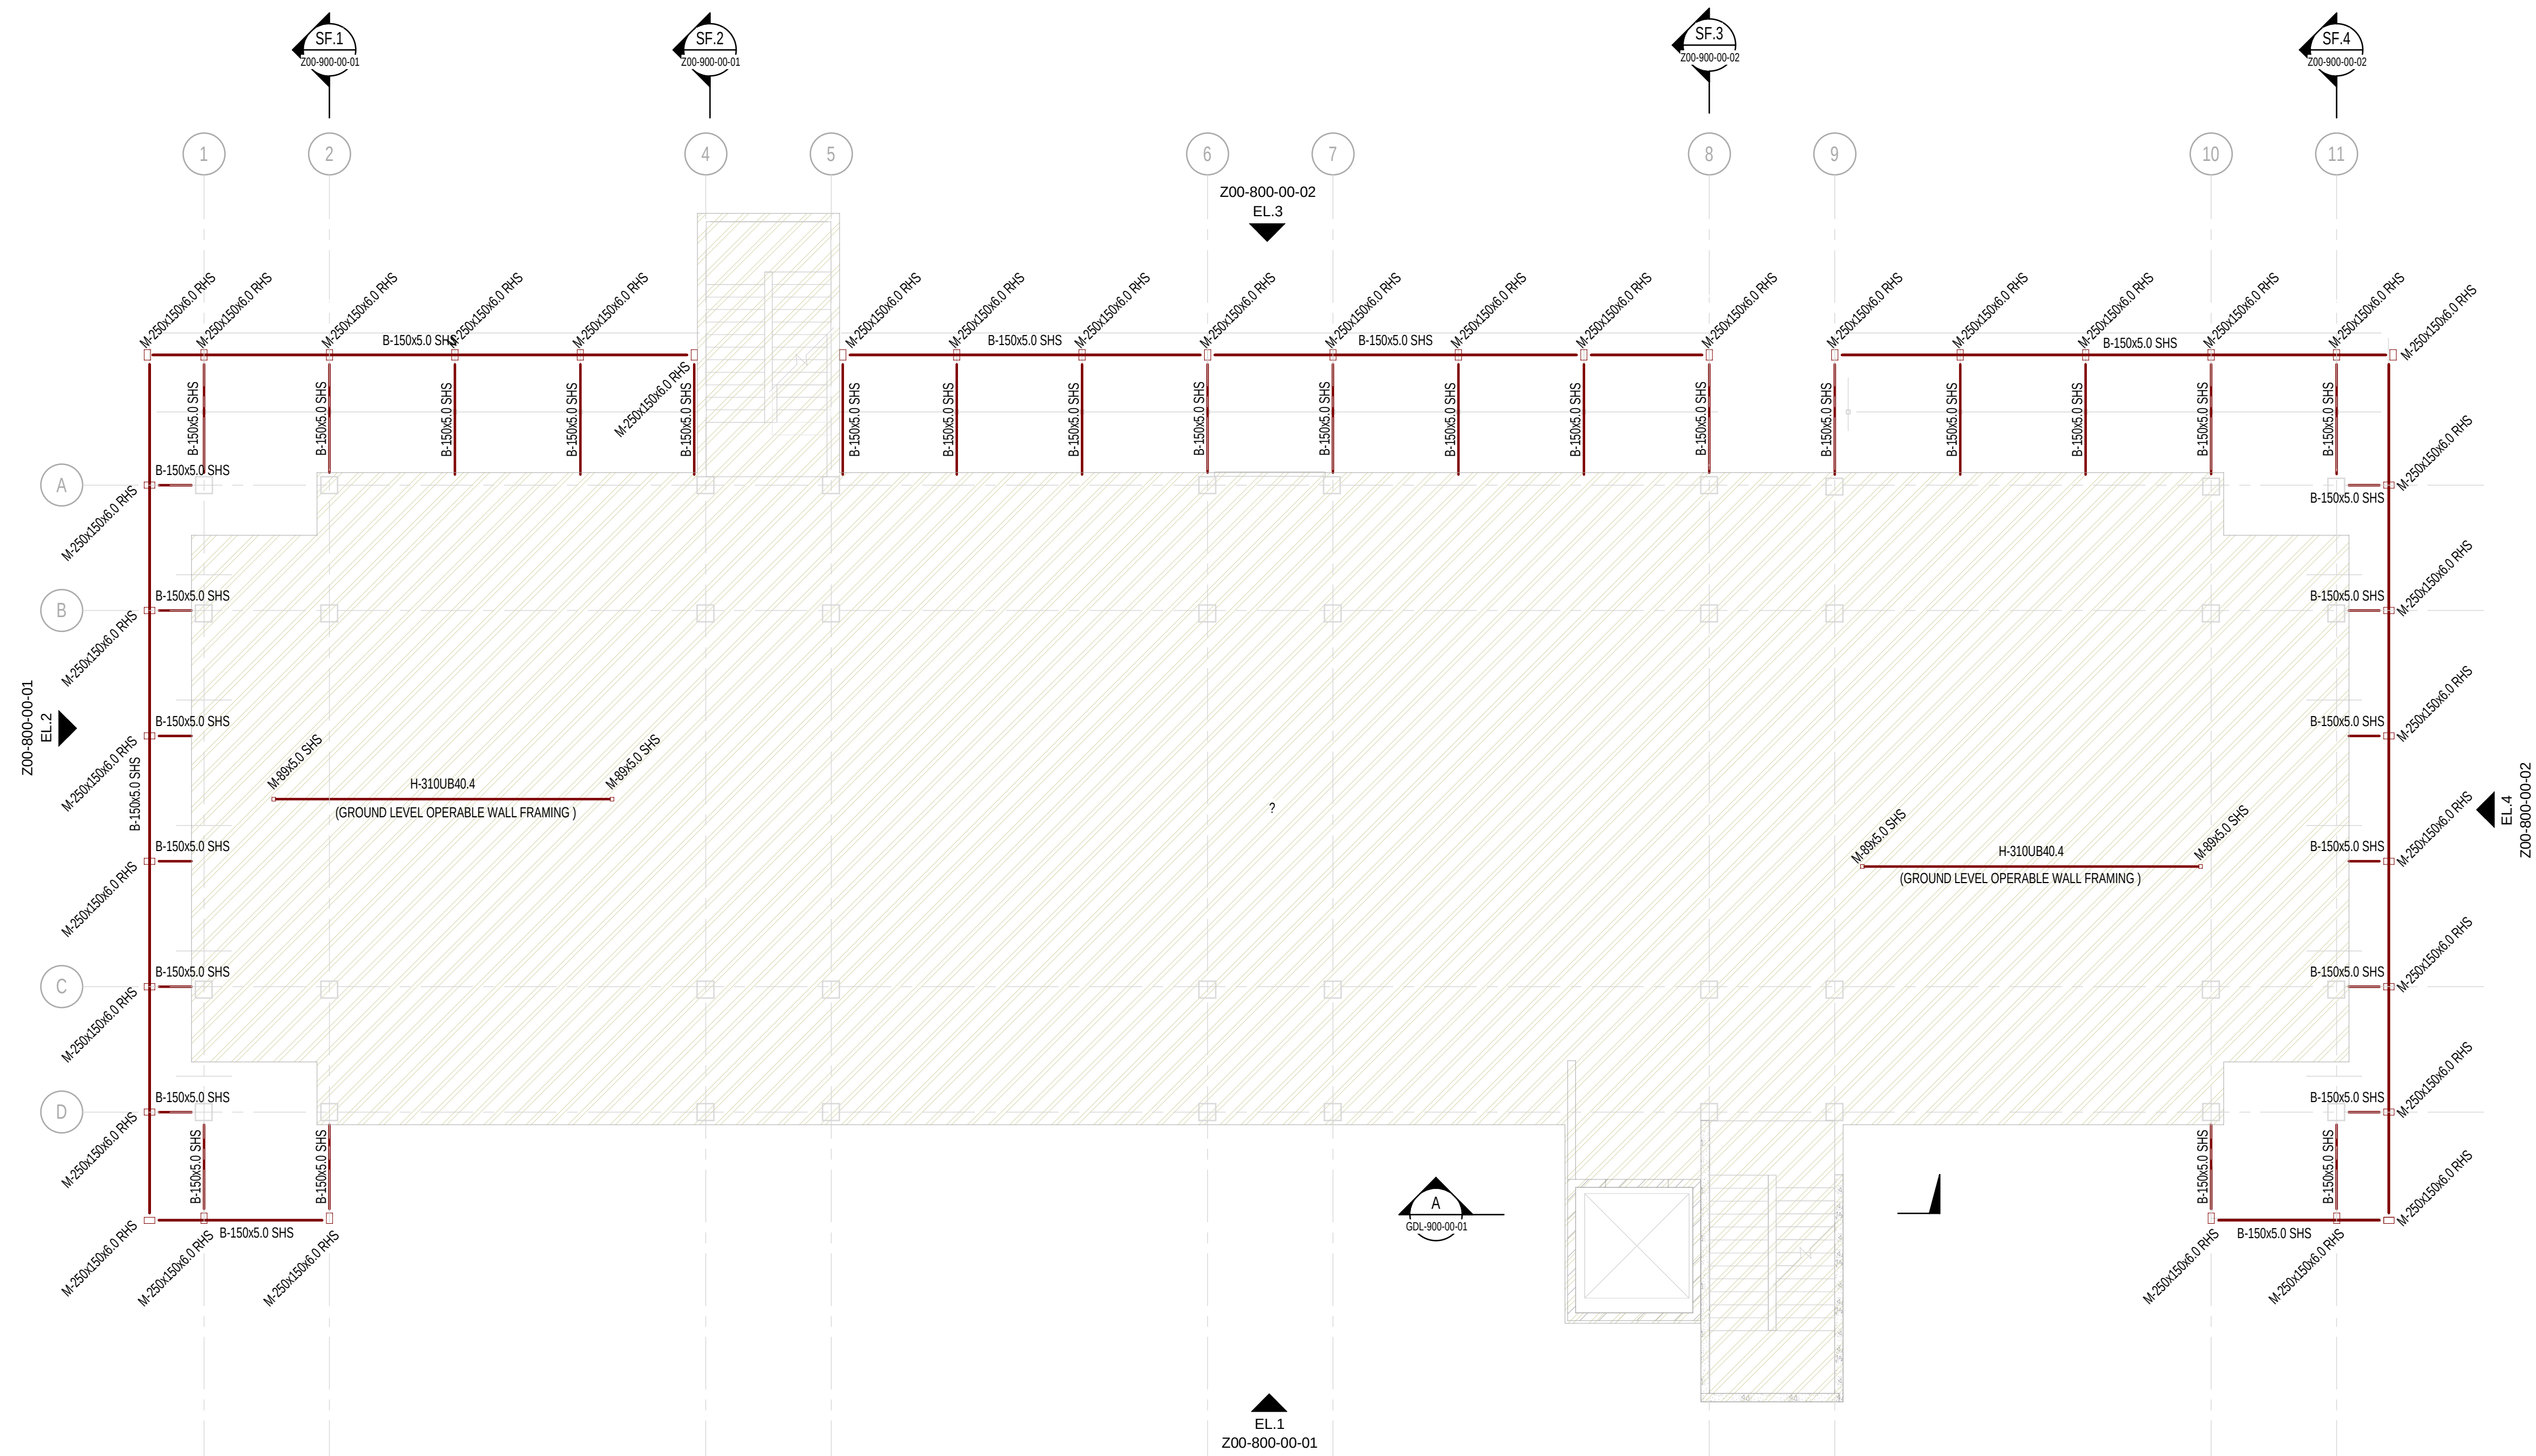

INFORMATION REFLECTED ON THIS DRAWING REPRESENTS STRUCTURAL DESIGN DEVELOPED FOR D&C TENDER ADVICE ONLY, AND SHOULD NOT BE REGARDED AS COMPLETE. THE D&C CONTRACTOR SHOULD REFER TO ALL ASSOCIATED ARCHITECTURAL AND OTHER DISCIPLINE DRAWINGS, PROJECT BRIEFS AND CLIENT REQUIREMENTS AND MAKE ADEQUATE ALLOWANCES FOR ALL NECESSARY STRUCTURAL WORKS TO MEET THESE REQUIREMENTS, EQUIPMENT SCHEDULES AND COMPLIANCE WITH THE NCC & APPROPRIATE AUSTRALIAN STANDARDS

A	12.02.2006	MSB		ISSUED FOR OAC TENDER	BW	DC
P1	30.01.2008	EB		DRAFT 6% DD ISSUE FOR REVIEW	JZ	DG
REV	DATE	BY		DESCRIPTION	CHK	APP
DRAWING STATUS:						
DESIGN DEVELOPMENT						



<http://www.wsp.com>

CLIENT:



THOMSON ADSETT + PEDDLE THORP

PROJECT:

CQU ROCKHAMPTON TAFE
CONSOLIDATION - STAGE 2

TITLE:

BUILDING 33
LEVEL 01 - SCREEN FRAMING PLAN

SCALE @ A1:

1:100

CHECKED:

JZ

PROVED:

OG

PROJECT NUMBER:

DRAWN:

50

DRAWING No:

33-ST-DR-L01-510-00-00

REV:

© WSP Australia Pty Ltd