

STEEL LEGEND:

	LOAD BEARING RC OVER
	LOAD BEARING PRECAST OVER
	LOAD BEARING MASONRY OVER
	STEEL
	LOAD BEARING RC UNDER
	LOAD BEARING PRECAST UNDER
	LOAD BEARING MASONRY UNDER
	STEEL UNDER
	REINFT TYPE PT = POST TENSIONED, RC = TRADITIONAL RC
	DENOTES SLAB THICKNESS REFER PLAN FOR SLAB THICKNESS
	Metal Deck Span Direction and Type
	DENOTES STEP LOCATION
	DENOTES CAST-IN PLATE CONNECTION LOCATION & TYPE. REFER TO DETAILS.
	DENOTES MOMENT SPLICE LOCATION & TYPE. REFER DETAILS.
	DENOTES RECTANGULAR BEAM WEB PENETRATION LOCATION & TYPE. REFER SCHEDULE.
	DENOTES CIRCULAR BEAM WEB PENETRATION LOCATION & TYPE. REFER SCHEDULE.
	DENOTES RECTANGULAR BEAM NOTCH LOCATION & TYPE. REFER SCHEDULE.
	COLUMNx/O DENOTES COLUMN OVER
	COLUMNx/U DENOTES COLUMN UNDER
	# DENOTES ROOF SUPPORT COLUMN
	(xx) DENOTES BEAM PRECAMBER IN MILLIMETRES
	<xx> DENOTES STUD TYPE - REFER SCHEDULE.

STEEL MEMBER MARKS:

	PREFIX = MEMBER FUNCTION / DESCRIPTION. REFER ABBREVIATIONS DRAWING T.B.C. FOR SCHEDULE OF DESCRIPTIONS
	MEMBER SIZE
	SUFFIX = MEMBER POSITION (IF SHOWN) REFER ABBREVIATIONS DRAWING T.B.C. FOR SCHEDULE OF MEMBER POSITIONS

STEELWORK ROOF:

NOTES:


CONTRACTOR TO ALLOW FOR ADDITIONAL PURLIN SUPPORTS UNDER ALL GUTTERS.

CONTRACTOR TO ALLOW FOR ADDITIONAL TRIMMER PURLINS AROUND ALL VOIDS. REFER TO ARCHITECTURAL & SERVICES DRAWINGS FOR FULL EXTENT OF PENETRATIONS THROUGH ROOF.

PLANT AREA PLATFORM & WALKWAYS TO BE DESIGN & SUPPLIED BY SPECIALIST. DETAILS TO BE ISSUED TO STRUCTURAL ENGINEER FOR FINALISATION OF DESIGN.

PLANT AREAS TO BE RE-CONFIRMED WITH STRUCTURAL ENGINEER PRIOR TO FABRICATION.

REFER TO ARCHITECT FOR WATERPROOFING & SET-OUT DETAILS.

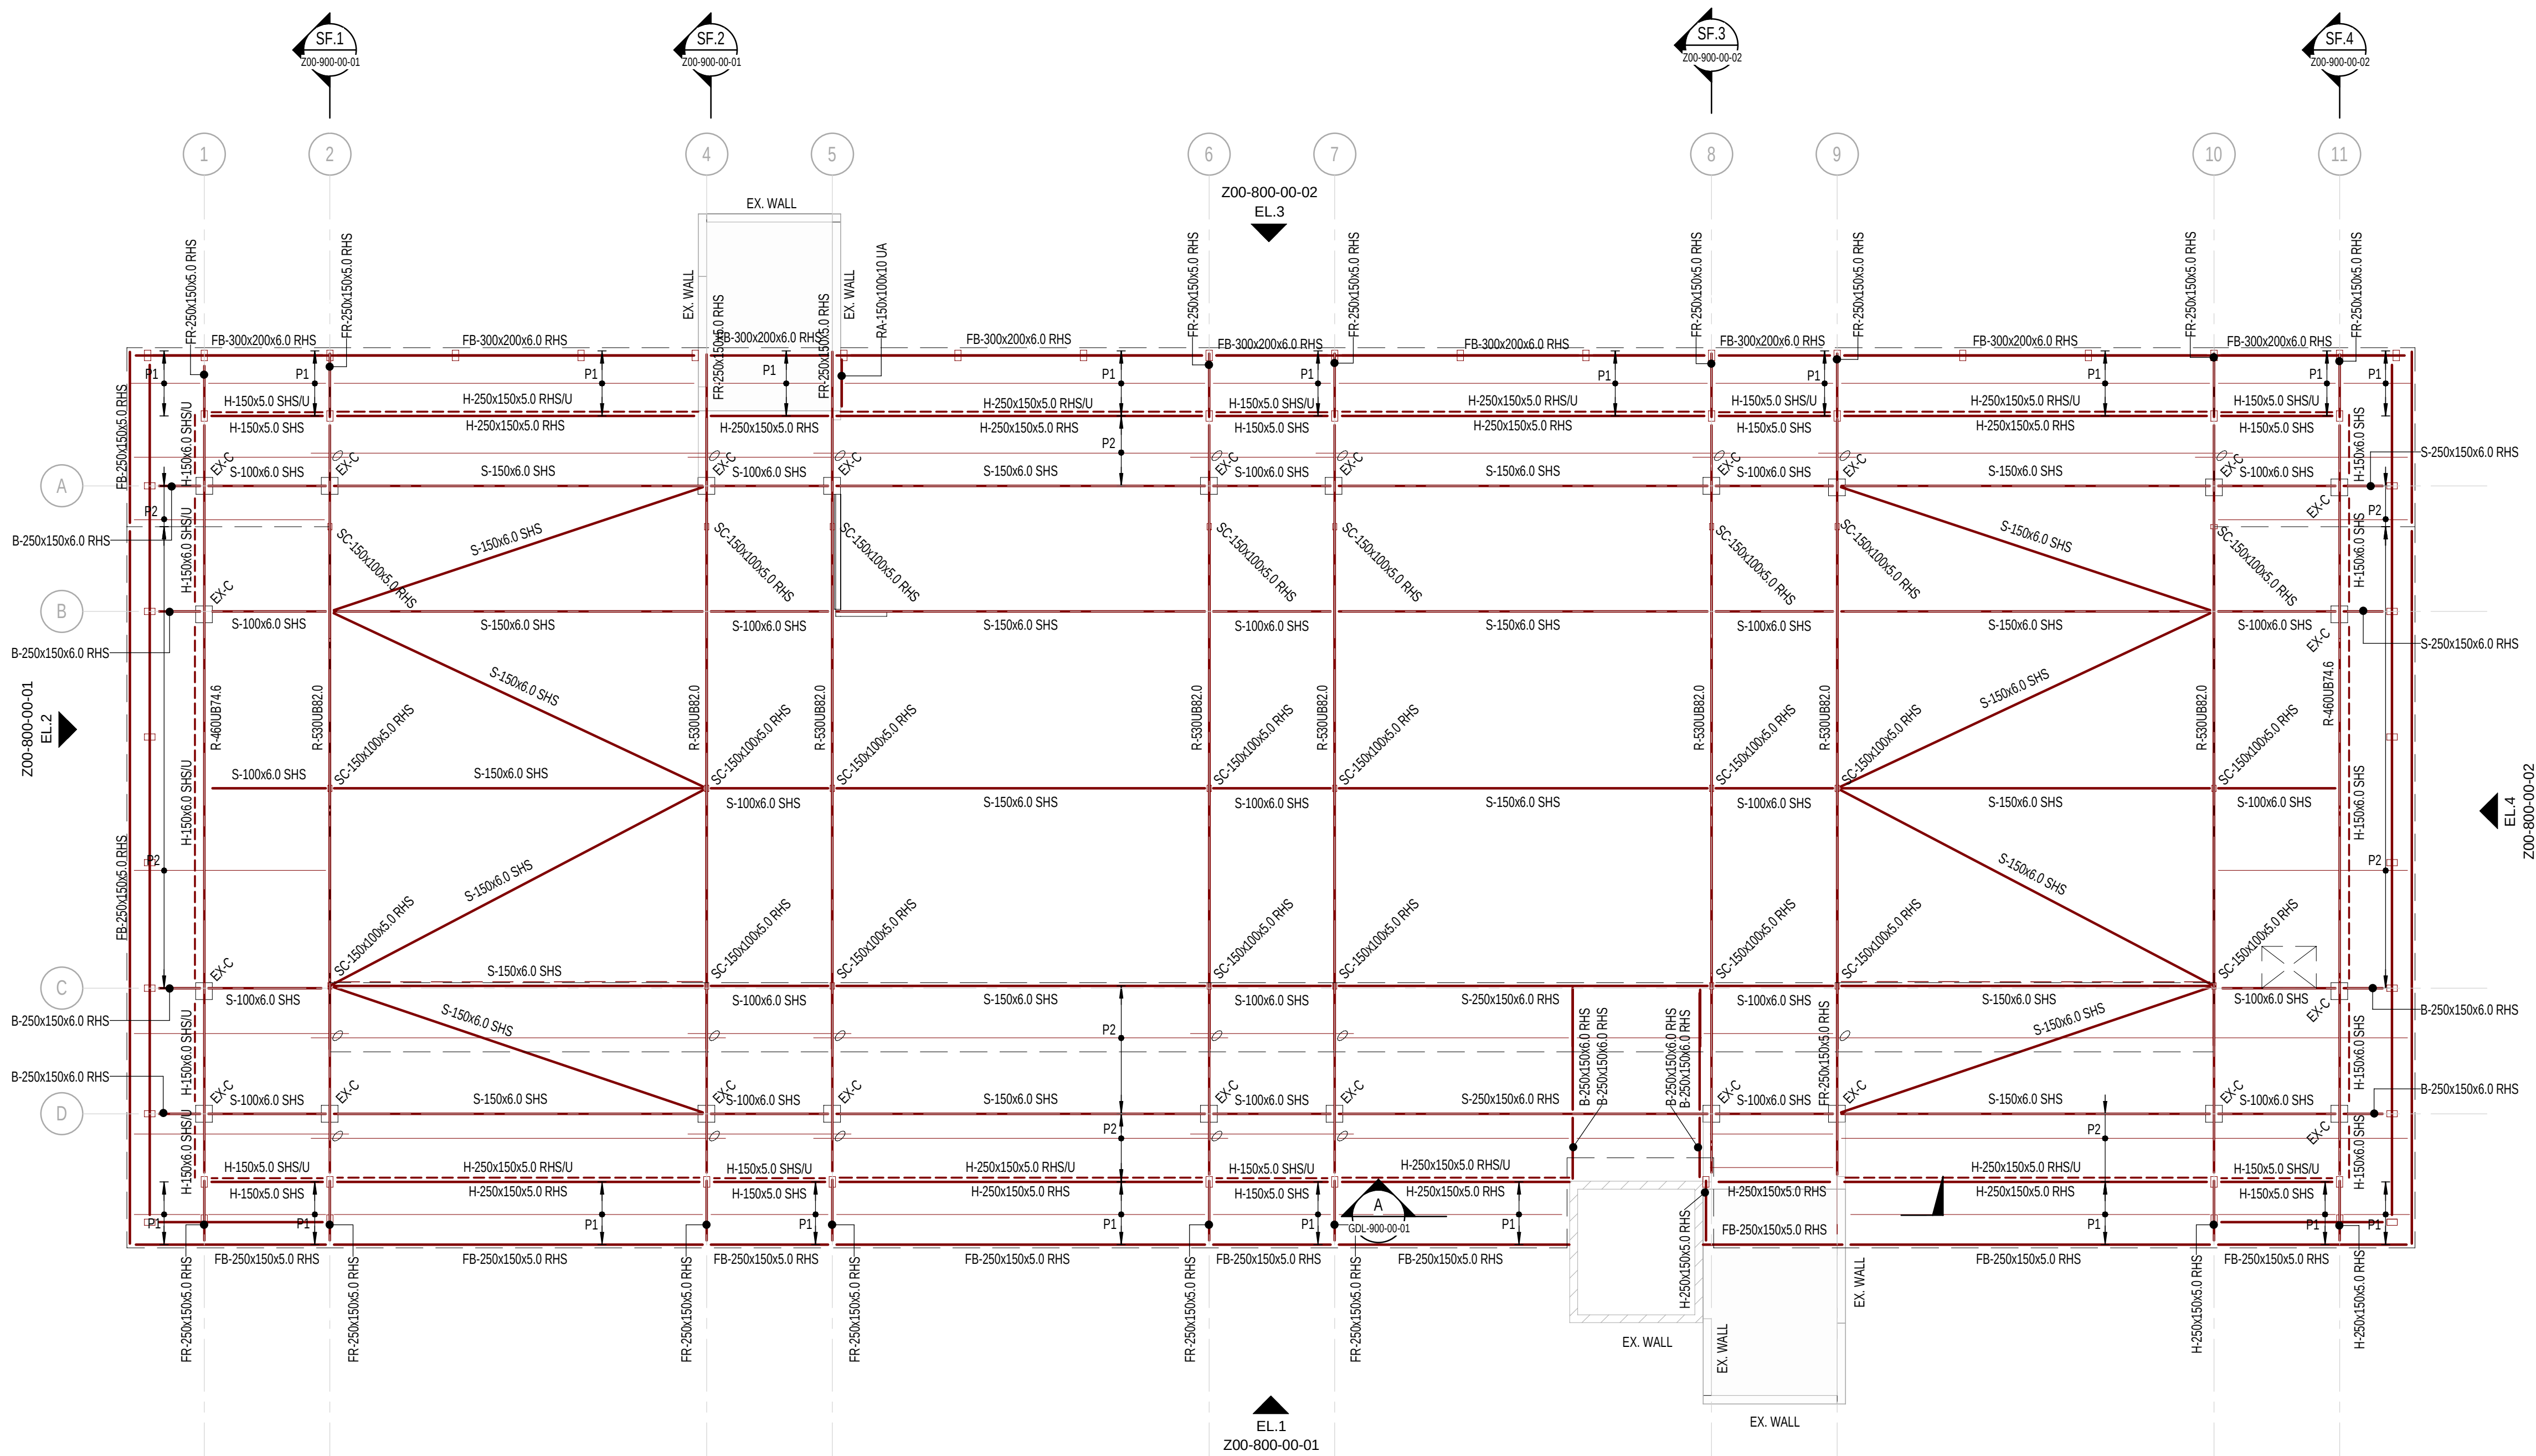

STEEL PURLINS SCHEDULE

MARK	SIZE	COMMENTS
P1	C250-24	PURLINS AT 800 MAX CRS.
P2	Z250-19	PURLINS AT 800 MAX CRS. CONTINUOUSLY LAPPED. (ALLOW FLY BRACING AT EVERY 3rd PURLIN)

INFORMATION REFLECTED ON THIS DRAWING REPRESENTS STRUCTURAL DESIGN DEVELOPED FOR D&C TENDER ADVICE ONLY, AND SHOULD NOT BE REGARDED AS COMPLETE. THE D&C CONTRACTOR SHOULD REFER TO ALL ASSOCIATED ARCHITECTURAL AND OTHER DISCIPLINE DRAWINGS, PROJECT BRIEFS AND CLIENT REQUIREMENTS AND MAKE ADEQUATE ALLOWANCES FOR ALL NECESSARY STRUCTURAL WORKS TO MEET THESE REQUIREMENTS, EQUIPMENT SCHEDULES AND COMPLIANCE WITH THE NCC & APPROPRIATE AUSTRALIAN STANDARDS

A	12.02.2026	MSB	ISSUED FOR D&C TENDER	BM	DG
PL	30.01.2026	EB	DRAFT 60% DD ISSUE FOR REVIEW	JZ	DG
REV	DATE	BY	DESCRIPTION	CHK	APP
DRAWING STATUS: DESIGN DEVELOPMENT					

<http://www.wsp.com>

CLIENT:



THOMSON ADSETT + PEDDLE THORP

PROJECT:

CQU ROCKHAMPTON TAFE
CONSOLIDATION - STAGE 2

TITLE:

BUILDING 33
LOWER ROOF FRAMING PLAN

SCALE @ AL:

1:100

CHECKED:

JZ

APPROVED:

DG

PROJECT NUMBER:

PS229518

DRAWN:

EGB

DATE:

15.12.25

DRAWING No:

33-ST-DR-Z00-710-00-00

REV:

A

© WSP Australia Pty Ltd