


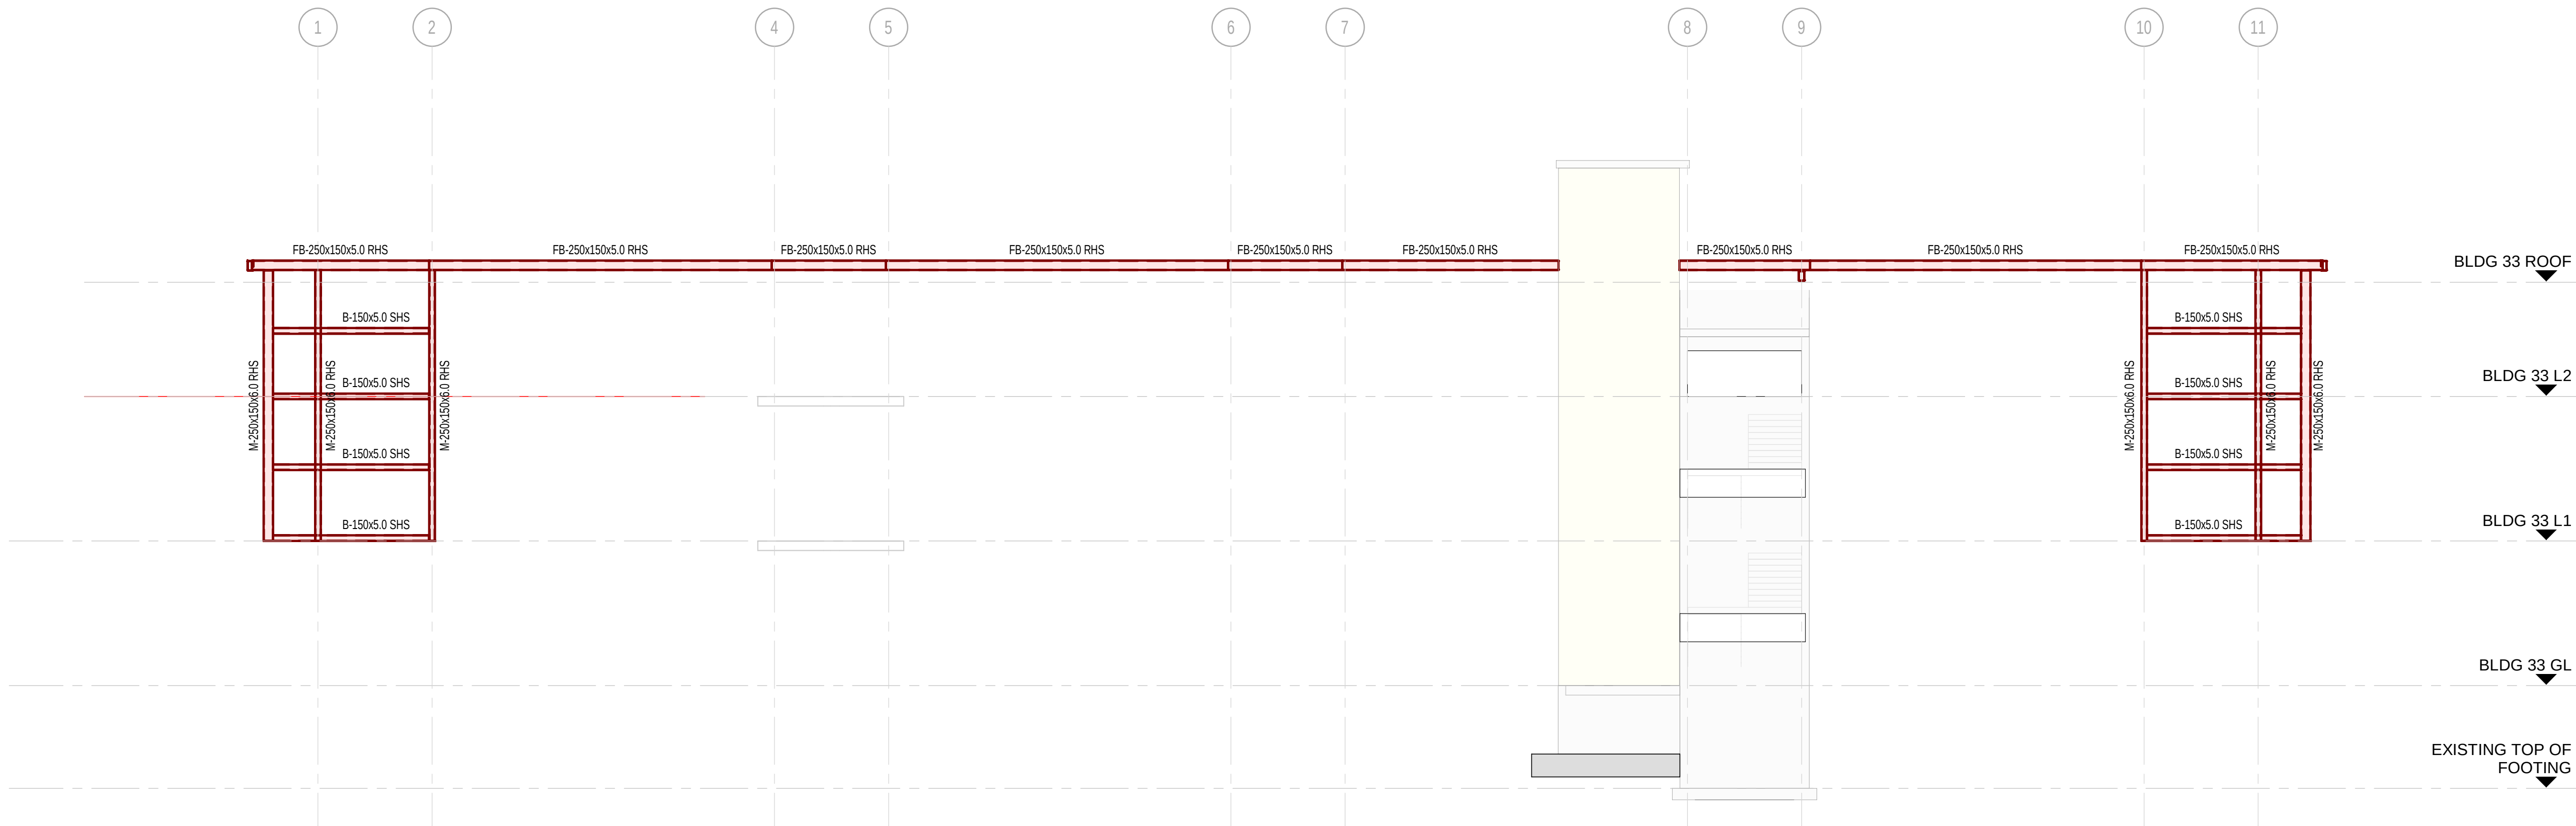

ELEVATION **EL.1** SOUTH ELEVATION
SCALE 1:100 GDL-510-00-00



ELEVATION **EL.2** WEST ELEVATION
SCALE 1:100 GDL-510-00-00

INFORMATION REFLECTED ON THIS DRAWING REPRESENTS STRUCTURAL DESIGN DEVELOPED FOR D&C TENDER ADVICE ONLY, AND SHOULD NOT BE REGARDED AS COMPLETE. THE D&C CONTRACTOR SHOULD REFER TO ALL ASSOCIATED ARCHITECTURAL AND OTHER DISCIPLINE DRAWINGS, PROJECT BRIEFS AND CLIENT REQUIREMENTS AND MAKE ADEQUATE ALLOWANCES FOR ALL NECESSARY STRUCTURAL WORKS TO MEET THESE REQUIREMENTS, EQUIPMENT SCHEDULES AND COMPLIANCE WITH THE NCC & APPROPRIATE AUSTRALIAN STANDARDS

A	12.02.2026	MSB	ISSUED FOR D&C TENDER	BM	DG
P1	30.01.2026	EB	DRAFT 60% DD ISSUE FOR REVIEW	JZ	DG
REV	DATE	BY	DESCRIPTION	CHK	APP
DRAWING STATUS: DESIGN DEVELOPMENT					



<http://www.wsp.com>

CLIENT:

ARCHITECT:
THOMSON ADSETT + PEDDLE THORP

PROJECT:
CQU ROCKHAMPTON TAFE
CONSOLIDATION - STAGE 2
TITLE:
BUILDING 33
BUILDING ELEVATIONS - SHEET 01

SCALE @ A1: 1:100	CHECKED: JZ	APPROVED: DG
PROJECT NUMBER: PS229518	DRAWN: EGB	DATE: 15.12.25
DRAWING No: 33-ST-DR-Z00-800-00-01		REV: A
© WSP Australia Pty Ltd		