


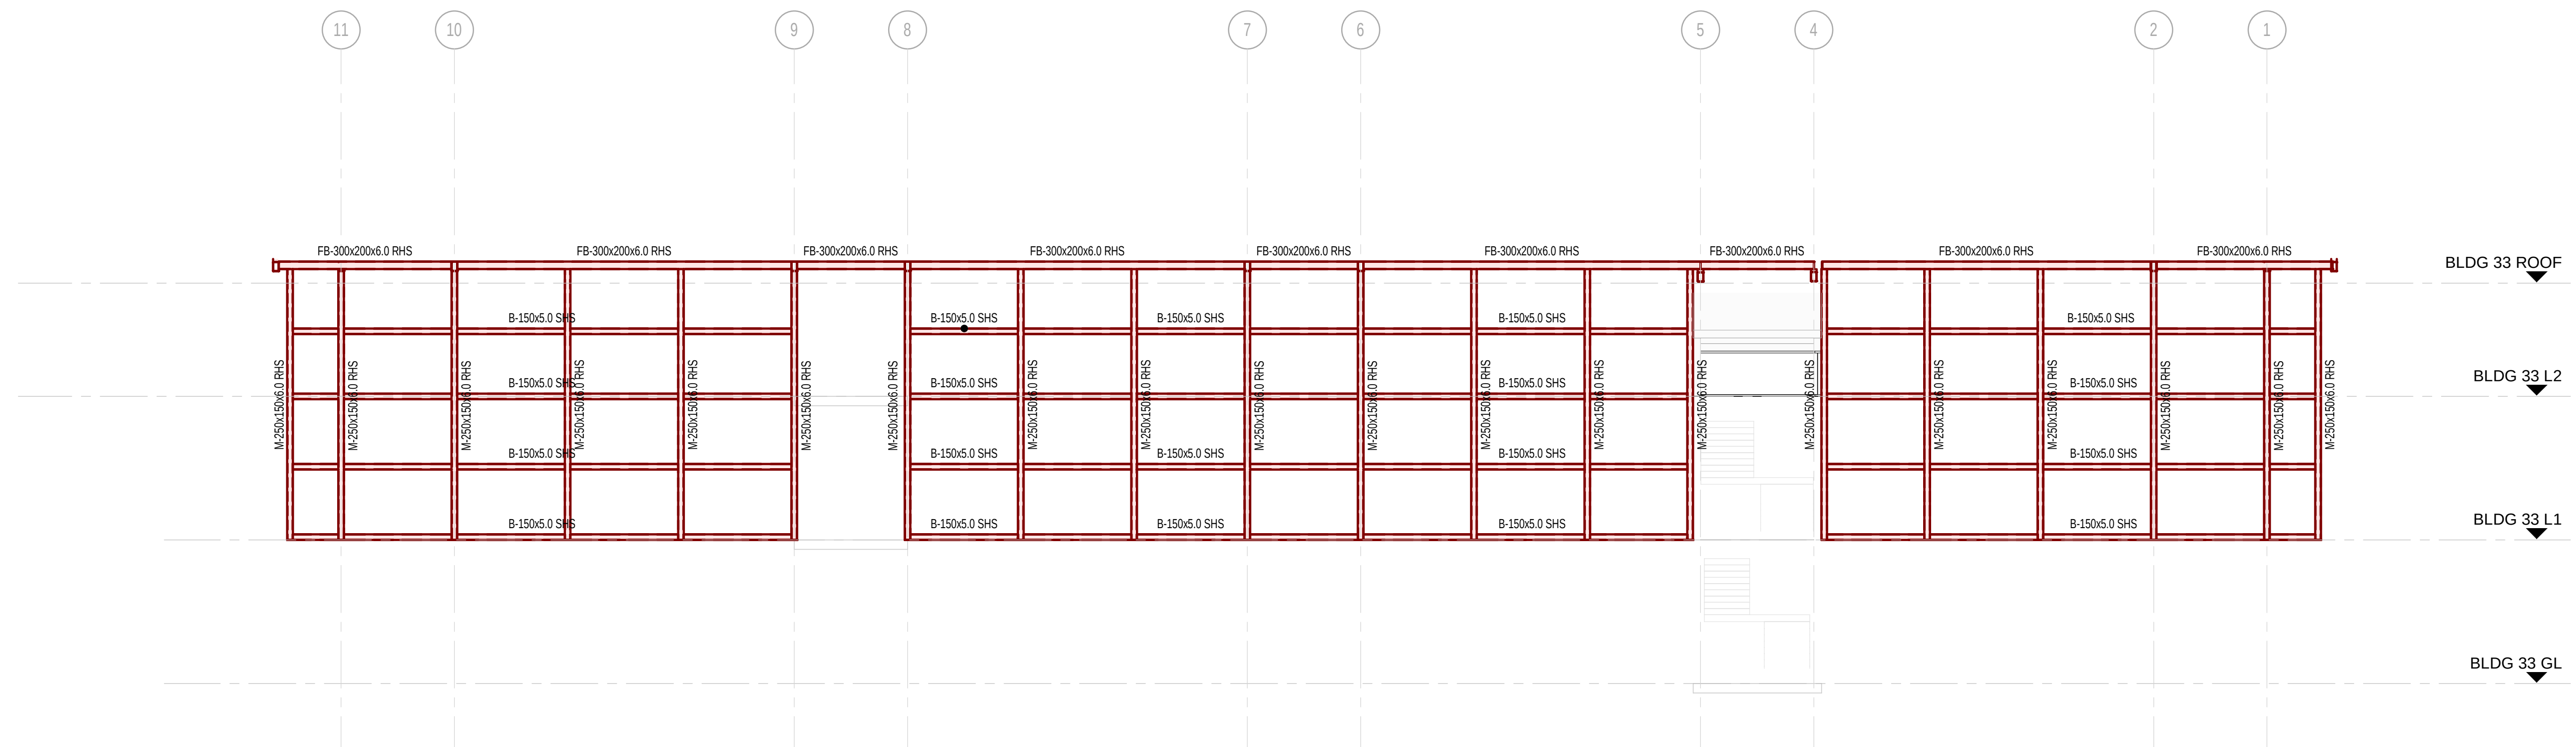

ELEVATION 1 NORTH ELEVATION
 SCALE 1:100 GDL-510-00-00



ELEVATION 2 EAST ELEVATION
SCALE 1:100 GDL-510-00-00

INFORMATION REFLECTED ON THIS DRAWING REPRESENTS STRUCTURAL DESIGN DEVELOPED FOR D&C TENDER ADVICE ONLY, AND SHOULD NOT BE REGARDED AS COMPLETE. THE D&C CONTRACTOR SHOULD REFER TO ALL ASSOCIATED ARCHITECTURAL AND OTHER DISCIPLINE DRAWINGS, PROJECT BRIEFS AND CLIENT REQUIREMENTS AND MAKE ADEQUATE ALLOWANCES FOR ALL NECESSARY STRUCTURAL WORKS TO MEET THESE REQUIREMENTS, EQUIPMENT SCHEDULES AND COMPLIANCE WITH THE NCC & APPROPRIATE AUSTRALIAN STANDARDS

[illegible]

CLIENT:

 **CQUniversity**
AUSTRALIA

ARCHITECT:

THOMSON ADSETT + PEDDLE THORP

PROJECT:

CQU ROCKHAMPTON TAFE
CONSOLIDATION - STAGE 2

TITLE:

BUILDING 33
BUILDING ELEVATIONS - SHEET 02

SCALE @ AL:	CHECKED:	APPROVED:
1:100	JZ	DG
PROJECT NUMBER:	DRAWN:	DATE:
PS229518	EGB	15.12.25
DRAWING NO:		REV:
33-ST-DR-Z00-800-00-02		A
© WSP Australia Pty Ltd		