



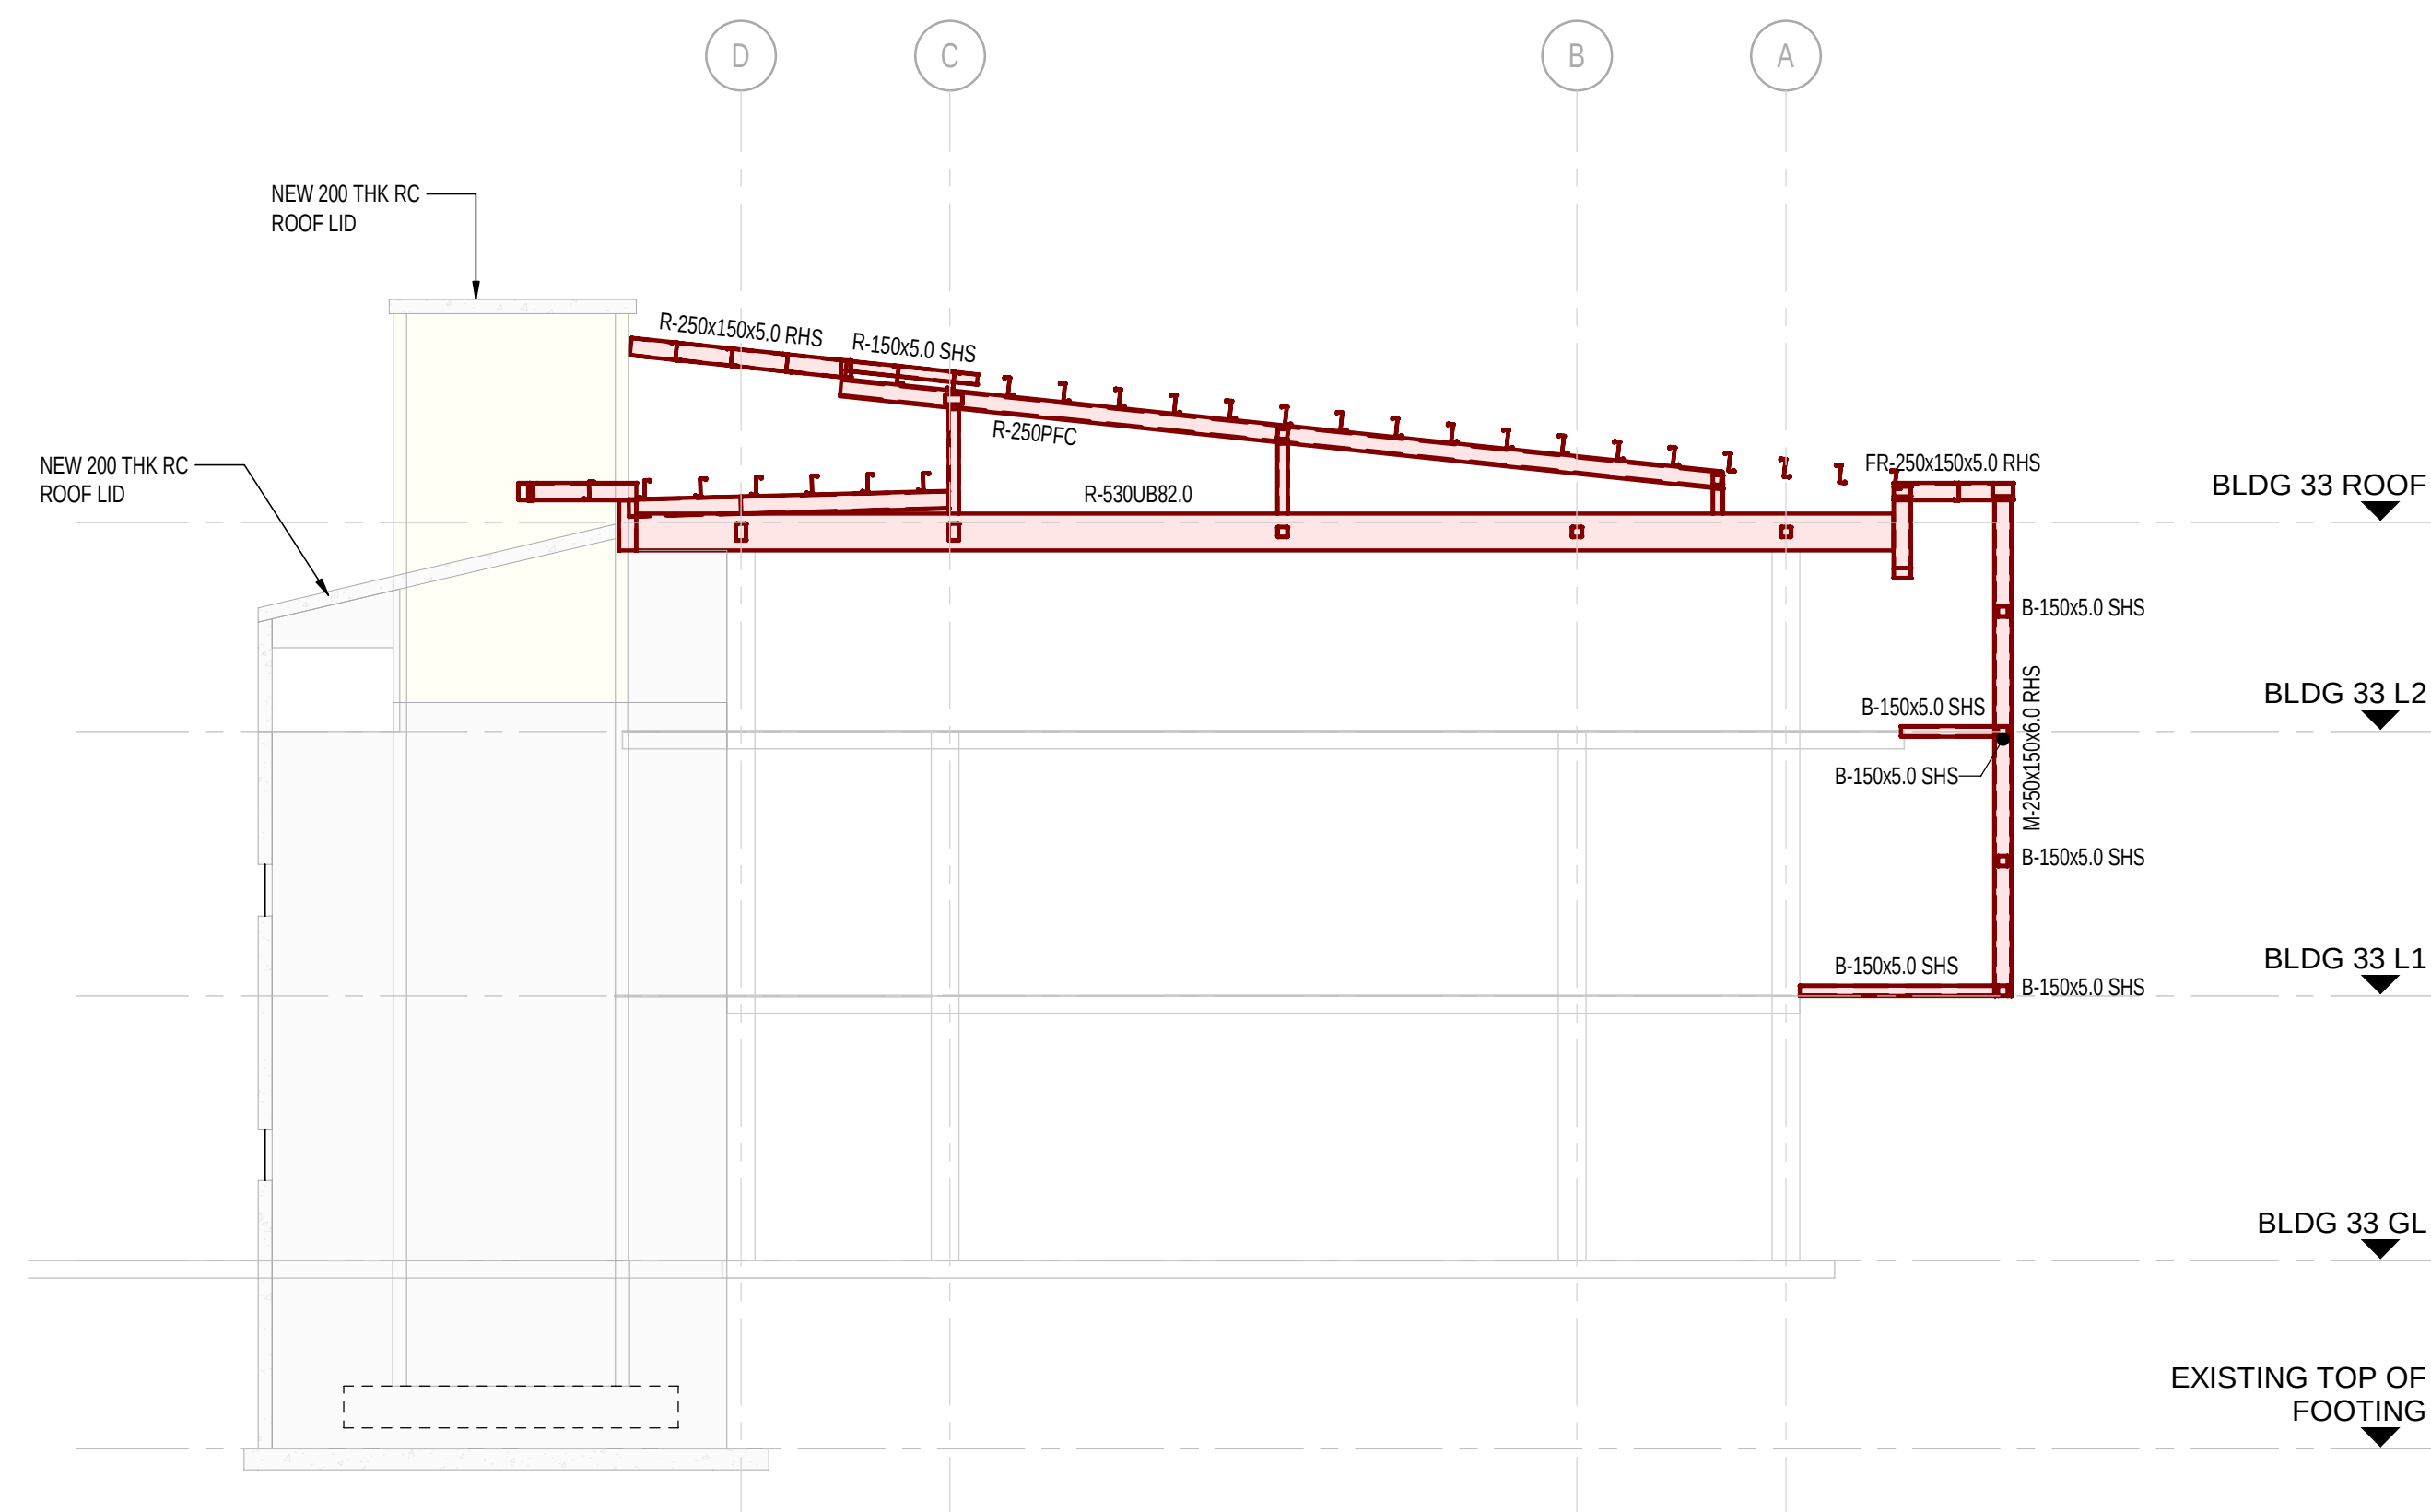

SECTION
SCALE 1:100

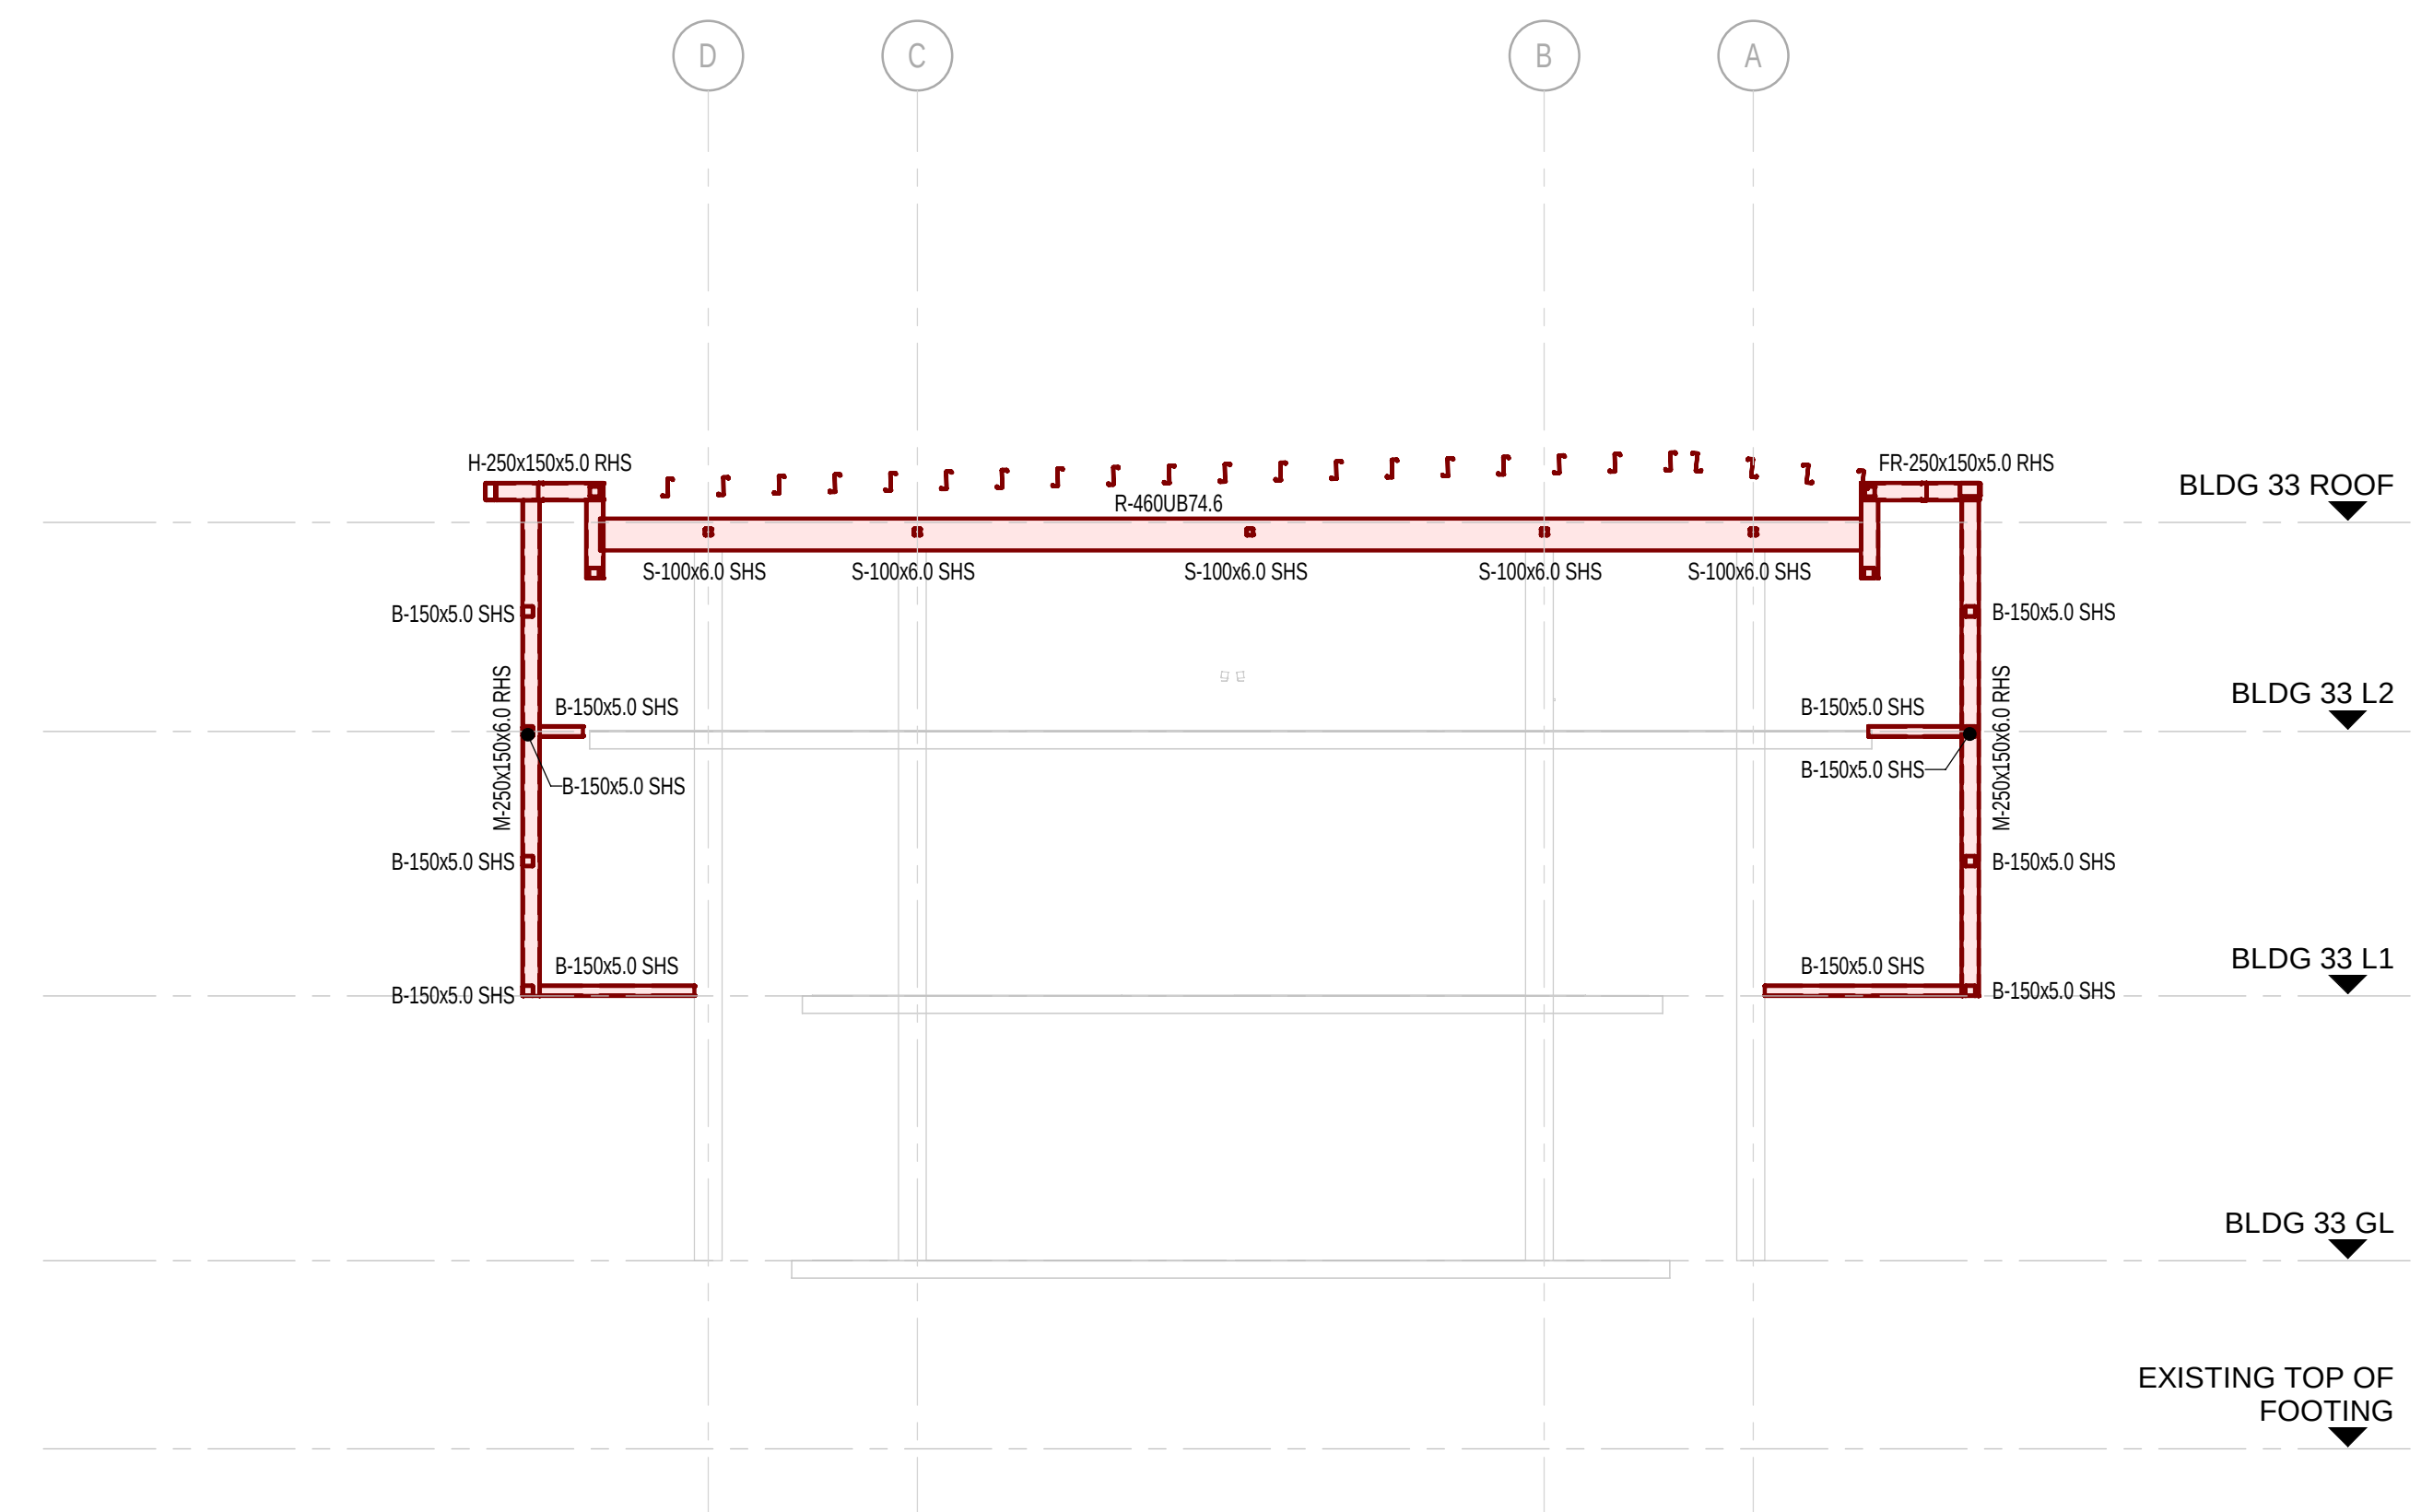

SECTION
SCALE 1 : 100

INFORMATION REFLECTED ON THIS DRAWING REPRESENTS STRUCTURAL DESIGN DEVELOPED FOR D&C TENDER ADVICE ONLY, AND SHOULD NOT BE REGARDED AS COMPLETE. THE D&C CONTRACTOR SHOULD REFER TO ALL ASSOCIATED ARCHITECTURAL AND OTHER DISCIPLINE DRAWINGS, PROJECT BRIEFS AND CLIENT REQUIREMENTS AND MAKE ADEQUATE ALLOWANCES FOR ALL NECESSARY STRUCTURAL WORKS TO MEET THESE REQUIREMENTS, EQUIPMENT SCHEDULES AND COMPLIANCE WITH THE NCC & APPROPRIATE AUSTRALIAN STANDARDS

[illegible]

<http://www.wsp.com>

CLIENT:



THOMSON ADSETT + PEDDLE THORP

PROJECT:

CQU ROCKHAMPTON TAFE
CONSOLIDATION - STAGE 2

TITLE:	
--------	--

BUILDING 33
BUILDING SECTIONS - SHEET 02

SCALE @ A1:

1:100

PROJECT NUMBER:
PS229518

CHECKED:	
----------	--

JZ

APPROVED:

DG

DATE: 15.12.25

DRAWING No:

33-ST-DR-Z00-900-00-02

EV:

A

© WSP Australia Pty Ltd