


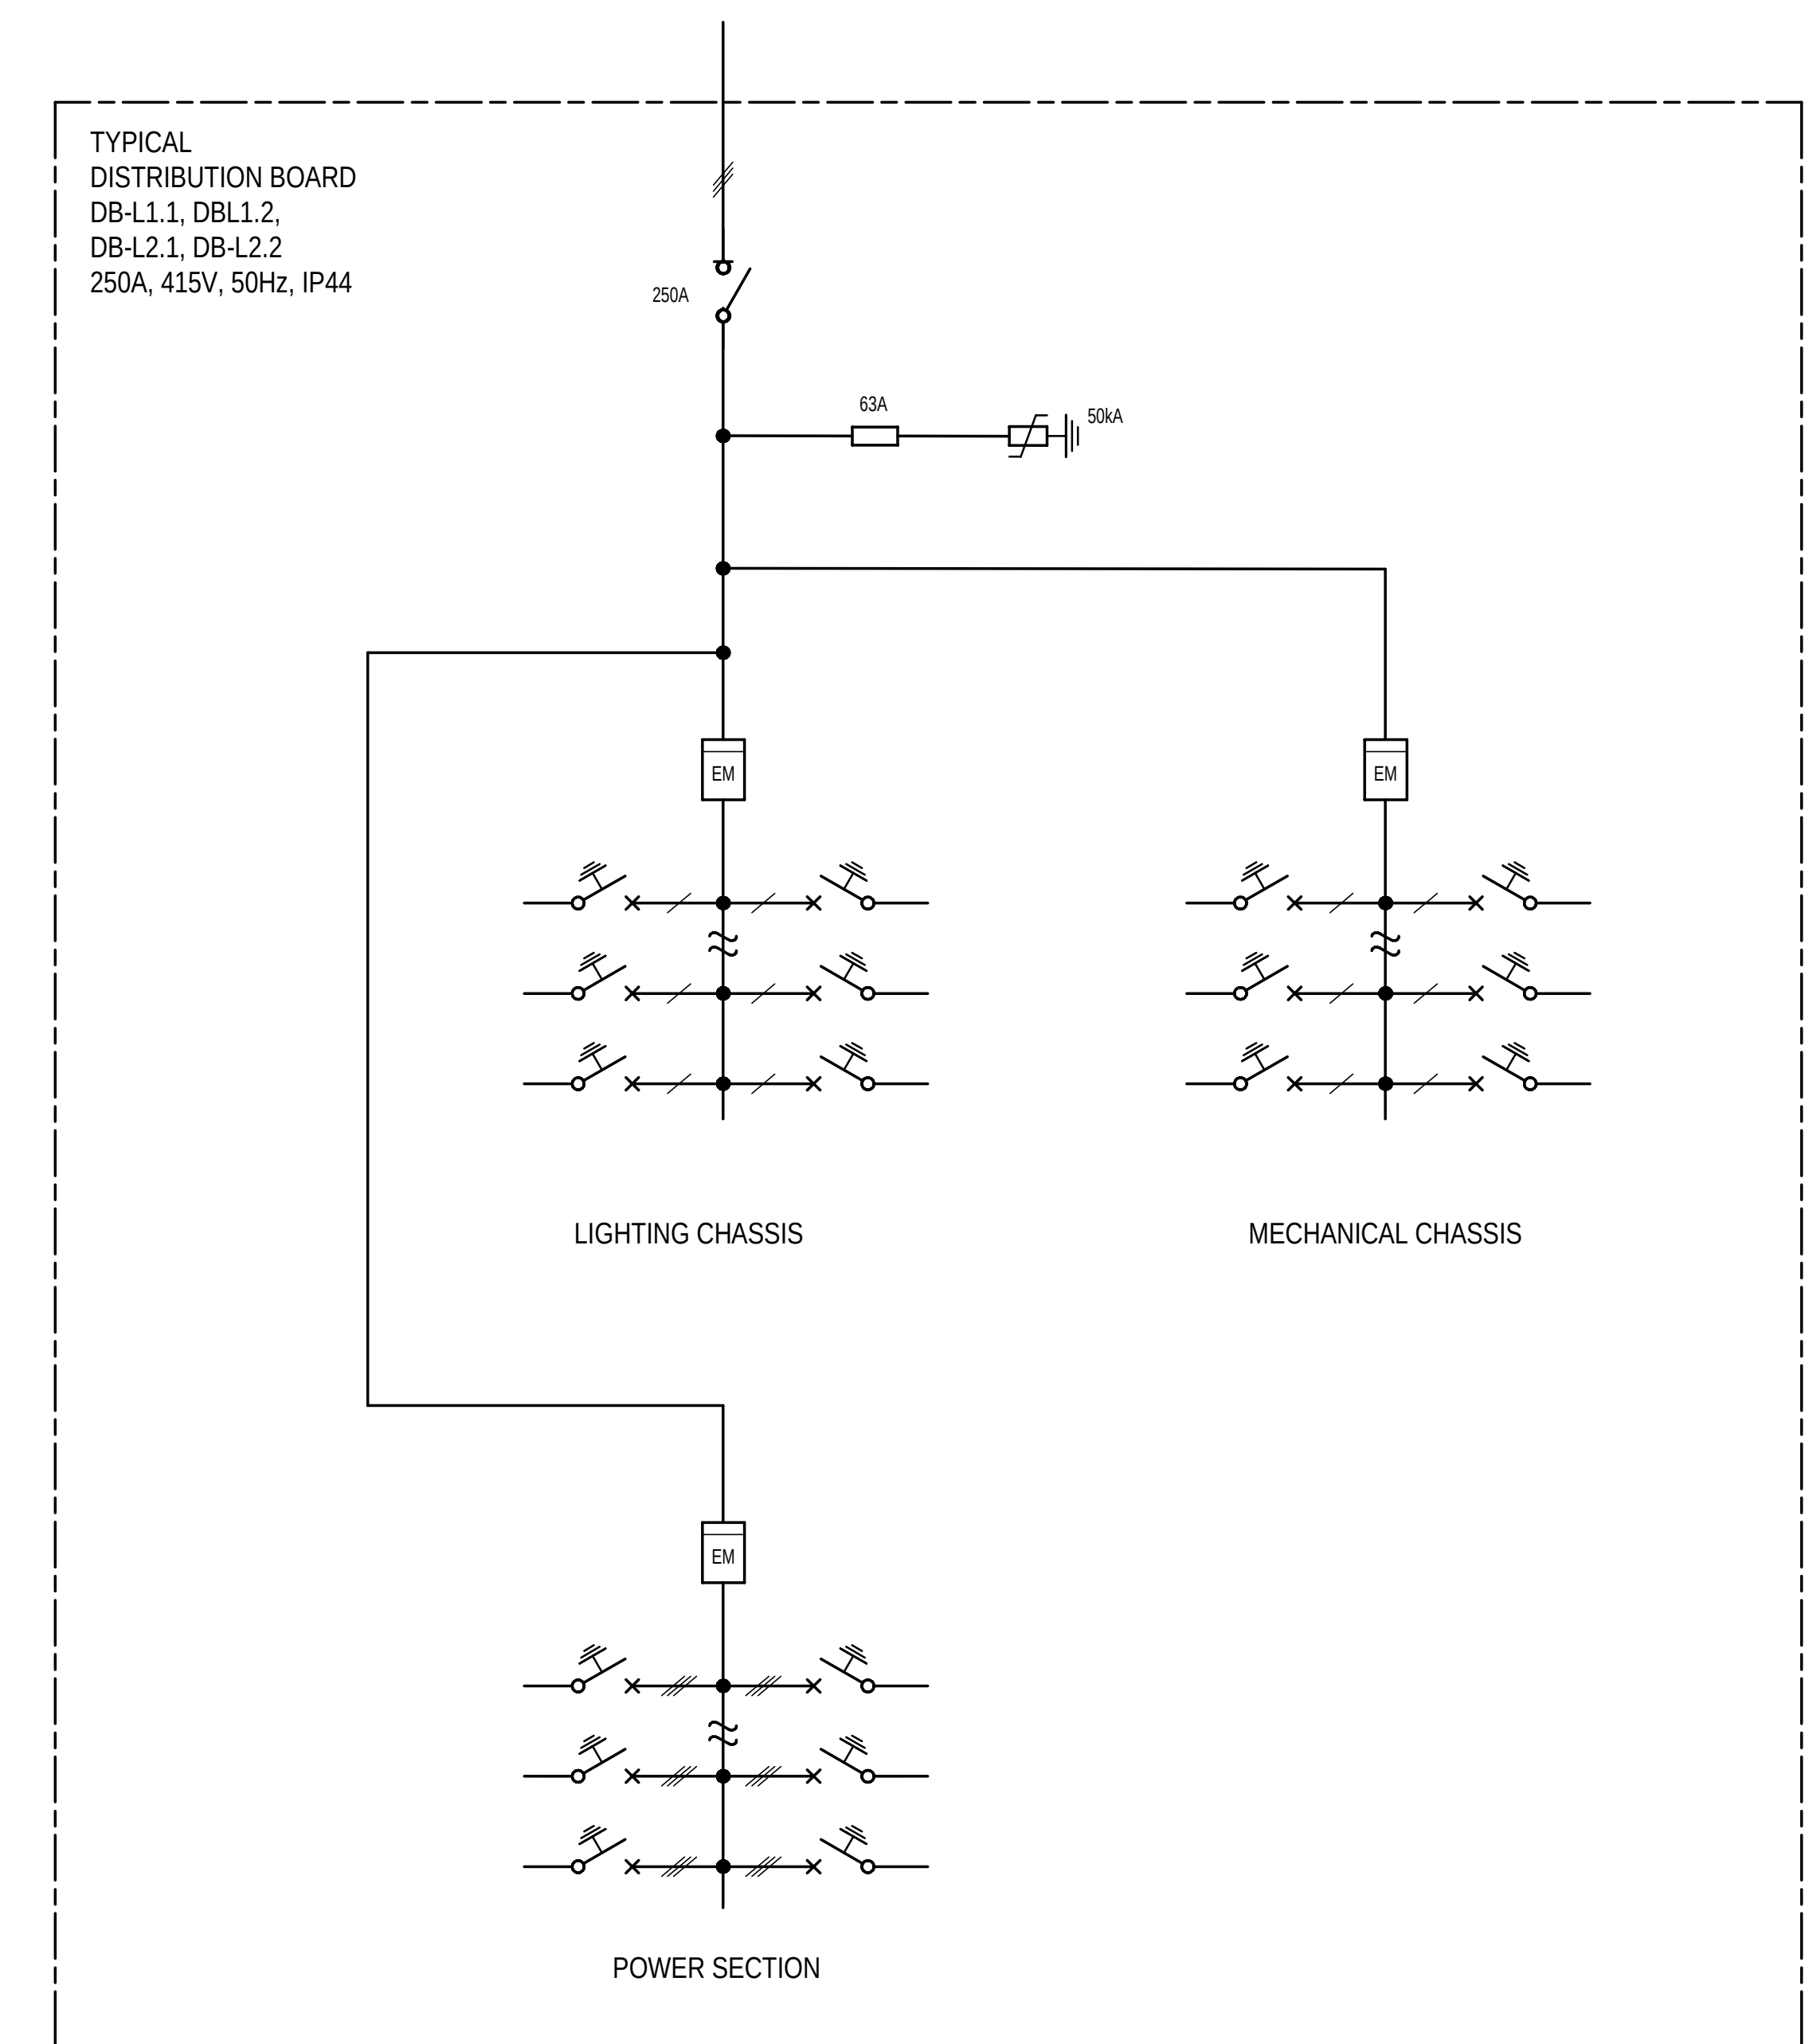

B	12.02.2026	MM	ISSUED FOR DAC TENDER	TP	SM
A	30.03.2026	MM	DRAFT 60% DD ISSUE FOR REVIEW	TP	SM
REV	DATE	BY	DESCRIPTION	CHK	APP

DESIGN DEVELOPMENT



900 Ann Street, Level 12, Fortitude Valley 4006
Tel: +61-7-3854-6200 Fax: +61-7-3854-6500
<http://www.vsp.com>

CLIENT: _____

ARCHITECT: THOMSON ADSETT / PEDDLE THORP

CQU ROCKHAMPTON TAFE CONSOLIDATION

TITLE:

ELECTRICAL SERVICES
BUILDING 33 - SCHEMATICS

SCALE @ A0: N.T.S	CHECKED: TP	APPROVED: SM
PROJECT NUMBER: PS229518	DRAWN: MM	DATE: JAN 2026

© WSP Australia Pty Ltd