




INFORMATION REFLECTED ON THIS DRAWING REPRESENTS ELECTRICAL SERVICES DESIGN DEVELOPED FOR D&C TENDER ADVISE ONLY, AND SHOULD NOT BE REGARDED AS COMPLETE. THE D&C CONTRACTOR SHOULD REFER TO ALL ASSOCIATED ARCHITECTURAL AND OTHER DISCIPLINE DRAWINGS, PROJECT BRIEFS AND CLIENT REQUIREMENTS AND MAKE ADEQUATE ALLOWANCES FOR ALL NECESSARY ELECTRICAL SERVICES WORKS TO MEET THESE REQUIREMENTS, EQUIPMENT SCHEDULES AND COMPLIANCE WITH THE NCC & APPROPRIATE AUSTRALIAN STANDARDS

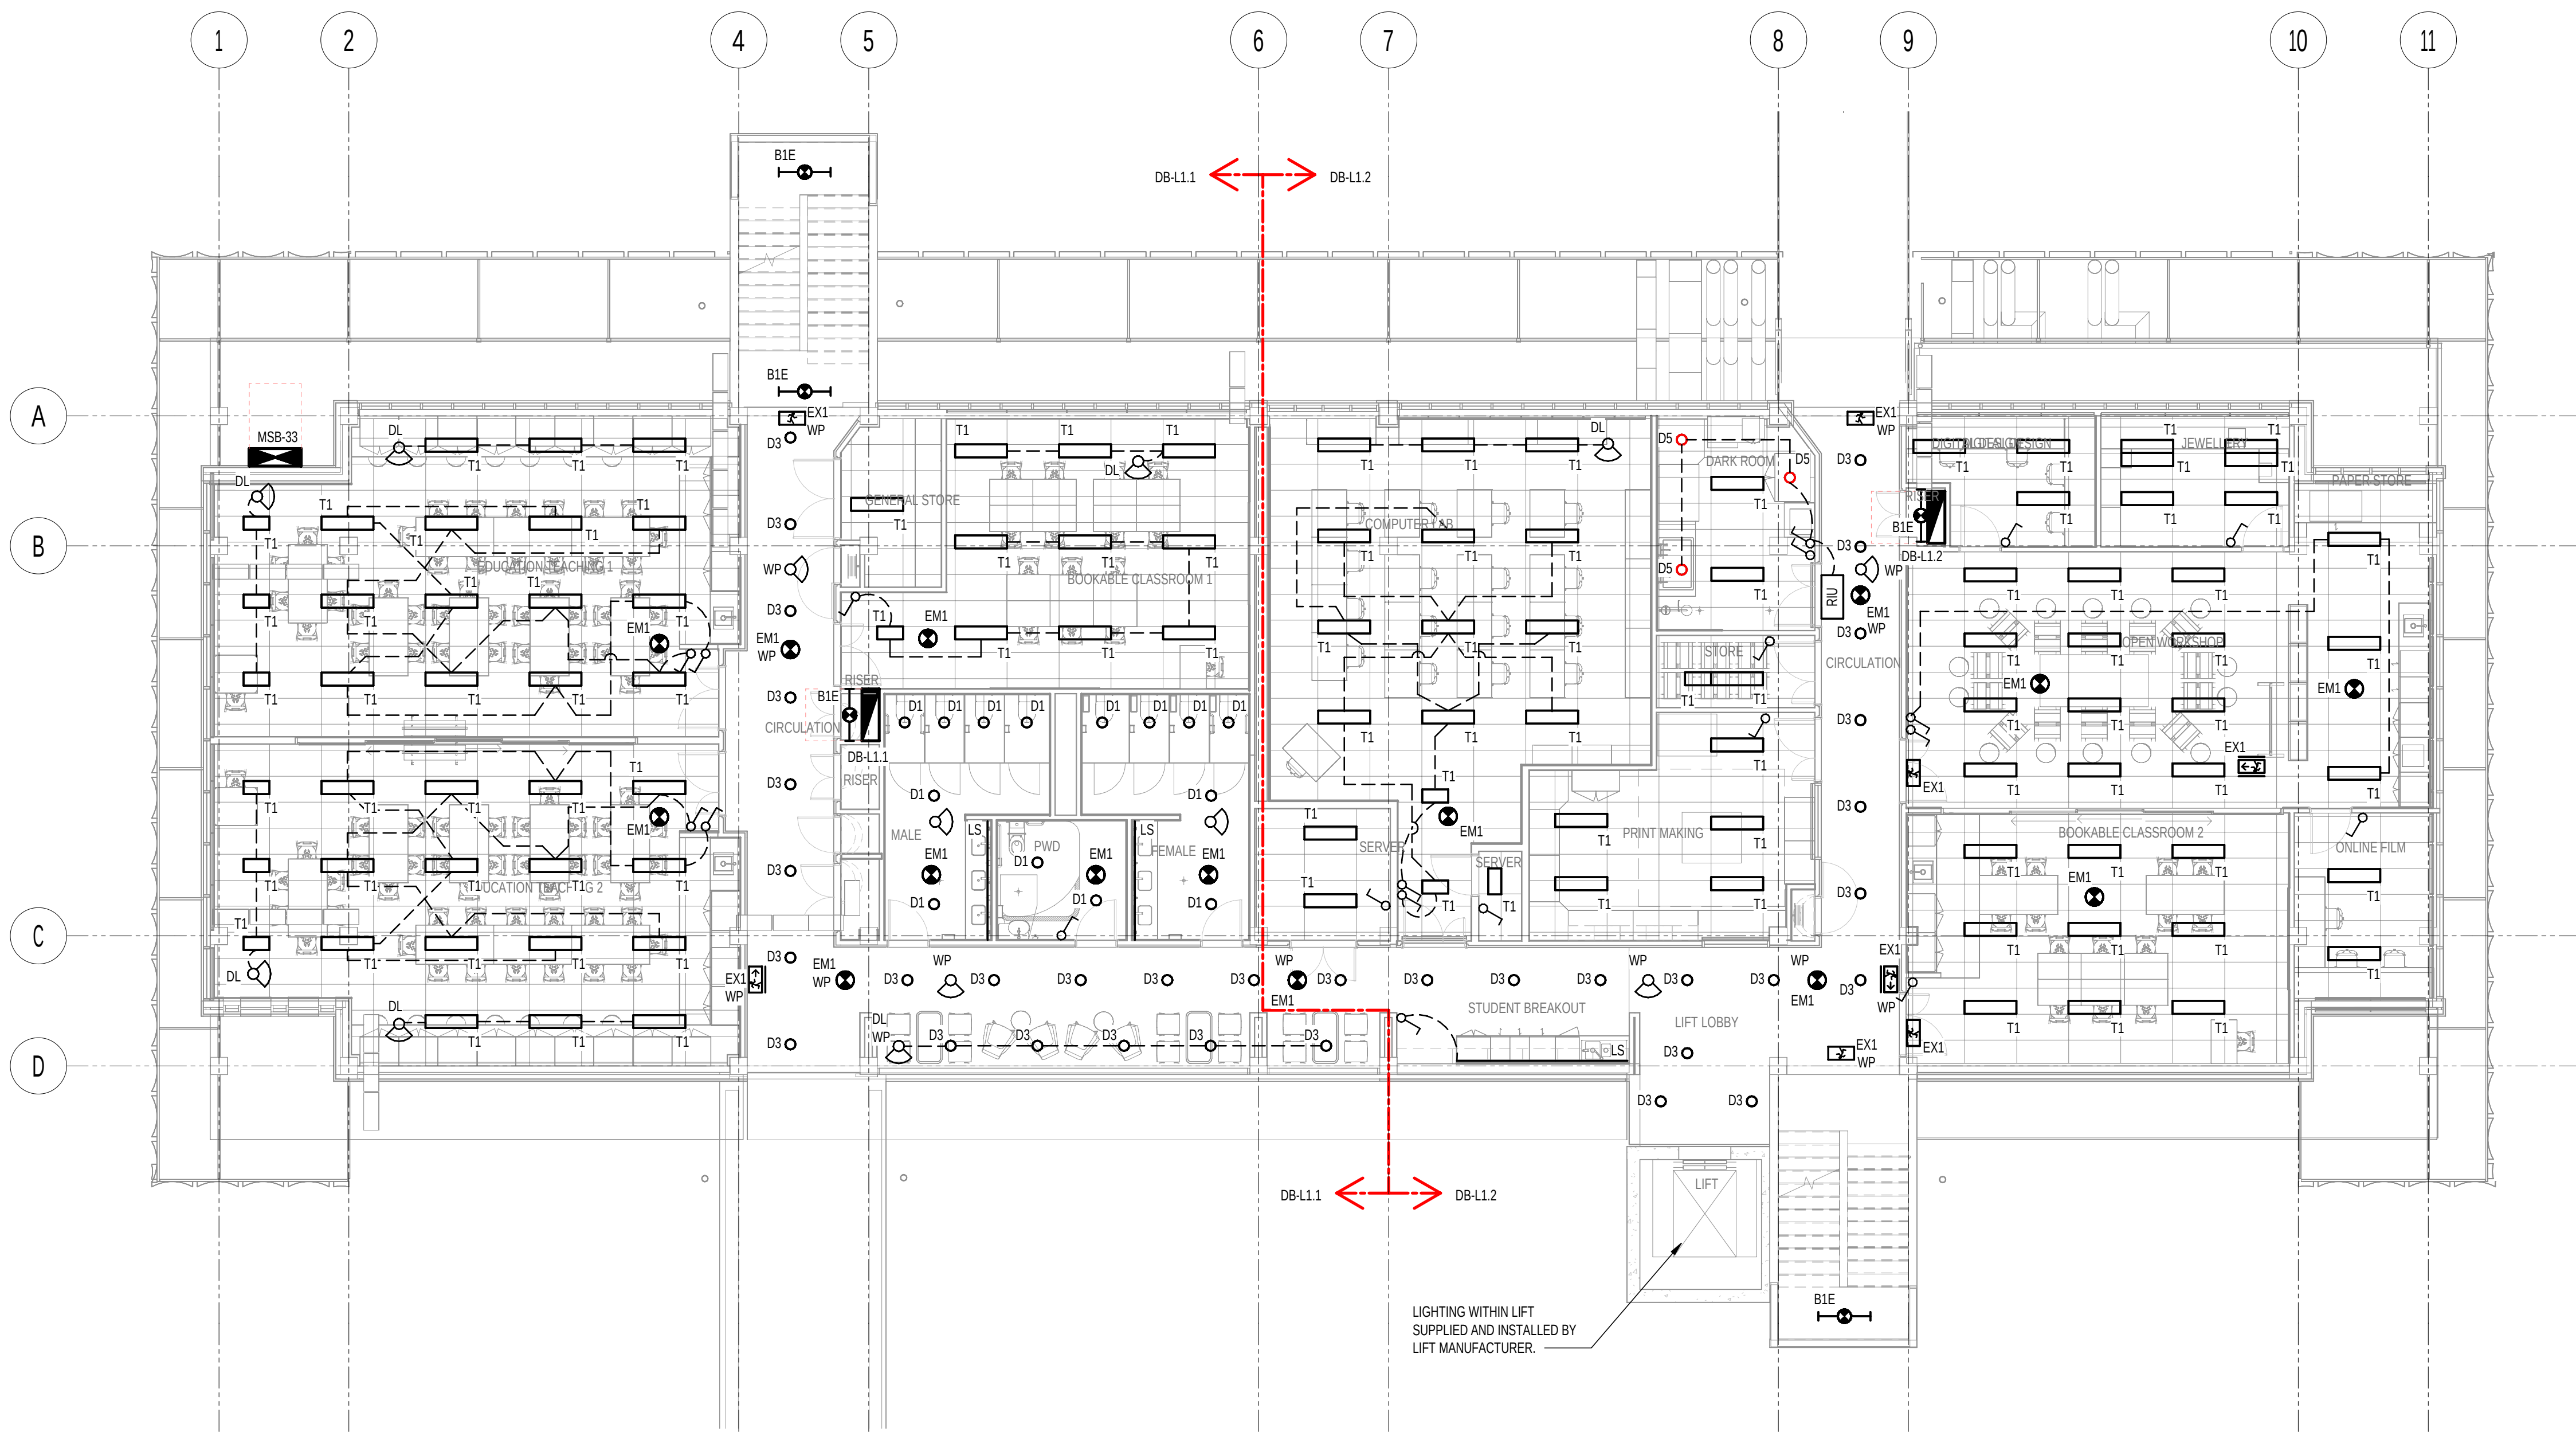

LIGHTING WITHIN LIFT
SUPPLIED AND INSTALLED BY
LIFT MANUFACTURER

B	12.02.2020	MM	ISSUED FOR D&C TENDER	TP	SM
A	10.02.2020	MM	DRAWN FOR REVIEW	TP	SM
REV	DATE	BY	DESCRIPTION	CHK	APP

DESIGN DEVELOPMENT



900 Ann Street, Level 12, Fortitude Valley 4006
Tel: +61-7-3854-6200 Fax: +61-7-3854-6500
http://www.wsp.com

CLIENT: CQU

ARCHITECT: THOMSON ADSETT / PEDDLE THORP

PROJECT: CQU ROCKHAMPTON TAFE CONSOLIDATION

TITLE: ELECTRICAL SERVICES
BUILDING 33 - LEVEL 01 - LIGHTING LAYOUT

SCALE @ A1	1:100	CHECKED	TP	APPROVED	SM
PROJECT NUMBER	PS229518	DRAWN	MM	DATE	JAN 2020

DRAWING NO:	B33-EL-DR-510-L01-00-00	REV:	B
-------------	-------------------------	------	---

© WSP Australia Pty Ltd