



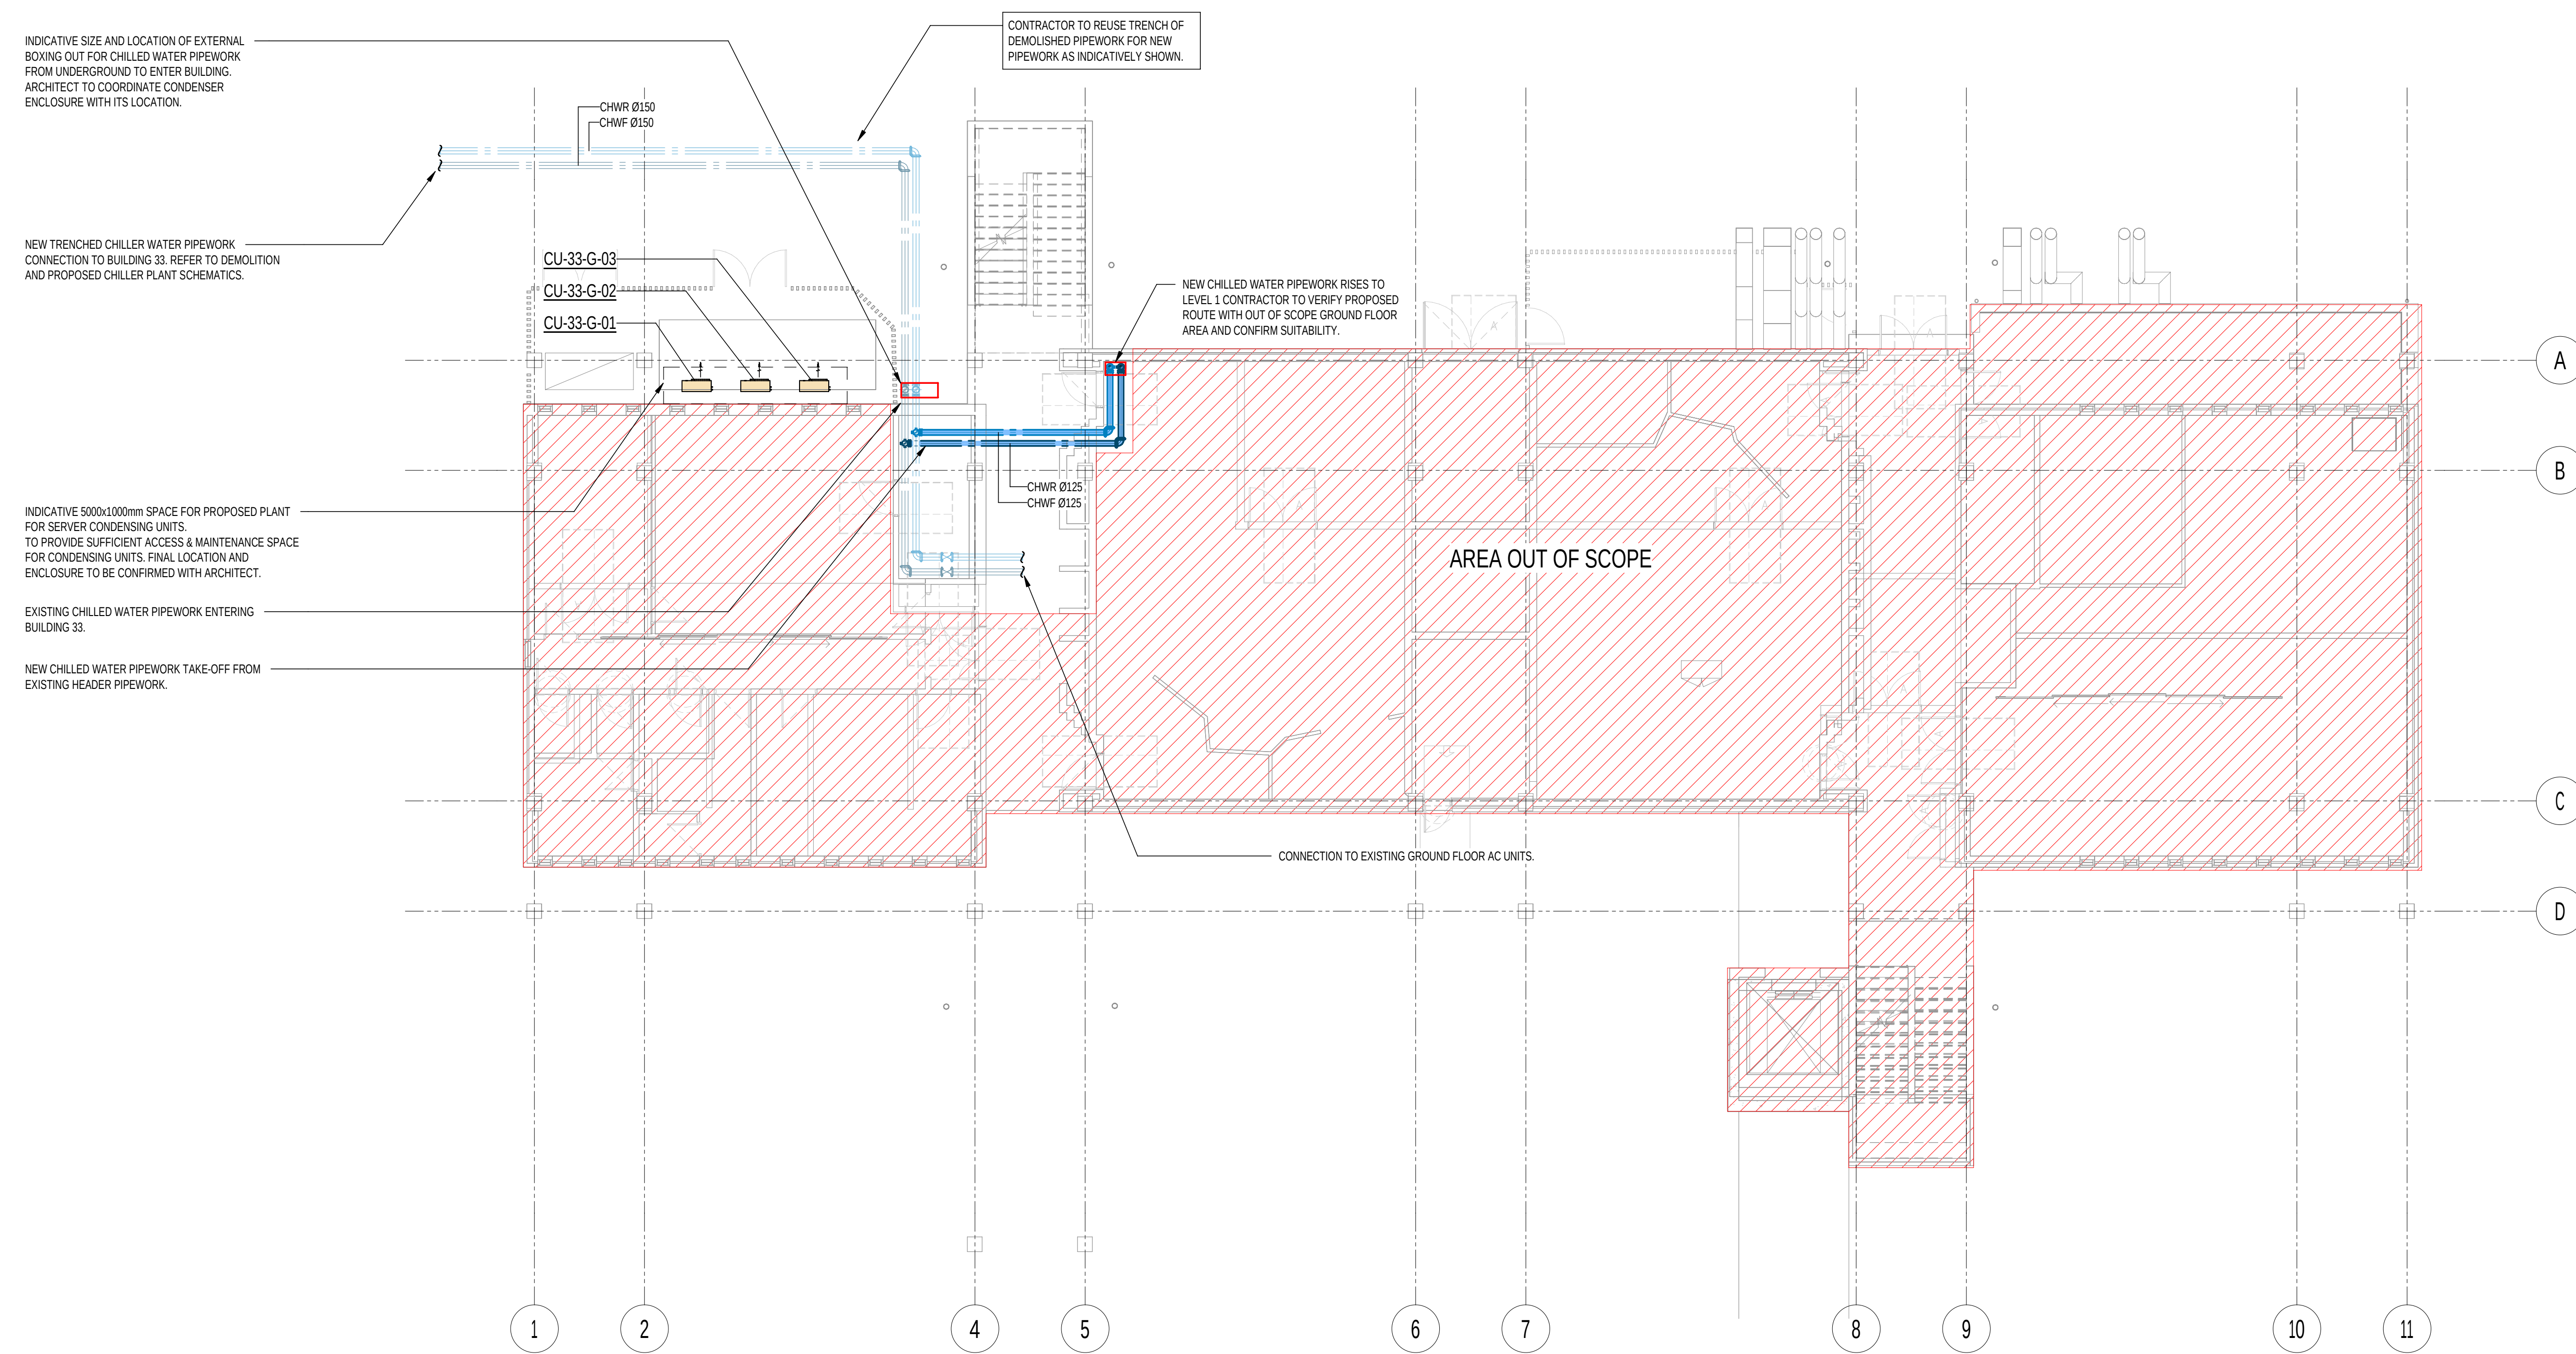

CENTRAL CHILLER -
PLANT COMPOUND

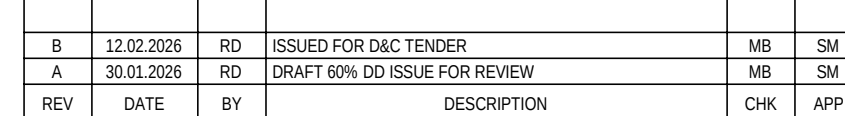

CIENT: CQU

PROJECT: COU ROCKHAMPTON TAFE CONSOLIDATION

TITLE:

MECHANICAL SERVICES
BUILDING 33 - GROUND LEVEL - HVAC LAYOUT

SCALE @ A0: 1:100	CHECKED: MB	APPROVED: SM
PROJECT NUMBER: PS220518	DRAWN: RD	DATE: FEB 2026

DRAWING No:	REV:
B33-ME-DR-510-L00-00-00	B

© WSP Australia Pty Ltd