


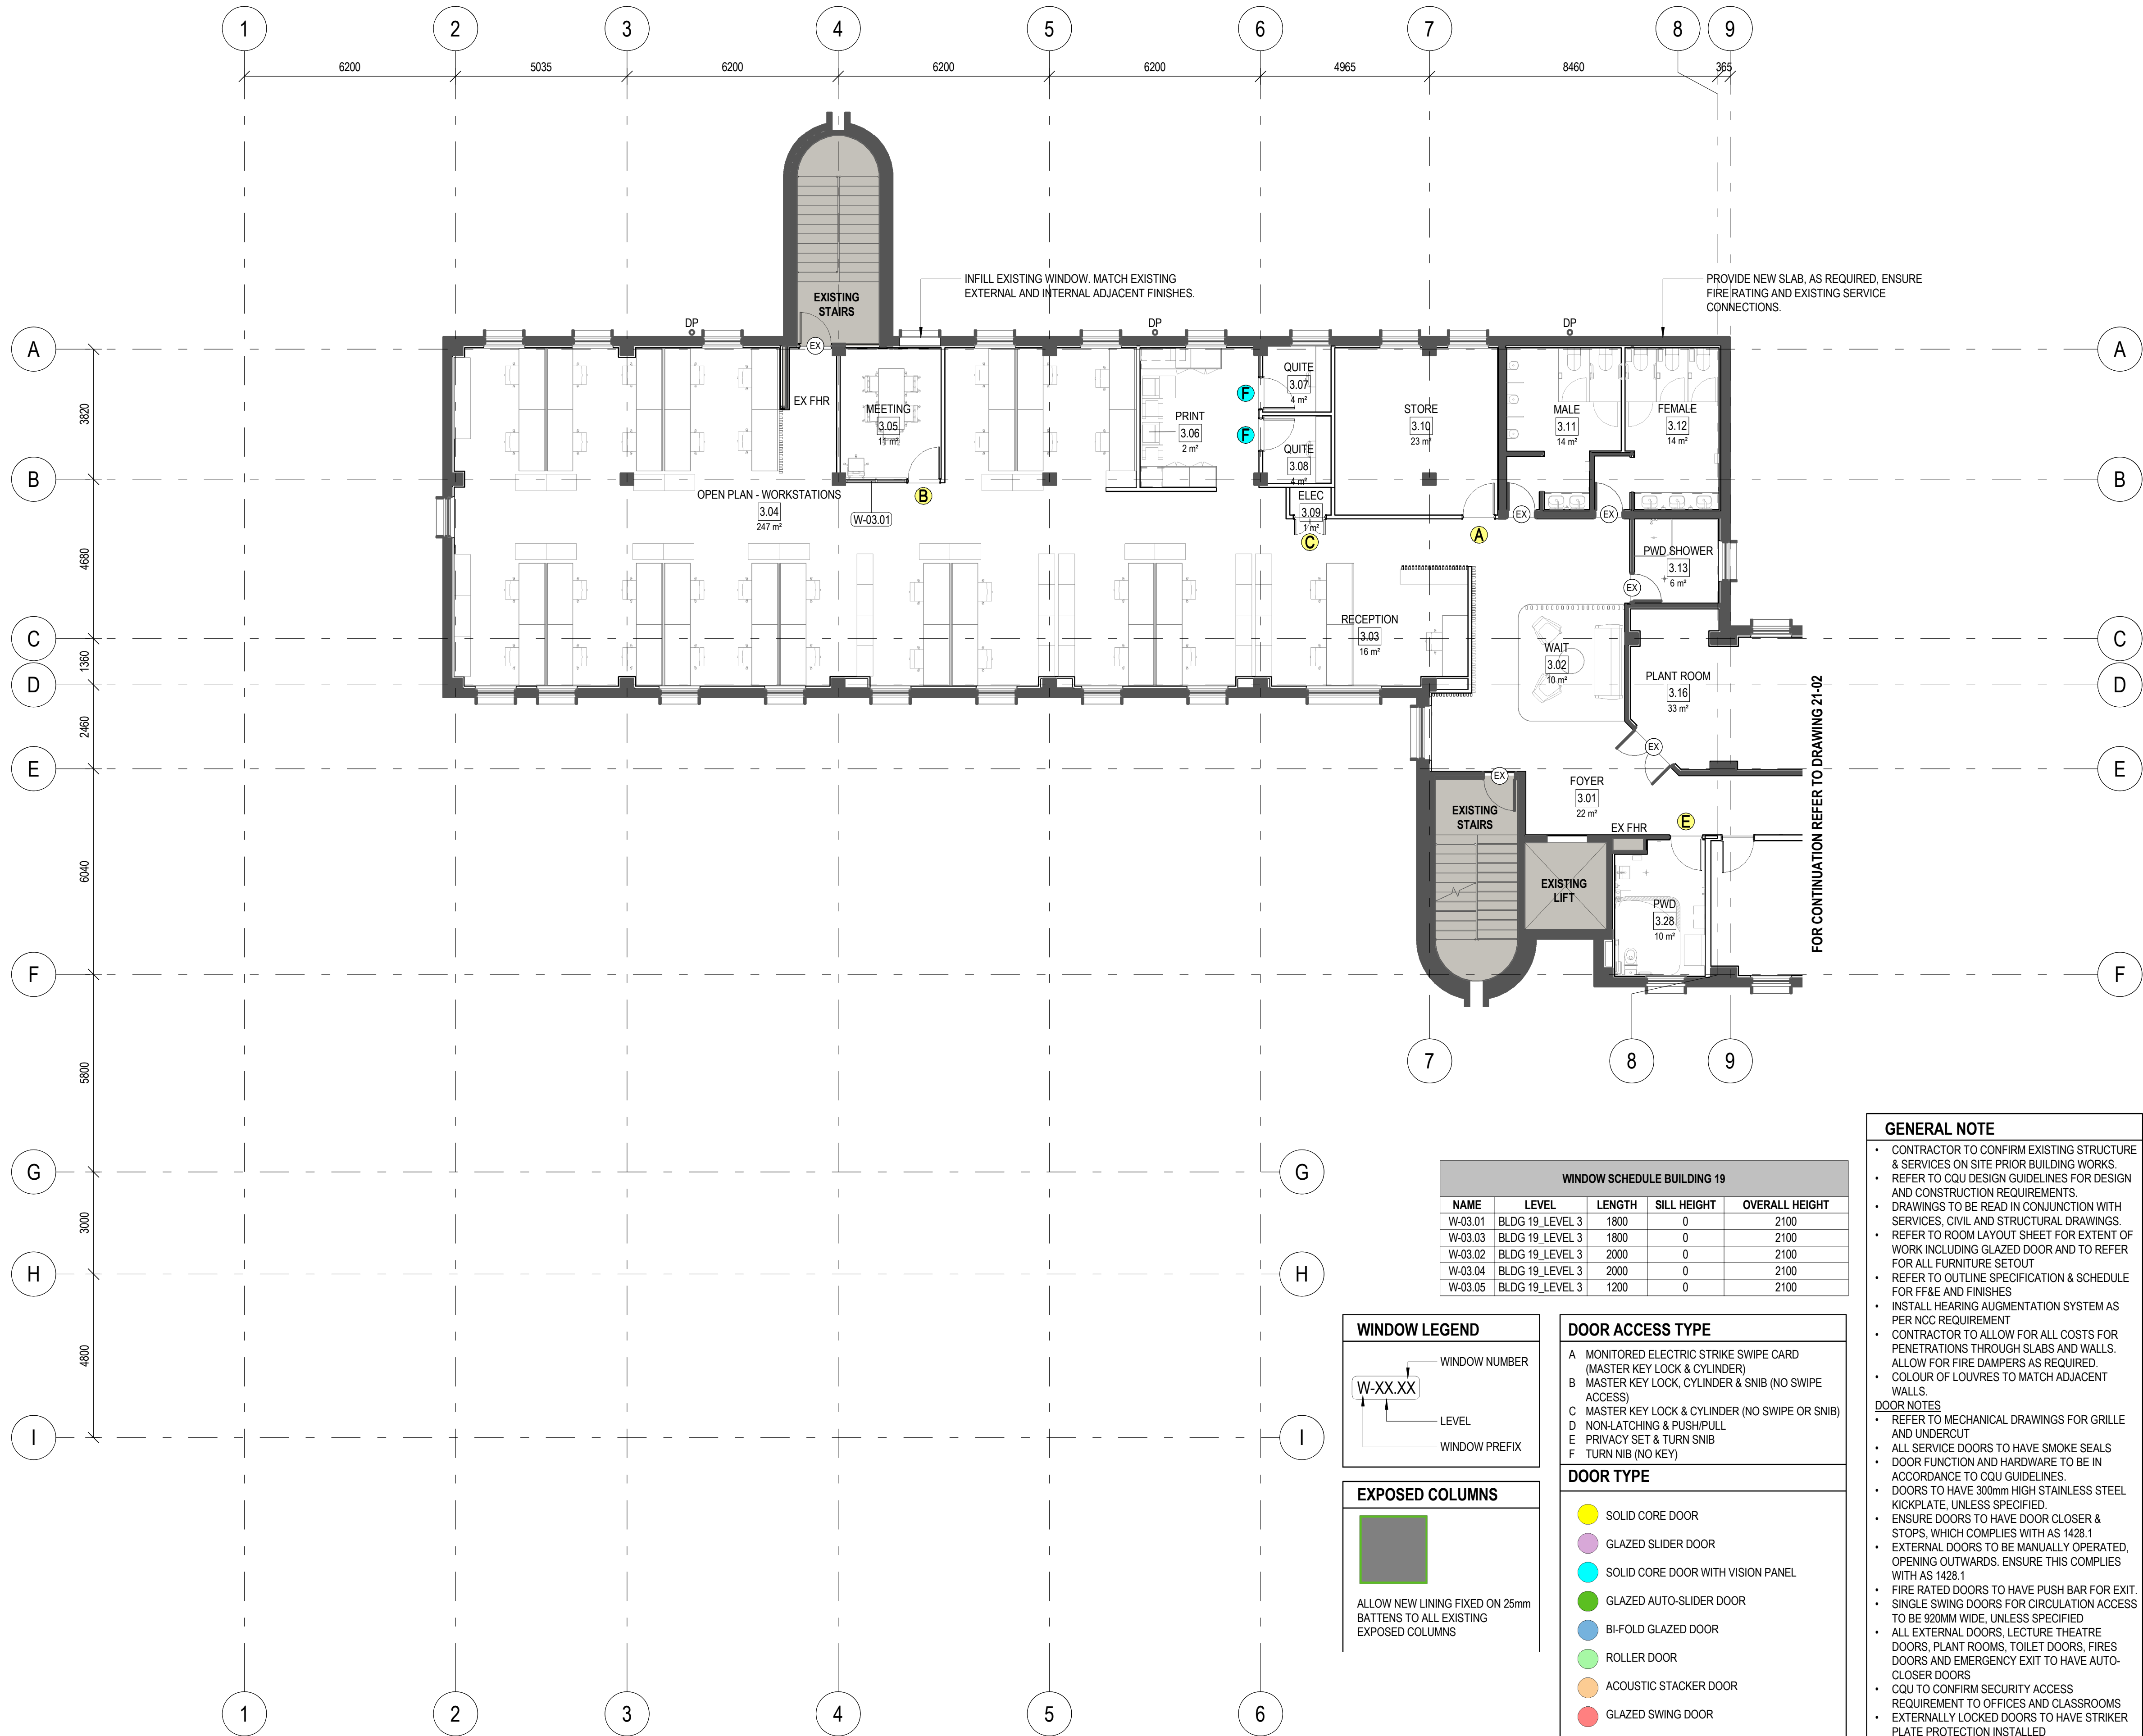

© Copyright
These drawings and designs and the copyright thereof are the property of Thomson Adsett Pty Ltd and must not be used, retained or copied without written permission of Thomson Adsett Pty Ltd. ABN 76 105 314 654 Trading as ThomsonAdsett. Dimensions take precedence over scaling. Do not measure off drawings as print sizes may vary


CQU ROCKHAMPTON TAFE CONSOLIDATION - STAGE 2

554/700 Yaamba Rd, Norman
Gardens QLD 4701



B	2026-03-05	ISSUED FOR TENDER	BC
A	2026-02-12	ISSUED FOR TENDER	BC
6	2026-01-30	60% DRAFT ISSUE	BC
5	2026-01-23	CONSULTANT ISSUES	BC
4	2025-12-19	UPDATED ISSUE	BC
3	2025-12-16	UPDATED ISSUE	BC
2	2025-12-15	CONSULTANTS REVIEW	BC
1	2025-11-24	50% COSTING ISSUE	PT

drawn	date
JS	19/01/2026
checked	date
SS	12/02/2026
verified	date

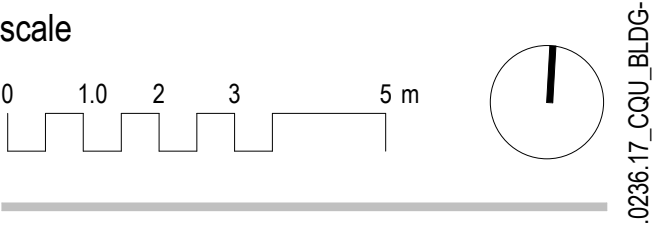

FLOOR PLAN - LEVEL 3 - PART 1 PROPOSED

scale 1 : 100 @ A1 project no. 25.0236.17

revision B sheet no. CQU-ROK-019-03-ARC-21-01

ISSUED FOR TENDER