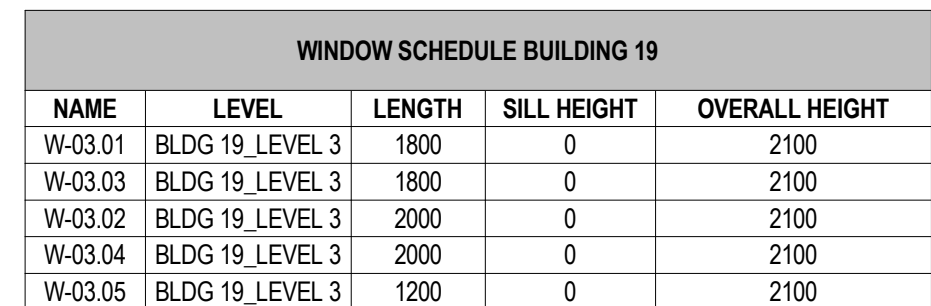


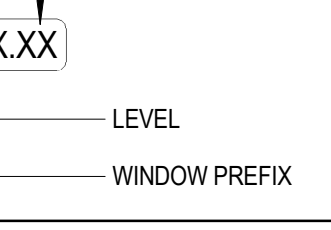
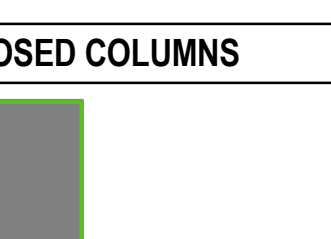
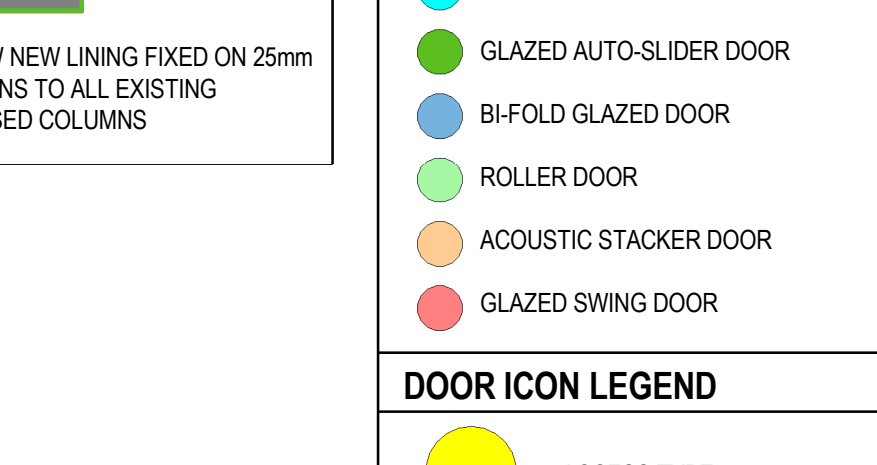
554/700 Yaamba Rd, Norman
Gardens QLD 4701

for



CQUniversity
AUSTRALIA



WINDOW LEGEND  WINDOW NUMBER W-XX.XX LEVEL WINDOW PREFIX	DOOR ACCESS TYPE - A MONITORED ELECTRIC STRIKE SWIPE CARD (MASTER KEY LOCK & CYLINDER) - B MASTER KEY LOCK, CYLINDER & SNIB (NO SWIPE ACCESS) - C MASTER KEY LOCK & CYLINDER (NO SWIPE OR SNIB) - D NON-LATCHING & PUSH/PULL - E PRIVACY SET & TURN SNIB - F TURN NIB (NO KEY)
EXPOSED COLUMNS  ALLOW NEW LINING FIXED ON 25mm BATTENS TO ALL EXISTING EXPOSED COLUMNS	DOOR TYPE  SOLID CORE DOOR  GLAZED SLIDER DOOR  SOLID CORE DOOR WITH VISION PANEL  GLAZED AUTO-SLIDER DOOR  BI-FOLD GLAZED DOOR  ROLLER DOOR  ACOUSTIC STACKER DOOR  GLAZED SWING DOOR
DOOR ICON LEGEND  ACCESS TYPE (TYPE MARK) xx DOOR TYPE (COLOUR SHADE)	

GENERAL NOTE

- CONTRACTOR TO CONFIRM EXISTING STRUCTURE & SERVICES ON SITE PRIOR BUILDING WORKS.
- REFER TO CQU DESIGN GUIDELINES FOR DESIGN AND CONSTRUCTION REQUIREMENTS.
- DRAWINGS TO BE READ IN CONJUNCTION WITH SERVICES, CIVIL AND STRUCTURAL DRAWINGS.
- REFER TO ROOM LAYOUT SHEET FOR EXTENT OF WORK INCLUDING GLAZED DOOR AND TO REFER FOR ALL FURNITURE SETOUT
- REFER TO OUTLINE SPECIFICATION & SCHEDULE FOR FR&E AND FINISHES
- INSTALL HEARING AUGMENTATION SYSTEM AS PER NCC REQUIREMENT
- CONTRACTOR TO ALLOW FOR ALL COSTS FOR PENETRATIONS THROUGH SLABS AND WALLS. ALLOW FOR FIRE DAMPERS AS REQUIRED.
- COLOUR OF LOUVRES TO MATCH ADJACENT WALLS.

DOOR NOTES

- REFER TO MECHANICAL DRAWINGS FOR GRILLE AND UNDERCUT
- ALL SERVICE DOORS TO HAVE SMOKE SEALS
- DOOR FUNCTION AND HARDWARE TO BE IN ACCORDANCE TO CQU GUIDELINES.
- DOORS TO HAVE 300mm HIGH STAINLESS STEEL KICKPLATE, UNLESS SPECIFIED.
- ENSURE DOORS TO HAVE DOOR CLOSER & STOPS, WHICH COMPLIES WITH AS 1428.1
- EXTERNAL DOORS TO BE MANUALLY OPERATED, OPENING OUTWARDS. ENSURE THIS COMPLIES WITH AS 1428.1
- FIRED RATED DOORS TO HAVE PUSH BAR FOR EXIT.
- SINGLE SWING DOORS FOR CIRCULATION ACCESS TO BE 920MM WIDE, UNLESS SPECIFIED
- ALL EXTERNAL DOORS, LECTURE THEATRE DOORS, PLANT ROOMS, TOILET DOORS, FIRES DOORS AND EMERGENCY EXIT TO HAVE AUTO-CLOSER DOORS
- CQU TO CONFIRM SECURITY ACCESS REQUIREMENT TO OFFICES AND CLASSROOMS
- EXTERNALLY LOCKED DOORS TO HAVE STRIKER PLATE PROTECTION INSTALLED
- PROVIDE DOOR CLOSERS TO ALL DOORS ENCLOSING AIR-CONDITIONED SPACES

WINDOW NOTES

- REFER TO SECTION J REPORT FOR THE REQUIRED GLAZING RATING

B	2026-03-05	ISSUED FOR TENDER	BC
A	2026-02-12	ISSUED FOR TENDER	BC
6	2026-01-30	60% DRAFT ISSUE	BC
5	2026-01-23	CONSULTANT ISSUES	BC
4	2025-12-19	UPDATED ISSUE	BC
3	2025-12-16	UPDATED ISSUE	BC
2	2025-12-15	CONSULTANTS REVIEW	BC
1	2025-11-24	50% COSTING ISSUE	PT
	rev. date	details	init.

drawn	date	
JS	19/01/2026	
checked	date	
SS	12/02/2026	
verified	date	v1

scale



0 1.0 2 3 5 m

36.17 CQU BLDG-1

**FLOOR PLAN - LEVEL 3 -
PART 2 PROPOSED**

scale 1 : 100 @ A1 project no. 25.0236.17
revision B
sheet no. CQU-ROK-019-03-ARG-21-02

ISSUED FOR TENDER