


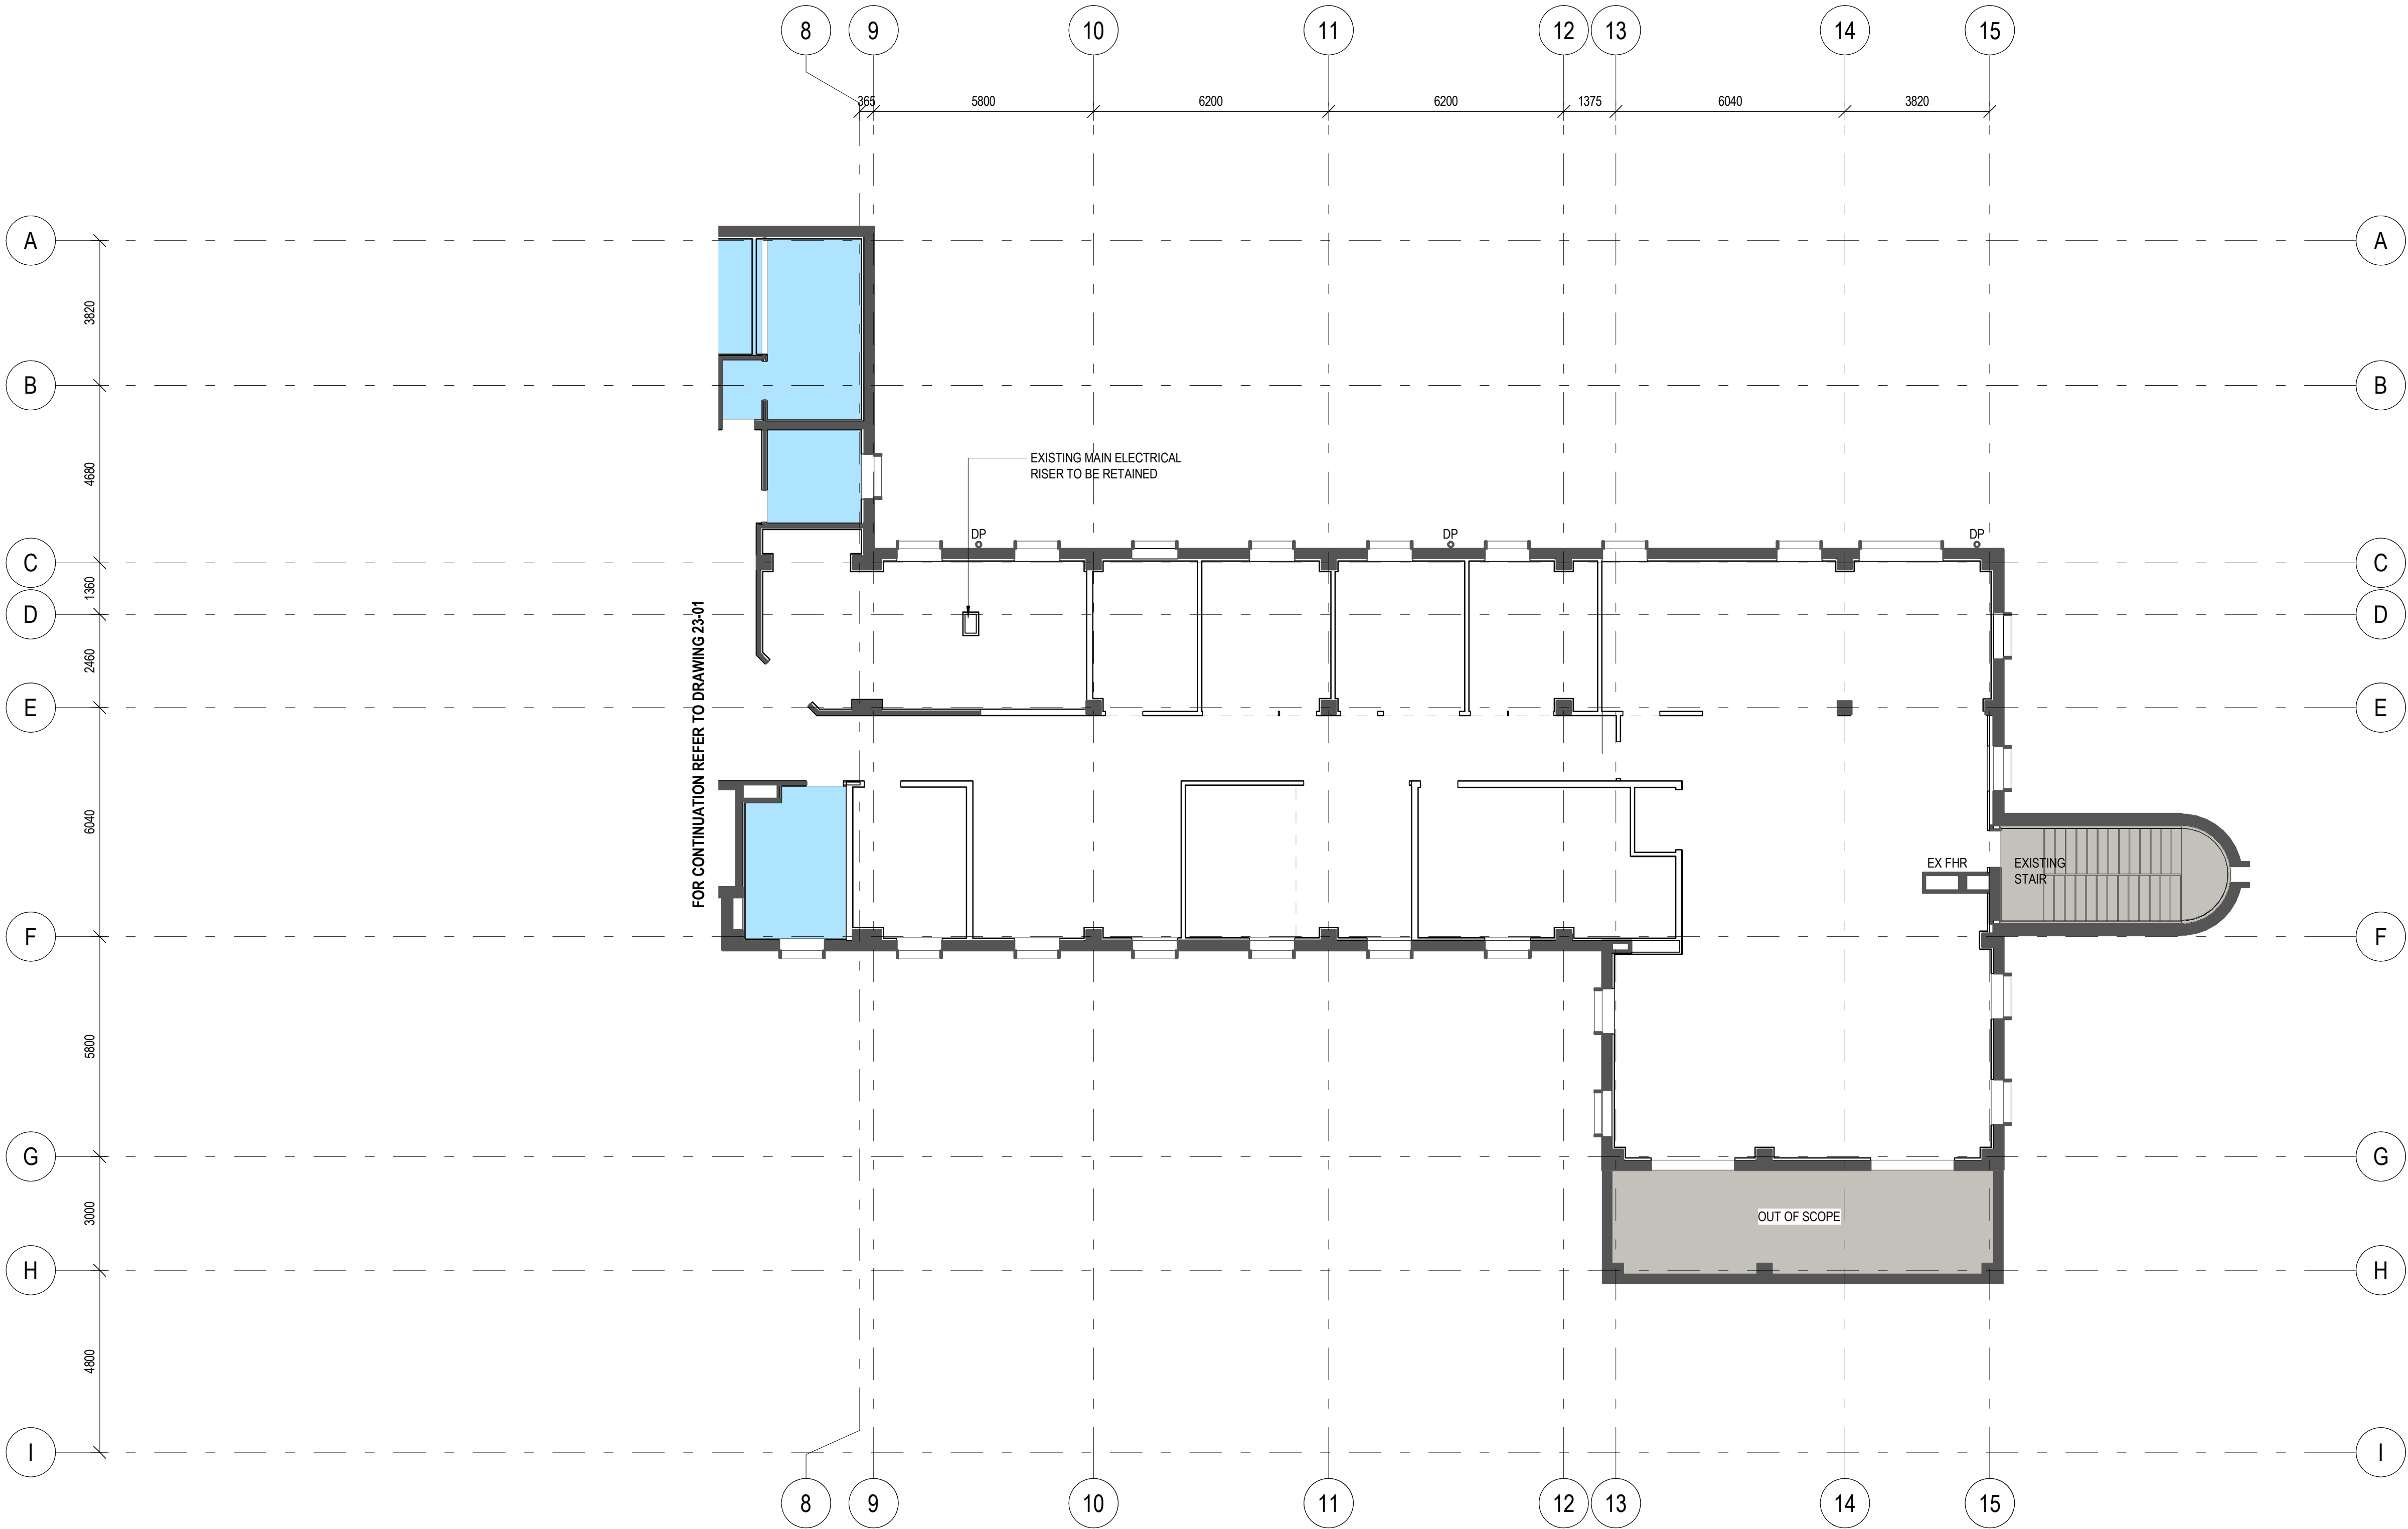

LEGEND	
	WATERPROOFING SYSTEM TO COMPLY WITH THE AUSTRALIAN STANDARDS & BUILDING CODE. ALLOW FOR NEW TOPPING TO CREATE REQUIRED FALLS. ENSURE LEVEL ACCESS TO COMPLY WITH AS1428.1.

SLAB NOTE	
- FOR COLUMN TYPE REFER TO STRUCTURAL DRAWINGS - WHERE CONSTRUCTION MOVEMENT JOINTS ARE NOTED REFER TO STRUCTURAL DRAWINGS FOR TYPE - CONTRACTOR TO VERIFY ALL DIMENSIONS ON SITE PRIOR TO LOCATING SERVICES - REFER TO ROOM LAYOUT SHEETS FOR SETOUT OF FIXTURE AND FITTINGS - RLS DIMENSIONS NOMINATE THE FITTING TO THE FACE OF THE WALL LINING: CONTRACTOR TO ADJUST AS REQUIRED WHEN SETTING OUT. FIXTURES SHOWN ON THIS DRAWING ARE AS A REFERENCE GUIDE ONLY - FLOOR WASTES ARE CENTRE OF ROOM UNLESS NOMINATED OTHERWISE ON THE ROOM LAYOUT SHEETS OR TYPICAL DETAILS (SHOWERS, BASINS WILL ALL BE SETOUT AS TYPICALS) - DRAWINGS TO BE READ IN CONJUNCTION WITH LATEST REVISION OF HYDRAULIC DRAWINGS - REFER ALSO TO STRUCTURAL AND HYDRAULIC DRAWINGS. NOT ALL PENETRATION ARE SHOWN HERE. - ARCHITECTURAL DRAWINGS WILL NOMINATE FINISH, EXTENT AND HEIGHT OF FLOORING, FOR ALL OTHER INFORMATION E.G. SLAB EDGE AND MATERIAL REFER TO STRUCTURAL ENGINEER DRAWINGS - CONTRACTOR TO ALLOW FOR WATERPROOFING SYSTEM TO WET AREA. ENSURE IT COMPLIES WITH AUSTRALIAN STANDARD	

ISSUED FOR TENDER

architecture | interiors | health | planning

Telephone +61 7 3840 9999
bne@thomsonadsett.com
Level 9, 470 St Pauls Terrace
Fortitude Valley
Qld 4006 Australia
thomsonadsett.com

© Copyright
These drawings and designs and the copyright thereof are the property of Thomson Adsett Pty Ltd and must not be used, retained or copied without written permission of Thomson Adsett Pty Ltd. ABN 76 105 314 654 Trading as ThomsonAdsett. Dimensions take precedence over scaling. Do not measure off drawings as print sizes may vary


CQU ROCKHAMPTON
TAFE
CONSOLIDATION -
STAGE 2

554/700 Yaamba Rd, Norman
Gardens QLD 4701

for

B	2026-03-05	ISSUED FOR TENDER	BC
A	2026-02-12	ISSUED FOR TENDER	BC
1	2026-01-30	60% DRAFT ISSUE	BC
rev	date	details	init.

drawn	date
JS	19/01/2026
checked	date
SS	12/02/2026
verified	date

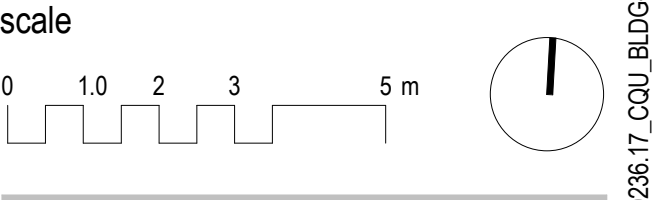

SLAB PLAN - LEVEL 3 - PART 2

scale	project no.
1 : 100 @ A1	25.0236.17
revision	
B	
sheet no.	
CQU-ROK-019-03-ARC-23-02	