


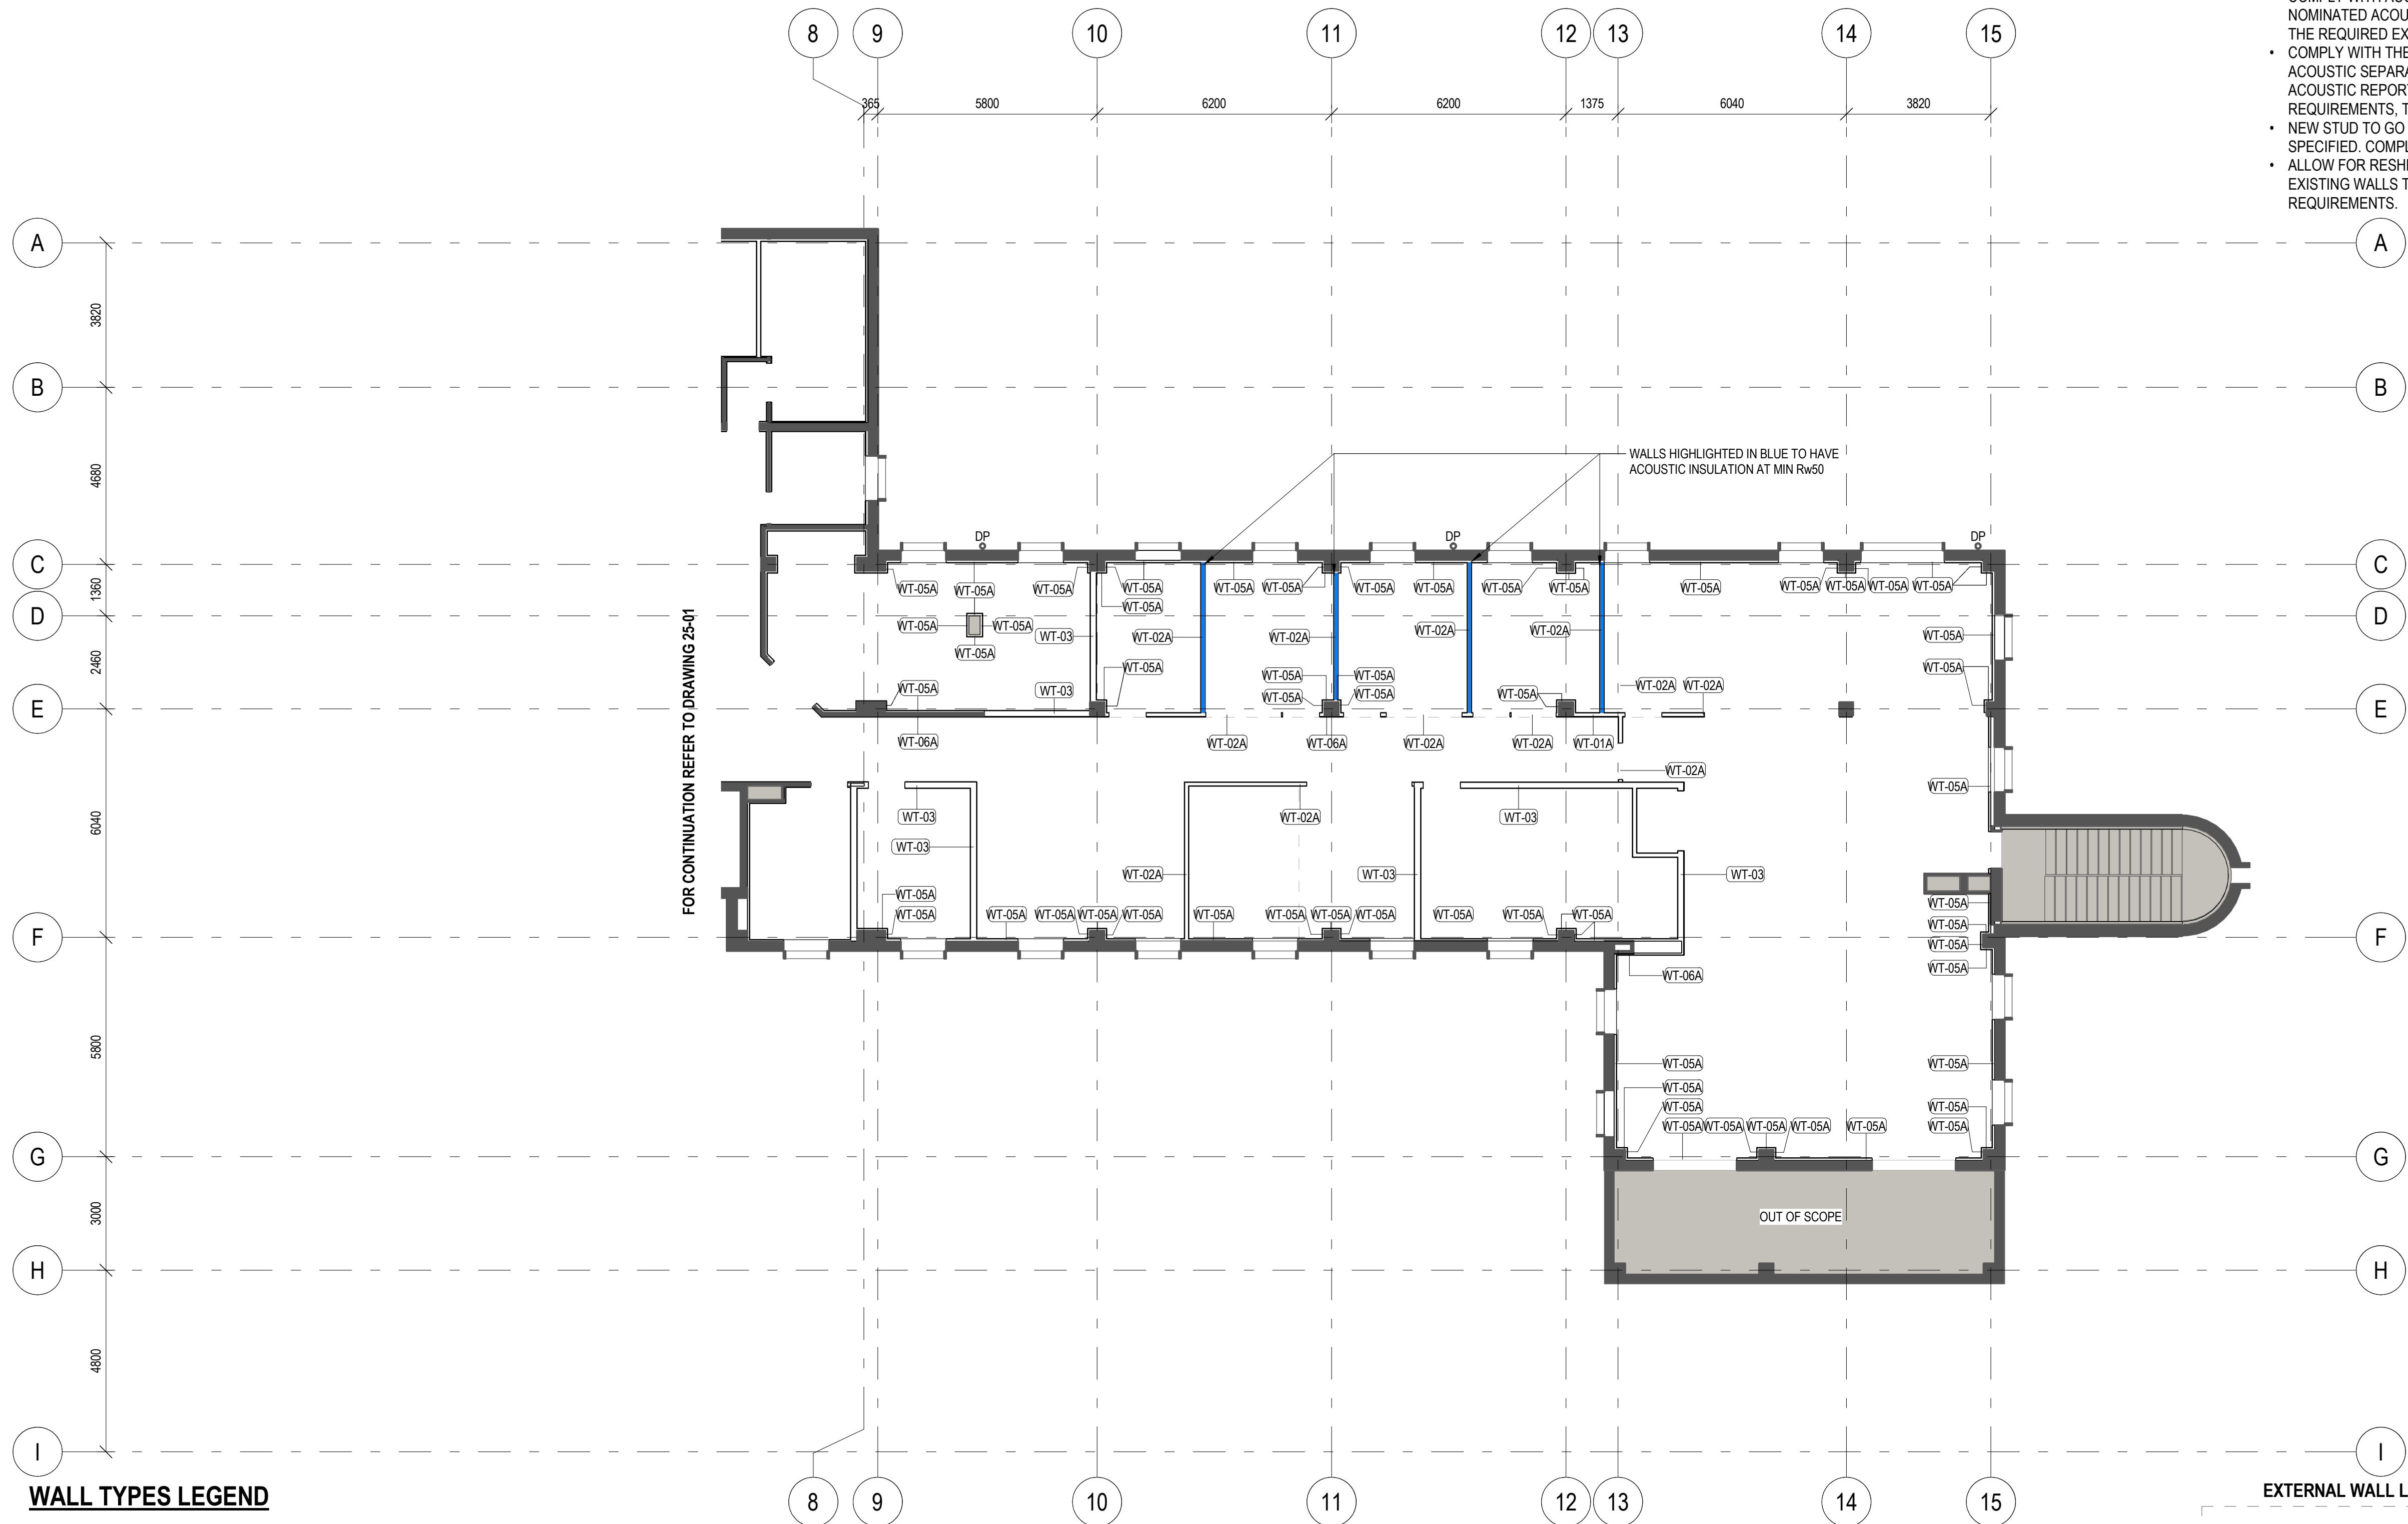

- COMPLY WITH ACOUSTIC REPORT TO ACHIEVE THE NOMINATED ACOUSTIC RATING AND SECTION J REPORT FOR THE REQUIRED EXTERNAL WALLS R VALUES.
- COMPLY WITH THE CQU DESIGN GUIDELINES FOR MINIMUM ACOUSTIC SEPARATION BETWEEN ROOMS. WHERE THE ACOUSTIC REPORT NOMINATES HIGHER PERFORMANCE REQUIREMENTS, THE HIGHER RW RATINGS ARE TO APPLY.
- NEW STUD TO GO UP TO UNDERSIDE OF SLAB, UNLESS SPECIFIED. COMPLY WITH ACOUSTIC REPORT.
- ALLOW FOR RESHEETING OF EXISTING WALLS. ENSURE EXISTING WALLS TO COMPLY WITH ACOUSTIC AND PART J REQUIREMENTS.

thomson adsett

PEDDLE THORP
architecture | interiors | health | planning

Telephone +61 7 3840 9999
bne@thomsonadsett.com
Level 9, 470 St Pauls Terrace
Fortitude Valley
Qld 4006 Australia
thomsonadsett.com

© Copyright
These drawings and designs and the copyright thereof are the property of Thomson Adsett Pty Ltd and must not be used, retained or copied without written permission of Thomson Adsett Pty Ltd. ABN 76 105 314 654 Trading as ThomsonAdsett. Dimensions take precedence over scaling. Do not measure off drawings as print sizes may vary

CQU ROCKHAMPTON TAFE CONSOLIDATION - STAGE 2

554/700 Yaamba Rd, Norman Gardens QLD 4701

for

CQUniversity AUSTRALIA

WALL TYPES LEGEND

WT-01A_SF 92_PB 13 / PB 13
13mm PLASTERBOARD LINING, FLUSH SET
92mm STEEL STUD
13mm PLASTERBOARD LINING, FLUSH SET

WT-01B_SF 92_PB 13 / PB WP 13
13mm PLASTERBOARD LINING, FLUSH SET
92mm STEEL STUD
13mm WATERPROOF PLASTERBOARD LINING, FLUSH SET

WT-01C_SF 92_PB WP 13 / PB WP 13
13mm PLASTERBOARD LINING, FLUSH SET
92mm STEEL STUD
13mm WATERPROOF PLASTERBOARD LINING, FLUSH SET

WT-02A_SF 92 INSUL_PB 13 / PB 13
13mm PLASTERBOARD LINING, FLUSH SET
92mm STEEL STUD + INSULATION
13mm PLASTERBOARD LINING, FLUSH SET

WT-02B_SF 92 INSUL_PB 13 / PB WP 13
13mm PLASTERBOARD LINING, FLUSH SET
92mm STEEL STUD + INSULATION
13mm WATERPROOF PLASTERBOARD LINING, FLUSH SET

WT-02C_SF 92 INSUL_PB WP 13 / PB WP 13
13mm WATERPROOF PLASTERBOARD LINING, FLUSH SET
92mm STEEL STUD + INSULATION
13mm WATERPROOF PLASTERBOARD LINING, FLUSH SET

WT-03A_SF 150 INSUL_PB 13 / PB WP 13
13mm PLASTERBOARD LINING, FLUSH SET
150mm STEEL STUD + INSULATION
13mm WATERPROOF PLASTERBOARD LINING, FLUSH SET

WT-03B_SF 150 INSUL_PB WP 13 / PB WP 13
13mm PLASTERBOARD LINING, FLUSH SET
150mm STEEL STUD + INSULATION
13mm WATERPROOF PLASTERBOARD LINING, FLUSH SET

WT-04A_Fur Chan 50_PB 13
50mm FURRING CHANNEL
13mm PLASTERBOARD LINING, FLUSH SET

WT-04B_Fur Chan 50_PB WP 13
50mm FURRING CHANNEL
13mm WATERPROOF PLASTERBOARD LINING, FLUSH SET

WT-05A_Fur Chan 50 INSUL_PB 13
50mm FURRING CHANNEL + INSULATION
13mm PLASTERBOARD LINING, FLUSH SET

WT-05B_Fur Chan 50 INSUL_PB WP 13
50mm FURRING CHANNEL + INSULATION
13mm WATERPROOF PLASTERBOARD LINING, FLUSH SET

WT-06A_Fur Chan 25_PB 13
25mm FURRING CHANNEL
13mm PLASTERBOARD LINING, FLUSH SET

WT-06B_Fur Chan 25_PB WP 13
25mm FURRING CHANNEL
13mm WATERPROOF PLASTERBOARD LINING, FLUSH SET

EXTERNAL WALL LINING

WT-07_WB 9 + 35 Fur.Chan / 9 EXOTEC
9mm EXOTEC FACADE PANEL
35mm EXOTEC TOP HAT
10mm HARDIE WRAP/WEATHER BARRIER

WT-08A_SF 92 INSUL_PB 13 / WB 9 + 35 Fur.Chan / 9 EXOTEC
13mm PLASTERBOARD LINING, FLUSH SET
92mm STEEL STUD + INSULATION
9mm HARDIE WRAP/WEATHER BARRIER
35mm EXOTEC TOP HAT
10mm EXOTEC FACADE PANEL

EXTERNAL WALL LINING

WT-08B_SF 92 INSUL_PB WP 13 / WB 9 + 35 Fur.Chan / 9 EXOTEC

WT-09_CONC 290 + RENDER 10
290mm CONCRETE, FORMED
10mm RENDER

WT-10_CONC 190
190mm CONCRETE, FORMED

INSULATION NOTES

ISSUED FOR TENDER

B	2026-03-05	ISSUED FOR TENDER	BC
A	2026-02-12	ISSUED FOR TENDER	BC
1	2026-01-30	60% DRAFT ISSUE	BC
rev	date	details	init.

drawn JS
checked SS
verified

date 19/01/2026
date 12/02/2026
date

scale
0 1.0 2 3 5 m

PARTITION PLAN - LEVEL 3 - PART 2 PROPOSED

scale As indicated @ A1
revision B
project no. 25.0236.17
sheet no. CQU-ROK-019-03-ARC-25-02