



FOYER, WAIT, OPEN PLAN - 4 WORKSTATIONS

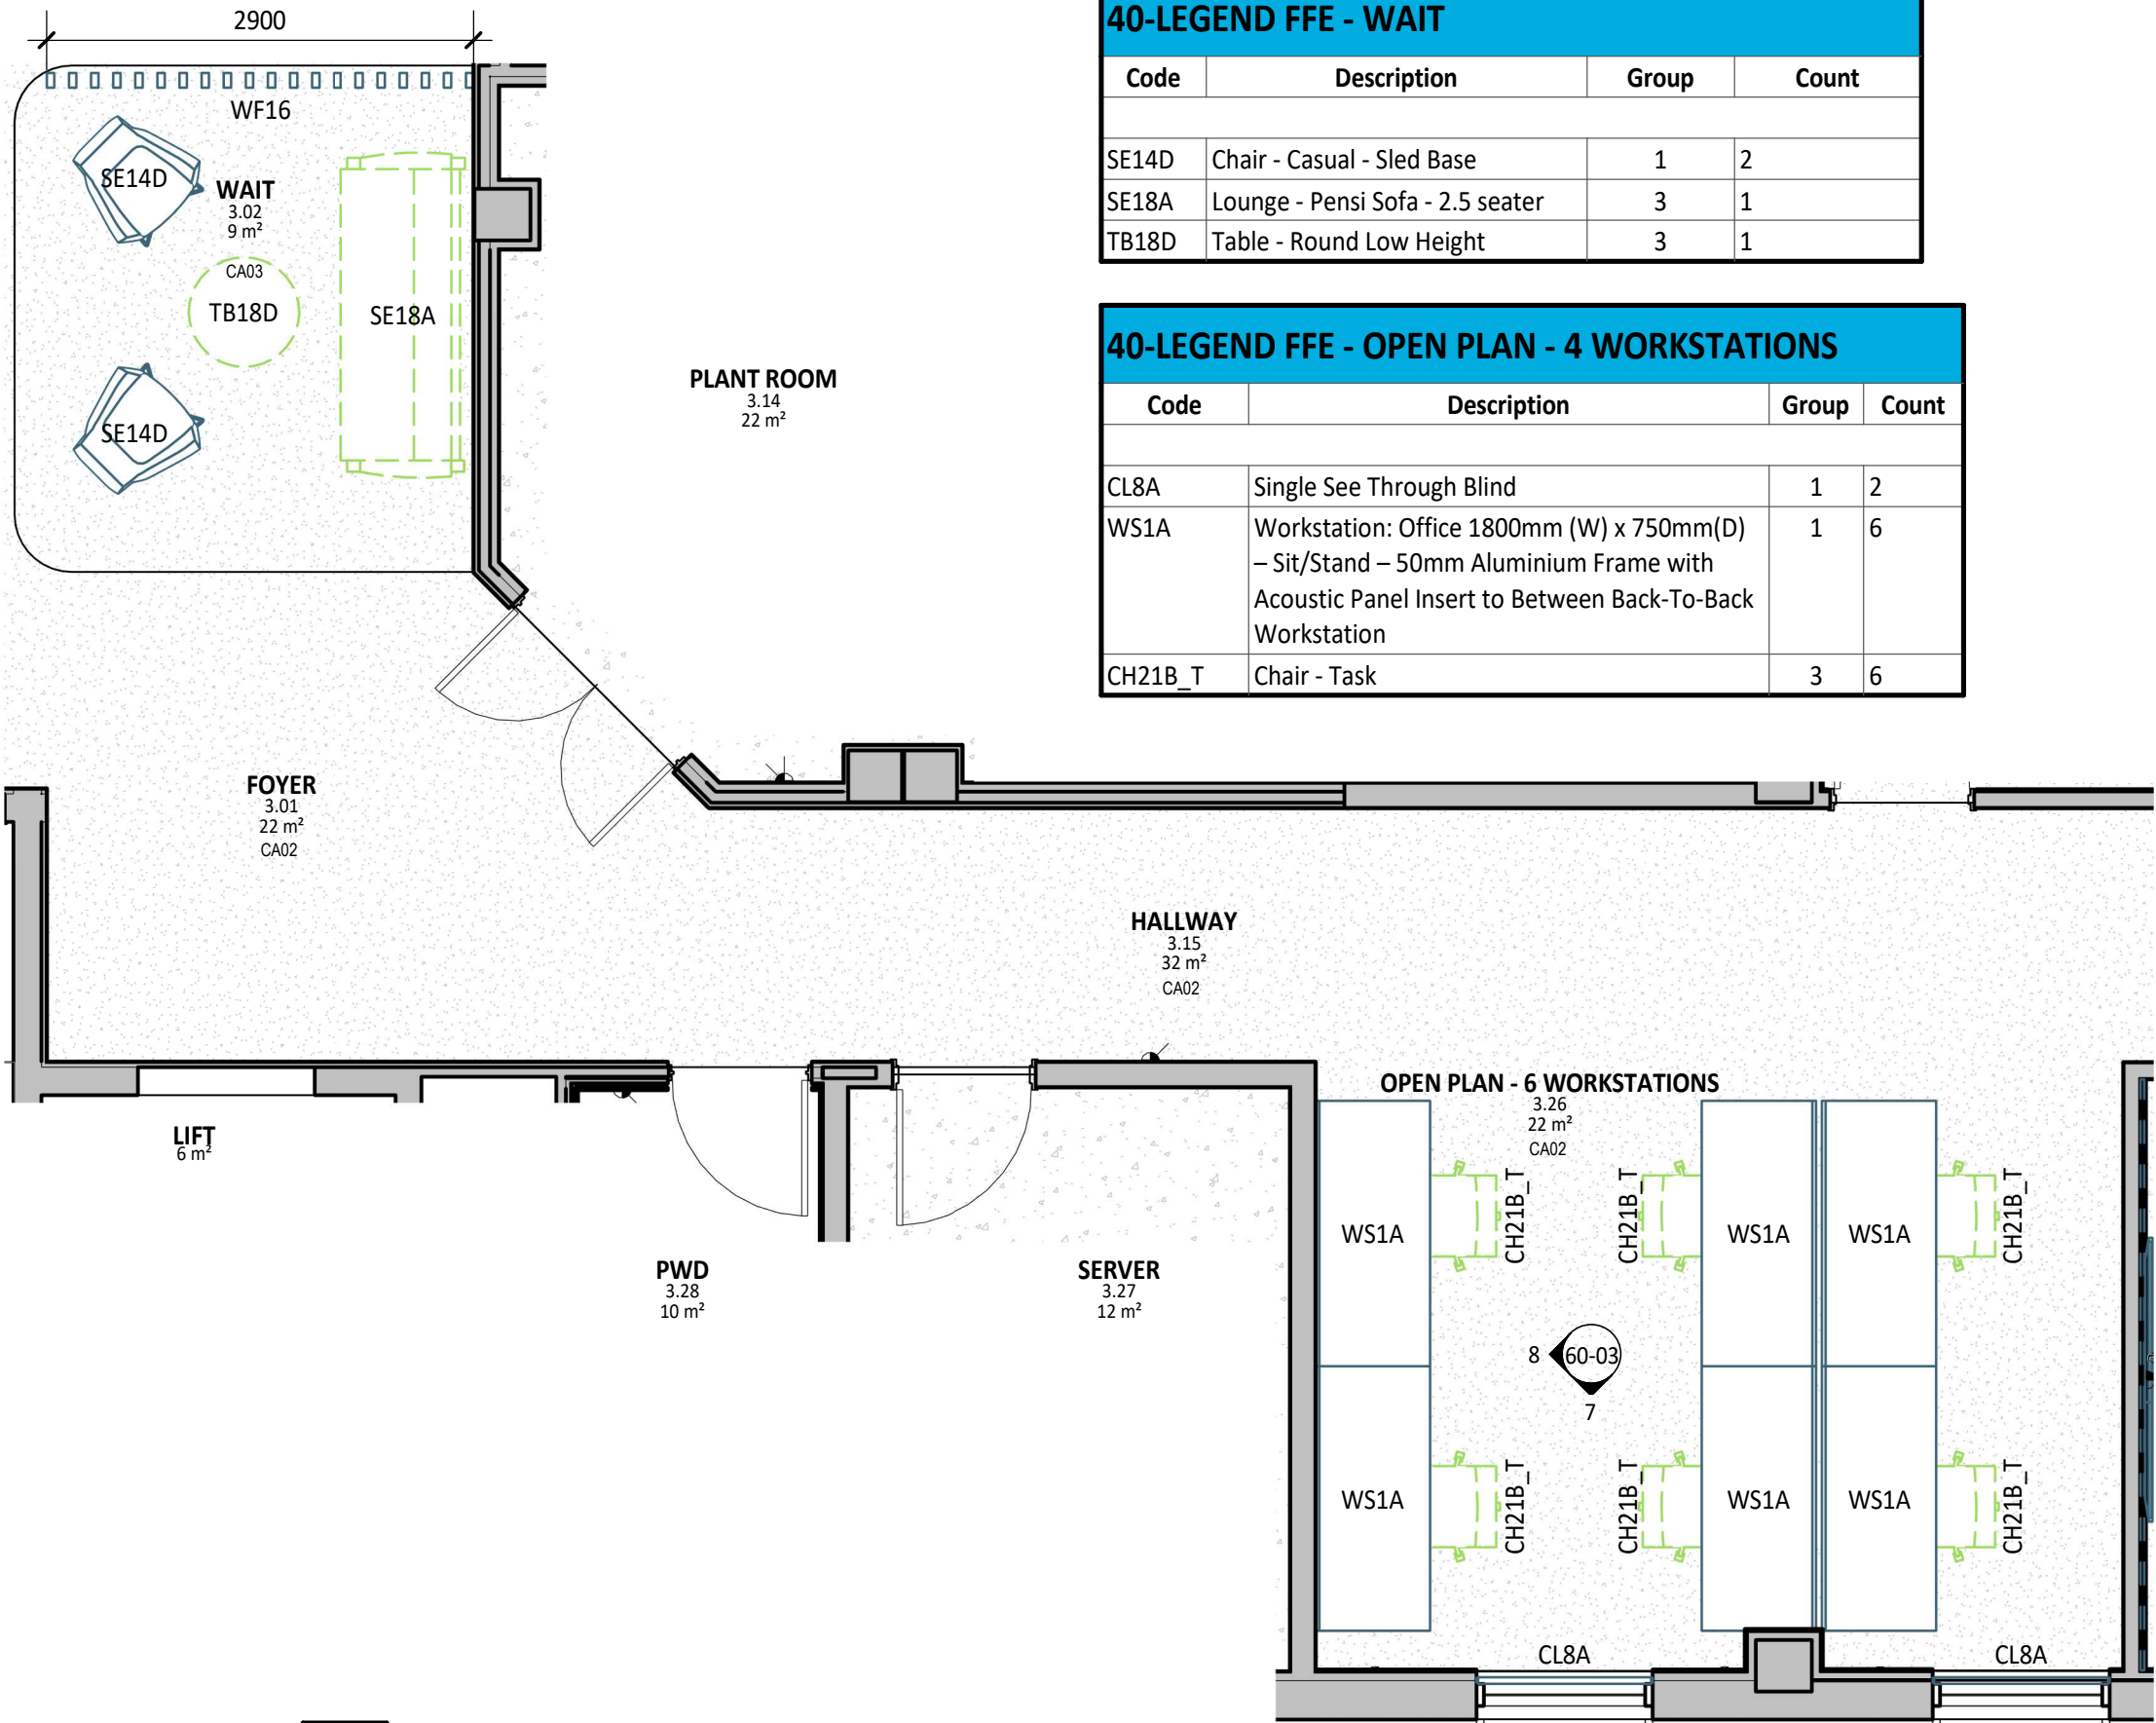


40-LEGEND FFE - WAIT			
Code	Description	Group	Count
SE14D	Chair - Casual - Sled Base	1	2
SE18A	Lounge - Pensi Sofa - 2.5 seater	3	1
TB18D	Table - Round Low Height	3	1

40-LEGEND FFE - OPEN PLAN - 4 WORKSTATIONS			
Code	Description	Group	Count
CL8A	Single See Through Blind	1	2
WS1A	Workstation: Office 1800mm (W) x 750mm(D) – Sit/Stand – 50mm Aluminium Frame with Acoustic Panel Insert to Between Back-To-Back Workstation	1	6
CH21B T	Chair - Task	3	6

1 PLAN DETAIL
1 : 50

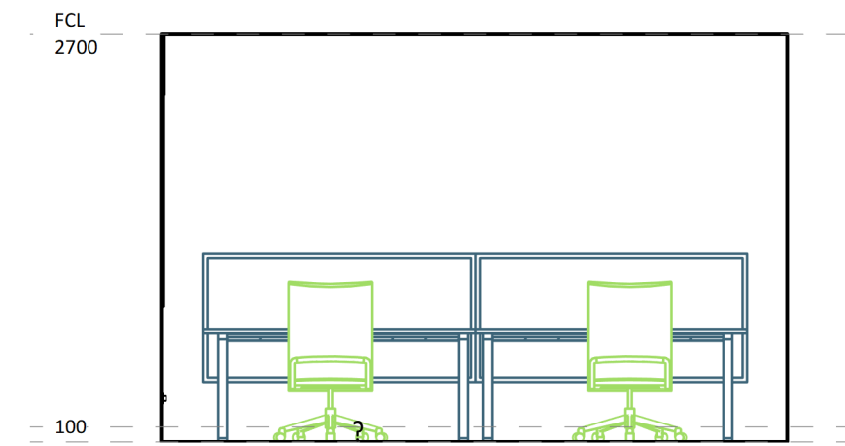


8 ELEVATION DETAIL
60-03 1 : 50

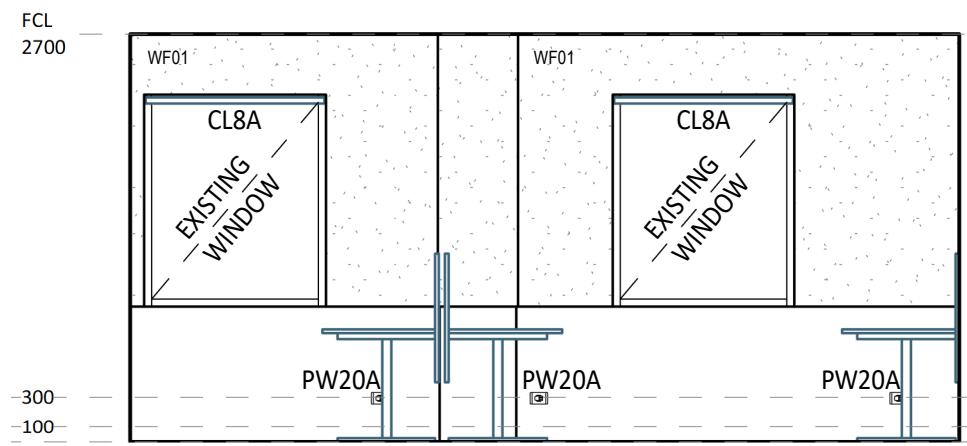


7 ELEVATION DETAIL
60-03 1 : 50


1PX OFFICE

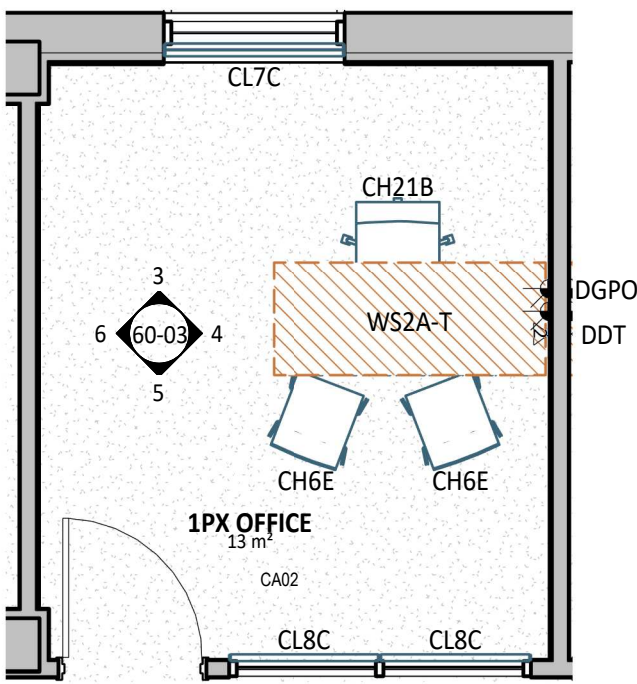

2 PLAN DETAIL
1 : 50

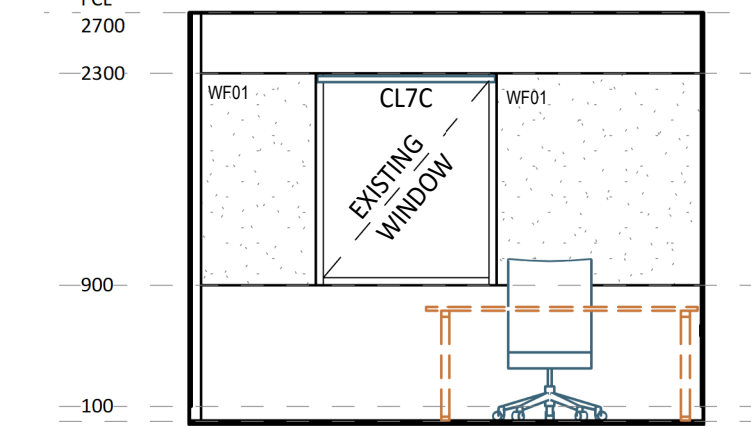


3 ELEVATION DETAIL
1 : 50

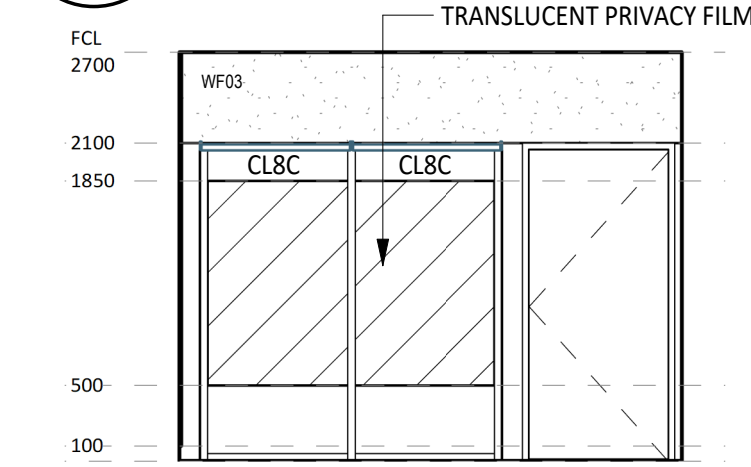


5 ELEVATION DETAIL
1 : 50

40-LEGEND FFE - 1PX OFFICE

Code	Description	Group	Count
CH6E	Chair - Sled Base Visitor Chair Upholstered Seat Pad	1	2
CH21B	Chair - Task	1	1
CL7C	Double Roller Blinds - Blockout	1	1
CL8C	Single Block Out Blind	1	2
WS2A-T	Workstation: Office 1800mm (W) x 750mm(D) – Sit/Stand	2T	1

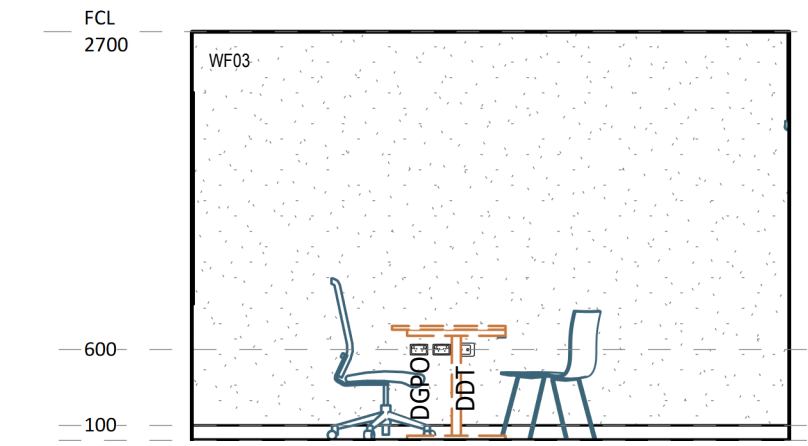

4 ELEVATION DETAIL
1 : 50

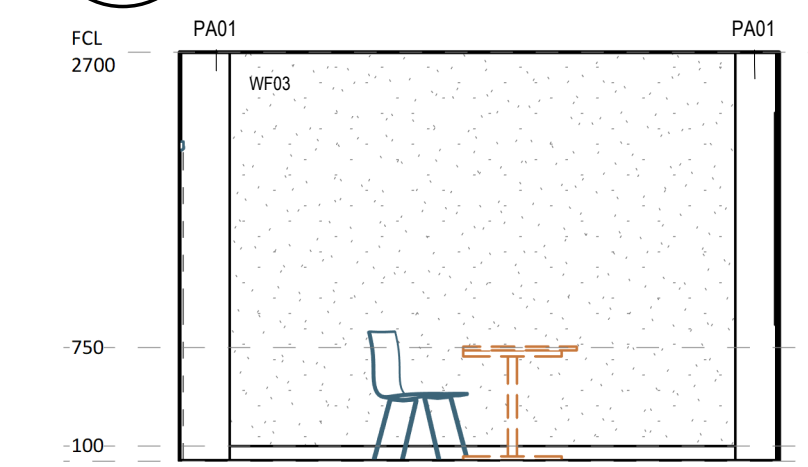

6 ELEVATION DETAIL
1 : 50

RLS NOTES

1. ALL ARCHITECTURAL DRAWINGS TO BE READ IN CONJUNCTION WITH OTHER DISCIPLINES.
2. REFER TO FF&E, SANITARYWARE SCHEDULES FOR ALL FURNITURE, FIXTURES, AND EQUIPMENT.
3. REFER TO HYDRAULIC ENGINEER'S DRAWINGS FOR HYDRAULIC SERVICES. FINISH OF VALVE/BOX COVERS TO MATCH ADJACENT WALL/JOINERY FINISH.
4. REFER TO ELECTRICAL DOCUMENTATION FOR OUTLET DETAILS (ie. POWER, DATA, COMMS etc.)
5. REFER TO AUDIO VISUAL DOCUMENTATION (VideoPro) FOR AV REQUIREMENTS AND DETAILS.
6. AV SUPPLIER TO CONFIRM EXACT POSITIONS OF EQUIPMENT ON SITE
7. ALL FF&E ITEMS ARE TO BE READ IN CONJUNCTION WITH FF&E SCHEDULES AND CQU DESIGN MANUAL.
8. ALL FF&E AND TRANSFER ITEMS TO BE REVIEWED AND CONFIRMED WITH CLIENT PRIOR TO COMMENCING ON SITE.
9. PROVIDE ALLOWANCE AND ADD SUPPORT TO WALLS, WHERE FITTINGS ARE WALL MOUNTED. THIS INCLUDES BUT NOT LIMITED TO HANDBASINS, HANDRAILS, SCREENS, PROJECTORS, etc.
10. FF&E COUNT IS FOR INFORMATION ONLY. THE TOTAL NUMBER OF FF&E ITEMS ARE TO BE CONFIRMED WITH CLIENT AND ARCHITECTS BEFORE PURCHASE OF ITEMS.
11. CONFIRM ALL DIMENSIONS ON SITE FOR JOINERY ITEMS.
12. ALL SANITARY FIXINGS & FIXTURES IN PWD TOILETS TO BE INSTALLED IN ACCORDANCE WITH AS1428.1
13. ALLOW FOR FIRE EXTINGUISHERS & FIRE BLANKETS AS PER AS2444.2001
14. POWER AND DATA POINTS SHOWN ON THE ROOM LAYOUT SHEETS WERE SHOWN AND DISCUSSED DURING USER GROUP BRIEFING. THESE RELATE TO PARTICULAR EQUIPMENT THAT WAS DISCUSSED AS REQUIRING POWER AND DATA. THESE REFLECT STAKEHOLDER EXPECTATIONS FOR SPECIFIC POWER AND DATA POINTS AND HAVE REMAINED IN THE DOCUMENTATION AS A USEFUL REFERENCE FOR THE CONTRACTOR. THESE ARE NOT A COMPLETE QUANTITY AND SPECIFICATION OF POWER AND DATA. THE CONTRACTOR IS TO REFER TO ELECTRICAL ENGINEER'S DOCUMENTATION FOR ALLOWANCE. REFER TO ELECTRICAL DOCUMENTATION FOR AMPS AND 3 PHASE POWER REQUIREMENTS. REFER TO AUDIO VISUAL (VIDEOPRO) DOCUMENTATION FOR ADDITIONAL POWER AND DATA REQUIREMENTS
15. ALLOW FOR STRUCTURAL PLY BACKING BEHIND PLASTERBOARD FOR FULL EXTENT OF WALLS WITH MOUNTED AUDIO VISUAL EQUIPMENT. REFER TO AUDIO VISUAL (VIDEOPRO) DOCUMENTATION FOR LOCATIONS OF WALL MOUNTED EQUIPMENT.
16. ALLOW FOR PRIVACY FILM TO ALL INTERNAL GLAZING (DOORS AND WINDOWS) TO OFFICES AND MEETING ROOMS. CONFIRM SET OUT PRIOR TO INSTALLATION
17. ALLOW FOR DOUBLE BLOCK OUT BLINDS TO ALL WINDOWS UNLESS NOTED OTHERWISE
18. ALL INTERNAL DOORS ARE TO BE SOLID CORE DOORS WITHIN ALUMINIUM FRAMED SUITES UNLESS NOTED OTHERWISE.
19. FLOOR BOXES MUST BE COORDINATED WITH BOTH THE STRUCTURAL AND ELECTRICAL ENGINEERS. BEFORE ANY CUTTING OF THE EXISTING SLAB OCCURS, CONFIRM THE EXACT LOCATIONS AND REQUIREMENTS WITH THE STRUCTURAL ENGINEER.
20. HEARING AUGMENTATION TO AUSTRALIAN STANDARDS – REFER VIDEOPRO AND ELECTRICAL SPECIFICATION

FF&E LEGEND

- GROUP 1 ITEMS (PROVIDED & FITTED UNDER CONTRACT)
- GROUP 2 ITEMS (PROVIDED BY CLIENT & FITTED UNDER CONTRACT)
- GROUP 2T ITEMS - EXISTING EQUIPMENT (PROVIDED BY CLIENT & FITTED UNDER CONTRACT)
- GROUP 3 ITEMS (PROVIDED & INSTALLED BY CLIENT)

PLANS TO BE PRINTED IN COLOUR

SCH_Code FF&E TAG

JO.PROC JOINERY TAG

ELECTRICAL LEGEND

- SINGLE POWER OUTLET
 - DOUBLE POWER OUTLET
 - SINGLE DATA
 - DOUBLE DATA
 - LIGHT SWITCH
 - TV
 - FLOOR BOX (FB)
- REFER TO ELECTRICAL ENGINEER'S DRAWINGS FOR DETAILS

thomson
adsett

PEDDLE THORP
architecture | interiors | health | planning

Telephone +61 7 3840 9999
bne@thomsonadsett.com
Level 9, 470 St Pauls Terrace
Fortitude Valley
QLD 4006 Australia
thomsonadsett.com

© Copyright

These drawings and designs and the copyright thereof are the property of Thomson Adsett Pty Ltd and must not be used, retained or copied without written permission of Thomson Adsett Pty Ltd. A.B.N 76 105 314 654 Trading as ThomsonAdsett. Dimensions take precedence over scaling. Do not measure off drawings as print sizes may vary

CQU ROCKHAMPTON
TAFE
CONSOLIDATION -
STAGE 2

554/700 Yaamba Rd, Norman
Gardens QLD 4701

for

CQUniversity
AUSTRALIA


B	05/03/26	ISSUED FOR TENDER	BS
A	12/02/26	ISSUED FOR TENDER	SM
2	30/01/26	60% DRAFT ISSUE	SM
1	23/01/26	FOR COORDINATION ISSUE	SM

rev	date	details	init.
-----	------	---------	-------

drawn	date
TA/PT	19/12/25

checked	date
JT/RJ	19/12/25

verified	date
JT/RJ	19/12/25

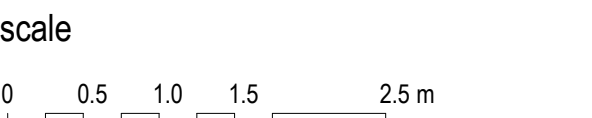

RLS - BLD19-L3 - OPEN
PLAN - 6 WORKSTATIONS,
WAIT, OFFICE

scale project no.
1 : 50 @ A1 260018

revision

B

sheet no.

CQU-ROK-019-03-ARC-60-03

ISSUE FOR TENDER

original sheet size - A1 (594mm x 841mm)