


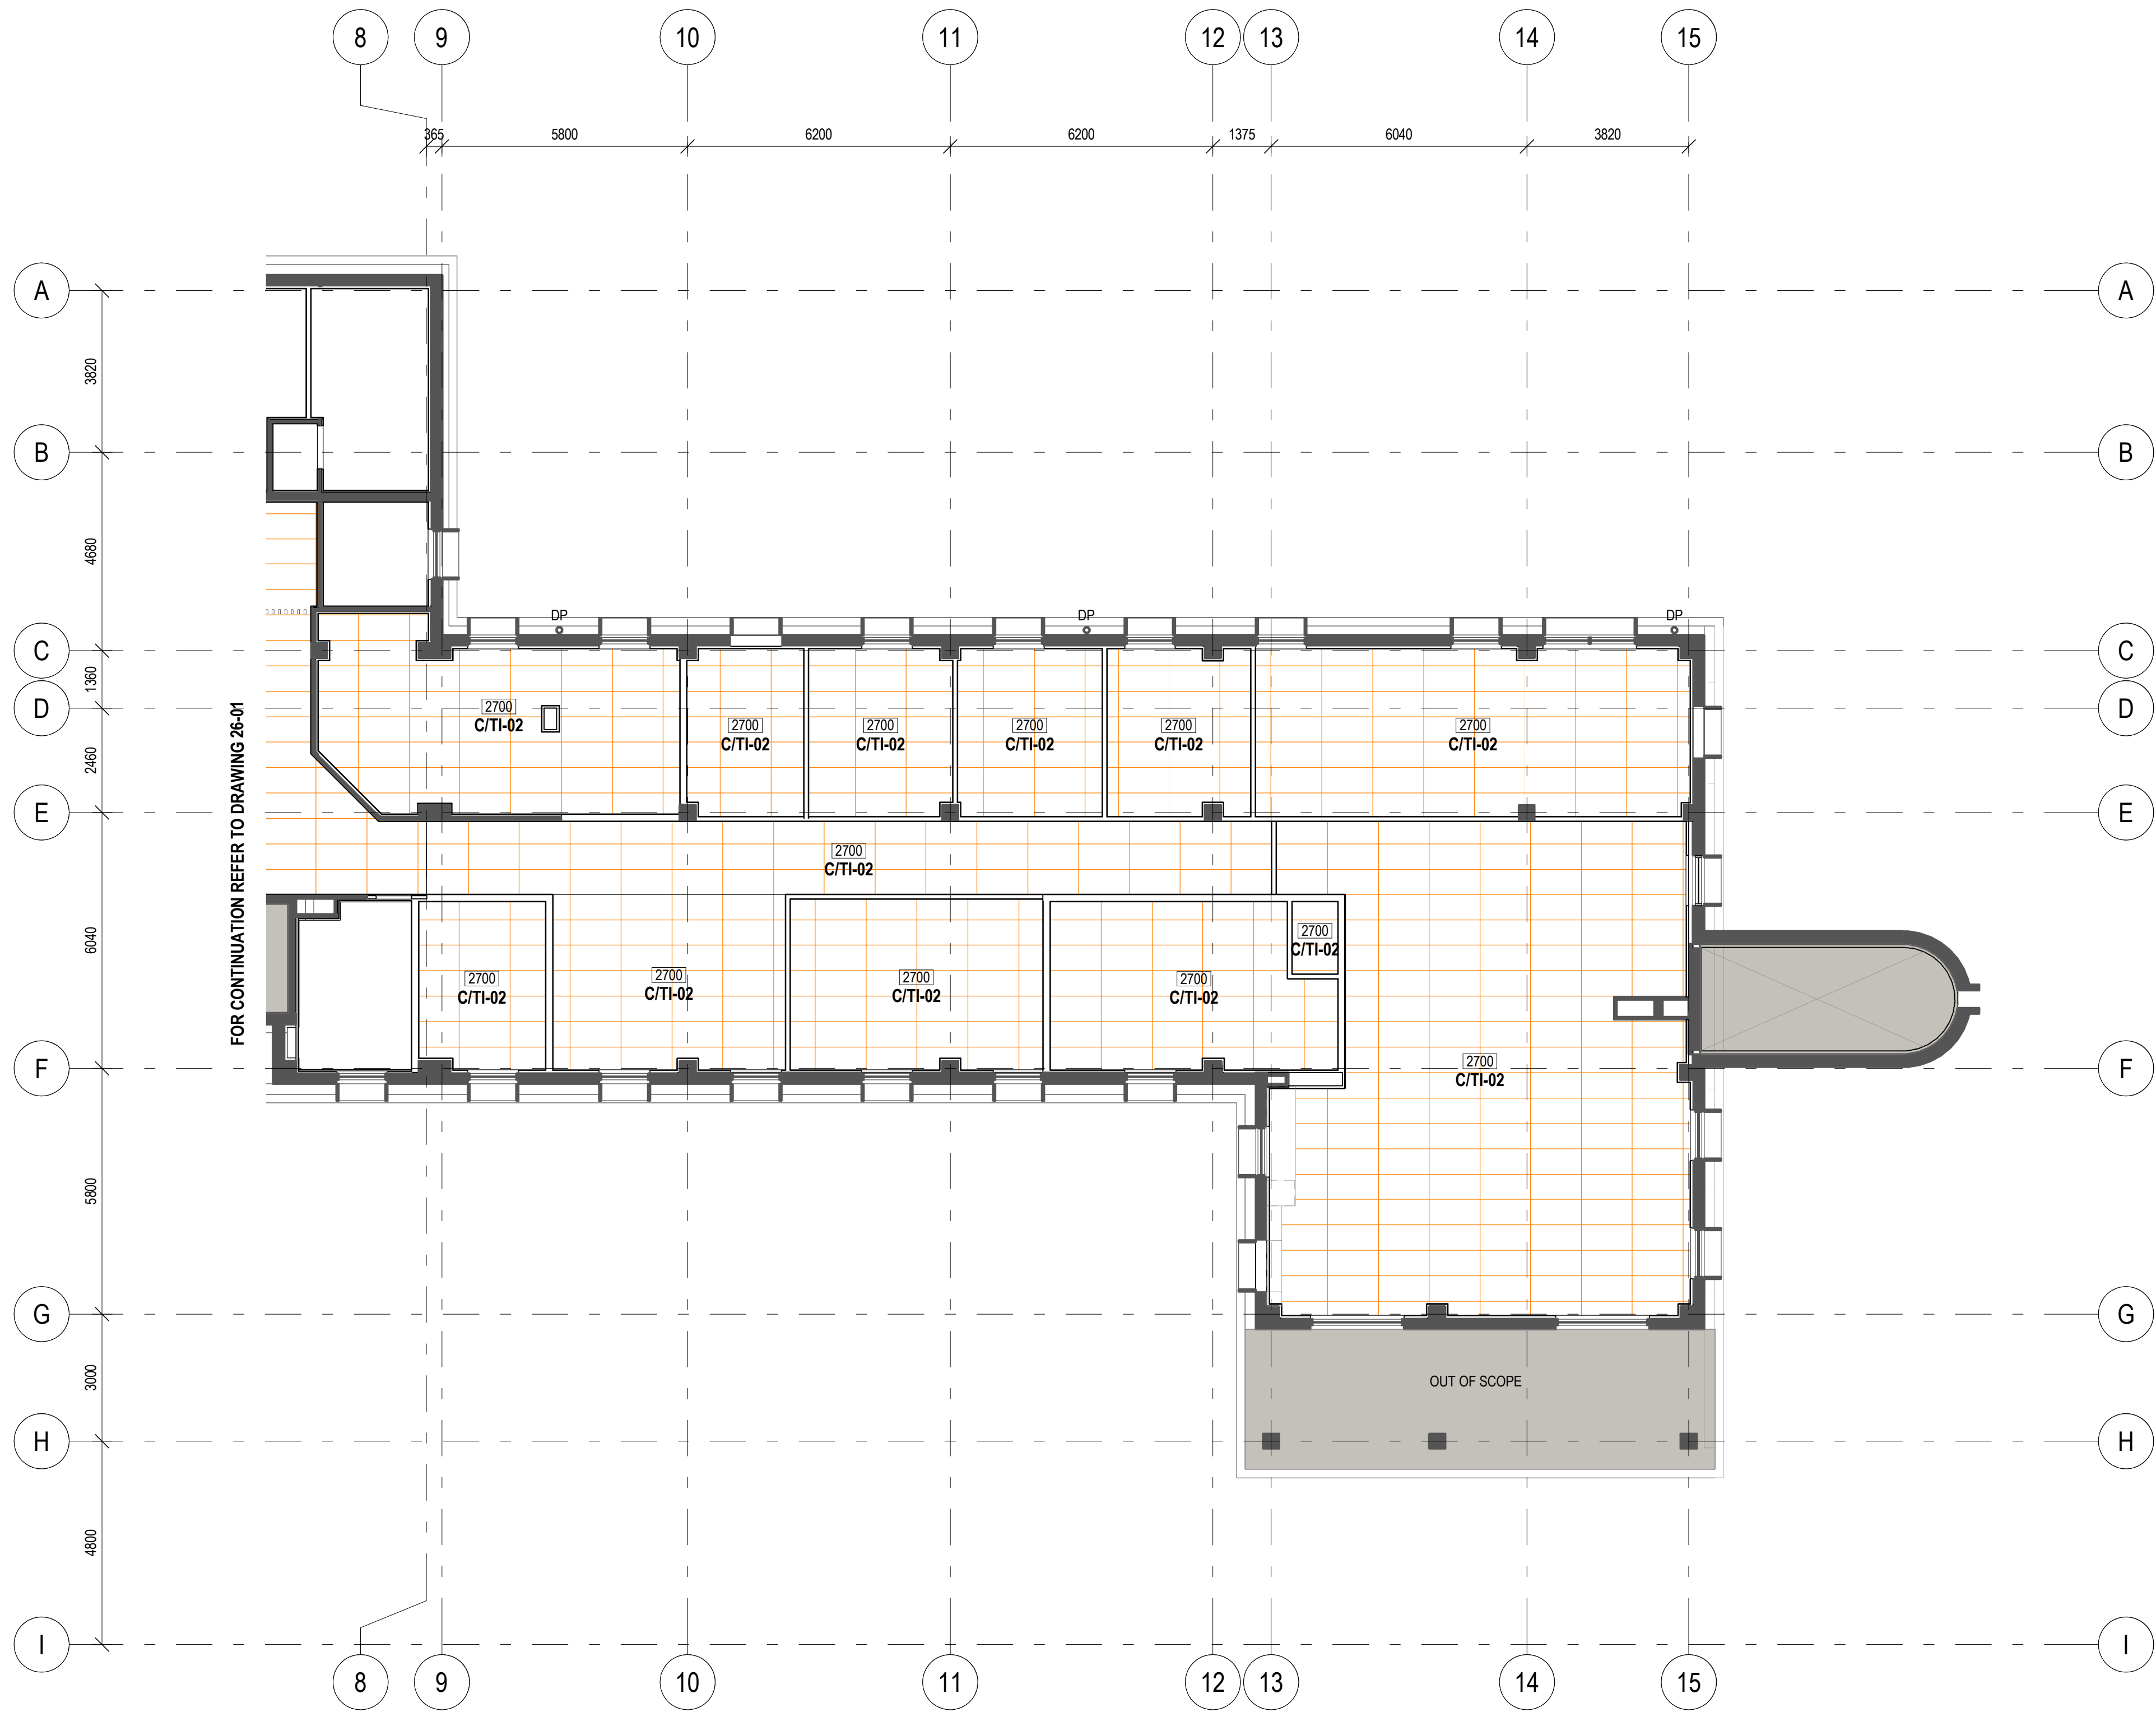

CEILING LEGEND	
	CEILING HEIGHT ABOVE FFL
	CEILING FINISHES
CEILING LEGEND	
C/TI-01	1200x600 CEILING TILES
C/TI-02	1200x600 ACOUSTIC CEILING TILES
C/PB-S1	FLUSH SET PLASTERBOARD SHEETING
C/PB-S2	WATERPROOF PLASTERBOARD SHEETING
C/FC-01	FLUSH SET FIBRE CEMENT SHEETING

GENERAL NOTES	
- CONTRACTOR TO CONFIRM EXISTING STRUCTURE & SERVICES ON SITE PRIOR BUILDING WORKS. - ALL REFLECTED CEILING PLANS ARE TO BE READ IN CONJUNCTION WITH SERVICE ENGINEERING DRAWINGS FOR MECHANICAL, FIRE, ELECTRICAL AND ALIKE. - CEILING REQUIREMENTS TO BE IN ACCORDANCE WITH CQU DESIGN GUIDELINES - REFER TO OUTLINE SPECIFICATION & SCHEDULE FOR FF&E AND FINISHES - SETOUT OF CEILING TILES TO BE CONFIRMED - READ IN CONJUNCTION WITH ACOUSTIC AND PART J REPORT. ALLOW ACOUSTIC INSULATION ABOVE AMENITIES. - CEILING GRID SET OUT CENTRED TO ROOM. - ALLOW FOR ACCESS HATCHES TO PLASTERBOARD CEILINGS. MIN. ONE PER ROOM.	

ISSUED FOR TENDER

© Copyright
These drawings and designs and the copyright thereof are the property of Thomson Adsett Pty Ltd and must not be used, retained or copied without written permission of Thomson Adsett Pty Ltd. ABN 76 105 314 654 Trading as ThomsonAdsett. Dimensions take precedence over scaling. Do not measure off drawings as print sizes may vary


**CQU ROCKHAMPTON
TAFE
CONSOLIDATION -
STAGE 2**

554/700 Yaamba Rd, Norman
Gardens QLD 4701



B	2026-03-05	ISSUED FOR TENDER	BC
A	2026-02-12	ISSUED FOR TENDER	BC
6	2026-01-30	60% DRAFT ISSUE	BC
5	2026-01-23	CONSULTANT ISSUES	BC
4	2025-12-19	UPDATED ISSUE	BC
3	2025-12-16	UPDATED ISSUE	BC
2	2025-12-15	CONSULTANTS REVIEW	BC
1	2025-11-24	50% COSTING ISSUE	PT
rev	date	details	init.

drawn	date
JS	19/01/2026
checked	date
SS	12/02/2026
verified	date

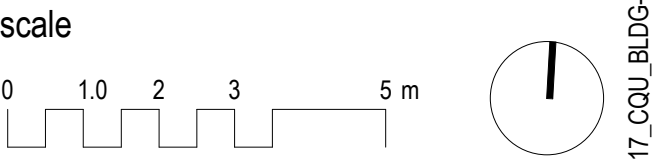

**CEILING PLAN - LEVEL 3 -
PART 2 PROPOSED**

scale project no.
1 : 100 @ A1 25.0236.17

revision
B
sheet no.
CQU-ROK-019-03-ARC-26-02