


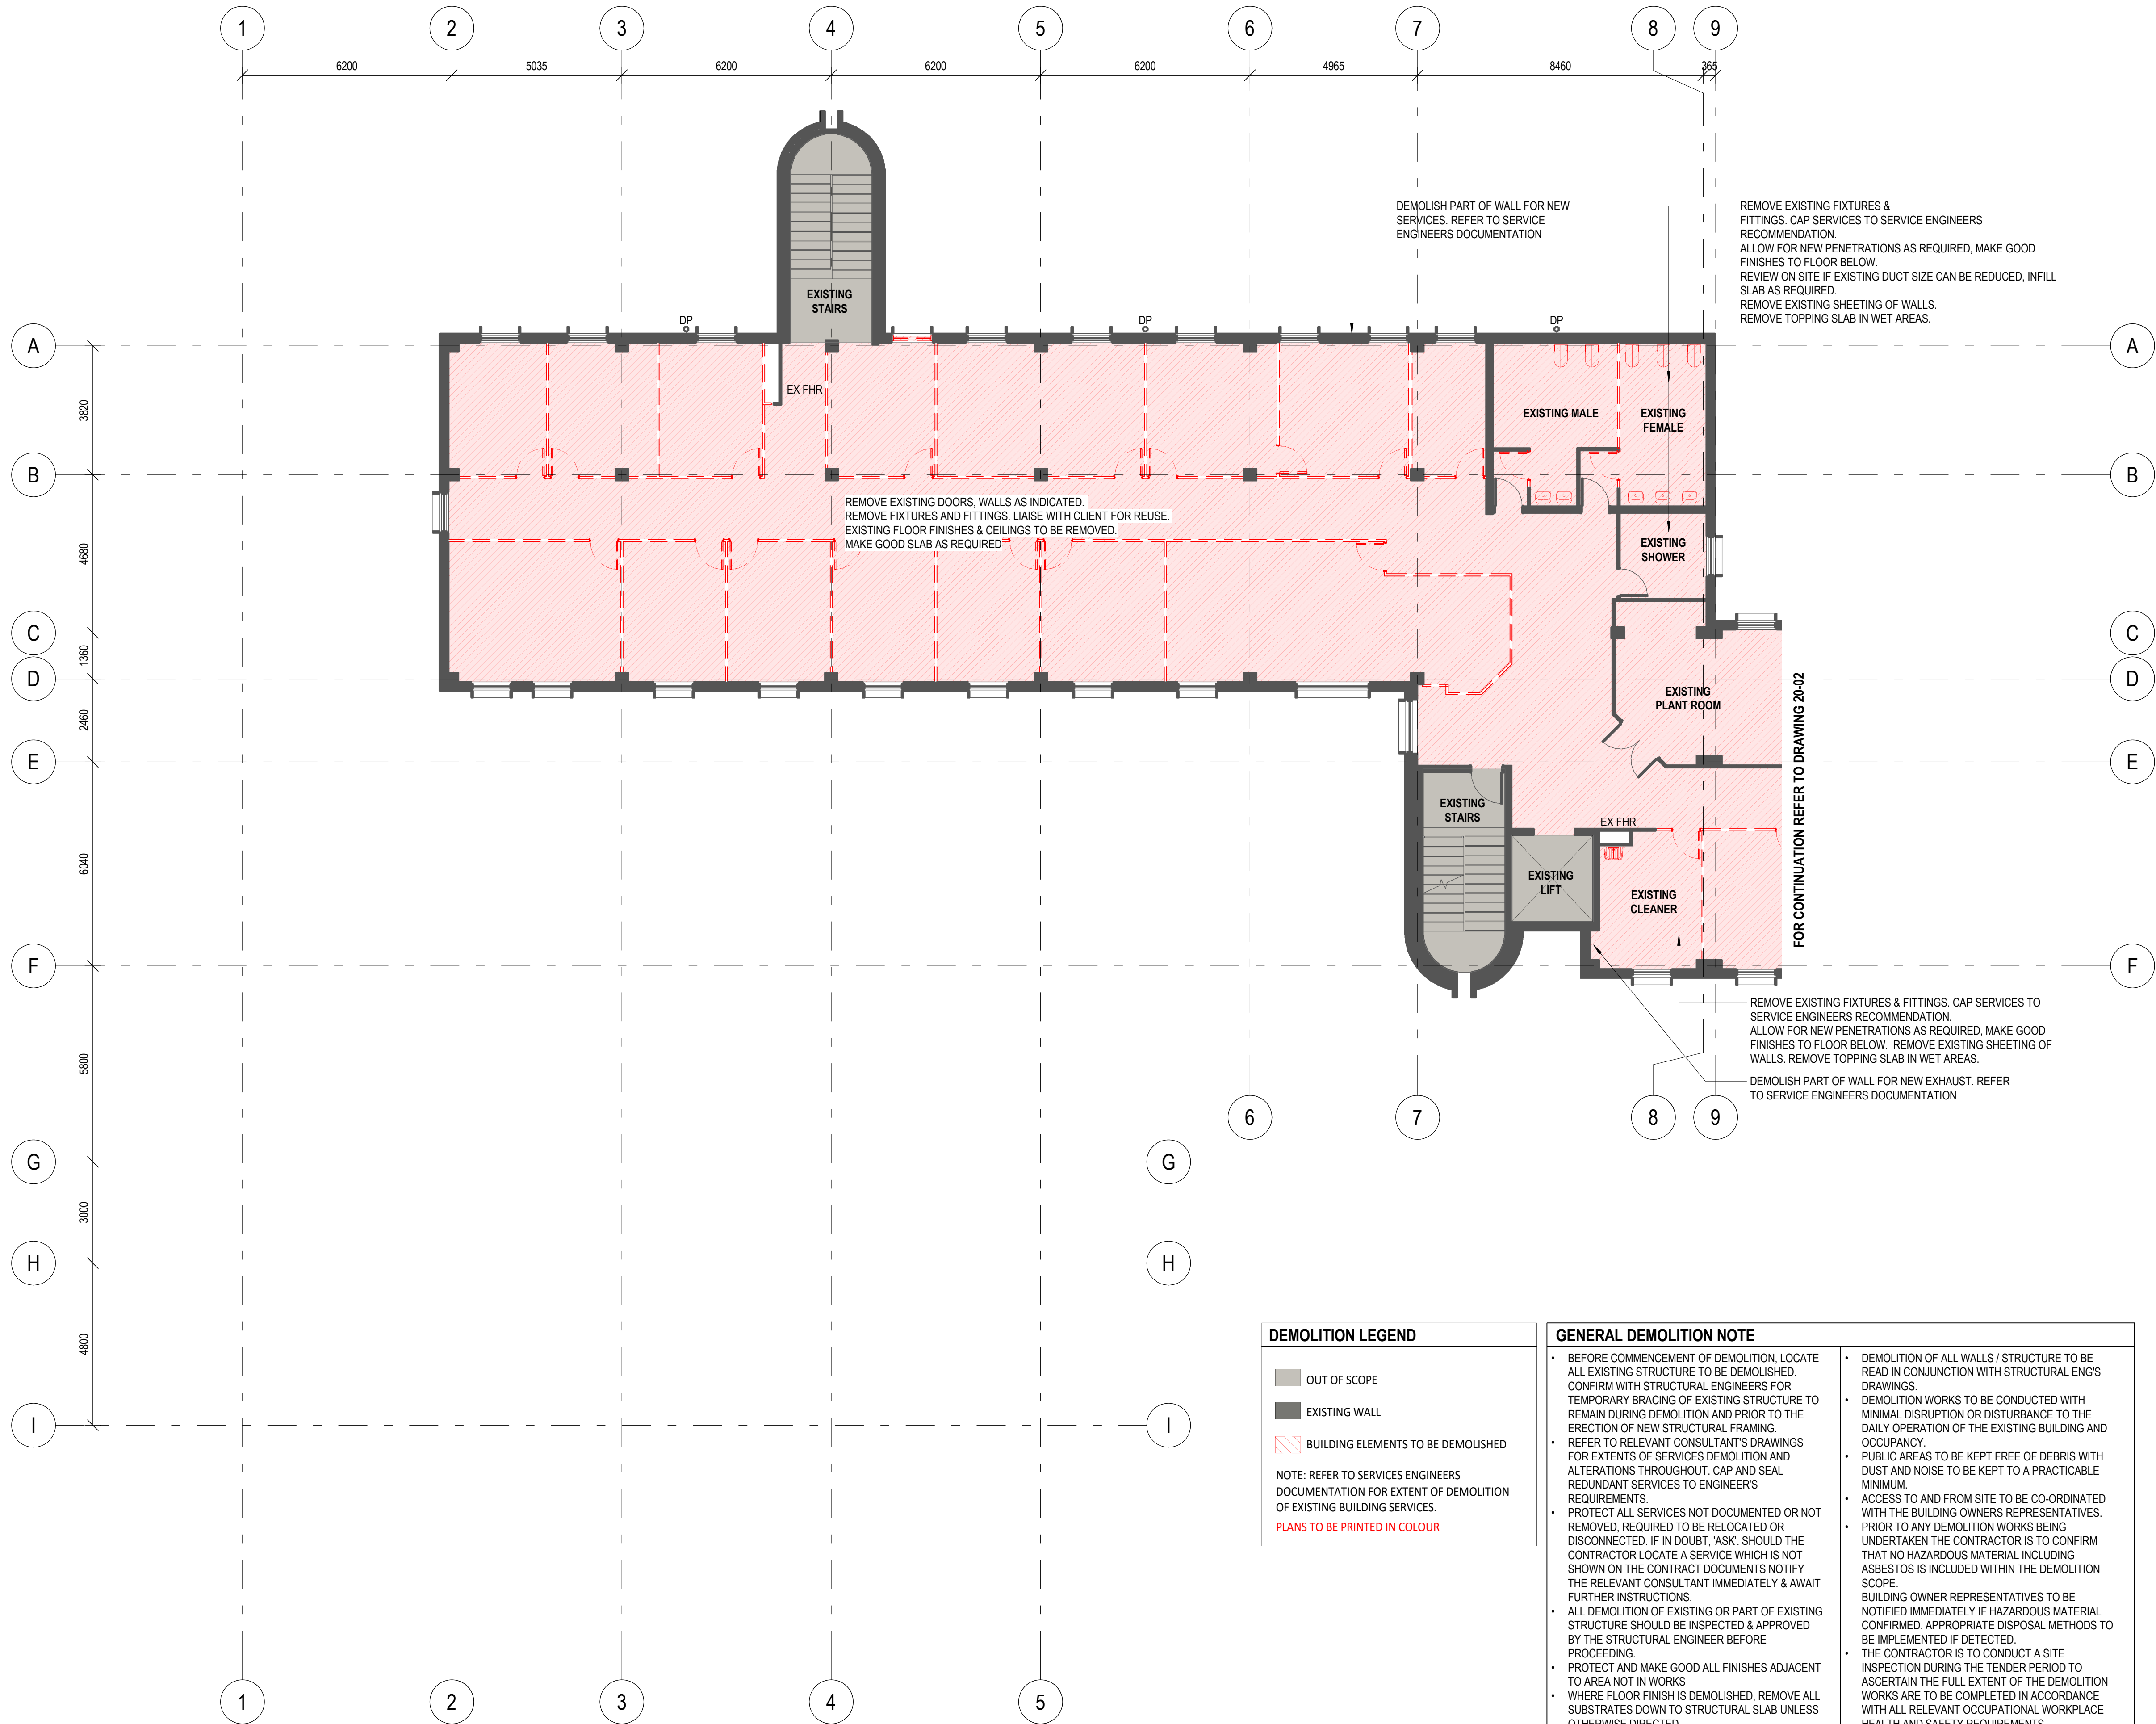

DEMOLITION LEGEND

- OUT OF SCOPE
 - EXISTING WALL
 - BUILDING ELEMENTS TO BE DEMOLISHED
- NOTE: REFER TO SERVICES ENGINEERS DOCUMENTATION FOR EXTENT OF DEMOLITION OF EXISTING BUILDING SERVICES.
- PLANS TO BE PRINTED IN COLOUR

GENERAL DEMOLITION NOTE

- BEFORE COMMENCEMENT OF DEMOLITION, LOCATE ALL EXISTING STRUCTURE TO BE DEMOLISHED. CONFIRM WITH STRUCTURAL ENGINEERS FOR TEMPORARY BRACING OF EXISTING STRUCTURE TO REMAIN DURING DEMOLITION AND PRIOR TO THE ERECTION OF NEW STRUCTURAL FRAMING.
- REFER TO RELEVANT CONSULTANT'S DRAWINGS FOR EXTENTS OF SERVICES DEMOLITION AND ALTERATIONS THROUGHOUT. CAP AND SEAL REDUNDANT SERVICES TO ENGINEER'S REQUIREMENTS.
- PROTECT ALL SERVICES NOT DOCUMENTED OR NOT REMOVED, REQUIRED TO BE RELOCATED OR DISCONNECTED. IF IN DOUBT, ASK: SHOULD THE CONTRACTOR LOCATE A SERVICE WHICH IS NOT SHOWN ON THE CONTRACT DOCUMENTS NOTIFY THE RELEVANT CONSULTANT IMMEDIATELY & AWAIT FURTHER INSTRUCTIONS.
- ALL DEMOLITION OF EXISTING OR PART OF EXISTING STRUCTURE SHOULD BE INSPECTED & APPROVED BY THE STRUCTURAL ENGINEER BEFORE PROCEEDING.
- PROTECT AND MAKE GOOD ALL FINISHES ADJACENT TO AREA NOT IN WORKS
- WHERE FLOOR FINISH IS DEMOLISHED, REMOVE ALL SUBSTRATES DOWN TO STRUCTURAL SLAB UNLESS OTHERWISE DIRECTED.
- PATCH, GRIND AND SMOOTH CONCRETE TO RECEIVE NEW FLOOR FINISHES. CONTRACTOR TO ALLOW FOR NEW LEVELLING COMPOUND IN PREPARATION OF SLAB SUBSTRATE.
- BUILDERS SITE ACCESS, SHED, PARKING, ENTRY POINTS & EXITS TO BE DETERMINED ON SITE WITH PROPRIETOR.
- DEMOLITION OF ALL WALLS / STRUCTURE TO BE READ IN CONJUNCTION WITH STRUCTURAL ENG'S DRAWINGS.
- DEMOLITION WORKS TO BE CONDUCTED WITH MINIMAL DISRUPTION OR DISTURBANCE TO THE DAILY OPERATION OF THE EXISTING BUILDING AND OCCUPANCY.
- PUBLIC AREAS TO BE KEPT FREE OF DEBRIS WITH DUST AND NOISE TO BE KEPT TO A PRACTICABLE MINIMUM.
- ACCESS TO AND FROM SITE TO BE CO-ORDINATED WITH THE BUILDING OWNERS REPRESENTATIVES.
- PRIOR TO ANY DEMOLITION WORKS BEING UNDERTAKEN THE CONTRACTOR IS TO CONFIRM THAT NO HAZARDOUS MATERIAL INCLUDING ASBESTOS IS INCLUDED WITHIN THE DEMOLITION SCOPE. BUILDING OWNER REPRESENTATIVES TO BE NOTIFIED IMMEDIATELY IF HAZARDOUS MATERIAL CONFIRMED. APPROPRIATE DISPOSAL METHODS TO BE IMPLEMENTED IF DETECTED.
- THE CONTRACTOR IS TO CONDUCT A SITE INSPECTION DURING THE TENDER PERIOD TO ASCERTAIN THE FULL EXTENT OF THE DEMOLITION WORKS ARE TO BE COMPLETED IN ACCORDANCE WITH ALL RELEVANT OCCUPATIONAL WORKPLACE HEALTH AND SAFETY REQUIREMENTS.
- INSTALL PROTECTIVE HOARDING AROUND WORK ZONE AND ADJACENT EXISTING AREAS WHICH ARE TO REMAIN UNAFFECTED BY DEMOLITION WORKS.
- CONTRACTOR TO ALLOW FOR REINSTATEMENT OF ANY EXISTING SERVICES WITHIN TENANCIES AFFECTED BY DEMOLITION WORKS.
- REMOVE INTERNAL SHEETING TO EXISTING WALLS AS REQUIRED (EXCLUDING LIFT AND STAIRS).

© Copyright
These drawings and designs and the copyright thereof are the property of Thomson Adsett Pty Ltd and must not be used, retained or copied without written permission of Thomson Adsett Pty Ltd. ABN 76 105 314 654 Trading as ThomsonAdsett. Dimensions take precedence over scaling. Do not measure off drawings as print sizes may vary


CQU ROCKHAMPTON TAFE CONSOLIDATION - STAGE 2

554/700 Yaamba Rd, Norman
Gardens QLD 4701



B	2026-03-05	ISSUED FOR TENDER	BC
A	2026-02-12	ISSUED FOR TENDER	BC
4	2026-01-30	60% DRAFT ISSUE	BC
3	2025-12-19	UPDATED ISSUE	BC
2	2025-12-15	CONSULTANTS REVIEW	BC
1	2025-11-24	50% COSTING ISSUE	PT
rev	date	details	init.

drawn	date
JS	19/01/2026
checked	date
SS	12/02/2026
verified	date

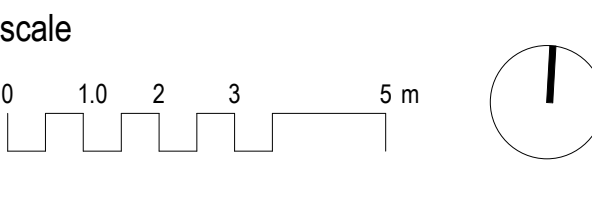

FLOOR PLAN - LEVEL 3 - PART 1 DEMOLITION

scale	project no.
As indicated @ A1	25.0236.17
revision	
B	
sheet no.	
CQU-ROK-019-03-ARC-20-01	

ISSUED FOR TENDER


**CQU ROCKHAMPTON
TAFE
CONSOLIDATION -
STAGE 2**

554/700 Yaamba Rd, Norman
Gardens QLD 4701




B	2026-03-05	ISSUED FOR TENDER	BC
A	2026-02-12	ISSUED FOR TENDER	BC
4	2026-01-30	60% DRAFT ISSUE	BC
3	2025-12-19	UPDATED ISSUE	BC
2	2025-12-15	CONSULTANTS REVIEW	BC
1	2025-11-24	50% COSTING ISSUE	PT
rev	date	details	init.

drawn	date
JS	19/01/2026
checked	date
SS	12/02/2026
verified	date

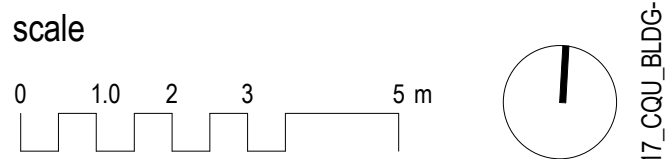

**FLOOR PLAN - LEVEL 3 -
PART 2 DEMOLITION**

scale project no.
As indicated @ A1 25.0236.17
revision
B
sheet no.
CQU-ROK-019-03-ARC-20-02

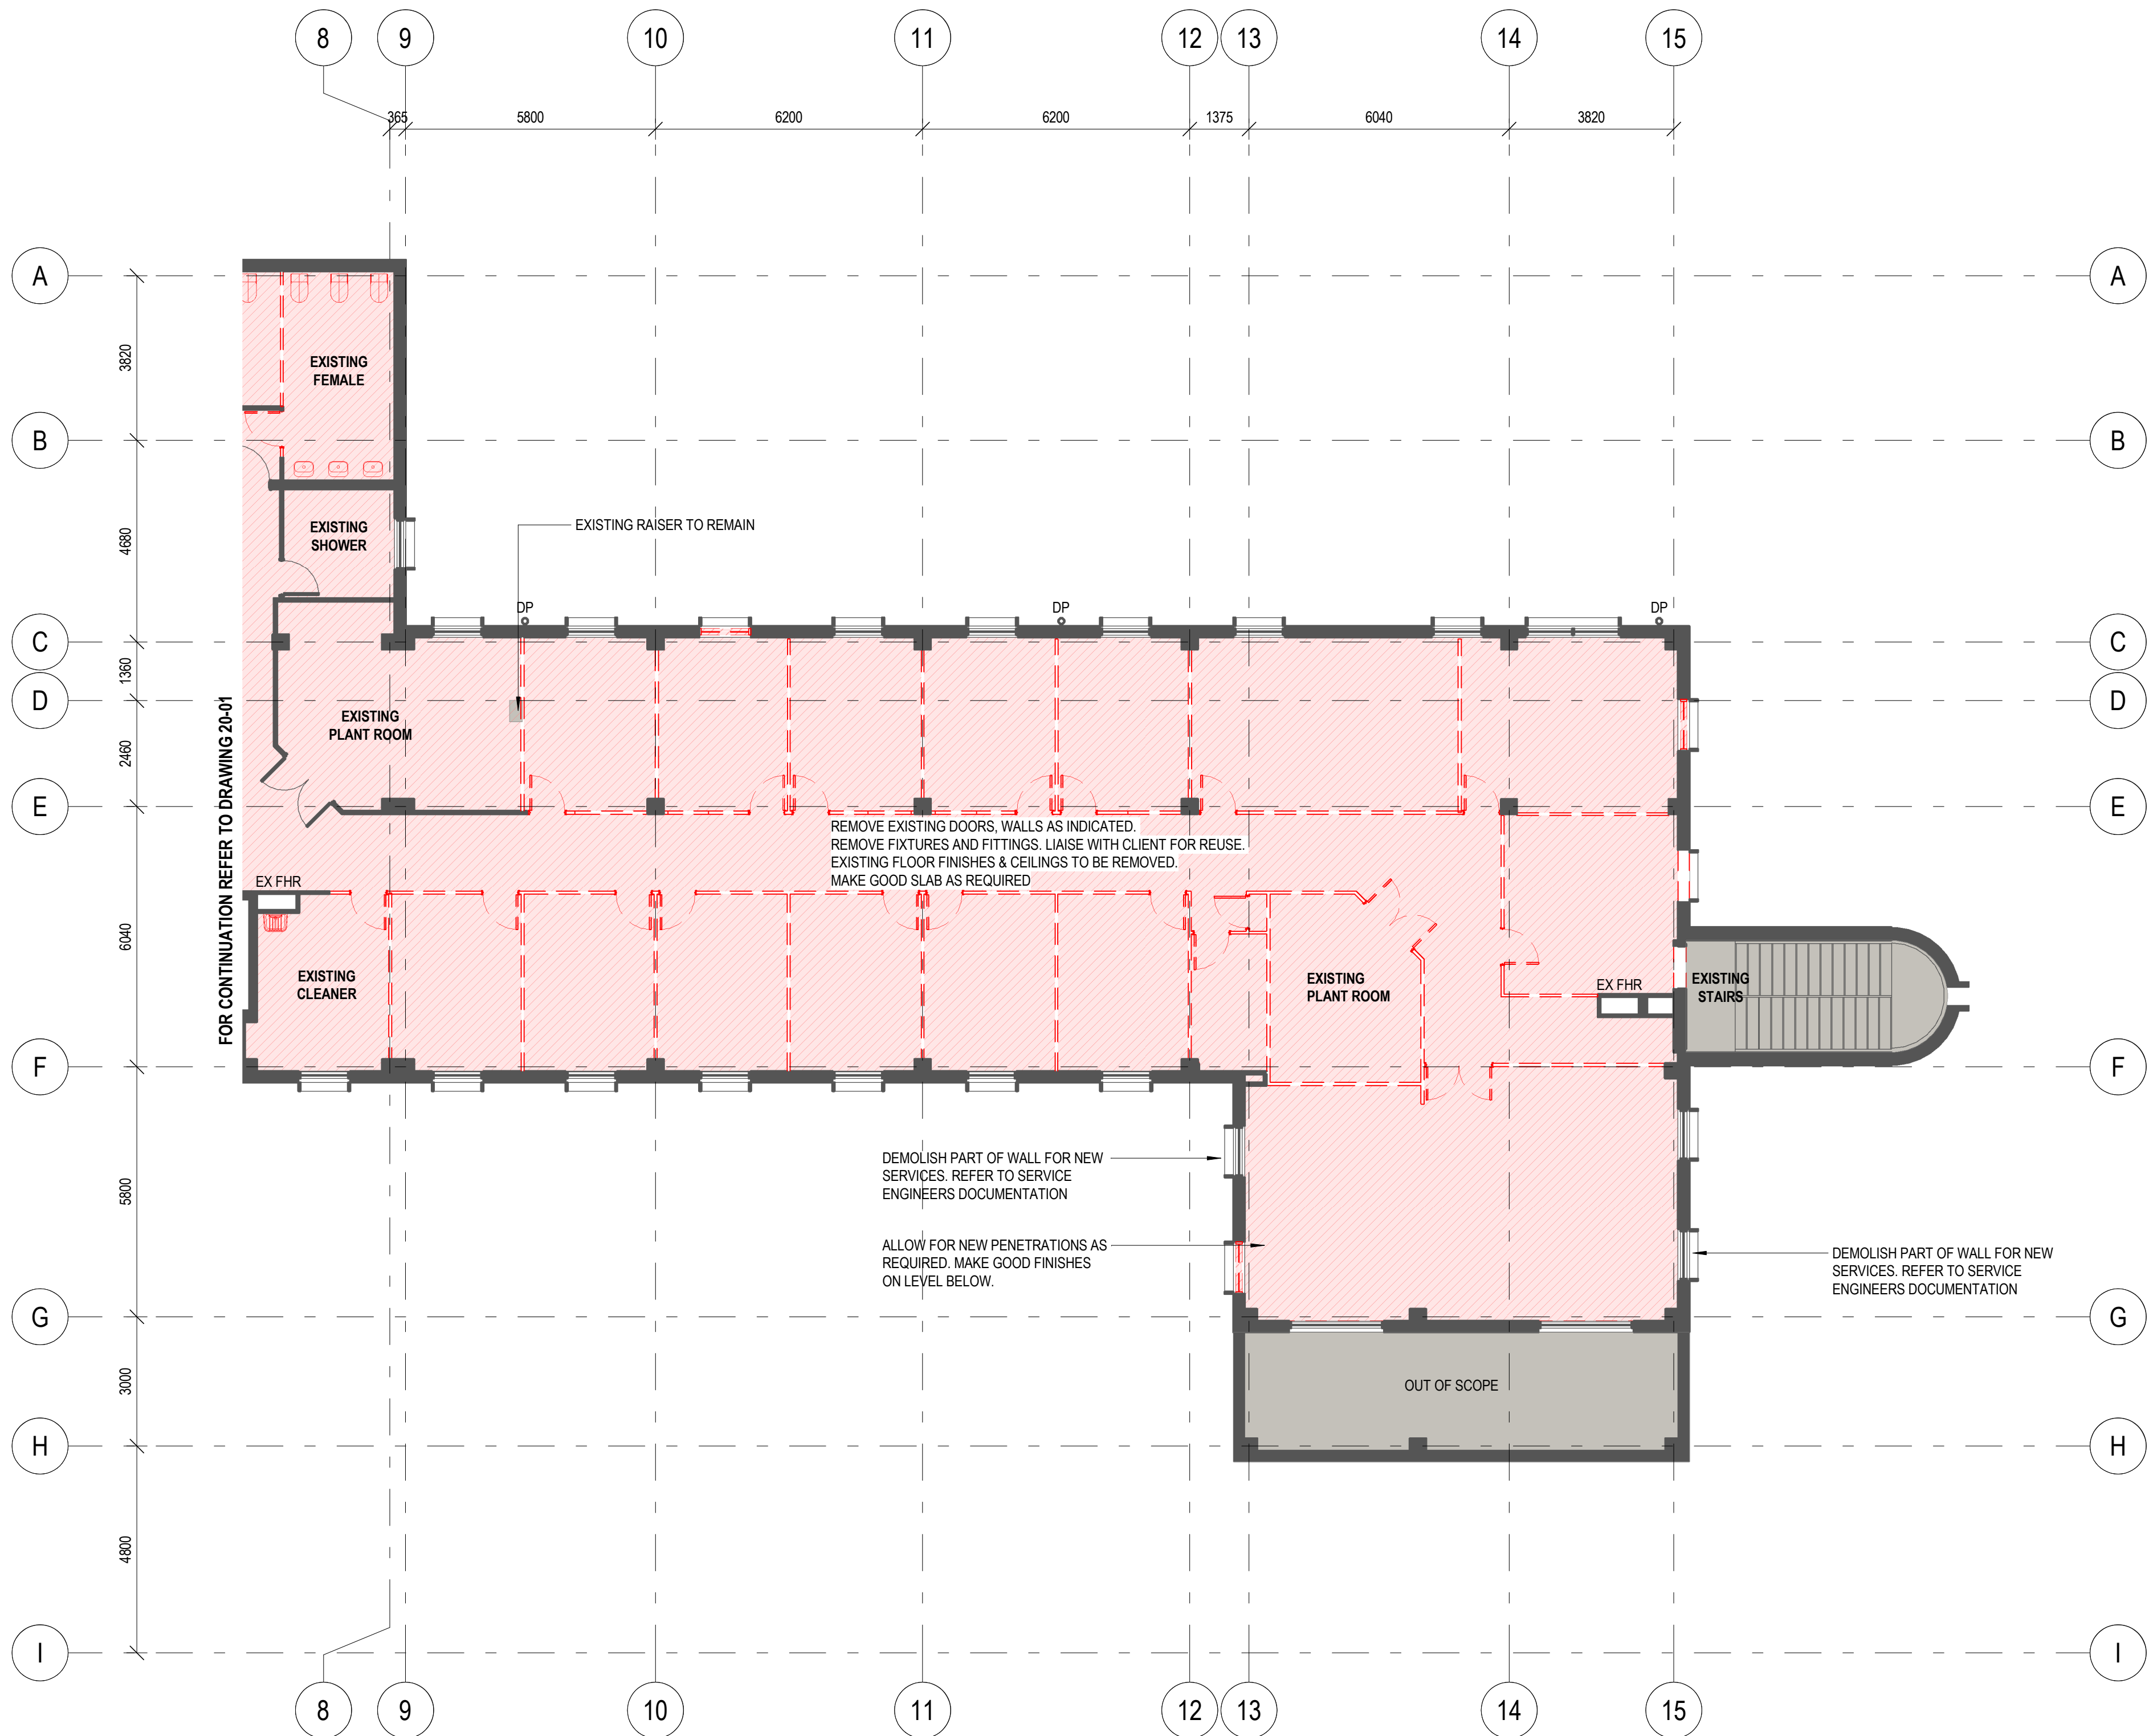


DEMOLITION LEGEND

- OUT OF SCOPE
 - EXISTING WALL
 - BUILDING ELEMENTS TO BE DEMOLISHED
- NOTE: REFER TO SERVICES ENGINEERS DOCUMENTATION FOR EXTENT OF DEMOLITION OF EXISTING BUILDING SERVICES.
PLANS TO BE PRINTED IN COLOUR

GENERAL DEMOLITION NOTE

- BEFORE COMMENCEMENT OF DEMOLITION, LOCATE ALL EXISTING STRUCTURE TO BE DEMOLISHED. CONFIRM WITH STRUCTURAL ENGINEERS FOR TEMPORARY BRACING OF EXISTING STRUCTURE TO REMAIN DURING DEMOLITION AND PRIOR TO THE ERECTION OF NEW STRUCTURAL FRAMING.
- REFER TO RELEVANT CONSULTANT'S DRAWINGS FOR EXTENTS OF SERVICES DEMOLITION AND ALTERATIONS THROUGHOUT. CAP AND SEAL REDUNDANT SERVICES TO ENGINEER'S REQUIREMENTS.
- PROTECT ALL SERVICES NOT DOCUMENTED OR NOT REMOVED, REQUIRED TO BE RELOCATED OR DISCONNECTED. IF IN DOUBT, ASK. SHOULD THE CONTRACTOR LOCATE A SERVICE WHICH IS NOT SHOWN ON THE CONTRACT DOCUMENTS NOTIFY THE RELEVANT CONSULTANT IMMEDIATELY & AWAIT FURTHER INSTRUCTIONS.
- ALL DEMOLITION OF EXISTING OR PART OF EXISTING STRUCTURE SHOULD BE INSPECTED & APPROVED BY THE STRUCTURAL ENGINEER BEFORE PROCEEDING.
- PROTECT AND MAKE GOOD ALL FINISHES ADJACENT TO AREA NOT IN WORKS
- WHERE FLOOR FINISH IS DEMOLISHED, REMOVE ALL SUBSTRATES DOWN TO STRUCTURAL SLAB UNLESS OTHERWISE DIRECTED.
- PATCH, GRIND AND SMOOTH CONCRETE TO RECEIVE NEW FLOOR FINISHES. CONTRACTOR TO ALLOW FOR NEW LEVELLING COMPOUND IN PREPARATION OF SLAB SUBSTRATE.
- BUILDERS SITE ACCESS, SHED, PARKING, ENTRY POINTS & EXITS TO BE DETERMINED ON SITE WITH PROPRIETOR.
- DEMOLITION OF ALL WALLS / STRUCTURE TO BE READ IN CONJUNCTION WITH STRUCTURAL ENG'S DRAWINGS.
- DEMOLITION WORKS TO BE CONDUCTED WITH MINIMAL DISRUPTION OR DISTURBANCE TO THE DAILY OPERATION OF THE EXISTING BUILDING AND OCCUPANCY.
- PUBLIC AREAS TO BE KEPT FREE OF DEBRIS WITH DUST AND NOISE TO BE KEPT TO A PRACTICABLE MINIMUM.
- ACCESS TO AND FROM SITE TO BE CO-ORDINATED WITH THE BUILDING OWNERS REPRESENTATIVES.
- PRIOR TO ANY DEMOLITION WORKS BEING UNDERTAKEN THE CONTRACTOR IS TO CONFIRM THAT NO HAZARDOUS MATERIAL INCLUDING ASBESTOS IS INCLUDED WITHIN THE DEMOLITION SCOPE. BUILDING OWNER REPRESENTATIVES TO BE NOTIFIED IMMEDIATELY IF HAZARDOUS MATERIAL CONFIRMED. APPROPRIATE DISPOSAL METHODS TO BE IMPLEMENTED IF DETECTED.
- THE CONTRACTOR IS TO CONDUCT A SITE INSPECTION DURING THE TENDER PERIOD TO ASCERTAIN THE FULL EXTENT OF THE DEMOLITION WORKS ARE TO BE COMPLETED IN ACCORDANCE WITH ALL RELEVANT OCCUPATIONAL WORKPLACE HEALTH AND SAFETY REQUIREMENTS.
- INSTALL PROTECTIVE HOARDING AROUND WORK ZONE AND ADJACENT EXISTING AREAS WHICH ARE TO REMAIN UNAFFECTED BY DEMOLITION WORKS.
- CONTRACTOR TO ALLOW FOR REINSTATEMENT OF ANY EXISTING SERVICES WITHIN TENANCIES AFFECTED BY DEMOLITION WORKS.
- REMOVE INTERNAL SHEETING TO EXISTING WALLS AS REQUIRED (EXCLUDING LIFT AND STAIRS).

ISSUED FOR TENDER

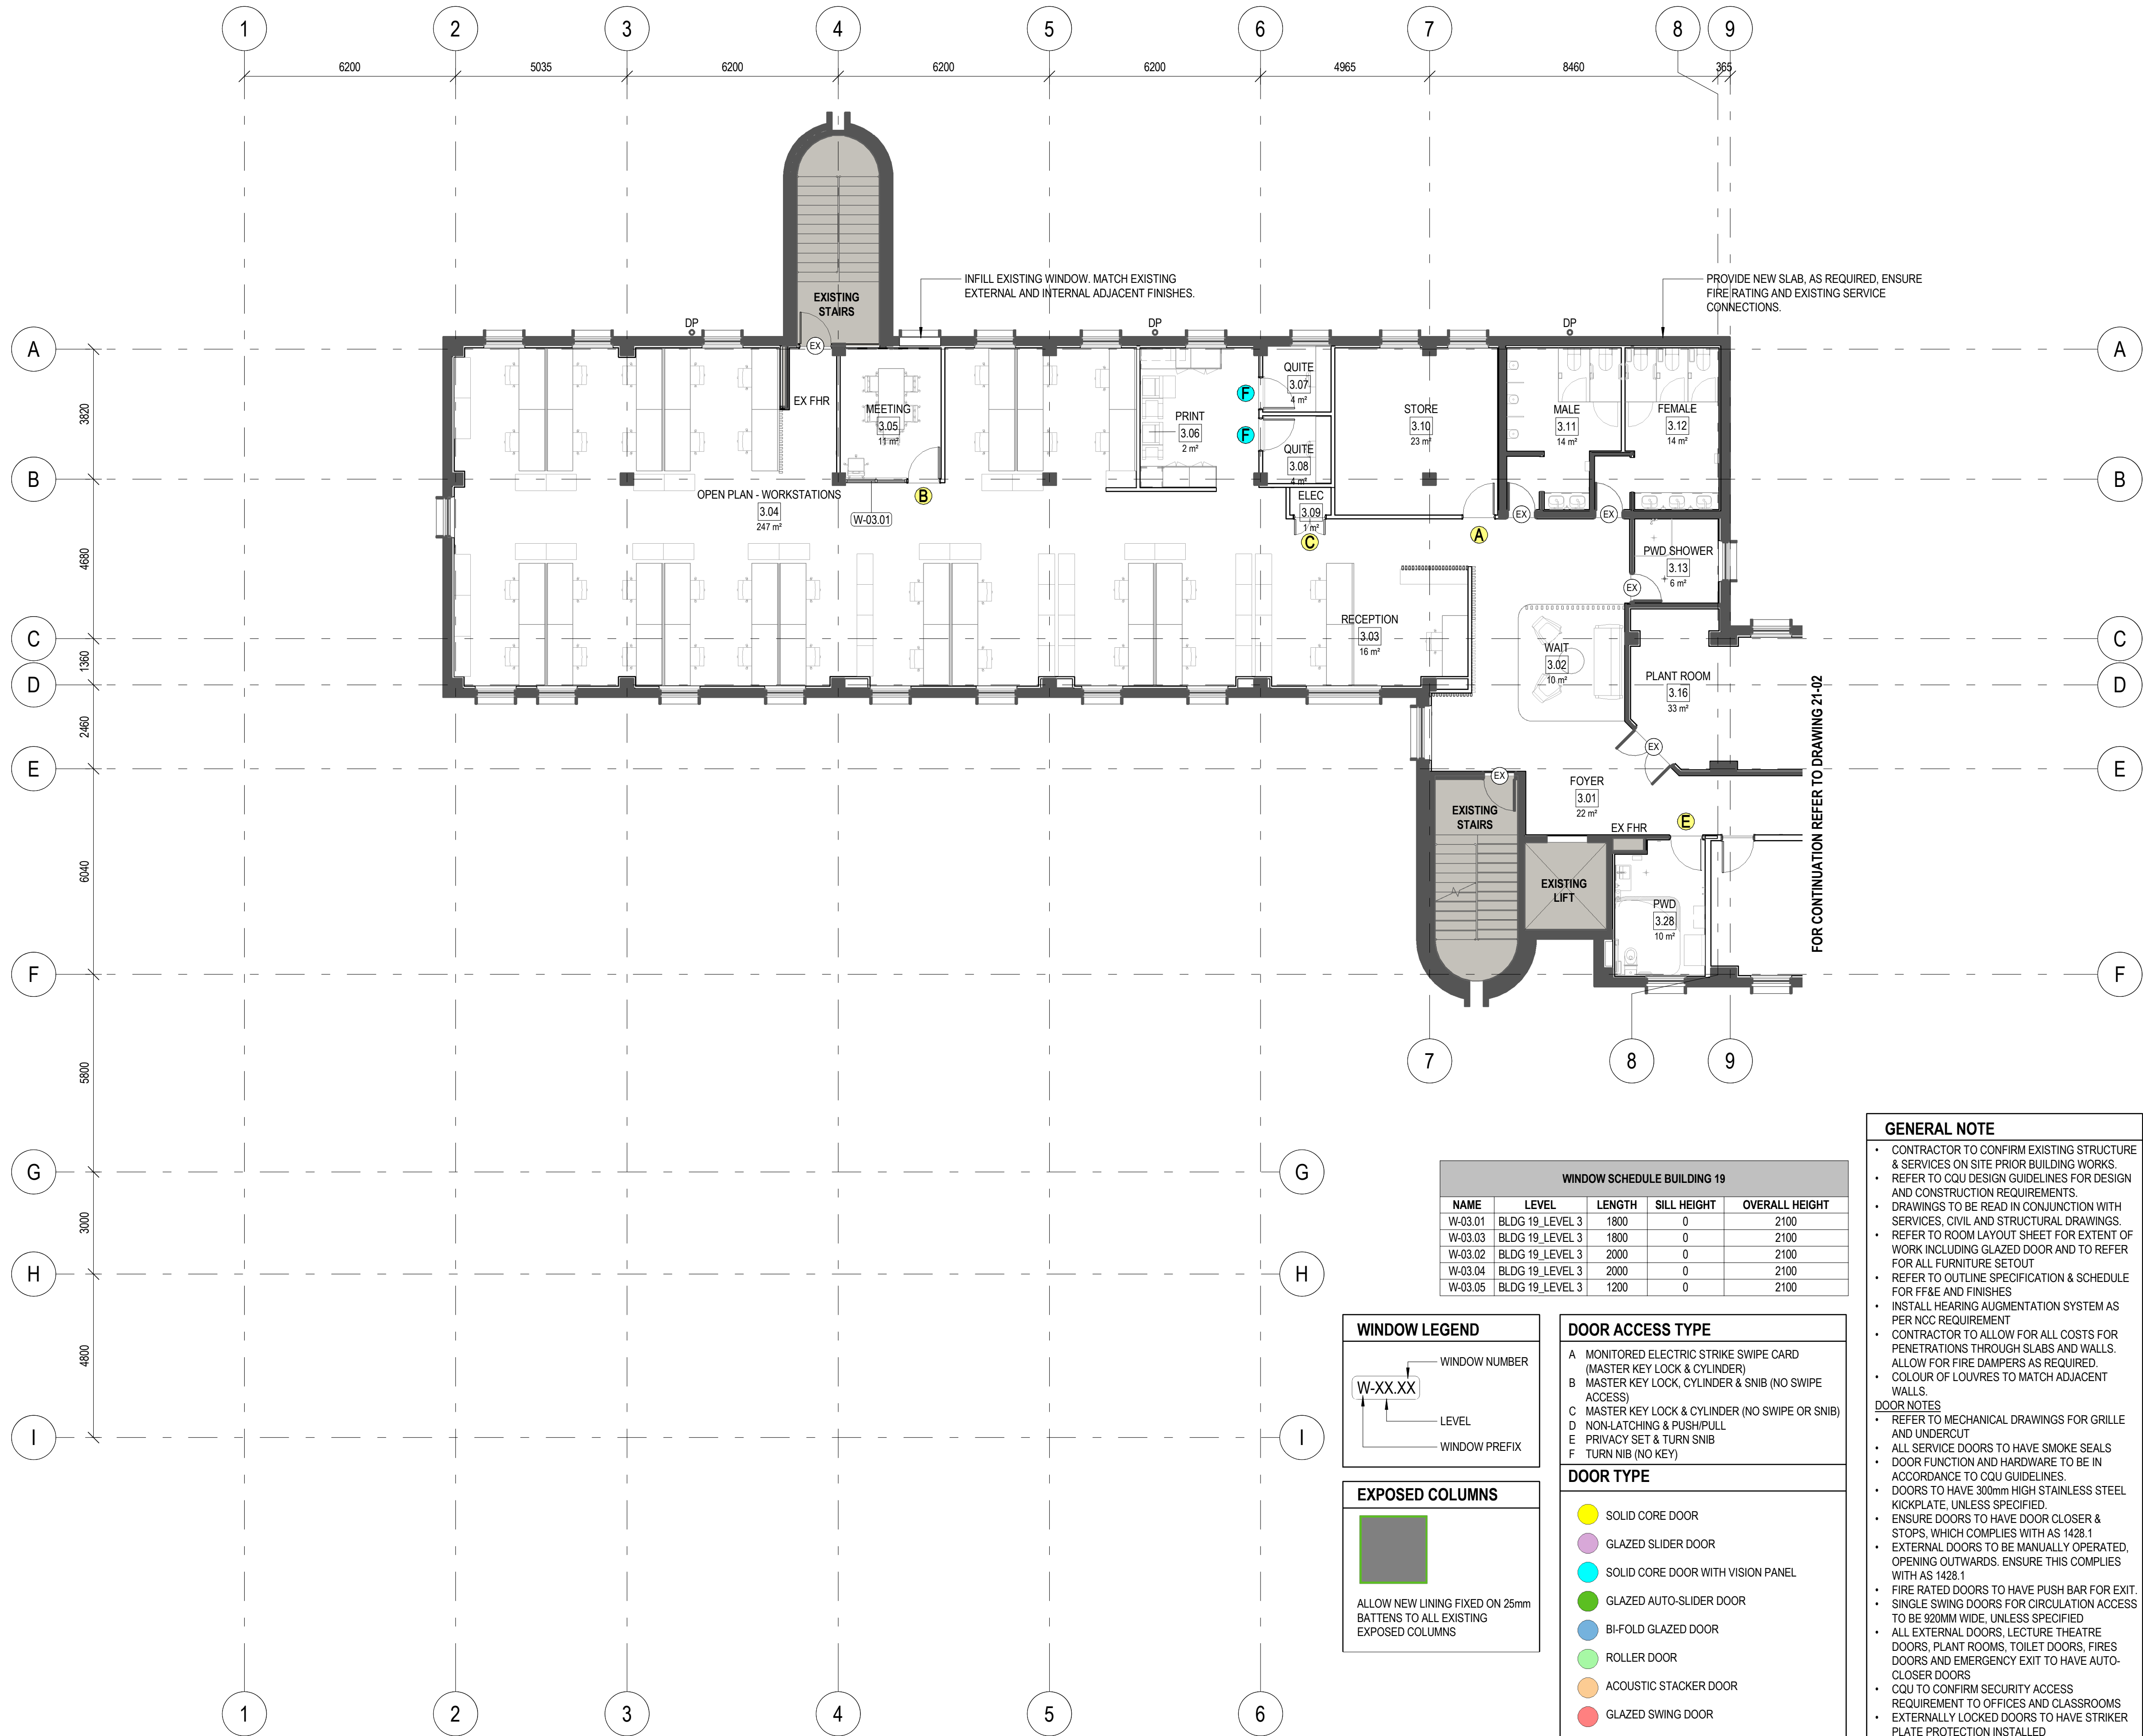

© Copyright
These drawings and designs and the copyright thereof are the property of Thomson Adsett Pty Ltd and must not be used, retained or copied without written permission of Thomson Adsett Pty Ltd. ABN 76 105 314 654 Trading as ThomsonAdsett. Dimensions take precedence over scaling. Do not measure off drawings as print sizes may vary


CQU ROCKHAMPTON TAFE CONSOLIDATION - STAGE 2

554/700 Yaamba Rd, Norman
Gardens QLD 4701



B	2026-03-05	ISSUED FOR TENDER	BC
A	2026-02-12	ISSUED FOR TENDER	BC
6	2026-01-30	60% DRAFT ISSUE	BC
5	2026-01-23	CONSULTANT ISSUES	BC
4	2025-12-19	UPDATED ISSUE	BC
3	2025-12-16	UPDATED ISSUE	BC
2	2025-12-15	CONSULTANTS REVIEW	BC
1	2025-11-24	50% COSTING ISSUE	PT
rev	date	details	init.

drawn	date
JS	19/01/2026
checked	date
SS	12/02/2026
verified	date

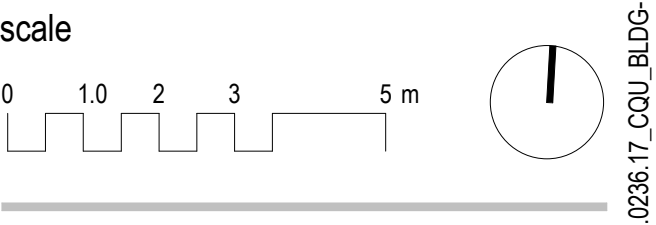

FLOOR PLAN - LEVEL 3 - PART 1 PROPOSED

scale 1 : 100 @ A1 project no. 25.0236.17

revision B sheet no. CQU-ROK-019-03-ARC-21-01

ISSUED FOR TENDER



CQU ROCKHAMPTON TAFE CONSOLIDATION - STAGE 2


554/700 Yaamba Rd, Norman
Gardens QLD 4701



for

B	2026-03-05	ISSUED FOR TENDER	BC
A	2026-02-12	ISSUED FOR TENDER	BC
6	2026-01-30	60% DRAFT ISSUE	BC
5	2026-01-23	CONSULTANT ISSUES	BC
4	2025-12-19	UPDATED ISSUE	BC
3	2025-12-16	UPDATED ISSUE	BC
2	2025-12-15	CONSULTANTS REVIEW	BC
1	2025-11-24	50% COSTING ISSUE	PT
rev	date	details	init.


drawn	date
JS	19/01/2026
checked	date
SS	12/02/2026
verified	date

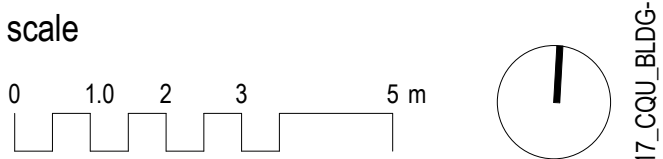

FLOOR PLAN - LEVEL 3 - PART 2 PROPOSED

scale project no.
1 : 100 @ A1 25.0236.17

revision
B
sheet no.
CQU-ROK-019-03-ARC-21-02

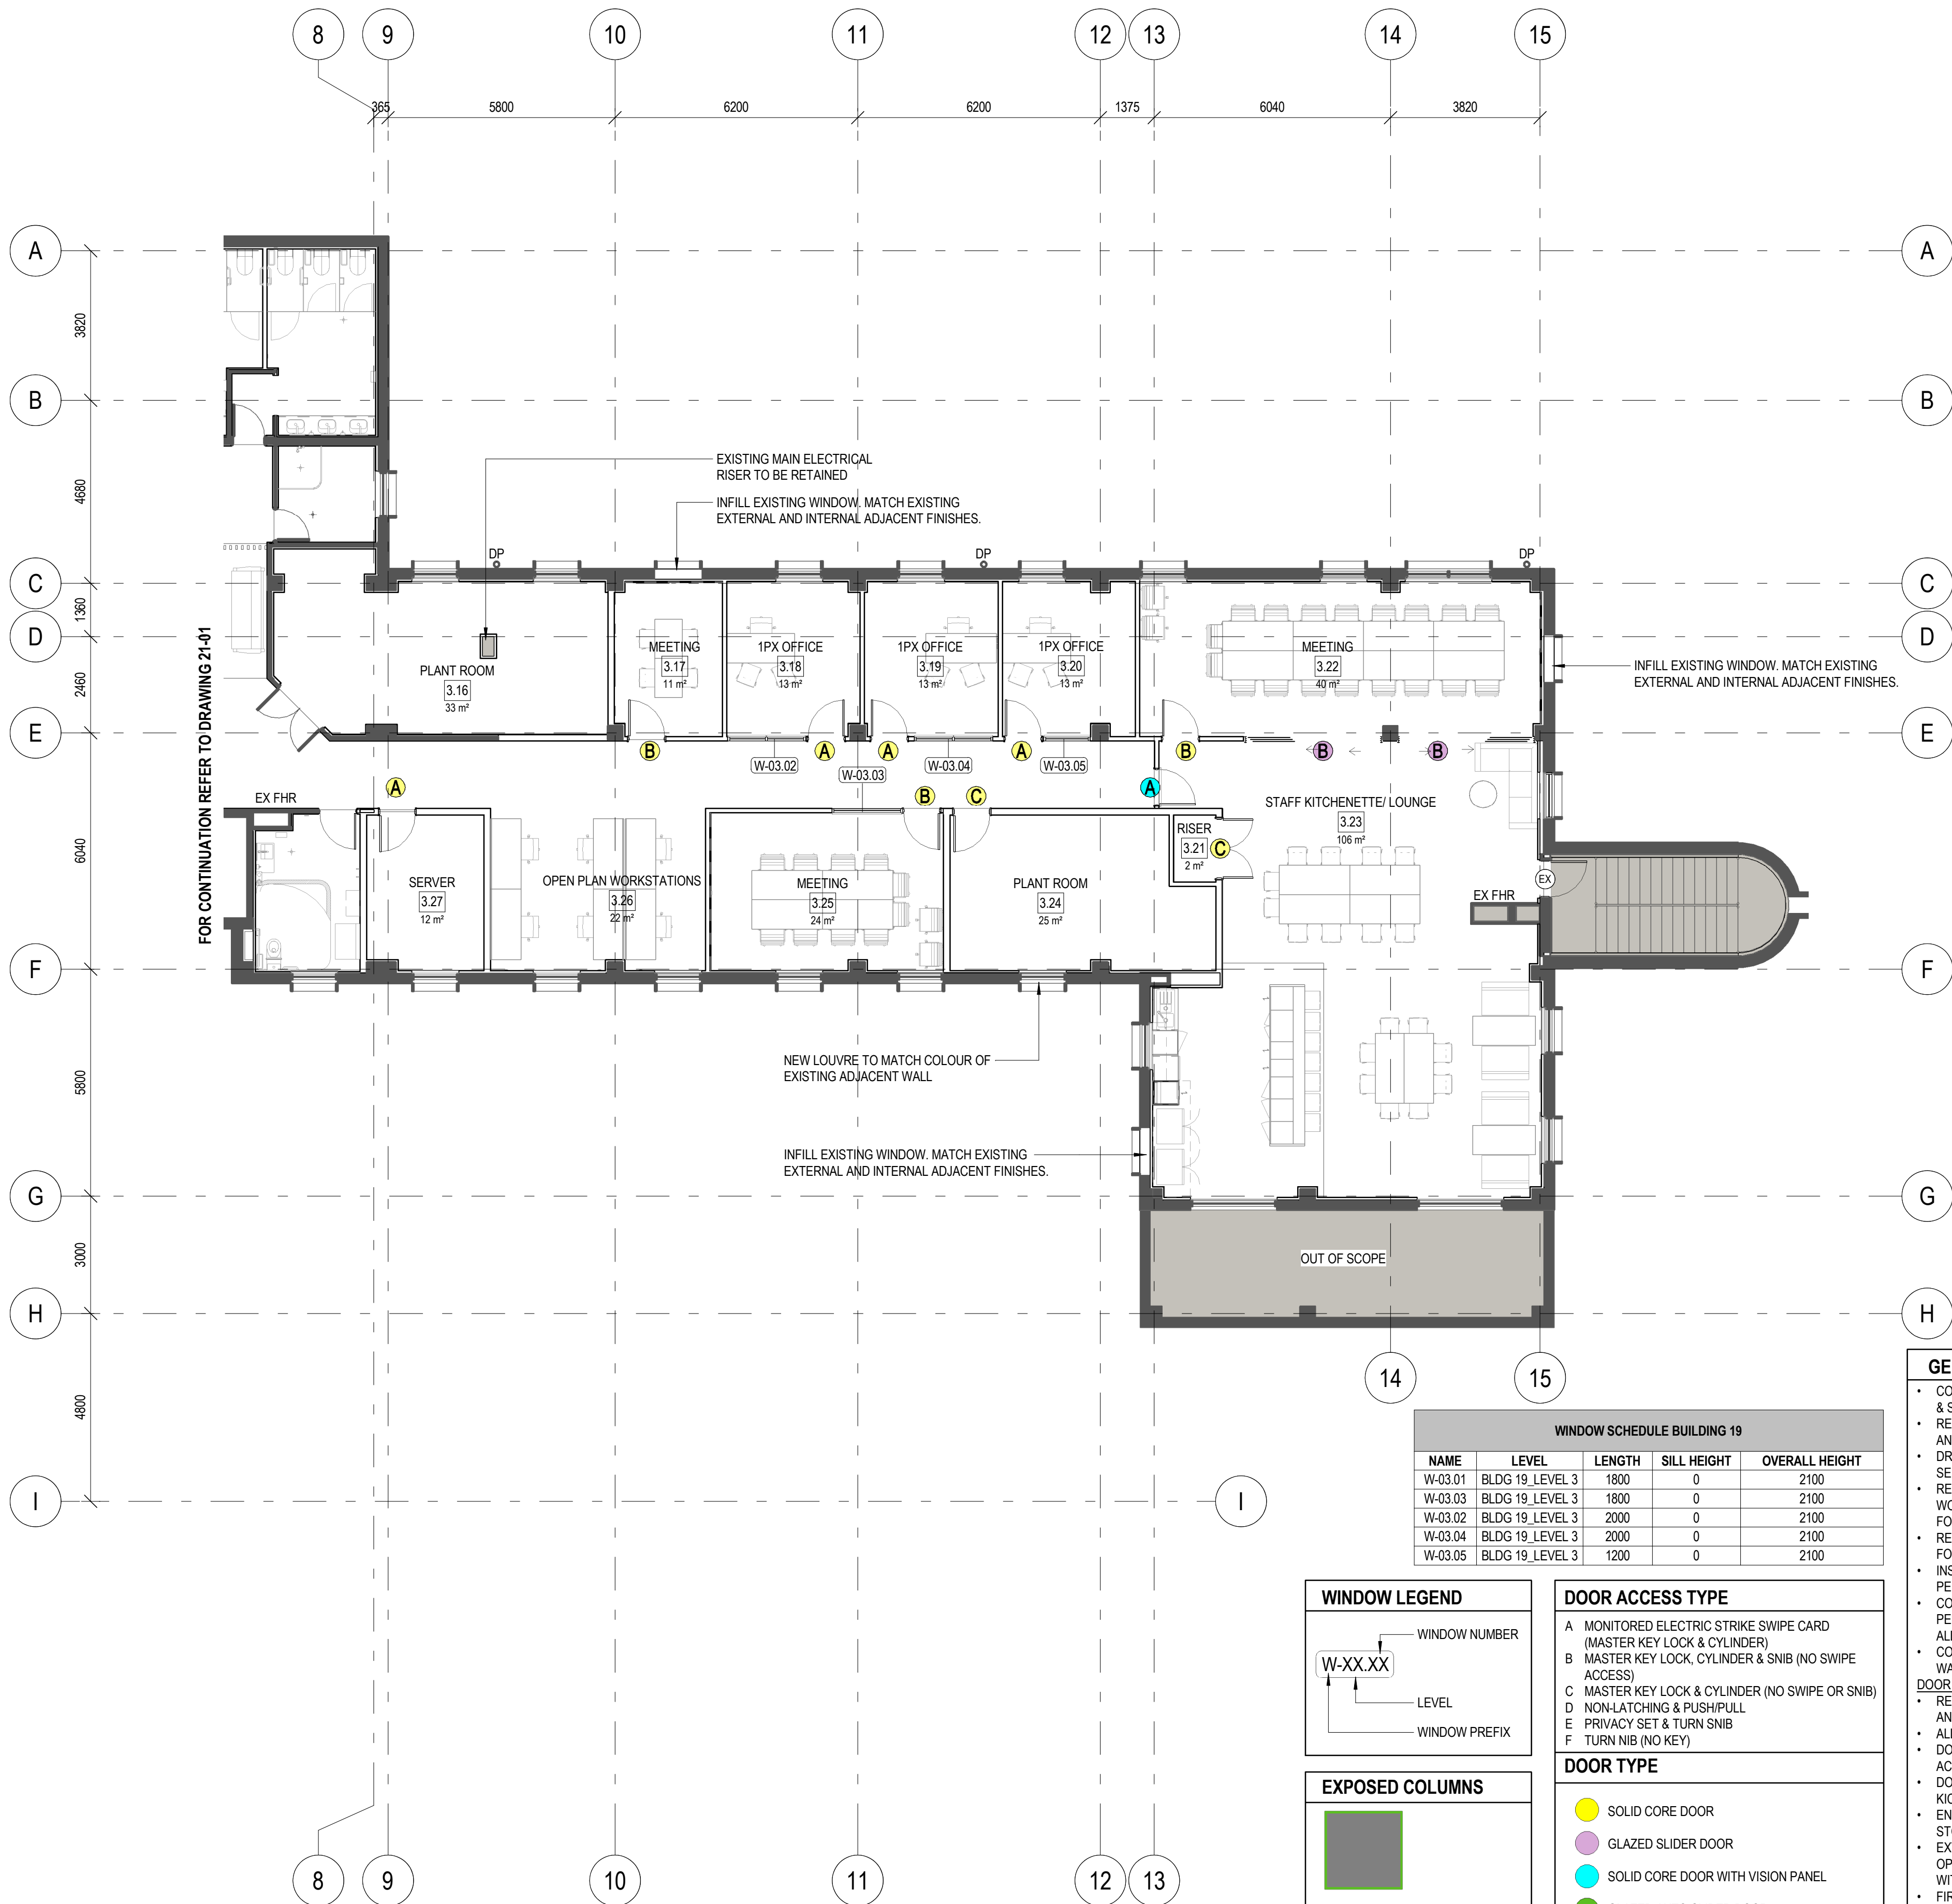

WINDOW SCHEDULE BUILDING 19				
NAME	LEVEL	LENGTH	SILL HEIGHT	OVERALL HEIGHT
W-03.01	BLDG 19 LEVEL 3	1800	0	2100
W-03.03	BLDG 19 LEVEL 3	1800	0	2100
W-03.02	BLDG 19 LEVEL 3	2000	0	2100
W-03.04	BLDG 19 LEVEL 3	2000	0	2100
W-03.05	BLDG 19 LEVEL 3	1200	0	2100

WINDOW LEGEND	
WINDOW NUMBER	
W-XX.XX	
LEVEL	
WINDOW PREFIX	

EXPOSED COLUMNS	
ALLOW NEW LINING FIXED ON 25mm BATTENS TO ALL EXISTING EXPOSED COLUMNS	


DOOR ACCESS TYPE	
A	MONITORED ELECTRIC STRIKE SWIPE CARD (MASTER KEY LOCK & CYLINDER)
B	MASTER KEY LOCK, CYLINDER & SNIB (NO SWIPE ACCESS)
C	MASTER KEY LOCK & CYLINDER (NO SWIPE OR SNIB)
D	NON-LATCHING & PUSH/PULL
E	PRIVACY SET & TURN SNIB
F	TURN NIB (NO KEY)

DOOR TYPE	
	SOLID CORE DOOR
	GLAZED SLIDER DOOR
	SOLID CORE DOOR WITH VISION PANEL
	GLAZED AUTO-SLIDER DOOR
	BI-FOLD GLAZED DOOR
	ROLLER DOOR
	ACOUSTIC STACKER DOOR
	GLAZED SWING DOOR

DOOR ICON LEGEND	
XX	ACCESS TYPE (TYPE MARK)
	DOOR TYPE (COLOUR SHADE)

- GENERAL NOTE**
- CONTRACTOR TO CONFIRM EXISTING STRUCTURE & SERVICES ON SITE PRIOR BUILDING WORKS.
 - REFER TO CQU DESIGN GUIDELINES FOR DESIGN AND CONSTRUCTION REQUIREMENTS.
 - DRAWINGS TO BE READ IN CONJUNCTION WITH SERVICES, CIVIL AND STRUCTURAL DRAWINGS.
 - REFER TO ROOM LAYOUT SHEET FOR EXTENT OF WORK INCLUDING GLAZED DOOR AND TO REFER FOR ALL FURNITURE SETOUT
 - REFER TO OUTLINE SPECIFICATION & SCHEDULE FOR FF&E AND FINISHES
 - INSTALL HEARING AUGMENTATION SYSTEM AS PER NCC REQUIREMENT
 - CONTRACTOR TO ALLOW FOR ALL COSTS FOR PENETRATIONS THROUGH SLABS AND WALLS. ALLOW FOR FIRE DAMPERS AS REQUIRED.
 - COLOUR OF LOUVRES TO MATCH ADJACENT WALLS.
- DOOR NOTES**
- REFER TO MECHANICAL DRAWINGS FOR GRILLE AND UNDERCUT
 - ALL SERVICE DOORS TO HAVE SMOKE SEALS
 - DOOR FUNCTION AND HARDWARE TO BE IN ACCORDANCE TO CQU GUIDELINES.
 - DOORS TO HAVE 300mm HIGH STAINLESS STEEL KICKPLATE, UNLESS SPECIFIED.
 - ENSURE DOORS TO HAVE DOOR CLOSER & STOPS, WHICH COMPLIES WITH AS 1428.1
 - EXTERNAL DOORS TO BE MANUALLY OPERATED, OPENING OUTWARDS. ENSURE THIS COMPLIES WITH AS 1428.1
 - FIRE RATED DOORS TO HAVE PUSH BAR FOR EXIT.
 - SINGLE SWING DOORS FOR CIRCULATION ACCESS TO BE 920MM WIDE, UNLESS SPECIFIED
 - ALL EXTERNAL DOORS, LECTURE THEATRE DOORS, PLANT ROOMS, TOILET DOORS, FIRES DOORS AND EMERGENCY EXIT TO HAVE AUTO-CLOSER DOORS
 - CQU TO CONFIRM SECURITY ACCESS REQUIREMENT TO OFFICES AND CLASSROOMS
 - EXTERNALLY LOCKED DOORS TO HAVE STRIKER PLATE PROTECTION INSTALLED
 - PROVIDE DOOR CLOSERS TO ALL DOORS ENCLOSING AIR-CONDITIONED SPACES
- WINDOW NOTES**
- REFER TO SECTION J REPORT FOR THE REQUIRED GLAZING RATING

ISSUED FOR TENDER

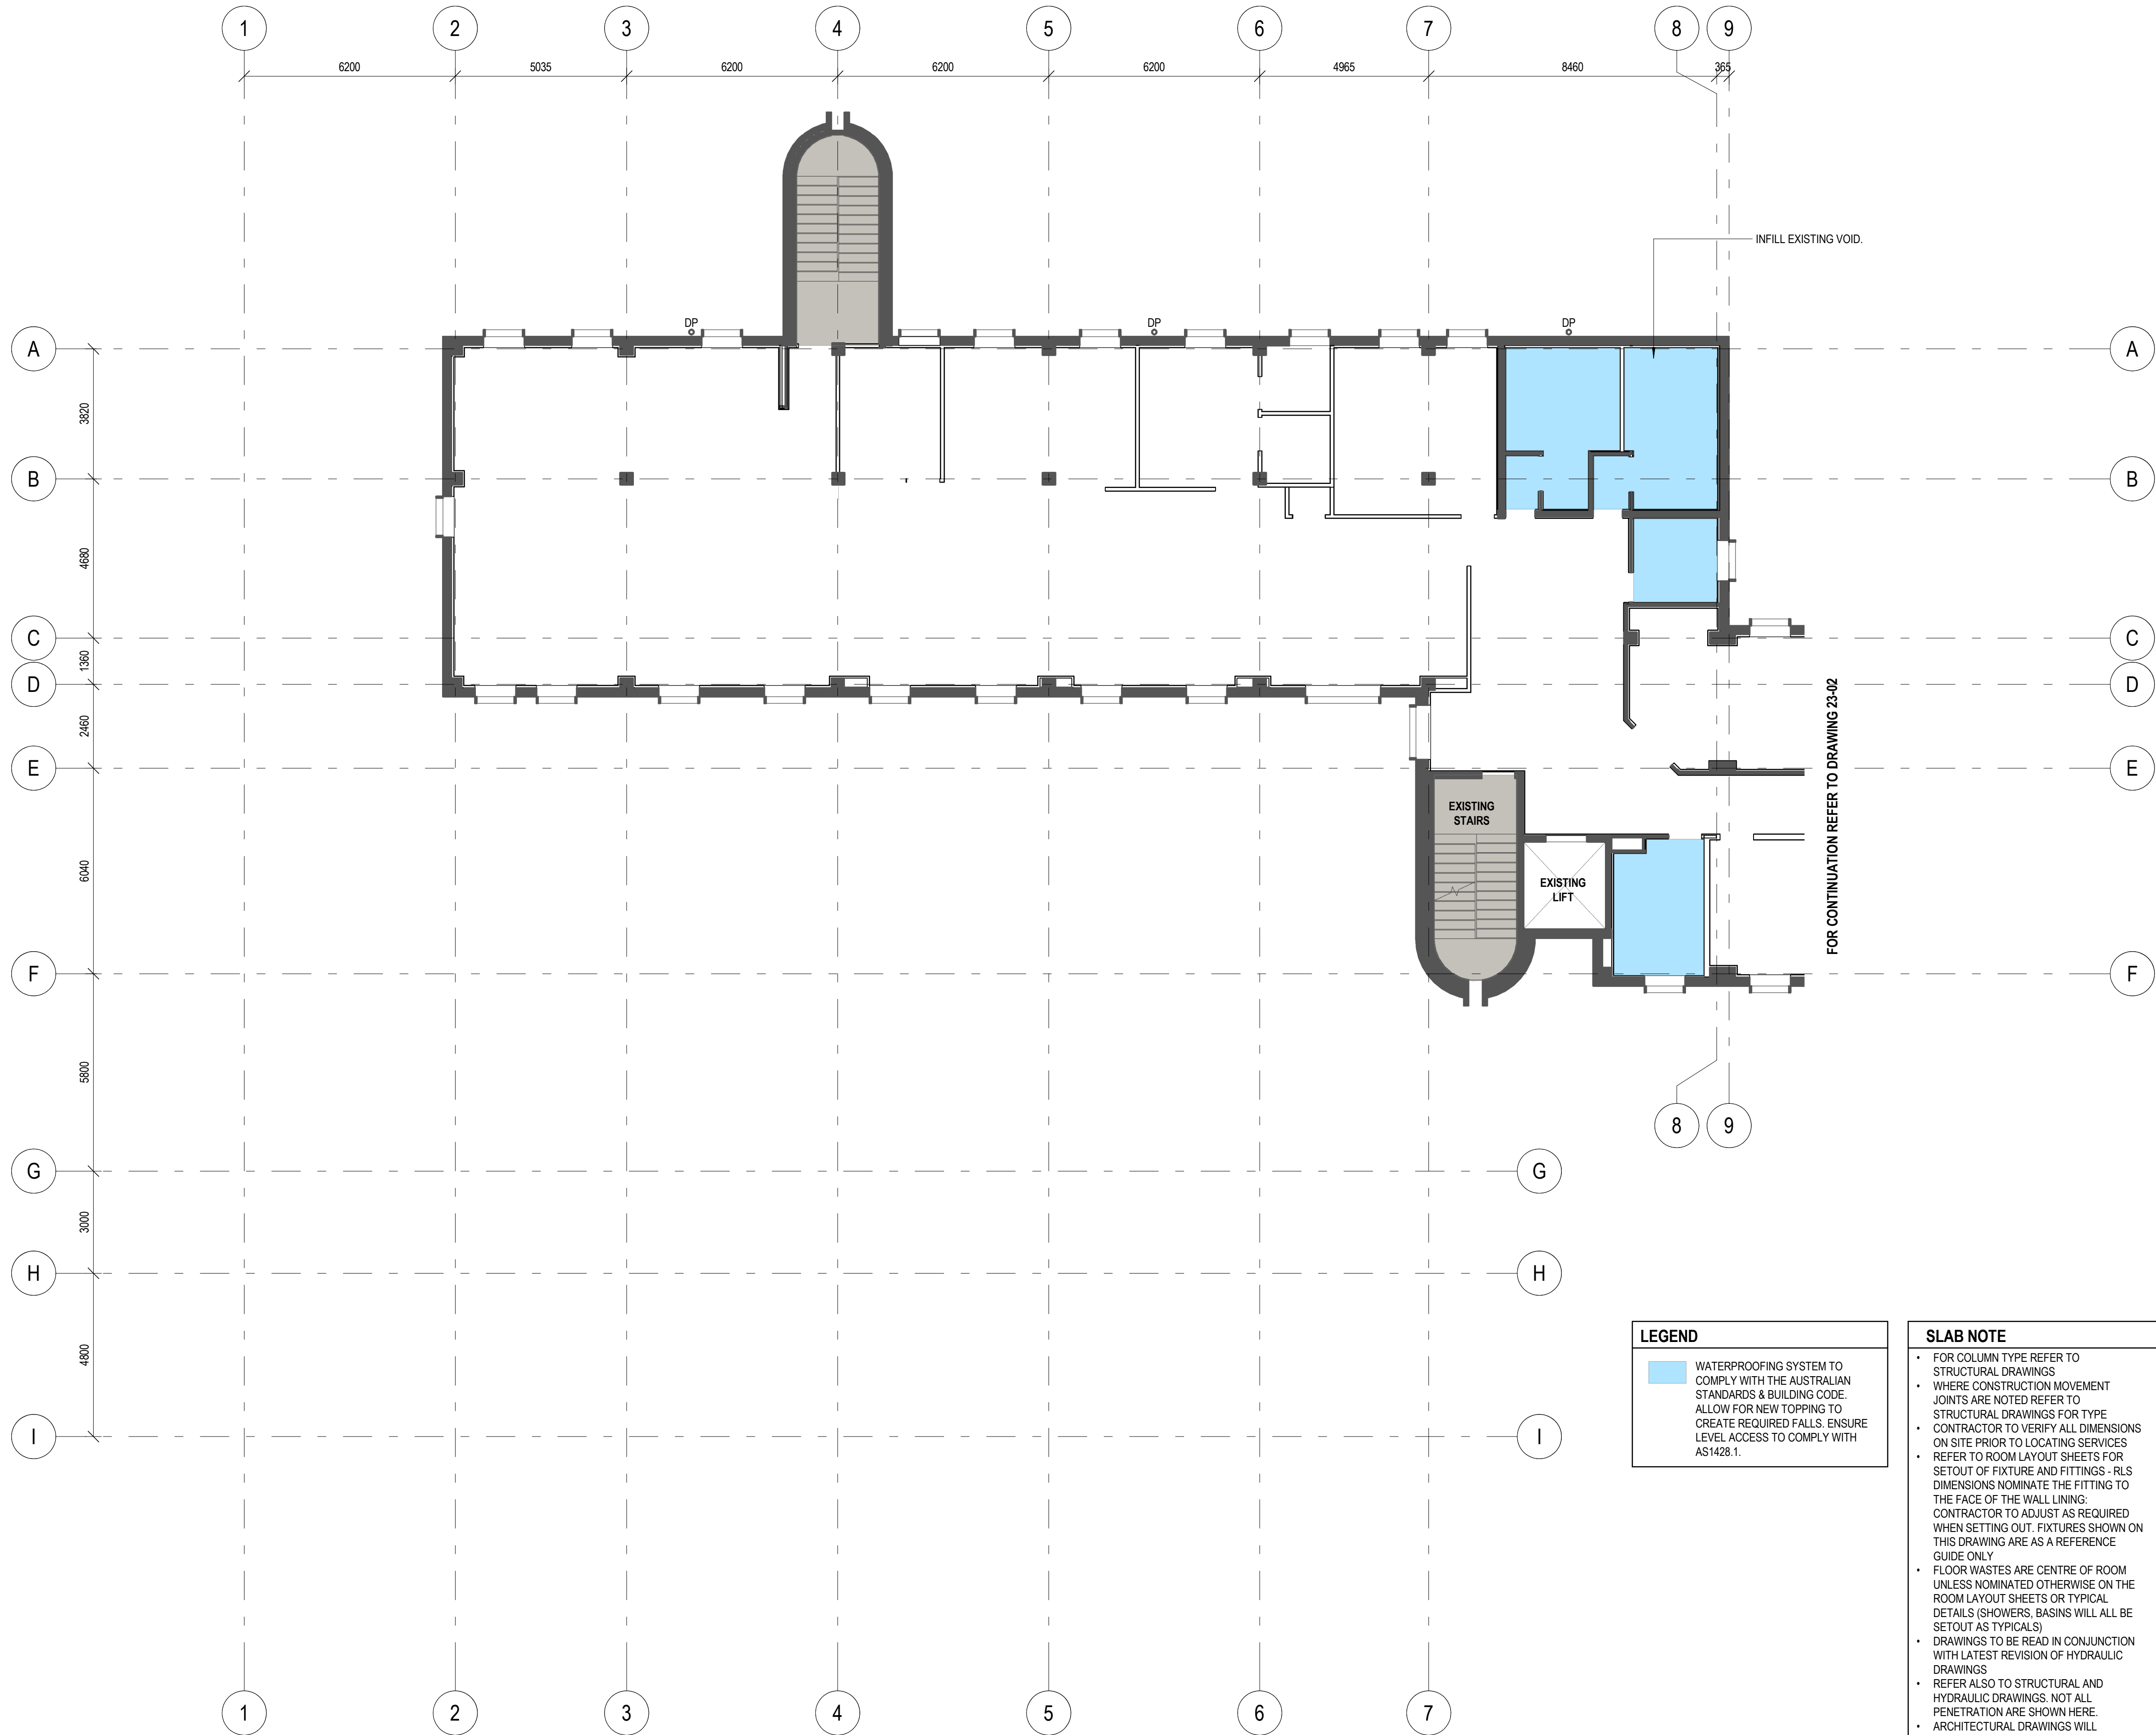

© Copyright
These drawings and designs and the copyright thereof are the property of Thomson Adsett Pty Ltd and must not be used, retained or copied without written permission of Thomson Adsett Pty Ltd. ABN 76 105 314 654 Trading as ThomsonAdsett. Dimensions take precedence over scaling. Do not measure off drawings as print sizes may vary


**CQU ROCKHAMPTON
TAFE
CONSOLIDATION -
STAGE 2**

554/700 Yaamba Rd, Norman
Gardens QLD 4701



B	2026-03-05	ISSUED FOR TENDER	BC
A	2026-02-12	ISSUED FOR TENDER	BC
1	2026-01-30	60% DRAFT ISSUE	BC
rev	date	details	init.

drawn	date
JS	19/01/2026
checked	date
SS	12/02/2026
verified	date

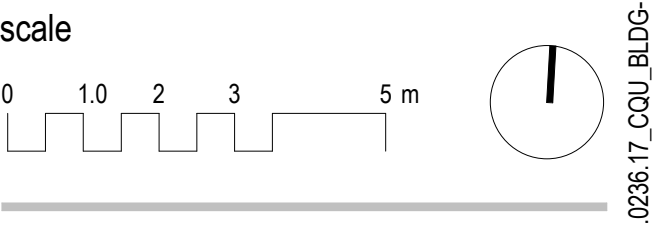

**SLAB PLAN - LEVEL 3 -
PART 1**

scale 1 : 100 @ A1 project no. 25.0236.17

revision B sheet no. CQU-ROK-019-03-ARC-23-01

ISSUED FOR TENDER

**CQU ROCKHAMPTON
TAFE
CONSOLIDATION -
STAGE 2**

554/700 Yaamba Rd, Norman
Gardens QLD 4701


fo



B	2026-03-05	ISSUED FOR TENDER	BC
A	2026-02-12	ISSUED FOR TENDER	BC
1	2026-01-30	60% DRAFT ISSUE	BC
rev	date	details	init

drawn	date
JS	19/01/2026
checked	date
SS	12/02/2026
verified	date

scale

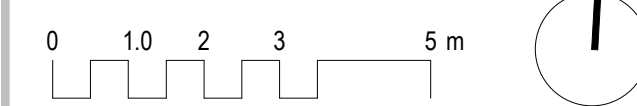

**SLAB PLAN - LEVEL 3 -
PART 2**

scale project no.
1 : 100 @ A1 25.0236.17


revisor

B
sheet no

CQU-ROK-019-03-ARC-23-02

original sheet size - A1 (594mm x 841mm)

ISSUED FOR TENDER

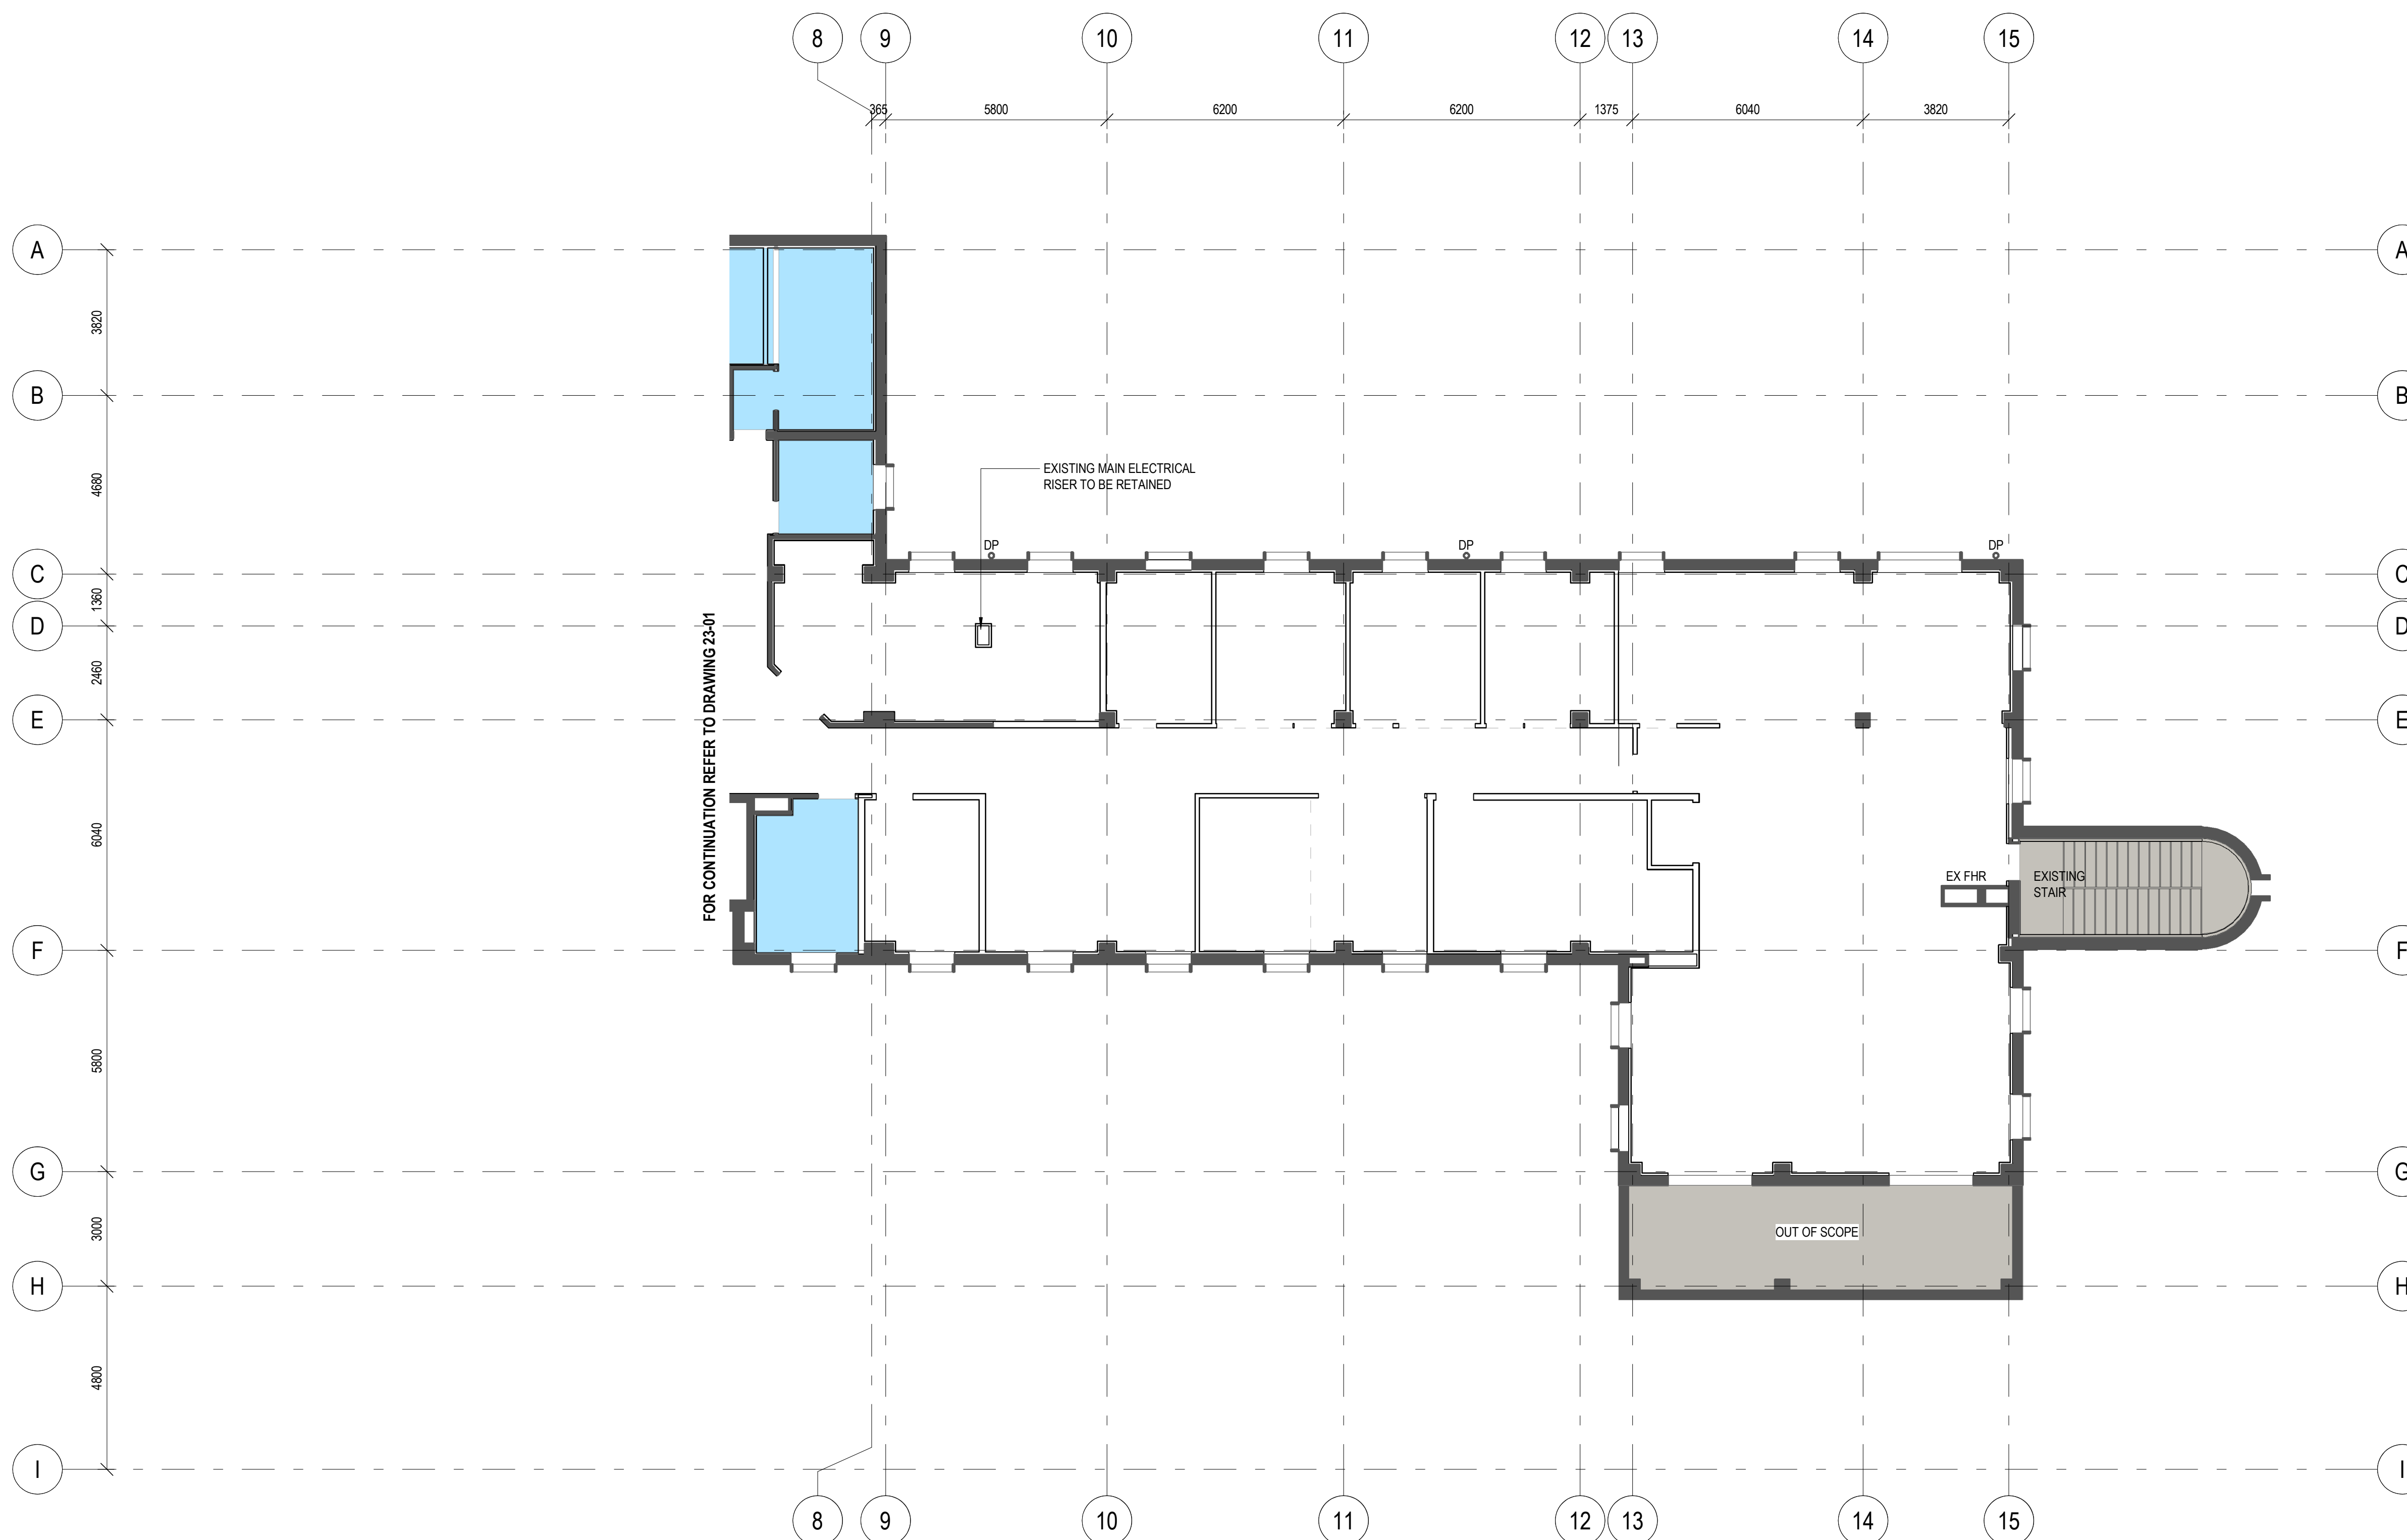

LEGEND

- WATERPROOFING SYSTEM TO COMPLY WITH THE AUSTRALIAN STANDARDS & BUILDING CODE. ALLOW FOR NEW TOPPING TO CREATE REQUIRED FALLS. ENSURE LEVEL ACCESS TO COMPLY WITH AS1428.1.


SLAB NOTE

- FOR COLUMN TYPE REFER TO STRUCTURAL DRAWINGS
- WHERE CONSTRUCTION MOVEMENT JOINTS ARE NOTED REFER TO STRUCTURAL DRAWINGS FOR TYPE
- CONTRACTOR TO VERIFY ALL DIMENSIONS ON SITE PRIOR TO LOCATING SERVICES
- REFER TO ROOM LAYOUT SHEETS FOR SETOUT OF FIXTURE AND FITTINGS - RLS DIMENSIONS NOMINATE THE FITTING TO THE FACE OF THE WALL LINING:
CONTRACTOR TO ADJUST AS REQUIRED WHEN SETTING OUT. FIXTURES SHOWN ON THIS DRAWING ARE AS A REFERENCE GUIDE ONLY
- FLOOR WASTES ARE CENTRE OF ROOM UNLESS NOMINATED OTHERWISE ON THE ROOM LAYOUT SHEETS OR TYPICAL DETAILS (SHOWERS, BASINS WILL ALL BE SETOUT AS TYPICALS)
- DRAWINGS TO BE READ IN CONJUNCTION WITH LATEST REVISION OF HYDRAULIC DRAWINGS
- REFER ALSO TO STRUCTURAL AND HYDRAULIC DRAWINGS NOT ALL PENETRATION ARE SHOWN HERE
- ARCHITECTURAL DRAWINGS WILL NOMINATE FINISH, EXTENT AND HEIGHT OF FLOORING, FOR ALL OTHER INFORMATION E.G. SLAB EDGE AND MATERIAL REFER TO STRUCTURAL ENGINEER DRAWINGS
- CONTRACTOR TO ALLOW FOR WATERPROOFING SYSTEM TO WET AREA, ENSURE IT COMPLIES WITH AUSTRALIAN STANDARD



original sheet size - A1 (594mm x 841mm)

5/03/2026 10:48:22 AM Autodesk Docs://CQU ROK TAFE/25.0236.17_CQU_BLDG-19_2025.nt

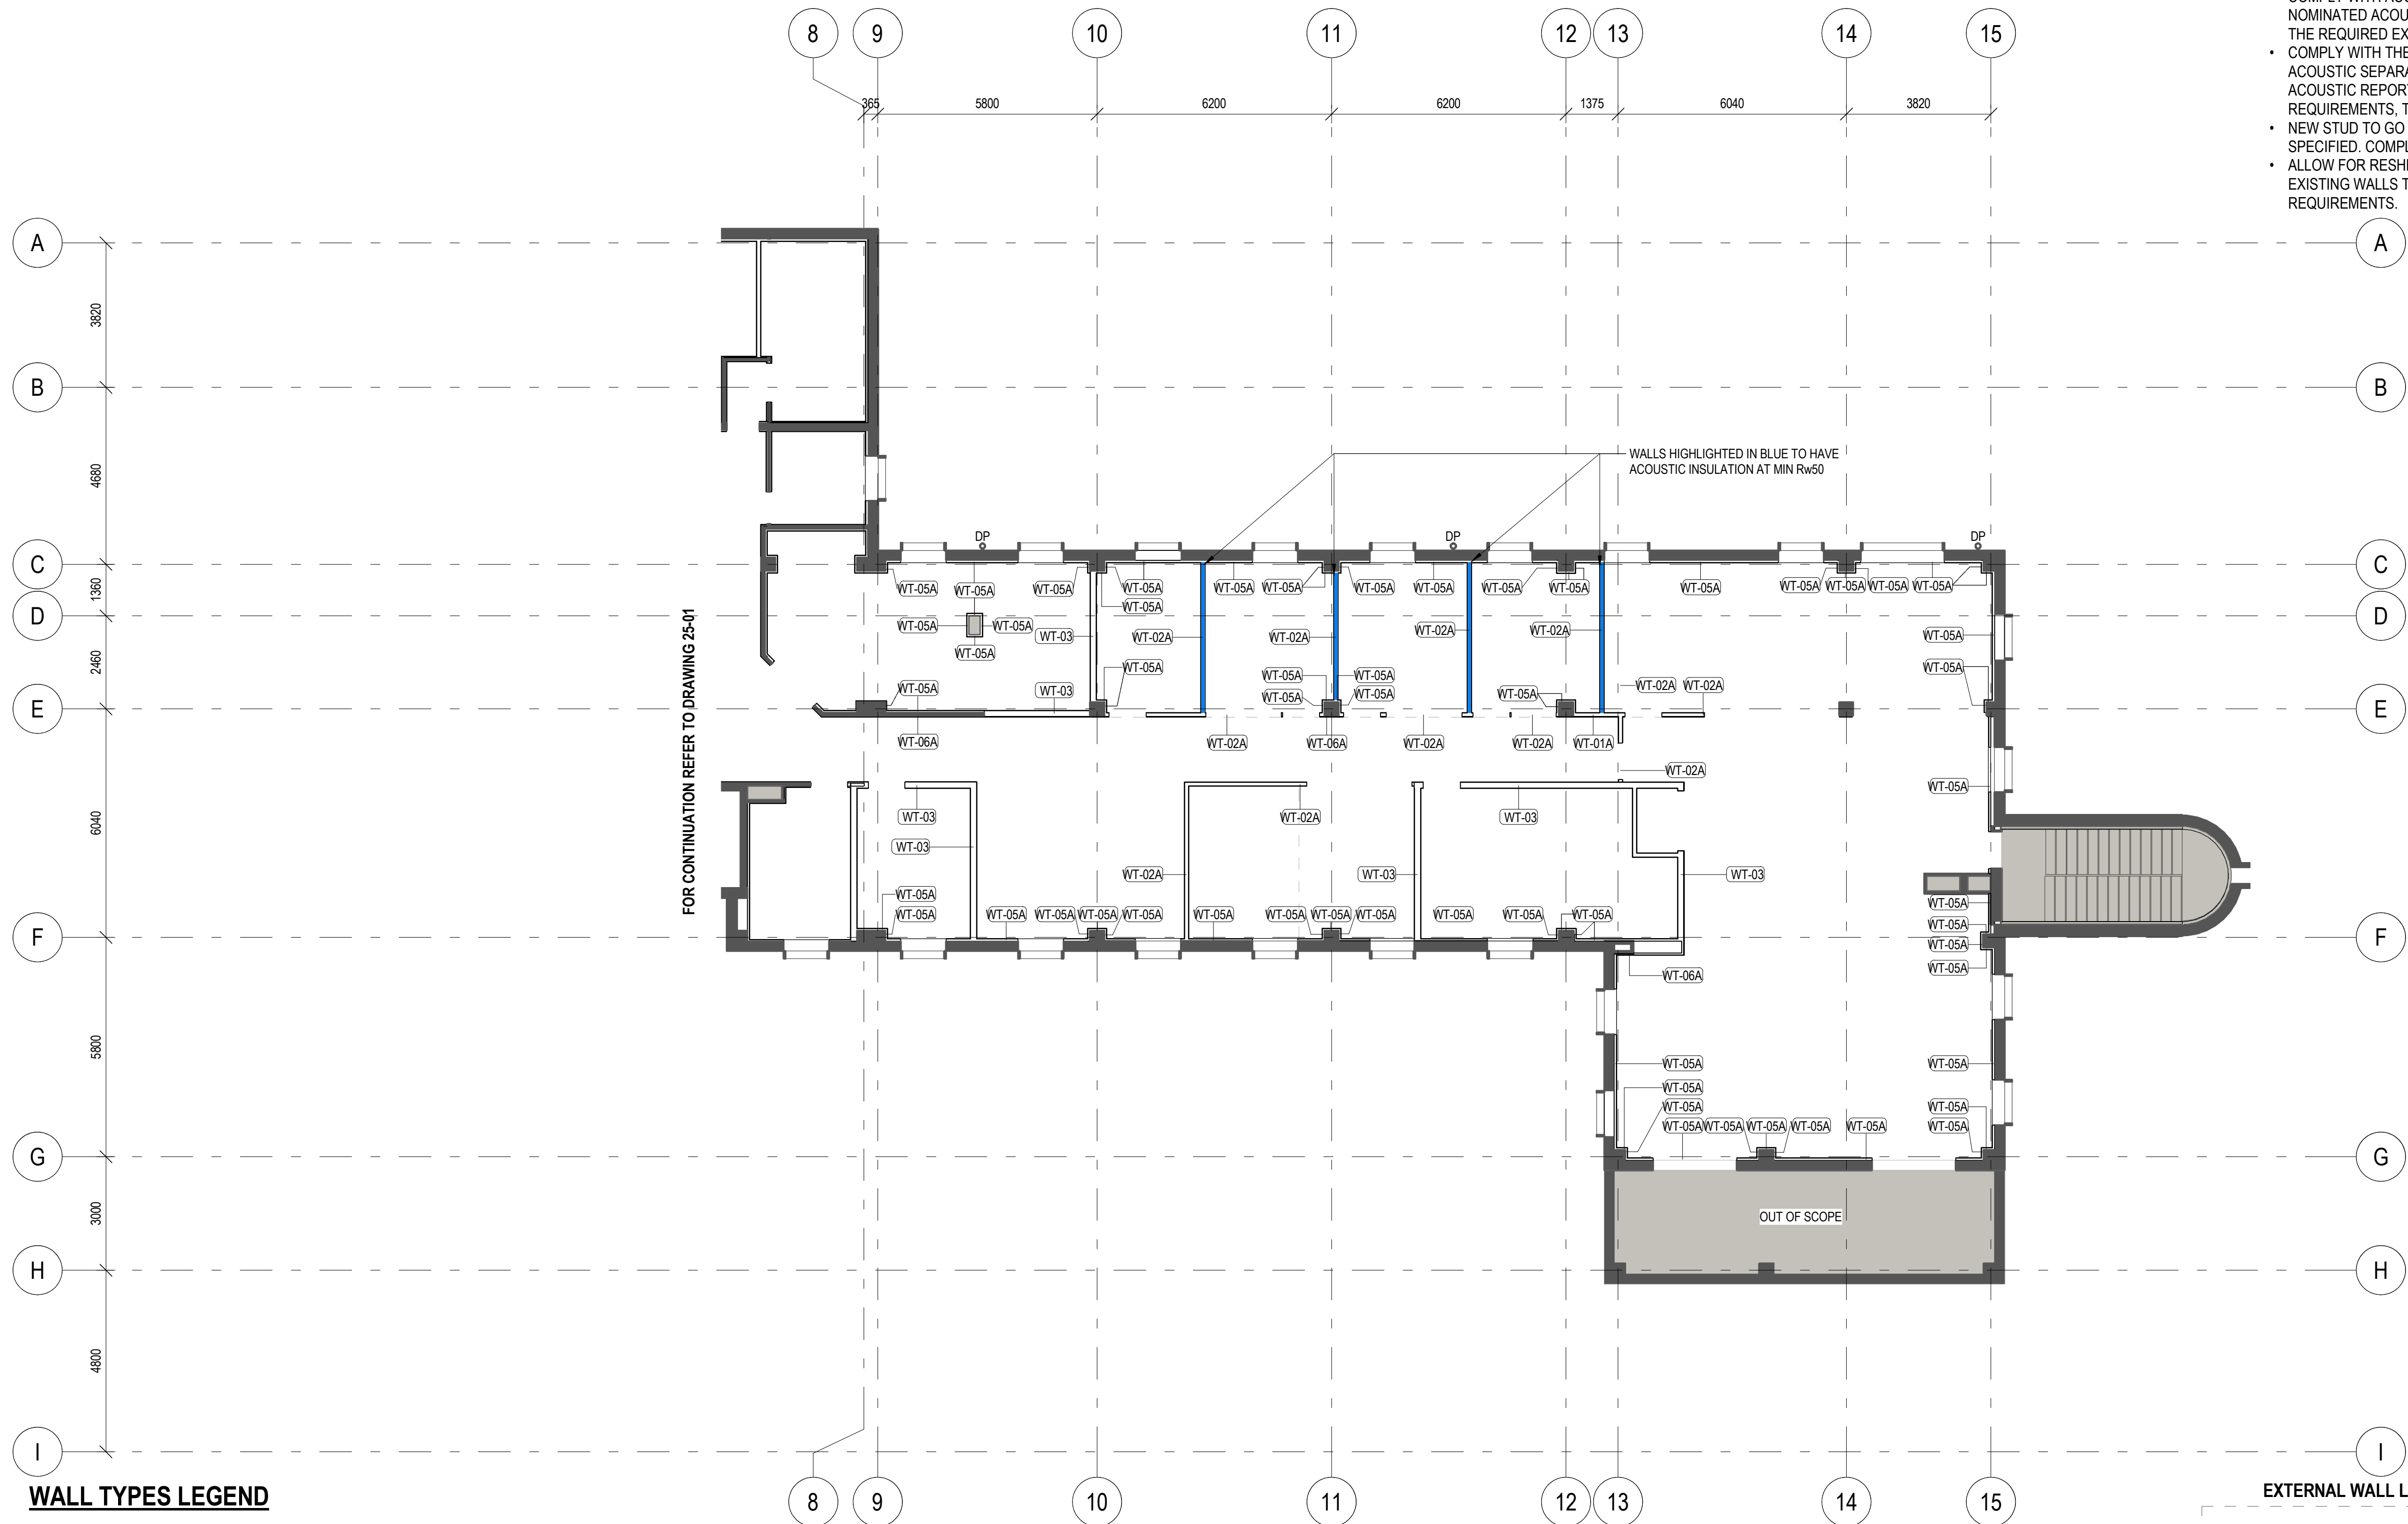

- COMPLY WITH ACOUSTIC REPORT TO ACHIEVE THE NOMINATED ACOUSTIC RATING AND SECTION J REPORT FOR THE REQUIRED EXTERNAL WALLS R VALUES.
- COMPLY WITH THE CQU DESIGN GUIDELINES FOR MINIMUM ACOUSTIC SEPARATION BETWEEN ROOMS. WHERE THE ACOUSTIC REPORT NOMINATES HIGHER PERFORMANCE REQUIREMENTS, THE HIGHER RW RATINGS ARE TO APPLY.
- NEW STUD TO GO UP TO UNDERSIDE OF SLAB, UNLESS SPECIFIED. COMPLY WITH ACOUSTIC REPORT.
- ALLOW FOR RESHEETING OF EXISTING WALLS. ENSURE EXISTING WALLS TO COMPLY WITH ACOUSTIC AND PART J REQUIREMENTS.

© Copyright
These drawings and designs and the copyright thereof are the property of Thomson Adsett Pty Ltd and must not be used, retained or copied without written permission of Thomson Adsett Pty Ltd. ABN 76 105 314 654 Trading as ThomsonAdsett. Dimensions take precedence over scaling. Do not measure off drawings as print sizes may vary

**CQU ROCKHAMPTON
TAFE
CONSOLIDATION -
STAGE 2**


554/700 Yaamba Rd, Norman
Gardens QLD 4701



B	2026-03-05	ISSUED FOR TENDER	BC
A	2026-02-12	ISSUED FOR TENDER	BC
1	2026-01-30	60% DRAFT ISSUE	BC
rev	date	details	init.

drawn JS
checked SS
verified

date 19/01/2026
date 12/02/2026
date

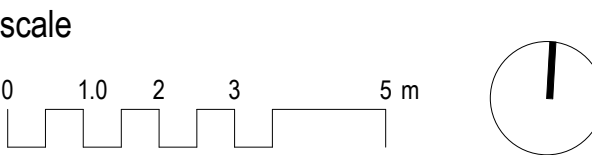


**PARTITION PLAN - LEVEL 3
- PART 2 PROPOSED**

scale As indicated @ A1
project no. 25.0236.17

revision
B
sheet no.
CQU-ROK-019-03-ARC-25-02

ISSUED FOR TENDER

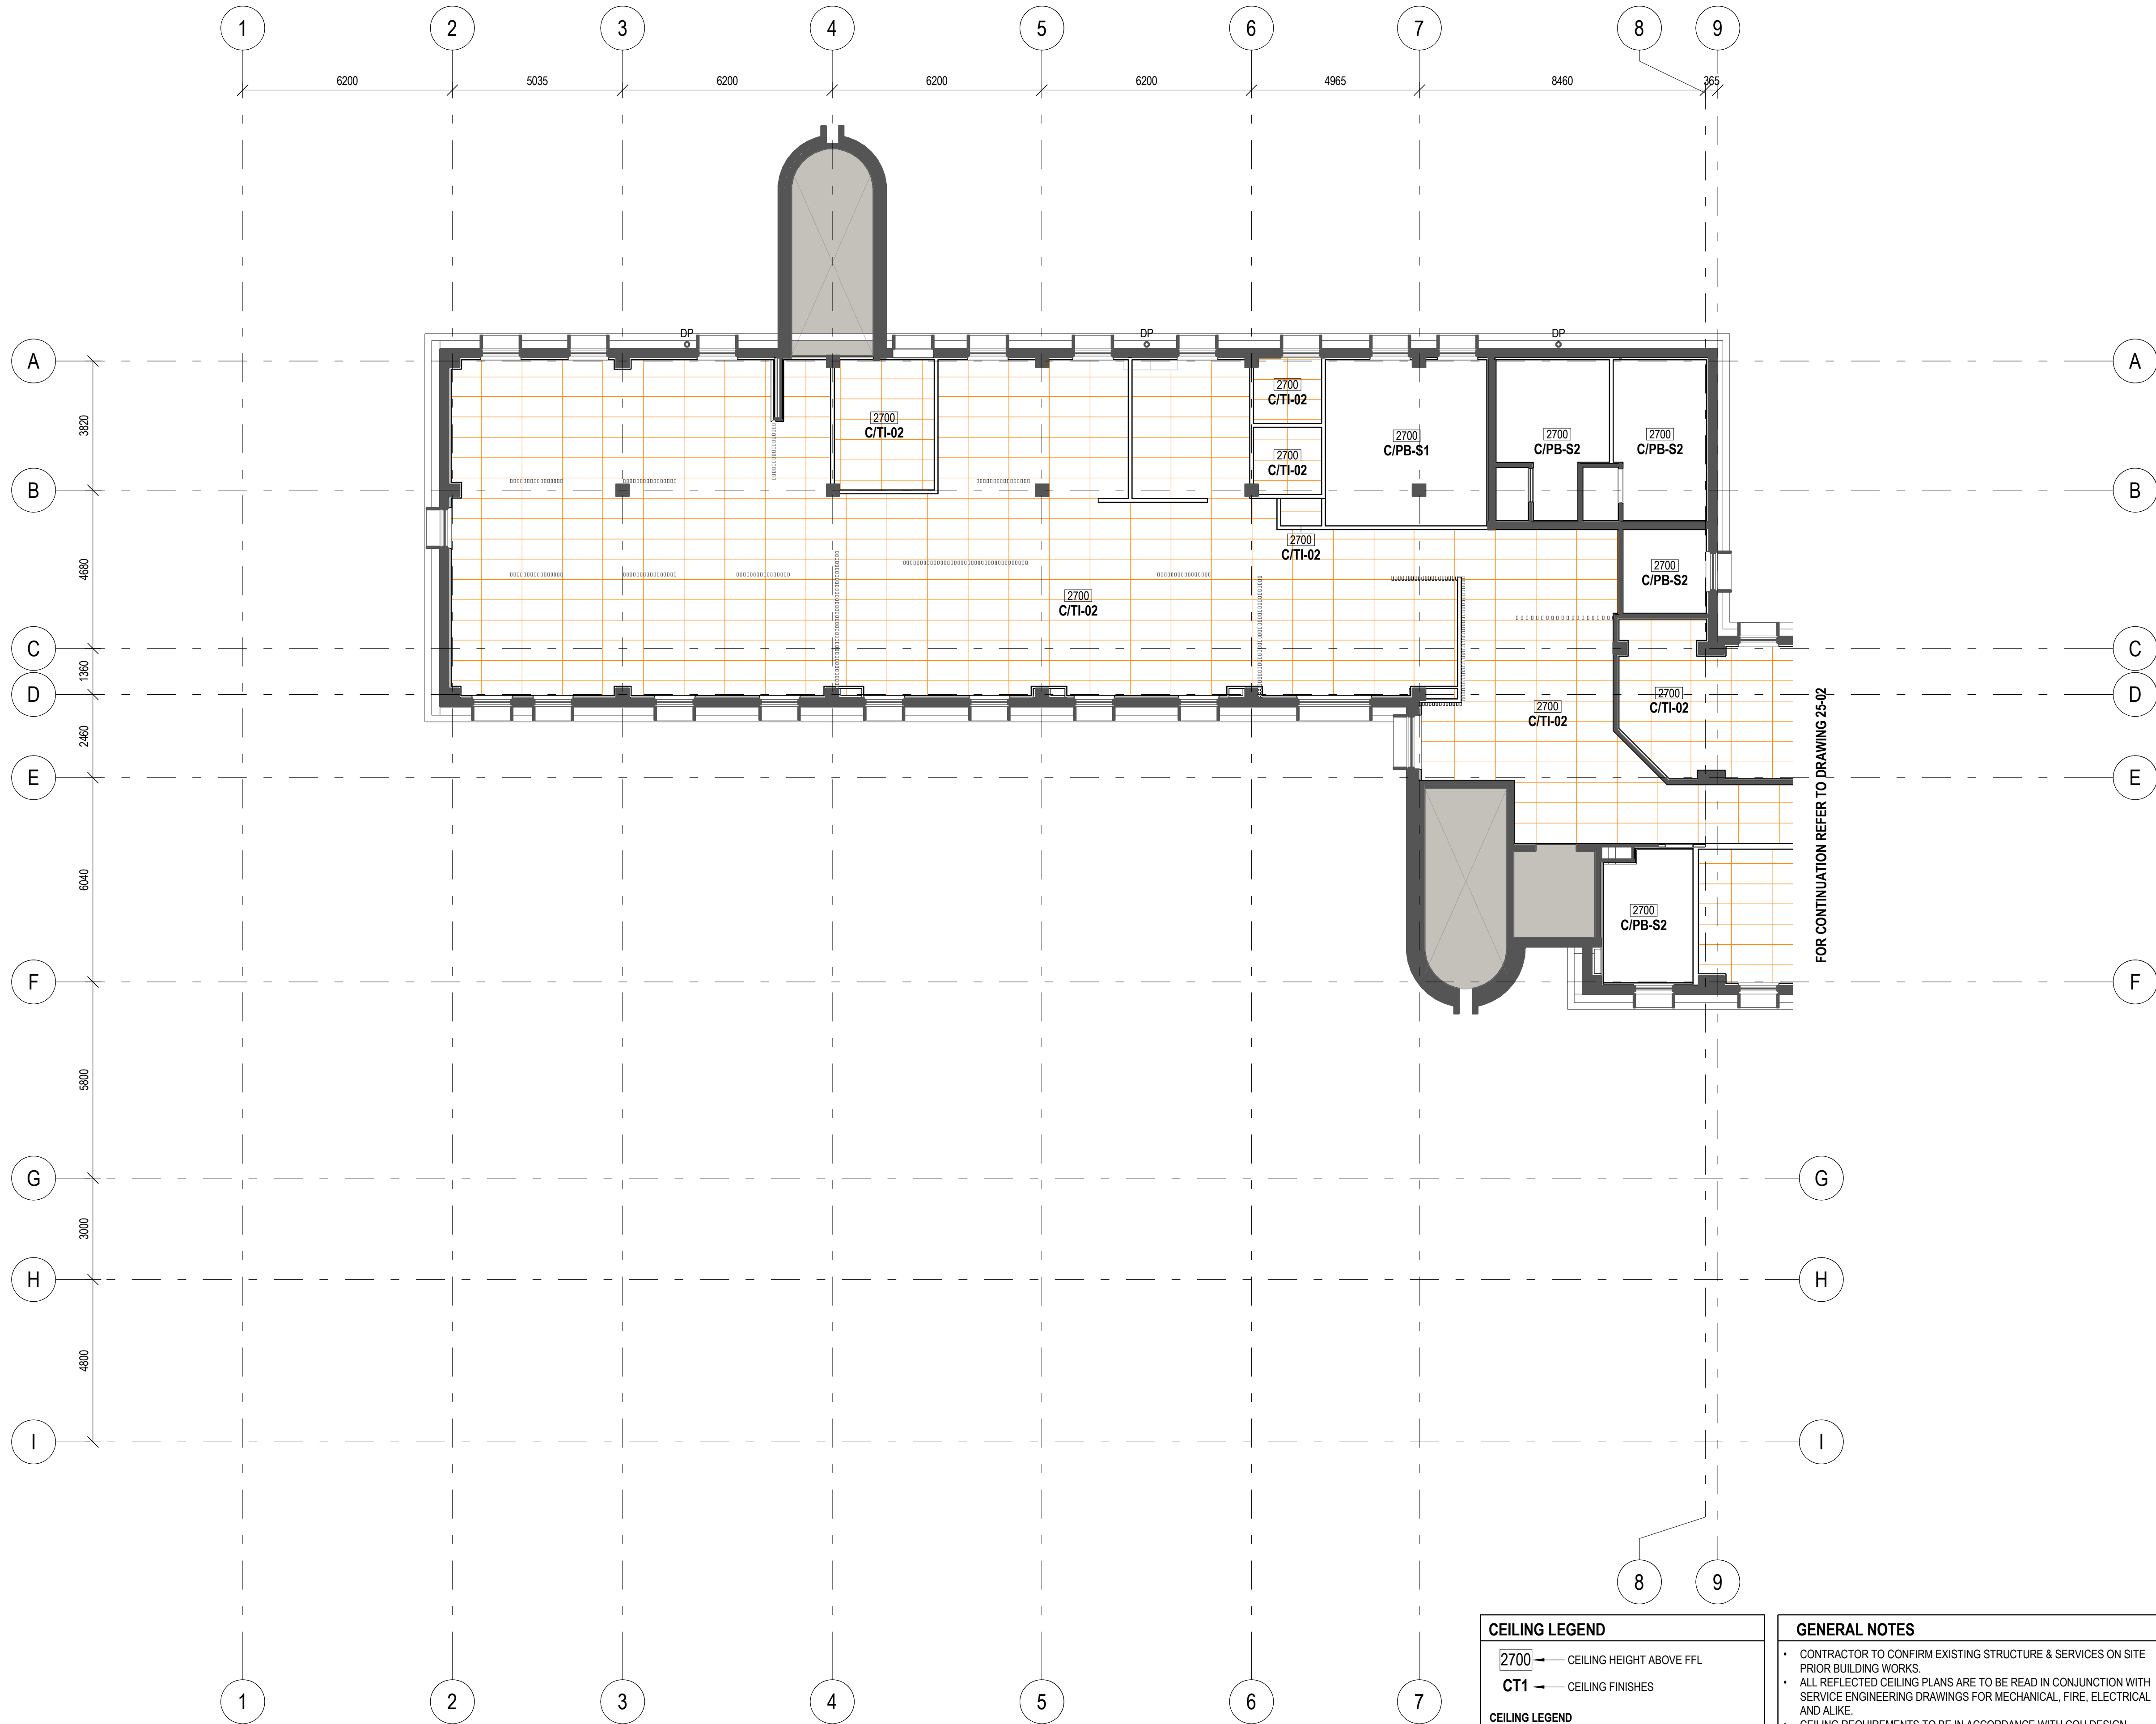

CEILING LEGEND	
[2700]	CEILING HEIGHT ABOVE FFL
CT1	CEILING FINISHES
CEILING LEGEND	
C/TI-01	1200x600 CEILING TILES
C/TI-02	1200x600 ACOUSTIC CEILING TILES
C/PB-S1	FLUSH SET PLASTERBOARD SHEETING
C/PB-S2	WATERPROOF PLASTERBOARD SHEETING
C/FC-01	FLUSH SET FIBRE CEMENT SHEETING

GENERAL NOTES	
• CONTRACTOR TO CONFIRM EXISTING STRUCTURE & SERVICES ON SITE PRIOR BUILDING WORKS.	
• ALL REFLECTED CEILING PLANS ARE TO BE READ IN CONJUNCTION WITH SERVICE ENGINEERING DRAWINGS FOR MECHANICAL, FIRE, ELECTRICAL AND ALIKE.	
• CEILING REQUIREMENTS TO BE IN ACCORDANCE WITH CQU DESIGN GUIDELINES	
• REFER TO OUTLINE SPECIFICATION & SCHEDULE FOR FF&E AND FINISHES	
• SETOUT OF CEILING TILES TO BE CONFIRMED	
• READ IN CONJUNCTION WITH ACOUSTIC AND PART J REPORT. ALLOW ACOUSTIC INSULATION ABOVE AMENITIES.	
• CEILING GRID SET OUT CENTRED TO ROOM.	
• ALLOW FOR ACCESS HATCHES TO PLASTERBOARD CEILINGS. MIN. ONE PER ROOM.	

ISSUED FOR TENDER

CEILING PLAN - LEVEL 3 - PART 1 PROPOSED

scale 1 : 100 @ A1 project no. 25.0236.17

revision B sheet no. CQU-ROK-019-03-ARC-26-01

5/03/2026 10:47:53 AM Autocad Desc:\CQU ROK TAFE25.0236.17_CQU_BLDG-19_2025.rvt

original sheet size - A1 (594mm x 841mm)

thomson
adsett



PEDDLE THORP
architecture | interiors | health | planning

Telephone +61 7 3840 9999
bne@thomsonadsett.com
Level 9, 470 St Pauls Terrace
Fortitude Valley
Qld 4006 Australia
thomsonadsett.com

© Copyright
These drawings and designs and the copyright thereof are the property of Thomson Adsett Pty Ltd and must not be used, retained or copied without written permission of Thomson Adsett Pty Ltd. ABN 76 105 314 654 Trading as ThomsonAdsett. Dimensions take precedence over scaling. Do not measure off drawings as print sizes may vary

CQU ROCKHAMPTON TAFE CONSOLIDATION - STAGE 2

554/700 Yaamba Rd, Norman Gardens QLD 4701

for



CQUniversity
AUSTRALIA


B	2026-03-05	ISSUED FOR TENDER	BC
A	2026-02-12	ISSUED FOR TENDER	BC
6	2026-01-30	60% DRAFT ISSUE	BC
5	2026-01-23	CONSULTANT ISSUES	BC
4	2025-12-19	UPDATED ISSUE	BC
3	2025-12-16	UPDATED ISSUE	BC
2	2025-12-15	CONSULTANTS REVIEW	BC
1	2025-11-24	50% COSTING ISSUE	PT

rev	date	details	init.
-----	------	---------	-------

drawn JS date 19/01/2026

checked SS date 12/02/2026

verified date

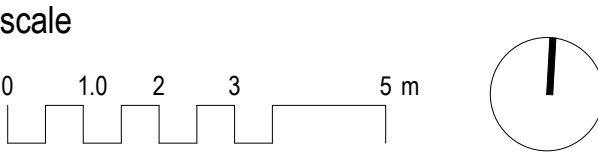

CEILING PLAN - LEVEL 3 - PART 1 PROPOSED

scale 1 : 100 @ A1 project no. 25.0236.17

revision B sheet no. CQU-ROK-019-03-ARC-26-01

5/03/2026 10:47:53 AM Autocad Desc:\CQU ROK TAFE25.0236.17_CQU_BLDG-19_2025.rvt

original sheet size - A1 (594mm x 841mm)

CQU ROCKHAMPTON TAFE CONSOLIDATION - STAGE 2

554/700 Yaamba Rd, Norman
Gardens QLD 4701


for



A	12/02/26	ISSUED FOR TENDER	SM
1	30/01/26	60% DRAFT ISSUE	SM

rev	date	details	init.
-----	------	---------	-------

drawn	date
TA/PT	27/01/26
checked	date
SZ	27/01/26
verified	date
	27/01/26

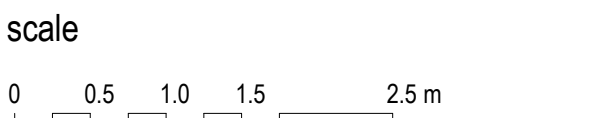

FLOOR & WALL FINISHES PLAN LEVEL 03

scale	project no.
1 : 100 @ A1	260018
revision	
A	
sheet no.	
CQU-ROK-019-03-ARC-28-01	



GENERAL NOTES:

- THIS DRAWING IS TO BE READ IN CONJUNCTION WITH ALL PROJECT DRAWINGS, SCHEDULES AND SPECIFICATIONS, PLUS ALL OTHER RELEVANT CONSULTANT DOCUMENTS.
- ALL WORKS TO COMPLY WITH BCA AND AUSTRALIAN STANDARDS.
- ANY DISCREPANCIES ON THE DRAWINGS OR IRREGULARITIES BETWEEN INFORMATION SHOWN ON INTERIOR DRAWINGS AND SERVICES CONSULTANTS DOCUMENTS ARE TO BE REFERRED TO THE DESIGNER FOR CLARIFICATION PRIOR TO THE WORKS PROCEEDING.
- ALL DIMENSIONS AND AREAS PROVIDED TO BE CONFIRMED ON SITE PRIOR TO COMMENCEMENT OF WORKS


FINISHES NOTES:

- ALL JUNCTIONS IN FLOOR FINISHES TO BE FLUSH.
- CHANGES TO FLOOR FINISH TO OCCUR UNDER THE CENTRE LINE OF THE DOOR LEAF UNLESS NOTED OTHERWISE.
- ALL WALLS TO BE PA01 UNLESS OTHERWISE NOTED.
- ALL SOLID CORE DOORS TO BE PA11 UNLESS OTHERWISE NOTED.
- REFER 60 SERIES DRAWINGS & SCH-INT-01 INTERIOR FINISHES SCHEDULE FOR SKIRTING TYPES AND SPECIFICATION. ALL WALLS TO RECEIVE SK01 SKIRTING UNLESS NOTED OTHERWISE.
- NEW SKIRTING TO MATCH EXISTING WHERE RELEVANT.
- ALL DOOR STATUTORY SIGNAGE AND ROOM SIGNAGE TO BE REMOVED BEFORE PAINTING.
- ALL WINDOW FURNISHING TO BE REMOVED BEFORE PAINTING, CLEANED AND REINSTALLED.
- FLOOR FINISHES TO CONTINUE UNDER NEW JOINERY.

FINISHES LEGEND

REFER SCH-INT-01 FINISHES SCHEDULE AND 60 SERIES DRAWINGS FOR FURTHER DETAILS AND SPECIFICATION

PA##	FEATURE WALL PAINT
TL##	WALL TILE
WF##	WALL FINISH
CA##	CARPET FLOOR FINISH
RF##	RESILIENT FLOOR FINISH
TL##	TILE FLOOR FINISH

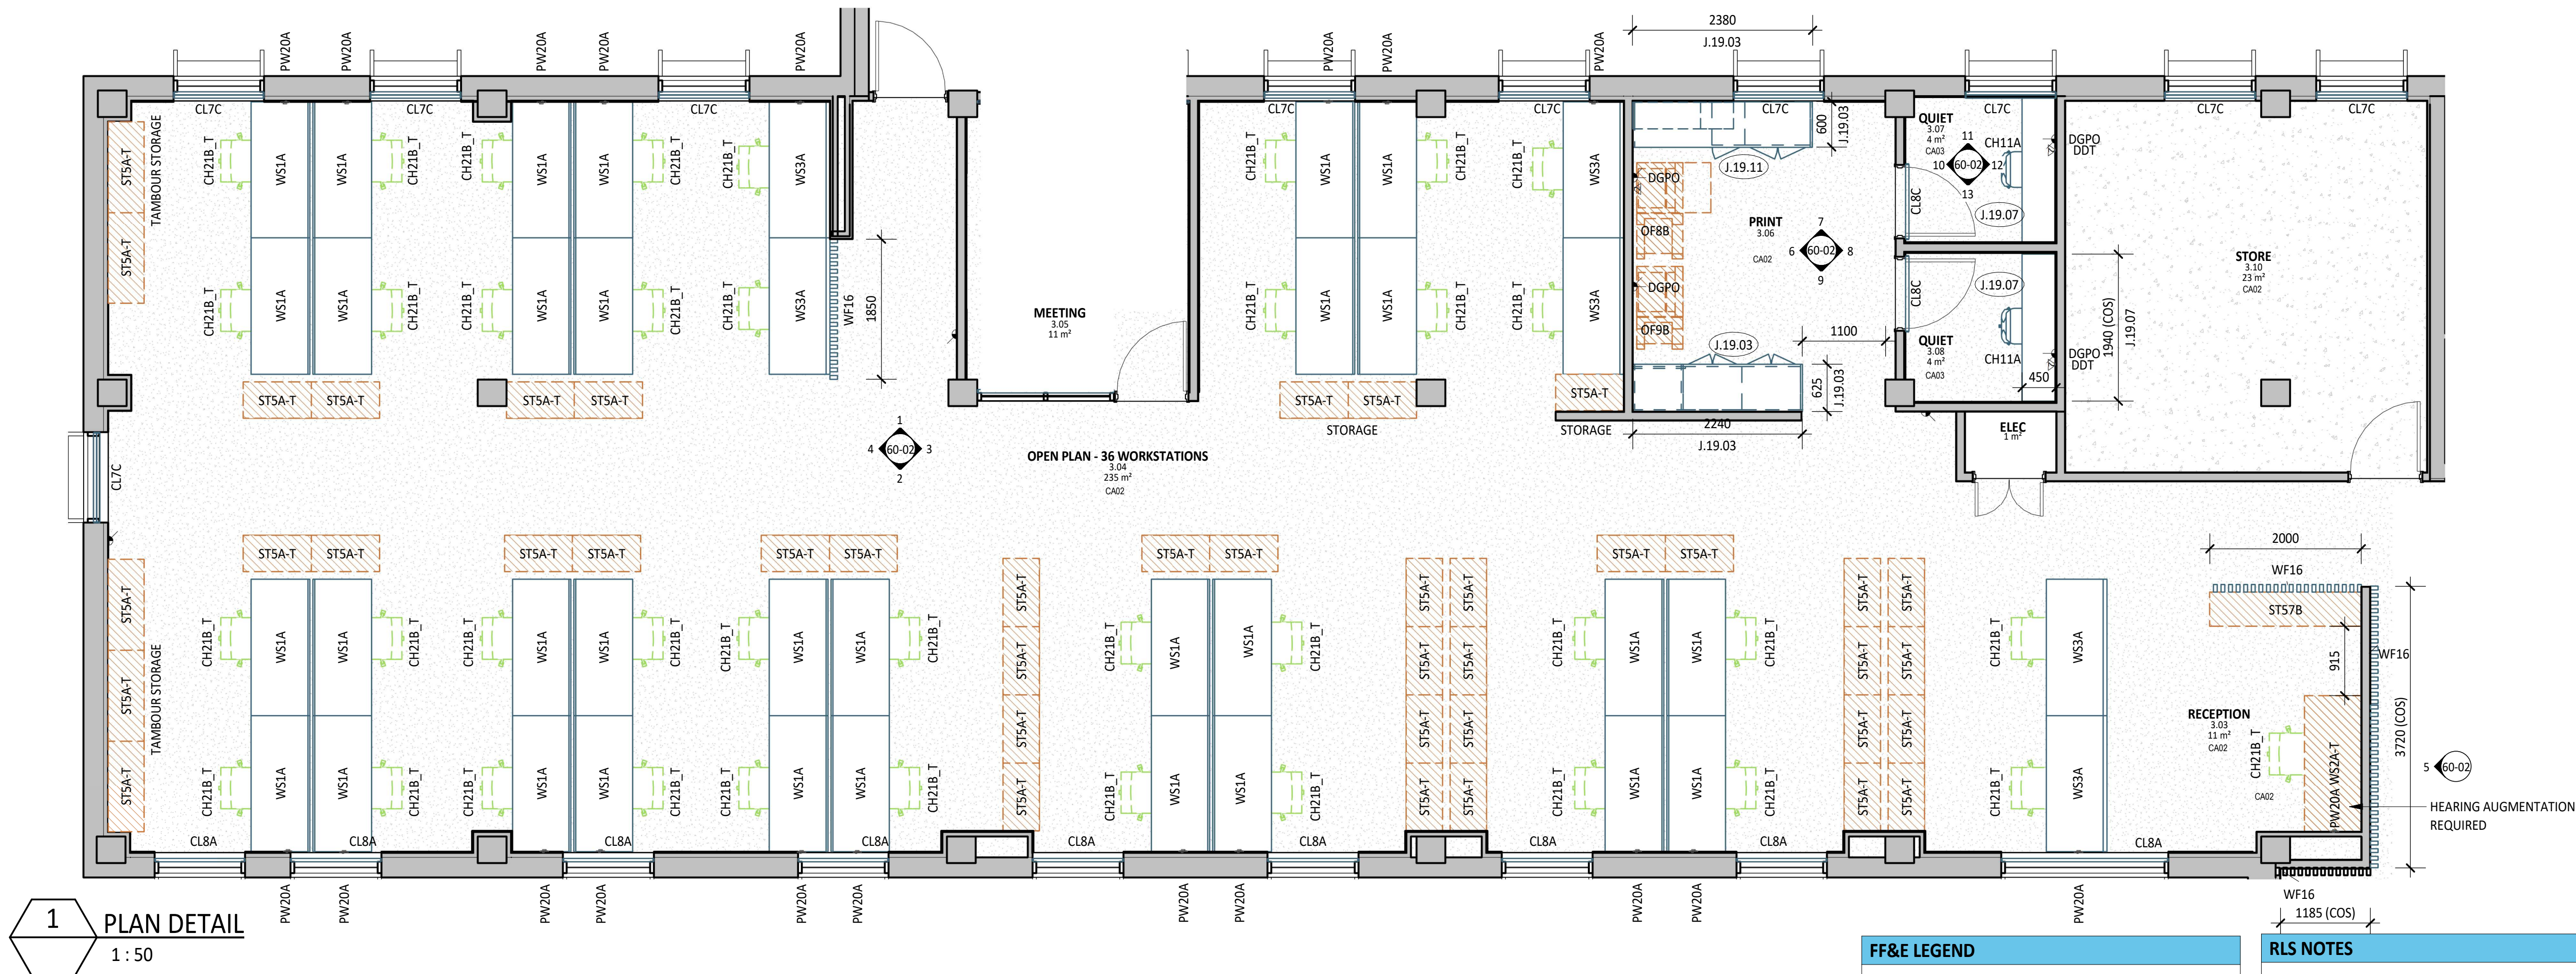

1 PLAN DETAIL
1 : 50

40-LEGEND FFE - OPEN PLAN - 33 WORKSTATIONS			
Code	Description	Group	Count
CL7C	Double Roller Blinds - Blockout	1	5
CL8A	Single See Through Blind	1	8
WS1A	Workstation: Office 1800mm (W) x 750mm(D) – Sit/Stand – 50mm Aluminium Frame with Acoustic Panel Insert to Between Back-To-Back Workstation	1	32
WS3A	Workstation: Office 1800mm (W) x 750mm(D) – Sit/Stand – 50mm Aluminium Frame with Acoustic Panel Insert to Workstation	1	4
ST5A-T	Cabinet - Tambour Double Door	2T	42
CH21B_T	Chair - Task	3	36

40-LEGEND FFE - RECEPTION			
Code	Description	Group	Count
ST57B	Brownbuilt Fleet Key Cupboard	2T	1
WS2A-T	Workstation: Office 1800mm (W) x 750mm(D) – Sit/Stand	2T	1
CH21B_T	Chair - Task	3	1

40-LEGEND FFE - PRINT BLD19			
Code	Description	Group	Count
CL7C	Double Roller Blinds - Blockout	1	1
OF8B	Printer - Office Workstation - A1	2T	1
OF9B	Printer - Office Workstation	2T	1

60-LEGEND JOINERY - BUILDING 19 - PRINT	
FFE_Mark	Comments
J.19.03	Underbench Cupboards, Benchtop
J.19.11	Underbench Cupboards, Benchtop, Acoustic Panels splashback, overhead cupboards, and acoustic panel bulkhead

40-LEGEND FFE - QUIET ROOM			
Code	Description	Group	Count
CH11A	Chair - Ergonomic	1	2
CL7C	Double Roller Blinds - Blockout	1	1
CL8C	Single Block Out Blind	1	2

60-LEGEND JOINERY - BUILDING 19 - QUIET	
FFE_Mark	Comments
J.19.07	Benchtop with Support Gables

FF&E LEGEND	
	GROUP 1 ITEMS (PROVIDED & FITTED UNDER CONTRACT)
	GROUP 2 ITEMS (PROVIDED BY CLIENT & FITTED UNDER CONTRACT)
	GROUP 2T ITEMS - EXISTING EQUIPMENT (PROVIDED BY CLIENT & FITTED UNDER CONTRACT)
	GROUP 3 ITEMS (PROVIDED & INSTALLED BY CLIENT)
PLANS TO BE PRINTED IN COLOUR	
SCH_Code	FF&E TAG
JQ.PROC	JOINERY TAG

ELECTRICAL LEGEND	
	SINGLE POWER OUTLET
	DOUBLE POWER OUTLET
	SINGLE DATA
	DOUBLE DATA
	LIGHT SWITCH
	TV
	FLOOR BOX (FB)
REFER TO ELECTRICAL ENGINEER'S DRAWINGS FOR DETAILS	

RLS NOTES	
1.	ALL ARCHITECTURAL DRAWINGS TO BE READ IN CONJUNCTION WITH OTHER DISCIPLINES.
2.	REFER TO FF&E, SANITARYWARE SCHEDULES FOR ALL FURNITURE, FIXTURES, AND EQUIPMENT.
3.	REFER TO HYDRAULIC ENGINEER'S DRAWINGS FOR HYDRAULIC SERVICES. FINISH OF VALVE/BOX COVERS TO MATCH ADJACENT WALL/JOINERY FINISH.
4.	REFER TO ELECTRICAL DOCUMENTATION FOR OUTLET DETAILS (ie. POWER, DATA, COMMS etc.)
5.	REFER TO AUDIO VISUAL DOCUMENTATION (VideoPro) FOR AV REQUIREMENTS AND DETAILS.
6.	AV SUPPLIER TO CONFIRM EXACT POSITIONS OF EQUIPMENT ON SITE
7.	ALL FF&E ITEMS ARE TO BE READ IN CONJUNCTION WITH FF&E SCHEDULES AND CQU DESIGN MANUAL.
8.	ALL FF&E AND TRANSFER ITEMS TO BE REVIEWED AND CONFIRMED WITH CLIENT PRIOR TO COMMENCING ON SITE.
9.	PROVIDE ALLOWANCE AND ADD SUPPORT TO WALLS, WHERE FITTINGS ARE WALL MOUNTED. THIS INCLUDES BUT NOT LIMITED TO HANDBASINS, HANDRAILS, SCREENS, PROJECTORS, etc.
10.	FF&E COUNT IS FOR INFORMATION ONLY. THE TOTAL NUMBER OF FF&E ITEMS ARE TO BE CONFIRMED WITH CLIENT AND ARCHITECTS BEFORE PURCHASE OF ITEMS.
11.	CONFIRM ALL DIMENSIONS ON SITE FOR JOINERY ITEMS.
12.	ALL SANITARY FIXINGS & FIXTURES IN PWD TOILETS TO BE INSTALLED IN ACCORDANCE WITH AS1428.1
13.	ALLOW FOR FIRE EXTINGUISHERS & FIRE BLANKETS AS PER AS2444.2001
14.	POWER AND DATA POINTS SHOWN ON THE ROOM LAYOUT SHEETS WERE SHOWN AND DISCUSSED DURING USER GROUP BRIEFING. THESE RELATE TO PARTICULAR EQUIPMENT THAT WAS DISCUSSED AS REQUIRING POWER AND DATA. THESE REFLECT STAKEHOLDER EXPECTATIONS FOR SPECIFIC POWER AND DATA POINTS AND HAVE REMAINED IN THE DOCUMENTATION AS A USEFUL REFERENCE FOR THE CONTRACTOR. THESE ARE NOT A COMPLETE QUANTITY AND SPECIFICATION OF POWER AND DATA. THE CONTRACTOR IS TO REFER TO ELECTRICAL ENGINEER'S DOCUMENTATION FOR ALLOWANCE. REFER TO ELECTRICAL DOCUMENTATION FOR AMPS AND 3 PHASE POWER REQUIREMENTS. REFER TO AUDIO VISUAL (VIDEOPRO) DOCUMENTATION FOR ADDITIONAL POWER AND DATA REQUIREMENTS
15.	ALLOW FOR STRUCTURAL PLY BACKING BEHIND PLASTERBOARD FOR FULL EXTENT OF WALLS WITH MOUNTED AUDIO VISUAL EQUIPMENT. REFER TO AUDIO VISUAL (VIDEOPRO) DOCUMENTATION FOR LOCATIONS OF WALL MOUNTED EQUIPMENT.
16.	ALLOW FOR PRIVACY FILM TO ALL INTERNAL GLAZING (DOORS AND WINDOWS) TO OFFICES AND MEETING ROOMS. CONFIRM SET OUT PRIOR TO INSTALLATION
17.	ALLOW FOR DOUBLE BLOCK OUT BLINDS TO ALL WINDOWS UNLESS NOTED OTHERWISE
18.	ALL INTERNAL DOORS ARE TO BE SOLID CORE DOORS WITHIN ALUMINIUM FRAMED SUITES UNLESS NOTED OTHERWISE.
19.	FLOOR BOXES MUST BE COORDINATED WITH BOTH THE STRUCTURAL AND ELECTRICAL ENGINEERS. BEFORE ANY CUTTING OF THE EXISTING SLAB OCCURS, CONFIRM THE EXACT LOCATIONS AND REQUIREMENTS WITH THE STRUCTURAL ENGINEER.
20.	HEARING AUGMENTATION TO AUSTRALIAN STANDARDS – REFER VIDEOPRO AND ELECTRICAL SPECIFICATION

ISSUE FOR TENDER

RLS - BLD19-L3 - OPEN PLAN - 33 WORKSTATIONS, PRINT, RECEPTION	
scale	project no.
1 : 50 @ A1	260018
revision	
B	
sheet no.	
CQU-ROK-019-03-ARC-60-01	

thomson adsett

PEDDLE THORP
architecture | interiors | health | planning

Telephone +61 7 3840 9999
bne@thomsonadsett.com
Level 9, 470 St Pauls Terrace
Fortitude Valley
Qld 4006 Australia
thomsonadsett.com

© Copyright
These drawings and designs and the copyright thereof are the property of Thomson Adsett Pty Ltd and must not be used, retained or copied without written permission of Thomson Adsett Pty Ltd. ABN 76 105 314 654 Trading as ThomsonAdsett. Dimensions take precedence over scaling. Do not measure off drawings as print sizes may vary

CQU ROCKHAMPTON TAFE CONSOLIDATION - STAGE 2


554/700 Yaamba Rd, Norman Gardens QLD 4701




B	05/03/26	ISSUED FOR TENDER	BS
A	12/02/26	ISSUED FOR TENDER	SM
2	30/01/26	60% DRAFT ISSUE	SM
1	23/01/26	FOR COORDINATION ISSUE	SM


rev	date	details	init.
-----	------	---------	-------

drawn	date
TA/PT	19/12/25
checked	date
JT/RJ	19/12/25
verified	date
JT/RJ	19/12/25

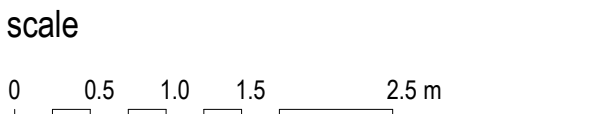


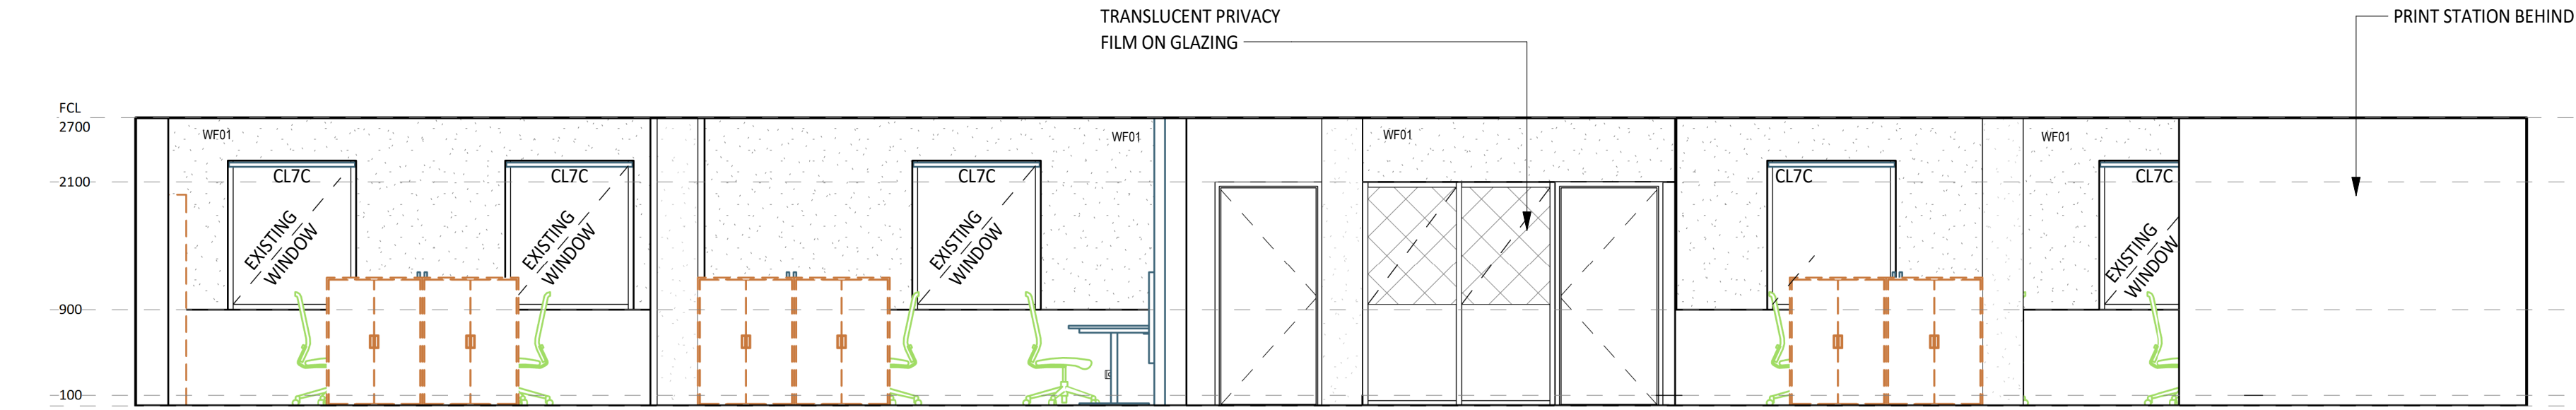


1 ELEVATION DETAIL
60-01 1:50

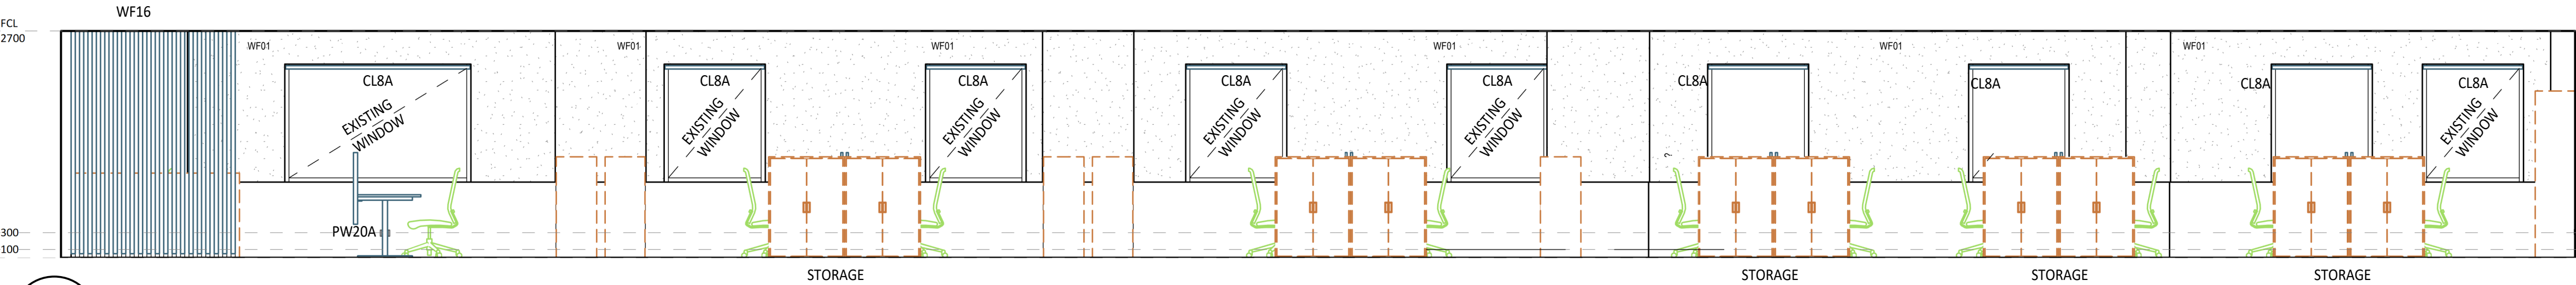


2 ELEVATION DETAIL
60-01 1:50

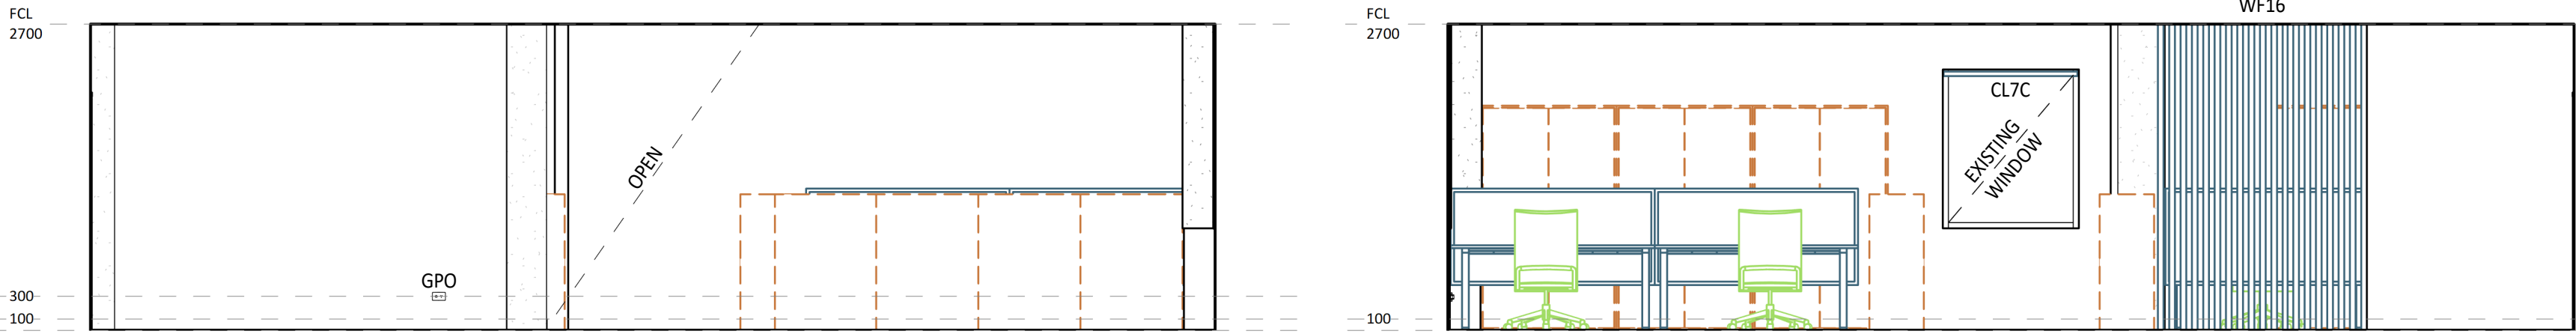

3 ELEVATION DETAIL
60-01 1:50

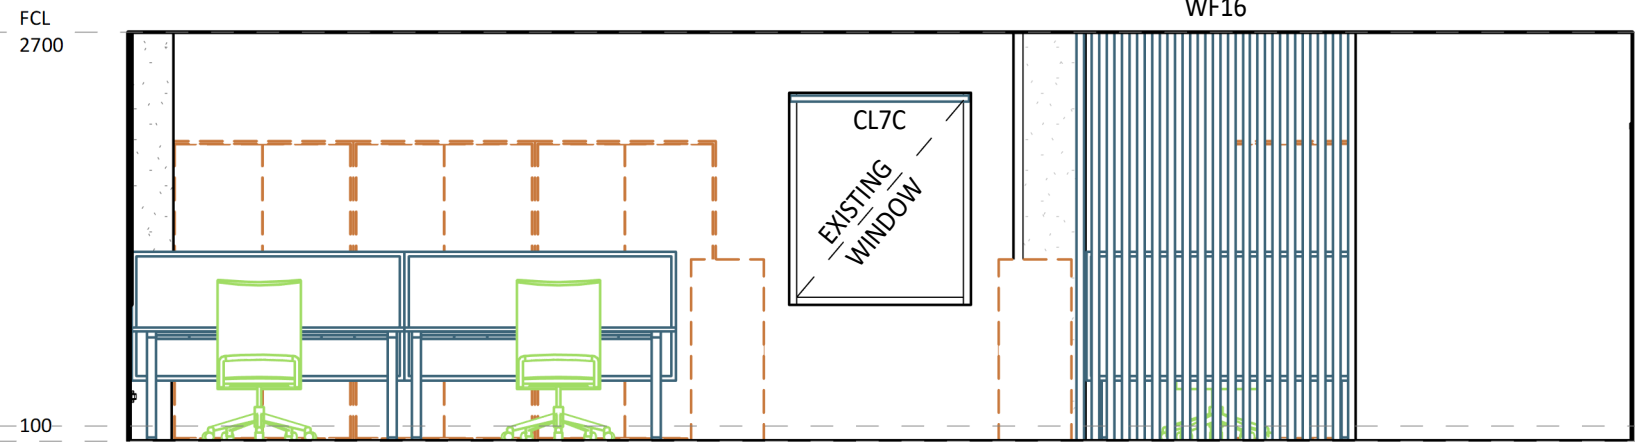


4 ELEVATION DETAIL
60-01 1:50

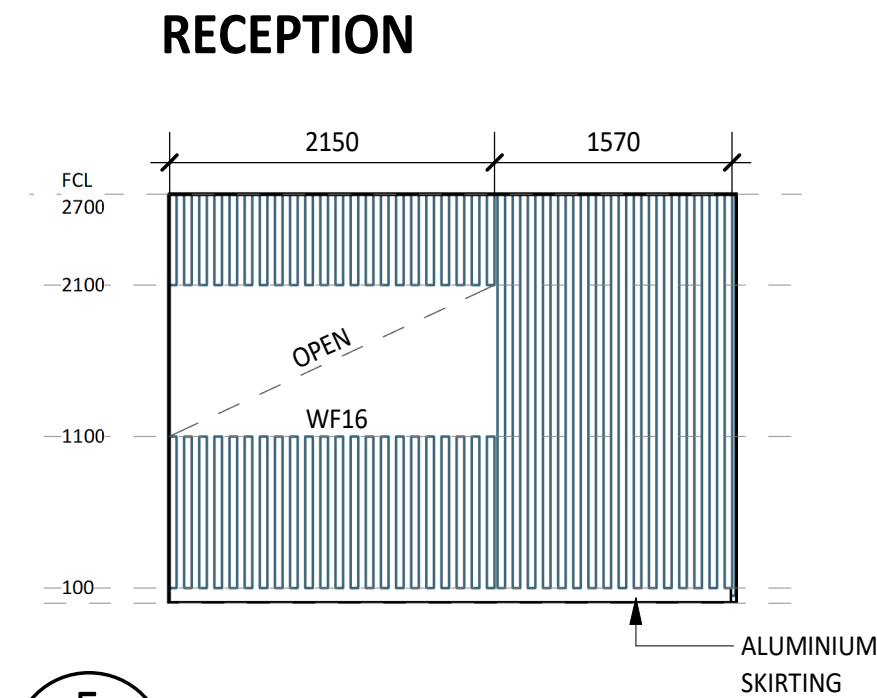


5 ELEVATION DETAIL
60-01 1:50


PRINT

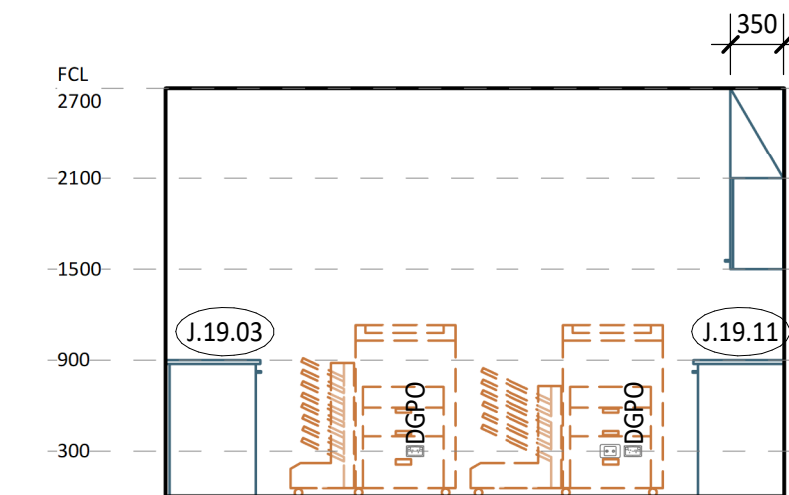


6 ELEVATION DETAIL
1:50

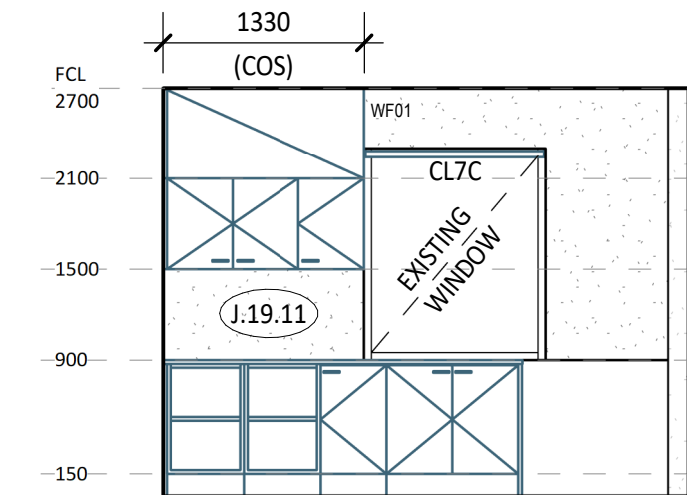

7 ELEVATION DETAIL
1:50

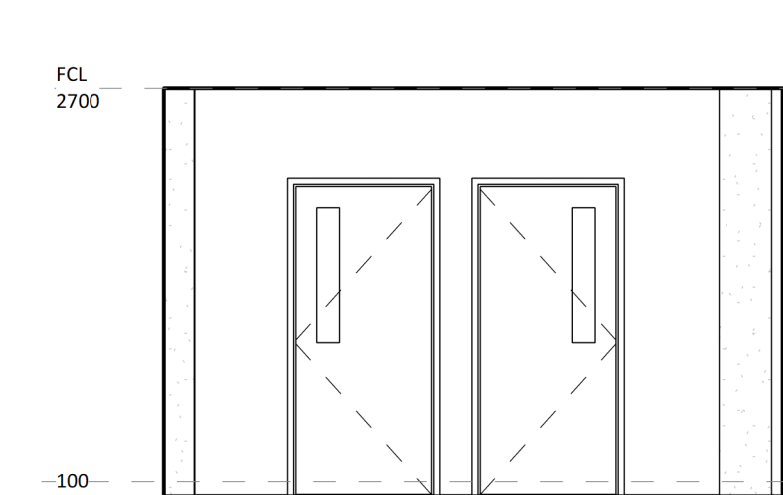


8 ELEVATION DETAIL
1:50

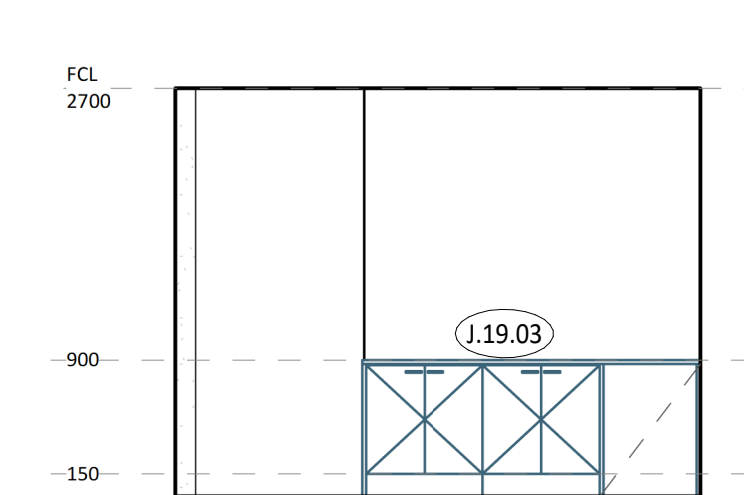


9 ELEVATION DETAIL
1:50


QUIET ROOM

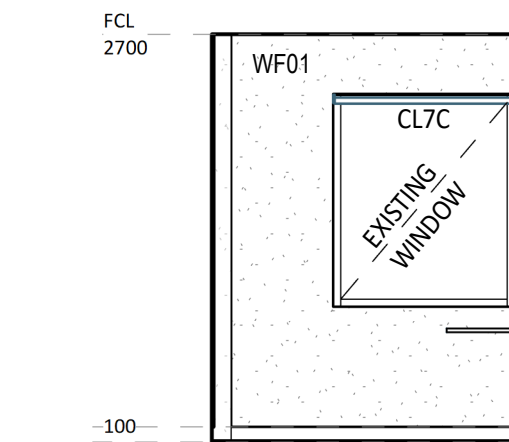


11 ELEVATION DETAIL
1:50

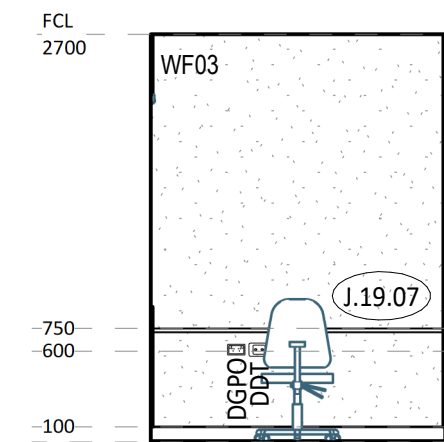

12 ELEVATION DETAIL
1:50

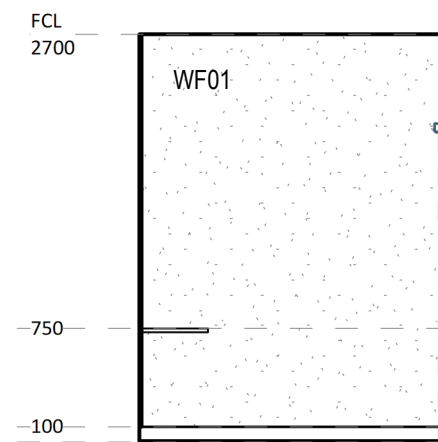

13 ELEVATION DETAIL
1:50

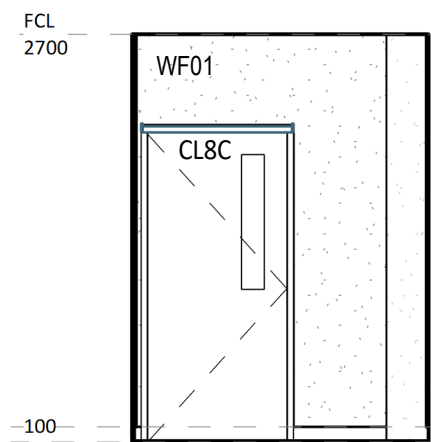

10 ELEVATION DETAIL
1:50

40-LEGEND FFE - QUIET ROOM			
Code	Description	Group	Count
CH11A	Chair - Ergonomic	1	2
CL7C	Double Roller Blinds - Blockout	1	1
CL8C	Single Block Out Blind	1	2

60-LEGEND JOINERY - BUILDING 19 - QUIET	
FFE_Mark	Comments
J.19.07	Benchtop with Support Gables

40-LEGEND FFE - OPEN PLAN - 33 WORKSTATIONS			
Code	Description	Group	Count
CL7C	Double Roller Blinds - Blockout	1	5
CL8A	Single See Through Blind	1	8
WS1A	Workstation: Office 1800mm (W) x 750mm(D) - Sit/Stand - 50mm Aluminium Frame with Acoustic Panel Insert to Between Back-To-Back Workstation	1	32
WS3A	Workstation: Office 1800mm (W) x 750mm(D) - Sit/Stand - 50mm Aluminium Frame with Acoustic Panel Insert to Workstation	1	4
ST5A-T	Cabinet - Tambour Double Door	2T	42
CH21B-T	Chair - Task	3	36

- ### RLS NOTES
- ALL ARCHITECTURAL DRAWINGS TO BE READ IN CONJUNCTION WITH OTHER DISCIPLINES.
 - REFER TO FF&E, SANITARYWARE SCHEDULES FOR ALL FURNITURE, FIXTURES, AND EQUIPMENT.
 - REFER TO HYDRAULIC ENGINEER'S DRAWINGS FOR HYDRAULIC SERVICES. FINISH OF VALVE/BOX COVERS TO MATCH ADJACENT WALL/JOINERY FINISH.
 - REFER TO ELECTRICAL DOCUMENTATION FOR OUTLET DETAILS (ie. POWER, DATA, COMMS etc.)
 - REFER TO AUDIO VISUAL DOCUMENTATION (VideoPro) FOR AV REQUIREMENTS AND DETAILS.
 - AV SUPPLIER TO CONFIRM EXACT POSITIONS OF EQUIPMENT ON SITE
 - ALL FF&E ITEMS ARE TO BE READ IN CONJUNCTION WITH FF&E SCHEDULES AND CQU DESIGN MANUAL.
 - ALL FF&E AND TRANSFER ITEMS TO BE REVIEWED AND CONFIRMED WITH CLIENT PRIOR TO COMMENCING ON SITE.
 - PROVIDE ALLOWANCE AND ADD SUPPORT TO WALLS, WHERE FITTINGS ARE WALL MOUNTED. THIS INCLUDES BUT NOT LIMITED TO HANDBASINS, HANDRAILS, SCREENS, PROJECTORS, etc.
 - FF&E COUNT IS FOR INFORMATION ONLY. THE TOTAL NUMBER OF FF&E ITEMS ARE TO BE CONFIRMED WITH CLIENT AND ARCHITECTS BEFORE PURCHASE OF ITEMS.
 - CONFIRM ALL DIMENSIONS ON SITE FOR JOINERY ITEMS.
 - ALL SANITARY FIXINGS & FIXTURES IN PWD TOILETS TO BE INSTALLED IN ACCORDANCE WITH AS1428.1
 - ALLOW FOR FIRE EXTINGUISHERS & FIRE BLANKETS AS PER AS2444.2001
 - POWER AND DATA POINTS SHOWN ON THE ROOM LAYOUT SHEETS WERE SHOWN AND DISCUSSED DURING USER GROUP BRIEFING. THESE RELATE TO PARTICULAR EQUIPMENT THAT WAS DISCUSSED AS REQUIRING POWER AND DATA. THESE REFLECT STAKEHOLDER EXPECTATIONS FOR SPECIFIC POWER AND DATA POINTS AND HAVE REMAINED IN THE DOCUMENTATION AS A USEFUL REFERENCE FOR THE CONTRACTOR. THESE ARE NOT A COMPLETE QUANTITY AND SPECIFICATION OF POWER AND DATA. THE CONTRACTOR IS TO REFER TO ELECTRICAL ENGINEER'S DOCUMENTATION FOR ALLOWANCE. REFER TO ELECTRICAL DOCUMENTATION FOR AMPS AND 3 PHASE POWER REQUIREMENTS. REFER TO AUDIO VISUAL (VIDEOPRO) DOCUMENTATION FOR ADDITIONAL POWER AND DATA REQUIREMENTS
 - ALLOW FOR STRUCTURAL PLY BACKING BEHIND PLASTERBOARD FOR FULL EXTENT OF WALLS WITH MOUNTED AUDIO VISUAL EQUIPMENT. REFER TO AUDIO VISUAL (VIDEOPRO) DOCUMENTATION FOR LOCATIONS OF WALL MOUNTED EQUIPMENT.
 - ALLOW FOR PRIVACY FILM TO ALL INTERNAL GLAZING (DOORS AND WINDOWS) TO OFFICES AND MEETING ROOMS. CONFIRM SET OUT PRIOR TO INSTALLATION
 - ALLOW FOR DOUBLE BLOCK OUT BLINDS TO ALL WINDOWS UNLESS NOTED OTHERWISE
 - ALL INTERNAL DOORS ARE TO BE SOLID CORE DOORS WITHIN ALUMINIUM FRAMED SUITES UNLESS NOTED OTHERWISE.
 - FLOOR BOXES MUST BE COORDINATED WITH BOTH THE STRUCTURAL AND ELECTRICAL ENGINEERS. BEFORE ANY CUTTING OF THE EXISTING SLAB OCCURS, CONFIRM THE EXACT LOCATIONS AND REQUIREMENTS WITH THE STRUCTURAL ENGINEER.
 - HEARING AUGMENTATION TO AUSTRALIAN STANDARDS - REFER VIDEOPRO AND ELECTRICAL SPECIFICATION

FF&E LEGEND	
GROUP 1 ITEMS (PROVIDED & FITTED UNDER CONTRACT)	
GROUP 2 ITEMS (PROVIDED BY CLIENT & FITTED UNDER CONTRACT)	
GROUP 2T ITEMS - EXISTING EQUIPMENT (PROVIDED BY CLIENT & FITTED UNDER CONTRACT)	
GROUP 3 ITEMS (PROVIDED & INSTALLED BY CLIENT)	
PLANS TO BE PRINTED IN COLOUR	
SCH_Code	FF&E TAG
JO.PROC	JOINERY TAG

ELECTRICAL LEGEND	
SINGLE POWER OUTLET	LIGHT SWITCH
DOUBLE POWER OUTLET	TV
SINGLE DATA	FLOOR BOX (FB)
DOUBLE DATA	
REFER TO ELECTRICAL ENGINEER'S DRAWINGS FOR DETAILS	

thomson
adsett

PEDDLE THORP
architecture | interiors | health | planning

Telephone +61 7 3840 9999
bne@thomsonadsett.com
Level 9, 470 St Pauls Terrace
Fortitude Valley
Qld 4006 Australia
thomsonadsett.com

© Copyright
These drawings and designs and the copyright thereof are the property of Thomson Adsett Pty Ltd and must not be used, retained or copied without written permission of Thomson Adsett Pty Ltd. ABN 76 105 314 654 Trading as ThomsonAdsett. Dimensions take precedence over scaling. Do not measure off drawings as print sizes may vary


CQU ROCKHAMPTON TAFE CONSOLIDATION - STAGE 2

554/700 Yaamba Rd, Norman Gardens QLD 4701



B	05/03/26	ISSUED FOR TENDER	BS
A	12/02/26	ISSUED FOR TENDER	SM
2	30/01/26	60% DRAFT ISSUE	SM
1	23/01/26	FOR COORDINATION ISSUE	SM

drawn	date
TA/PT	19/12/25
checked	date
JT/RJ	19/12/25
verified	date
JT/RJ	19/12/25

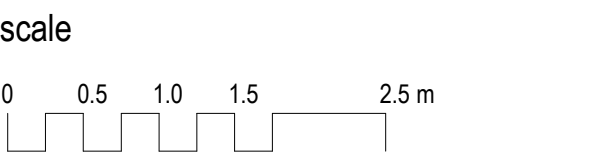

RLS - BLD19-L3 - OPEN PLAN - 33 WORKSTATIONS, RECEPTION


scale 1:50 @ A1 project no. 260018

revision B


sheet no. CQU-ROK-019-03-ARC-60-02

ISSUE FOR TENDER


FOYER, WAIT, OPEN PLAN - 4 WORKSTATIONS

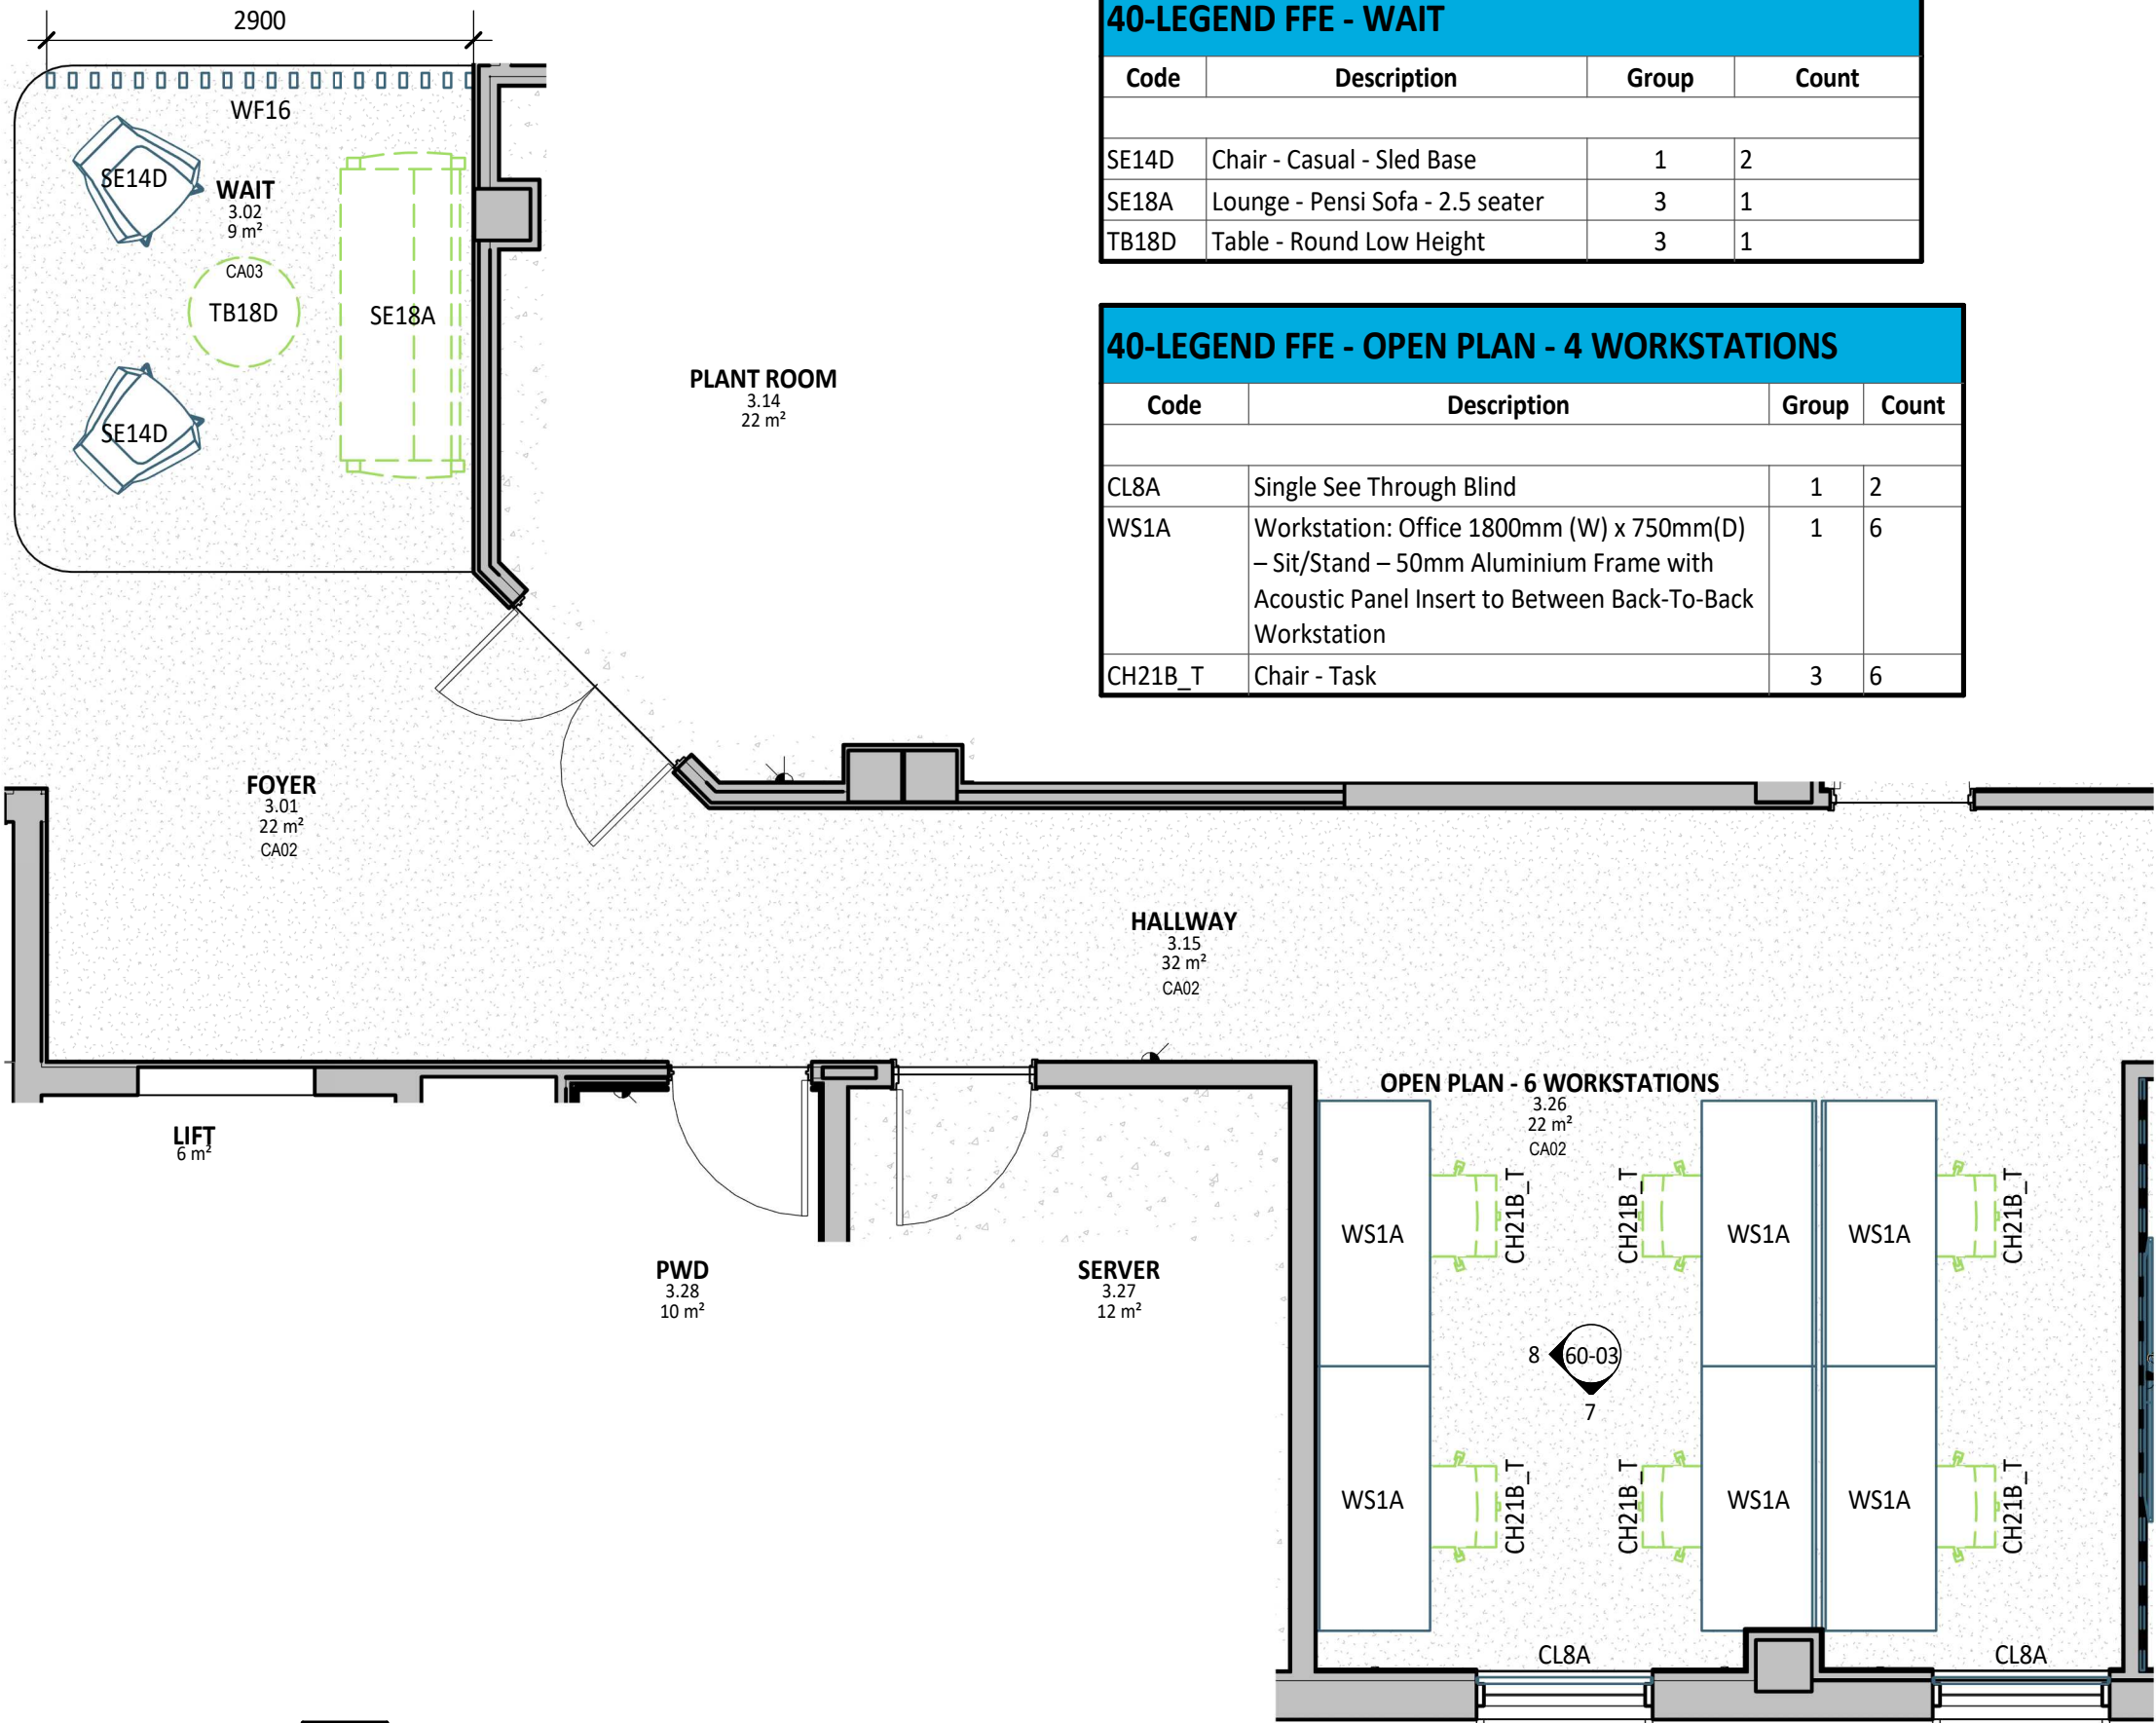

1 PLAN DETAIL
1 : 50

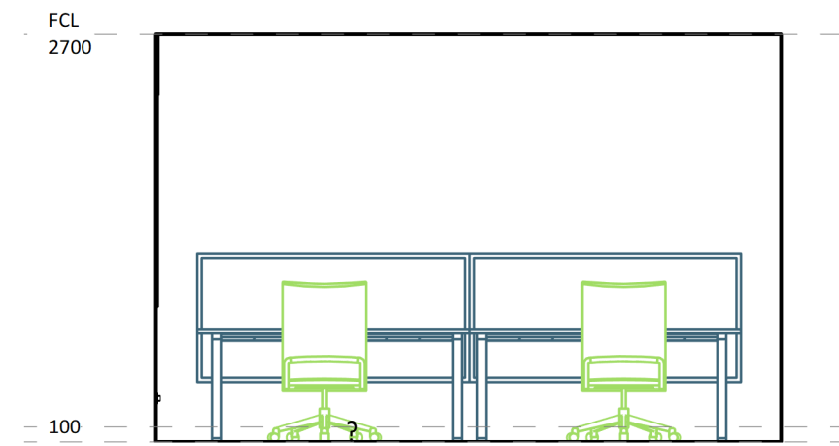

8 ELEVATION DETAIL
60-03 1 : 50

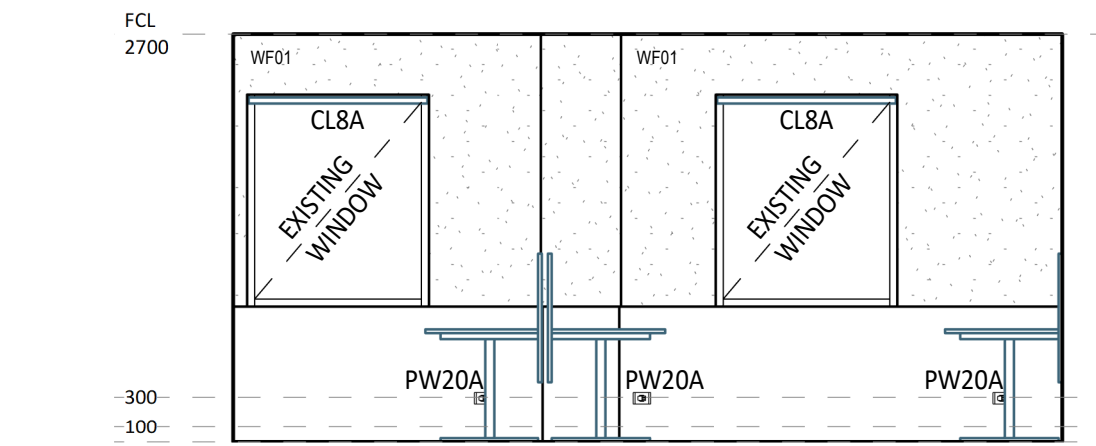


7 ELEVATION DETAIL
60-03 1 : 50


40-LEGEND FFE - WAIT			
Code	Description	Group	Count
SE14D	Chair - Casual - Sled Base	1	2
SE18A	Lounge - Pensi Sofa - 2.5 seater	3	1
TB18D	Table - Round Low Height	3	1

40-LEGEND FFE - OPEN PLAN - 4 WORKSTATIONS			
Code	Description	Group	Count
CL8A	Single See Through Blind	1	2
WS1A	Workstation: Office 1800mm (W) x 750mm(D) – Sit/Stand – 50mm Aluminium Frame with Acoustic Panel Insert to Between Back-To-Back Workstation	1	6
CH21B T	Chair - Task	3	6


1PX OFFICE

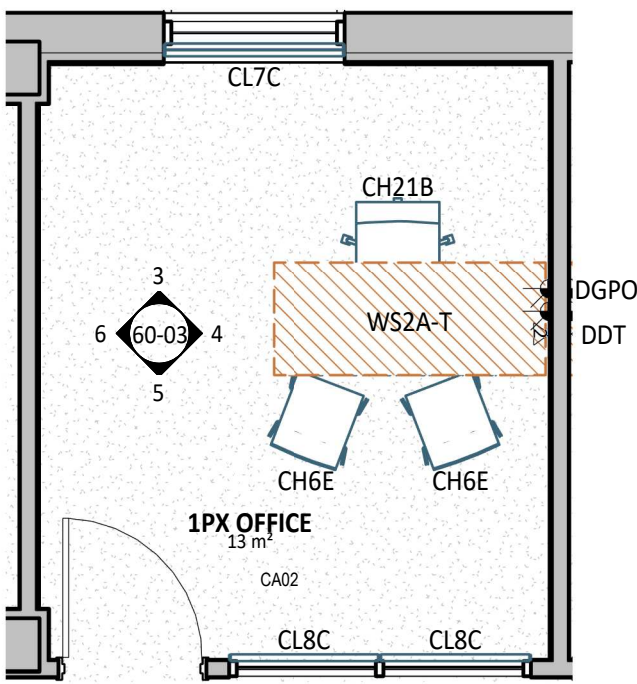

2 PLAN DETAIL
1 : 50

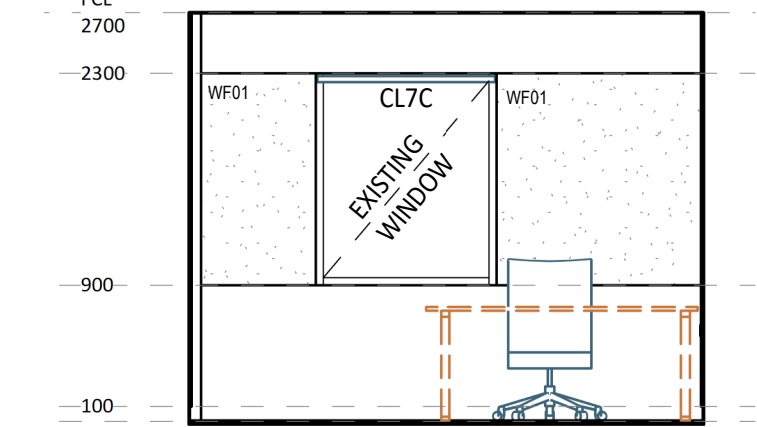


3 ELEVATION DETAIL
1 : 50

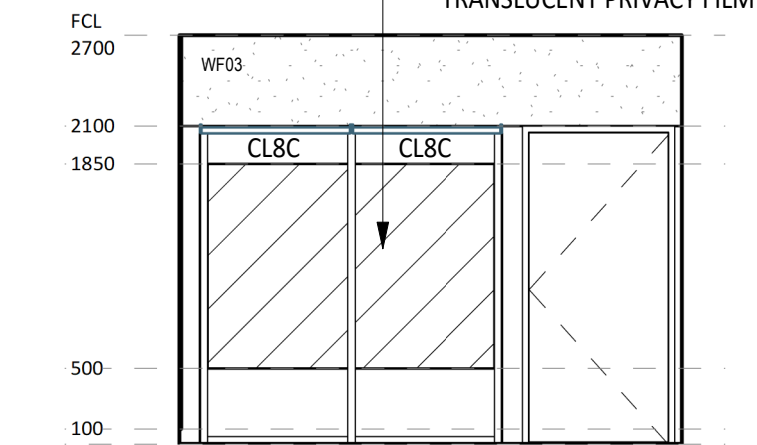


5 ELEVATION DETAIL
1 : 50

40-LEGEND FFE - 1PX OFFICE			
Code	Description	Group	Count
CH6E	Chair - Sled Base Visitor Chair Upholstered Seat Pad	1	2
CH21B	Chair - Task	1	1
CL7C	Double Roller Blinds - Blockout	1	1
CL8C	Single Block Out Blind	1	2
WS2A-T	Workstation: Office 1800mm (W) x 750mm(D) – Sit/Stand	2T	1

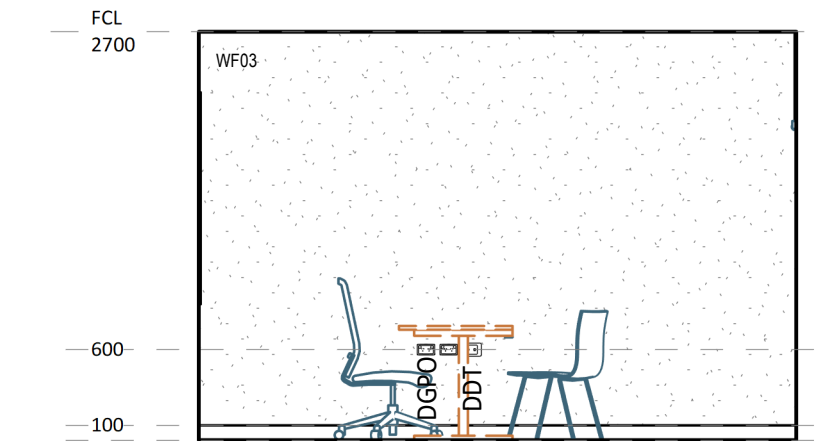

4 ELEVATION DETAIL
1 : 50

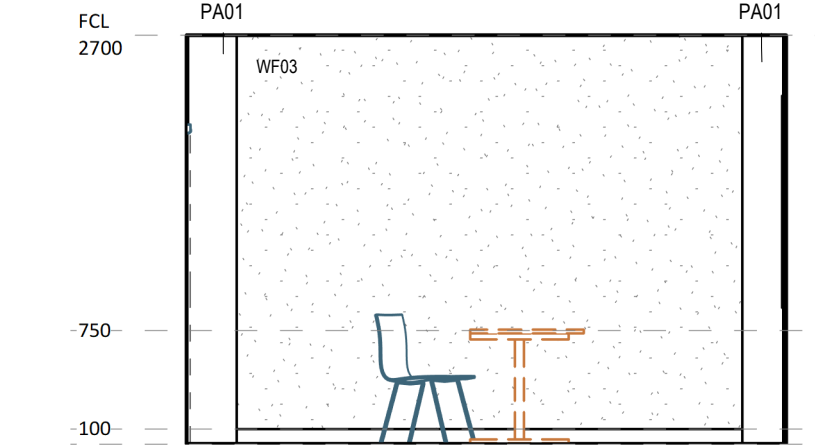

6 ELEVATION DETAIL
1 : 50

RLS NOTES

1. ALL ARCHITECTURAL DRAWINGS TO BE READ IN CONJUNCTION WITH OTHER DISCIPLINES.
2. REFER TO FF&E, SANITARYWARE SCHEDULES FOR ALL FURNITURE, FIXTURES, AND EQUIPMENT.
3. REFER TO HYDRAULIC ENGINEER'S DRAWINGS FOR HYDRAULIC SERVICES. FINISH OF VALVE/BOX COVERS TO MATCH ADJACENT WALL/JOINERY FINISH.
4. REFER TO ELECTRICAL DOCUMENTATION FOR OUTLET DETAILS (ie. POWER, DATA, COMMS etc.)
5. REFER TO AUDIO VISUAL DOCUMENTATION (VideoPro) FOR AV REQUIREMENTS AND DETAILS.
6. AV SUPPLIER TO CONFIRM EXACT POSITIONS OF EQUIPMENT ON SITE
7. ALL FF&E ITEMS ARE TO BE READ IN CONJUNCTION WITH FF&E SCHEDULES AND CQU DESIGN MANUAL.
8. ALL FF&E AND TRANSFER ITEMS TO BE REVIEWED AND CONFIRMED WITH CLIENT PRIOR TO COMMENCING ON SITE.
9. PROVIDE ALLOWANCE AND ADD SUPPORT TO WALLS, WHERE FITTINGS ARE WALL MOUNTED. THIS INCLUDES BUT NOT LIMITED TO HANDBASINS, HANDRAILS, SCREENS, PROJECTORS, etc.
10. FF&E COUNT IS FOR INFORMATION ONLY. THE TOTAL NUMBER OF FF&E ITEMS ARE TO BE CONFIRMED WITH CLIENT AND ARCHITECTS BEFORE PURCHASE OF ITEMS.
11. CONFIRM ALL DIMENSIONS ON SITE FOR JOINERY ITEMS.
12. ALL SANITARY FIXINGS & FIXTURES IN PWD TOILETS TO BE INSTALLED IN ACCORDANCE WITH AS1428.1
13. ALLOW FOR FIRE EXTINGUISHERS & FIRE BLANKETS AS PER AS2444.2001
14. POWER AND DATA POINTS SHOWN ON THE ROOM LAYOUT SHEETS WERE SHOWN AND DISCUSSED DURING USER GROUP BRIEFING. THESE RELATE TO PARTICULAR EQUIPMENT THAT WAS DISCUSSED AS REQUIRING POWER AND DATA. THESE REFLECT STAKEHOLDER EXPECTATIONS FOR SPECIFIC POWER AND DATA POINTS AND HAVE REMAINED IN THE DOCUMENTATION AS A USEFUL REFERENCE FOR THE CONTRACTOR. THESE ARE NOT A COMPLETE QUANTITY AND SPECIFICATION OF POWER AND DATA. THE CONTRACTOR IS TO REFER TO ELECTRICAL ENGINEER'S DOCUMENTATION FOR ALLOWANCE. REFER TO ELECTRICAL DOCUMENTATION FOR AMPS AND 3 PHASE POWER REQUIREMENTS. REFER TO AUDIO VISUAL (VIDEOPRO) DOCUMENTATION FOR ADDITIONAL POWER AND DATA REQUIREMENTS
15. ALLOW FOR STRUCTURAL PLY BACKING BEHIND PLASTERBOARD FOR FULL EXTENT OF WALLS WITH MOUNTED AUDIO VISUAL EQUIPMENT. REFER TO AUDIO VISUAL (VIDEOPRO) DOCUMENTATION FOR LOCATIONS OF WALL MOUNTED EQUIPMENT.
16. ALLOW FOR PRIVACY FILM TO ALL INTERNAL GLAZING (DOORS AND WINDOWS) TO OFFICES AND MEETING ROOMS. CONFIRM SET OUT PRIOR TO INSTALLATION
17. ALLOW FOR DOUBLE BLOCK OUT BLINDS TO ALL WINDOWS UNLESS NOTED OTHERWISE
18. ALL INTERNAL DOORS ARE TO BE SOLID CORE DOORS WITHIN ALUMINIUM FRAMED SUITES UNLESS NOTED OTHERWISE.
19. FLOOR BOXES MUST BE COORDINATED WITH BOTH THE STRUCTURAL AND ELECTRICAL ENGINEERS. BEFORE ANY CUTTING OF THE EXISTING SLAB OCCURS, CONFIRM THE EXACT LOCATIONS AND REQUIREMENTS WITH THE STRUCTURAL ENGINEER.
20. HEARING AUGMENTATION TO AUSTRALIAN STANDARDS – REFER VIDEOPRO AND ELECTRICAL SPECIFICATION

FF&E LEGEND

- GROUP 1 ITEMS (PROVIDED & FITTED UNDER CONTRACT)
- GROUP 2 ITEMS (PROVIDED BY CLIENT & FITTED UNDER CONTRACT)
- GROUP 2T ITEMS - EXISTING EQUIPMENT (PROVIDED BY CLIENT & FITTED UNDER CONTRACT)
- GROUP 3 ITEMS (PROVIDED & INSTALLED BY CLIENT)

PLANS TO BE PRINTED IN COLOUR

SCH_Code FF&E TAG

JO. PROC JOINERY TAG

ELECTRICAL LEGEND

- SINGLE POWER OUTLET
- DOUBLE POWER OUTLET
- SINGLE DATA
- DOUBLE DATA
- LIGHT SWITCH
- TV
- FLOOR BOX (FB)
- REFER TO ELECTRICAL ENGINEER'S DRAWINGS FOR DETAILS

thomson
adsett

PEDDLE THORP
architecture | interiors | health | planning

Telephone +61 7 3840 9999
bne@thomsonadsett.com
Level 9, 470 St Pauls Terrace
Fortitude Valley
QLD 4006 Australia
thomsonadsett.com

© Copyright
These drawings and designs and the copyright thereof are the property of Thomson Adsett Pty Ltd and must not be used, retained or copied without written permission of Thomson Adsett Pty Ltd. ABN 76 105 314 654 Trading as ThomsonAdsett. Dimensions take precedence over scaling. Do not measure off drawings as print sizes may vary

CQU ROCKHAMPTON
TAFE
CONSOLIDATION -
STAGE 2


554/700 Yaamba Rd, Norman
Gardens QLD 4701

for
CQUniversity
AUSTRALIA

B	05/03/26	ISSUED FOR TENDER	BS
A	12/02/26	ISSUED FOR TENDER	SM
2	30/01/26	60% DRAFT ISSUE	SM
1	23/01/26	FOR COORDINATION ISSUE	SM

rev	date	details	init.
-----	------	---------	-------

drawn	date
TA/PT	19/12/25
checked	date
JT/RJ	19/12/25
verified	date
JT/RJ	19/12/25

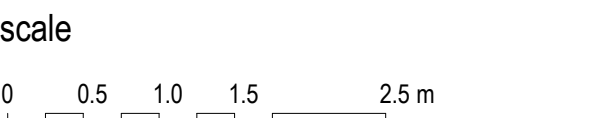

RLS - BLD19-L3 - OPEN
PLAN - 6 WORKSTATIONS,
WAIT, OFFICE

scale project no.
1 : 50 @ A1 260018

revision
B

sheet no.

CQU-ROK-019-03-ARC-60-03

ISSUE FOR TENDER

CQU ROCKHAMPTON TAFE CONSOLIDATION - STAGE 2

554/700 Yaamba Rd, Norman
Gardens QLD 4701



RLS NOTES

- ALL ARCHITECTURAL DRAWINGS TO BE READ IN CONJUNCTION WITH OTHER DISCIPLINES.
- REFER TO FF&E, SANITARYWARE SCHEDULES FOR ALL FURNITURE, FIXTURES, AND EQUIPMENT.
- REFER TO HYDRAULIC ENGINEER'S DRAWINGS FOR HYDRAULIC SERVICES. FINISH OF VALVE/BOX COVERS TO MATCH ADJACENT WALL/JOINERY FINISH.
- REFER TO ELECTRICAL DOCUMENTATION FOR OUTLET DETAILS (ie. POWER, DATA, COMMS etc.)
- REFER TO AUDIO VISUAL DOCUMENTATION (VideoPro) FOR AV REQUIREMENTS AND DETAILS.
- AV SUPPLIER TO CONFIRM EXACT POSITIONS OF EQUIPMENT ON SITE
- ALL FF&E ITEMS ARE TO BE READ IN CONJUNCTION WITH FF&E SCHEDULES AND CQU DESIGN MANUAL.
- ALL FF&E AND TRANSFER ITEMS TO BE REVIEWED AND CONFIRMED WITH CLIENT PRIOR TO COMMENCING ON SITE.
- PROVIDE ALLOWANCE AND ADD SUPPORT TO WALLS, WHERE FITTINGS ARE WALL MOUNTED. THIS INCLUDES BUT NOT LIMITED TO HANDBASINS, HANDRAILS, SCREENS, PROJECTORS, etc.
- FF&E COUNT IS FOR INFORMATION ONLY. THE TOTAL NUMBER OF FF&E ITEMS ARE TO BE CONFIRMED WITH CLIENT AND ARCHITECTS BEFORE PURCHASE OF ITEMS.
- CONFIRM ALL DIMENSIONS ON SITE FOR JOINERY ITEMS.
- ALL SANITARY FIXINGS & FIXTURES IN PWD TOILETS TO BE INSTALLED IN ACCORDANCE WITH AS1428.1
- ALLOW FOR FIRE EXTINGUISHERS & FIRE BLANKETS AS PER AS2444.2001
- POWER AND DATA POINTS SHOWN ON THE ROOM LAYOUT SHEETS WERE SHOWN AND DISCUSSED DURING USER GROUP BRIEFING. THESE RELATE TO PARTICULAR EQUIPMENT THAT WAS DISCUSSED AS REQUIRING POWER AND DATA. THESE REFLECT STAKEHOLDER EXPECTATIONS FOR SPECIFIC POWER AND DATA POINTS AND HAVE REMAINED IN THE DOCUMENTATION AS A USEFUL REFERENCE FOR THE CONTRACTOR. THESE ARE NOT A COMPLETE QUANTITY AND SPECIFICATION OF POWER AND DATA. THE CONTRACTOR IS TO REFER TO ELECTRICAL ENGINEER'S DOCUMENTATION FOR ALLOWANCE. REFER TO ELECTRICAL DOCUMENTATION FOR AMPS AND 3 PHASE POWER REQUIREMENTS. REFER TO AUDIO VISUAL (VIDEOPRO) DOCUMENTATION FOR ADDITIONAL POWER AND DATA REQUIREMENTS
- ALLOW FOR STRUCTURAL PLY BACKING BEHIND PLASTERBOARD FOR FULL EXTENT OF WALLS WITH MOUNTED AUDIO VISUAL EQUIPMENT. REFER TO AUDIO VISUAL (VIDEOPRO) DOCUMENTATION FOR LOCATIONS OF WALL MOUNTED EQUIPMENT.
- ALLOW FOR PRIVACY FILM TO ALL INTERNAL GLAZING (DOORS AND WINDOWS) TO OFFICES AND MEETING ROOMS. CONFIRM SET OUT PRIOR TO INSTALLATION
- ALLOW FOR DOUBLE BLOCK OUT BLINDS TO ALL WINDOWS UNLESS NOTED OTHERWISE
- ALL INTERNAL DOORS ARE TO BE SOLID CORE DOORS WITHIN ALUMINIUM FRAMED SUITES UNLESS NOTED OTHERWISE.
- FLOOR BOXES MUST BE COORDINATED WITH BOTH THE STRUCTURAL AND ELECTRICAL ENGINEERS. BEFORE ANY CUTTING OF THE EXISTING SLAB OCCURS, CONFIRM THE EXACT LOCATIONS AND REQUIREMENTS WITH THE STRUCTURAL ENGINEER.
- HEARING AUGMENTATION TO AUSTRALIAN STANDARDS -- REFER VIDEOPRO AND ELECTRICAL SPECIFICATION

FF&E LEGEND

- GROUP 1 ITEMS (PROVIDED & FITTED UNDER CONTRACT)
- GROUP 2 ITEMS (PROVIDED BY CLIENT & FITTED UNDER CONTRACT)
- GROUP 2T ITEMS - EXISTING EQUIPMENT (PROVIDED BY CLIENT & FITTED UNDER CONTRACT)
- GROUP 3 ITEMS (PROVIDED & INSTALLED BY CLIENT)

PLANS TO BE PRINTED IN COLOUR


SCH_Code	FF&E TAG
10.PROC	JOINERY TAG

ELECTRICAL LEGEND

- SINGLE POWER OUTLET
 - DOUBLE POWER OUTLET
 - SINGLE DATA
 - DOUBLE DATA
 - LIGHT SWITCH
 - TV
 - FLOOR BOX (FB)
- REFER TO ELECTRICAL ENGINEER'S DRAWINGS FOR DETAILS

A	12/02/26	ISSUED FOR TENDER	SM
2	30/01/26	60% DRAFT ISSUE	SM
1	23/01/26	FOR COORDINATION ISSUE	SM
rev/	date	details	init.

drawn	date
TA/PT	19/12/25
checked	date
JT/RJ	19/12/25
verified	date
JT/RJ	19/12/25

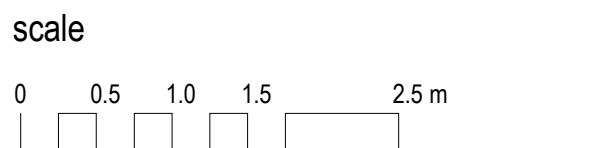

RLS - BLD19-L3 - MEETING ROOMS


scale	project no.
1 : 50 @ A1	260018
revision	
A	
sheet no.	
CQU-ROK-019-03-ARC-60-04	

6PX MEETING ROOM


40-LEGEND FFE - MEETING 6P

Code	Description	Group	Count
AV23C	Television - Wall Mounted. Refer To AV Consultant's Documentation for Specification	1	1
CH15A	Chair - Meeting Room with no arms	1	6
CL8C	Single Block Out Blind	1	2
EP15H	Rectangular Gable	1	1
TB13B	Table - Meeting	1	1
TVAV	OUTLET: MATV	1	1
AV8A	Wall Mounted Tv Bracket	3	1


1 PLAN DETAIL 1 : 50

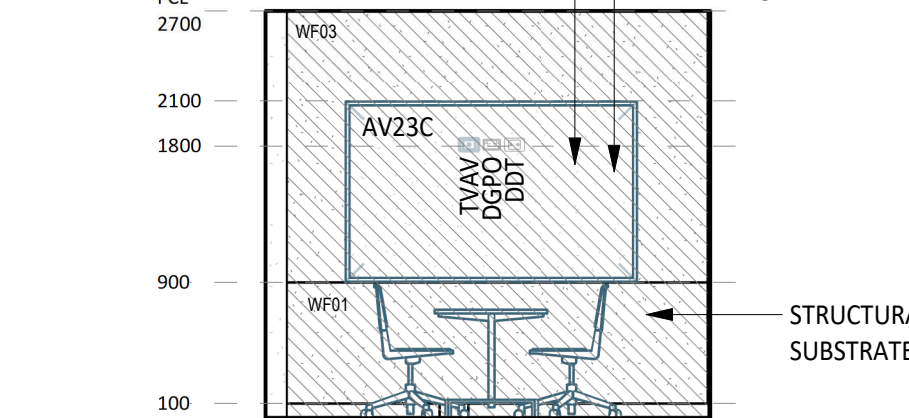


2 ELEVATION DETAIL 1 : 50

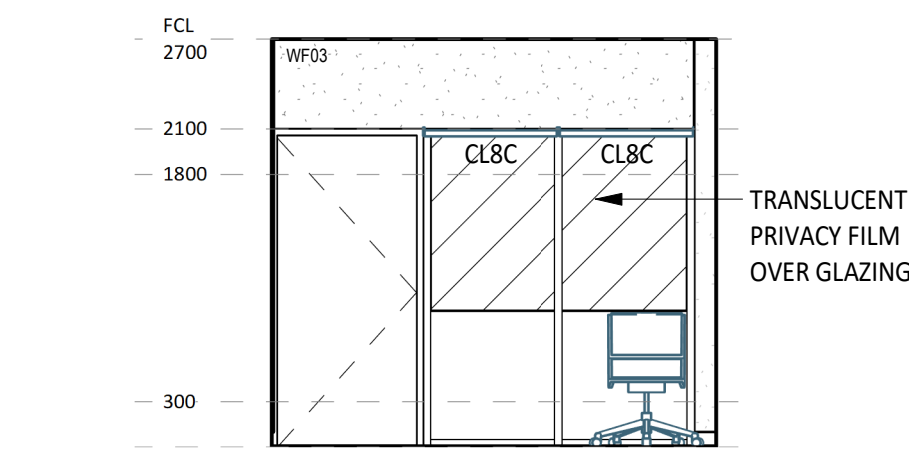


4 ELEVATION DETAIL 1 : 50

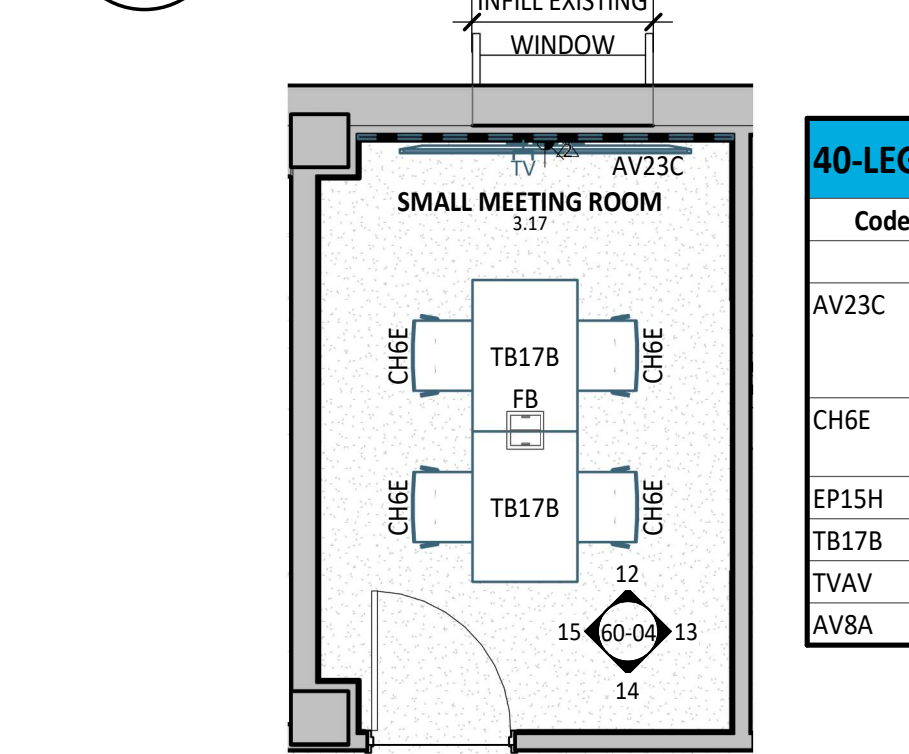

11 PLAN DETAIL 1 : 50

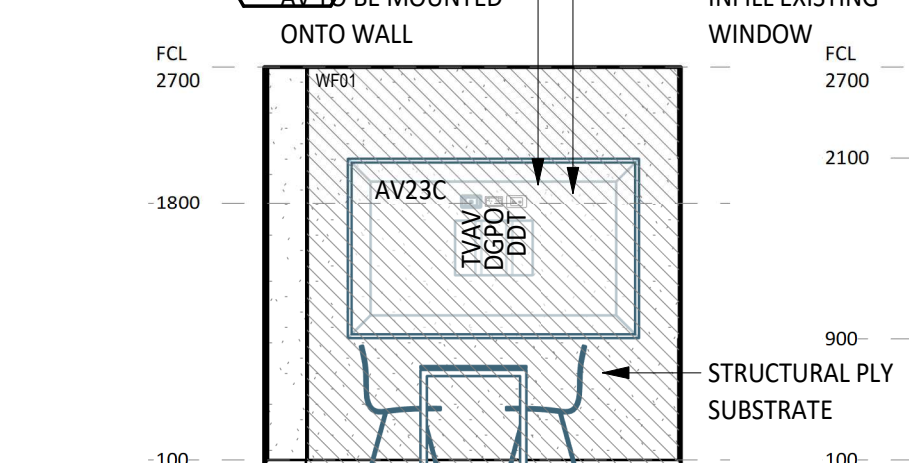


12 ELEVATION DETAIL 1 : 50

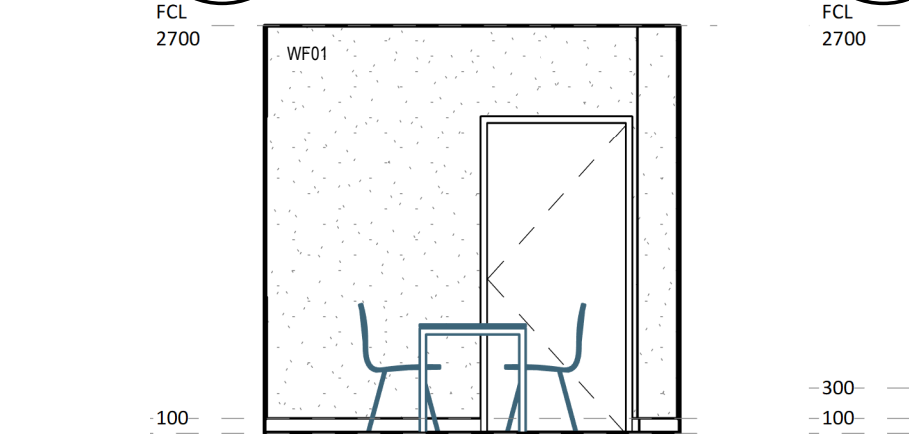


14 ELEVATION DETAIL 1 : 50




3 ELEVATION DETAIL 1 : 50

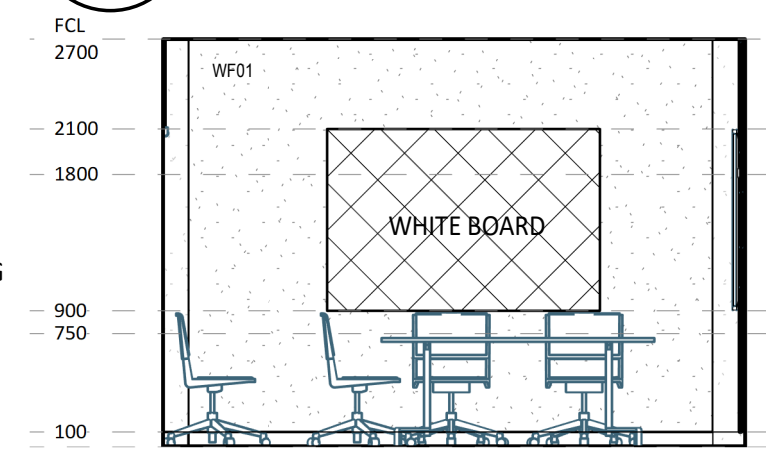


5 ELEVATION DETAIL 1 : 50

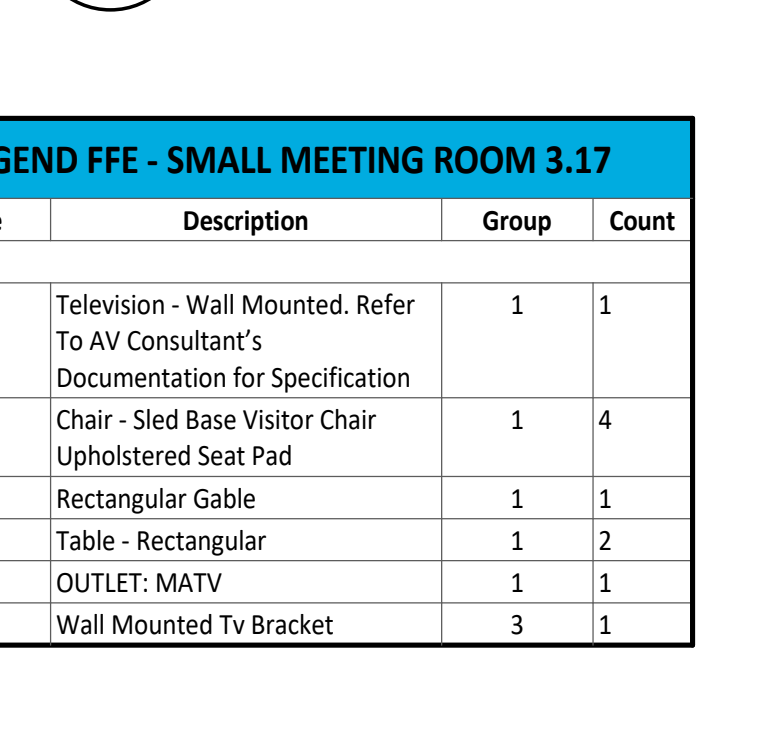

13 ELEVATION DETAIL 1 : 50

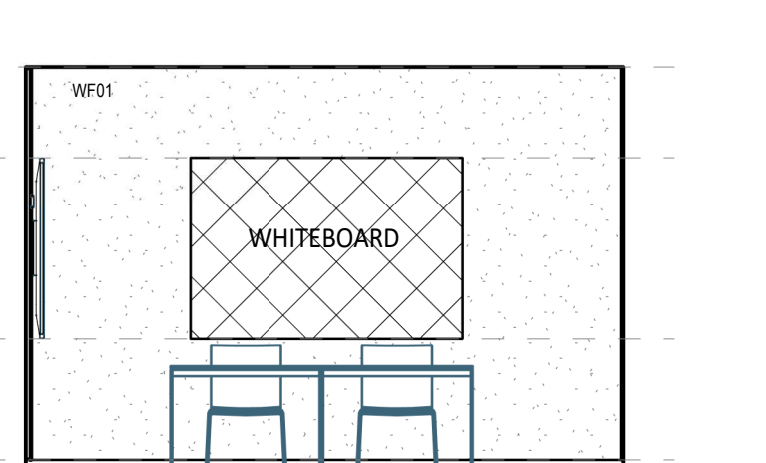

15 ELEVATION DETAIL 1 : 50

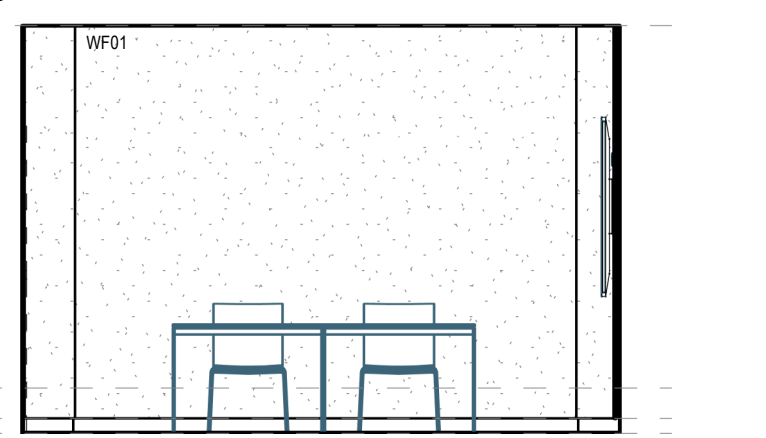

15 ELEVATION DETAIL 1 : 50




MEETING ROOM


40-LEGEND FFE - MEETING

Code	Description	Group	Count
AV23C	Television - Wall Mounted. Refer To AV Consultant's Documentation for Specification	1	1
CH4A	Chair - Conference Room With Arms	1	12
CL8A	Single See Through Blind	1	2
CL8C	Single Block Out Blind	1	1
TB13B	Table - Meeting	1	4
TVAV	OUTLET: MATV	1	1
AV8A	Wall Mounted Tv Bracket	3	1


6 PLAN DETAIL 1 : 50

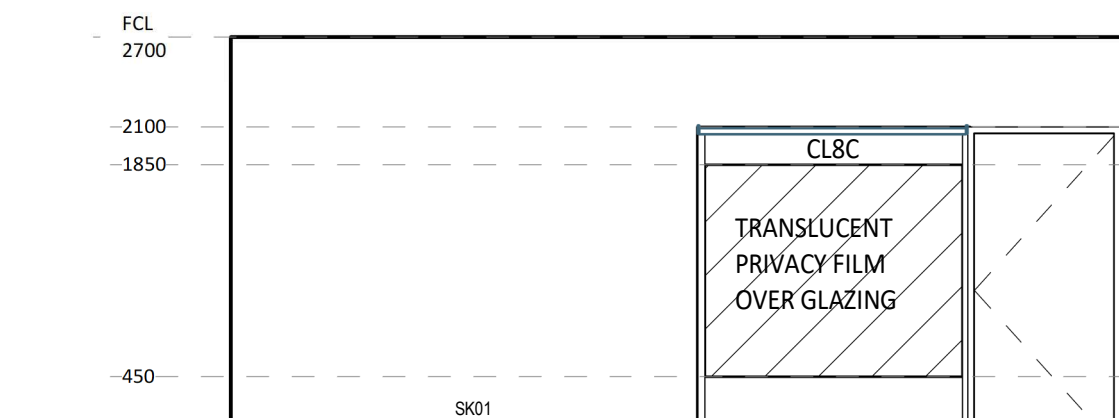


7 ELEVATION DETAIL 1 : 50

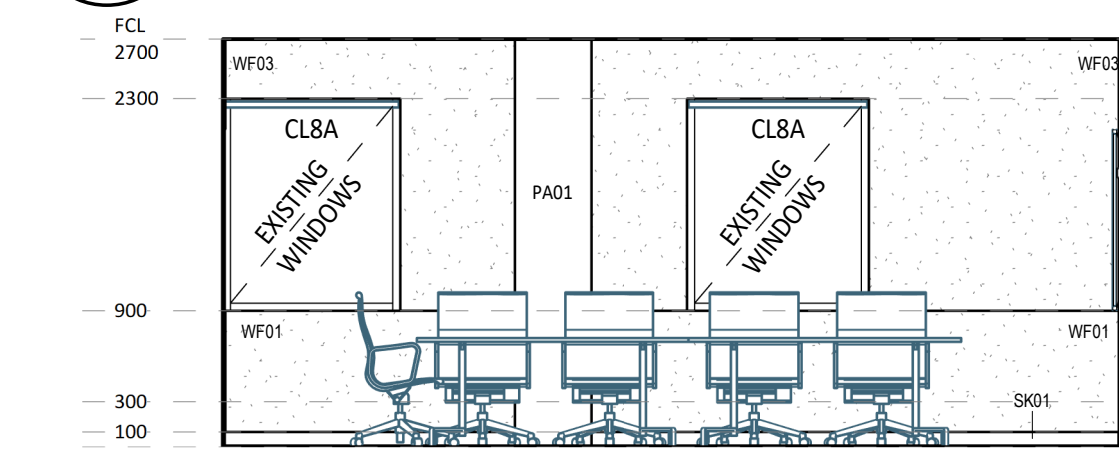


9 ELEVATION DETAIL 1 : 50

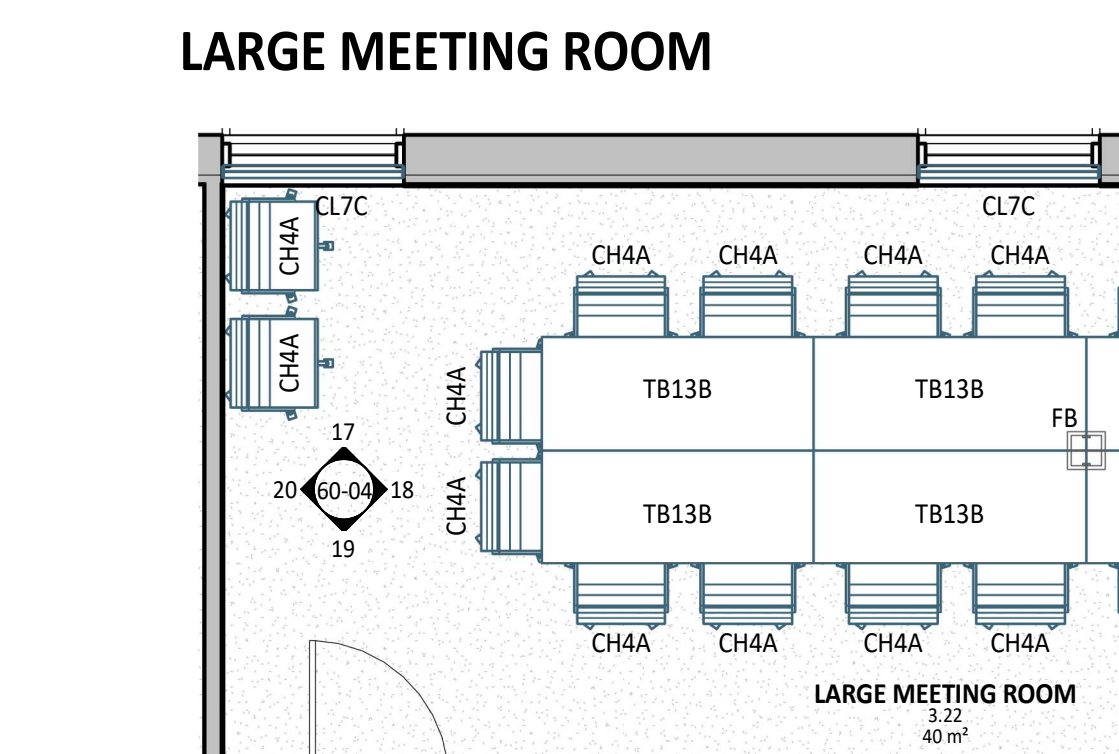

16 PLAN DETAIL 1 : 50

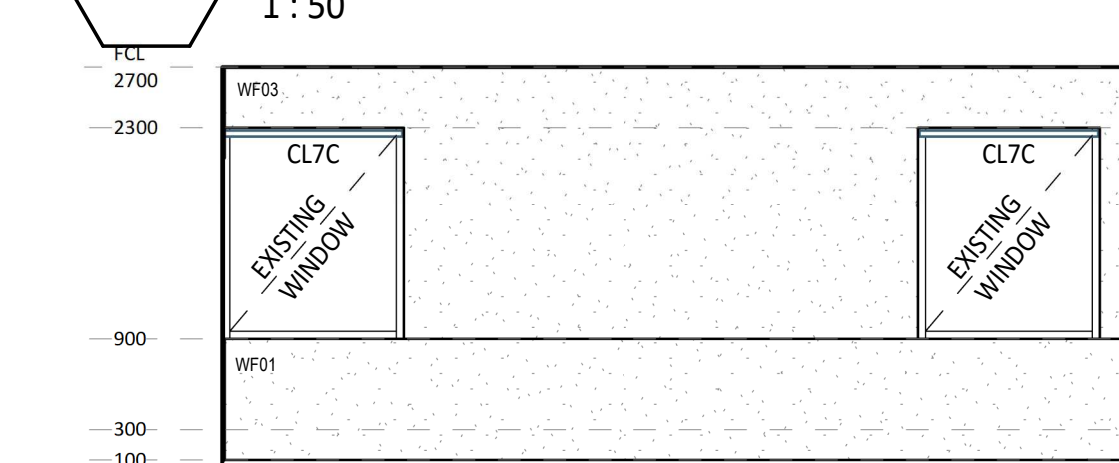


17 ELEVATION DETAIL 1 : 50

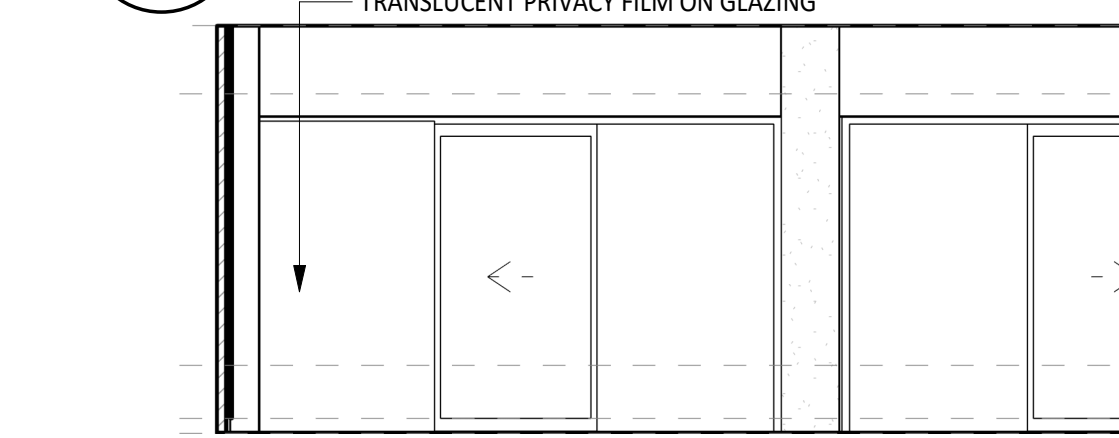


19 ELEVATION DETAIL 1 : 50




8 ELEVATION DETAIL 1 : 50

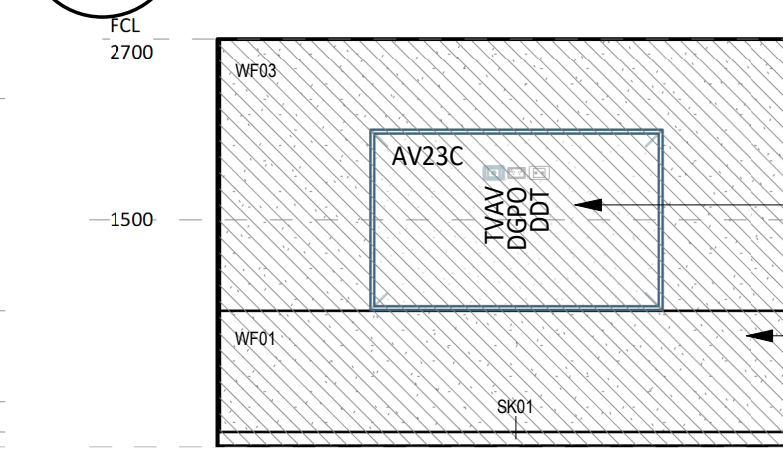


10 ELEVATION DETAIL 1 : 50

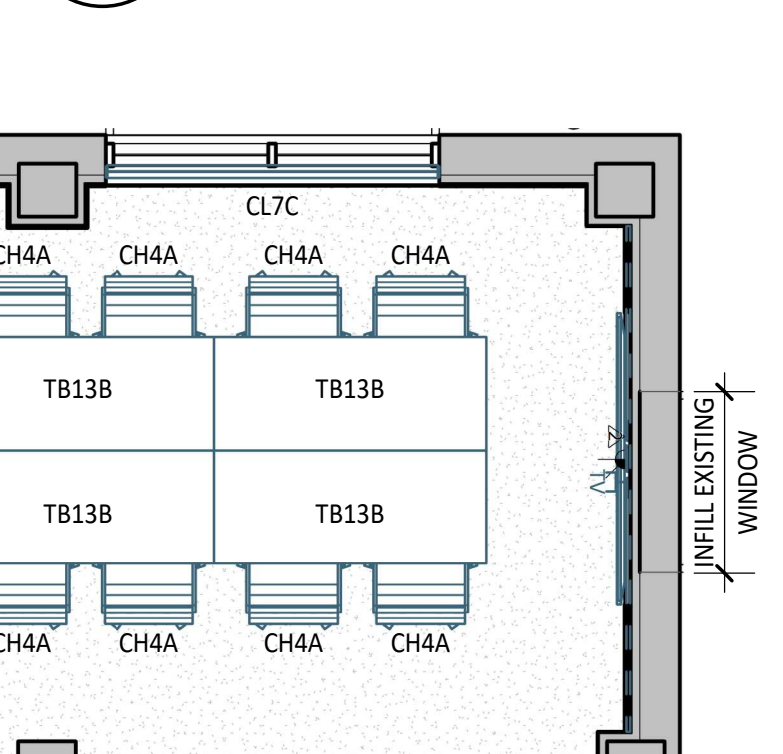

16 PLAN DETAIL 1 : 50

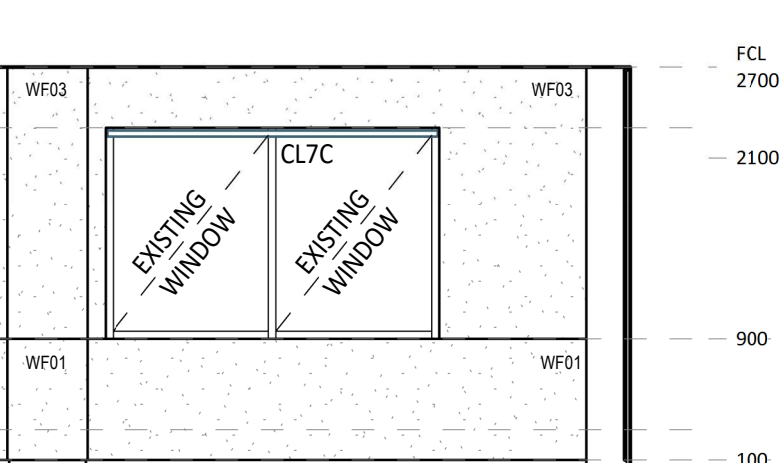

17 ELEVATION DETAIL 1 : 50

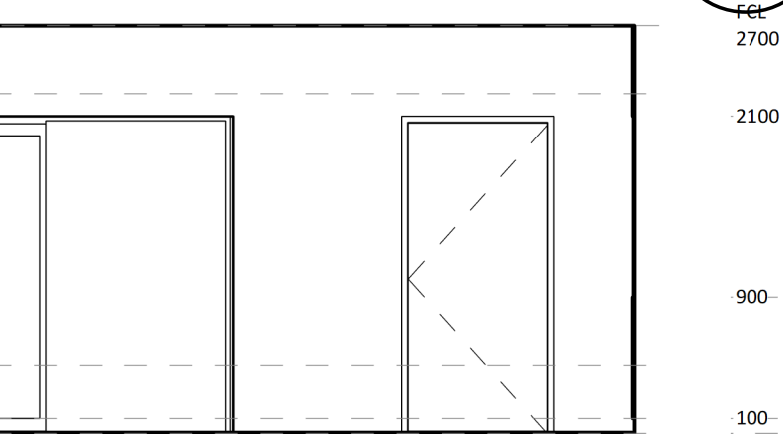

19 ELEVATION DETAIL 1 : 50




LARGE MEETING ROOM


40-LEGEND FFE - LARGE MEETING...

Code	Description	Group	Count
AV23C	Television - Wall Mounted. Refer To AV Consultant's Documentation for Specification	1	1
CH4A	Chair - Conference Room With Arms	1	20
CL7C	Double Roller Blinds - Blockout	1	3
EP15H	Rectangular Gable	1	1
TB13B	Table - Meeting	1	8
TVAV	OUTLET: MATV	1	1
AV8A	Wall Mounted Tv Bracket	3	1

16 PLAN DETAIL 1 : 50

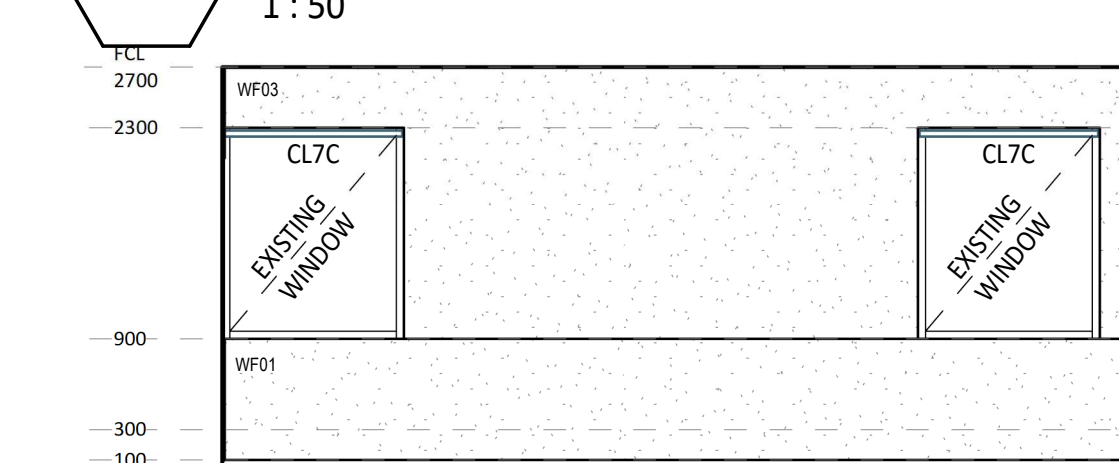


17 ELEVATION DETAIL 1 : 50

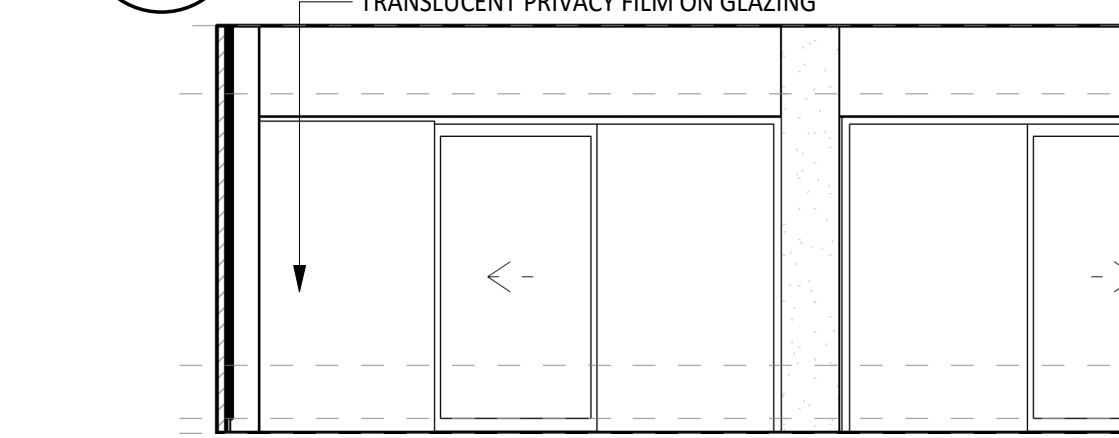


19 ELEVATION DETAIL 1 : 50



16 PLAN DETAIL 1 : 50

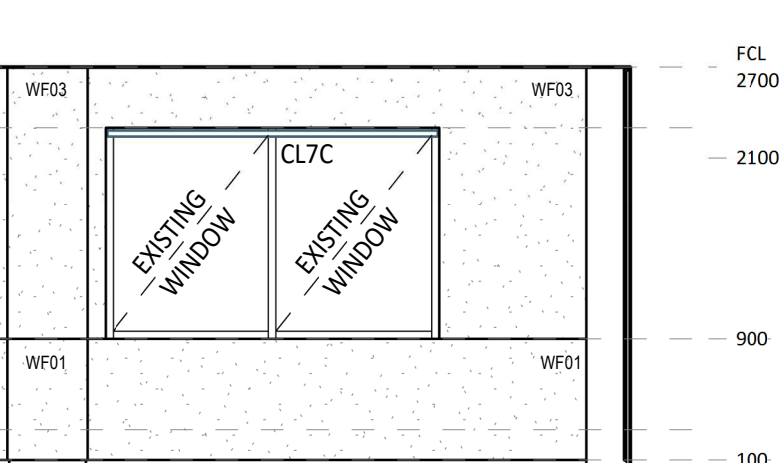


17 ELEVATION DETAIL 1 : 50

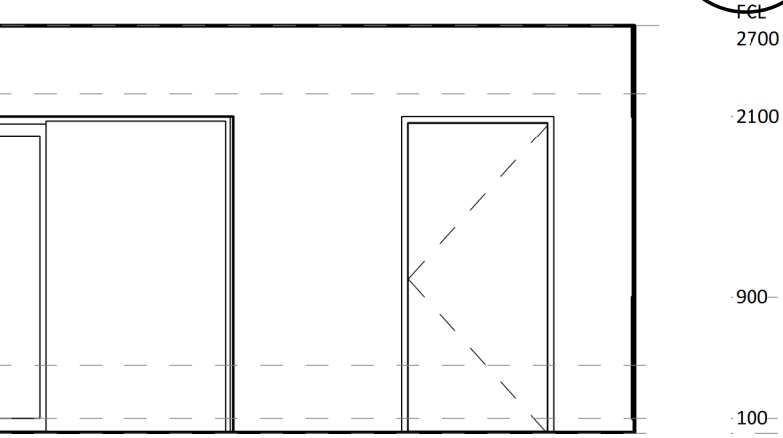


19 ELEVATION DETAIL 1 : 50



16 PLAN DETAIL 1 : 50

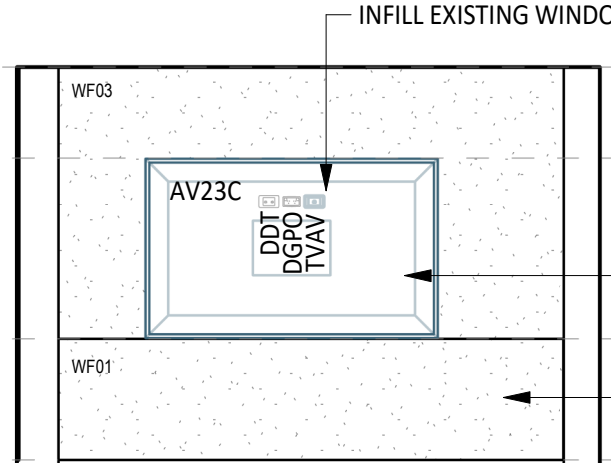


17 ELEVATION DETAIL 1 : 50

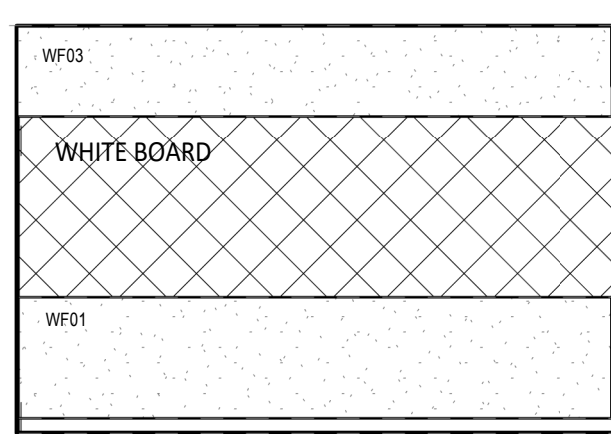


19 ELEVATION DETAIL 1 : 50




ISSUE FOR TENDER

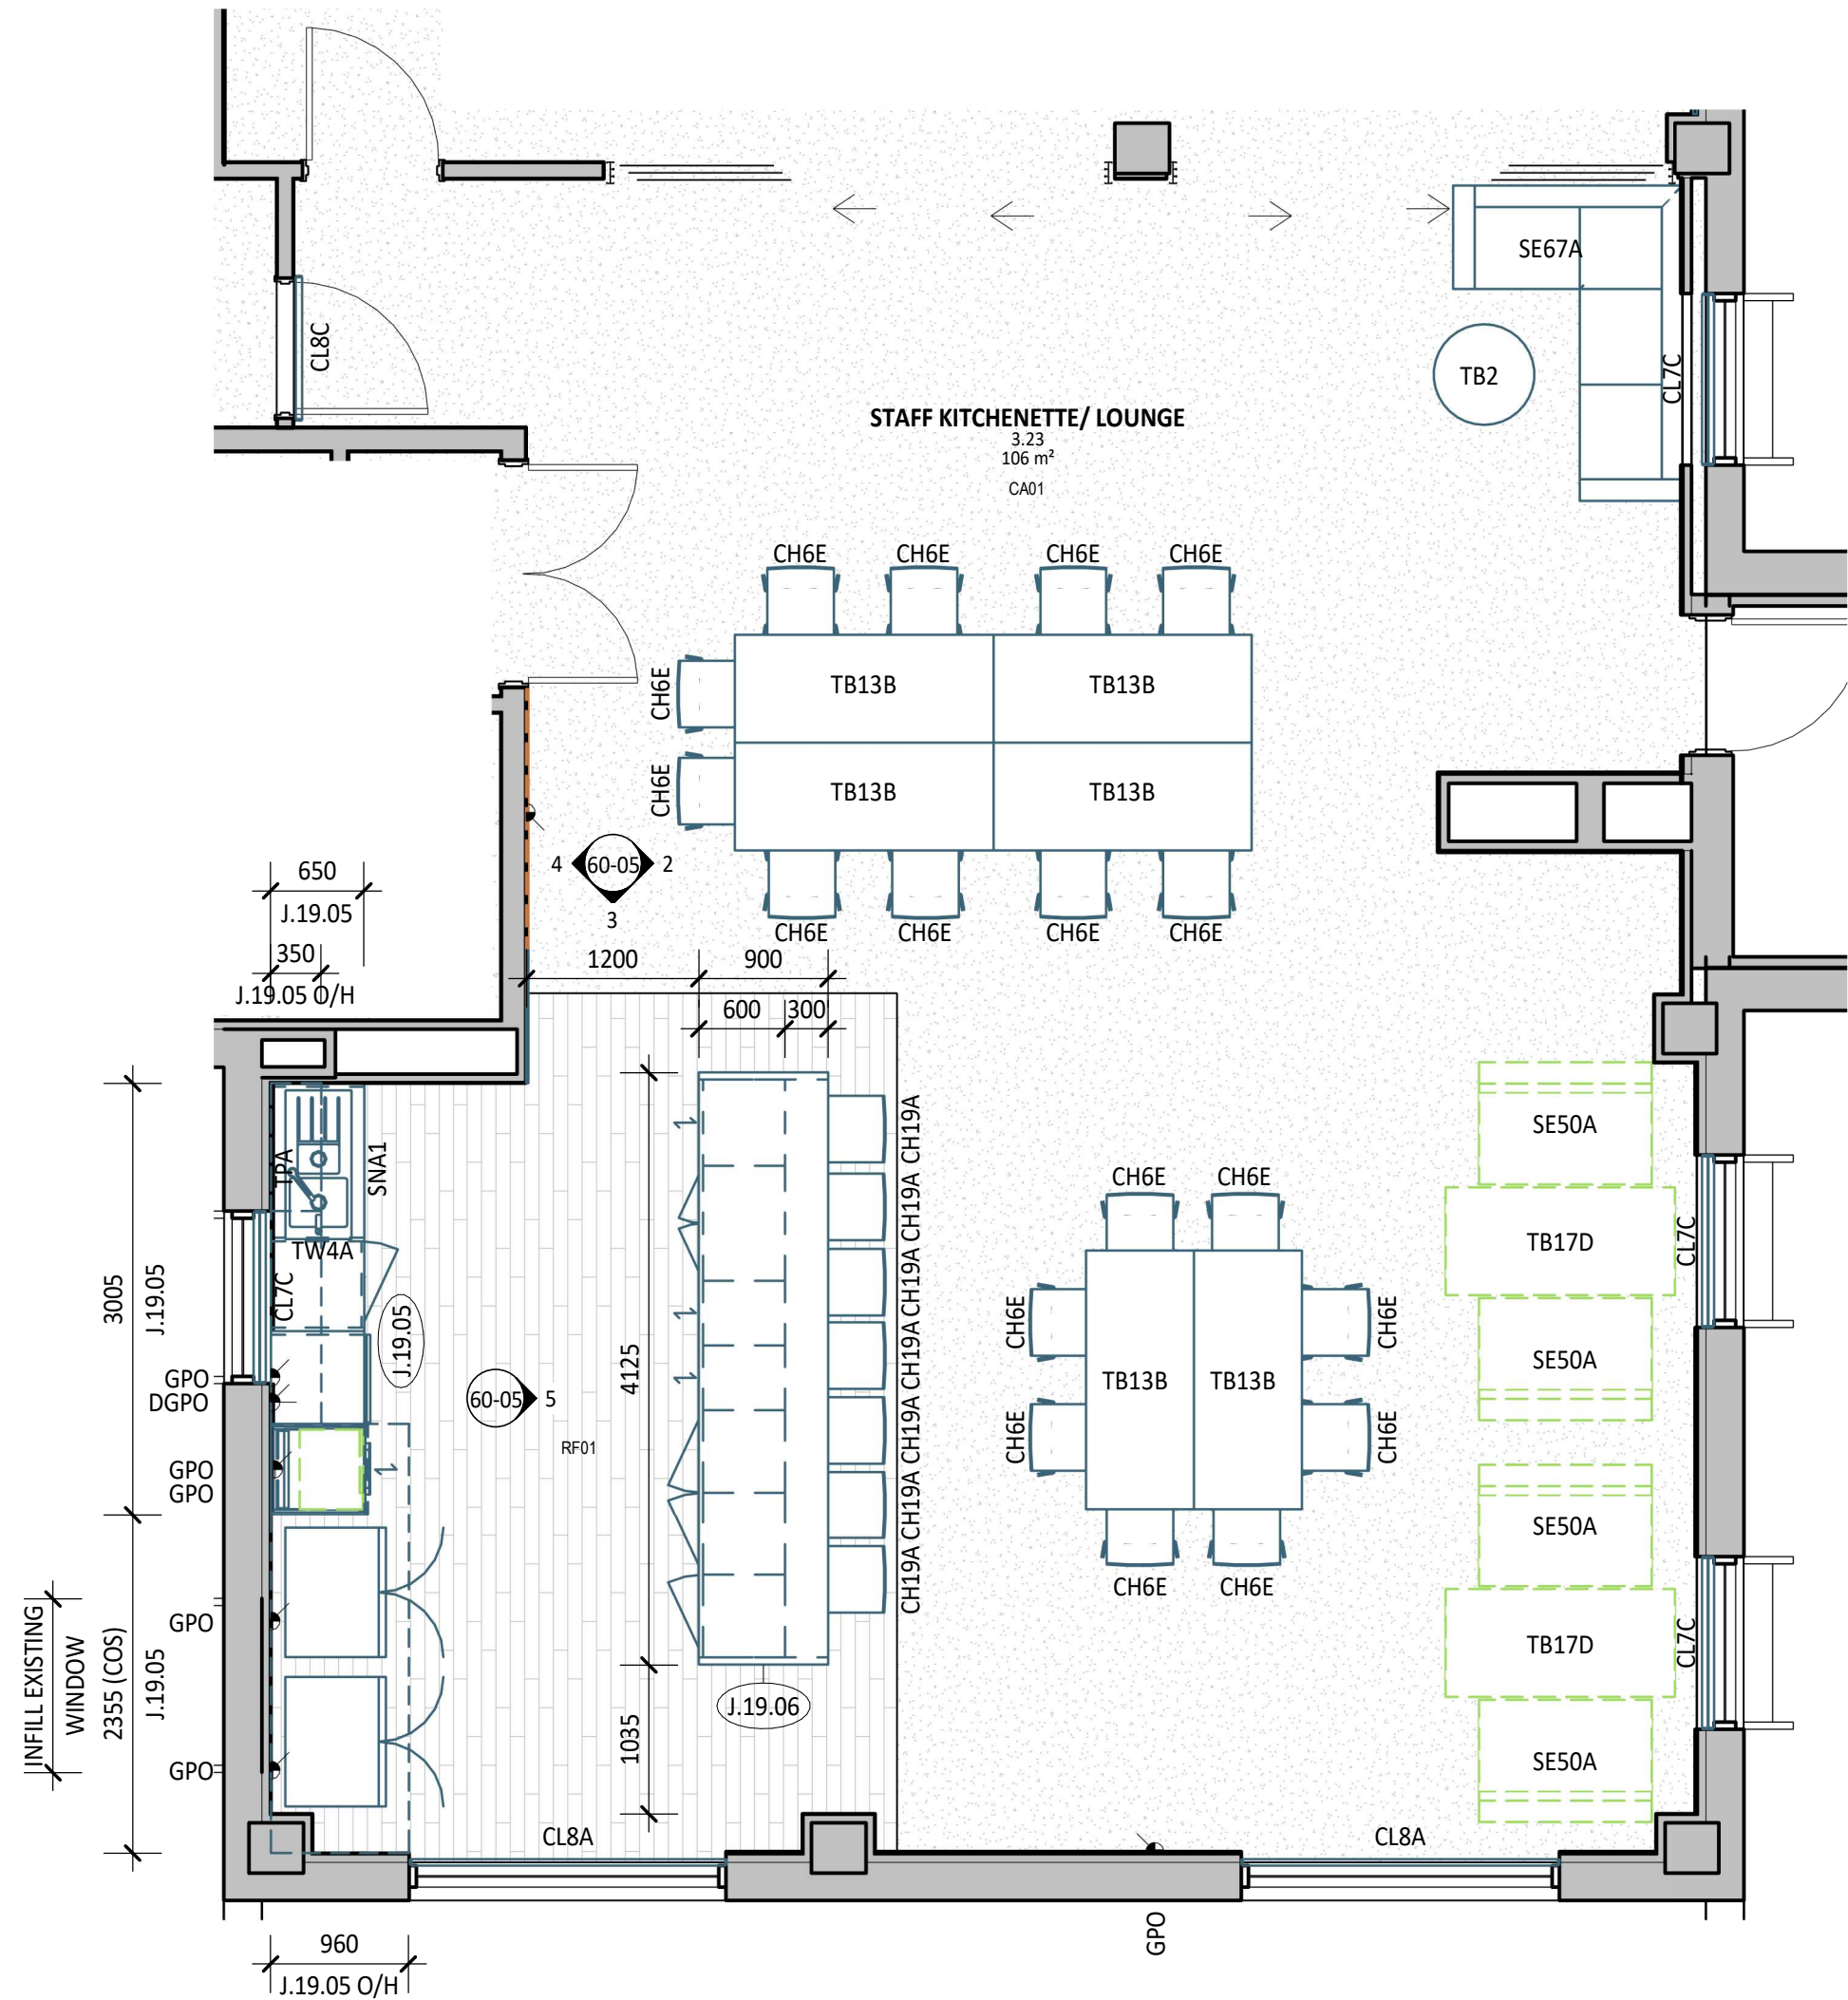

1 PLAN DETAIL
1 : 50

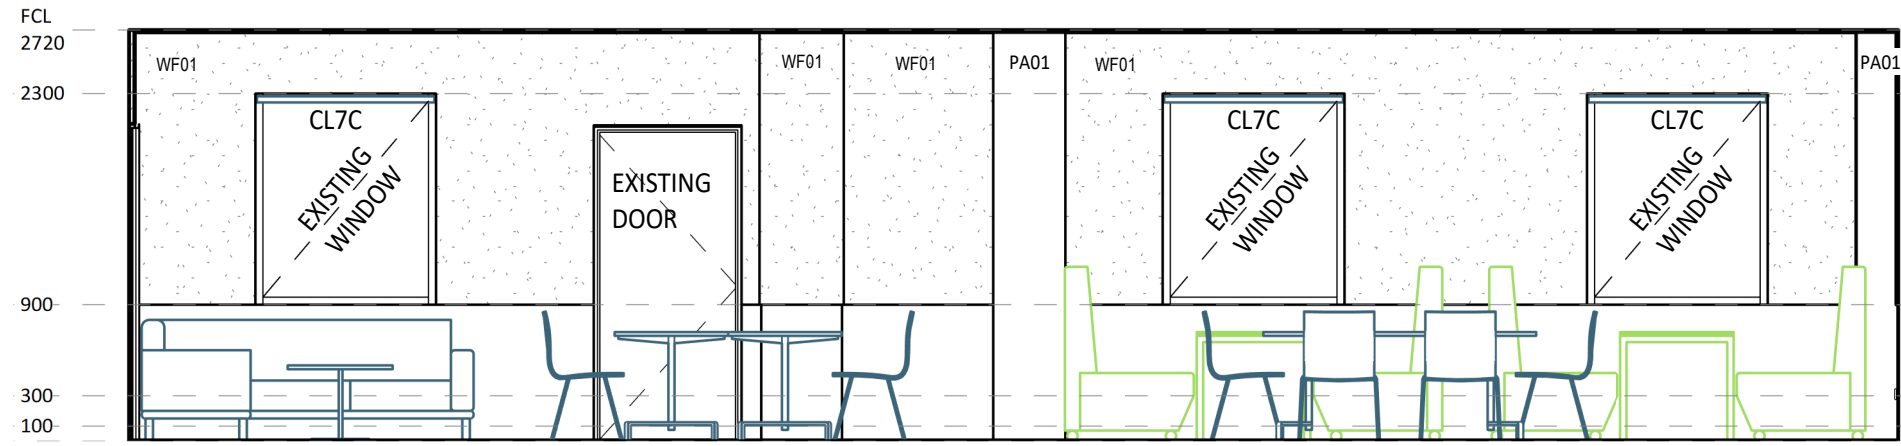


2 ELEVATION DETAIL
1 : 50

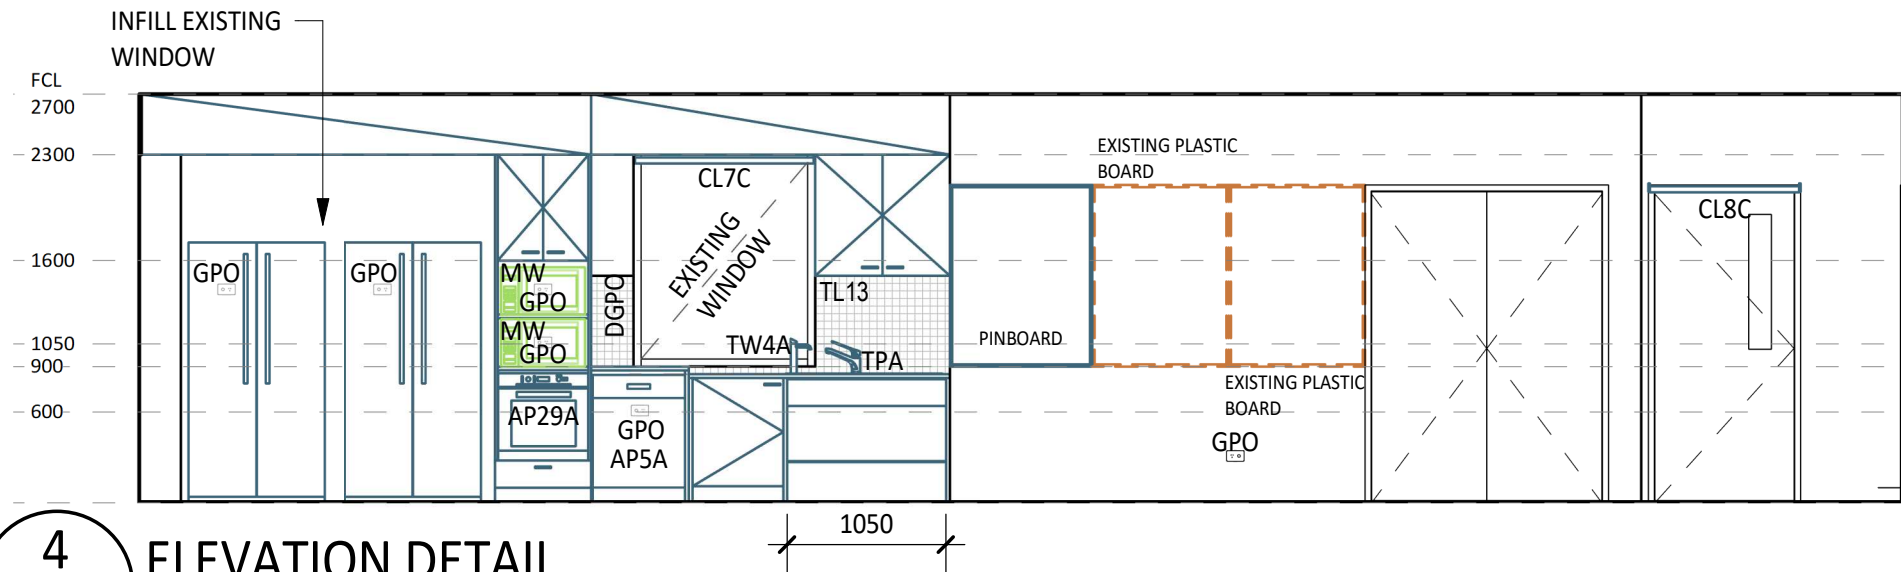


4 ELEVATION DETAIL
1 : 50

40-LEGEND FFE - STAFF KITCHENETTE/ LOUNGE			
Code	Description	Group	Count
APSA	Dishwasher	1	1
AP17D	Refrigerator - Freezer Above	1	2
AP29A	Oven - Built-in	1	1
CH6E	Chair - Sled Base Visitor Chair Upholstered Seat Pad	1	18
CH19A	Chair - Stool Moulded With Sled Base	1	7
CL7C	Double Roller Blinds - Blockout	1	3
CL8A	Single See Through Blind	1	2
CL8C	Single Block Out Blind	1	1
SE67A	Lounge - L Shaped With Siderests	1	1
SNA1	Sink - Accessible	1	1
TB2	Table - Round Low Height	1	1
TB13B	Table - Meeting	1	6
TPA	Mixer - Sink Accessible	1	1
TW4A	Tapware - Hot and Cold Water Boiling Unit	1	1
MW	Microwave	3	2
SE50A	Lounge - Straight Ottomans	3	4
TB17D	Table - Rectangular	3	2

60-LEGEND JOINERY - BUILDING 19 - STAFF KITCHENETTE/LOUNGE	
FFE_Mark	Comments
J.19.05	Kitchen benchtops, underbench cupboards, dda knee clearance, 1.5 sinks, zip tap, tap, dishwasher, oven and microwaves stack tower, tiles splashbacks, overhead cupboards, and bulkhead
J.19.06	Kitchen Benctops, gables, underbench drawers, underbench bins, underbenchcupboards

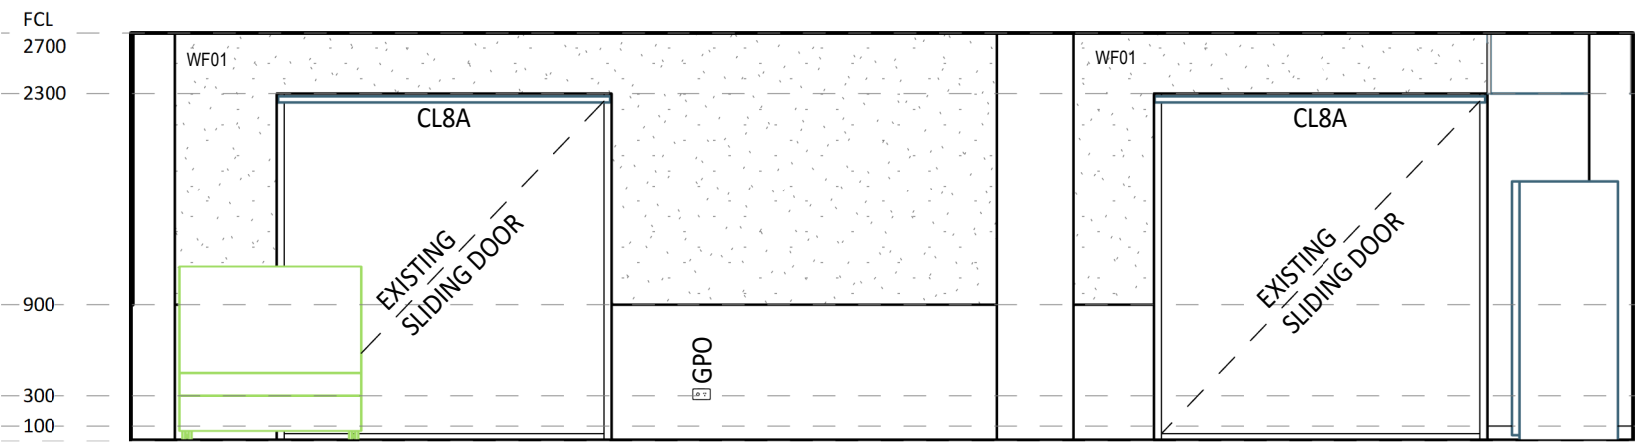

3 ELEVATION DETAIL
1 : 50

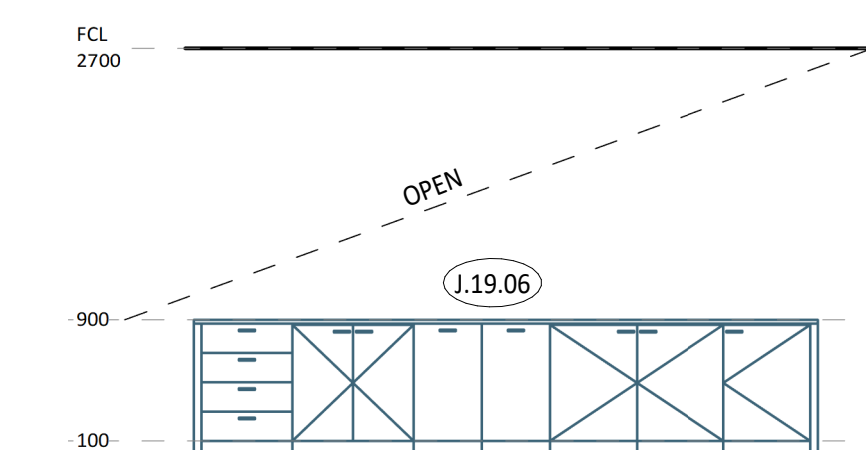

5 ELEVATION DETAIL
1 : 50

- RLS NOTES
1. ALL ARCHITECTURAL DRAWINGS TO BE READ IN CONJUNCTION WITH OTHER DISCIPLINES.

2. REFER TO FF&E, SANITARYWARE SCHEDULES FOR ALL FURNITURE, FIXTURES, AND EQUIPMENT.

3. REFER TO HYDRAULIC ENGINEER'S DRAWINGS FOR HYDRAULIC SERVICES. FINISH OF VALVE/BOX COVERS TO MATCH ADJACENT WALL/JOINERY FINISH.

4. REFER TO ELECTRICAL DOCUMENTATION FOR OUTLET DETAILS (ie. POWER, DATA, COMMS etc.)

5. REFER TO AUDIO VISUAL DOCUMENTATION (VideoPro) FOR AV REQUIREMENTS AND DETAILS.

6. AV SUPPLIER TO CONFIRM EXACT POSITIONS OF EQUIPMENT ON SITE

7. ALL FF&E ITEMS ARE TO BE READ IN CONJUNCTION WITH FF&E SCHEDULES AND CQU DESIGN MANUAL.

8. ALL FF&E AND TRANSFER ITEMS TO BE REVIEWED AND CONFIRMED WITH CLIENT PRIOR TO COMMENCING ON SITE.

9. PROVIDE ALLOWANCE AND ADD SUPPORT TO WALLS, WHERE FITTINGS ARE WALL MOUNTED. THIS INCLUDES BUT NOT LIMITED TO HANDBASINS, HANDRAILS, SCREENS, PROJECTORS, etc.

10. FF&E COUNT IS FOR INFORMATION ONLY. THE TOTAL NUMBER OF FF&E ITEMS ARE TO BE CONFIRMED WITH CLIENT AND ARCHITECTS BEFORE PURCHASE OF ITEMS.

11. CONFIRM ALL DIMENSIONS ON SITE FOR JOINERY ITEMS.

12. ALL SANITARY FIXINGS & FIXTURES IN PWD TOILETS TO BE INSTALLED IN ACCORDANCE WITH AS1428.1

13. ALLOW FOR FIRE EXTINGUISHERS & FIRE BLANKETS AS PER AS2444.2001

14. POWER AND DATA POINTS SHOWN ON THE ROOM LAYOUT SHEETS WERE SHOWN AND DISCUSSED DURING USER GROUP BRIEFING. THESE RELATE TO PARTICULAR EQUIPMENT THAT WAS DISCUSSED AS REQUIRING POWER AND DATA. THESE REFLECT STAKEHOLDER EXPECTATIONS FOR SPECIFIC POWER AND DATA POINTS AND HAVE REMAINED IN THE DOCUMENTATION AS A USEFUL REFERENCE FOR THE CONTRACTOR. THESE ARE NOT A COMPLETE QUANTITY AND SPECIFICATION OF POWER AND DATA. THE CONTRACTOR IS TO REFER TO ELECTRICAL ENGINEER'S DOCUMENTATION FOR ALLOWANCE. REFER TO ELECTRICAL DOCUMENTATION FOR AMPS AND 3 PHASE POWER REQUIREMENTS. REFER TO AUDIO VISUAL (VIDEOPRO) DOCUMENTATION FOR ADDITIONAL POWER AND DATA REQUIREMENTS

15. ALLOW FOR STRUCTURAL PLY BACKING BEHIND PLASTERBOARD FOR FULL EXTENT OF WALLS WITH MOUNTED AUDIO VISUAL EQUIPMENT. REFER TO AUDIO VISUAL (VIDEOPRO) DOCUMENTATION FOR LOCATIONS OF WALL MOUNTED EQUIPMENT.

16. ALLOW FOR PRIVACY FILM TO ALL INTERNAL GLAZING (DOORS AND WINDOWS) TO OFFICES AND MEETING ROOMS. CONFIRM SET OUT PRIOR TO INSTALLATION

17. ALLOW FOR DOUBLE BLOCK OUT BLINDS TO ALL WINDOWS UNLESS NOTED OTHERWISE

18. ALL INTERNAL DOORS ARE TO BE SOLID CORE DOORS WITHIN ALUMINIUM FRAMED SUITES UNLESS NOTED OTHERWISE.

19. FLOOR BOXES MUST BE COORDINATED WITH BOTH THE STRUCTURAL AND ELECTRICAL ENGINEERS. BEFORE ANY CUTTING OF THE EXISTING SLAB OCCURS, CONFIRM THE EXACT LOCATIONS AND REQUIREMENTS WITH THE STRUCTURAL ENGINEER.

20. HEARING AUGMENTATION TO AUSTRALIAN STANDARDS – REFER VIDEOPRO AND ELECTRICAL SPECIFICATION

FF&E LEGEND	
	GROUP 1 ITEMS (PROVIDED & FITTED UNDER CONTRACT)
	GROUP 2 ITEMS (PROVIDED BY CLIENT & FITTED UNDER CONTRACT)
	GROUP 2T ITEMS - EXISTING EQUIPMENT (PROVIDED BY CLIENT & FITTED UNDER CONTRACT)
	GROUP 3 ITEMS (PROVIDED & INSTALLED BY CLIENT)
PLANS TO BE PRINTED IN COLOUR	
SCH_Code	FF&E TAG
	JOINERY TAG

ELECTRICAL LEGEND	
	SINGLE POWER OUTLET
	DOUBLE POWER OUTLET
	SINGLE DATA
	DOUBLE DATA
	LIGHT SWITCH
	TV
	FLOOR BOX (FB)
REFER TO ELECTRICAL ENGINEER'S DRAWINGS FOR DETAILS	

thomson
adsett

PEDDLE THORP
architecture | interiors | health | planning

Telephone +61 7 3840 9999
bne@thomsonadsett.com
Level 9, 470 St Pauls Terrace
Fortitude Valley
Qld 4006 Australia
thomsonadsett.com

© Copyright
These drawings and designs and the copyright thereof are the property of Thomson Adsett Pty Ltd and must not be used, retained or copied without written permission of Thomson Adsett Pty Ltd. AEN 76 105 314 654 Trading as ThomsonAdsett. Dimensions take precedence over scaling. Do not measure off drawings as print sizes may vary


CQU ROCKHAMPTON
TAFE
CONSOLIDATION -
STAGE 2

554/700 Yaamba Rd, Norman
Gardens QLD 4701



A	12/02/26	ISSUED FOR TENDER	SM
2	30/01/26	60% DRAFT ISSUE	SM
1	23/01/26	FOR COORDINATION ISSUE	SM
rev	date	details	init.

drawn	date
TA/PT	19/12/25
checked	date
JT/RJ	19/12/25
verified	date
JT/RJ	19/12/25

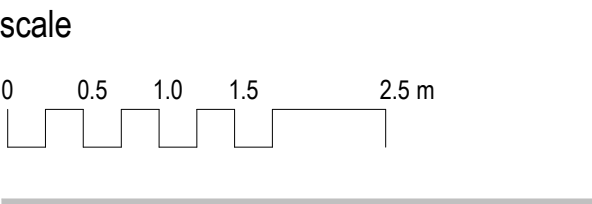

RLS - BLD19-L3 - STAFF KITCHENETTE & LOUNGE

scale
1 : 50 @ A1

revision
A

project no.
260018

sheet no.
CQU-ROK-019-03-ARC-60-05

ISSUE FOR TENDER

© Copyright

These drawings and designs and the copyright thereof are the property of Thomson Adsett Pty Ltd and must not be used, retained or copied without written permission of Thomson Adsett Pty Ltd. ABN 76 105 314 654 Trading as ThomsonAdsett. Dimensions take precedence over scaling. Do not measure off drawings as print sizes may vary

CQU ROCKHAMPTON TAFE CONSOLIDATION - STAGE 2

554/700 Yaamba Rd, Norman
Gardens QLD 4701

for



RLS NOTES

1. ALL ARCHITECTURAL DRAWINGS TO BE READ IN CONJUNCTION WITH OTHER DISCIPLINES.
2. REFER TO FF&E, SANITARYWARE SCHEDULES FOR ALL FURNITURE, FIXTURES, AND EQUIPMENT.
3. REFER TO HYDRAULIC ENGINEER'S DRAWINGS FOR HYDRAULIC SERVICES. FINISH OF VALVE/BOX COVERS TO MATCH ADJACENT WALL/JOINERY FINISH.
4. REFER TO ELECTRICAL DOCUMENTATION FOR OUTLET DETAILS (ie. POWER, DATA, COMMS etc.)
5. REFER TO AUDIO VISUAL DOCUMENTATION (VideoPro) FOR AV REQUIREMENTS AND DETAILS.
6. AV SUPPLIER TO CONFIRM EXACT POSITIONS OF EQUIPMENT ON SITE
7. ALL FF&E ITEMS ARE TO BE READ IN CONJUNCTION WITH FF&E SCHEDULES AND CQU DESIGN MANUAL.
8. ALL FF&E AND TRANSFER ITEMS TO BE REVIEWED AND CONFIRMED WITH CLIENT PRIOR TO COMMENCING ON SITE.
9. PROVIDE ALLOWANCE AND ADD SUPPORT TO WALLS, WHERE FITTINGS ARE WALL MOUNTED. THIS INCLUDES BUT NOT LIMITED TO HANDBASINS, HANDRAILS, SCREENS, PROJECTORS, etc.
10. FF&E COUNT IS FOR INFORMATION ONLY. THE TOTAL NUMBER OF FF&E ITEMS ARE TO BE CONFIRMED WITH CLIENT AND ARCHITECTS BEFORE PURCHASE OF ITEMS.
11. CONFIRM ALL DIMENSIONS ON SITE FOR JOINERY ITEMS.
12. ALL SANITARY FIXINGS & FIXTURES IN PWD TOILETS TO BE INSTALLED IN ACCORDANCE WITH AS1428.1
13. ALLOW FOR FIRE EXTINGUISHERS & FIRE BLANKETS AS PER AS2444.2001
14. POWER AND DATA POINTS SHOWN ON THE ROOM LAYOUT SHEETS WERE SHOWN AND DISCUSSED DURING USER GROUP BRIEFING. THESE RELATE TO PARTICULAR EQUIPMENT THAT WAS DISCUSSED AS REQUIRING POWER AND DATA. THESE REFLECT STAKEHOLDER EXPECTATIONS FOR SPECIFIC POWER AND DATA POINTS AND HAVE REMAINED IN THE DOCUMENTATION AS A USEFUL REFERENCE FOR THE CONTRACTOR. THESE ARE NOT A COMPLETE QUANTITY AND SPECIFICATION OF POWER AND DATA. THE CONTRACTOR IS TO REFER TO ELECTRICAL ENGINEER'S DOCUMENTATION FOR ALLOWANCE. REFER TO ELECTRICAL DOCUMENTATION FOR AMPS AND 3 PHASE POWER REQUIREMENTS. REFER TO AUDIO VISUAL (VIDEOPRO) DOCUMENTATION FOR ADDITIONAL POWER AND DATA REQUIREMENTS
15. ALLOW FOR STRUCTURAL PLY BACKING BEHIND PLASTERBOARD FOR FULL EXTENT OF WALLS WITH MOUNTED AUDIO VISUAL EQUIPMENT. REFER TO AUDIO VISUAL (VIDEOPRO) DOCUMENTATION FOR LOCATIONS OF WALL MOUNTED EQUIPMENT.
16. ALLOW FOR PRIVACY FILM TO ALL INTERNAL GLAZING (DOORS AND WINDOWS) TO OFFICES AND MEETING ROOMS. CONFIRM SET OUT PRIOR TO INSTALLATION
17. ALLOW FOR DOUBLE BLOCK OUT BLINDS TO ALL WINDOWS UNLESS NOTED OTHERWISE
18. ALL INTERNAL DOORS ARE TO BE SOLID CORE DOORS WITHIN ALUMINIUM FRAMED SUITES UNLESS NOTED OTHERWISE.
19. FLOOR BOXES MUST BE COORDINATED WITH BOTH THE STRUCTURAL AND ELECTRICAL ENGINEERS. BEFORE ANY CUTTING OF THE EXISTING SLAB OCCURS, CONFIRM THE EXACT LOCATIONS AND REQUIREMENTS WITH THE STRUCTURAL ENGINEER.
20. HEARING AUGMENTATION TO AUSTRALIAN STANDARDS – REFER VIDEOPRO AND ELECTRICAL SPECIFICATION

FF&E LEGEND

- GROUP 1 ITEMS
(PROVIDED & FITTED UNDER CONTRACT)
- GROUP 2 ITEMS
(PROVIDED BY CLIENT & FITTED UNDER CONTRACT)
- GROUP 2T ITEMS - EXISTING EQUIPMENT
(PROVIDED BY CLIENT & FITTED UNDER CONTRACT)
- GROUP 3 ITEMS
(PROVIDED & INSTALLED BY CLIENT)

PLANS TO BE PRINTED IN COLOUR

SCH_Code FF&E TAG
JO.PROC JOINERY TAG

AMENITIES NOTES


- SETOUT DENOTES TILE SETOUT POINT.
MARKER NB: WALL TILES ALIGN WITH FLOOR TILES.
- NOTE: ALL SANITARY FITTINGS AND FIXTURES IN PWD WC INSTALLED IN ACCORDANCE WITH AUSTRALIAN STANDARD AS1428.1
- NOTE: REFER TO SCHEDULES FOR ALL SANITARY FIXTURES AND FITTINGS.
- PROVIDE NOGGINGS IN PARTITION WALLS TO SUPPORT SANITARY FIXTURES AND FITTINGS; INCLUDING IN-WALL CISTERNS, AS REQUIRED.

ELECTRICAL LEGEND

- SINGLE POWER OUTLET
 - DOUBLE POWER OUTLET
 - SINGLE DATA
 - DOUBLE DATA
 - LIGHT SWITCH
 - TV
 - FLOOR BOX (FB)
- REFER TO ELECTRICAL ENGINEER'S DRAWINGS FOR DETAILS

40-LEGEND FFE - SHOWER 93


Code	Description	Group	Count
AR18C	Curtain Rail - Two Sides	1	1
SR8A	Shower - Outlet	1	1

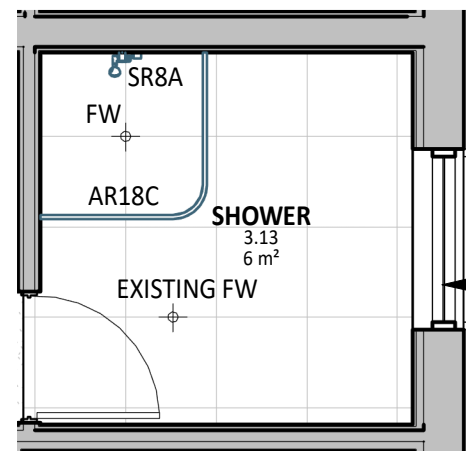PRIVACY FILM
OVER WINDOW

16 PLAN DETAIL
1 : 50

60-LEGEND JOINERY - BUILDING 19 - PWD


FFE_Mark	Comments
J.19.08	Wall Cabinet

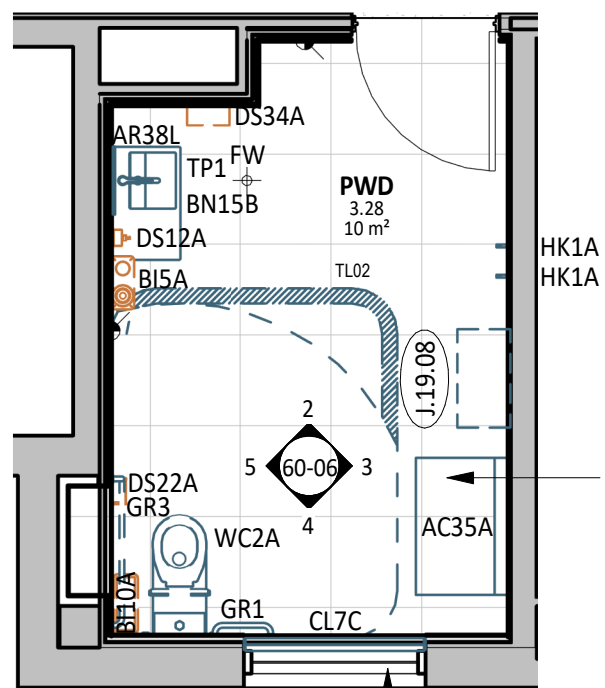


Confirm with the Client the requirement for provision and installation of a baby change table within the PWD sanitary facility

PRIVACY FILM OVER WINDOW


1 PLAN DETAIL
1 : 50

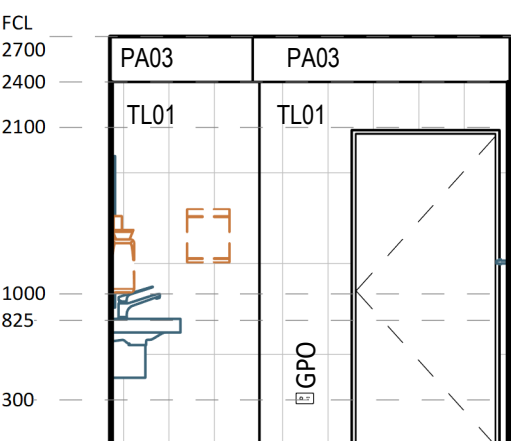


2 ELEVATION DETAIL
1 : 50

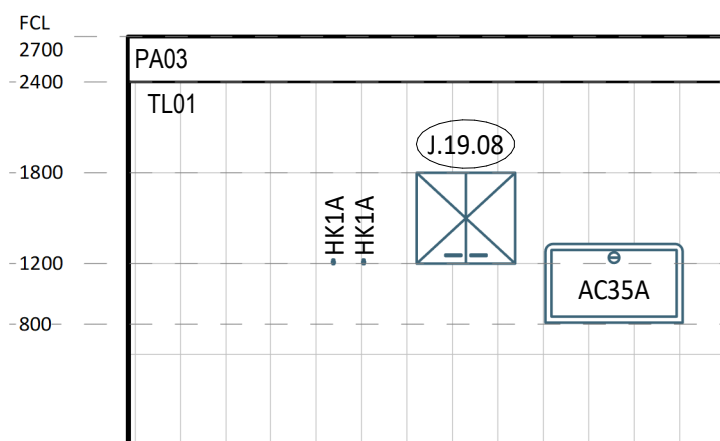


3 ELEVATION DETAIL
1 : 50

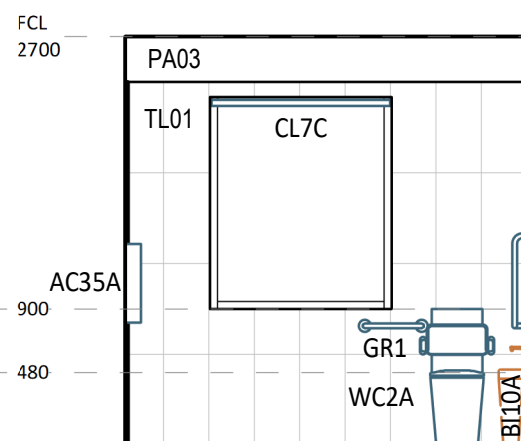

4 ELEVATION DETAIL
1 : 50

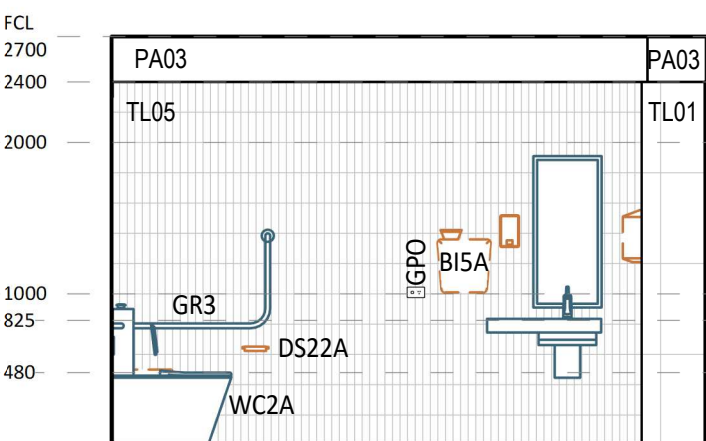

5 ELEVATION DETAIL
1 : 50

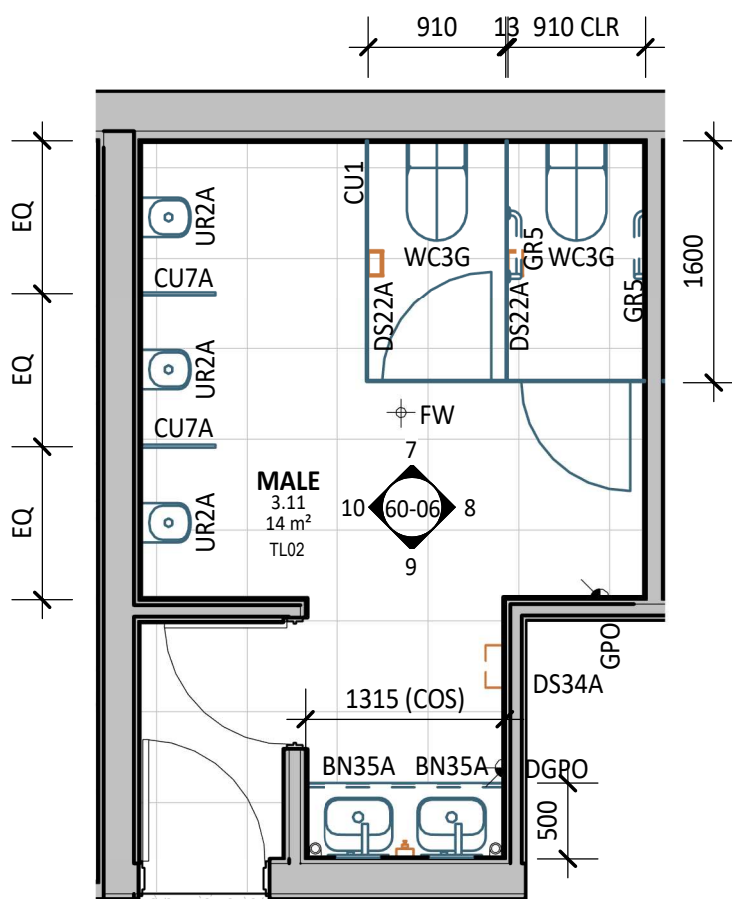


6 PLAN DETAIL
1 : 50

40-LEGEND FFE - MALE 3.11


Code	Description	Group	Count
AR45A	Mirror - Oval	1	2
BN35A	Caroma Luna Inset Basin	1	2
CU1	Cubicles - Toilet Partition	1	2
CU7A	Cubicle - Urinals Privacy Panel	1	2
GR5	Accessible - Grab Rail 90°	1	1
TW9A	Tapware - Wall Mounted Basin Mixer	1	2
UR2A	Urinal - Wall Mounted	1	3
WC3G	Toilets - Concealed Unit	1	2
DS11A	Dispenser - Soap	2	1
DS22A	Dispenser - Toilet Tissue Roll Drop	2	2
DS34A	Dispenser - Paper Hand Towel	2	1

60-LEGEND JOINERY - BUILDING 19 - MALE TOILET


FFE_Mark	Comments
J.19.09	<varies>

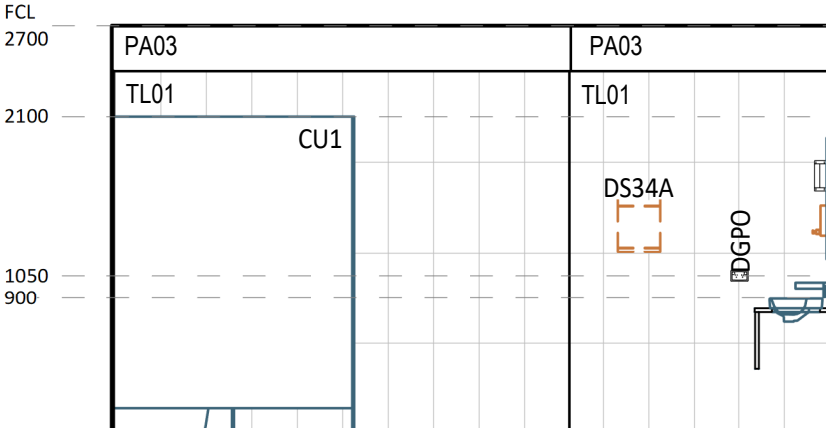


8 ELEVATION DETAIL
1 : 50

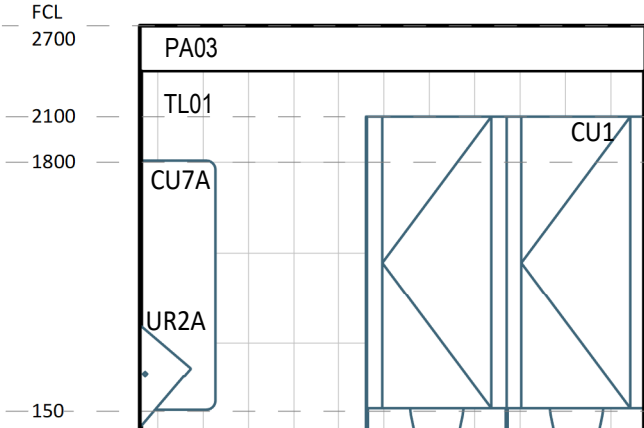


7 ELEVATION DETAIL
1 : 50

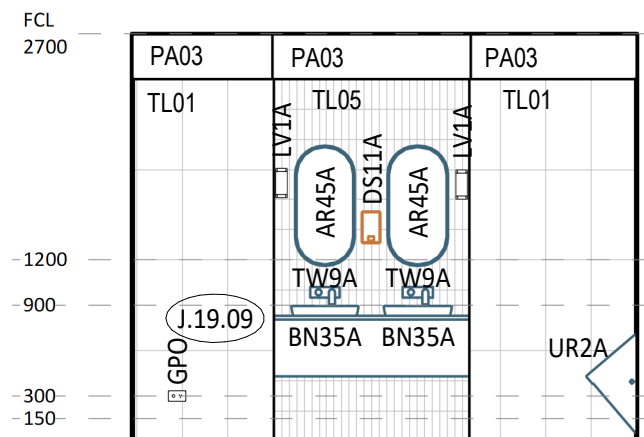

9 ELEVATION DETAIL
1 : 50

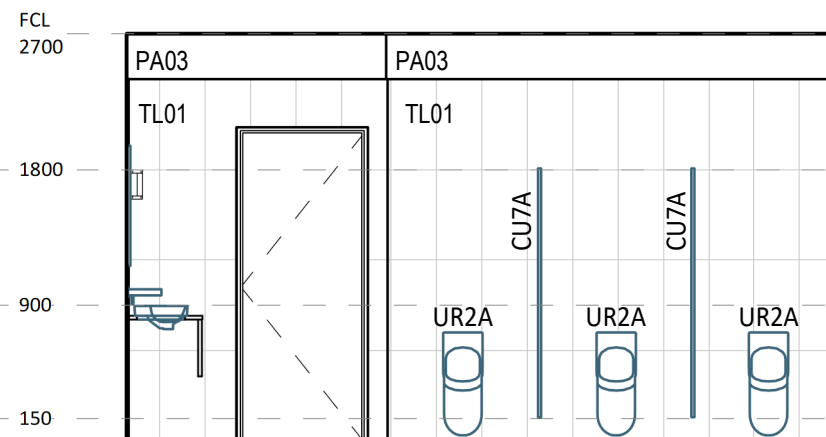

10 ELEVATION DETAIL
1 : 50

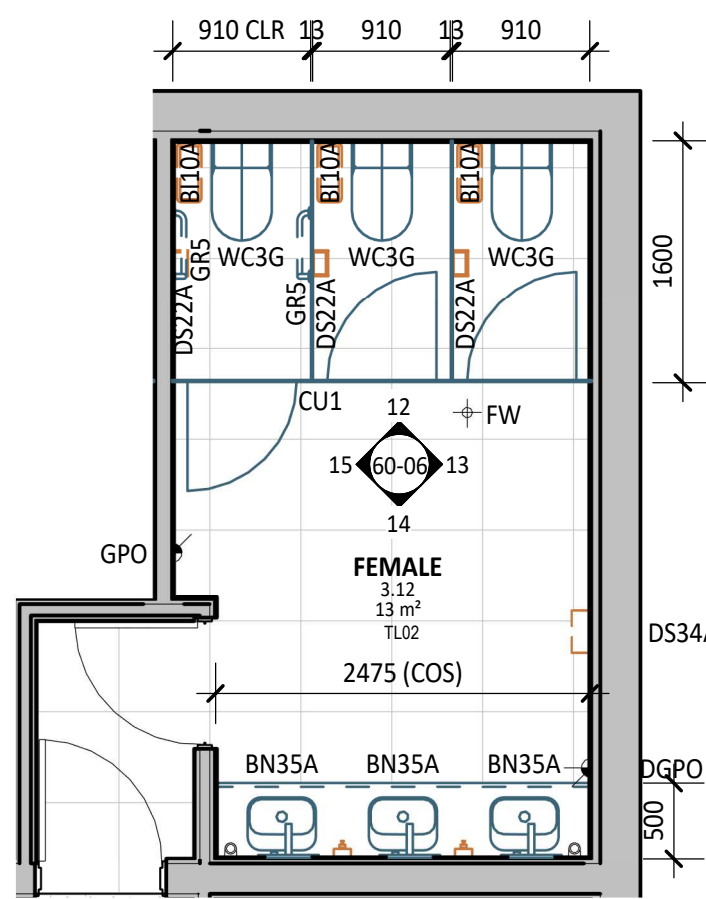


11 PLAN DETAIL
1 : 50

40-LEGEND FFE - FEMALE 3.12


Code	Description	Group	Count
AR45A	Mirror - Oval	1	3
BN35A	Caroma Luna Inset Basin	1	3
CU1	Cubicles - Toilet Partition	1	3
GR5	Accessible - Grab Rail 90°	1	1
TW9A	Tapware - Wall Mounted Basin Mixer	1	3
WC3G	Toilets - Concealed Unit	1	3
BI10A	Bin - Sanitary Waste	2	3
DS11A	Dispenser - Soap	2	2
DS22A	Dispenser - Toilet Tissue Roll Drop	2	3
DS34A	Dispenser - Paper Hand Towel	2	1

60-LEGEND JOINERY - BUILDING 19 - FEMALE TOILET


FFE_Mark	Comments
J.19.10	Female Toilet Wash Basin

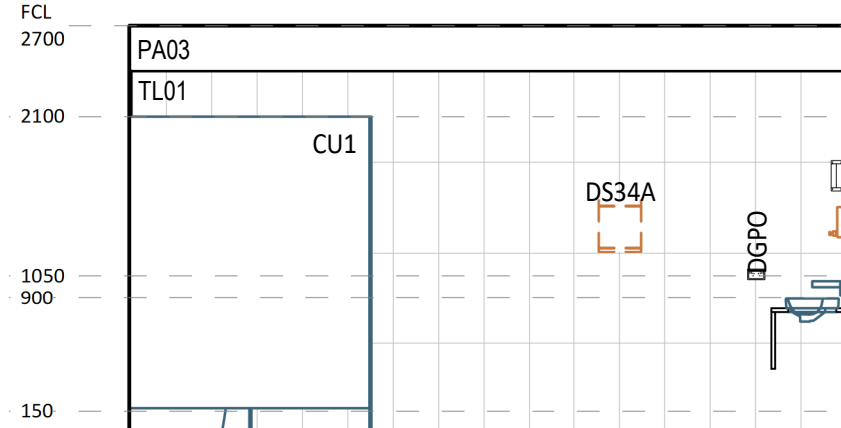


13 ELEVATION DETAIL
1 : 50

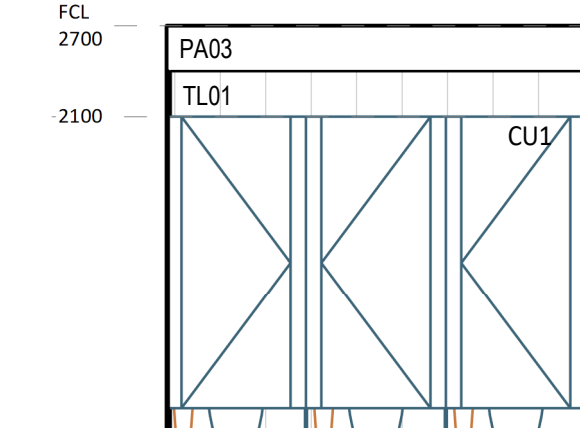

12 ELEVATION DETAIL
1 : 50

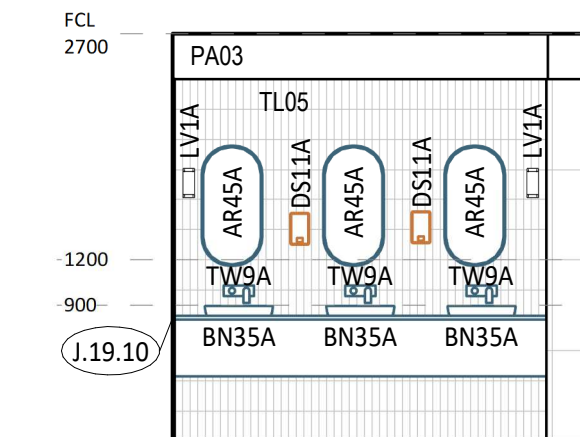

14 ELEVATION DETAIL
1 : 50

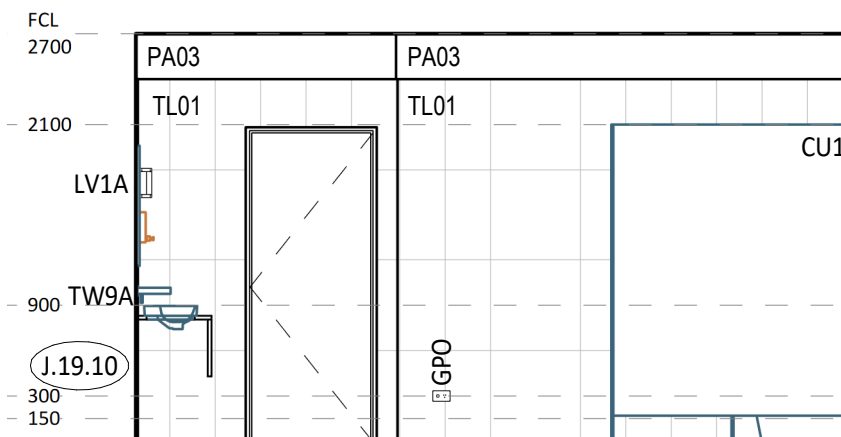

15 ELEVATION DETAIL
1 : 50

ISSUE FOR TENDER

RLS - BLD19-L3 - PWD, TOILETS

scale project no.
1 : 50 @ A1 260018

revision
A

sheet no.
CQU-ROK-019-03-ARC-60-06