

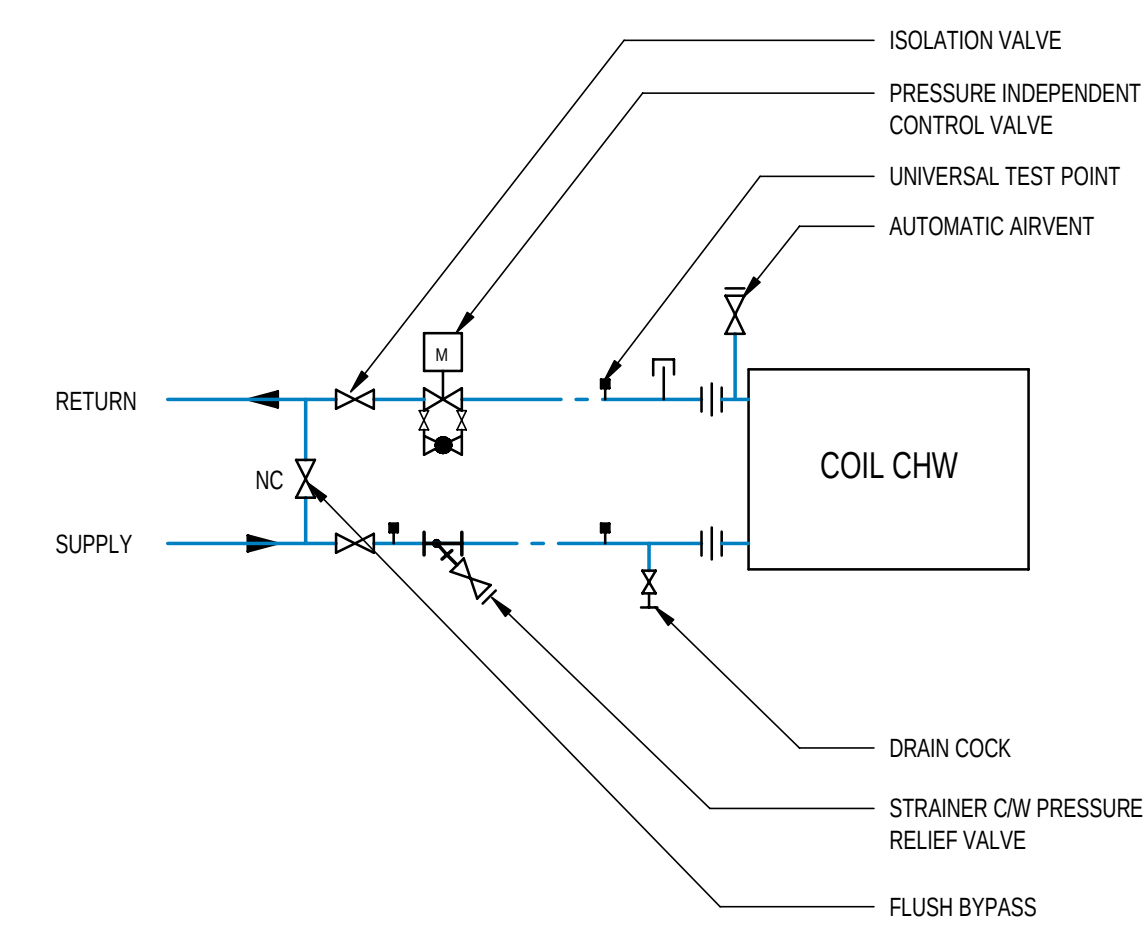
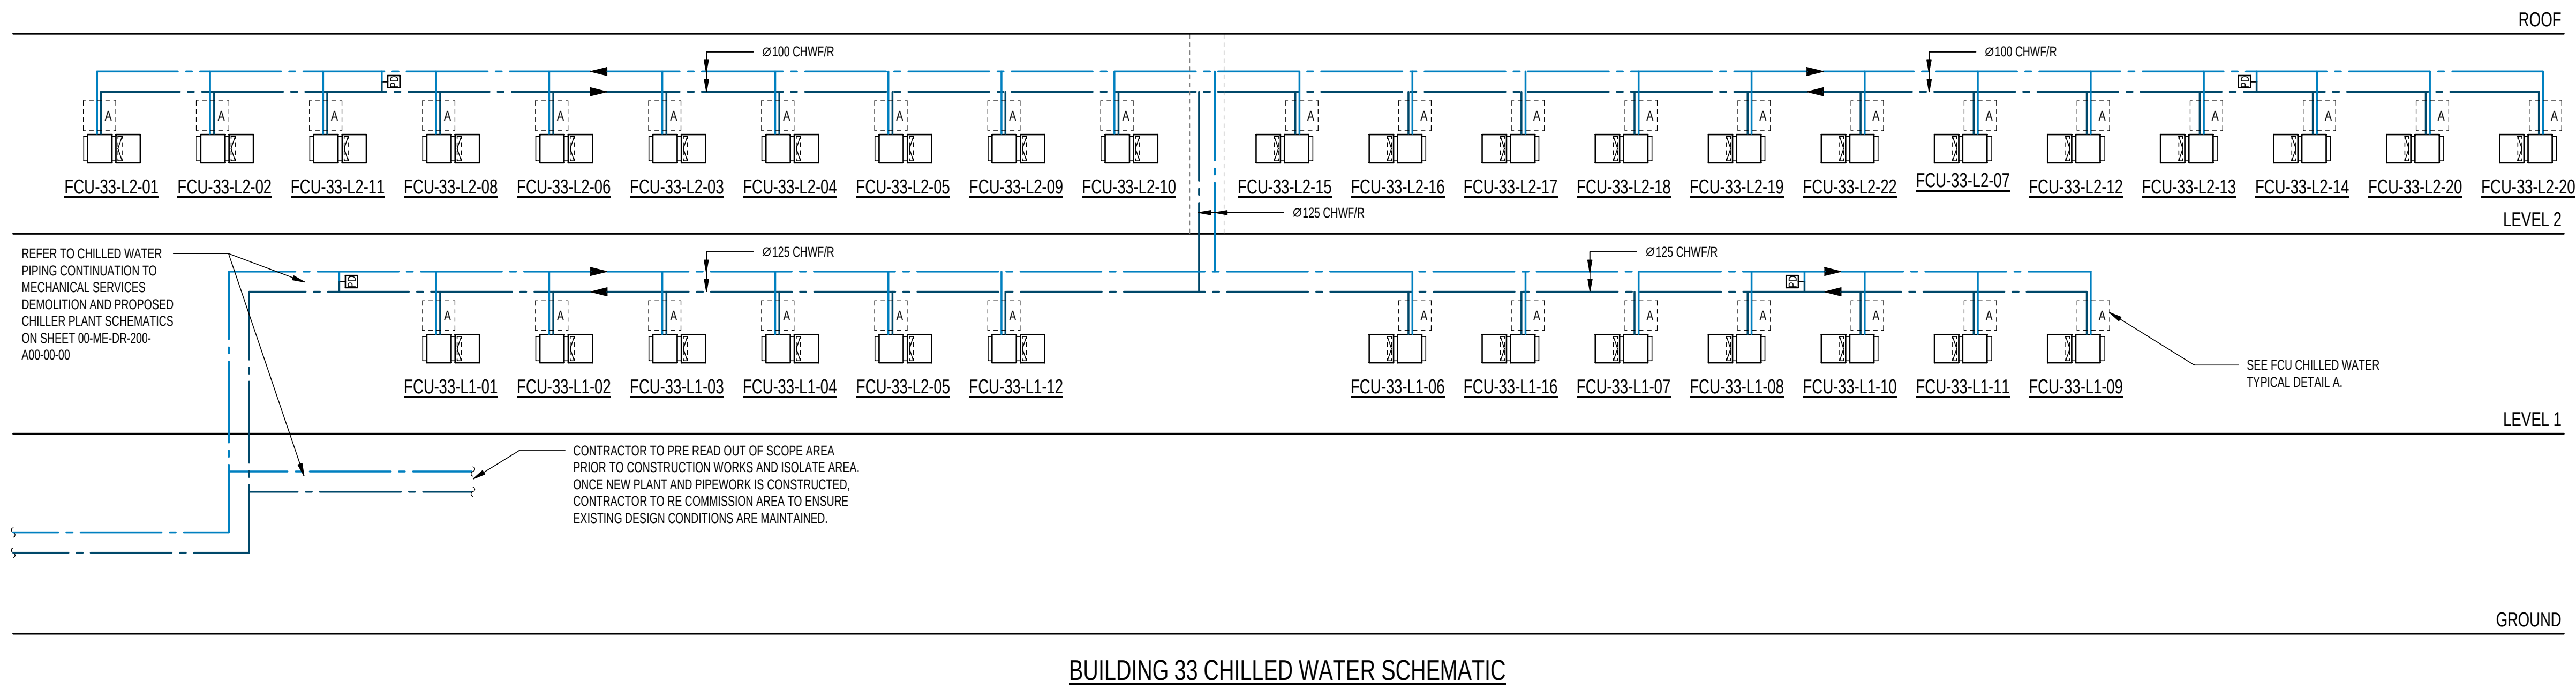
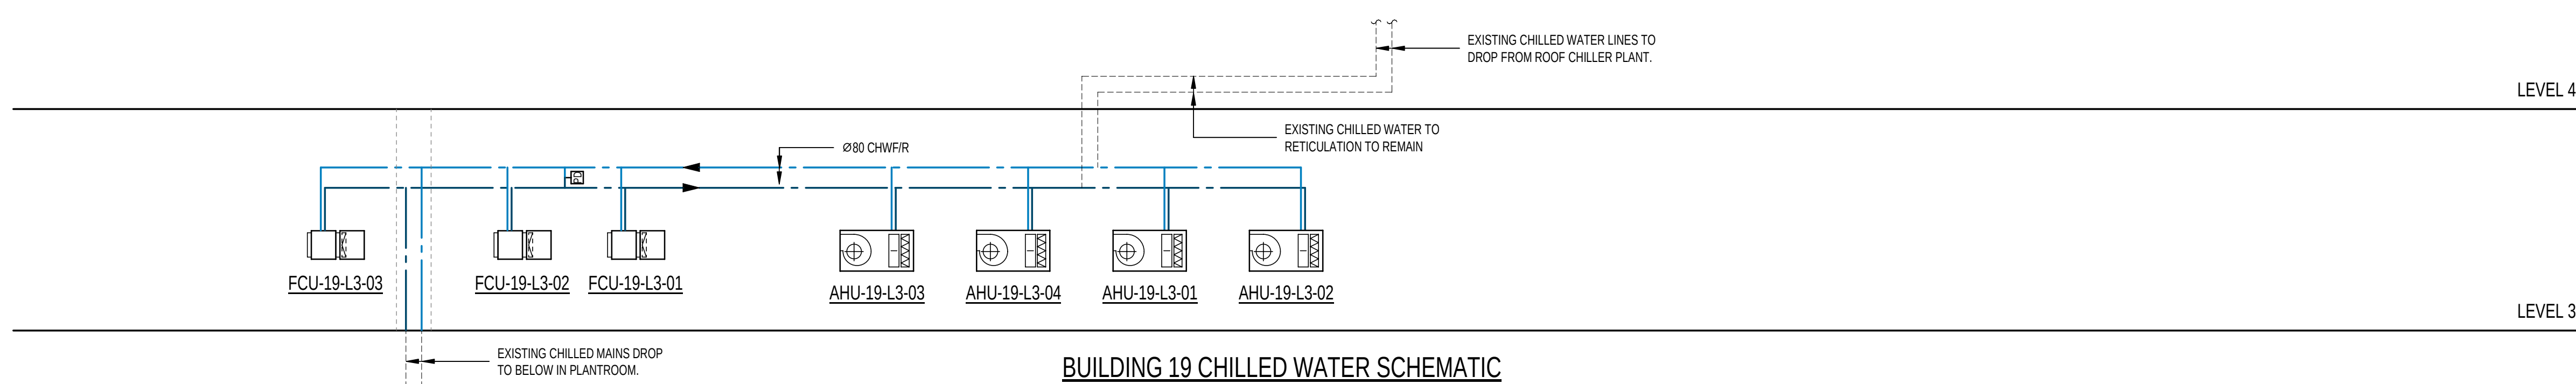


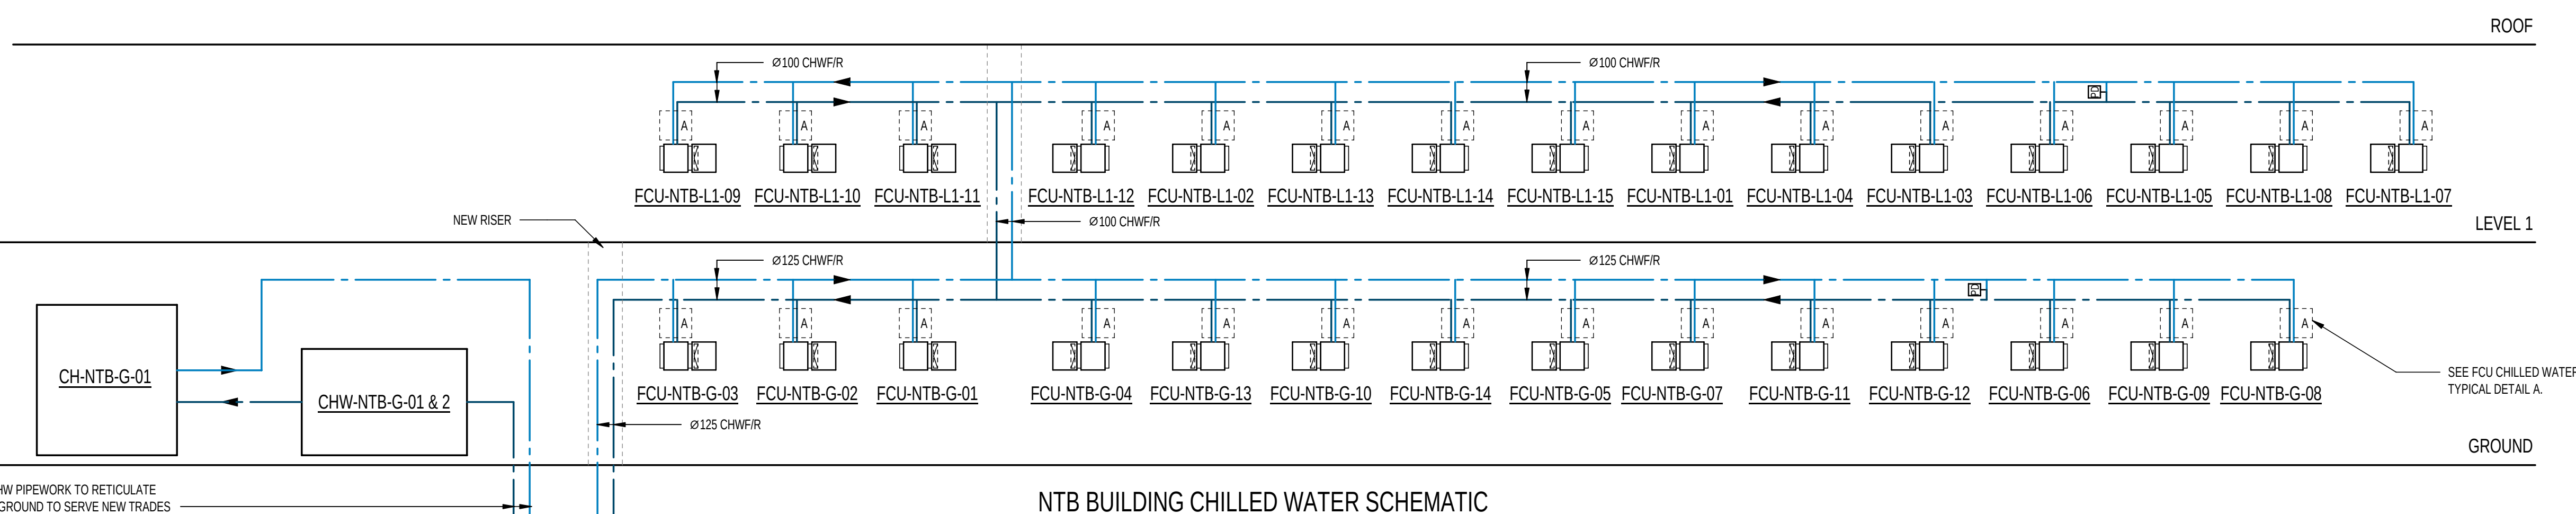

DETAIL A - CHW COIL CONNECTION DETAIL
N.T.S.

INFORMATION REFLECTED ON THIS DRAWING REPRESENTS MECHANICAL SERVICES DESIGN DEVELOPED FOR D&C TENDER ADVISE ONLY, AND SHOULD NOT BE REGARDED AS COMPLETE. THE D&C CONTRACTOR SHOULD REFER TO ALL ASSOCIATED ARCHITECTURAL AND OTHER DISCIPLINE DRAWINGS, PROJECT BRIEFS AND CLIENT REQUIREMENTS AND MAKE ADEQUATE ALLOWANCES FOR ALL NECESSARY MECHANICAL SERVICES WORKS TO MEET THESE REQUIREMENTS, EQUIPMENT SCHEDULES AND COMPLIANCE WITH THE NCC & APPROPRIATE AUSTRALIAN STANDARDS

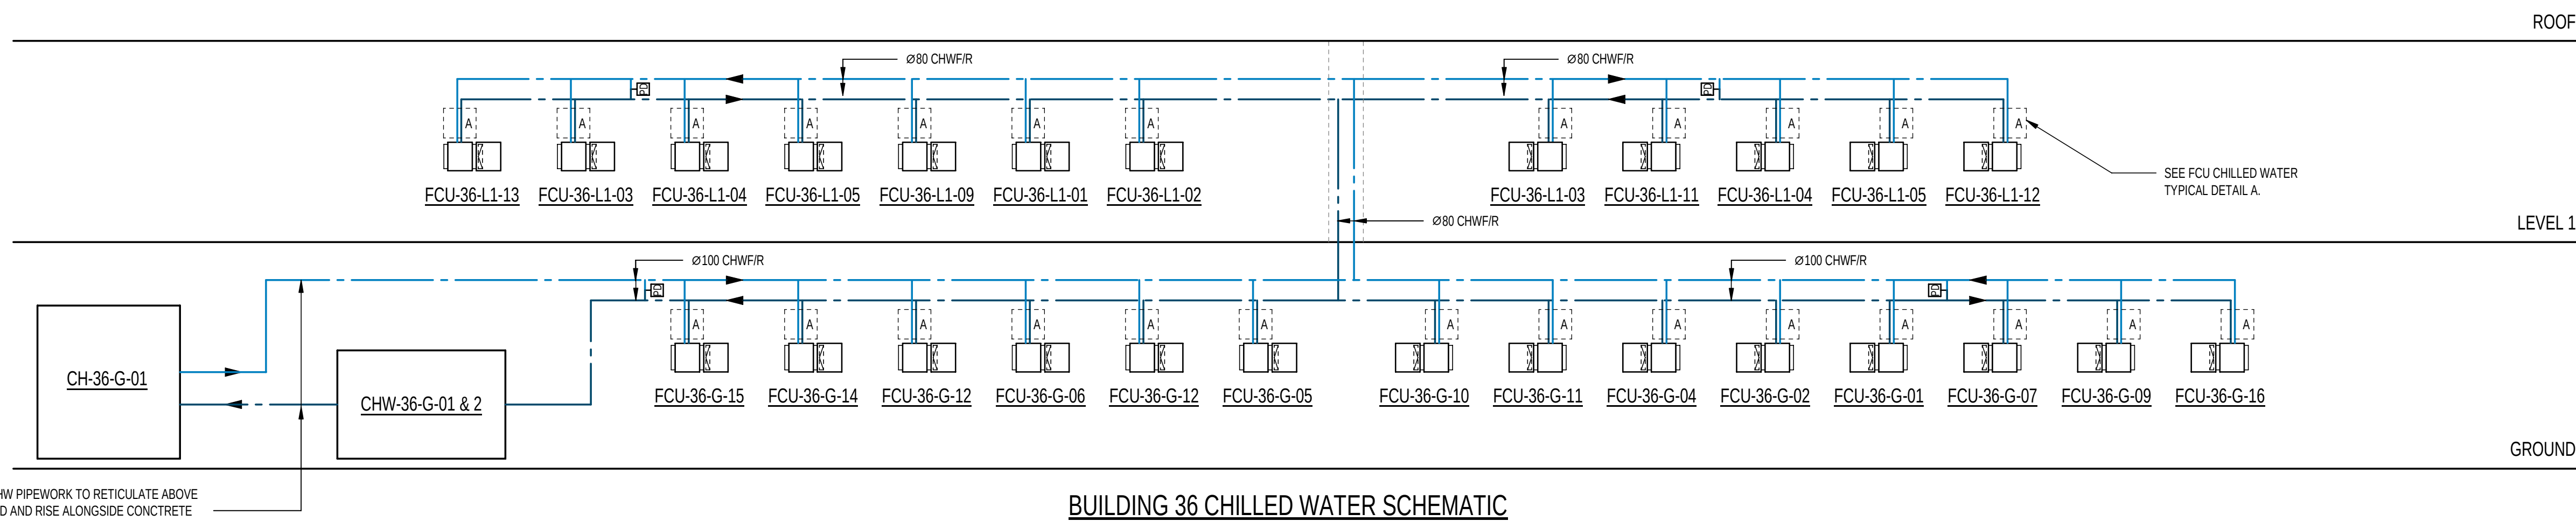

A	15.01.2020	RD	ISSUED FOR D&C TENDER	MB	SM
REV	DATE	BY	DESCRIPTION	CHK	APP
DRAWING STATUS					
DESIGN DEVELOPMENT					
CLIENT: CQU					
ARCHITECT: THOMSON ADSETT / PEDDLE THORP					
PROJECT: CQU ROCKHAMPTON TAFE CONSOLIDATION					
TITLE: MECHANICAL SERVICES - CHILLED WATER PIPING SCHEMATICS					
SCALE @ A1	N.T.S.	CHECKED: MB	APPROVED: SM		
PROJECT NUMBER: PS229518		DRAWN: RD	DATE: FEB 2026		
DRAWING NO: 00-ME-DR-210-A00-00-01				REV: A	
© WSP Australia Pty Ltd					